FONDATIONS au -4
Ech: 1/50

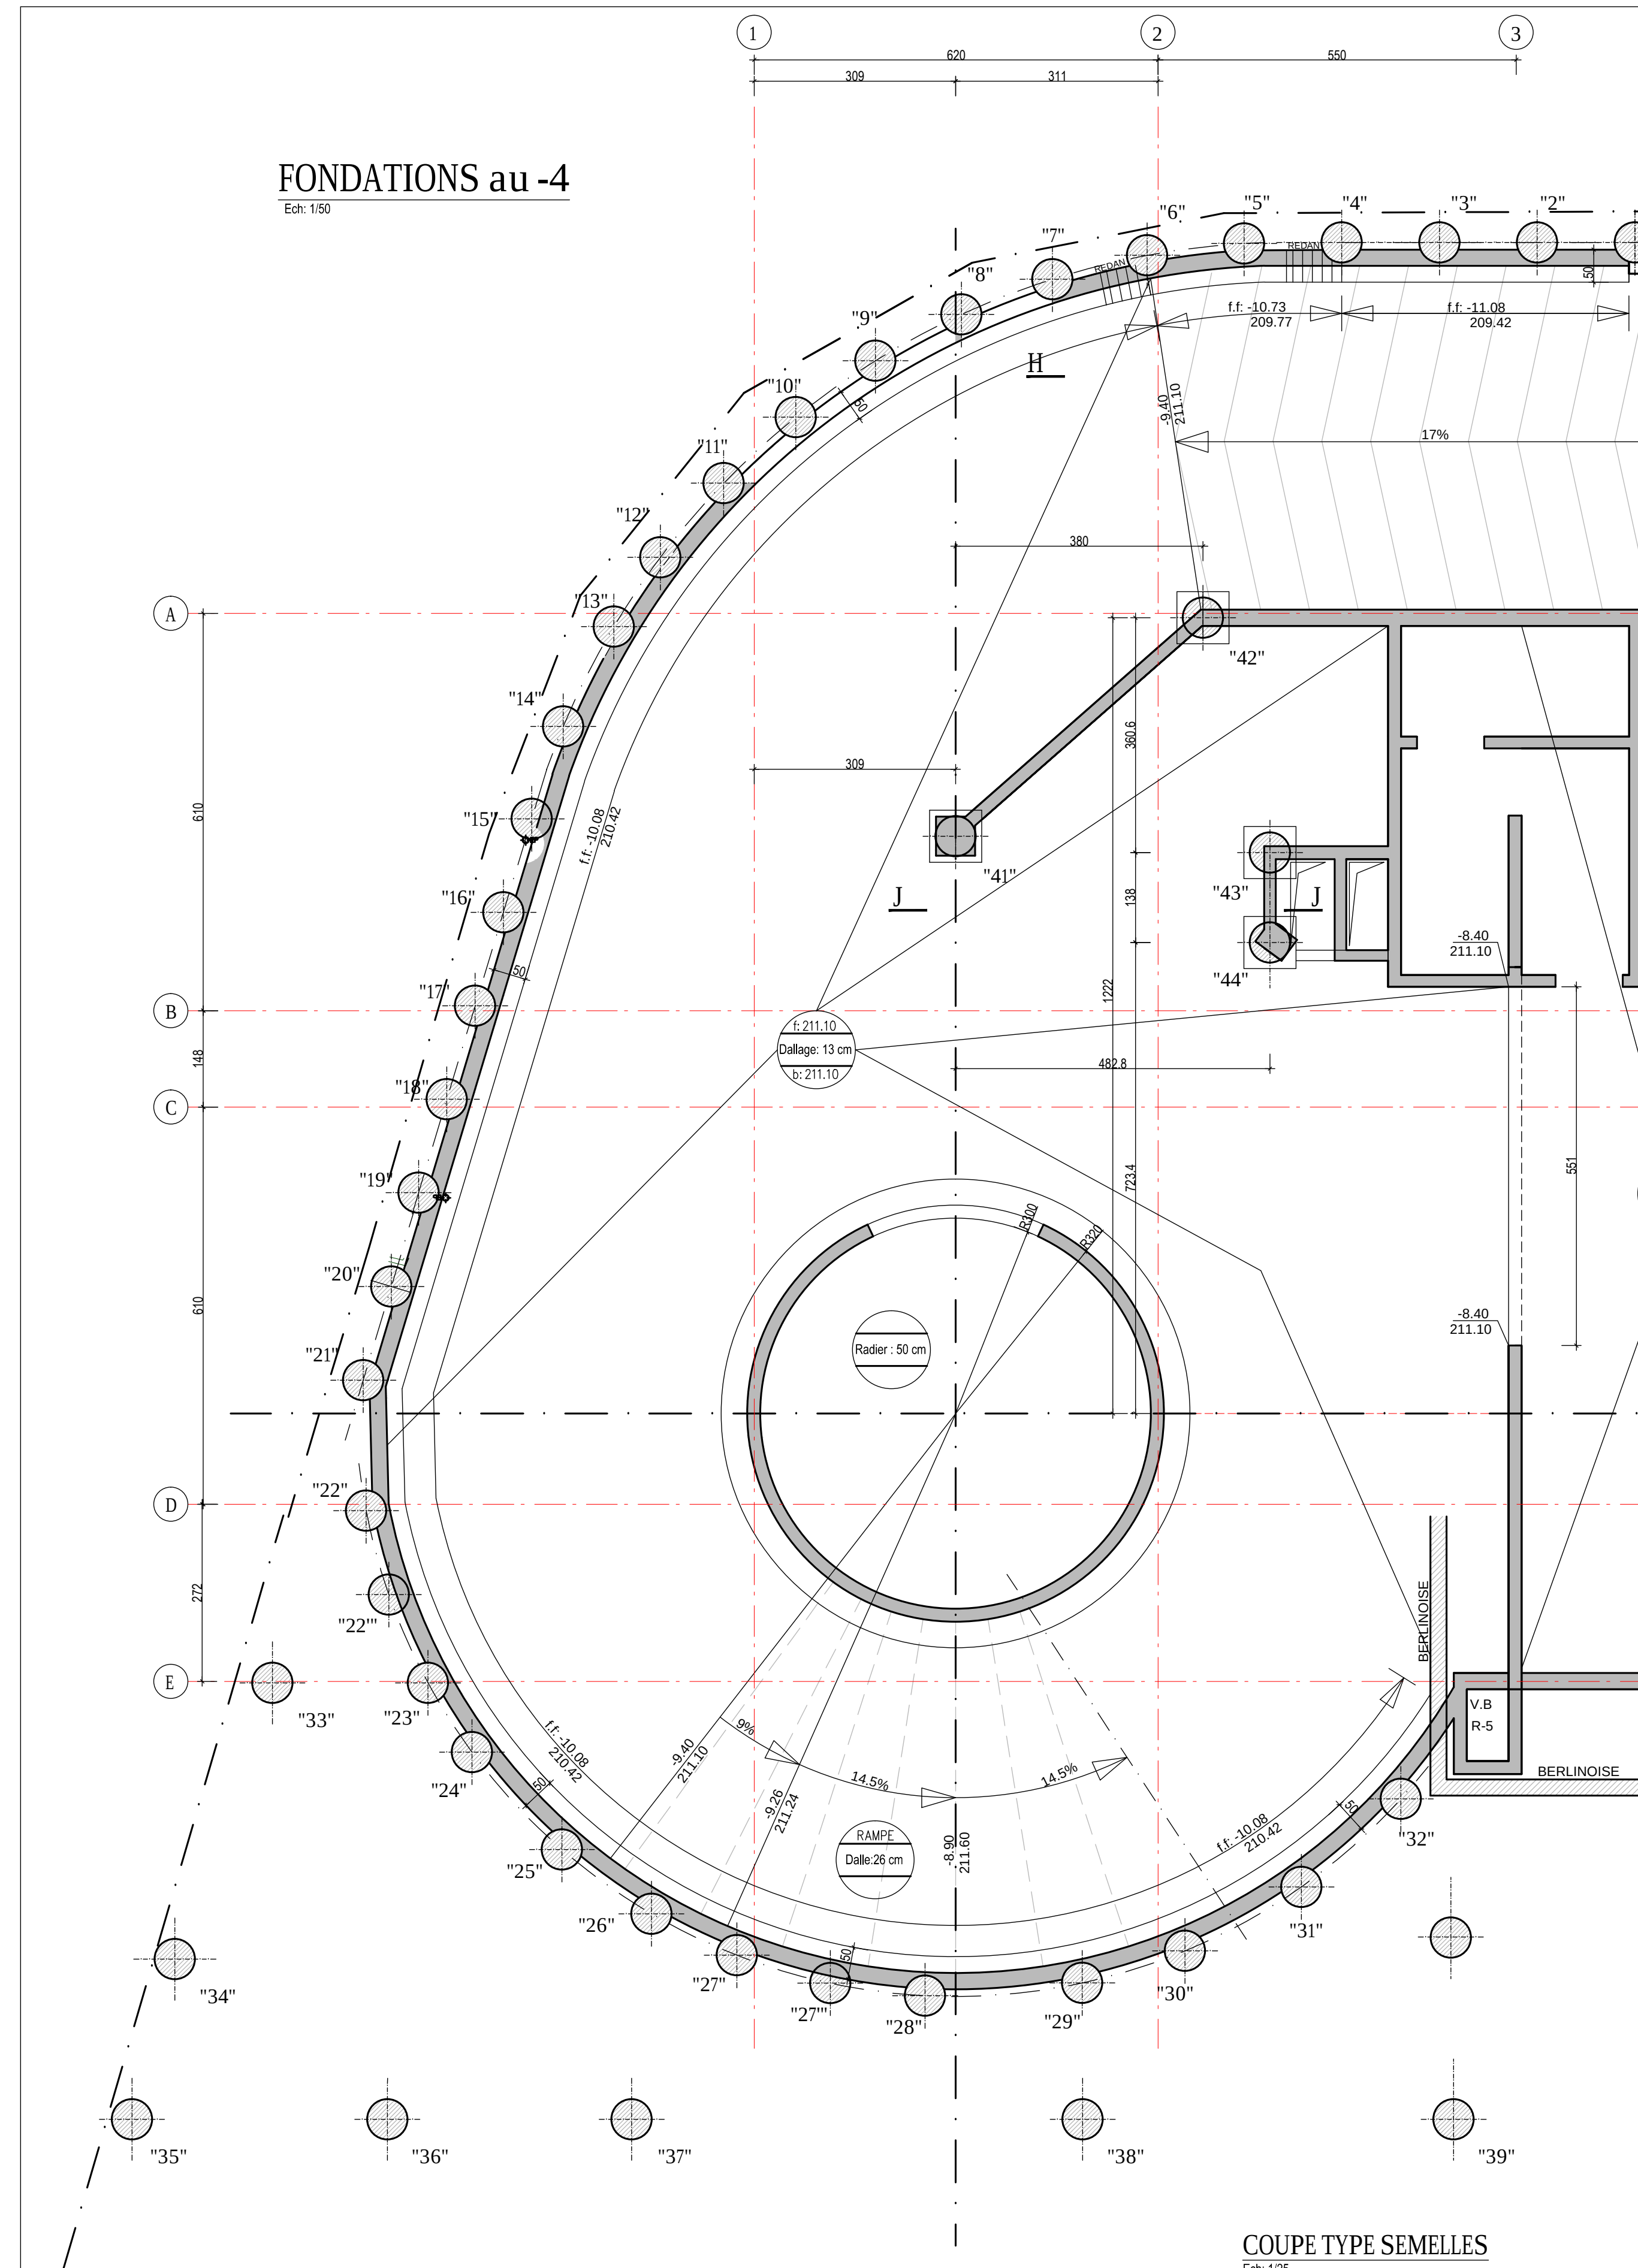
1
2
3
620
309
311
550
A
B
C
D
E
"1"
"2"
"3"
"4"
"5"
"6"
"7"
"8"
"9"
"10"
"11"
"12"
"13"
"14"
"15"
"16"
"17"
"18"
"19"
"20"
"21"
"22"
"22'"
"23"
"24"
"25"
"26"
"27"
"27'"
"28"
"29"
"30"
"31"
"32"
"33"
"34"
"35"
"36"
"37"
"38"
"39"
"41"
"42"
"43"
"44"
H
J
f.f: -10.73 209.77
f.f: -11.08 209.42
-10.70 209.80
-9.40 211.10
17%
380
309
f: 211.10 Dallage: 13 cm b: 211.10
-8.40 211.10
f: 211.10 Dalle:23 cm b: 211.10
Radier : 50 cm
R300
R320
f.f: -10.08 210.42
-9.40 211.10
-9.26 211.24
-8.90 211.60
9%
14.5%
RAMPE Dalle:26 cm
V.B R-5
BERLINOISE
REDAN

PLANCHER SUR -3
Ech: 1/50

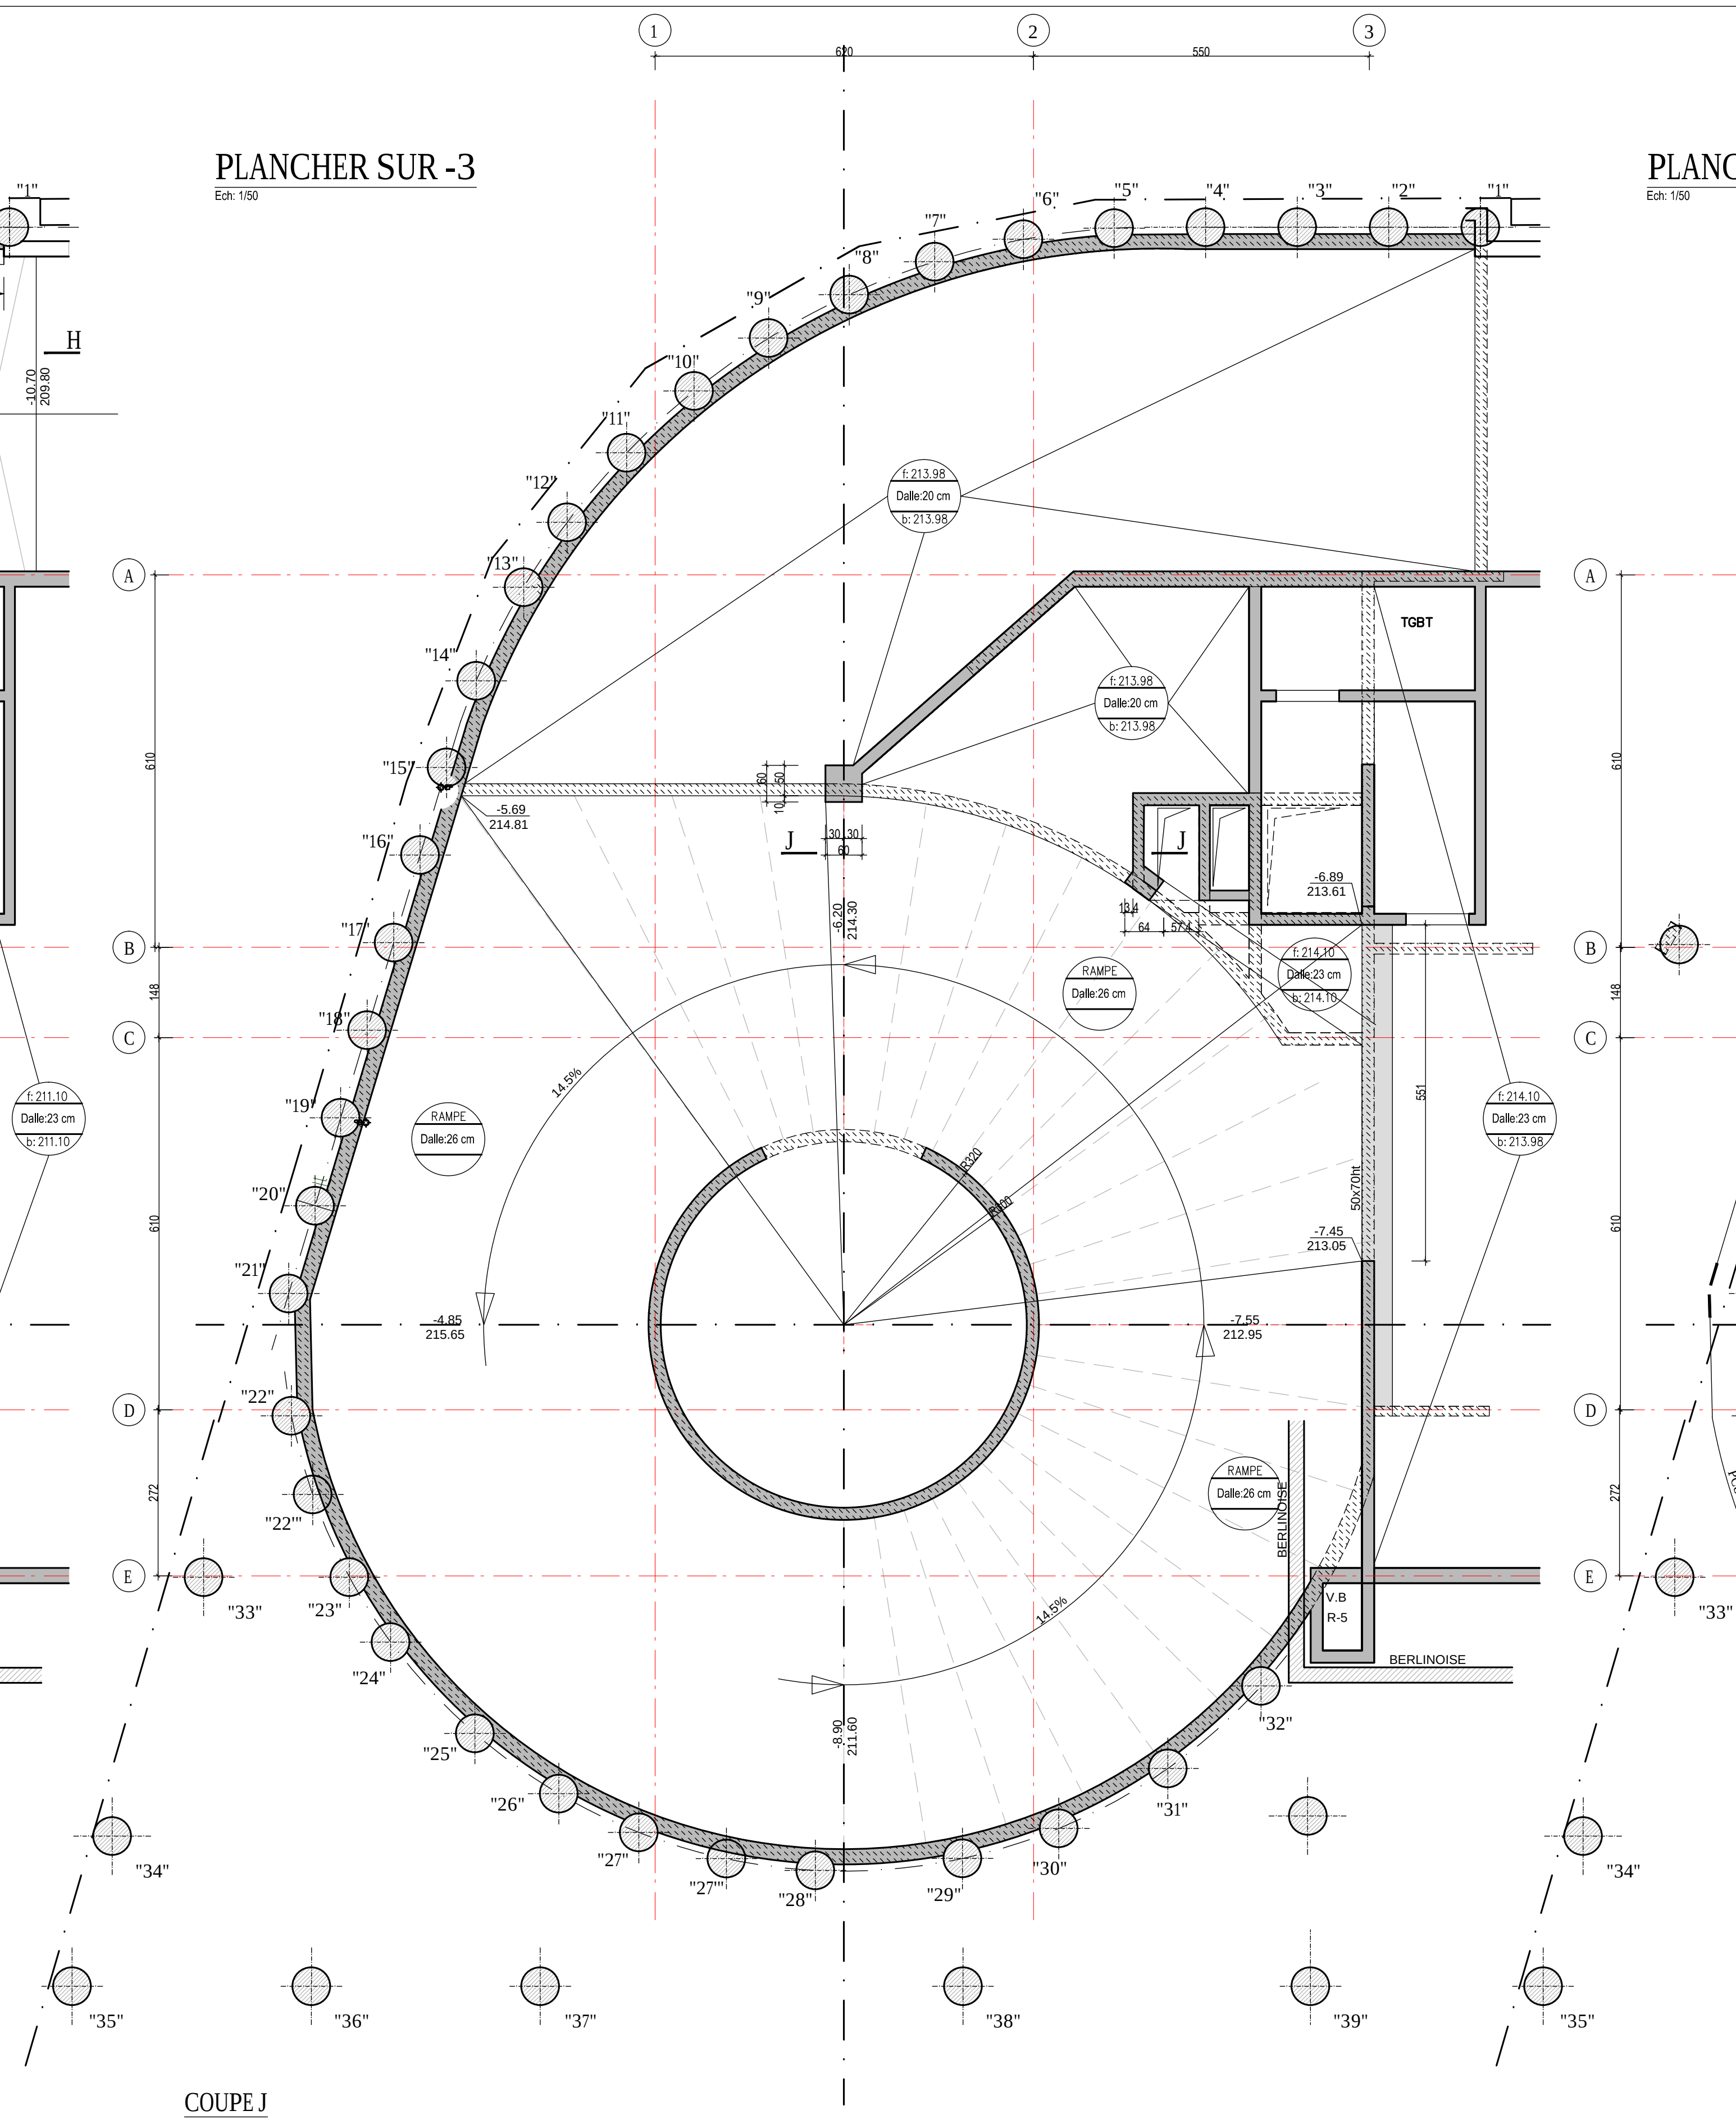
1
2
3
620
550
TGBT
f: 213.98 Dalle:20 cm b: 213.98
-5.69 214.81
-6.20 214.30
-6.89 213.61
f: 214.10 Dalle:23 cm b: 214.10
RAMPE Dalle:26 cm
f: 214.10 Dalle:23 cm b: 213.98
-7.45 213.05
-4.85 215.65
-7.55 212.95
-8.90 211.60
14.5%
50x70ht
R320
R300
V.B R-5
BERLINOISE
"33"
"34"
"35"
"36"
"37"
"38"
"39"

PLANCHER SUR -2
Ech: 1/50

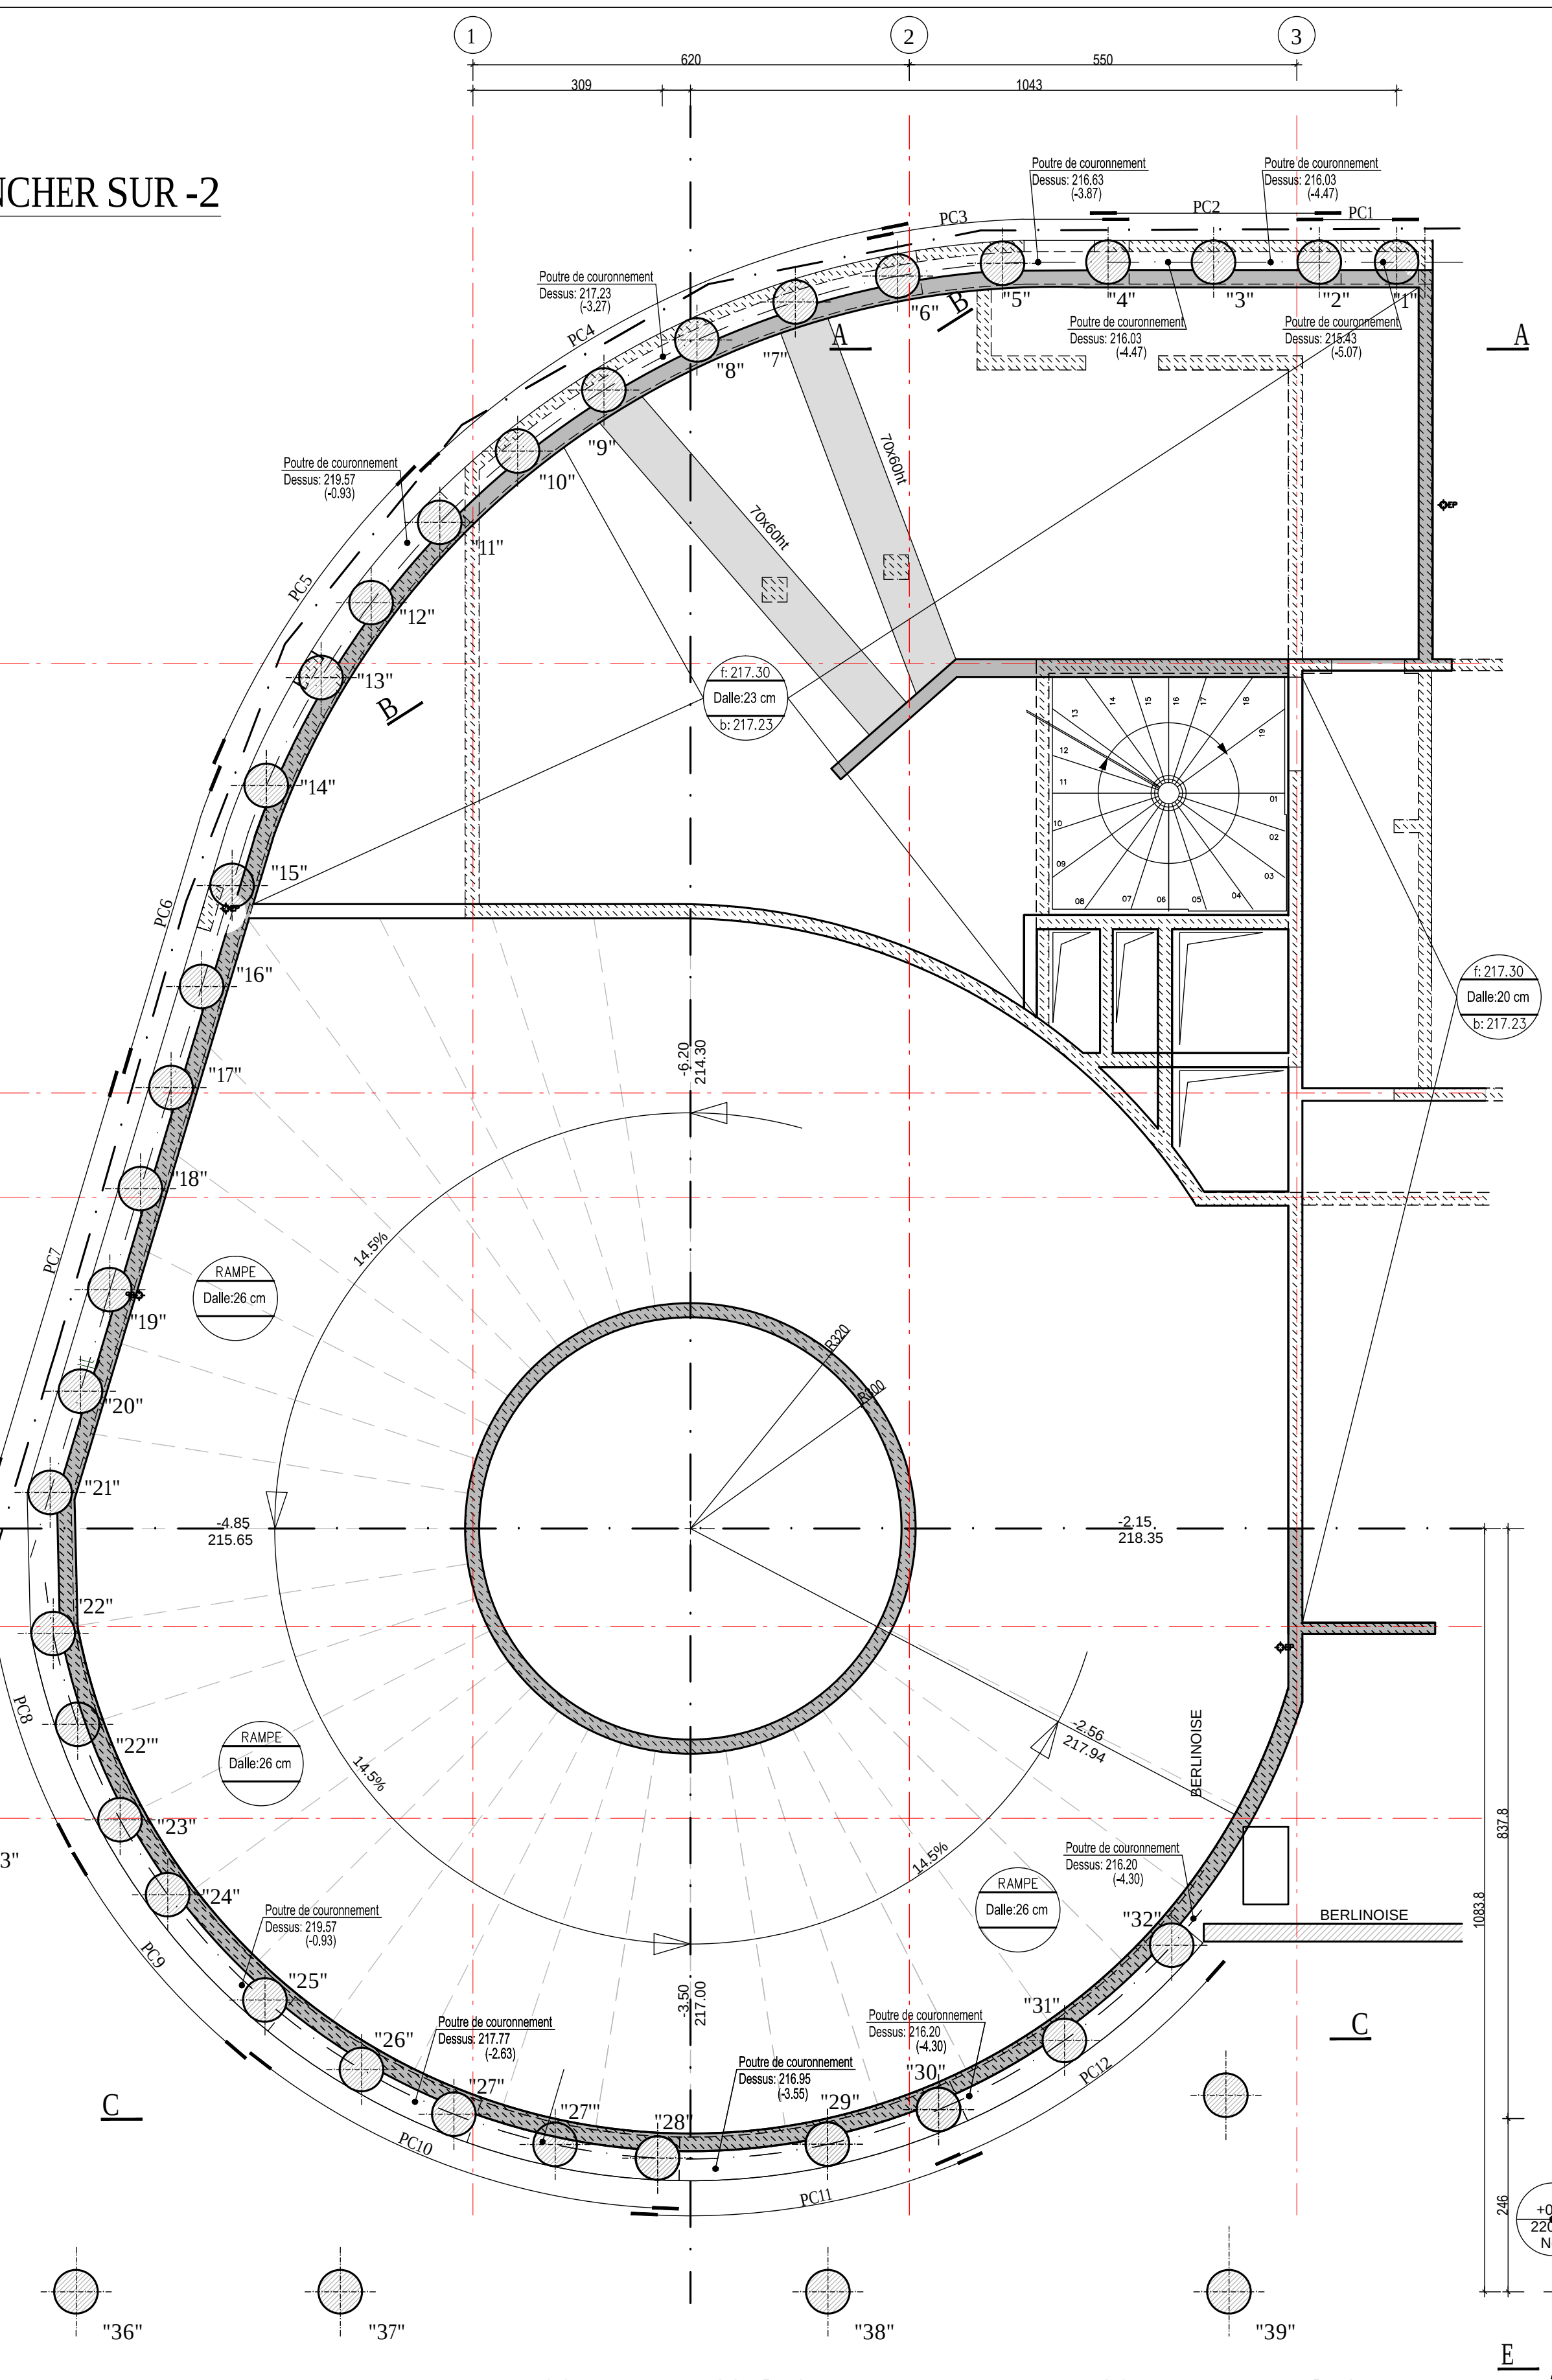
1
2
3
620
309
1043
550
PC1
PC2
PC3
PC4
PC5
PC6
PC7
PC8
PC9
PC10
PC11
PC12
Poutre de couronnement Dessus: 216,63 (-3,87)
Poutre de couronnement Dessus: 216,03 (-4,47)
Poutre de couronnement Dessus: 217,23 (-3,27)
Poutre de couronnement Dessus: 216,03 (-4,47)
Poutre de couronnement Dessus: 215,43 (-5,07)
Poutre de couronnement Dessus: 219,57 (-0,93)
Poutre de couronnement Dessus: 217,77 (-2,63)
Poutre de couronnement Dessus: 216,95 (-3,55)
Poutre de couronnement Dessus: 216,20 (-4,30)
70x60ht
f: 217.30 Dalle:23 cm b: 217.23
f: 217.30 Dalle:20 cm b: 217.23
-6.20 214.30
-4.85 215.65
-2.15 218.35
-2.56 217.94
-3.50 217.00
RAMPE Dalle:26 cm
14.5%
BERLINOISE
A
B
C

PLANCHER SUR -1
Ech: 1/50

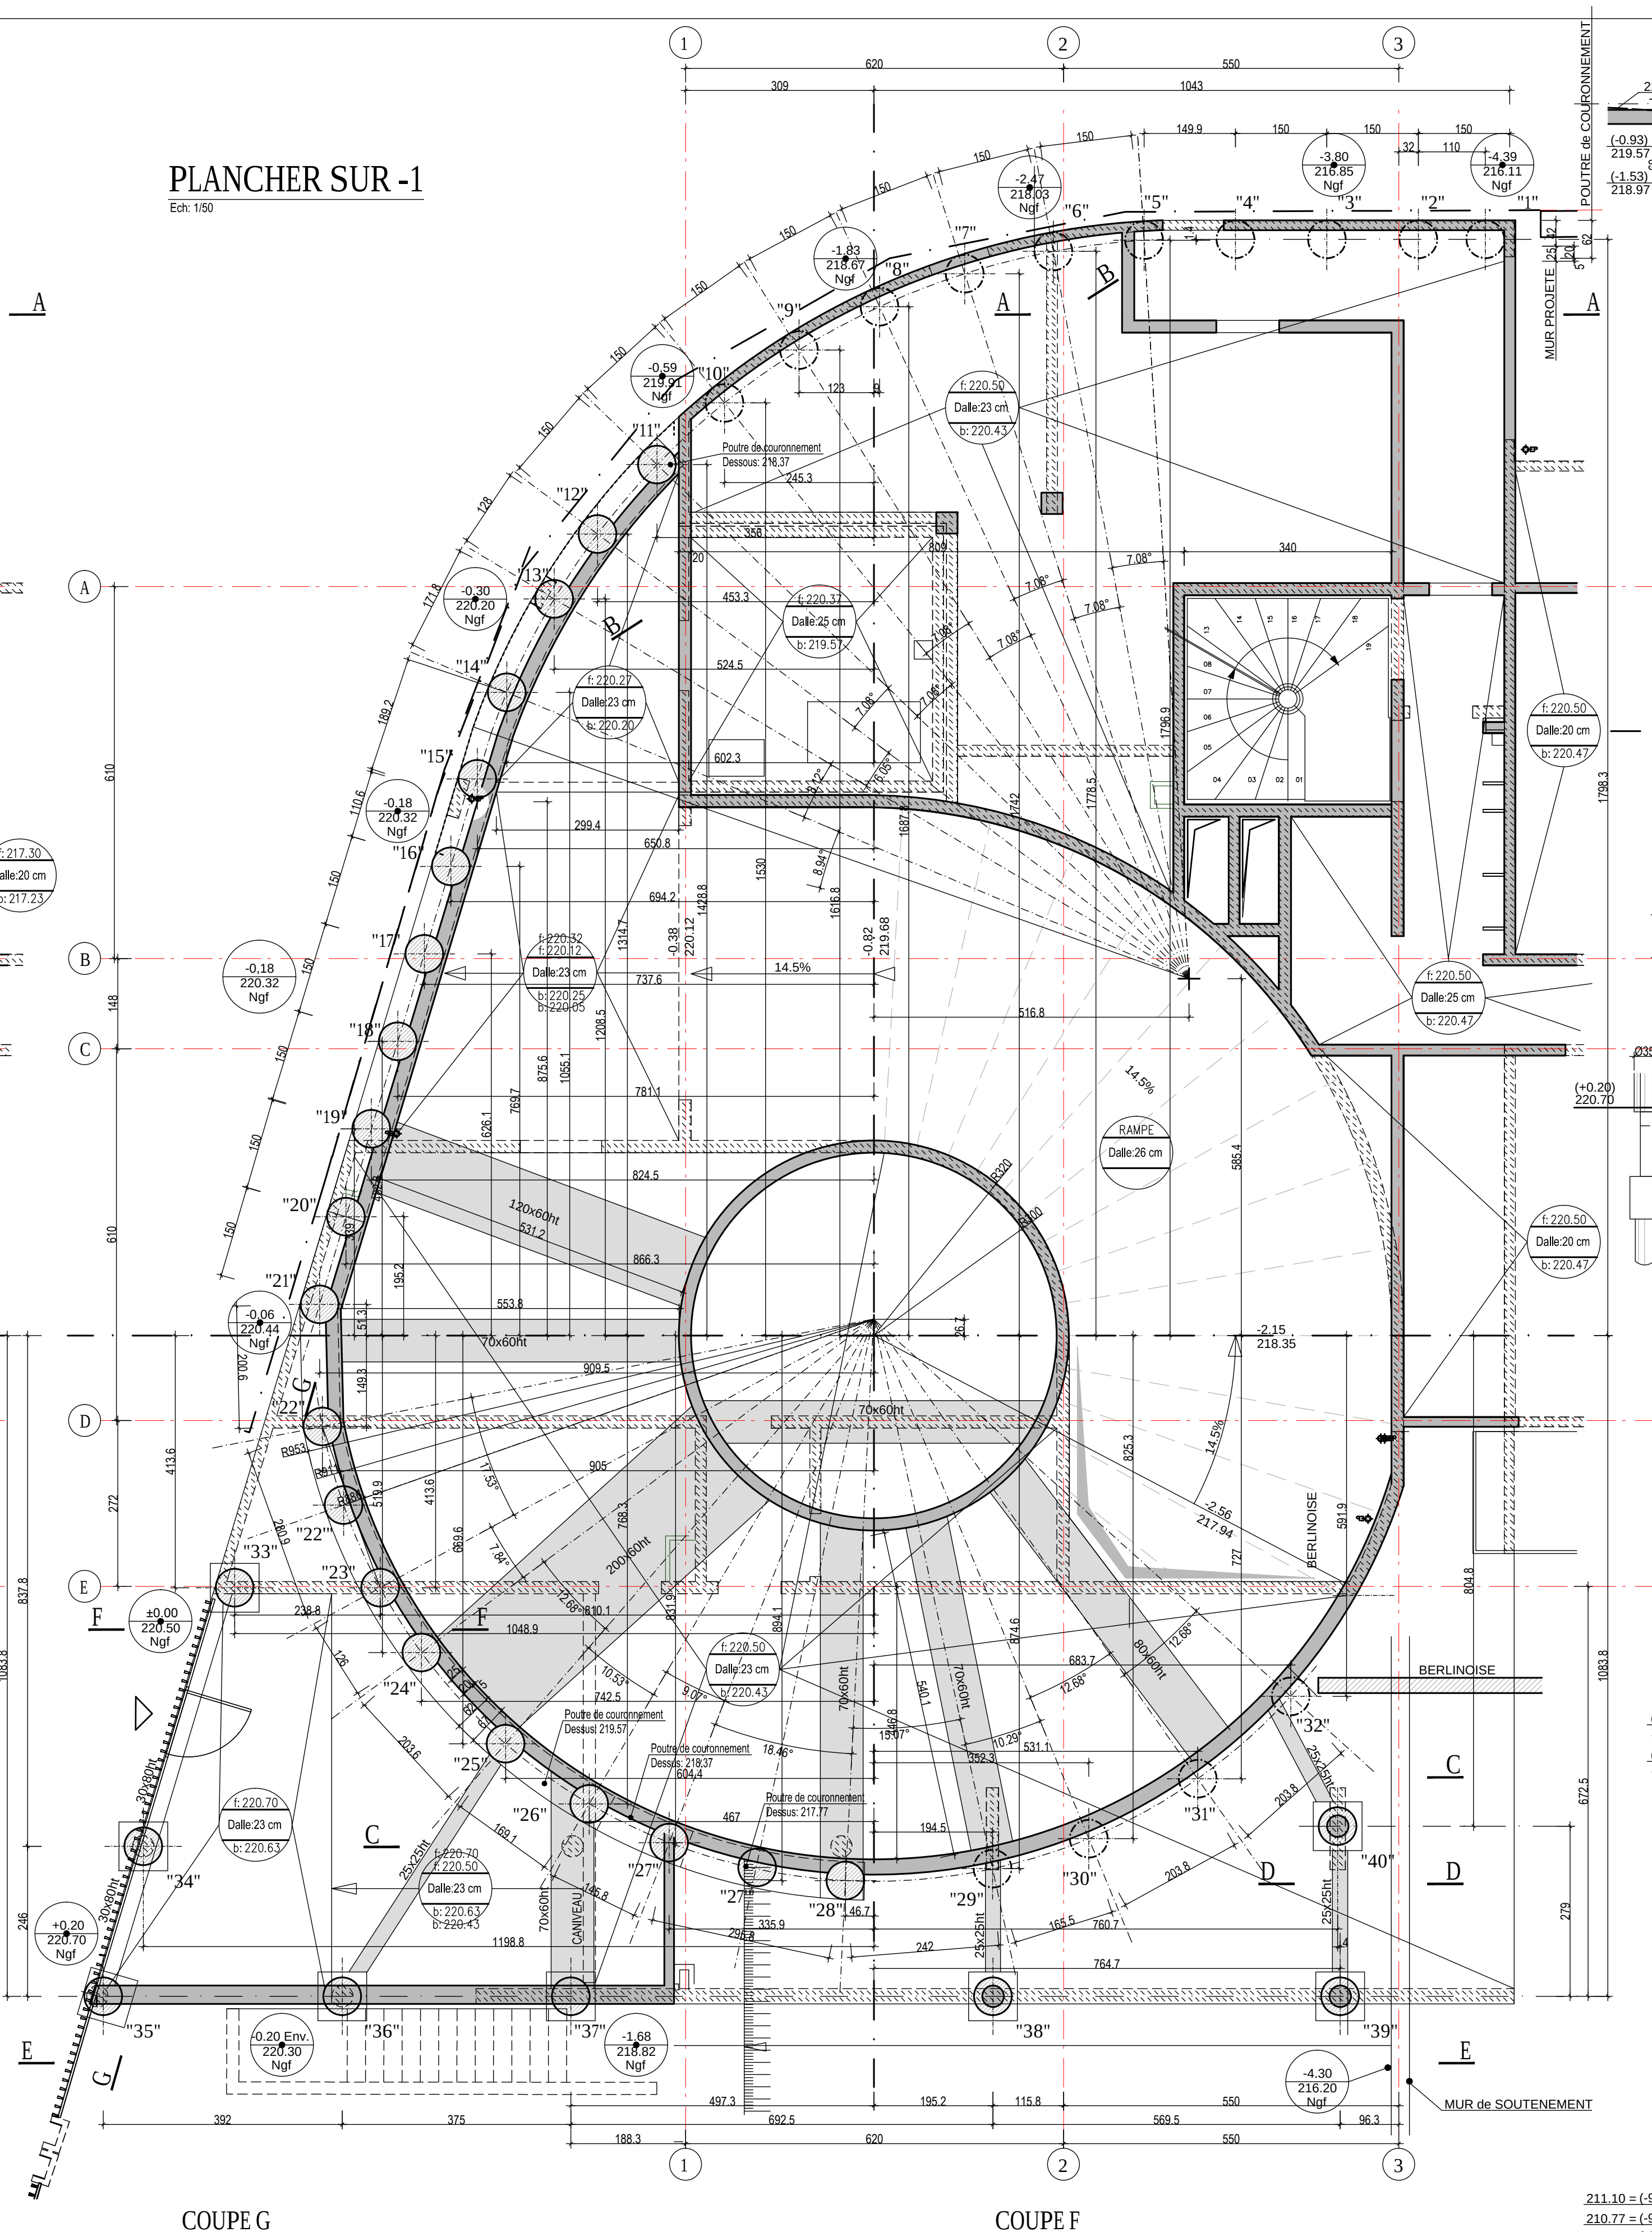
1
2
3
620
309
1043
550
-2.47 218.03 Ngf
-3.80 216.85 Ngf
-4.39 216.11 Ngf
-1.83 218.67 Ngf
-0.59 219.91 Ngf
-0.30 220.20 Ngf
-0.18 220.32 Ngf
-0.06 220.44 Ngf
±0.00 220.50 Ngf
+0.20 220.70 Ngf
-0.20 Env. 220.30 Ngf
-1.68 218.82 Ngf
-4.30 216.20 Ngf
f: 220.50 Dalle:23 cm b: 220.43
f: 220.37 Dalle:25 cm b: 219.57
f: 220.27 Dalle:23 cm b: 220.20
f: 220.50 Dalle:20 cm b: 220.47
f: 220.50 Dalle:25 cm b: 220.47
f: 220.70 Dalle:23 cm b: 220.63
RAMPE Dalle:26 cm
Poutre de couronnement Dessus: 216,37
Poutre de couronnement Dessus: 219,57
Poutre de couronnement Dessus: 218,37
Poutre de couronnement Dessus: 217,77
120x60ht
70x60ht
200x60ht
80x60ht
25x25ht
30x80ht
CANIVEAU
14.5%
7.08°
12.68°
MUR PROJETE
POUTRE de COURONNEMENT
MUR de SOUTENEMENT
BERLINOISE
A
B
C
D
E
F
G

COUPE B
Ech: 1/50

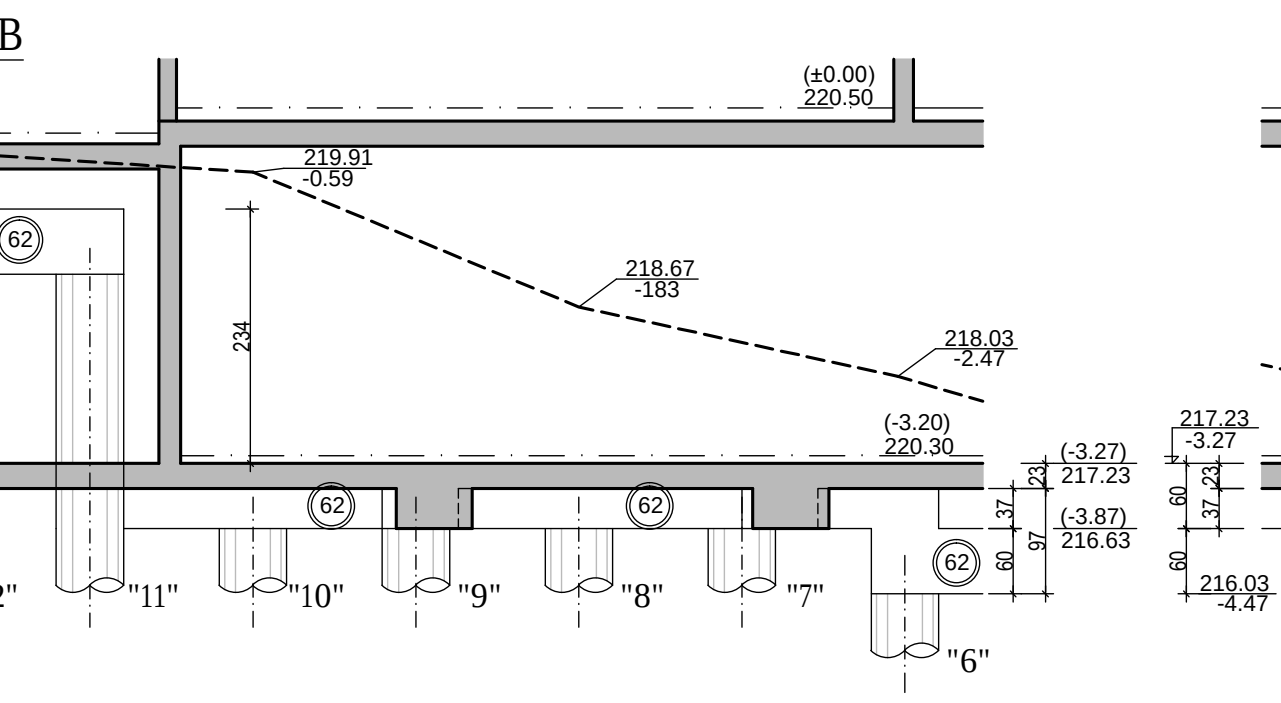
220.20 -0.30
(±0.00) 220.50
219.91 -0.59
218.67 -183
218.03 -2.47
(-0.93) 219.57
(-1.53) 218.97
(-3.20) 220.30
(-3.27) 217.23
(-3.87) 216.63
62
234
"12"
"11"
"10"
"9"
"8"
"7"
"6"

COUPE A
Ech: 1/50

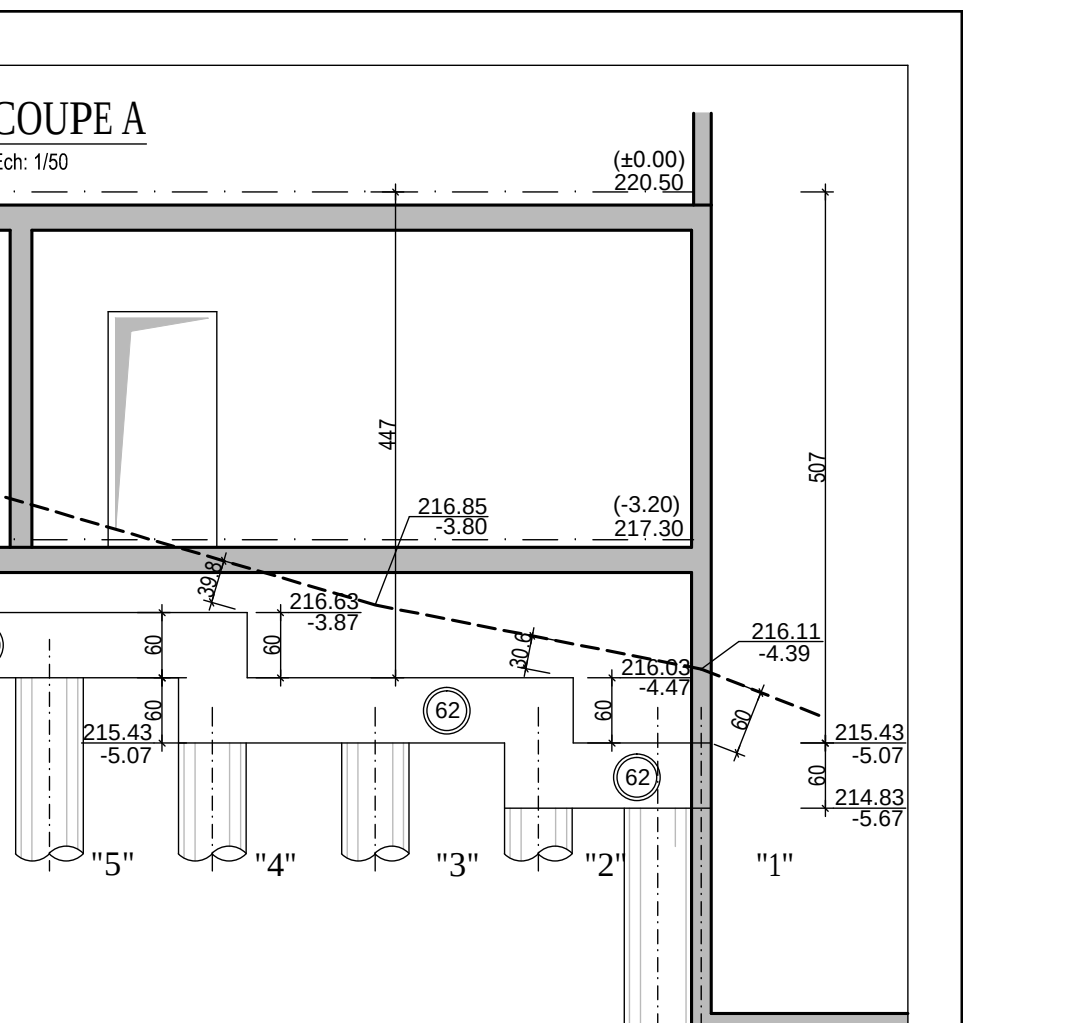
(±0.00) 220.50
218.03 -2.47
217.23 -3.27
216.85 -3.80
216.63 -3.87
216.03 -4.47
(-3.20) 217.30
216.11 -4.39
216.03 -4.47
215.43 -5.07
214.83 -5.67
447
507
62
"6"
"5"
"4"
"3"
"2"
"1"

COUPE D
Ech: 1/50

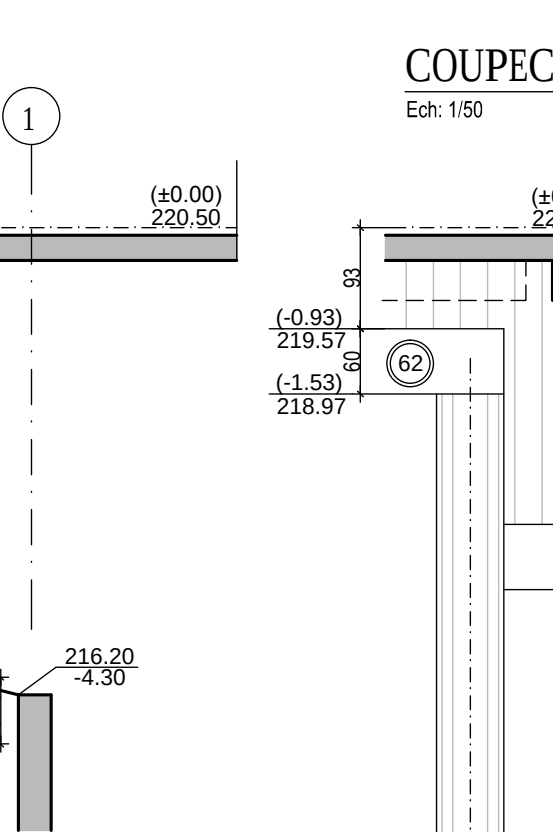
1
(±0.00) 220.50
216.20 -4.30
(-4.75) 215.75
(-5.45) 215.05
"40"

COUPEC
Ech: 1/50

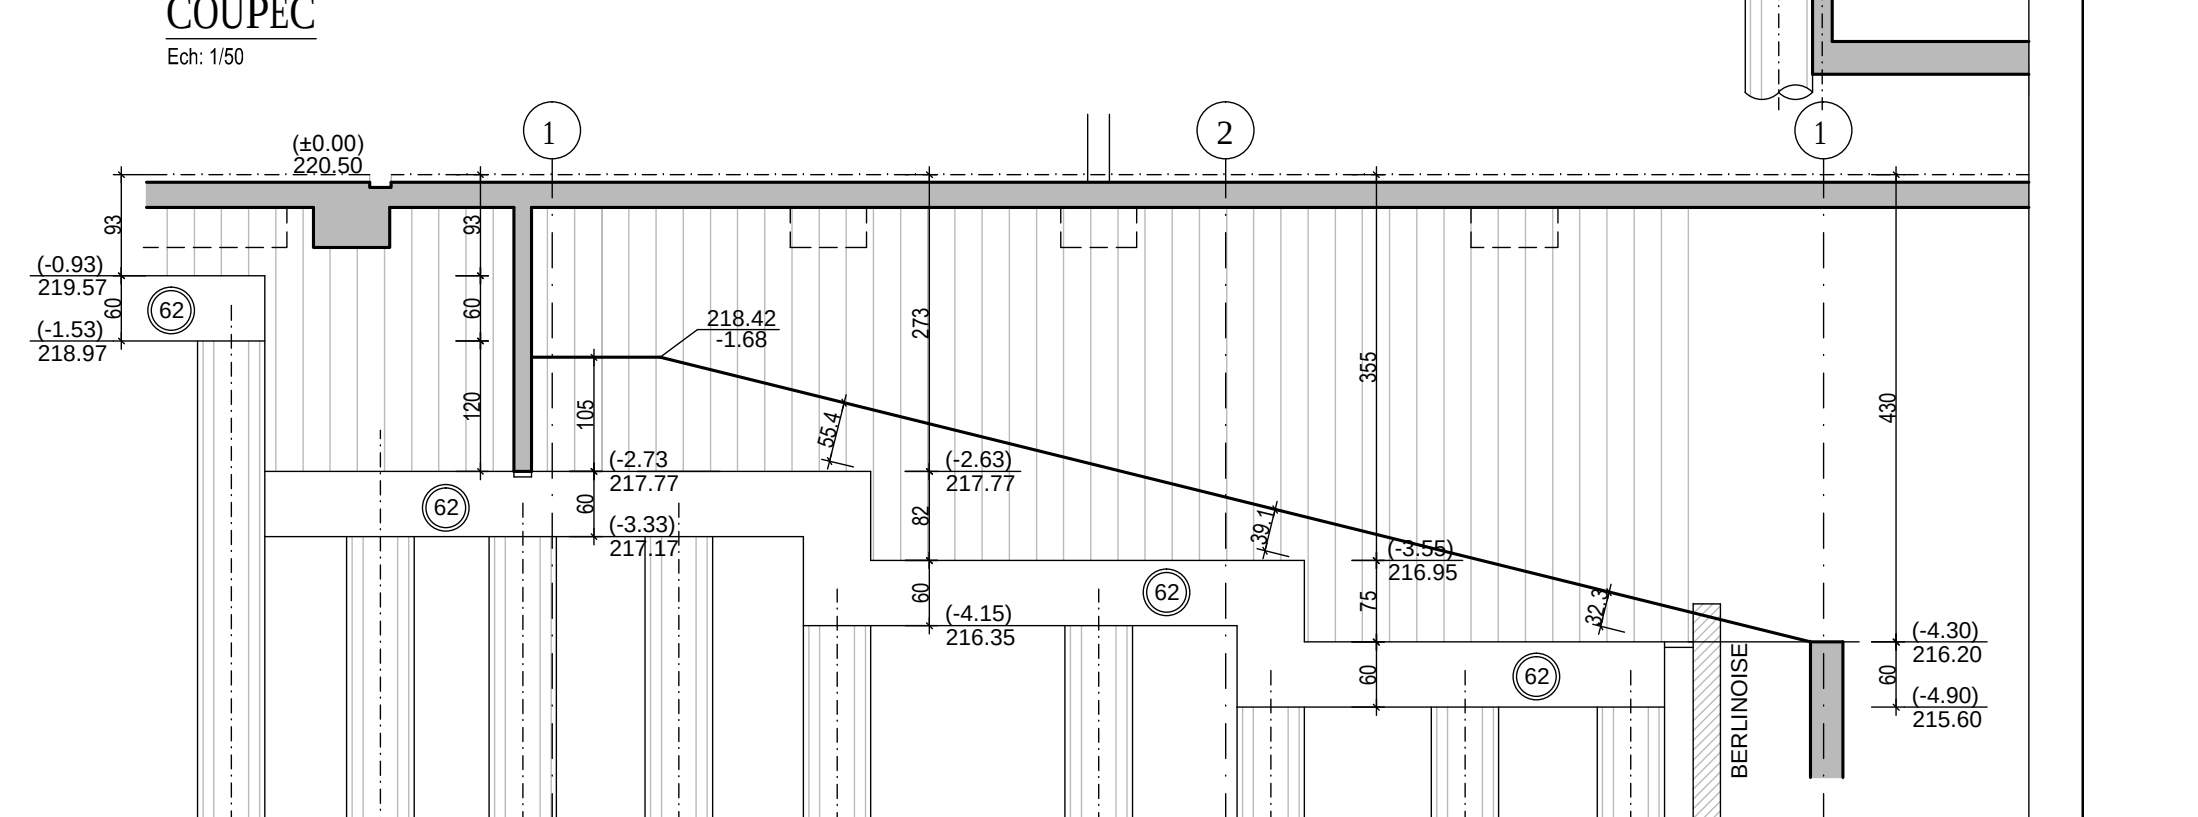
1
2
(±0.00) 220.50
(-0.93) 219.57
(-1.53) 218.97
218.42 -1.68
(-2.73) 217.77
(-3.33) 217.17
(-2.63) 217.77
(-3.55) 216.95
(-4.15) 216.35
(-4.30) 216.20
(-4.90) 215.60
62
BERLINOISE
"25"
"26"
"27"
"27'"
"28"
"29"
"30"
"31"
"32"

COUPE E
Ech: 1/50

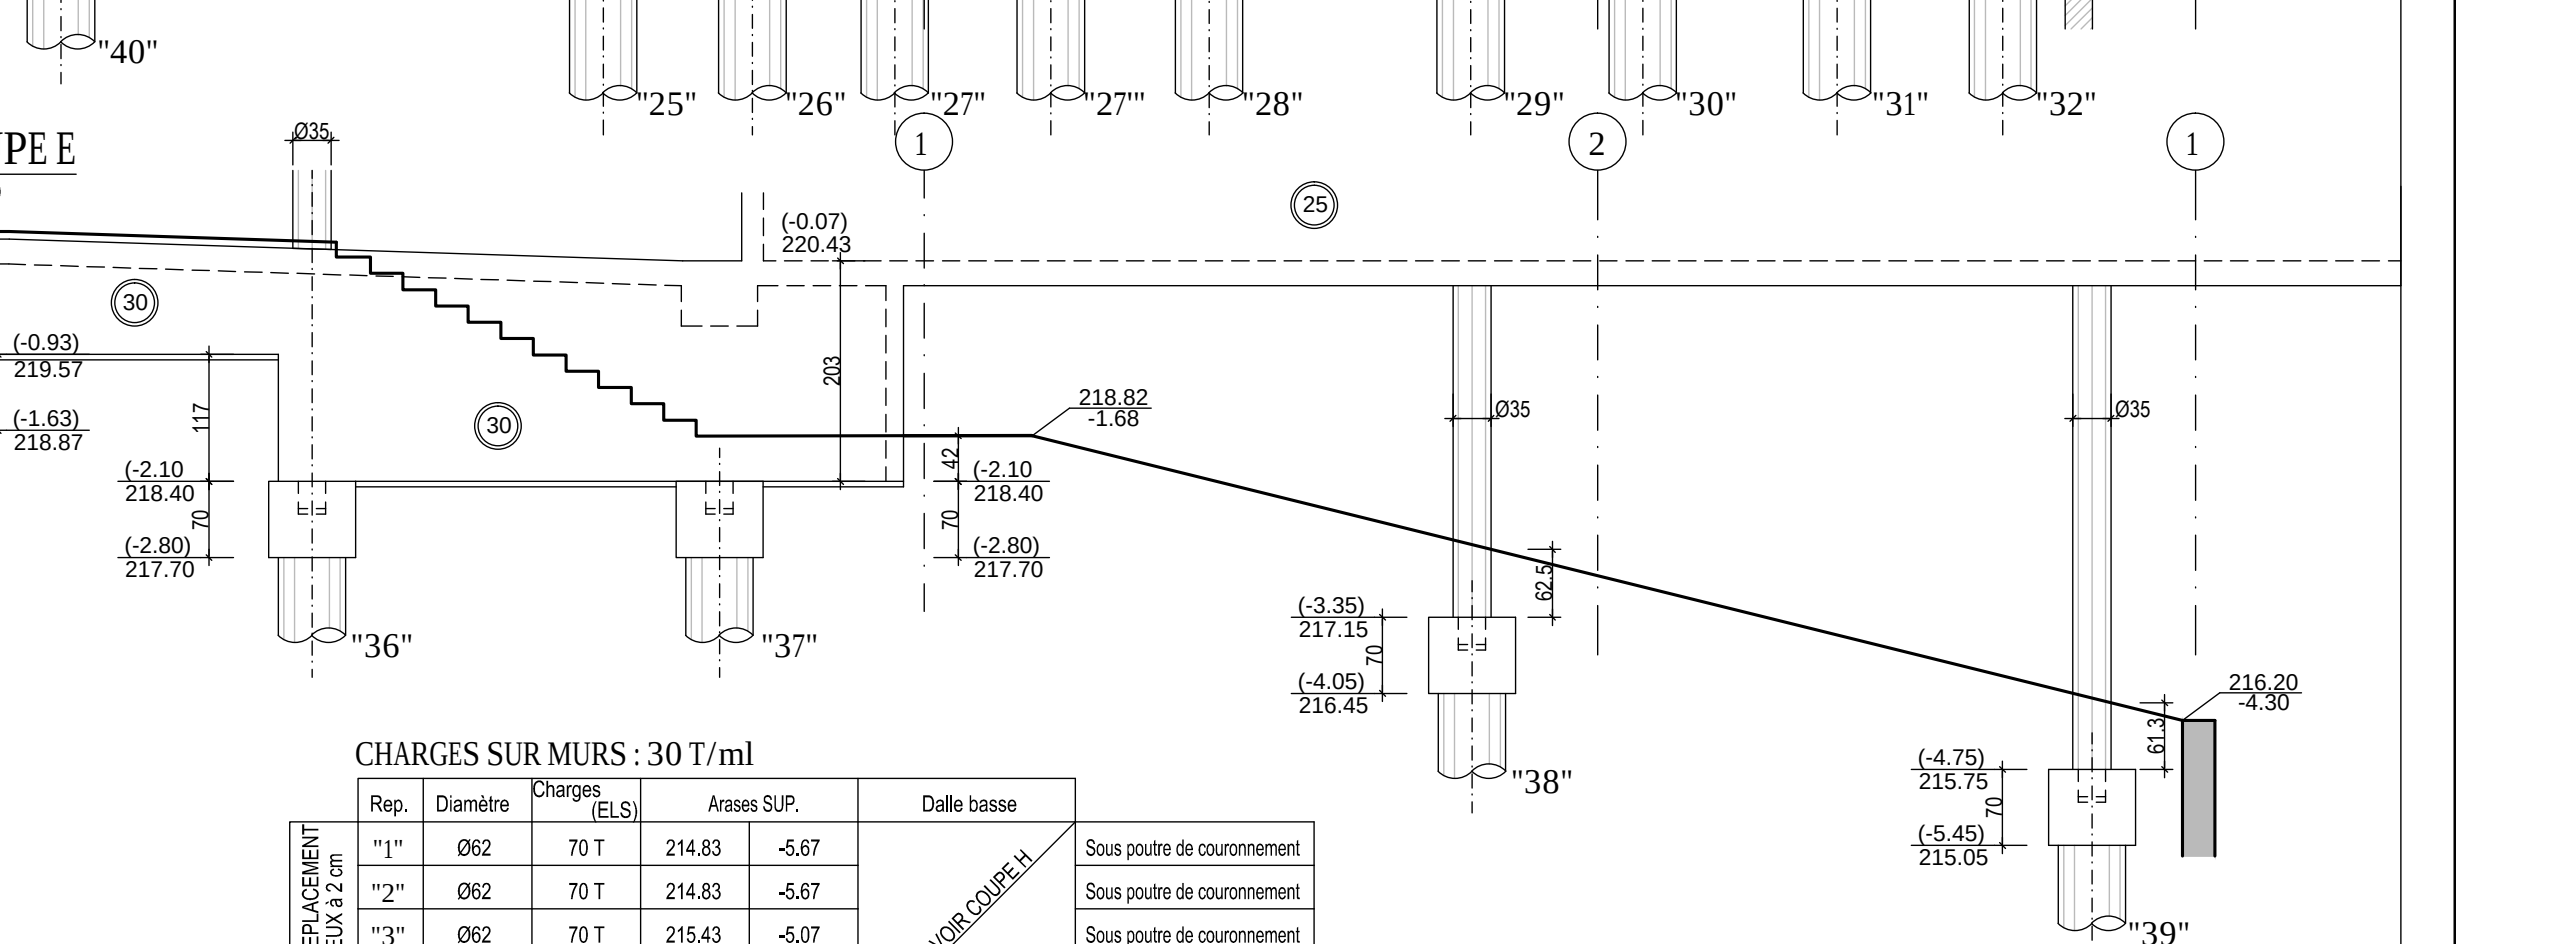
(+0.20) 220.70
(-0.07) 220.43
(-0.93) 219.57
(-1.63) 218.87
(-2.10) 218.40
(-2.80) 217.70
218.82 -1.68
(-3.35) 217.15
(-4.05) 216.45
216.20 -4.30
(-4.75) 215.75
(-5.45) 215.05
Ø35
30
25
"35"
"36"
"37"
"38"
"39"

±0.00 = 220.50

CHARGES SUR MURS : 30 T/ml

LIMMITER LE DEPLACEMENT EN TETE DE PIEUX à 2 cm

	Rep.	Diamètre	Charges (ELS)	Arases SUP.		Dalle basse		
	"1"	Ø62	70 T	214.83	-5.67	VOIR COUPE H		Sous poutre de couronnement
	"2"	Ø62	70 T	214.83	-5.67			Sous poutre de couronnement
	"3"	Ø62	70 T	215.43	-5.07			Sous poutre de couronnement
	"4"	Ø62	70 T	215.43	-5.07			Sous poutre de couronnement
	"5"	Ø62	70 T	216.03	-4.47			Sous poutre de couronnement
	"6"	Ø62	70 T	216.03	-4.47	211.10	-9.40	Sous poutre de couronnement
	"7"	Ø62	70 T	216.63	-3.87	211.10	-9.40	Sous poutre de couronnement
	"8"	Ø62	70 T	216.63	-3.87	211.10	-9.40	Sous poutre de couronnement
	"9"	Ø62	70 T	216.63	-3.87	211.10	-9.40	Sous poutre de couronnement
	"10"	Ø62	70 T	216.63	-3.87	211.10	-9.40	Sous poutre de couronnement
	"11"	Ø62	70 T	218.97	-1.53	211.10	-9.40	Sous poutre de couronnement
	"12"	Ø62	70 T	218.97	-1.53	211.10	-9.40	Sous poutre de couronnement
	"13"	Ø62	70 T	218.97	-1.53	211.10	-9.40	Sous poutre de couronnement
	"14"	Ø62	70 T	218.97	-1.53	211.10	-9.40	Sous poutre de couronnement
	"15"	Ø62	70 T	218.97	-1.53	211.10	-9.40	Sous poutre de couronnement
	"16"	Ø62	70 T	218.97	-1.53	211.10	-9.40	Sous poutre de couronnement
	"17"	Ø62	70 T	218.97	-1.53	211.10	-9.40	Sous poutre de couronnement
	"18"	Ø62	70 T	218.97	-1.53	211.10	-9.40	Sous poutre de couronnement
	"19"	Ø62	100 T	218.97	-1.53	211.10	-9.40	Sous poutre de couronnement
	"20"	Ø62	100 T	218.97	-1.53	211.10	-9.40	Sous poutre de couronnement
	"21"	Ø62	120 T	218.97	-1.53	211.10	-9.40	Sous poutre de couronnement
"22'"	"22"	Ø62	120 T	218.97	-1.53	211.10	-9.40	Sous poutre de couronnement
	"23"	Ø62	120 T	218.97	-1.53	211.10	-9.40	Sous poutre de couronnement
	"24"	Ø62	100 T	218.97	-1.53	211.10	-9.40	Sous poutre de couronnement
	"25"	Ø62	100 T	218.97	-1.53	211.10	-9.40	Sous poutre de couronnement
	"26"	Ø62	70 T	217.17	-3.33	211.10	-9.40	Sous poutre de couronnement
"27'"	"27"	Ø62	70 T	217.17	-3.33	211.10	-9.40	Sous poutre de couronnement
	"28"	Ø62	100 T	216.35	-4.15	211.10	-9.40	Sous poutre de couronnement
	"29"	Ø62	100 T	216.35	-4.15	211.10	-9.40	Sous poutre de couronnement
	"30"	Ø62	100 T	215.60	-4.90	211.10	-9.40	Sous poutre de couronnement
	"31"	Ø62	100 T	215.60	-4.90	211.10	-9.40	Sous poutre de couronnement
	"32"	Ø62	100 T	215.60	-4.90	211.10	-9.40	Sous poutre de couronnement
	"33"	Ø62	150 T	218.87	-1.63			Sous tête de pieux 80x80x70HT
	"34"	Ø62	150 T	218.87	-1.63			Sous tête de pieux 80x80x70HT
	"35"	Ø62	150 T	218.87	-1.63			Sous tête de pieux 80x80x70HT
	"36"	Ø62	150 T	217.70	-2.80			Sous tête de pieux 80x80x70HT
	"37"	Ø62	162 T	217.70	-2.80			Sous tête de pieux 80x80x70HT
	"38"	Ø62	162 T	216.45	-4.05			Sous tête de pieux 80x80x70HT
	"39"	Ø62	165 T	215.05	-5.45			Sous tête de pieux 80x80x70HT
	"40"	Ø62	152 T	215.05	-5.45			Sous tête de pieux 80x80x70HT
	"41"	Ø72	220 T	210.07	-10.43			Sous tête de pieux 80x80x70HT
	"42"	Ø62	120 T	210.07	-10.43			Sous tête de pieux 80x80x70HT
	"43"	Ø62	90 T	210.07	-10.43			Sous tête de pieux 80x80x70HT
	"44"	Ø62	120 T	210.07	-10.43			Sous tête de pieux 80x80x70HT

LIMMITER LE DEPLACEMENT EN TETE DE PIEUX à 2 cm

COUPE TYPE
Pieux "11" à "25"
Ech: 1/50

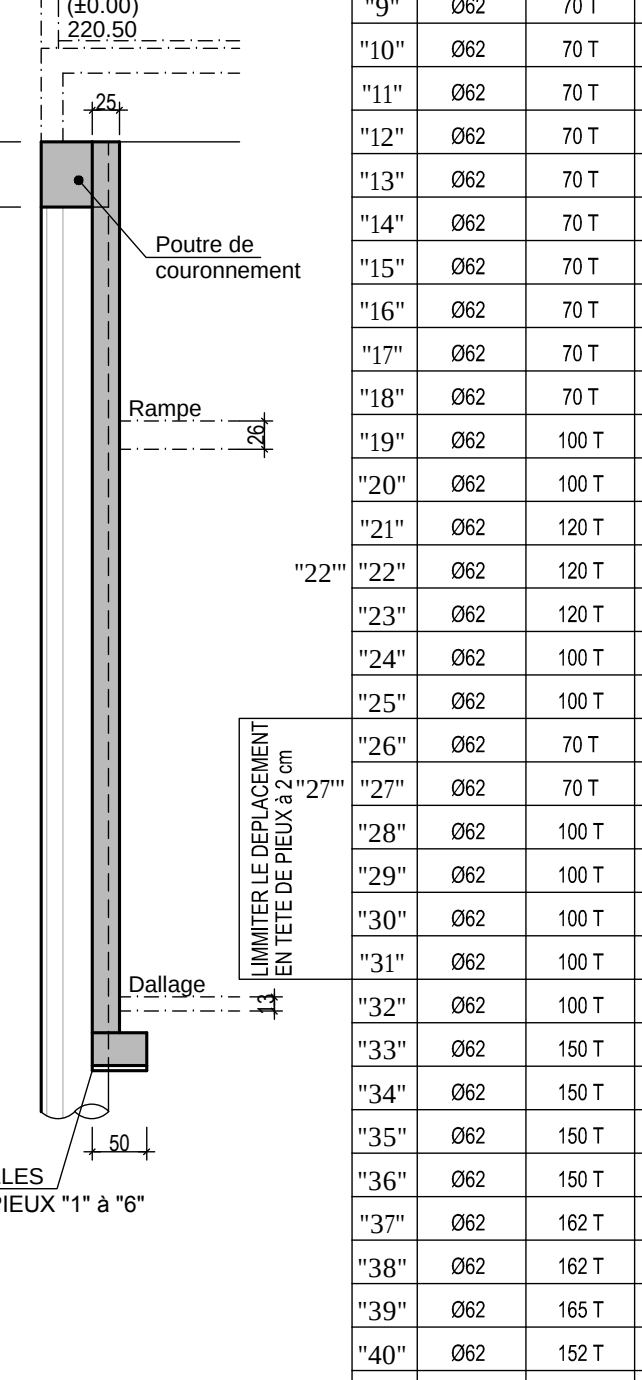
(±0.00) 220.50
25
93
60
(-0.93) 219.57
(-1.53) 218.97
Poutre de couronnement
Rampe
26
Dallage
211.10 = (-9.40)
210.77 = (-9.73)
210.47= (-10.03)
50
NIVEAUX DE SEMELLES A ADAPTER POUR PIEUX "1" à "6" VOIR COUPE H

COUPE H
Ech: 1/25

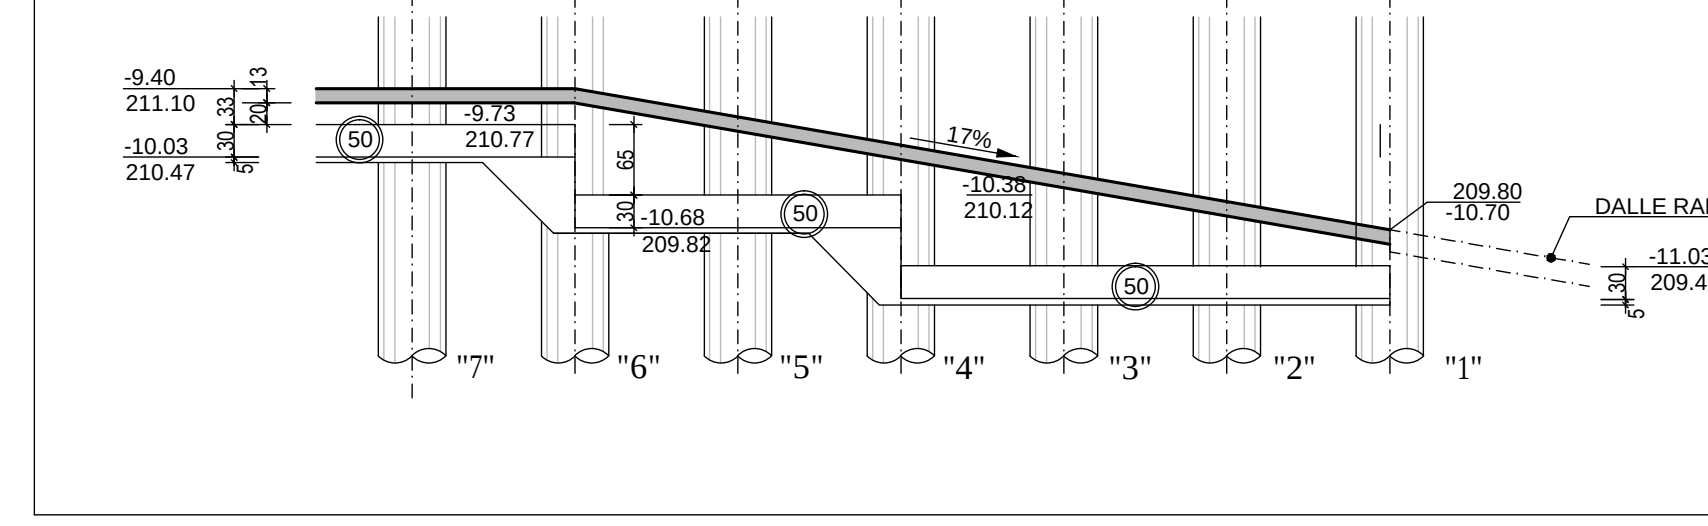
-9.40 211.10
-10.03 210.47
-9.73 210.77
-10.68 209.82
-10.38 210.12
17%
209.80 -10.70
-11.03 209.47
DALLE RAMPE
50
"7"
"6"
"5"
"4"
"3"
"2"
"1"

COUPE TYPE SEMELLES
Ech: 1/25

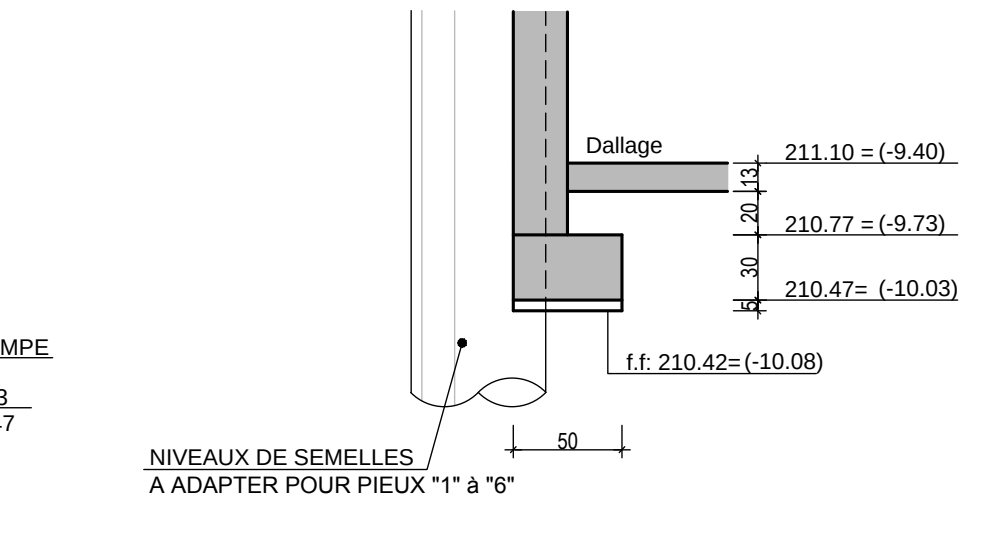
Dallage
211.10 = (-9.40)
210.77 = (-9.73)
210.47= (-10.03)
f.f: 210.42= (-10.08)
50
NIVEAUX DE SEMELLES A ADAPTER POUR PIEUX "1" à "6"

COUPE J
Ech: 1/25

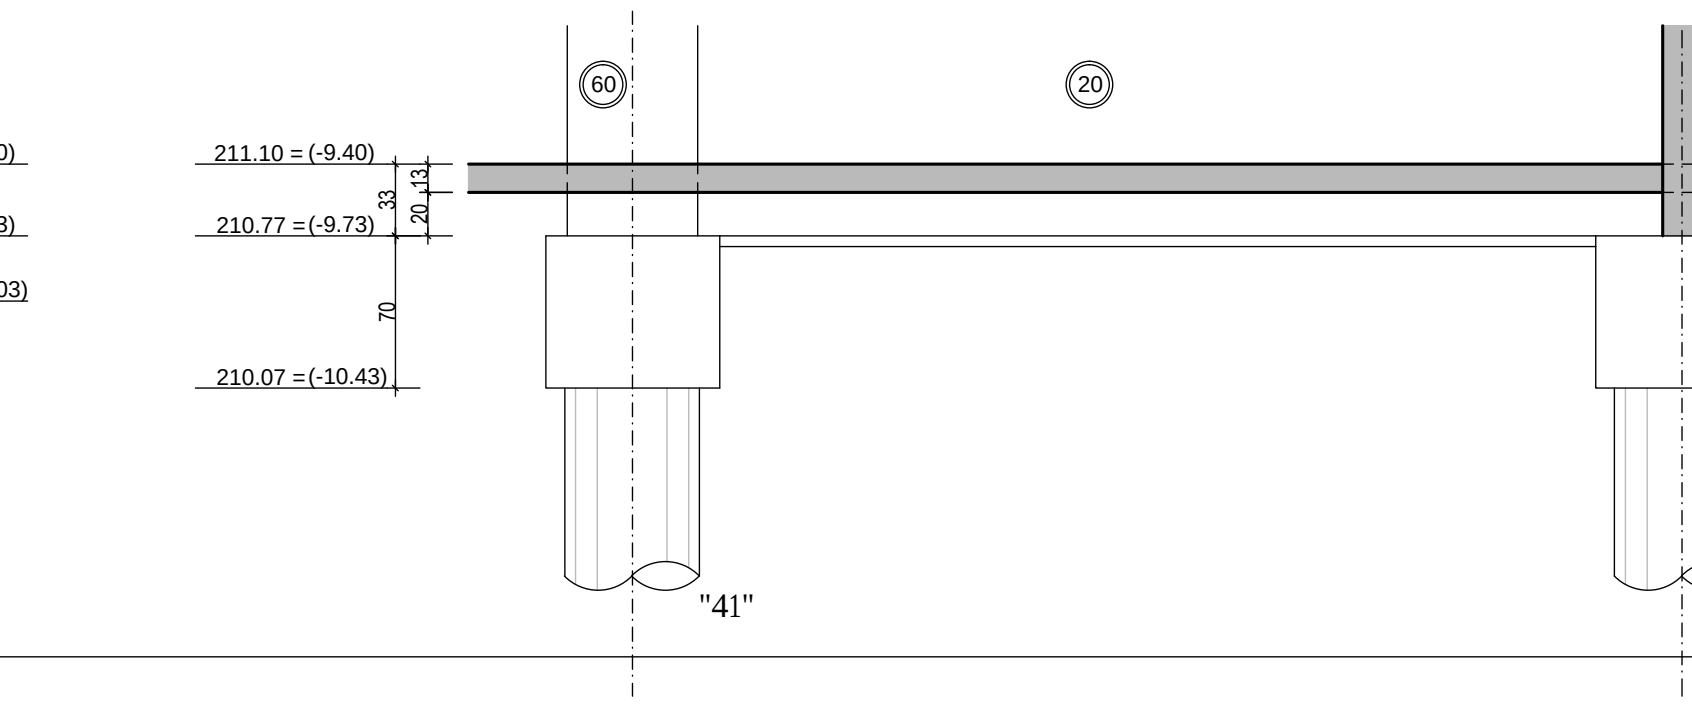
60
20
211.10 = (-9.40)
210.77 = (-9.73)
210.07 = (-10.43)
"41"
"43" "44"

COUPE PIEUX "22" à "25"
Ech: 1/25

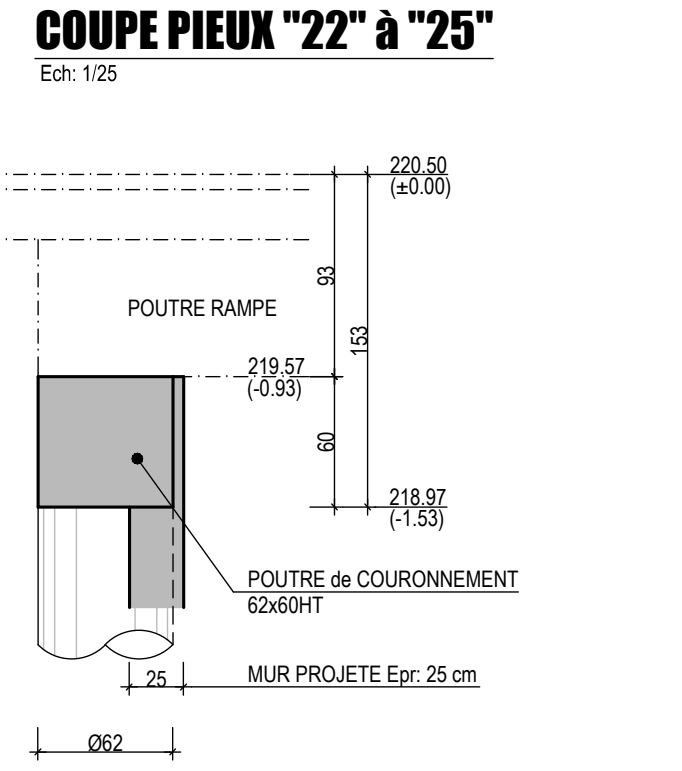
220.50 (±0.00)
POUTRE RAMPE
219.57 (-0.93)
218.97 (-1.53)
93
153
60
POUTRE de COURONNEMENT 62x60HT
MUR PROJETE Epr: 25 cm
25
Ø62

COUPE PIEUX "11" à "21"
Ech: 1/25

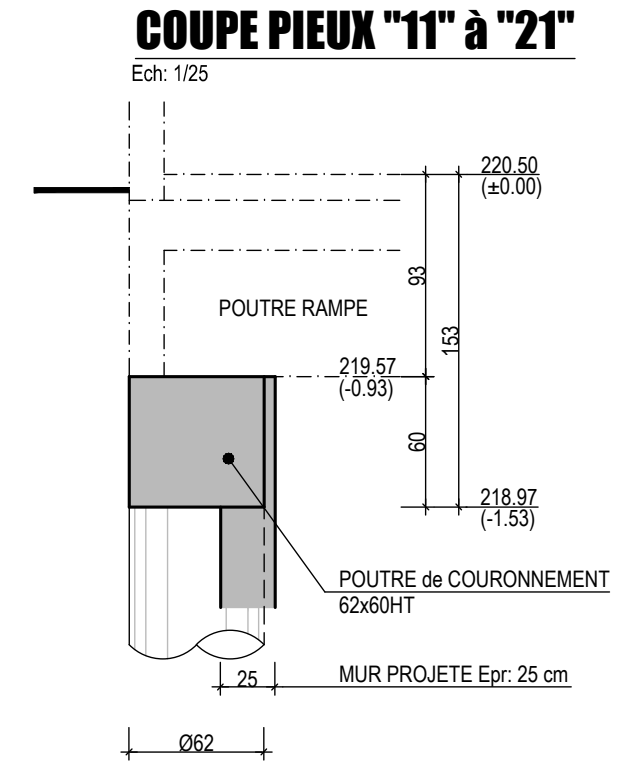
220.50 (±0.00)
POUTRE RAMPE
219.57 (-0.93)
218.97 (-1.53)
93
153
60
POUTRE de COURONNEMENT 62x60HT
MUR PROJETE Epr: 25 cm
25
Ø62

COUPE G
Ech: 1/50

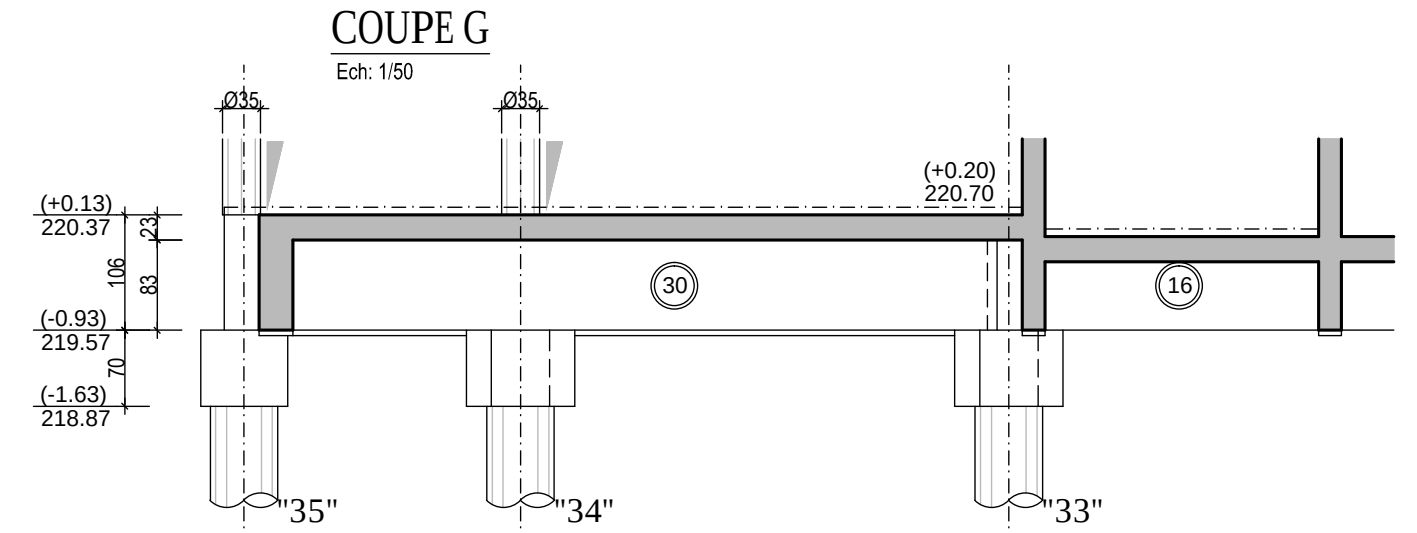
Ø35
(+0.13) 220.37
(-0.93) 219.57
(-1.63) 218.87
(+0.20) 220.70
(-0.07) 219.93
(-0.93) 219.07
30
16
"35"
"34"
"33"

COUPE F
Ech: 1/50

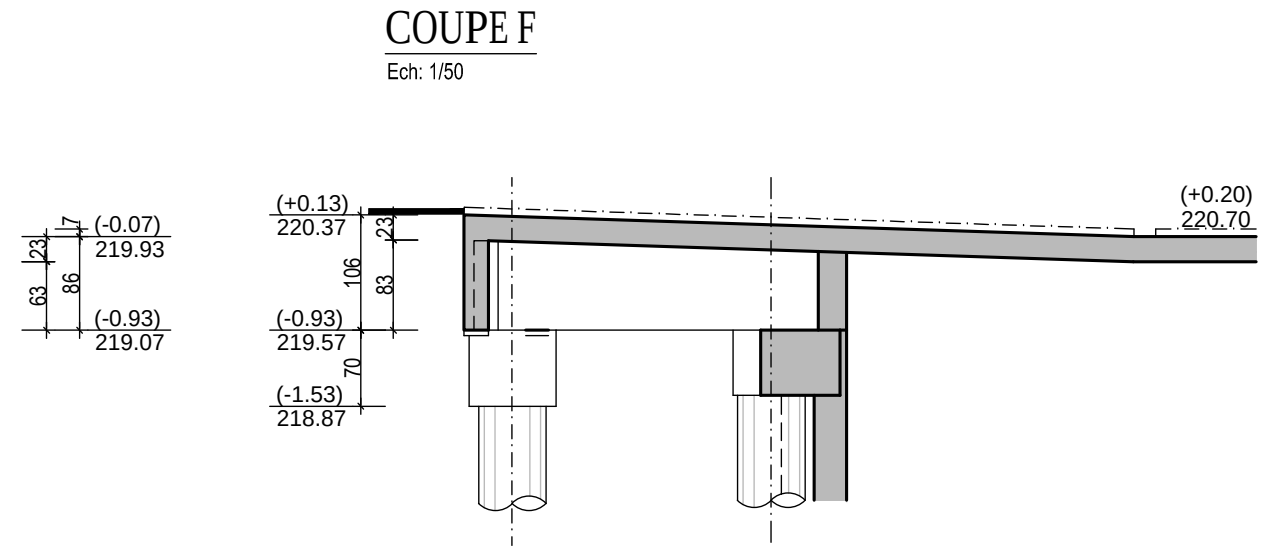
(+0.13) 220.37
(-0.93) 219.57
(-1.63) 218.87
(+0.20) 220.70
(-0.07) 219.93

NOAHO

LE 180°
Chemin de Fontanière - 69350 La Mulatière

Création de logements

Les entreprises réalisant les travaux devront tenir compte des derniers plans architecte lors de la réalisation des travaux
Les plans du be MATTE ne doivent servir qu'au corps d'état concerné et doivent être des plans d'exécution.

ARCHITECTE(S): ATELIER DE LA PASSERELLE
BET STRUCTURE: MATTE SAS
BET FLUIDES: PRELEM
ECONOMISTE: EXECO
BUREAU DE CONTROLE: Bureau VERITAS
MO DELEGUE:
MOE: PSO Ingénierie
CSPS: SUD EST COORDINATION
OPC:
ENTREPRISE(S): Fontanel

Bât:A
PIEUX RAMPE D'ACCES
Coffrage

DOE

Contrainte de sol: 8 bars ELS
Aciers HA (T) FeE500
Aciers Doux (Ø) FeE 235
Aciers TS FeE 500
Béton fc28 >= 25MPa
Enrobage = 3 cm

INDICE	DATE	MODIFICATIONS
A	03/06/2015	MISE A JOUR PIEUX, AJOUTE REPERAGE POUTRE de C

PLAN N°
A01 A
DATE : 11/05/2015

MATTÉ
BUREAU D'ÉTUDES
STRUCTURES ET FLUIDES
119 BOULEVARD STALINGRAD 69100 VILLEURBANNE
Tél. 04 72 44 02 87 Fax 04 72 44 26 59
E-mail : bet@matte.fr

Dessiné par : J.BO
Contrôlé par : P.LIN
Echelle : 1/50°

Affaire N°
13.12.118