COUPE 1

Ech: 1/50

1
2
3
4
5
6
7
8
9
10
11
12
13
14
15
16
17
18
19
620
550
610
579
18
579
279.6
546
534
280
615.3
148
603
596
424
600
510
TERRE
-7.56
212.94
-6.56
213.94
-8.86
211.64
-7.86
212.64
-10.19
210.31
-9.59
210.91
-11.57
208.93
-10.93
209.57
-12.71
207.79
-12.26
208.24
-14.20
206.30
-13.70
206.80
-15.07
205.43
-15.47
205.03
-14.38
206.12
R-3
-9.40
211.10
-10.03
210.47
-9.73
210.77
50
FER
210.37
-10.38
210.12
-10.68
209.82
-11.03
209.47
FER
209.13
-11.63
208.87
-12.03
208.47
-12.13
208.37
FER
207.63
-12.53
207.97
-12.63
208.87
-13.03
207.47
NIVEAUX RSO de SGC
NIVEAUX HAUTS des FERS
-12.40
208.10
Accès R-4
-12.40
208.10
17.1%
18%
"7"
"6"
"5"
"4"
"3"
"2"
"1"
VOIR PLAN N° A01
288.4
284.2
182
300
128
172
900
104
196
83.5
216.5
270.5
263.5
36.5
826.9
120
183
99
1460
1409.7
FER
206.92
-13.18
207.32
FER
206.87
-13.58
206.92
FER
206.43
-13.73
206.77
-15.03
206.37
-14.28
206.22
FER
205.21
-14.68
205.82
FER
205.00
-14.83
205.67
-15.23
205.37
FER
204.83
-15.38
205.12
FER
204.61
-15.78
204.72
-15.73
204.77
FER
204.09
-16.13
204.47
FER
203.82
Accès R-5
-15.47
205.03
-16.28
204.22
-15.78
203.82
FER
203.60
-16.83
203.67
FER
202.93
-16.43
203.42
-17.38
203.12
FER
202.97
-17.78
203.02
-17.93
202.57
-18.33
202.17
-18.48
202.02
-18.88
201.62
-18.80
201.70
-19.20
201.30
Accès R-6
-18.47
202.03
503.7
259.9
243.7
V.B
409
275
109
-18.47
202.03
-19.20
201.30
5
4
3
2

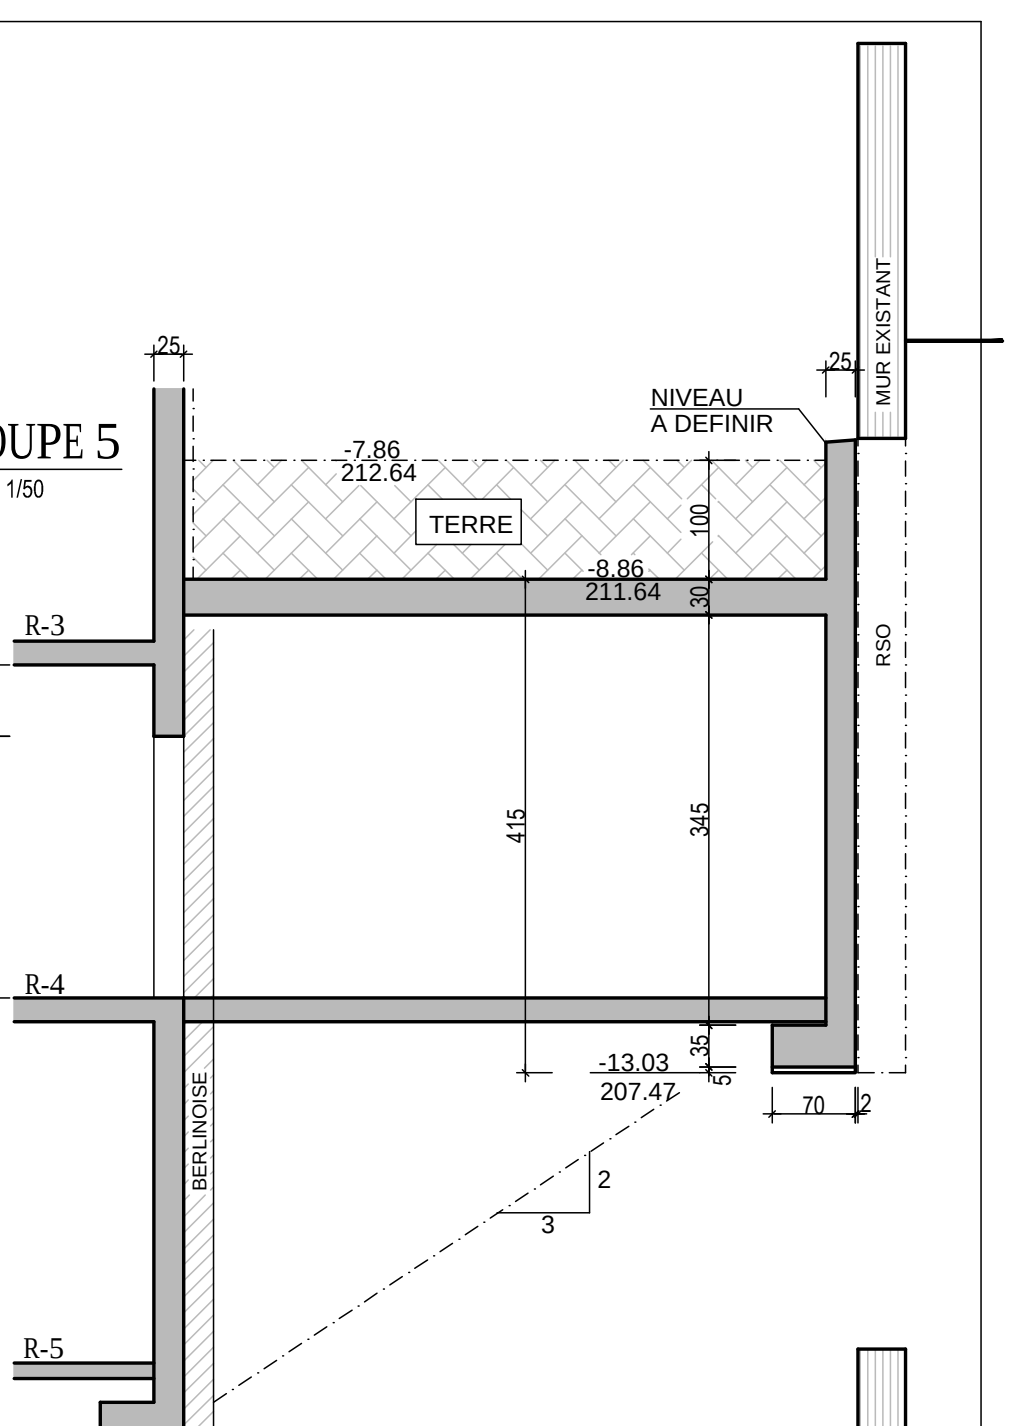

COUPE 5

Ech: 1/50

MUR EXISTANT
NIVEAU
A DEFINIR
-7.86
212.64
TERRE
-8.86
211.64
R-3
-9.40
205.10
R-4
-12.40
208.10
-13.03
207.47
R-5
-15.47
205.03
-16.18
204.32
BERLINOISE
RSO
415
345
300
280
220
60
307
287
70
25
3
2

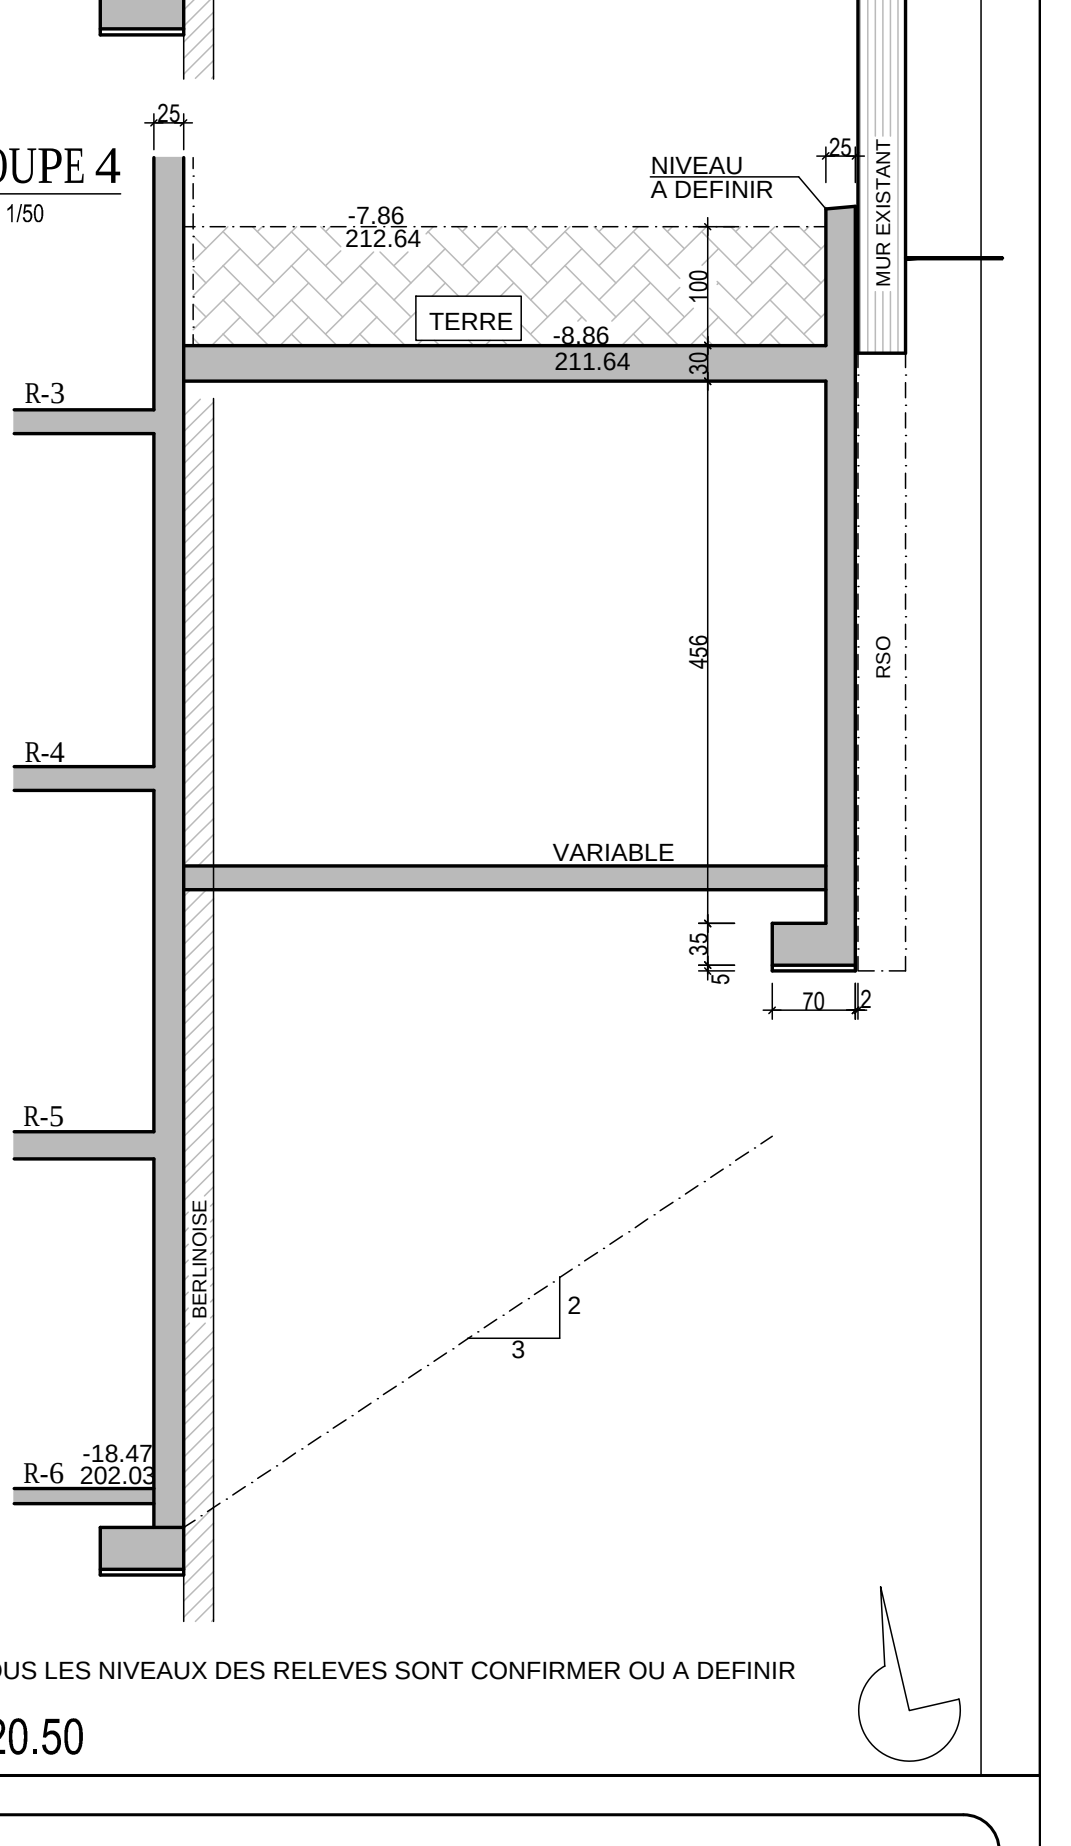

COUPE 4

Ech: 1/50

MUR EXISTANT
NIVEAU
A DEFINIR
-7.86
212.64
TERRE
-8.86
211.64
R-3
-9.40
205.10
R-4
-12.40
208.10
VARIABLE
R-5
-15.47
205.03
R-6
-18.47
202.03
BERLINOISE
RSO
456
300
280
307
287
277
73
70
25
3
2

VUE EN PLAN COUVERTURE

Ech: 1/50

MUR EXISTANT
"1"
"2"
"3"
"4"
"5"
"6"
"7"
"8"
"9"
"10"
"11"
"12"
"13"
Réserve: 7 cm
f: −3.20
f: 217.30
Dallage: 13 cm
b: 217.23
b: −3.27
TERRE Epr: 100 cm
−6.56
f: 213.94
Dalle: 30 cm
b: 212.94
−7.56
C.P: 1800Kg/m2
C.E: 150Kg/m2
TERRE Epr: 100 cm
−7.86
f: 212.64
Dalle: 30 cm
b: 211.64
−8.86
C.P: 1800Kg/m2
C.E: 150Kg/m2
TERRE Epr: 60 cm
−9.59
f: 210.91
Dalle: 25 cm
b: 210.31
−10.19
C.P: 1100Kg/m2
C.E: 150Kg/m2
TERRE Epr: 64 cm
−10.93
f: 209.57
Dalle: 25 cm
b: 208.93
−11.57
C.P: 1150Kg/m2
C.E: 150Kg/m2
BOIS sur plots: 30 cm
−12.41
f: 208.09
Dalle: 25 cm
b: 207.79
−12.71
C.P: 250Kg/m2
C.E: 150Kg/m2
TERRE Epr: 45 cm
−12.26
f: 208.24
Dalle: 25 cm
b: 207.79
−12.71
C.P: 800Kg/m2
C.E: 150Kg/m2
TERRE Epr: 50 cm
−13.70
f: 206.80
Dalle: 25 cm
b: 206.30
−14.20
C.P: 900Kg/m2
C.E: 150Kg/m2
TERRE Epr: 40 cm
f: −15.07
f: 205.43
Dalle: 25 cm
b: 205.03
−15.47
C.P: 750Kg/m2
C.E: 150Kg/m2
A
Accès R-4
-12.40
208.10
497
Accès R-5
-15.47
205.03
BERLINOISE
80x70HT
594
Accès R-6
-18.47
202.03
80x75HT
715
Bât: A
Bât: B
VB R−6
0.5m2
50*70
1
5
4
3
2

VUE EN PLAN FONDATIONS

Ech: 1/50

MUR EXISTANT
REDAN
"1"
"2"
"3"
"4"
"5"
"6"
"7"
"8"
"9"
"10"
"11"
"12"
"13"
"42"
f: −9.40
f: 211.10
Dallage: 13 cm
b: 211.10
b: −9.40
f.f: -10.73
209.77
f.f: -11.08
209.42
-9.40
211.10
-10.70
209.80
f.f: -12.03
208.47
f.f: -12.53
207.97
f.f: -13.03
207.47
1754 x 17.1%=300
1667
-12.40
208.10
f: −12.40
f: 208.10
Dallage: 20 cm
b: 208.10
b: −12.40
579
517
60
70.1
f.f: -13.58
206.92
f.f: -15.03
206.37
f.f: -14.68
205.82
f.f: -15.23
205.37
f.f: -15.78
204.72
f.f: -16.13
204.47
1706 x 18%=307
1706
f: −15.47
f: 205.03
Dallage: 20 cm
b: 205.03
b: −15.47
621
607
f.f: -19.20
201.30
BERLINOISE
Accès R-5
-15.47
205.03
594
f.f: -15.78
203.82
f.f: -16.43
203.42
f.f: -17.78
203.02
f.f: -18.33
202.17
f.f: -18.88
201.62
f.f: -19.20
201.30
1667 x 18%=300
1667
f: −18.47
f: 202.03
Dallage: 20 cm
b: 202.03
b: −15.47
1220
Accès R-4
-12.40
208.10
497
Accès R-6
-18.47
202.03
715
Bât: A
Bât: B
182
300
128
172
900
104
196
83.5
216.5
270.5
263.5
36.5
826.9
148
120
183
99
1460
1409.7
321
VB R−6
0.5m2
50*70
1
5
4
3
2

NOTA TOUS LES NIVEAUX DES RELEVES SONT CONFIRMER OU A DEFINIR

±0.00 = 220.50

NOAHO

LE 180°
Chemin de Fontanière - 69350 La Mulatière

Création de logements

Les entreprises réalisant les travaux devront tenir compte des derniers plans architecte lors de la réalisation des travaux
Les plans du be MATTE ne doivent servir qu'au corps d'état concerné et doivent être des plans d'exécution.

ARCHITECTE(S):	ATELIER DE LA PASSERELLE	MO DELEGUE:	
BET STRUCTURE:	MATTE SAS	MOE:	PSO Ingénierie
BET FLUIDES:	PRELEM	CSPS:	SUD EST COORDINATION
ECONOMISTE:	EXECO	OPC:	
BUREAU DE CONTROLE:	Bureau VERITAS	ENTREPRISE(S):	Fontanel

Bât:A et B
RAMPE D'ACCES NORD
Coffrage

DOE

Contrainte de sol: 8 bars ELS

Aciers HA (T) FeE500
Aciers Doux (Ø) FeE 235
Aciers TS FeE 500
Béton fc28 >= 25MPa
Enrobage = 3 cm

INDICE	DATE	MODIFICATIONS
A	14/04/2016	AJOUTE CHARGES

PLAN N°
A02 A
DATE : 17/05/2015

MATTÉ
BUREAU D'ÉTUDES
STRUCTURES ET FLUIDES
119 BOULEVARD STALINGRAD 69100 VILLEURBANNE
Tél. 04 72 44 02 87 Fax 04 72 44 26 59
E-mail : bet@matte.fr

Dessiné par : J.BO
Contrôlé par : P.LIN
Echelle : 1/50°

Affaire N°
13.12.118