

NOHAO

Chemin de Fontanière-69350 La Mulatière
Création de logements

Les entreprises réalisant les travaux devront tenir compte des derniers plans architecte lors de la réalisation des travaux
Les plans du be MATTE ne doivent servir qu'au corps d'état concerné et doivent être des plans d'exécution.

ARCHITECTE(S):	Atelier DE LA PASSERELLE	M.O. Délégué:	.
BET STRUCTURE:	BET MATTE	M.O.:	.
BET FLUIDES:	PRELEM	CSPS:	PSO ingénierie
ECONOMISTE:	EXECO	M.O.E.:	SUD EST COORDINATION
BUREAU DE CONTROLE:	VERITAS	ENTREPRISE(S):	Fontanel-pbc

Bât: A
POUTRE DE COURONNEMENT
ARMATURES

INDICE	DATE	MODIFICATIONS

Aciers HA (T) FeE500
Aciers Doux (Ø) FeE 235
Aciers TS FeE 500
Béton fc28 >= 25MPa
Enrobage = 3 cm

PLAN N°
A03 0

DATE : 30-11-2015

MATTÉ

BUREAU D'ÉTUDES
STRUCTURES ET FLUIDES


119 BOULEVARD STALINGRAD 69100 VILLEURBANNE
Tél. 04 72 44 02 87 Fax 04 72 44 26 59
E-mail : bet@matte.fr

Dessiné par : J.BONDETTI
Contrôlé par : P. LIN
Ech :

Affaire N°
S.13.12.118


VUE EN PLAN

Ech: 1/25

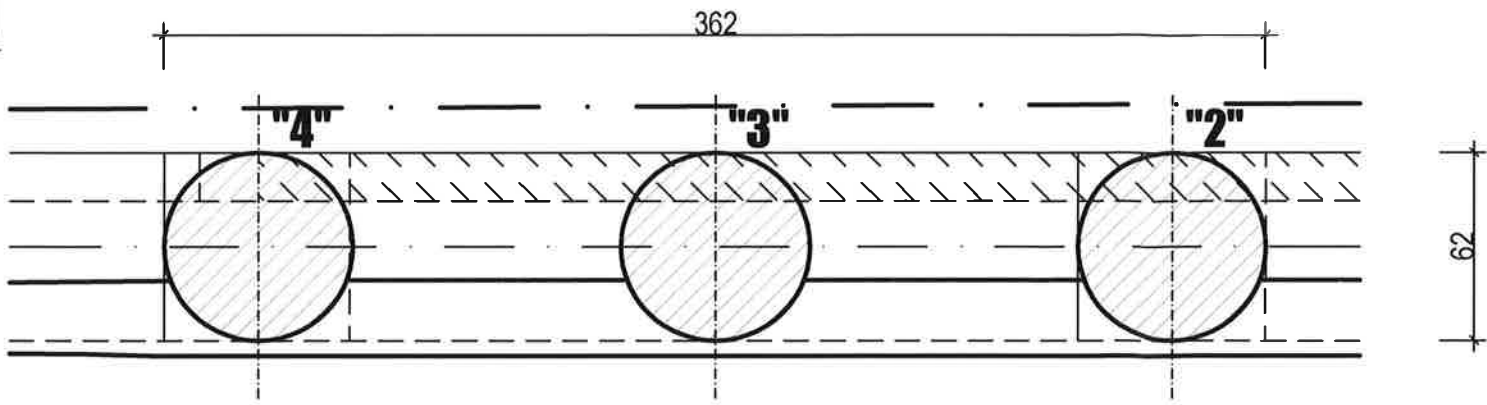


VUE de DESSUS

Ech: 1/25

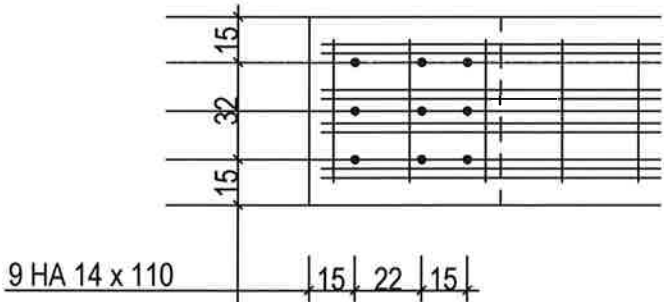


ELEVATION

Ech: 1/25

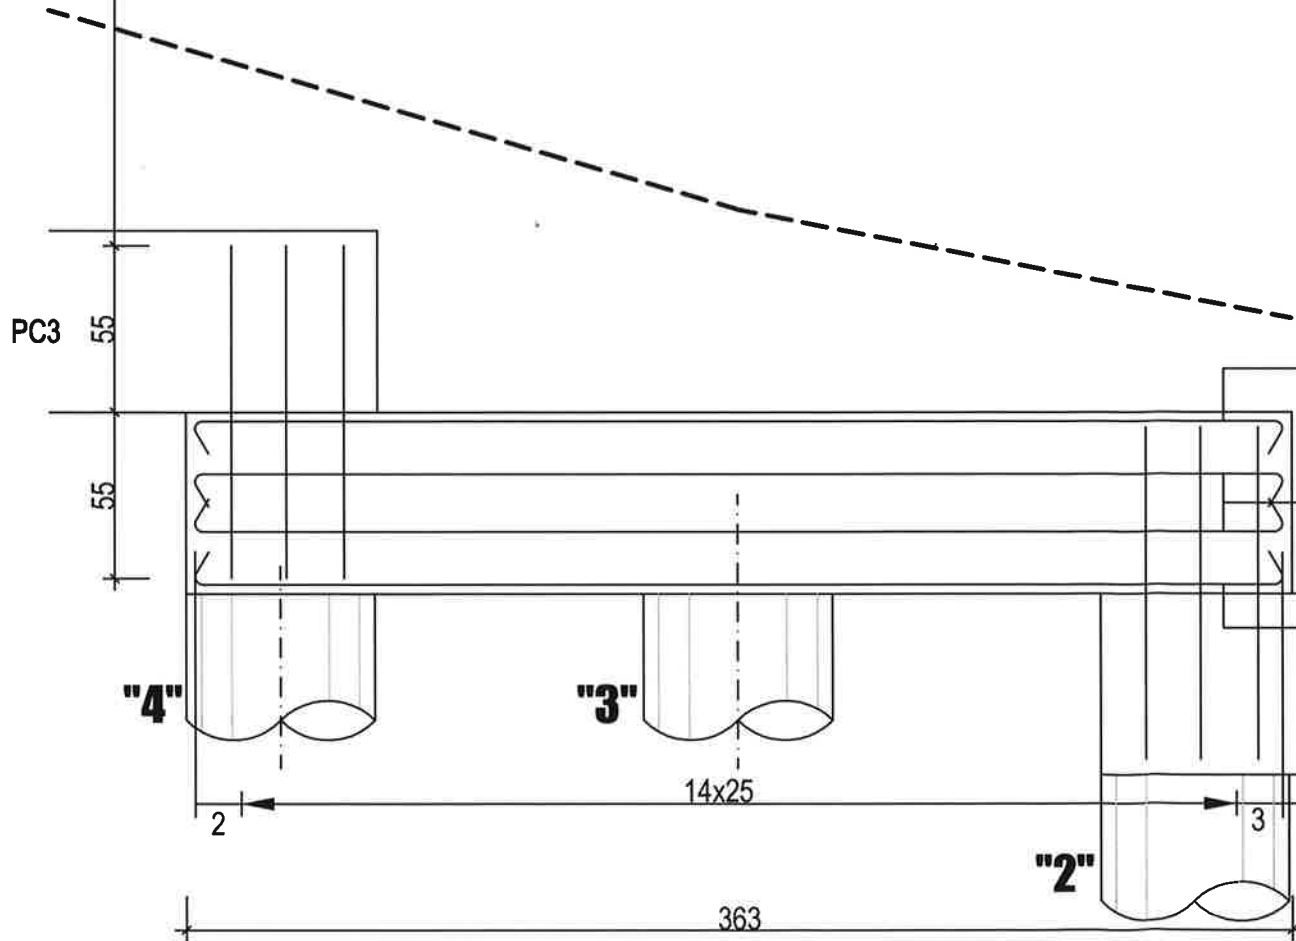

COUPE

Ech: 1/25

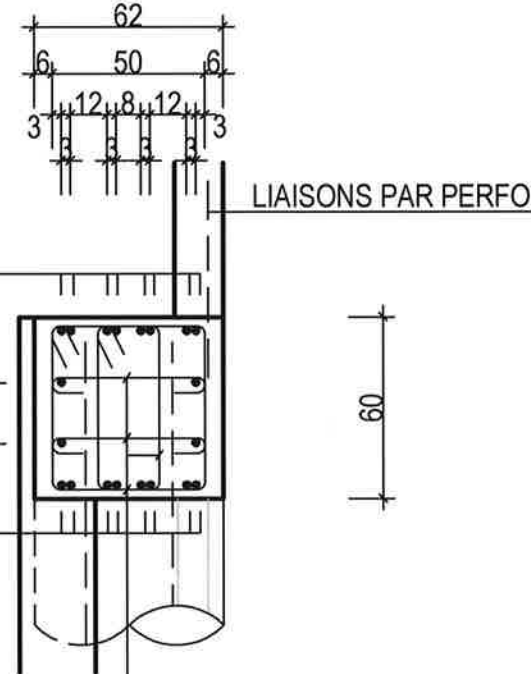


PC2

1 Pièce


VUE EN PLAN

Ech: 1/25

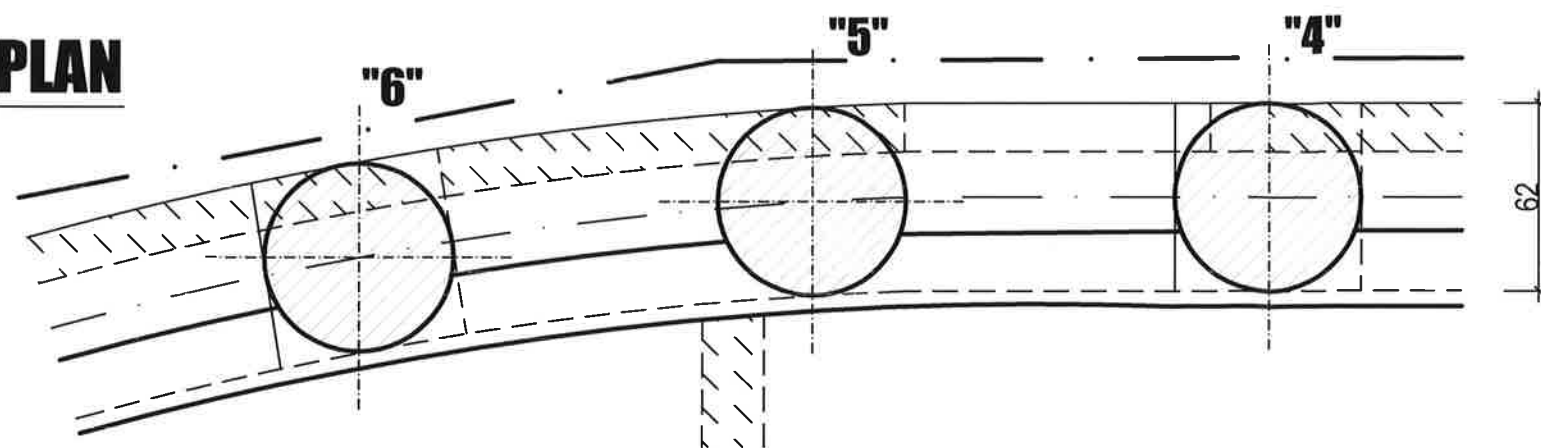

VUE de DESSUS

Ech: 1/25

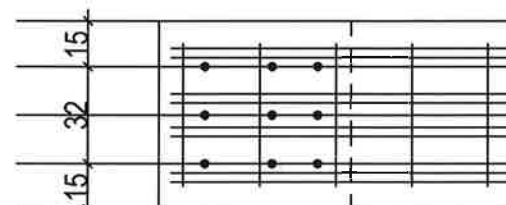

ELEVATION

Ech: 1/25

9 HA 14 x 110

15 22 15

PC4

55

55

"6"

"5"

"4"

14x25

3

3

363

2 HA 16 x 25

350

25

R: 1192

2 HA 16 x 25

352

25

R: 1197

2 HA 16 x 25

354

25

R: 1208

2 HA 16 x 25

356

25

R: 1223

2 HA 12 x 20

350

20

R: 1192

2 HA 14 x 25

356

25

R: 1223

2 HA 14 x 25

354

25

R: 1208

2 HA 14 x 25

352

25

R: 1197

2 HA 14 x 25

350

25

R: 1192

15 Cad HA 10 x

50

54

15 Cad HA 10 x

20

54

2x15 Ep HA 10 x

50

LIAISONS PAR PERFO

2 HA 12 x 20

356

20

R: 1223

NOTA


CADRES RAYONNANTS
ESPACEMENTS BARRES EXT.

PC3

1 Pièce

COUPE

Ech: 1/25

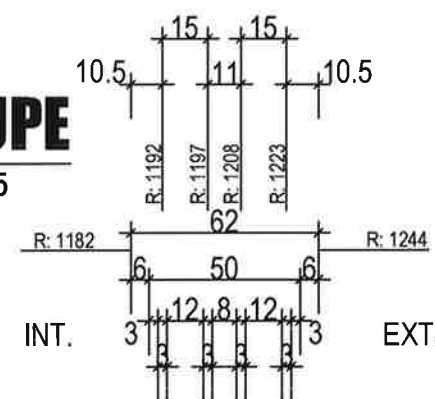

Ech: 1/25

Ech: 1/25

Ech: 1/25

Ech: 1/25


Ech: 1/25

Ech: 1/25




VUE EN PLAN

Ech: 1/25

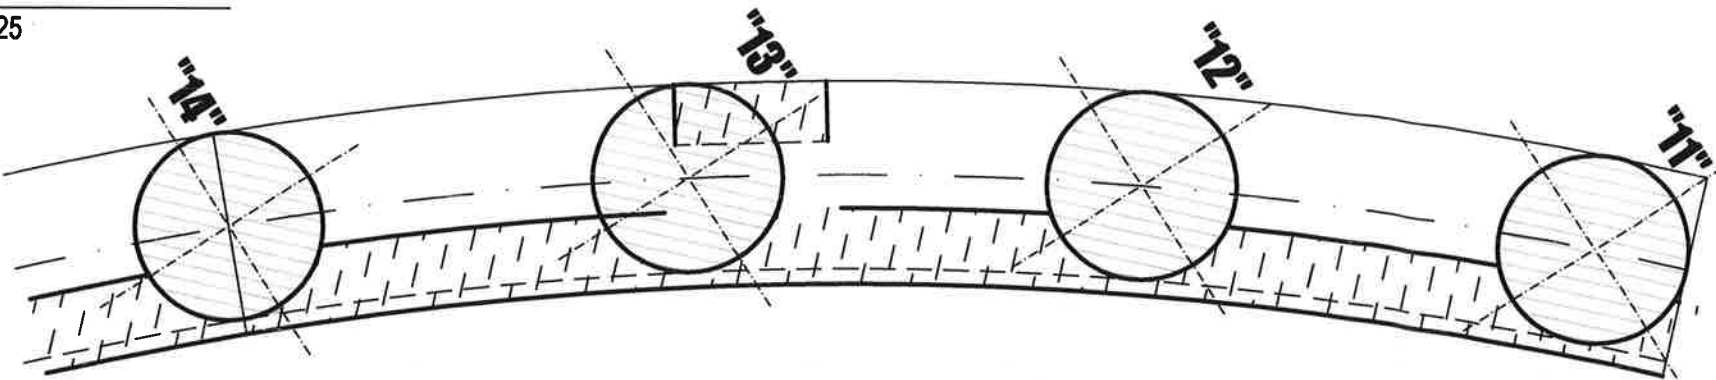


COUPE

Ech: 1/25

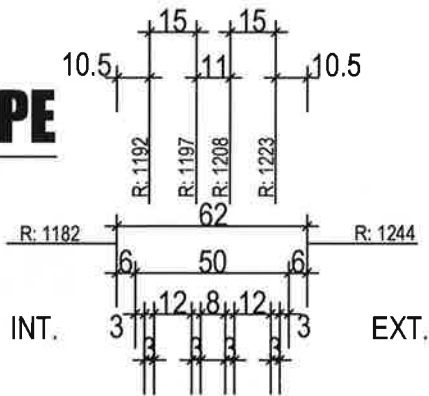

ELEVATION

Ech: 1/25

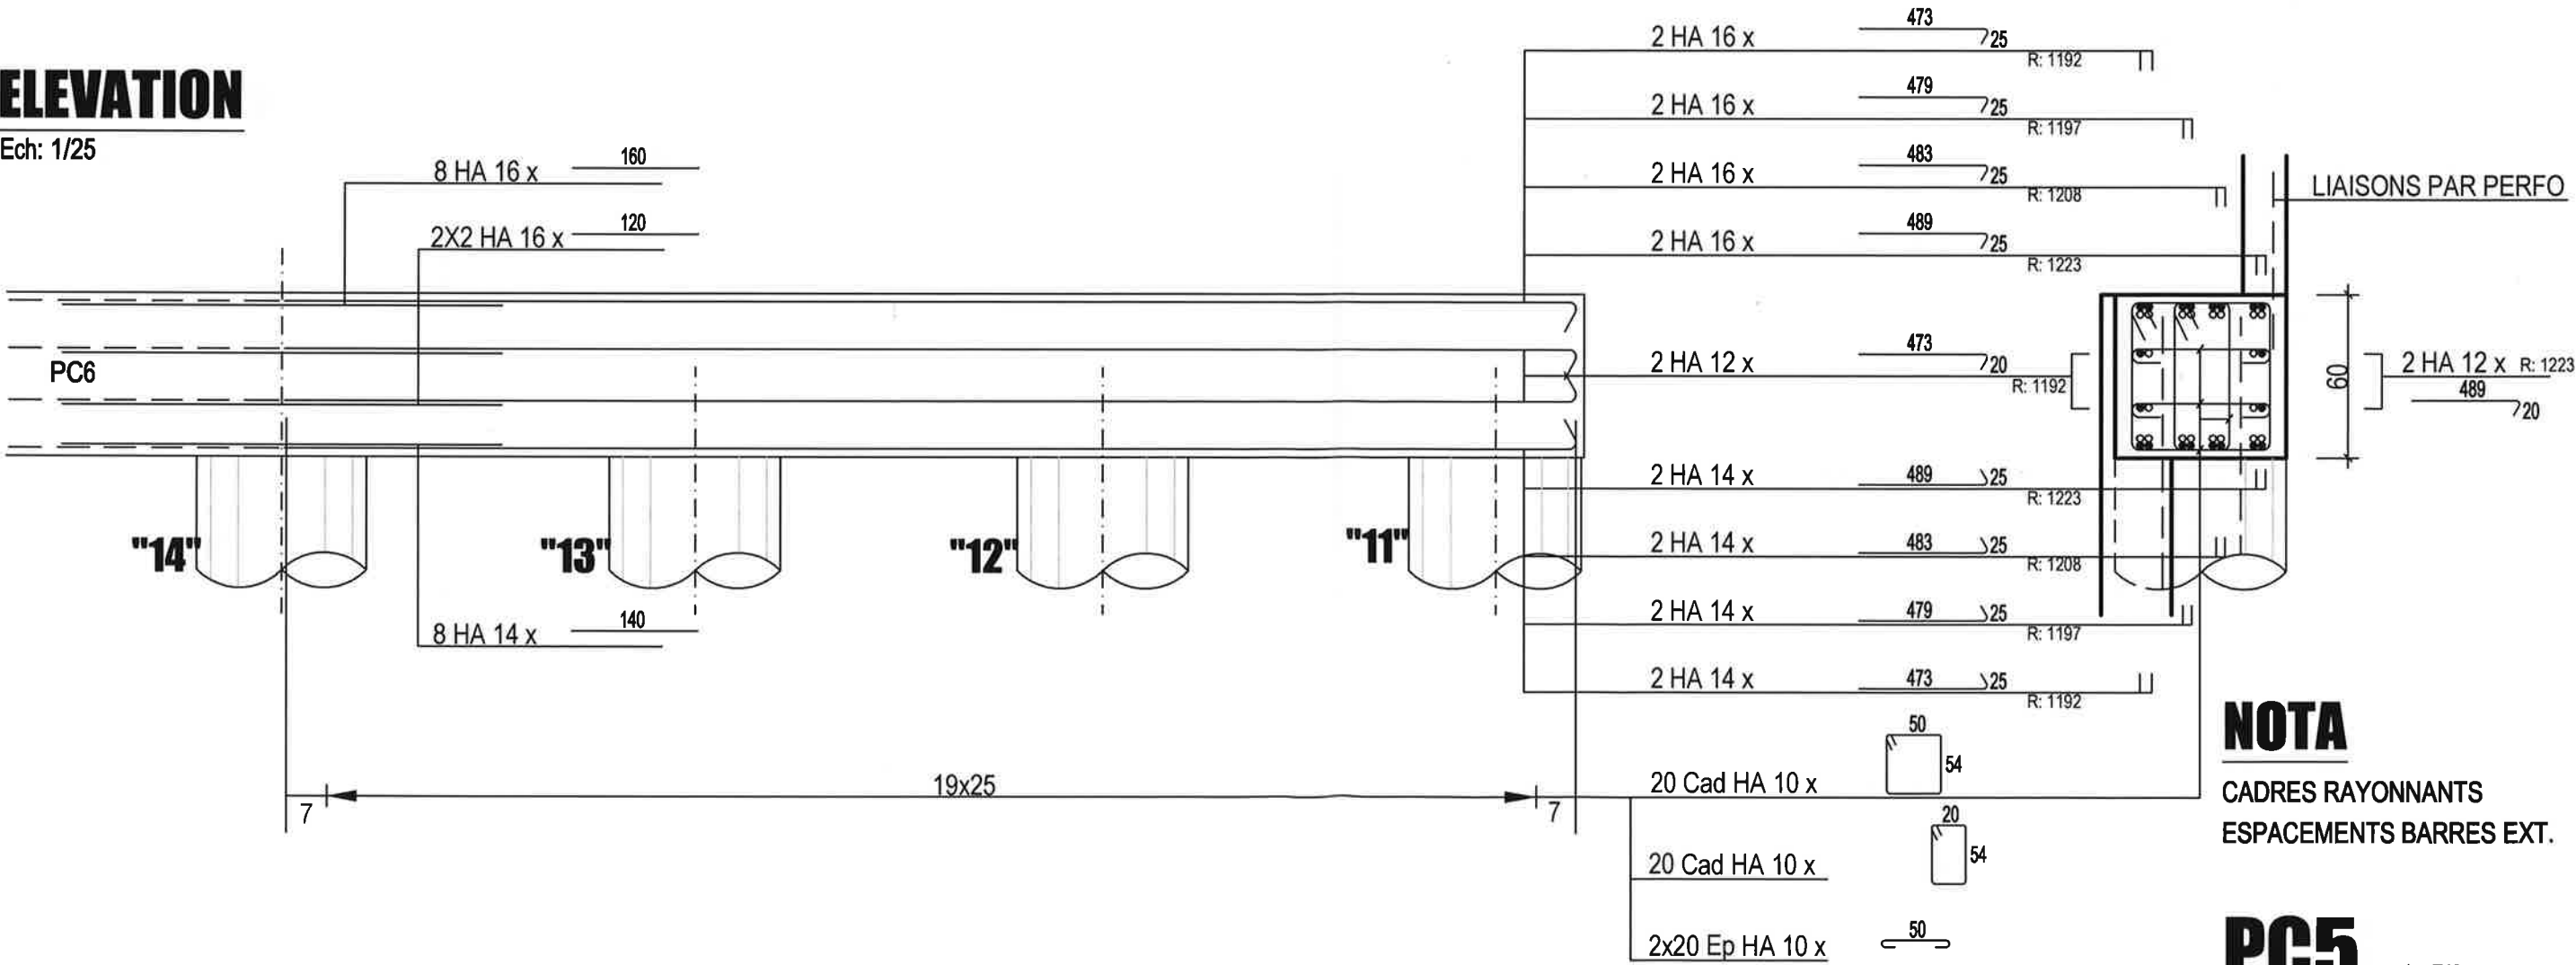

NOTA


CADRES RAYONNANTS
ESPACEMENTS BARRES EXT.

PC5



1 Pièce

Ech: 1/25

Ech: 1/25

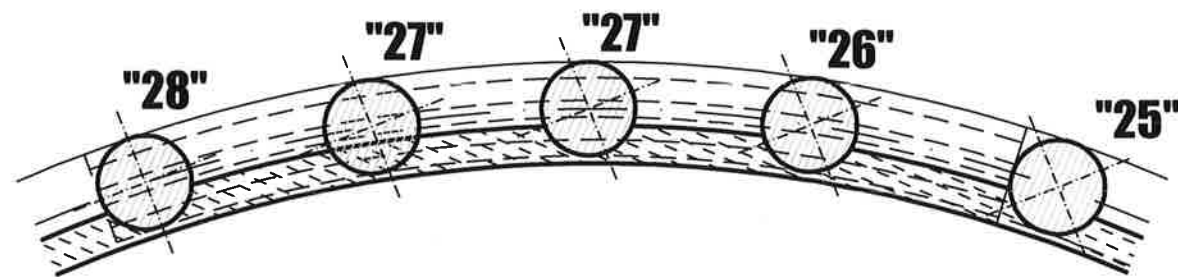

Ech: 1/25

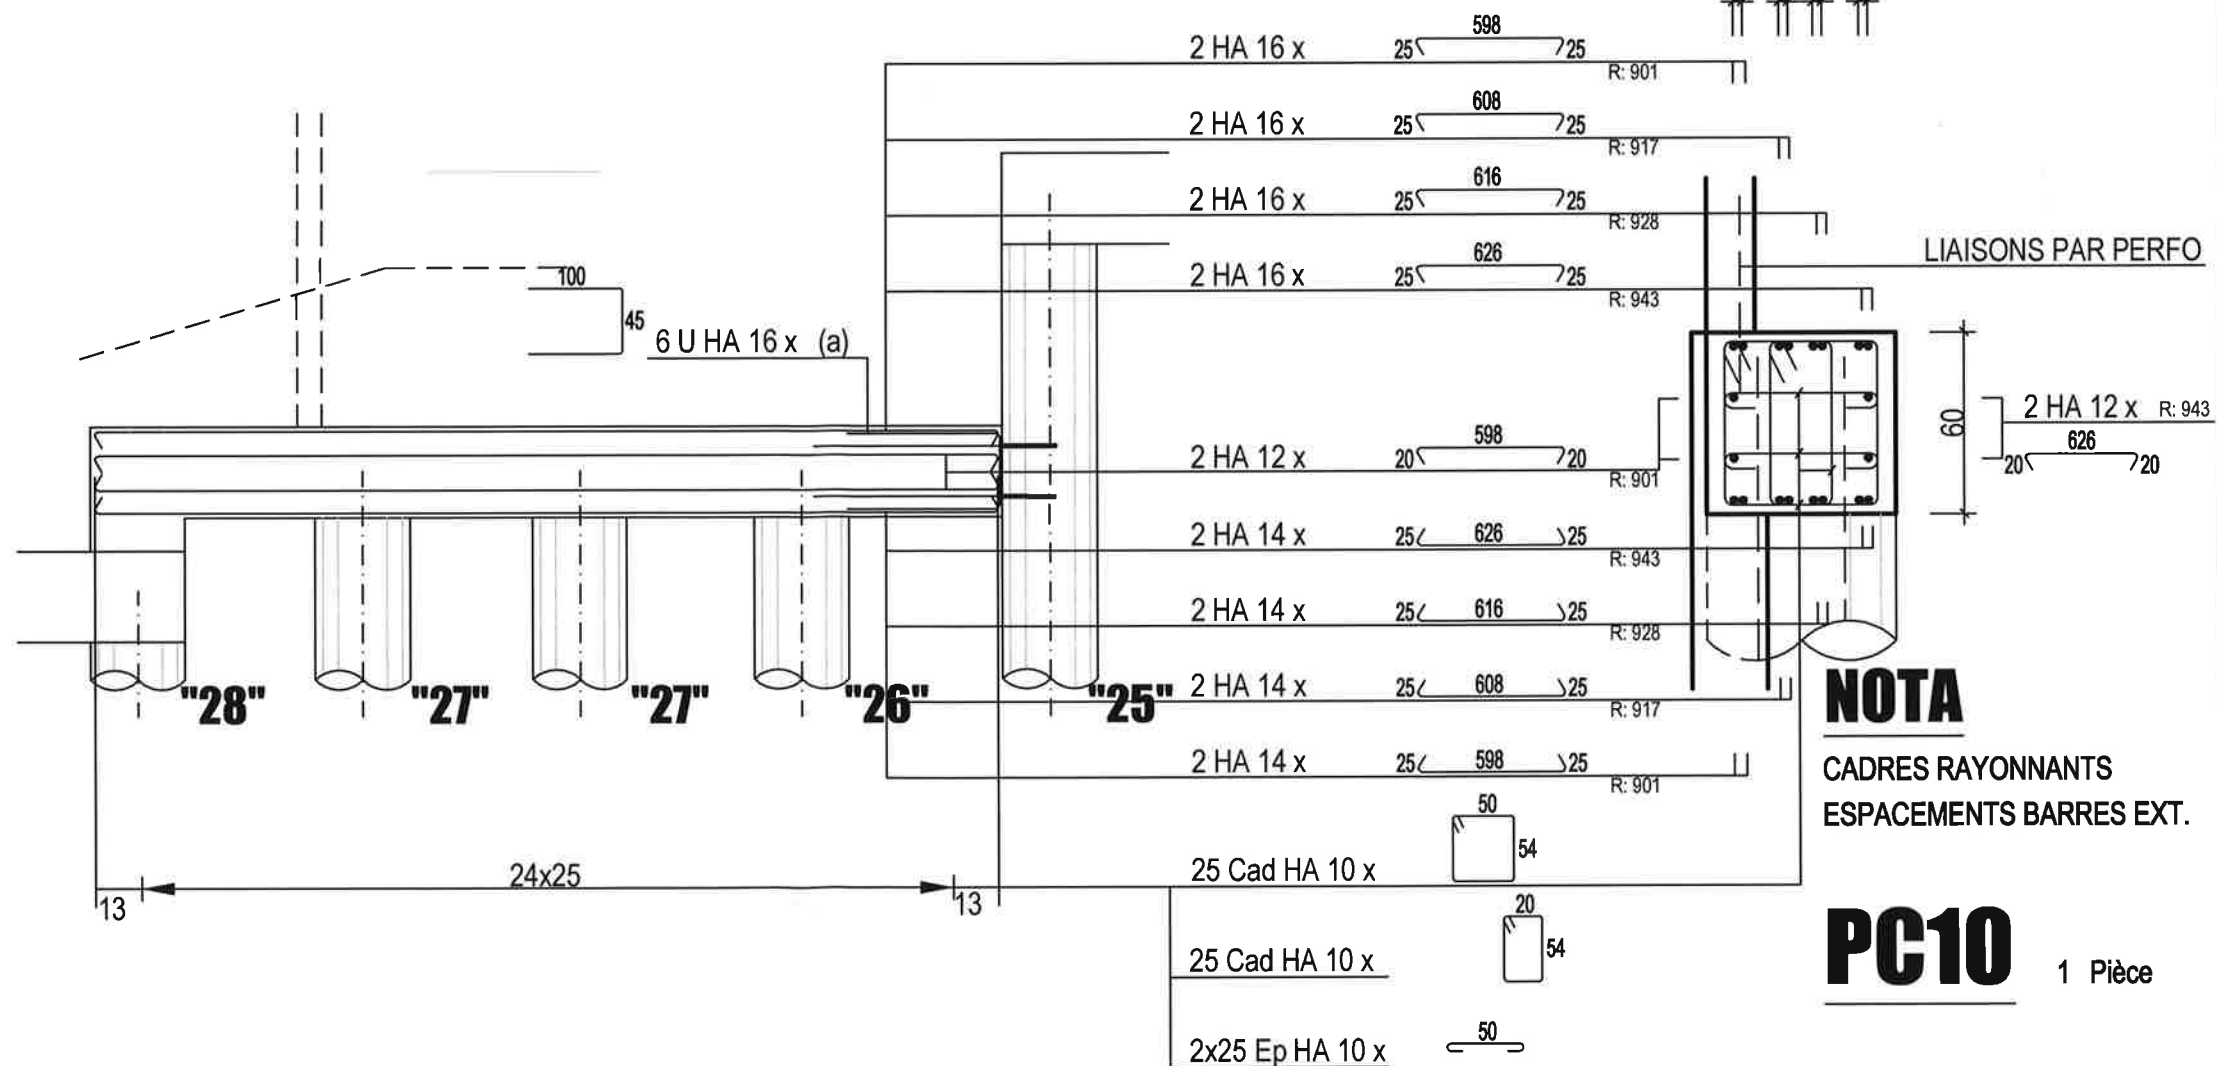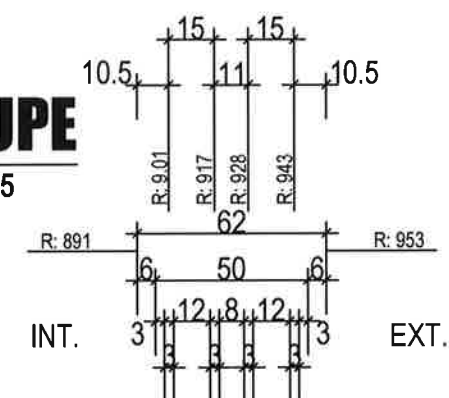

CADRES RAYONNANTS
ESPACEMENTS BARRES EXT.

PC10

1 Pièce