

NOAHO
LE 180°
Chemin de Fontanière - 69350 La Mulatière
Création de logements

Les entreprises réalisant les travaux devront tenir compte des derniers plans architecte lors de la réalisation des travaux
Les plans du be MATTE ne doivent servir qu'au corps d'état concerné et doivent être des plans d'exécution.

ARCHITECTE(S): ATELIER DE LA PASSERELLE MO DELEGUE:
BET STRUCTURE: MATTE SAS MOE: PSO Ingénierie
BET FLUIDES: PRELEM CSPS: SUD EST COORDINATION
ECONOMISTE: EXECO OPC:
BUREAU DE CONTROLE: Bureau VERITAS ENTREPRISE(S): Fontanel

Bât:A
LOCAL TRANSFO
Coffrage

DOE

Contrainte de sol: 8 bars ELS

INDICE	DATE	MODIFICATIONS
A	09-09-2015	MISE A JOUR SUIVANT REMARQUES ERDF
B	27/01/2016	MISE A JOUR NIVEAU DALLE EXTERIEURE, AJOUTE AMC
C	09/02/2016	MISE A JOUR SUIVANT C
D	11/02/2016	MISE A JOUR FEUILLURES B.T et TRANSFO

Aciers HA (T) FeE500
Aciers Doux (Ø) FeE 235
Aciers TS FeE 500
Béton fc28 >= 25MPa
Enrobage = 3 cm

PLAN N°
A04 D
DATE : 07/07/2015

MATTÉ
BUREAU D'ÉTUDES
STRUCTURES ET FLUIDES

119 BOULEVARD STALINGRAD 69100 VILLEURBANNE
Tél. 04 72 44 02 87 Fax 04 72 44 26 59
E-mail : bet@matte.fr


Dessiné par : J.BO
Contrôlé par : P.LIN
Echelle : 1/50°

Affaire N°
13.12.118

VUE EN PLAN

Ech: 1/50

4 FOI''

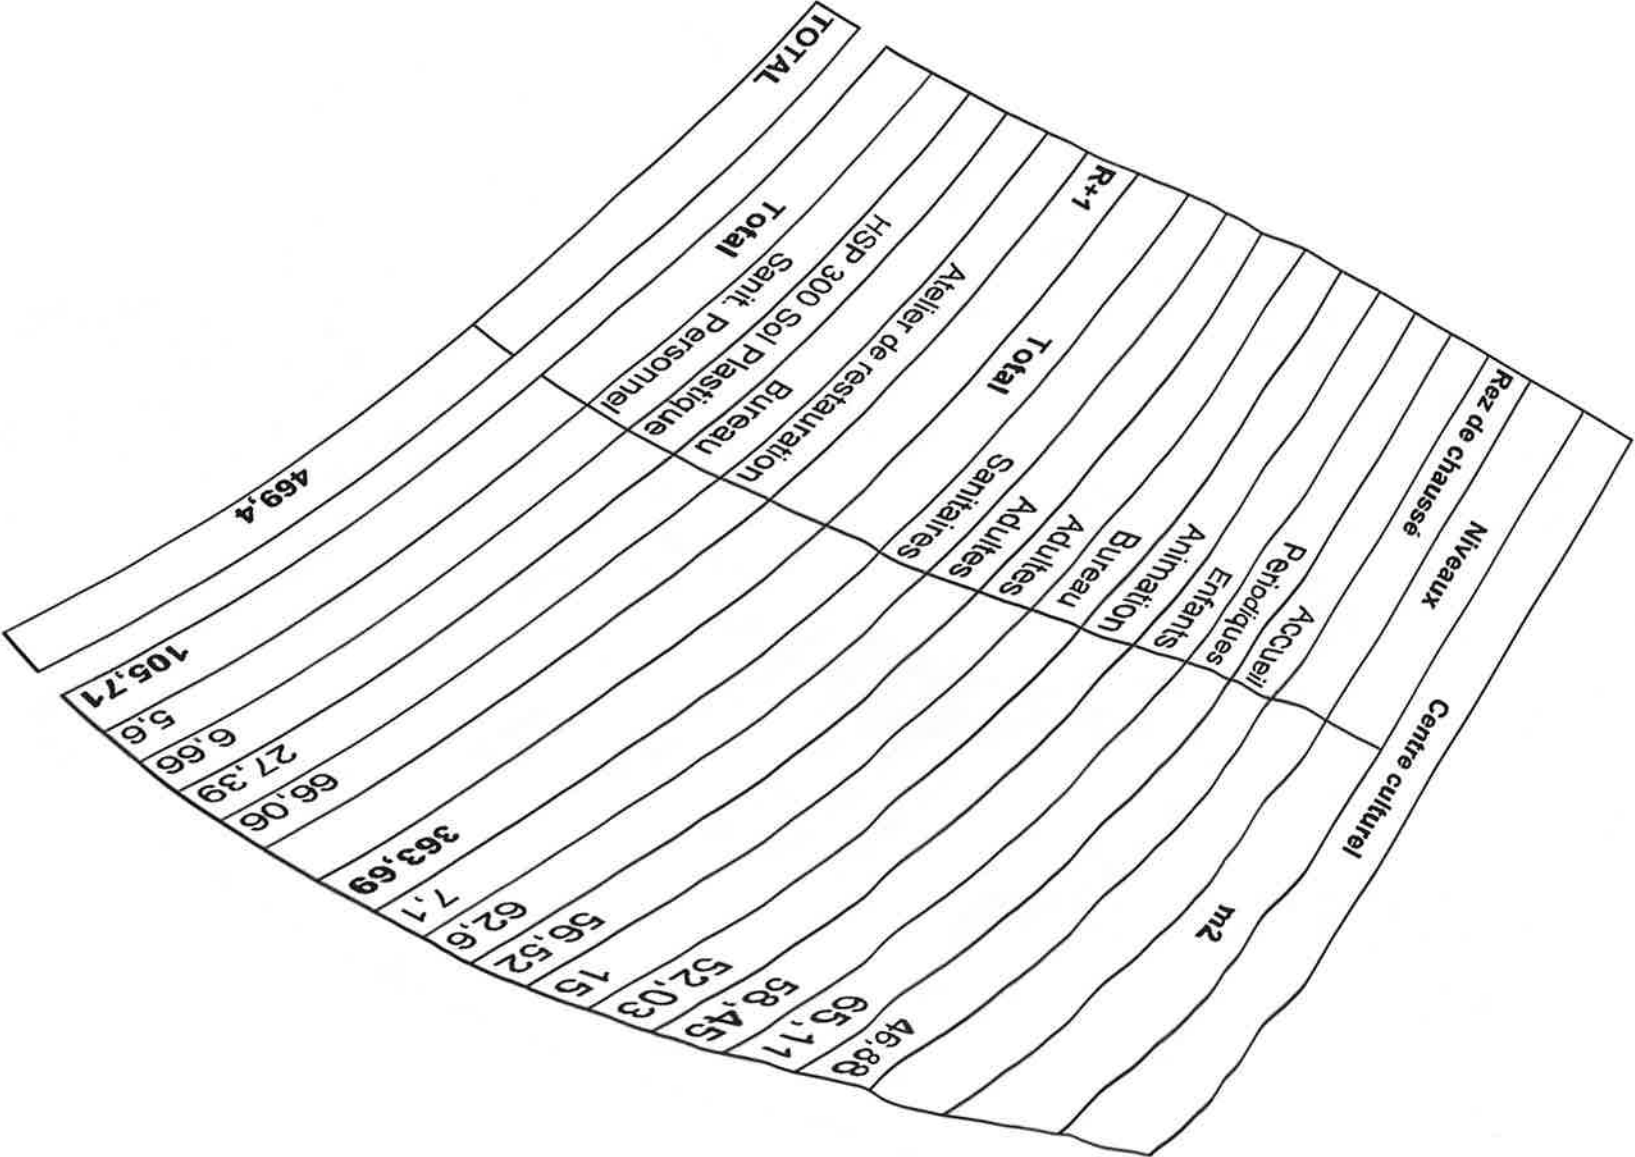

AFF: S.13.12.118	Bât: A	LA MULATIERE-69350 LaMulatiere CREATION de LOGEMENTS	TRANSFO Coffrage	Plan n° A 04	Page: 7
------------------	--------	---	------------------	--------------	---------