

NOAHO

Armatures

Chemin de Fontanière - 69350 La Mulatière

Création de logements

Les entreprises réalisant les travaux devront tenir compte des derniers plans architecte lors de la réalisation des travaux
Les plans du be MATTE ne doivent servir qu'au corps d'état concerné et doivent être des plans d'exécution.

ARCHITECTE(S):	ATELIER DE LA PASSERELLE	MO DELEGUE:	
BET STRUCTURE:	MATTE SAS	MOE:	PSO Ingénierie
BET FLUIDES:	PRELEM	CSPS:	SUD EST COORDINATION
ECONOMISTE:	EXECO	OPC:	
BUREAU DE CONTROLE:	Bureau VERITAS	ENTREPRISE(S):	Fontanel

Bât:A

FONDATIONS au-3 et du SILO

Armatures

INDICE	DATE	MODIFICATIONS

MATTÉ
BUREAU D'ÉTUDES
STRUCTURES ET FLUIDES
119 BOULEVARD STALINGRAD 69100 VILLEURBANNE
Tél. 04 72 44 02 87 Fax 04 72 44 26 59
E-mail : bet@matte.fr

Dessiné par : J.BO
Contrôlé par : P.LIN
Echelle : 1/50°

DOE


Contrainte de sol: 8 bars ELS

Aciers HA (T) FeE500
Aciers Doux (Ø) FeE 235
Aciers TS FeE 500
Béton fc28 >= 25MPa
Enrobage = 3 cm


PLAN N°
A08 0

DATE : 11/09/2015


Affaire N°
13.12.118

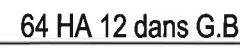
[illegible]

SCELLEMENT DANS "ANCROBOX"


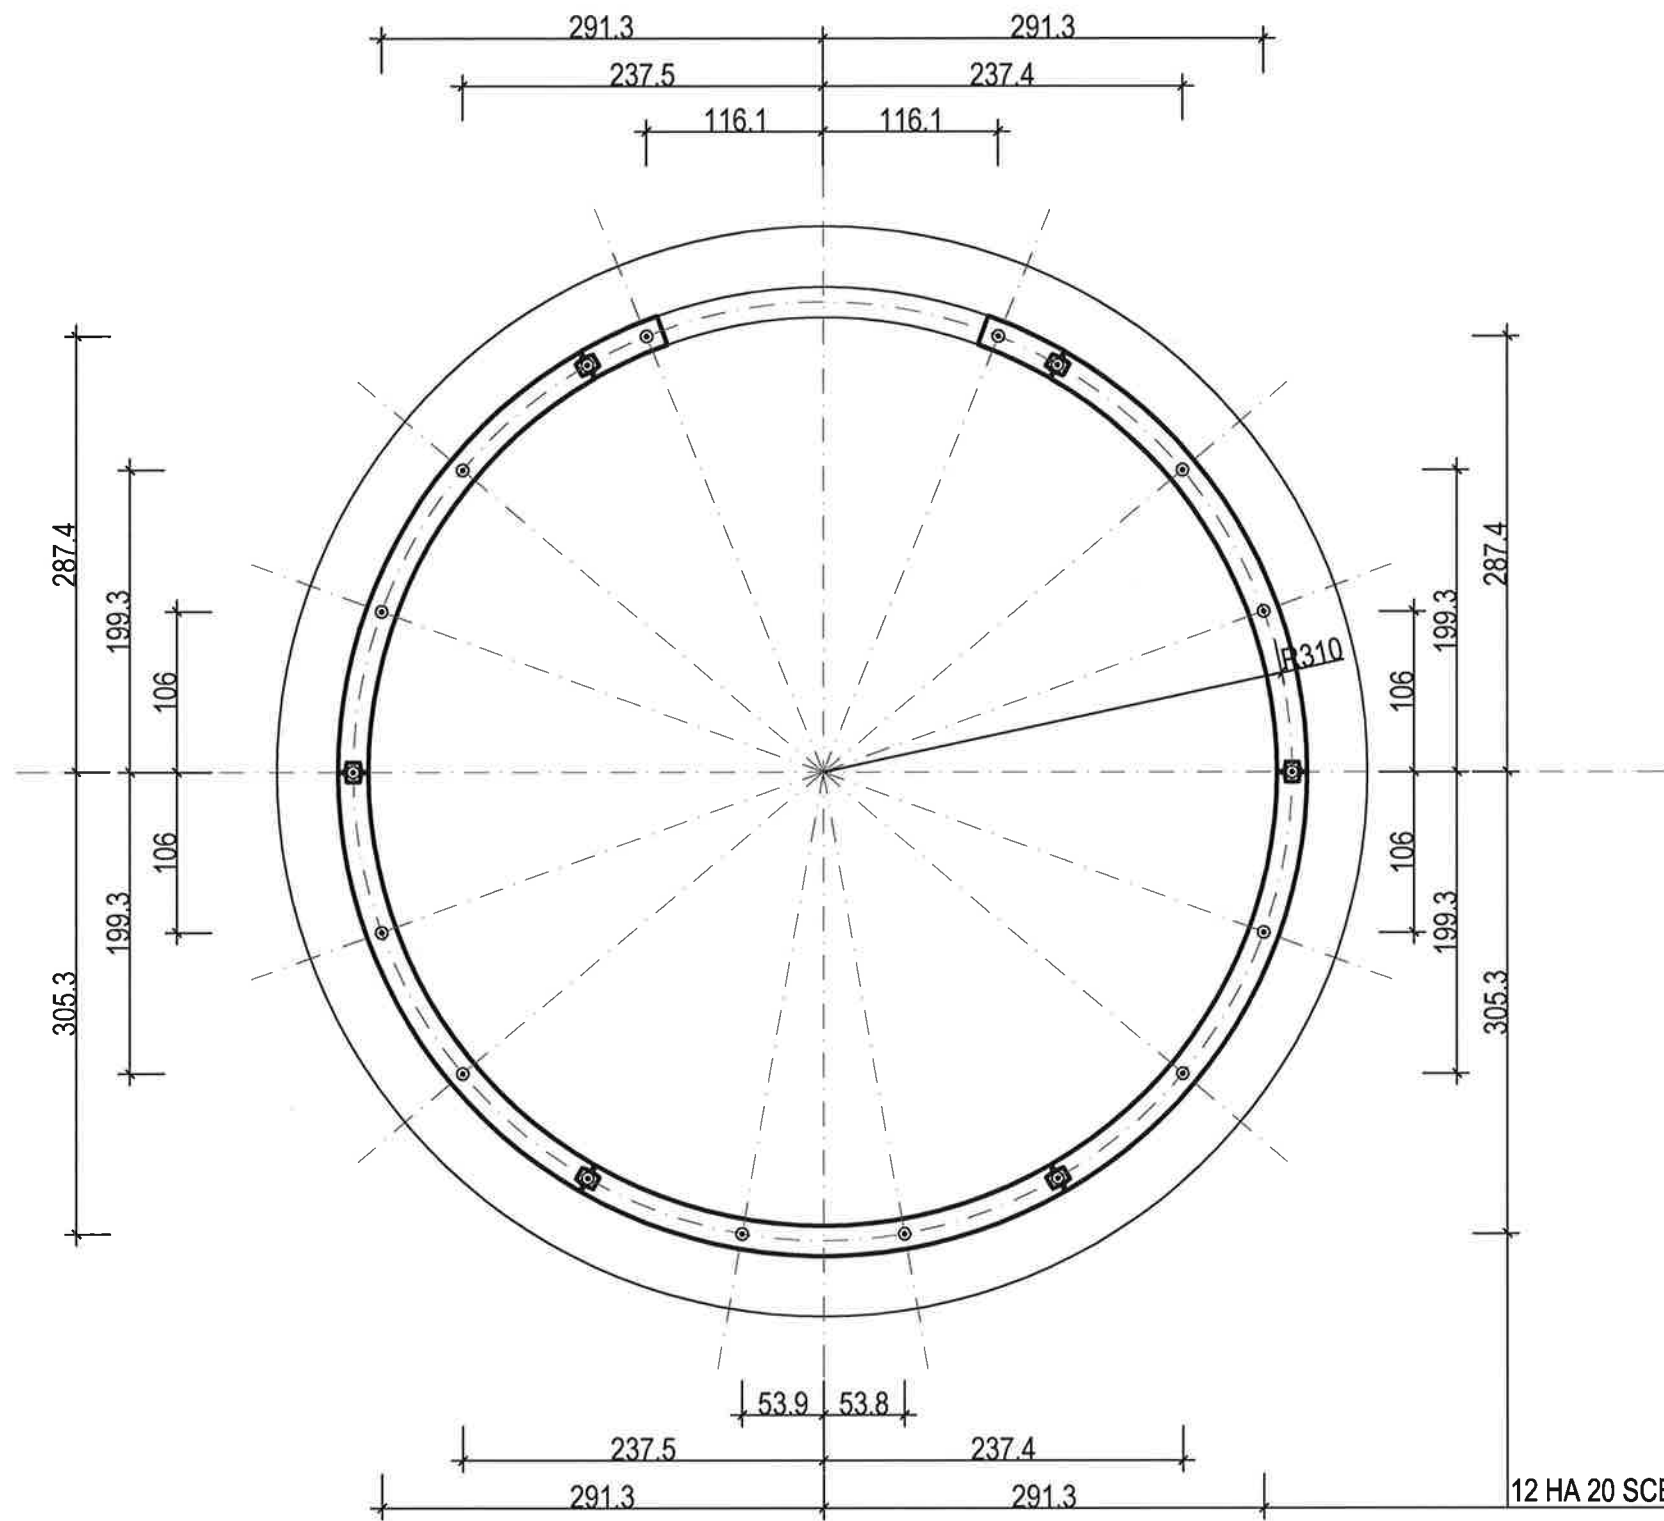


12 HA 20 SCELL2S DANS "ANCROBOX"

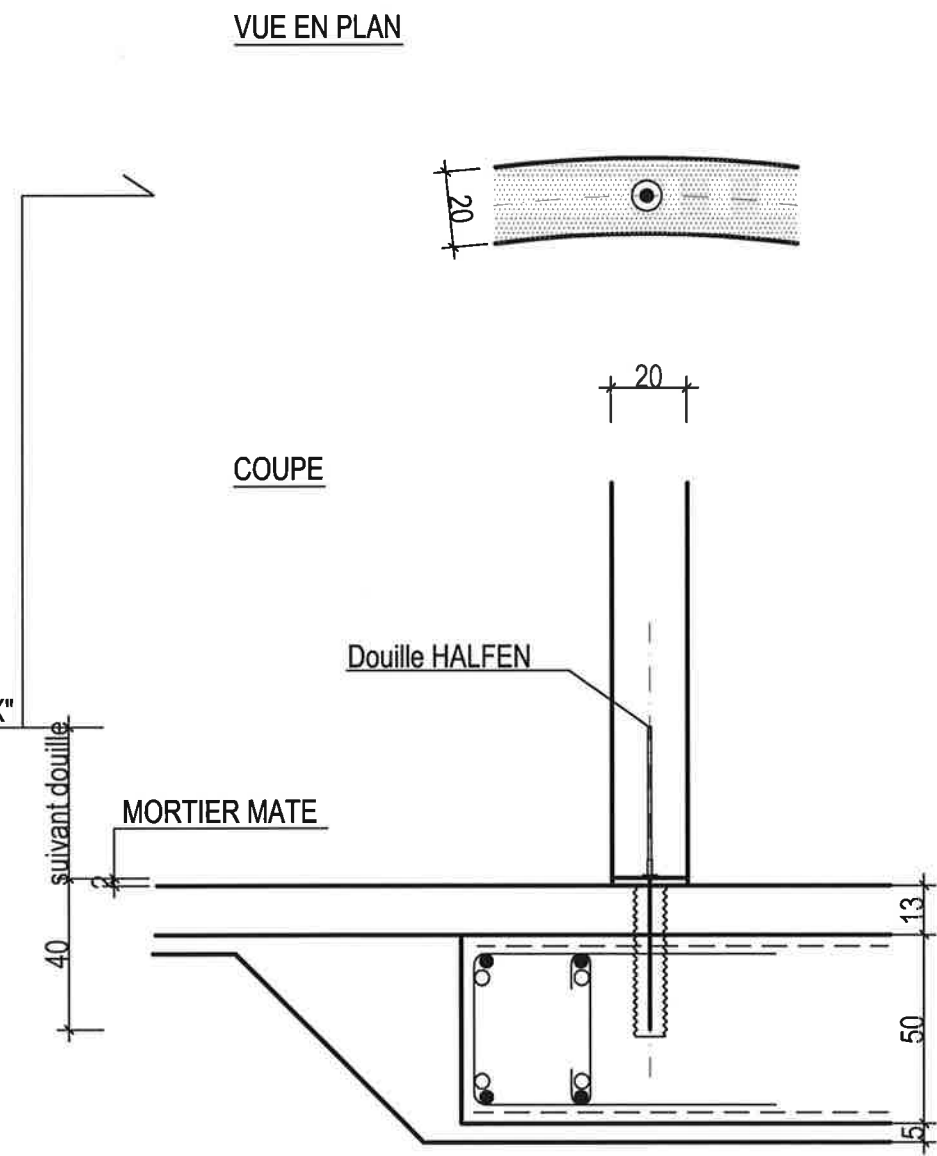

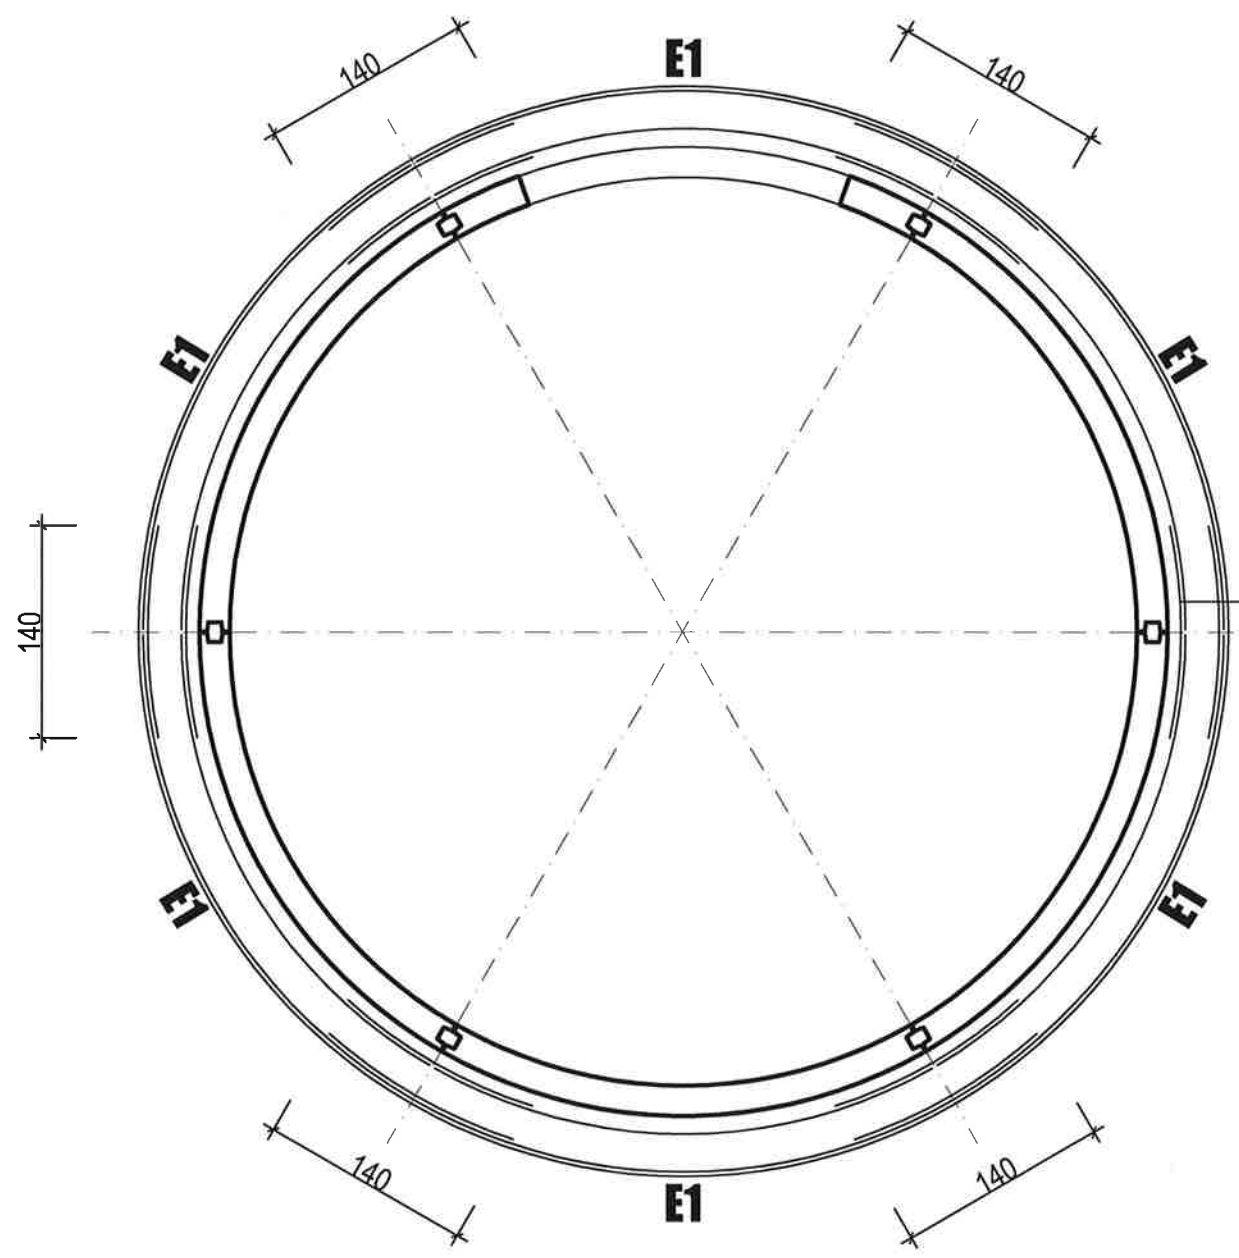


Clavetage
Valable 6 fois

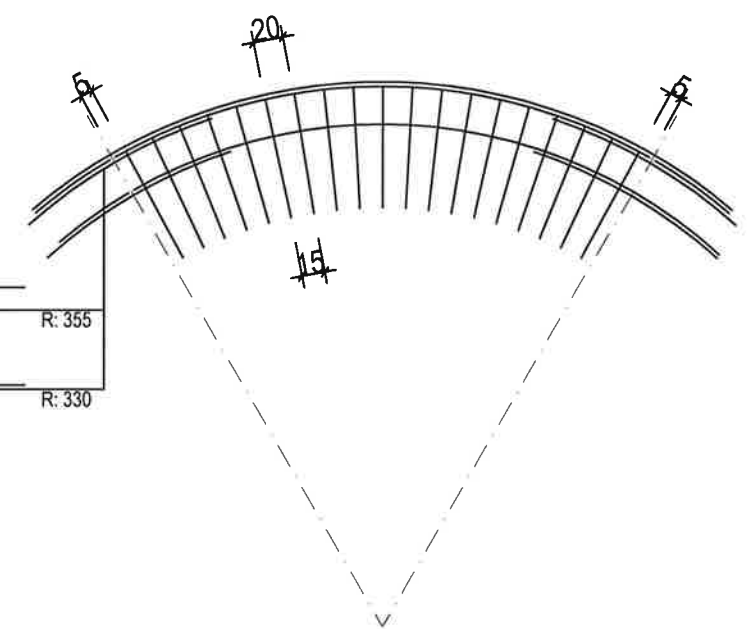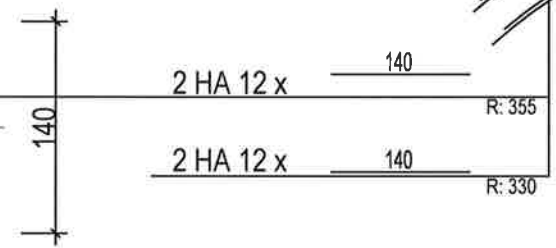


E1 6 pièces
NOTA

CADRES RAYONNANTS
ESPACEMENTS 20 cm BARRES EXT.



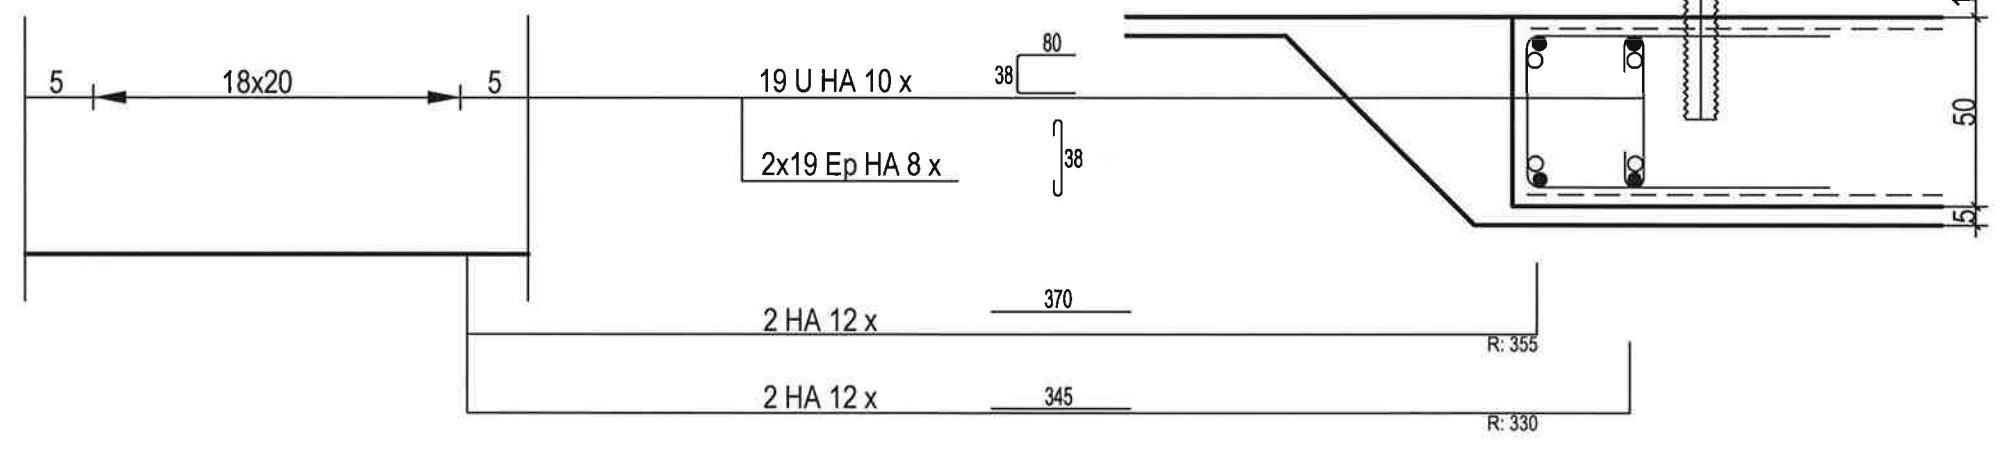


ARMATURES RADIER

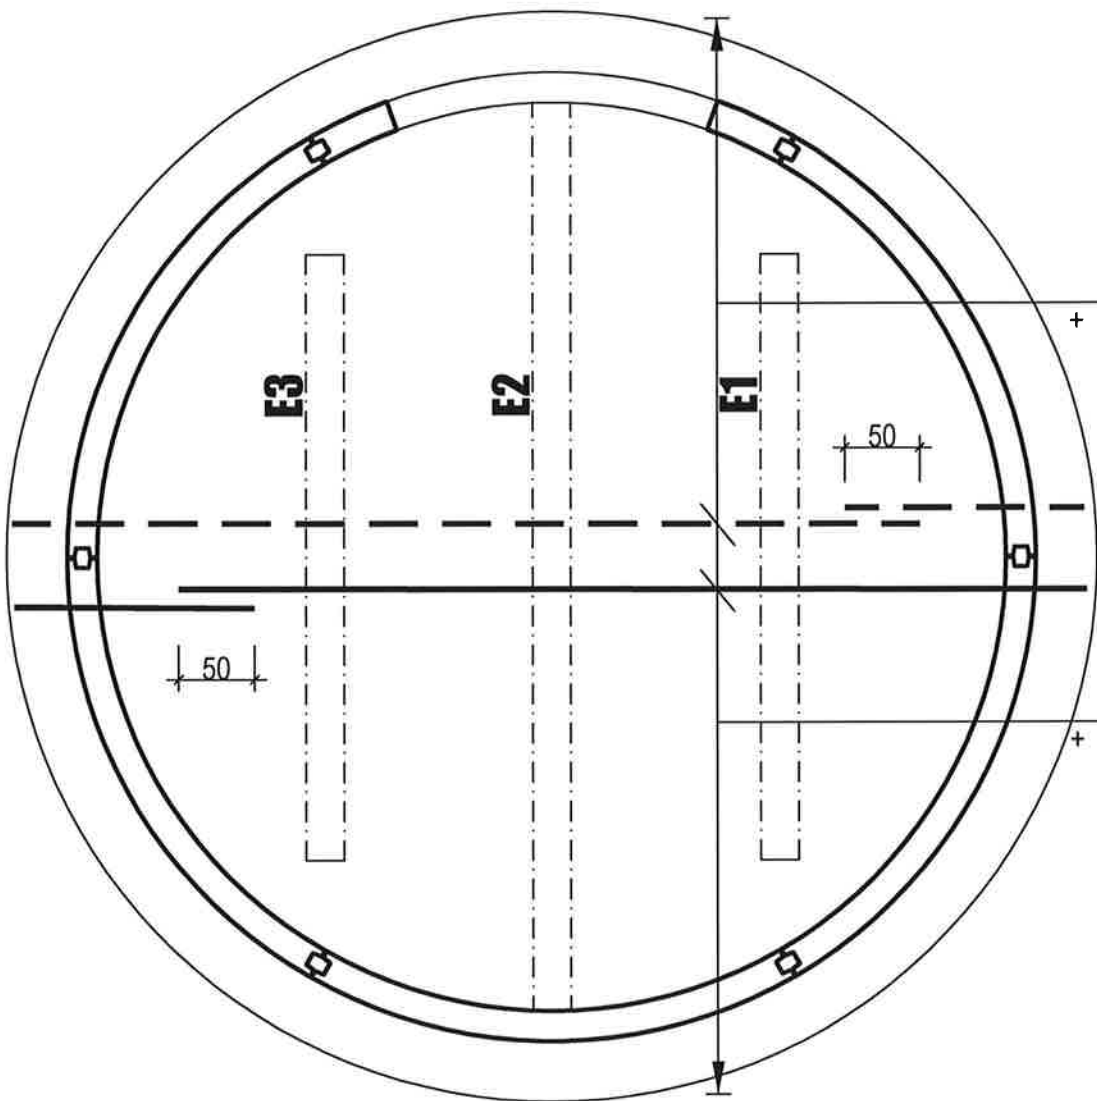


SUP.
1/2+3 Pan ST 25C (600x240)
+ 2 Pan ST 25C (160x240)
Rec :40 cm


INF.
1/2+3 Pan ST 50C (600x240)
+ 2 Pan ST 50C (160x240)
Rec :40 cm

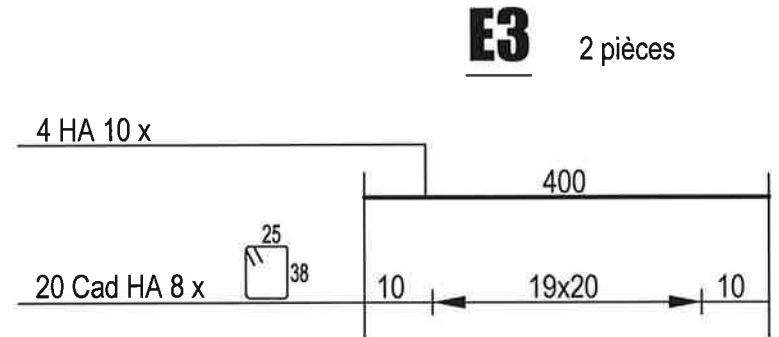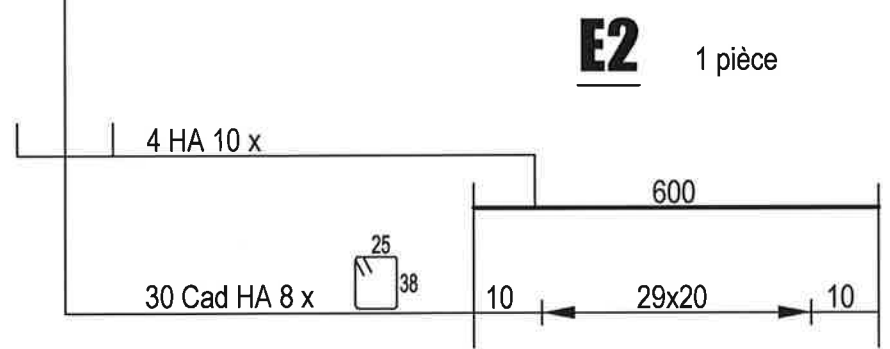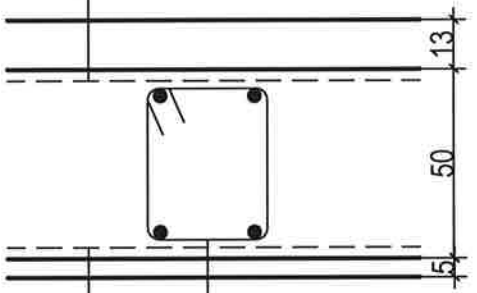

VUE EN PLAN

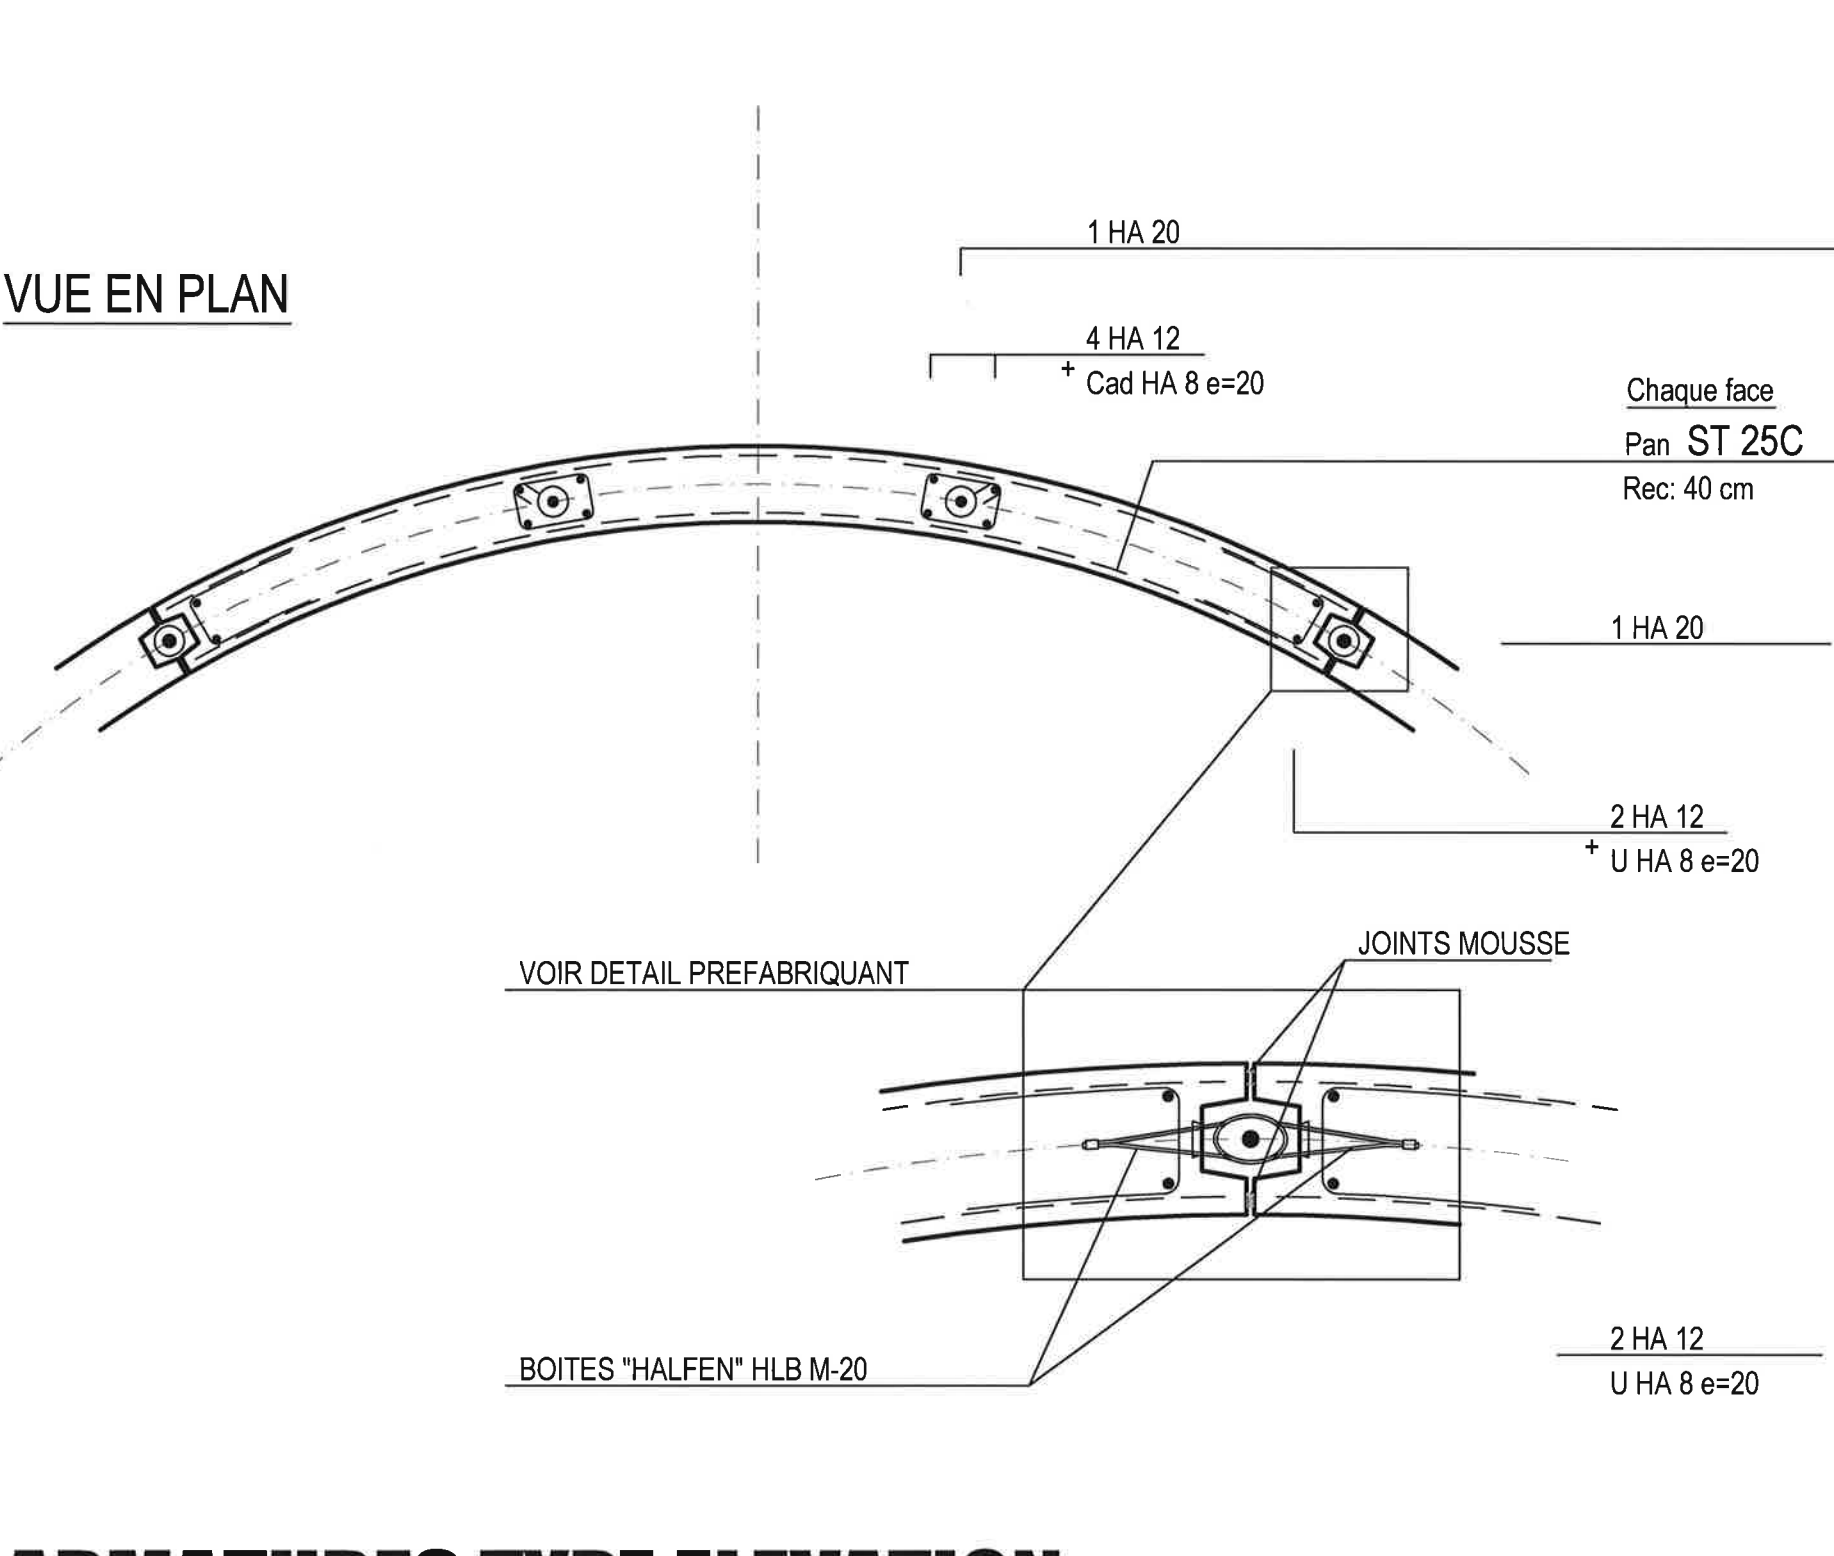



ELEVATION

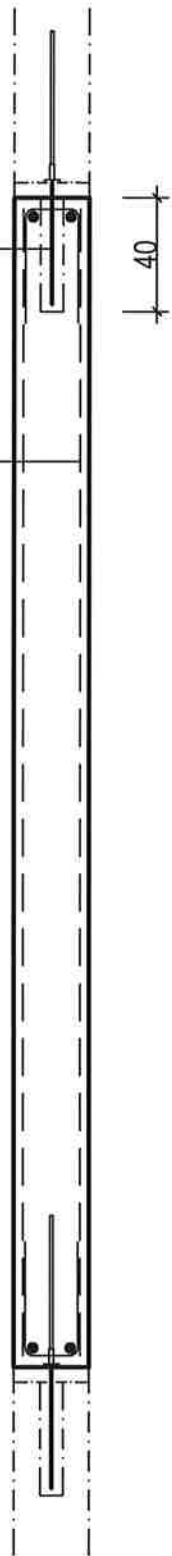


ARMATURES TYPE ELEVATION

COMMANDE ARMATURES VOIR PREFABRIQUANT


T1a (1p) **T1b** (1p) **T1c** (1p) **T1d** (1p)

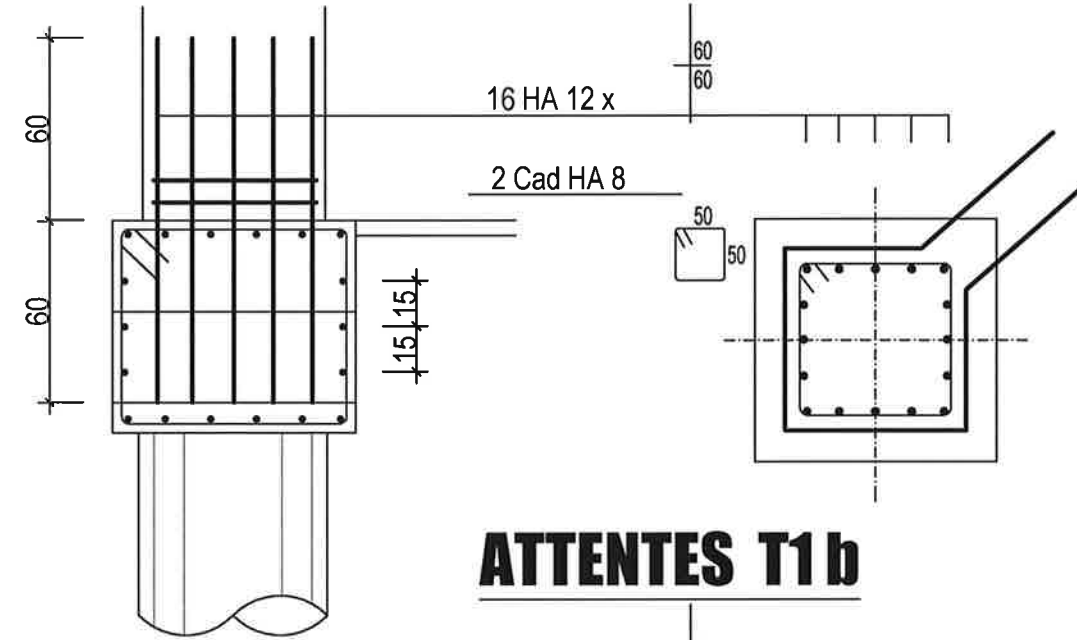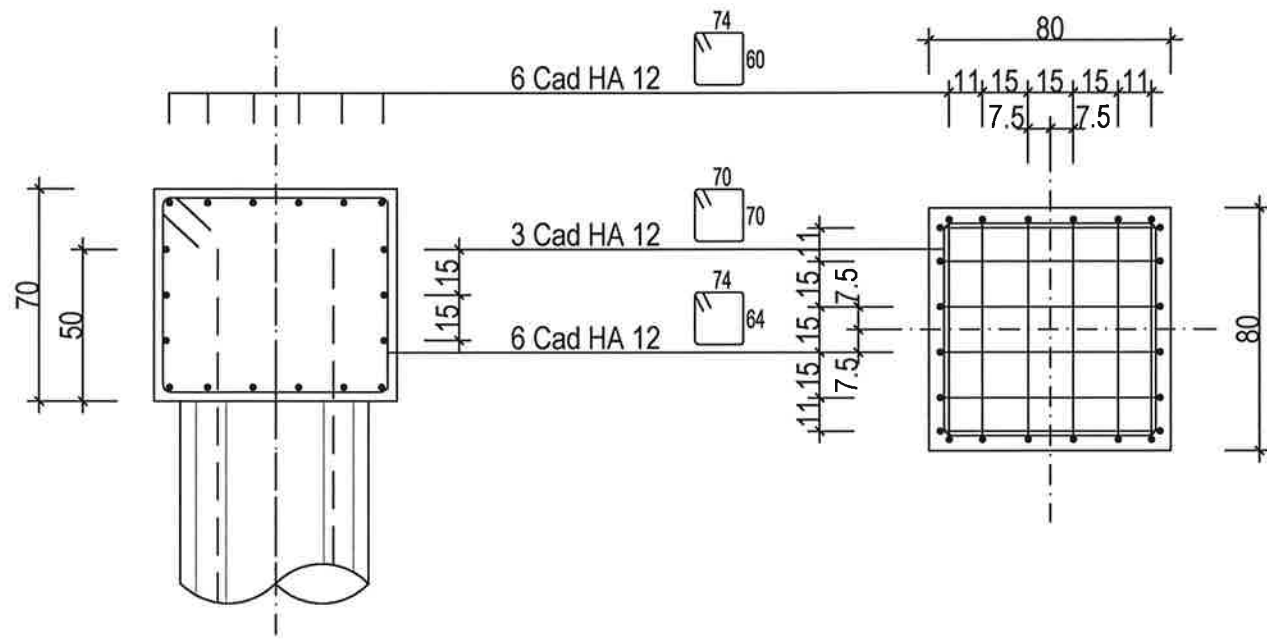

ATTENTES T1b

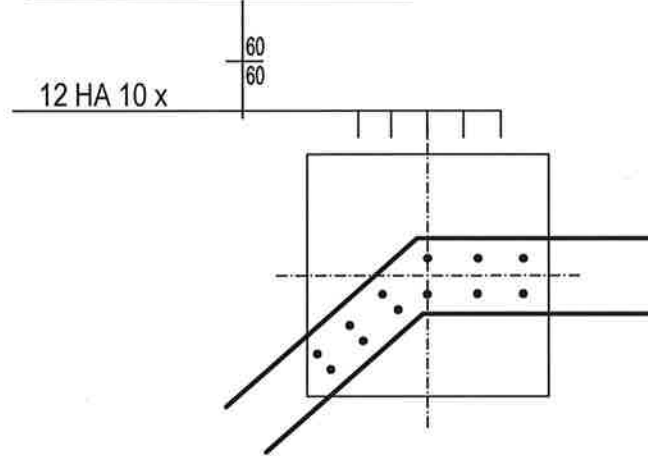

ATTENTES T1c

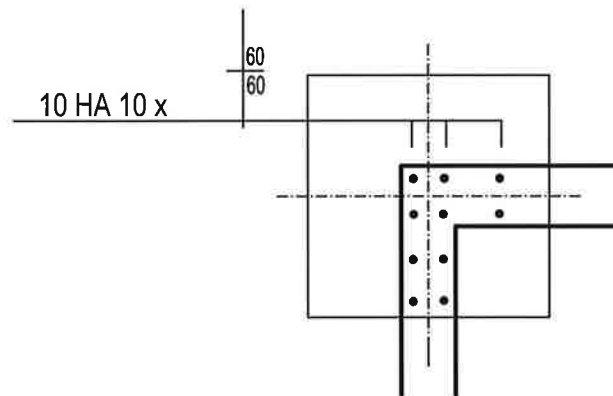

ATTENTES T1d

