

NOAHO
LE 180°
Chemin de Fontanière - 69350 La Mulatière
Création de logements

Les entreprises réalisant les travaux devront tenir compte des derniers plans architecte lors de la réalisation des travaux
Les plans du be MATTE ne doivent servir qu'au corps d'état concerné et doivent être des plans d'exécution.

ARCHITECTE(S):	ATELIER DE LA PASSERELLE	MO DELEGUE:	
BET STRUCTURE:	MATTE SAS	MOE:	PSO Ingénierie
BET FLUIDES:	PRELEM	CSPS:	SUD EST COORDINATION
ECONOMISTE:	EXECO	OPC:	
BUREAU DE CONTROLE:	Bureau VERITAS	ENTREPRISE(S):	Fontanel

Bât:A
REPRISES AU REZ

INDICE	DATE	MODIFICATIONS

MATTÉ
BUREAU D'ÉTUDES
STRUCTURES ET FLUIDES

119 BOULEVARD STALINGRAD 69100 VILLEURBANNE
Tél. 04 72 44 02 87 Fax 04 72 44 26 59
E-mail : bet@matte.fr

Dessiné par : J.BO
Contrôlé par : P.LIN
Echelle : 1/50°

DOE

Contrainte de sol: 8 bars ELS

Aciers HA (T) FeE500
Aciers Doux (Ø) FeE 235
Aciers TS FeE 500
Béton fc28 >= 25MPa
Enrobage = 3 cm


PLAN N°
A100 0

DATE : 11/04/2016

Affaire N°
13.12.118


COUPE 1

Ech: 1/25

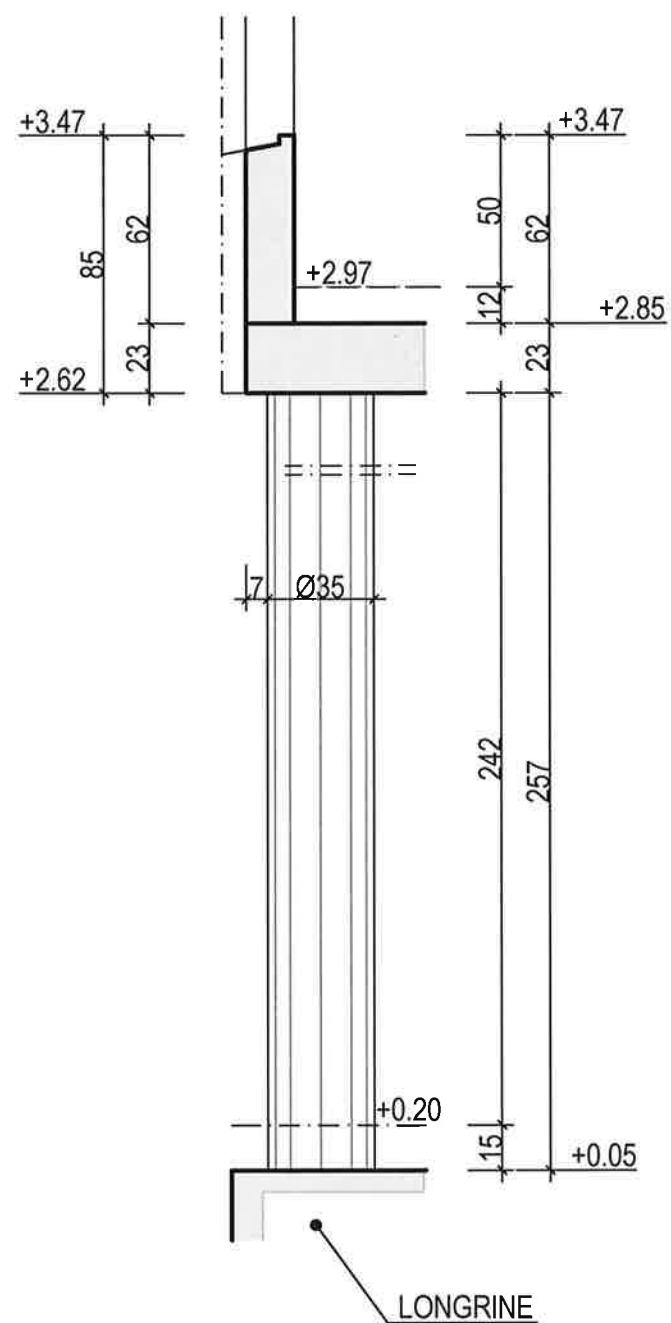


COUPE 2

Ech: 1/25

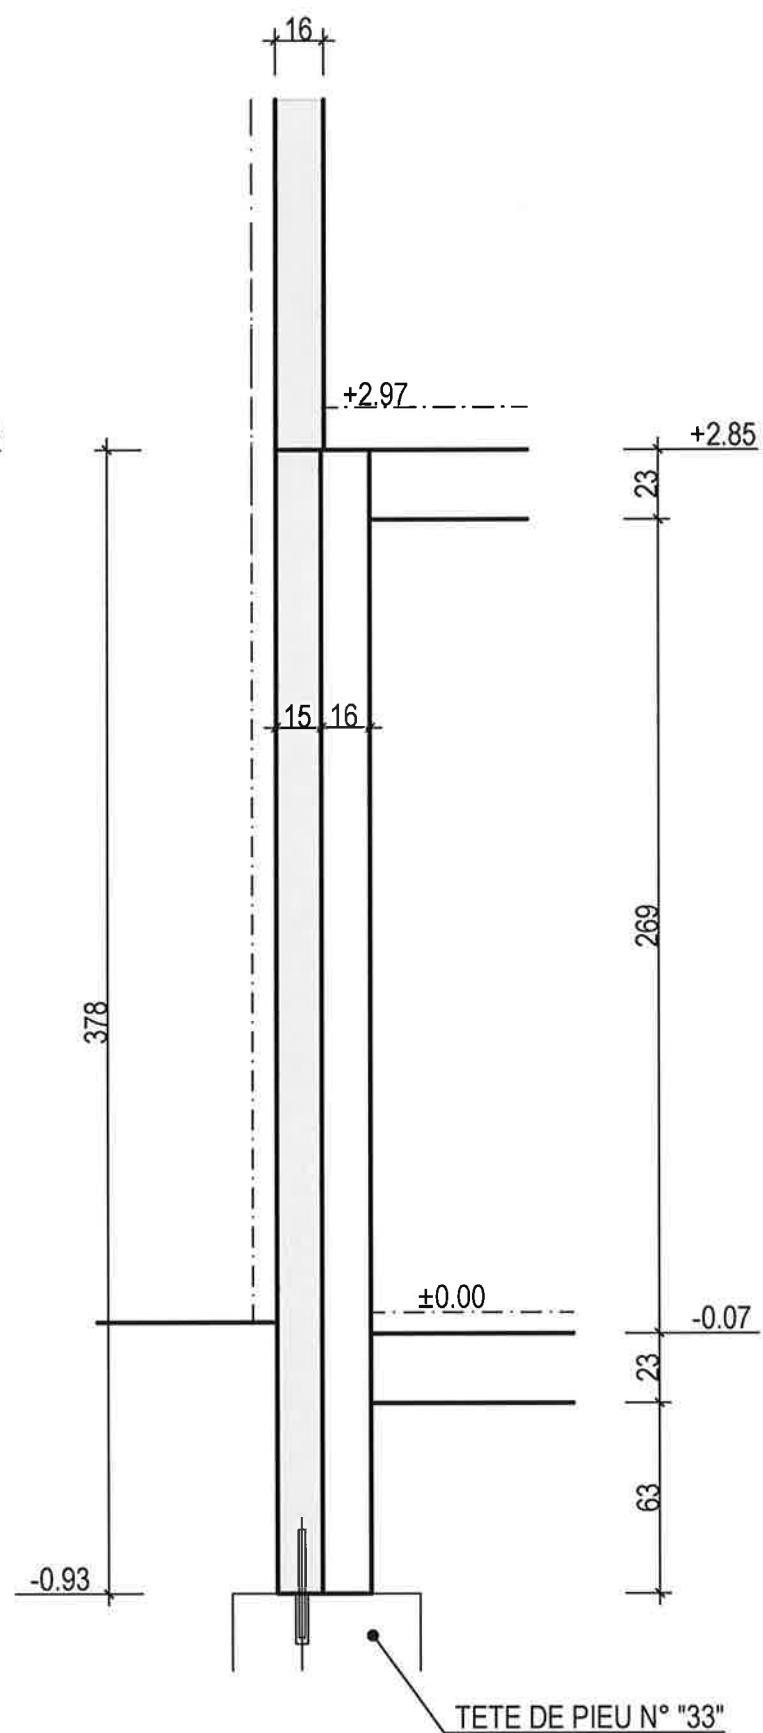


COUPE 3

Ech: 1/25

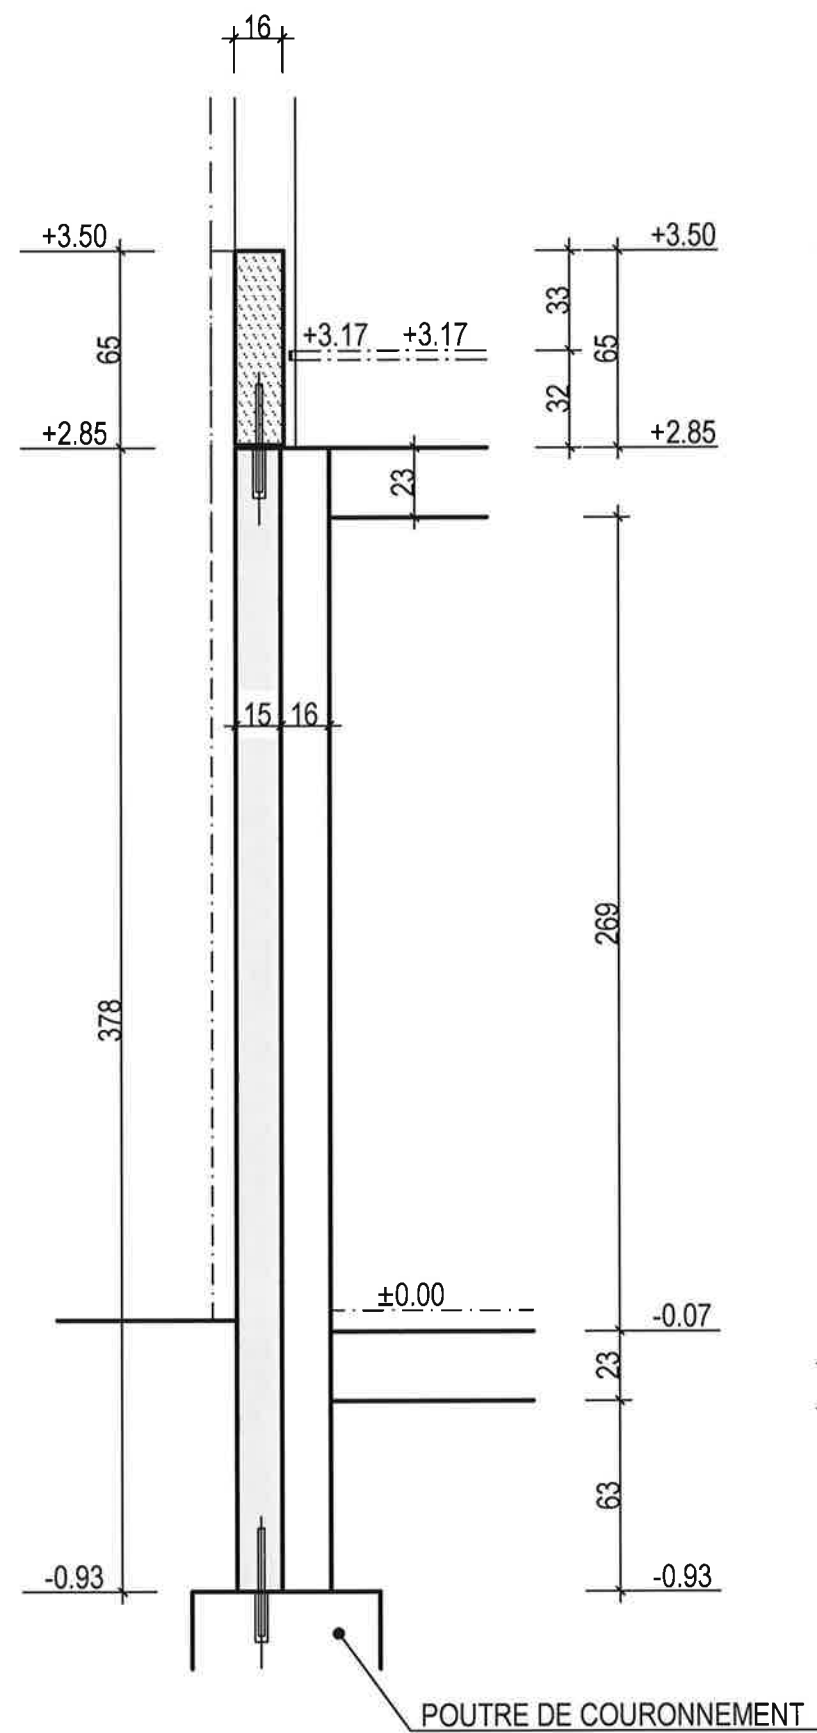

COUPE 4

Ech: 1/25

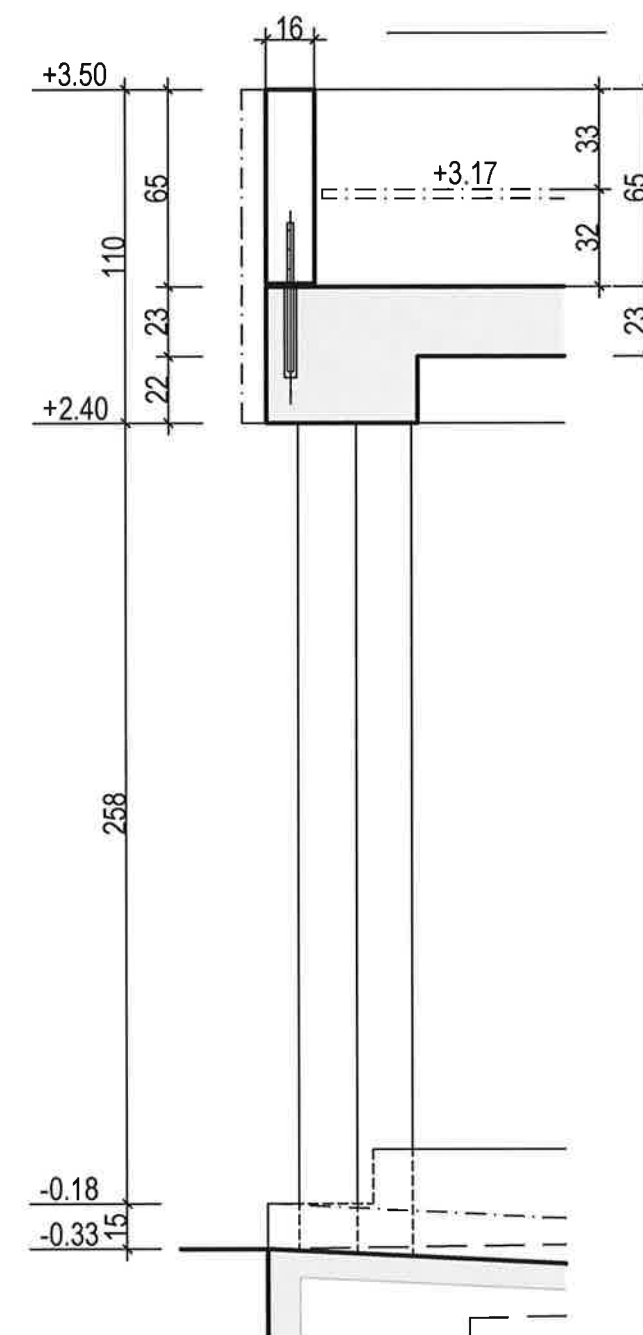

RENFORT SUR POTEAU P1 et P2

VUE de DESSUS

SUP.
5 HA 16 16 100

A

SUP.
4 HA 16 x 400

B

COUPE

ELEVATION

BN1

Nombre: 2

PV15 PV15

PV15

PV16

(a) 3 U HA 8 x

ATT2

ATT2

Clavetage ATT2
2x2 HA 10 x140

P3

P3

7 Cad HA 8
5 Cad HA 8

LIAISONS POTEAU
2x2 HA 12 x SCILLE A LA RESINE
ou ATTENTES EXISTANTES

AFF: S.13.12.119

Bât: A

LA MULATIERE-69350 LaMulatiere
CREATION de LOGEMENTS

REPRISE

Plan n° A 100

3

RENFORT SUR POTEAU P1 et P2

VUE de DESSUS

SUP.
5 HA 16 16 100

A

SUP.
4 HA 16 400

B

COUPE

ELEVATION

CHAPITEAU
50x50x20 HT

20 Cad HA 8

2x20 Ep HA 8

4 HA 16

4 HA 10

BN1

Nombre: 2

PV15 PV16

PV15

PV16

(a) 3 U HA 8 x

B

ATT2

ATT2

Clavetage ATT2
2x2 HA 10 x140

P3

P3

7 Cad HA 8
5 Cad HA 8

LIAISONS POTEAU
2x2 HA 12 x SCELLE A LA RESINE
ou ATTENTES EXISTANTES

AFF: S.13.12.119

Bât: A



LA MULATIERE-69350 LaMulatiere
CREATION de LOGEMENTS

REPRISE


Plan n° A 100

3

MUR M1

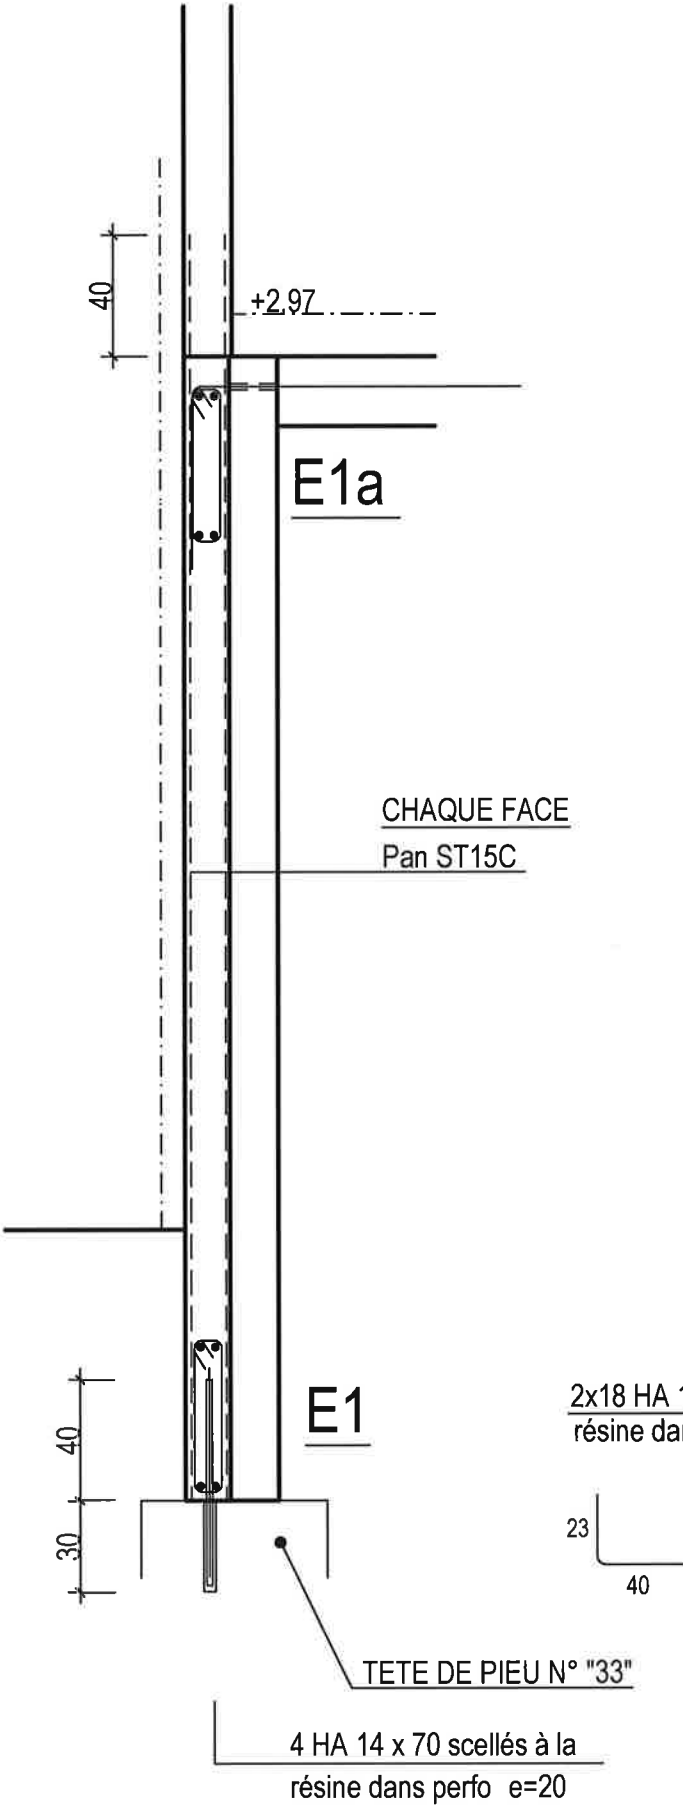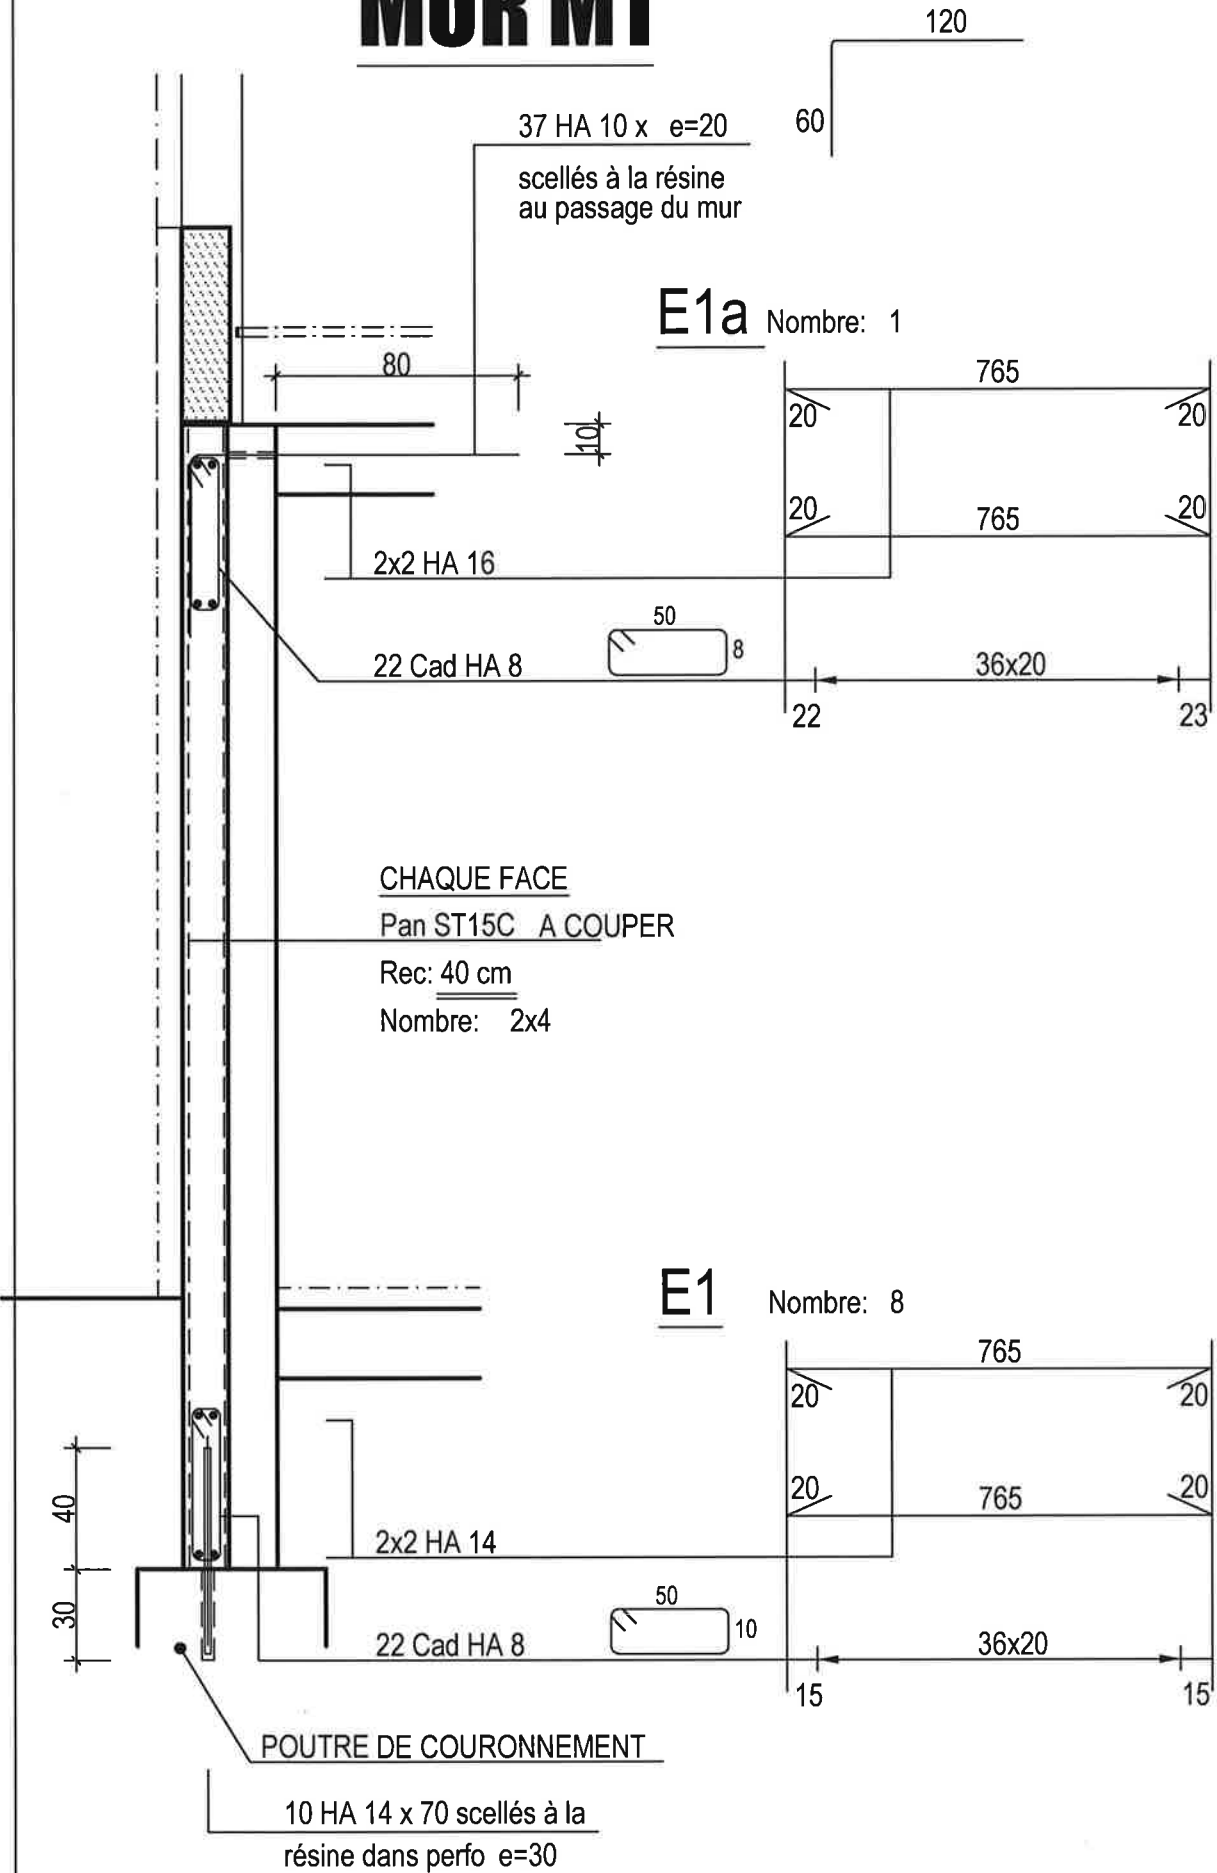

ELEVATION

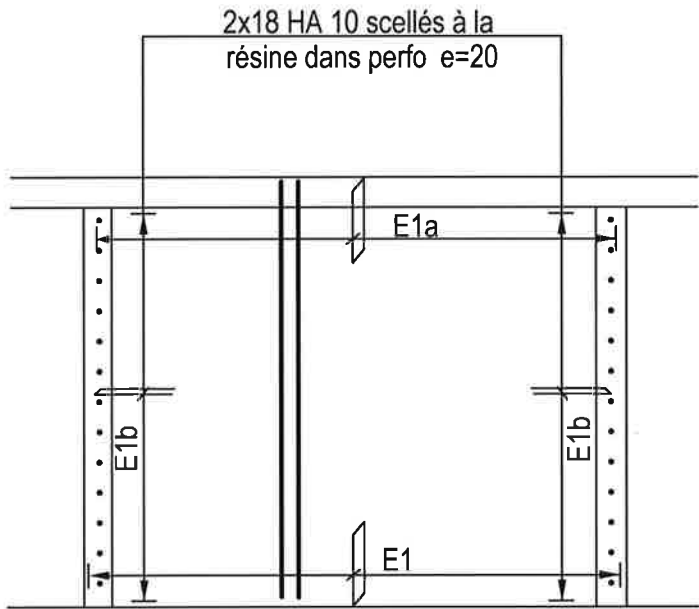

E1b Nombre: 2

