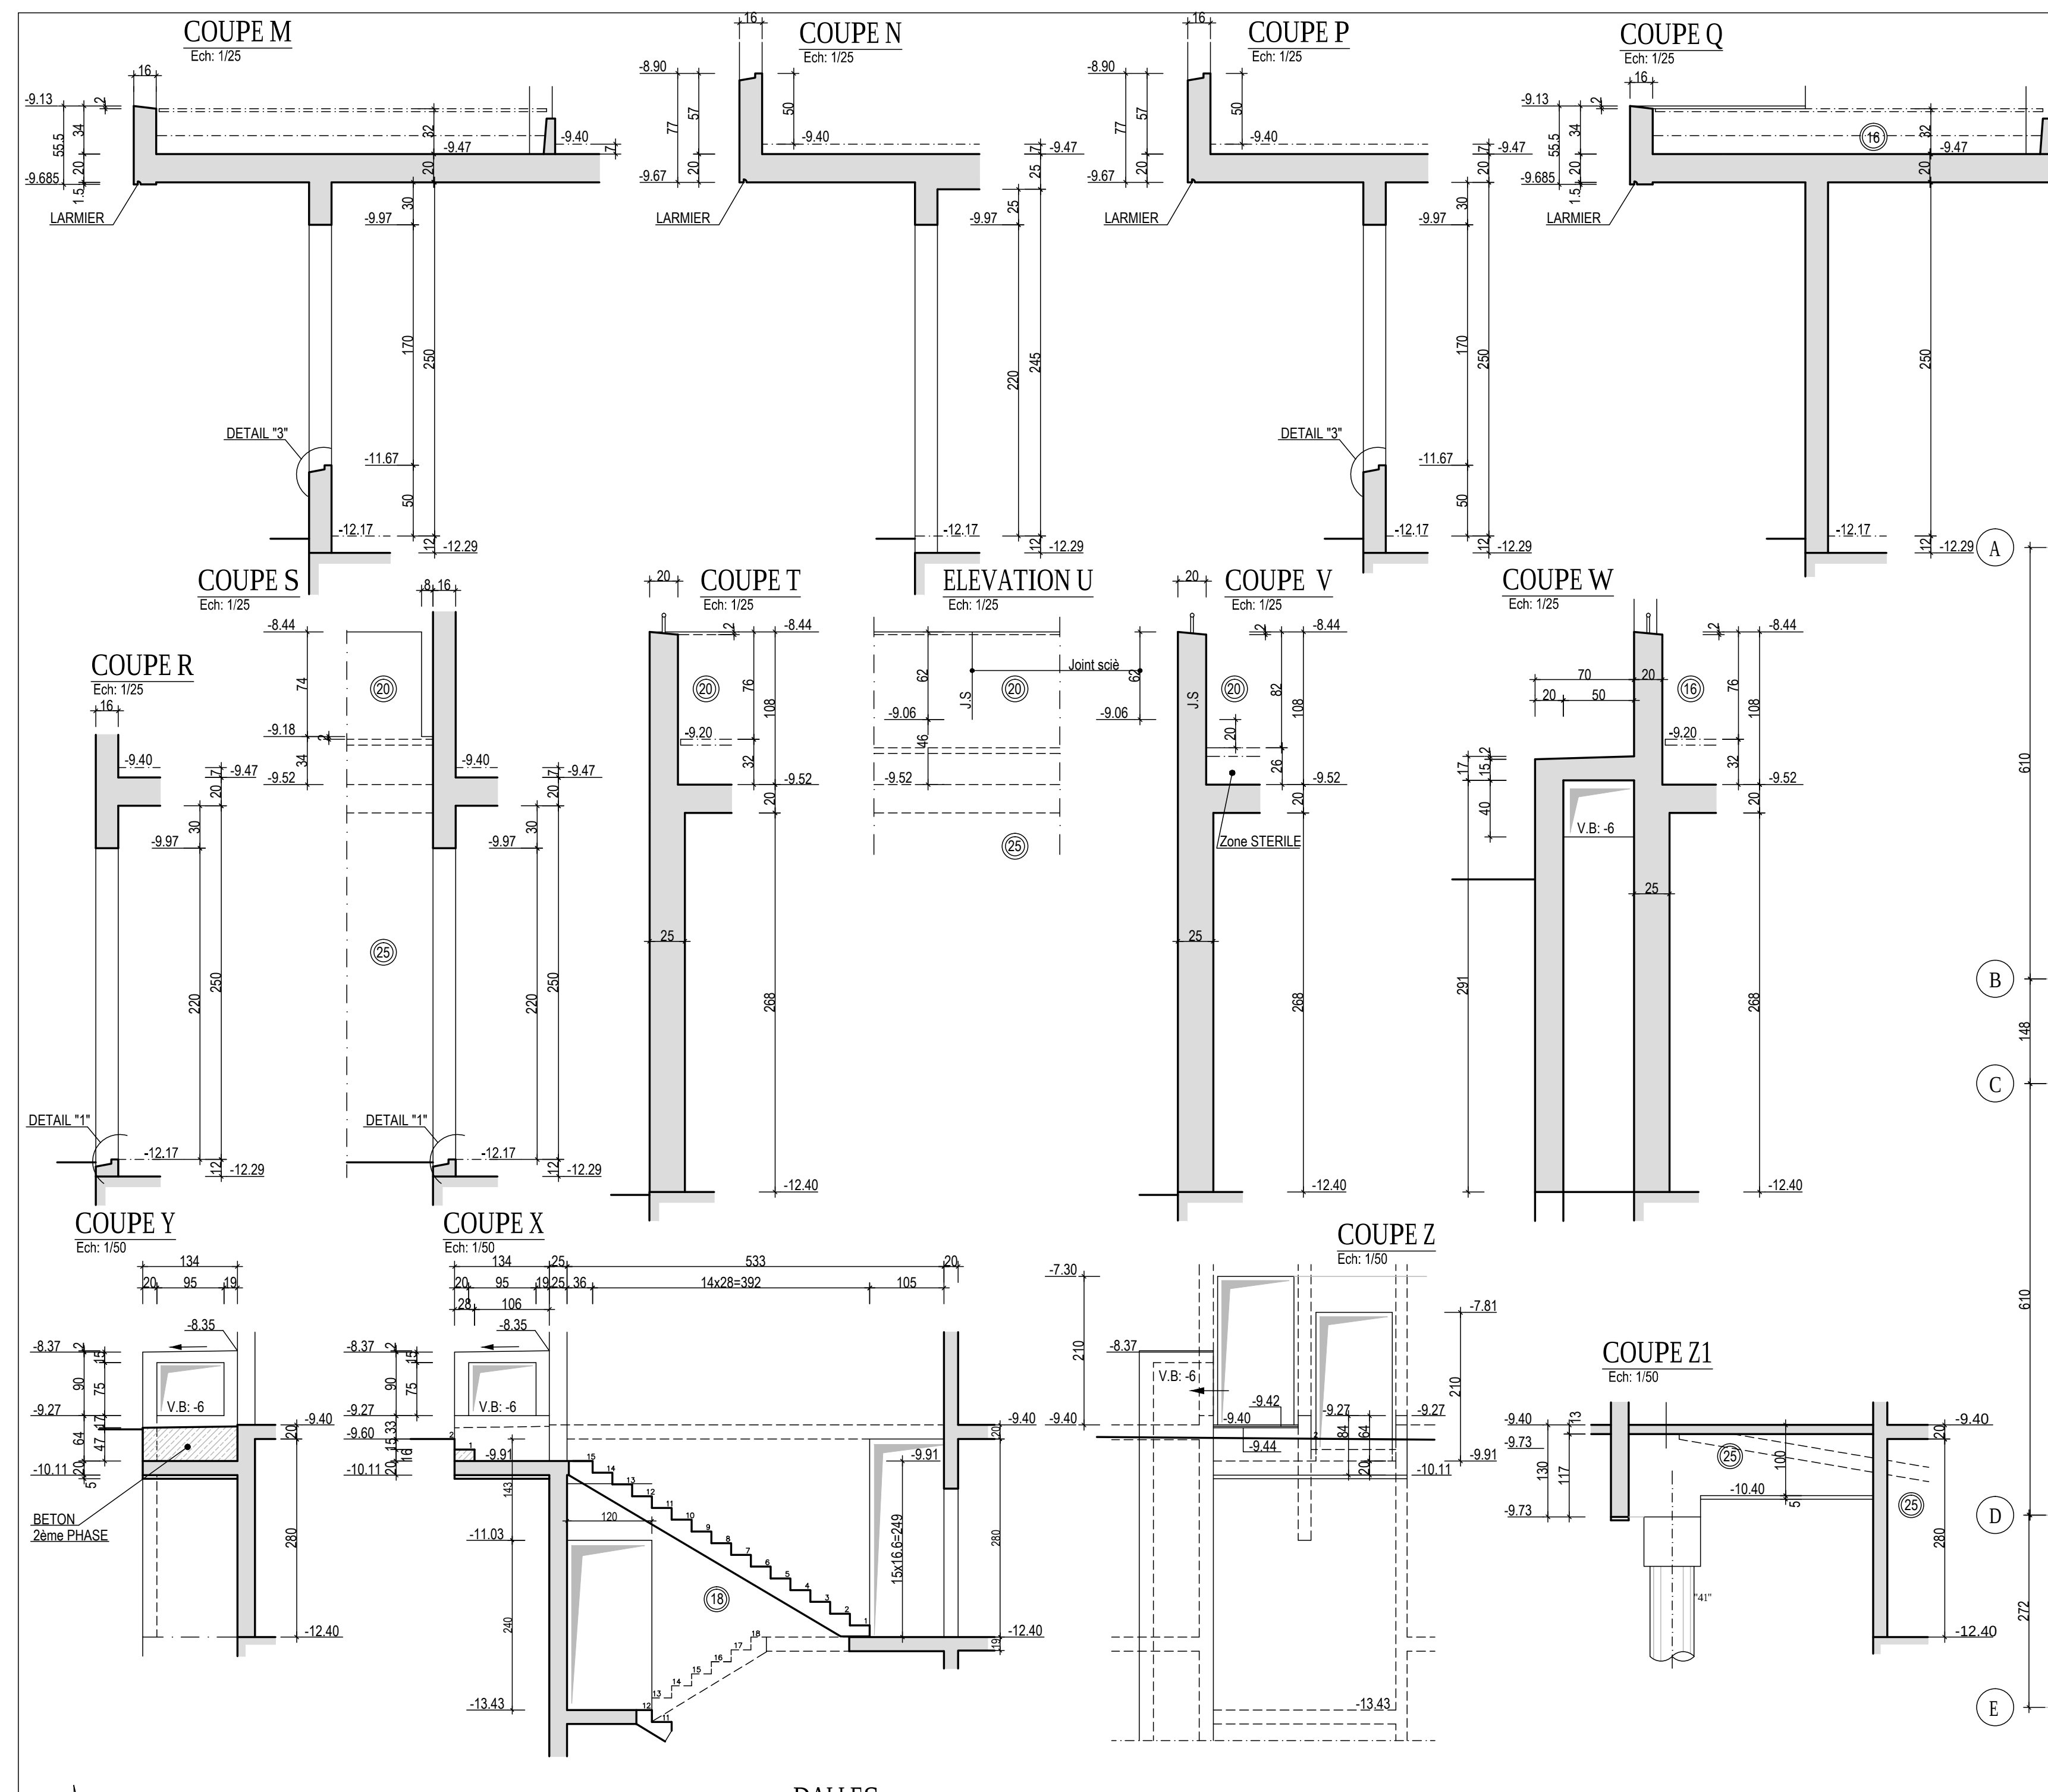
COUPE M
Ech: 1/25
COUPE N
Ech: 1/25
COUPE P
Ech: 1/25
COUPE Q
Ech: 1/25
LARMIER
DETAIL "3"
COUPE S
Ech: 1/25
COUPE R
Ech: 1/25
COUPE T
Ech: 1/25
ELEVATION U
Ech: 1/25
Joint scié
COUPE V
Ech: 1/25
Zone STERILE
COUPE W
Ech: 1/25
V.B: -6
DETAIL "1"
COUPE Y
Ech: 1/50
BETON
2ème PHASE
COUPE X
Ech: 1/50
14x28=392
15x16.6=249
COUPE Z
Ech: 1/50
COUPE Z1
Ech: 1/50
-12.40

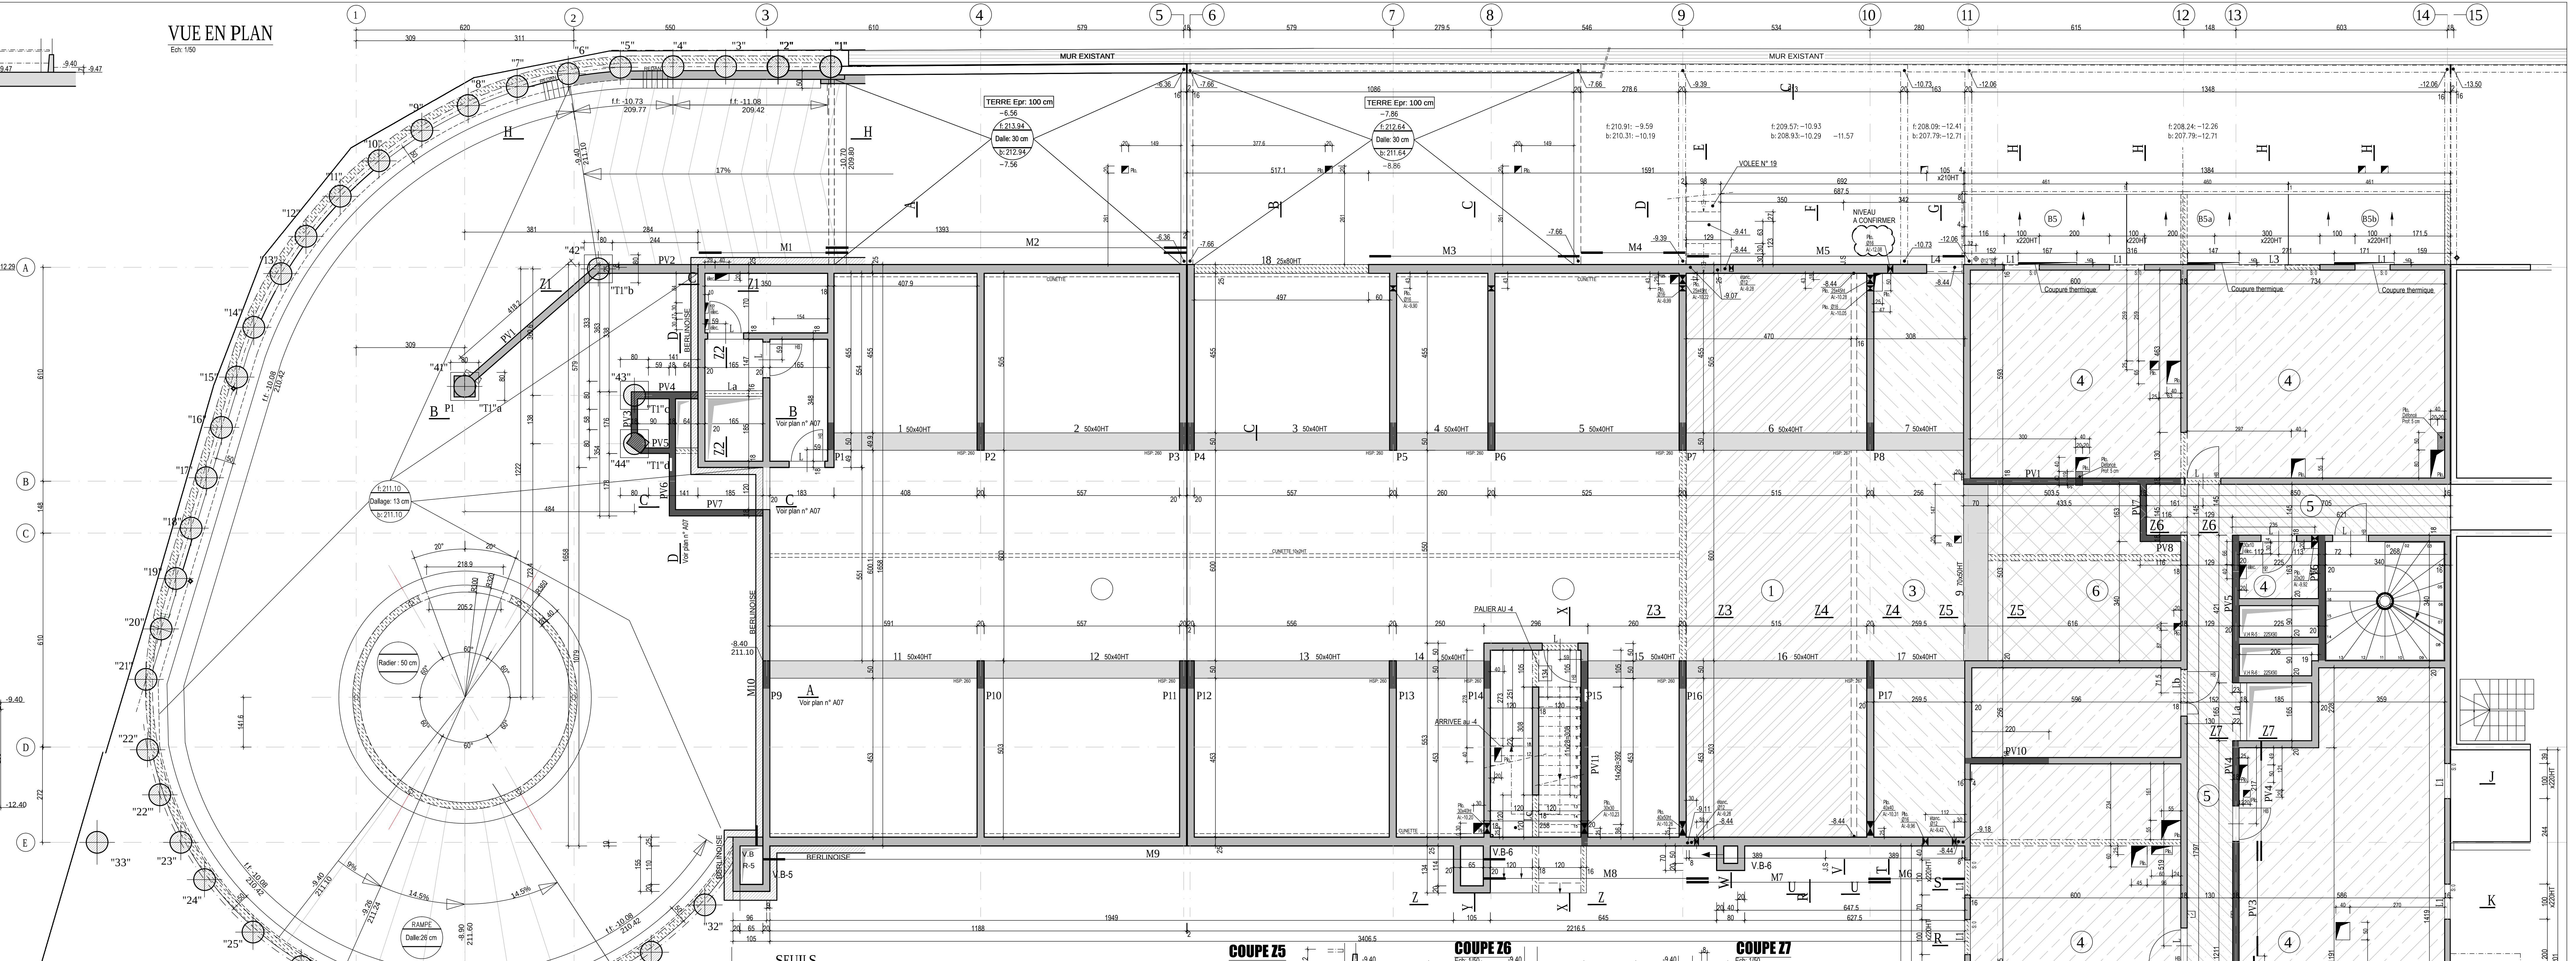
VUE EN PLAN
Ech: 1/50
MUR EXISTANT
TERRE Epr: 100 cm
Dalle: 30 cm
f: 213.94
b: 212.94
f: 212.64
b: 211.64
Dallage: 13 cm
f: 211.10
b: 211.10
Radier : 50 cm
RAMPE
Dalle:26 cm
BERLINOISE
VOLEE N° 19
NIVEAU A CONFIRMER
PALIER AU -4
ARRIVEE au -4
Coupure thermique
CUNETTE
Voir plan n° A07
M1
M2
M3
M4
M5
M8
M9
M10
PV1
PV2
PV7
PV8
PV10
PV11
P1
P2
P3
P4
P5
P6
P7
P8
P9
P10
P11
P12
P13
P14
P15
P16
P17
50x40HT
25x80HT
x220HT
V.B-5
V.B-6

±0.00 = 220.50

DALLES

○	FINI: -9.40=211.10 DALLE BA Epr: 20 cm DESSUS BRUT:-9.40 RESERVE: 0 cm
①	FINI: -9.15=211.35 DALLE BA Epr: 20 cm DESSUS BRUT:-9.52 RESERVE: 37 cm (TERRE)
③	FINI: -9.20=211.30 DALLE BA Epr: 20 cm DESSUS BRUT:-9.52 RESERVE: 32 cm (Terrasse)
④	FINI: -9.40=211.10 DALLE BA Epr: 20 cm DESSUS BRUT:-9.47 RESERVE: 7 cm
⑤	FINI: -9.40=211.10 DALLE BA Epr: 25 cm DESSUS BRUT:-9.47 RESERVE: 7 cm
⑥	FINI: -9.40=211.10 DALLE BA Epr: 45 cm DESSUS BRUT:-9.52 RESERVE: 12 cm
⑦	FINI: -9.33=211.17 DALLE BA Epr: 20 cm DESSUS BRUT:-9.47 RESERVE: 14 cm

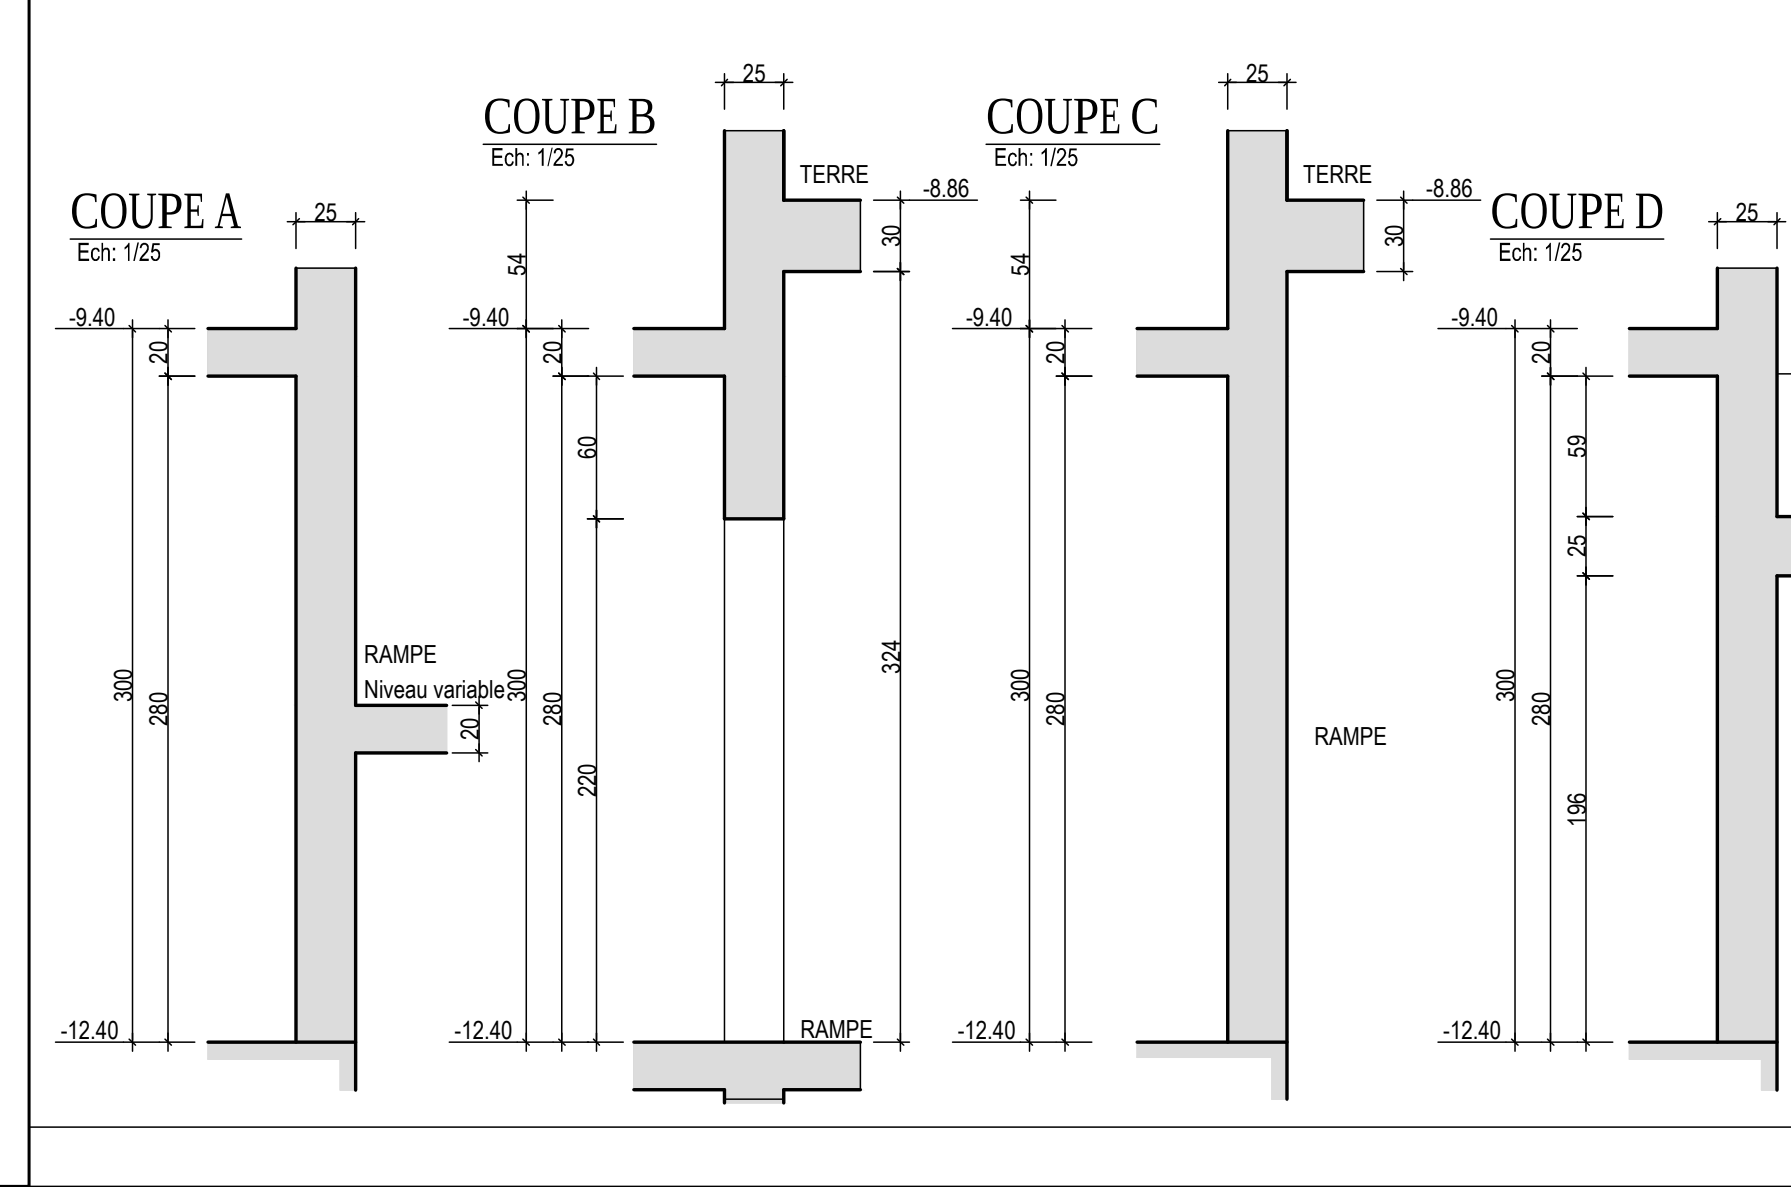
COUPE A
Ech: 1/25
RAMPE
Niveau variable
COUPE B
Ech: 1/25
TERRE
COUPE C
Ech: 1/25
COUPE D
Ech: 1/25
-12.40

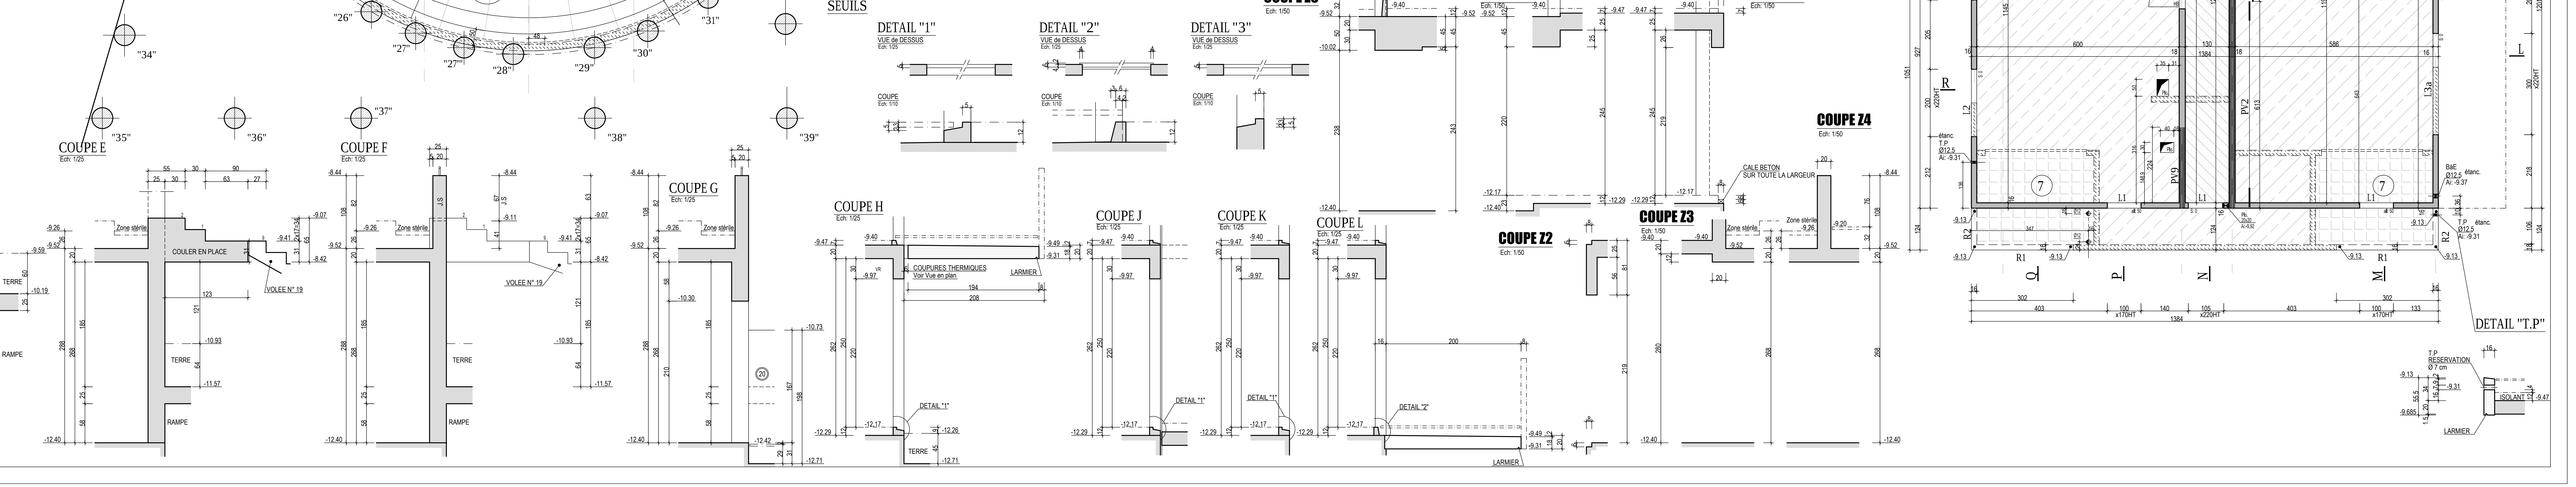
COUPE E
Ech: 1/25
Zone stérile
COULER EN PLACE
VOLEE N° 19
COUPE F
Ech: 1/25
COUPE G
Ech: 1/25
COUPE H
Ech: 1/25
COUPURES THERMIQUES
Voir Vue en plan
LARMIER
COUPE J
Ech: 1/25
COUPE K
Ech: 1/25
COUPE L
Ech: 1/25
SEUILS
DETAIL "1"
DETAIL "2"
DETAIL "3"
VUE de DESSUS
COUPE
Ech: 1/10
COUPE Z5
COUPE Z6
COUPE Z7
COUPE Z4
COUPE Z2
COUPE Z3
Ech: 1/50
CALE BETON
SUR TOUTE LA LARGEUR
DETAIL "T.P"
T.P
RESERVATION
Ø 7 cm
ISOLANT
x170HT
x220HT
1384

NOAHO

Chemin de Fontanière - 69350 La Mulatière

Création de logements

Les entreprises réalisant les travaux devront tenir compte des derniers plans architecte lors de la réalisation des travaux
Les plans du be MATTE ne doivent servir qu'au corps d'état concerné et doivent être des plans d'exécution.

ARCHITECTE(S):	ATELIER DE LA PASSERELLE	MO DELEGUE:	
BET STRUCTURE:	MATTE SAS	MOE:	PSO Ingénièrie
BET FLUIDES:	PRELEM	CSPS:	SUD EST COORDINATION
ECONOMISTE:	EXECO	OPC:	
BUREAU DE CONTROLE:	Bureau VERITAS	ENTREPRISE(S):	Fontanel-pbc

Bât: A
PLANCHER sur -4
Coffrage

DOE

Contrainte de sol: 8 bars ELS
Aciers HA (T) FeE500
Aciers Doux (Ø) FeE 235
Aciers TS FeE 500
Béton fc28 >= 25MPa
Enrobage = 3 cm

INDICE	DATE	MODIFICATIONS
A	20/11/2015	MISE A JOUR RELEVE et DEP
B		
C		

PLAN N°
A14 A
DATE : 10/11/2015

MATTÉ
BUREAU D'ÉTUDES
STRUCTURES ET FLUIDES
119 BOULEVARD STALINGRAD 69100 VILLEURBANNE
Tél. 04 72 44 02 87 Fax 04 72 44 26 59
E-mail : bet@matte.fr

Dessiné par : J.BO
Contrôlé par : P.LIN
Echelle : 1/50°

Affaire N°
13.12.119