

NOHAO

Chemin de Fontanière-69350 La Mulatière

Création de logements

Les entreprises réalisant les travaux devront tenir compte des derniers plans architecte lors de la réalisation des travaux
Les plans du be MATTE ne doivent servir qu'au corps d'état concerné et doivent être des plans d'exécution.

ARCHITECTE(S): Atelier DE LA PASSERELLE
BET STRUCTURE: BET MATTE
BET FLUIDES: PRELEM
ECONOMISTE: EXECO
BUREAU DE CONTROLE: VERITAS

M.O. Délégué: .
M.O.: .
CSPS: PSO ingénierie
M.O.E.: SUD EST COORDINATION
ENTREPRISE(S): Fontanel-pbc

Bât: A
BA au -4

EXE

INDICE	DATE	MODIFICATIONS
--------	------	---------------

A		

Aciers HA (T) FeE500

Aciers Doux (Ø) FeE 235

Aciers TS FeE 500

Béton fc28 >= 25MPa

Enrobage = 3 cm

PLAN N°
A15 A

DATE : 9-11-2015

MATTÉ

BUREAU D'ÉTUDES
STRUCTURES ET FLUIDES

119 BOULEVARD STALINGRAD 69100 VILLEURBANNE

Tél: 04 72 44 02 87 Fax 04 72 44 26 59

E-mail : bet@matte.fr

Dessiné par : J.BONDETTI


Contrôlé par : P. LIN

Ech :

Affaire N°

S.13.12.118


MURS M1

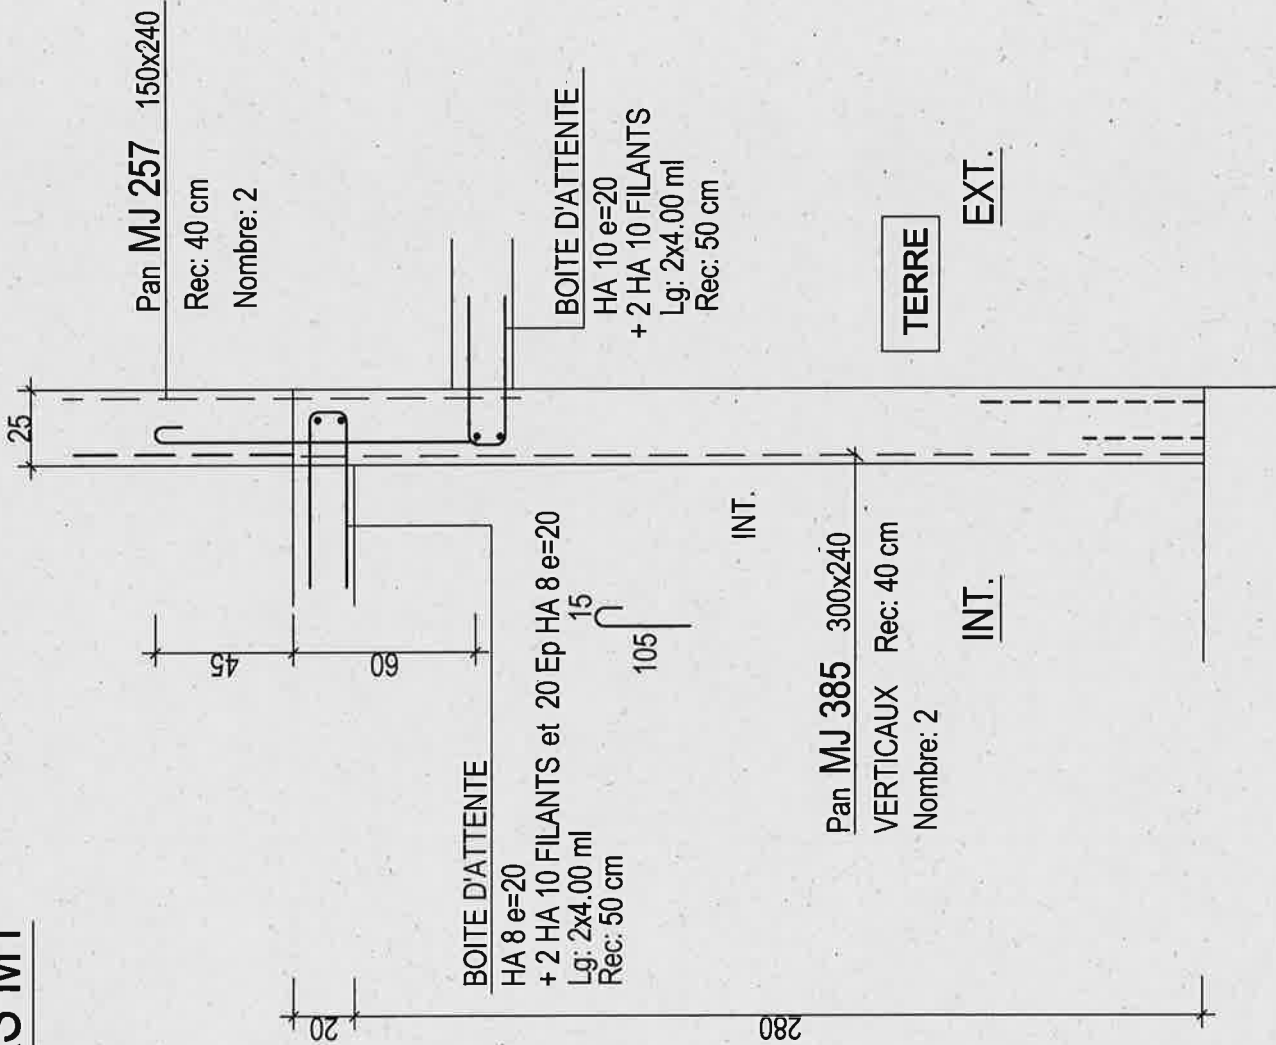


18°
A15


11

MURS M2

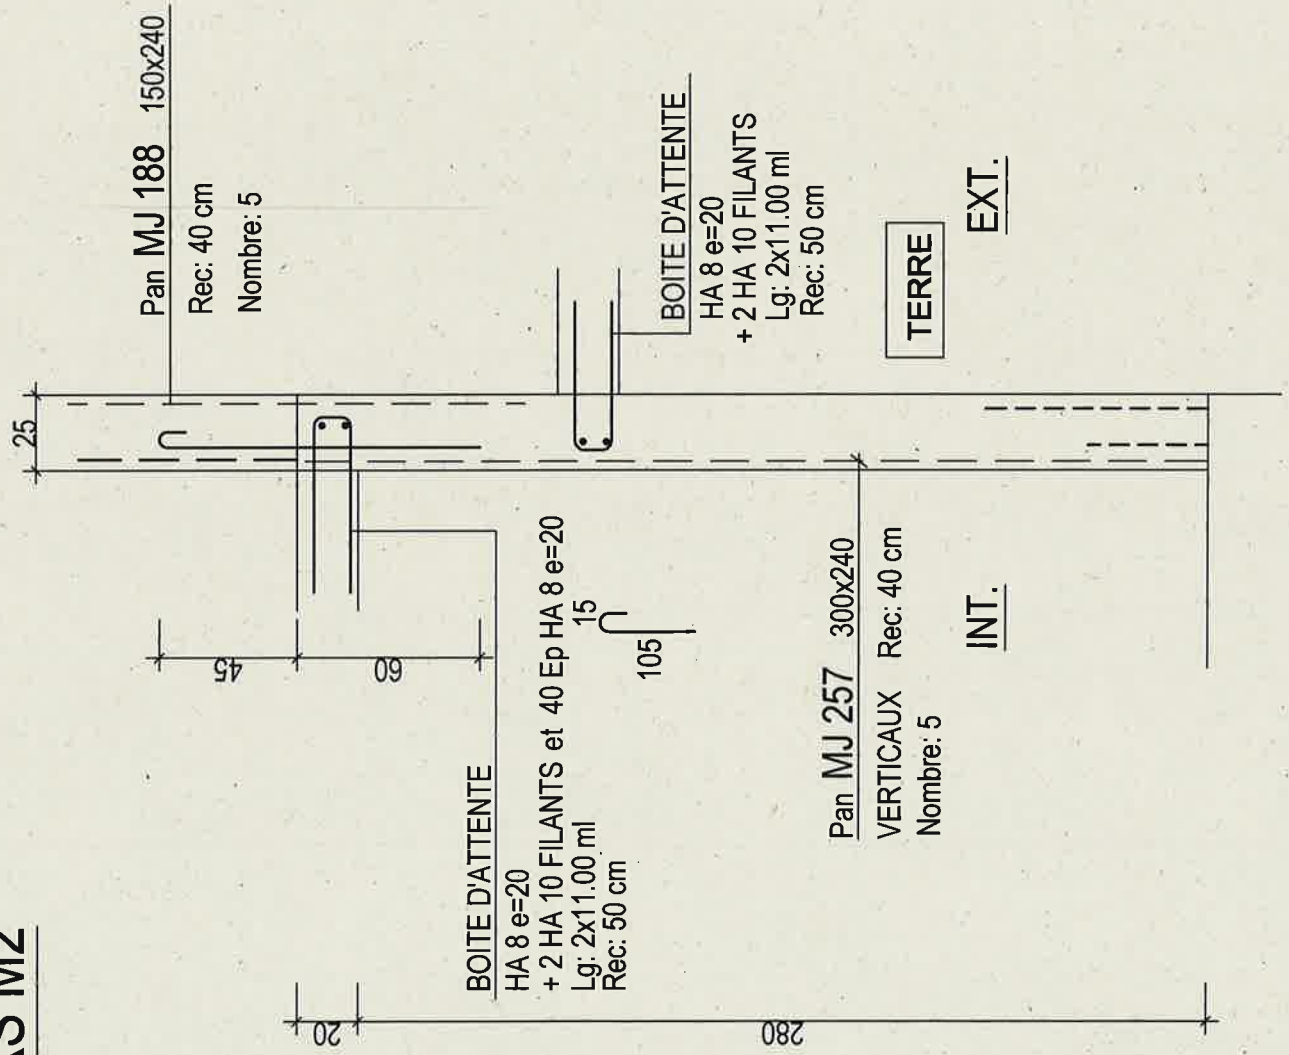


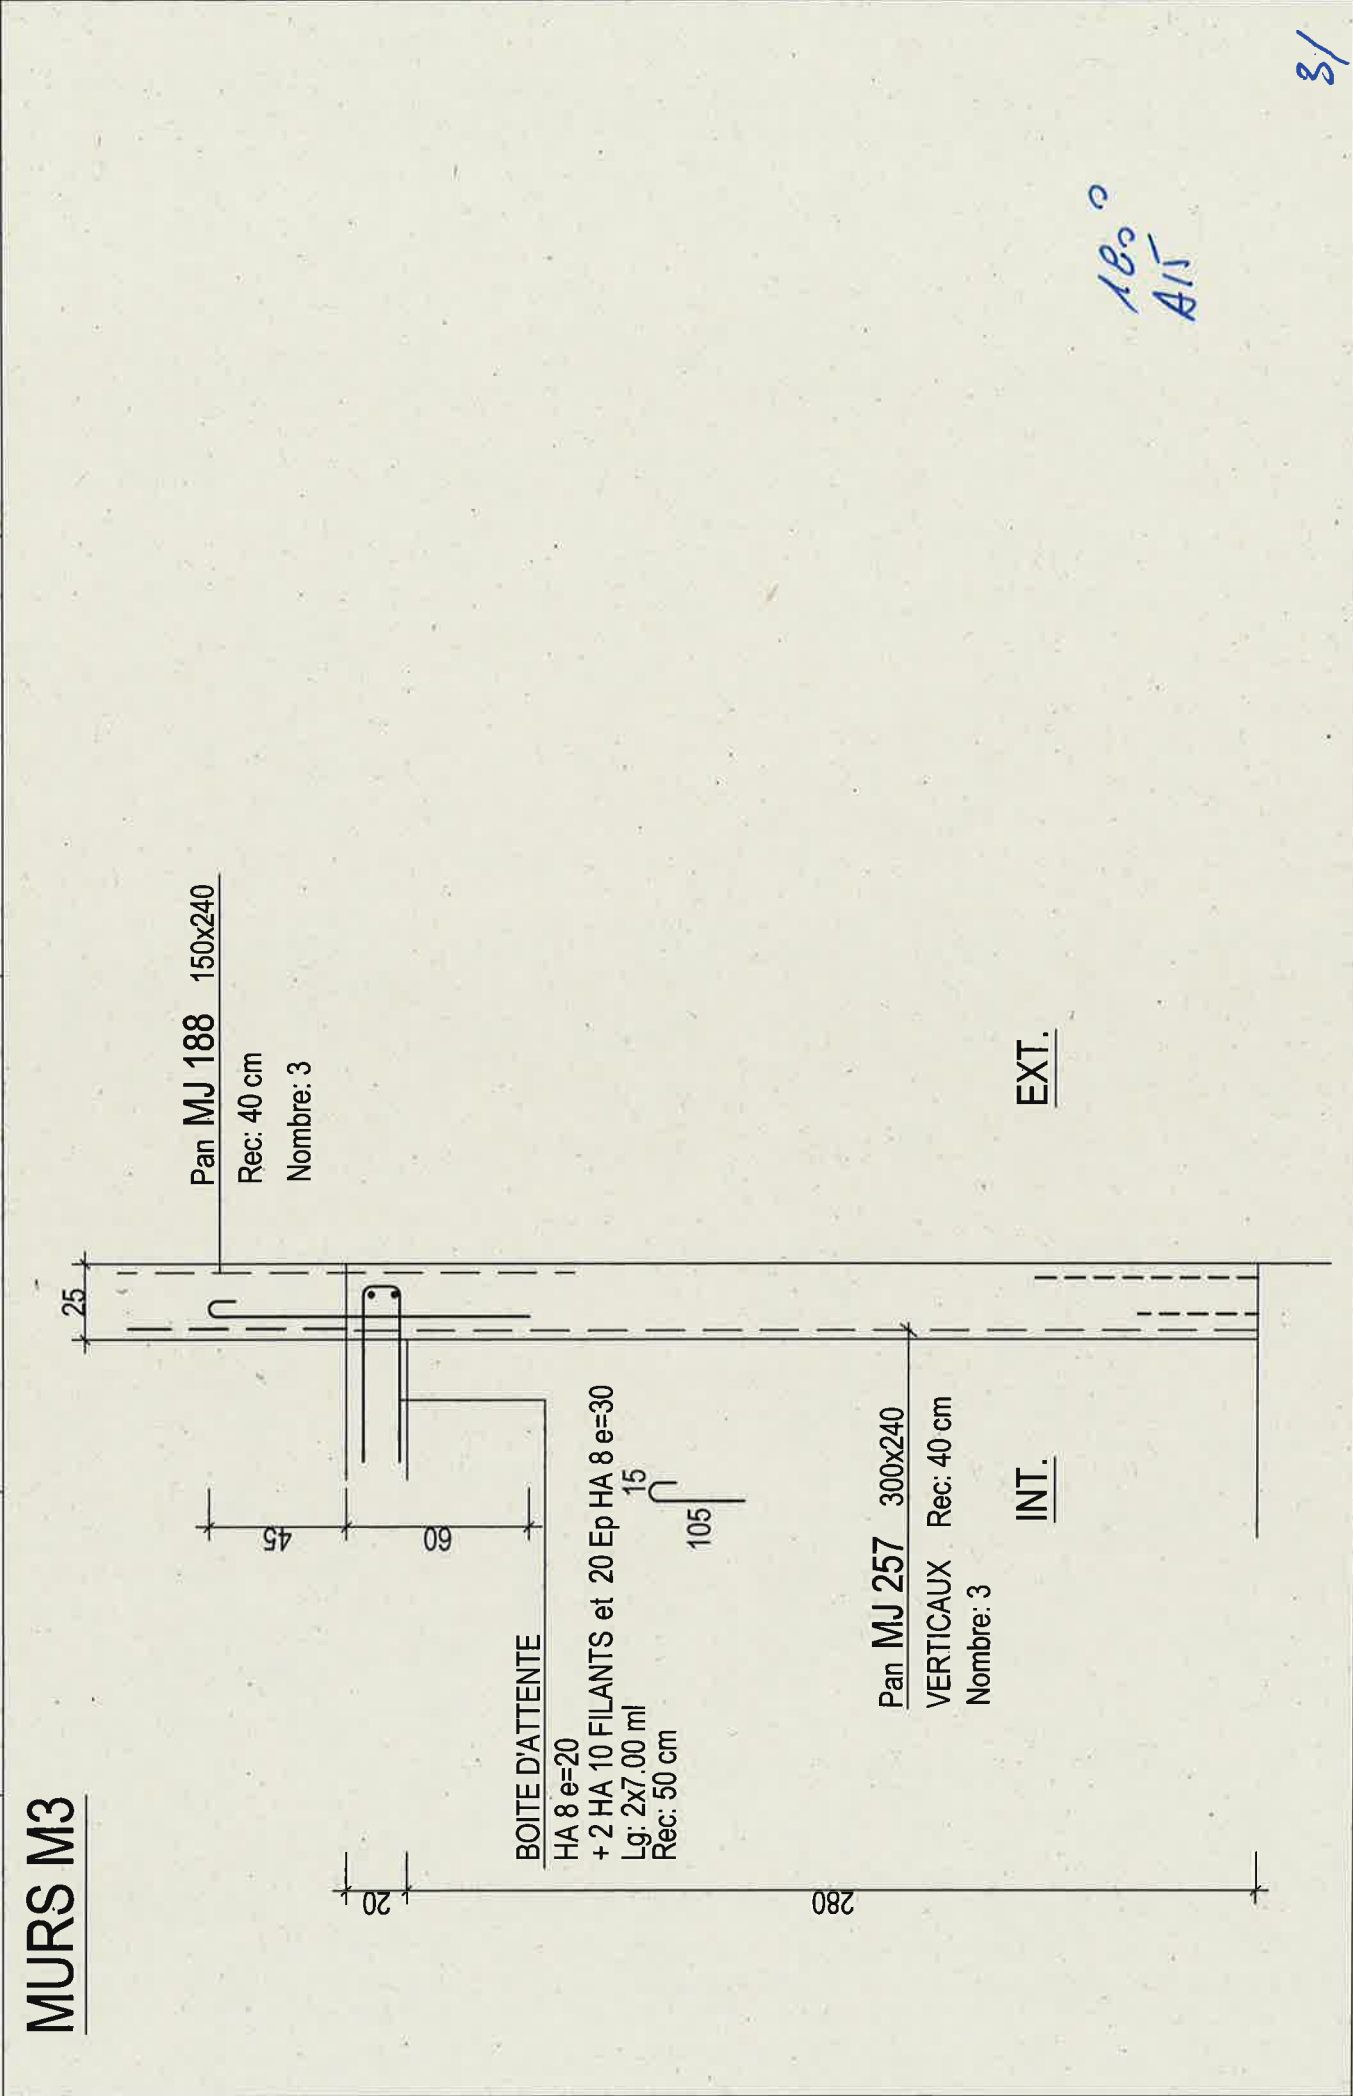


MURS M4

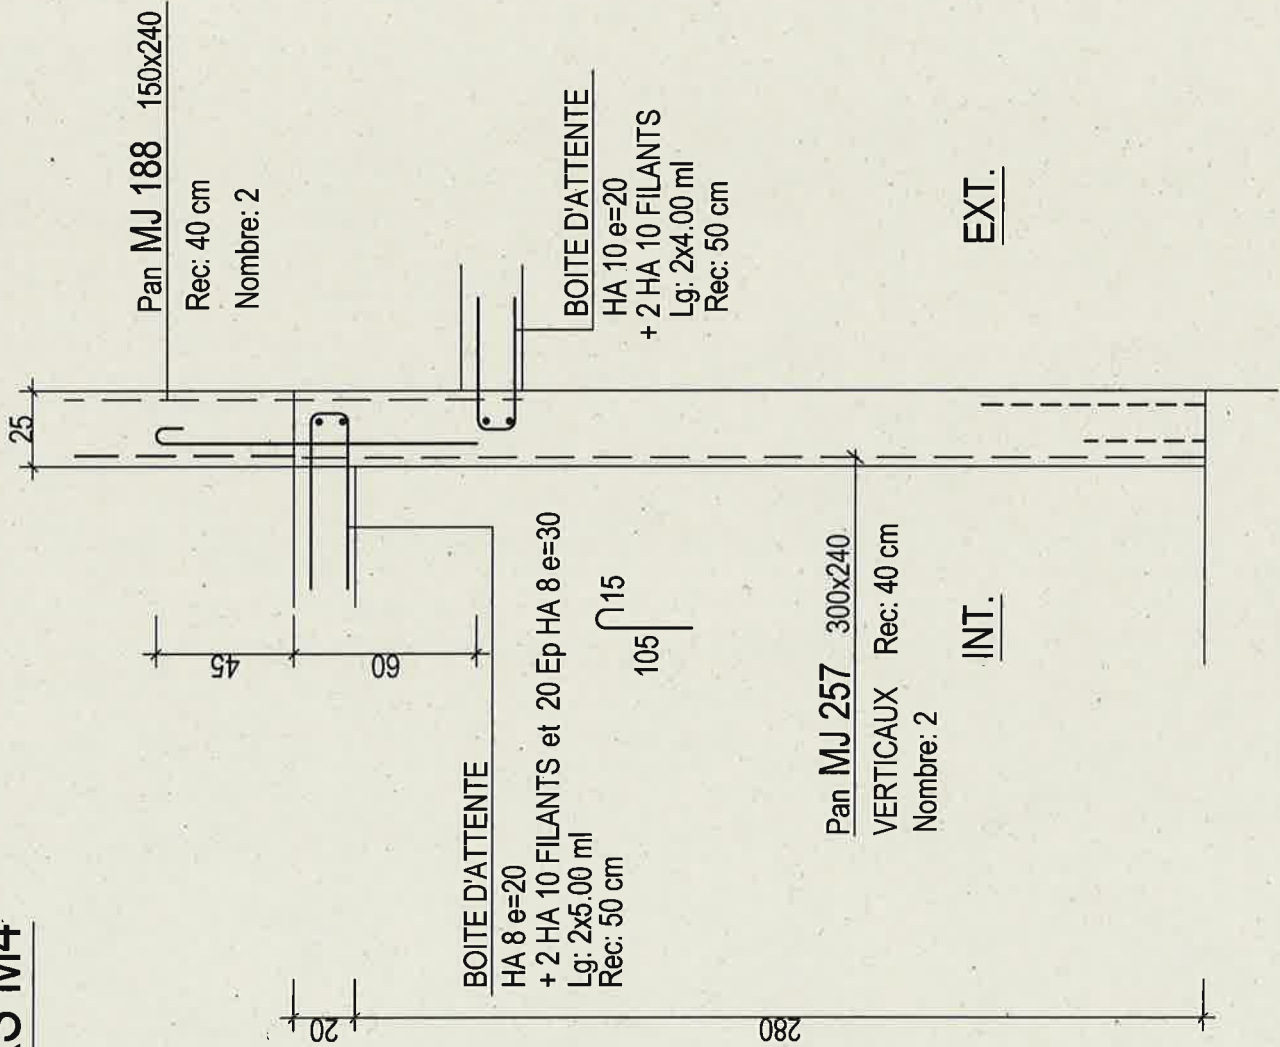

180°
A15

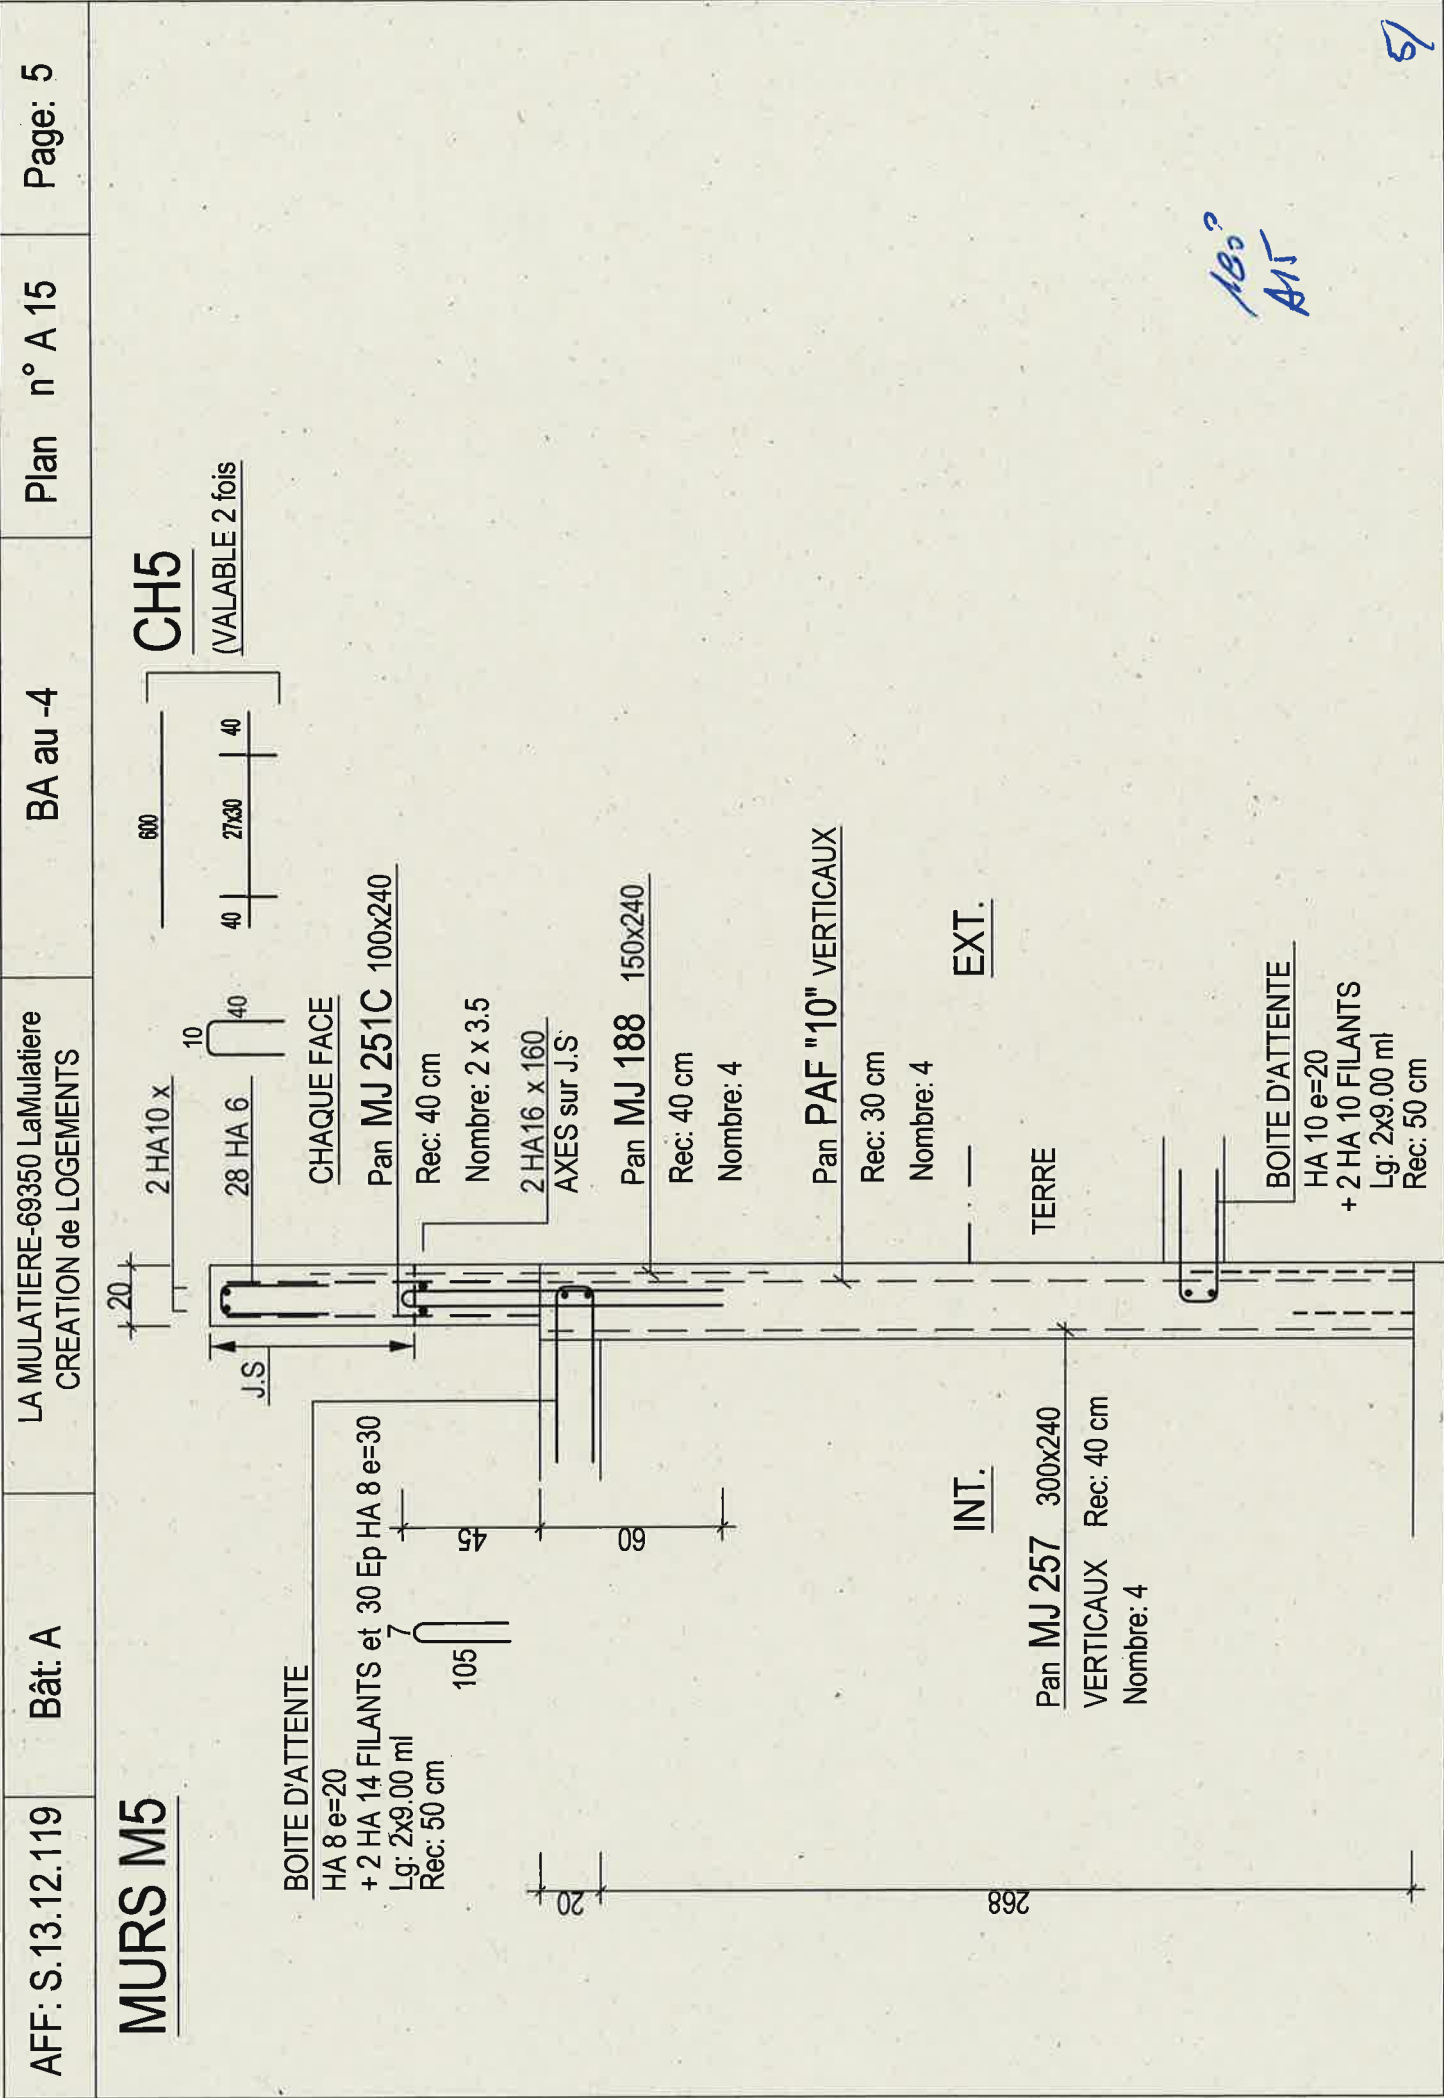


MURS M5 au DROIT DE L'ESCALIER

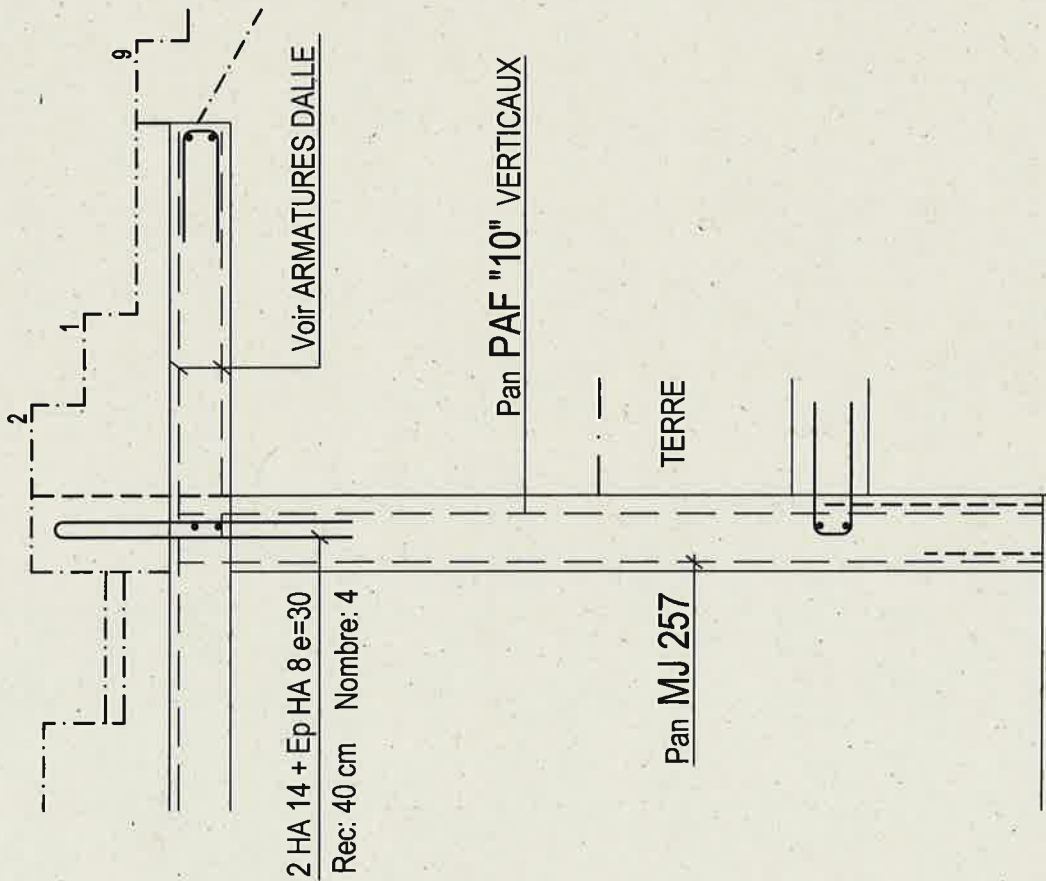

180°
A15

AFF: S.13.12.119	Bât: A	LA MULATIERE-69350 LaMulatiere CREATION de LOGEMENTS	BA au -4	Plan n° A 15	Page: 7
MURS M6 CHAQUE FACE Pan MJ 251C 100x240 Rec: 40 cm Nombre: 2 x 1.5 Pan PAF "10" VERTICAUX Nombre: 1.5 Rec: 40 cm EXT. INT. 18° A15 71					


MURS M7

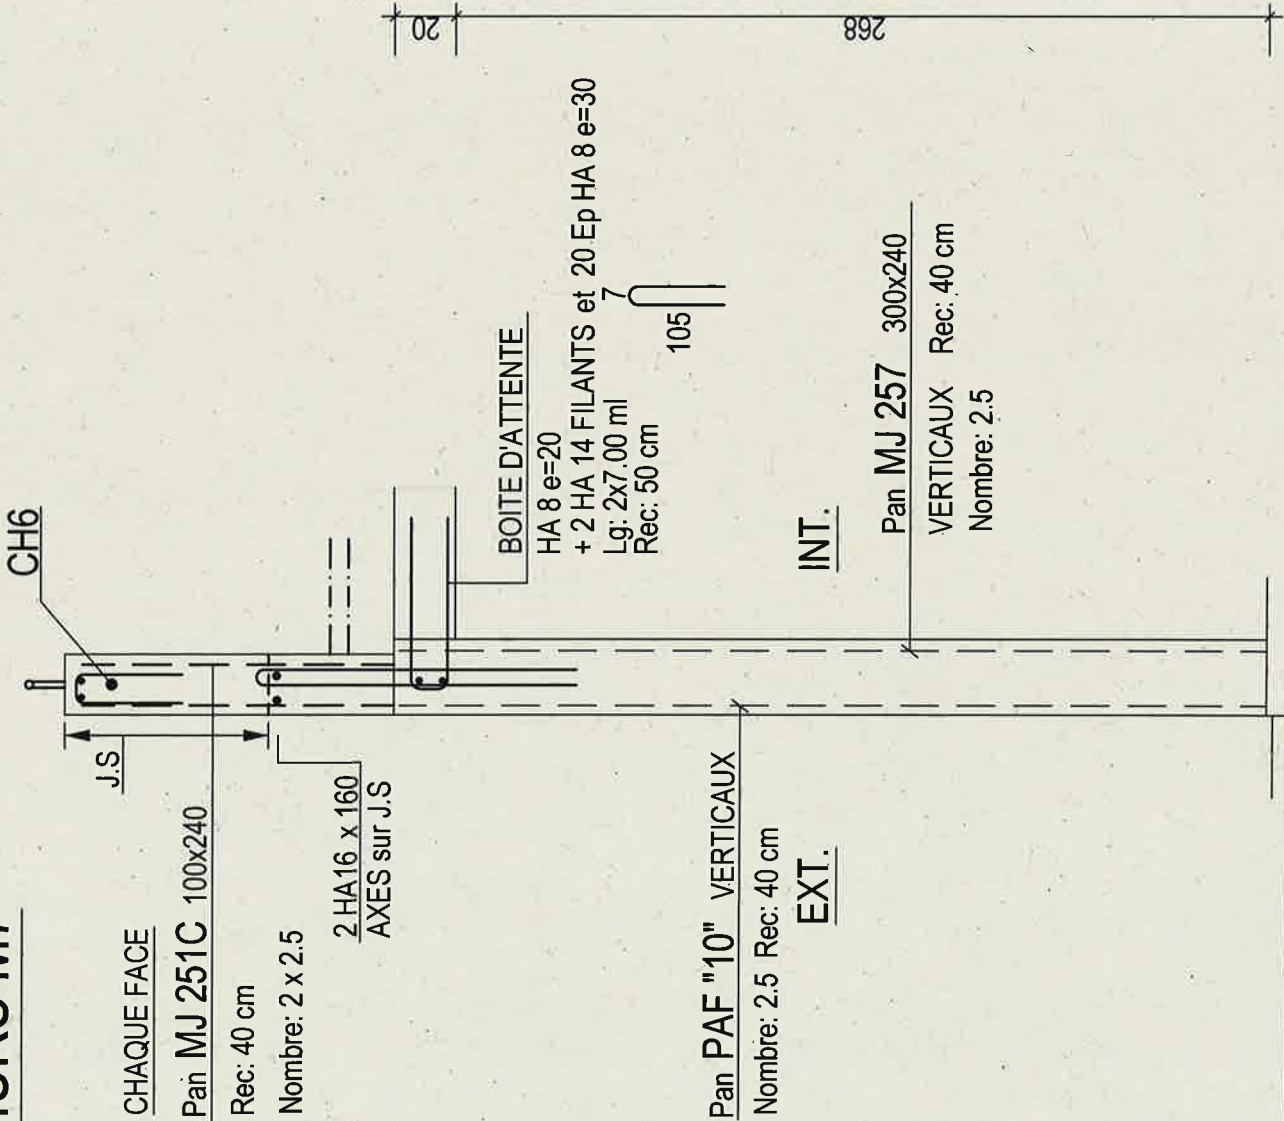

120°
A15

8/

MURS M8

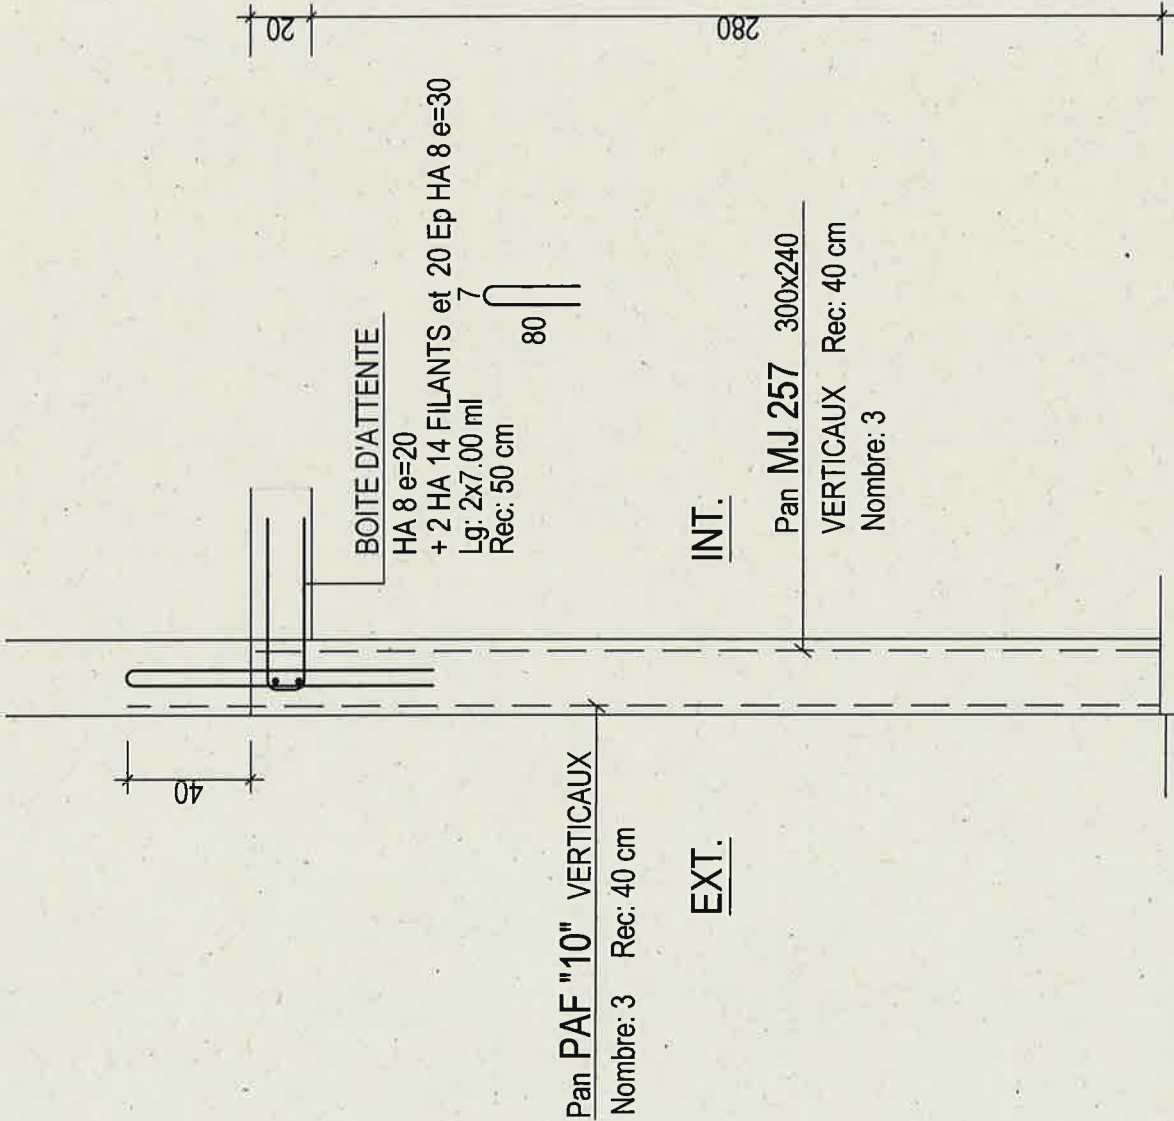

180°
A15


MURS M8

ELEVATION EXTERIEURE

Ech: 1/50


COUPEB

Ech: 1/50

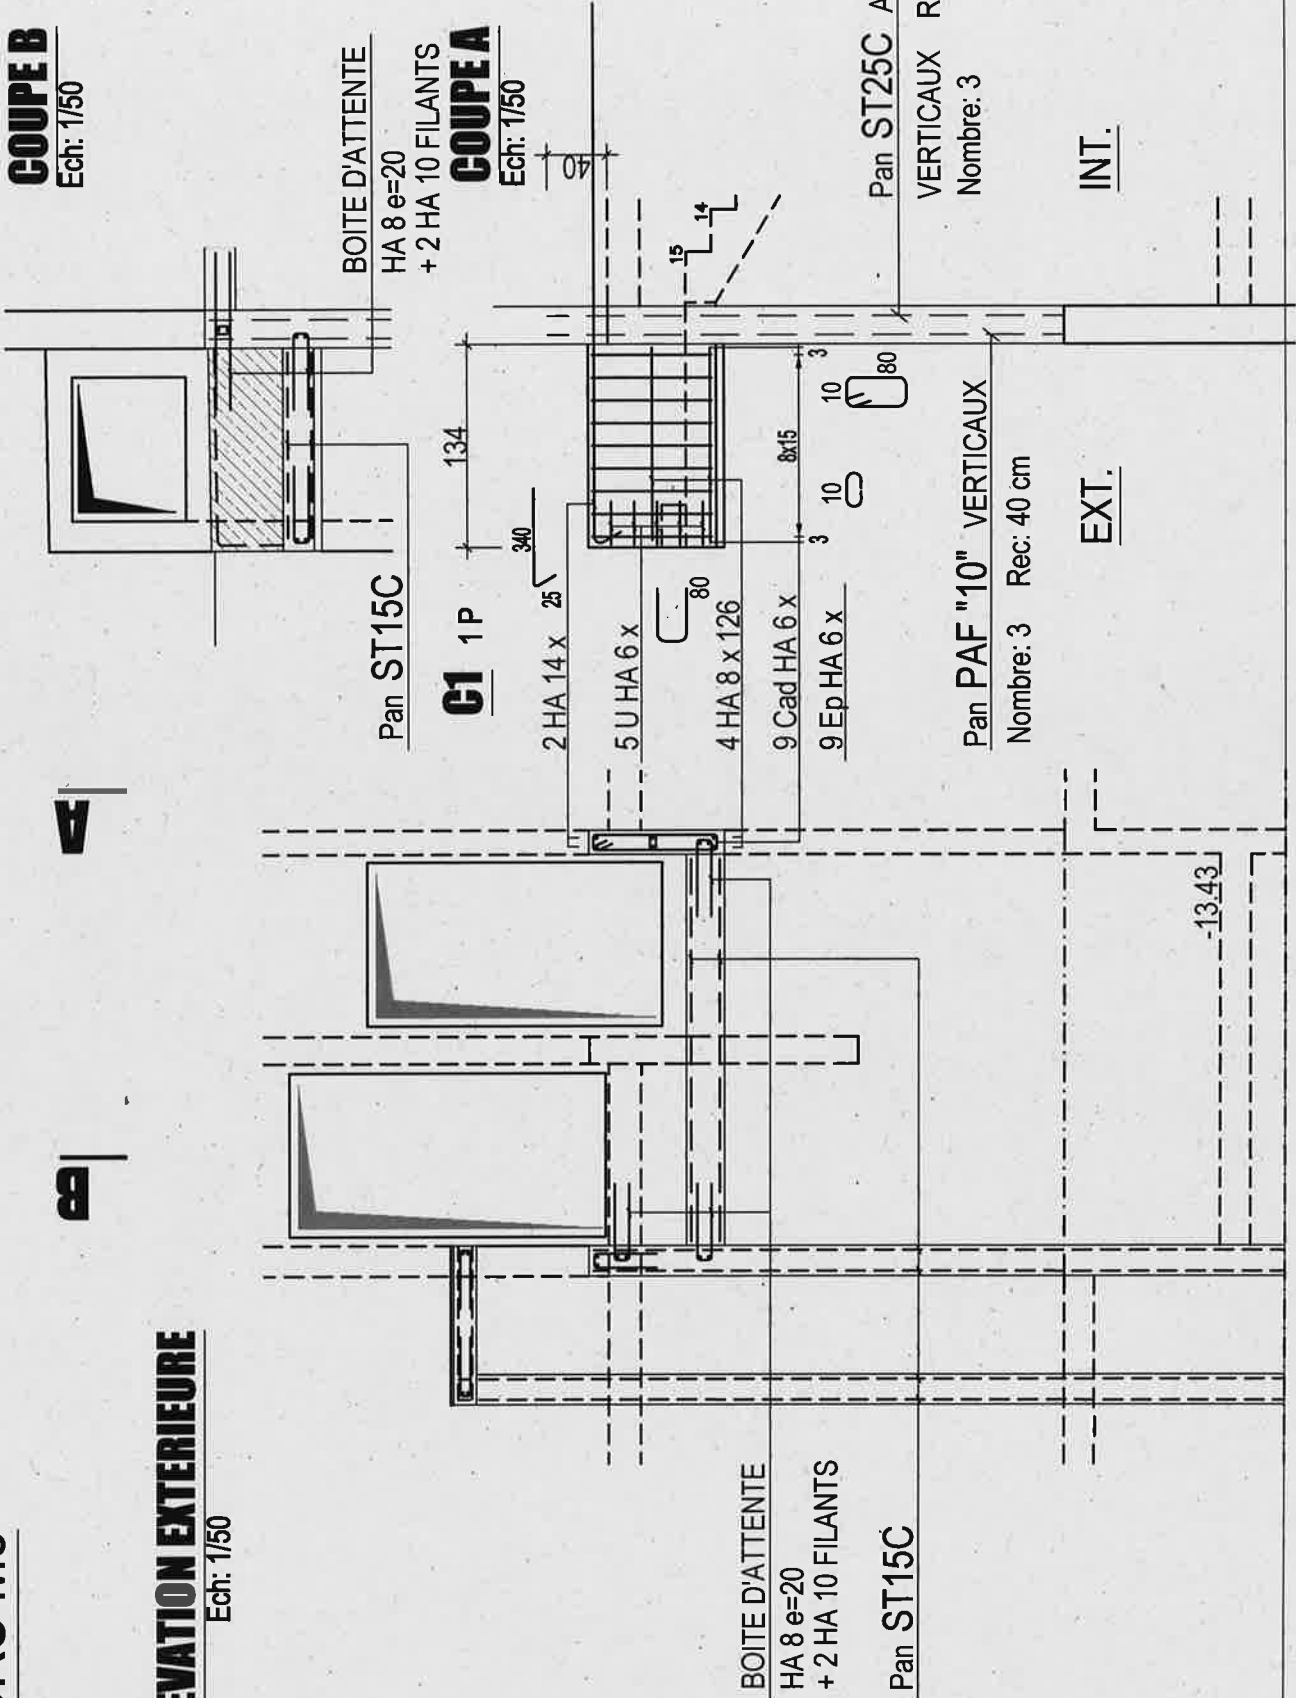

AFF: S.13.12.119	Bât: A	LA MULATIERE-69350 LaMulatiere CREATION de LOGEMENTS	BA au -4	Plan n° A 15	Page: 11
MURS M9 BOITE D'ATTENTE HA 8 e=20 + 2 HA 10 FILANTS et 70 Ep HA 8 e=30 Lg: 2x22.00 ml Rec: 50 cm INT. Pan MJ 385 300x240 VERTICAUX Rec: 40 cm Nombre: 11 18° A15 [Signature]					


MURS M10

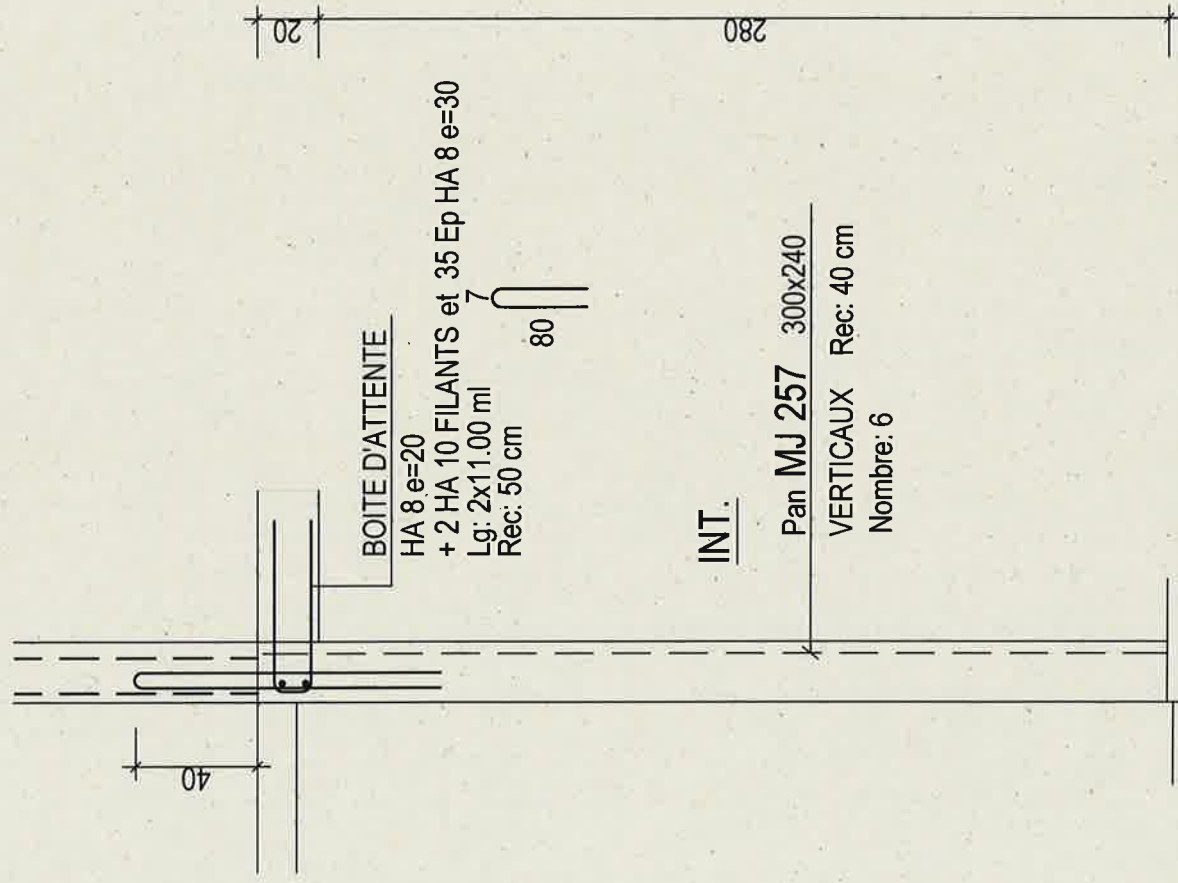

MURS M1 à M10

DETAILS D'ANGLES

ANGLES MURS



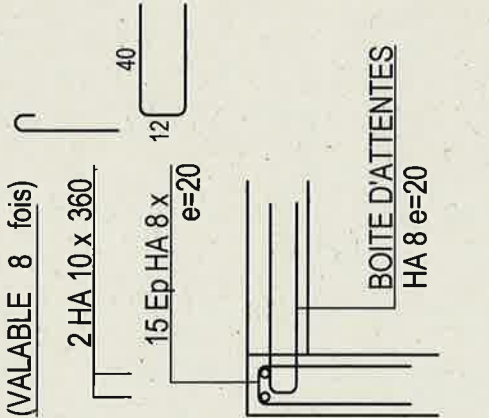


186°
A15
13/

MURS EXTERIEURS

ANGLES MURS

ARMATURES TETES DE MURS
et OUVERTURES

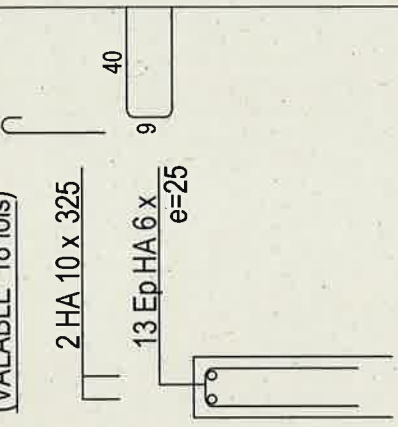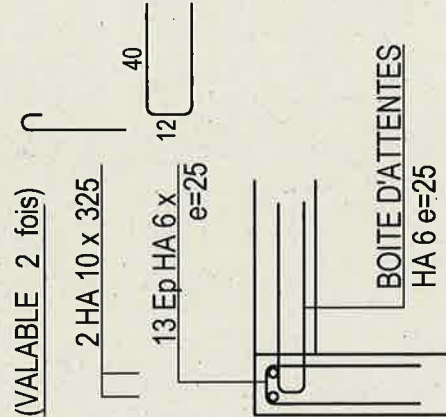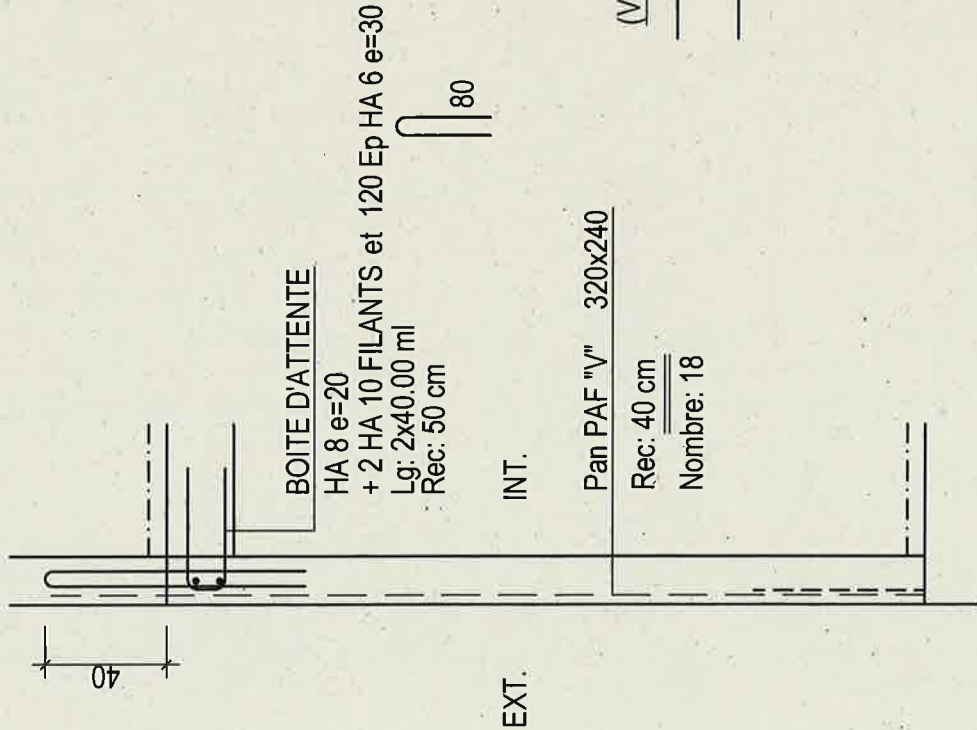

EXT.



INT.

Pan PAF "V" 320x240
Rec: 40 cm
Nombre: 18

ARMATURES REJINGOT

(VALABLE 1 fois)

A COUPER SUIVANT OUVERTURES

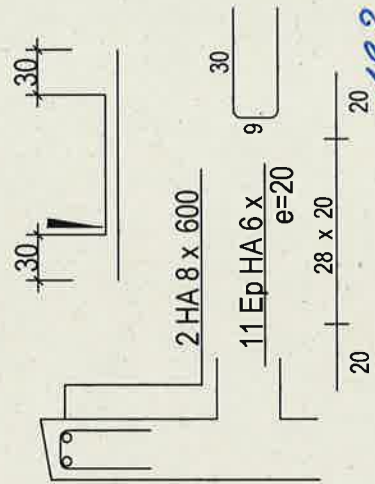
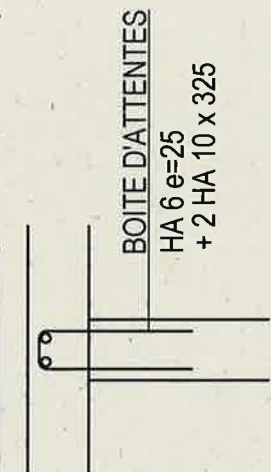


1832
815


141

MURS INTERIEURS AVEC CONTINUITE


ARMATURES TETES DE MURS

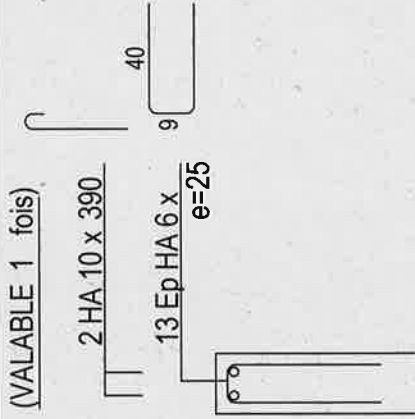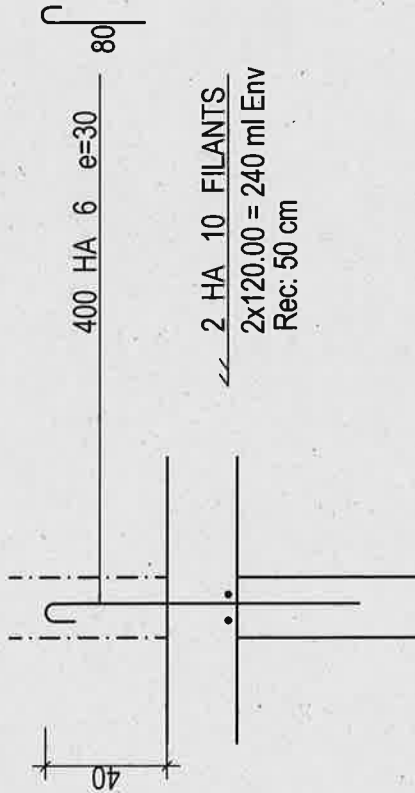

ANGLES MURS

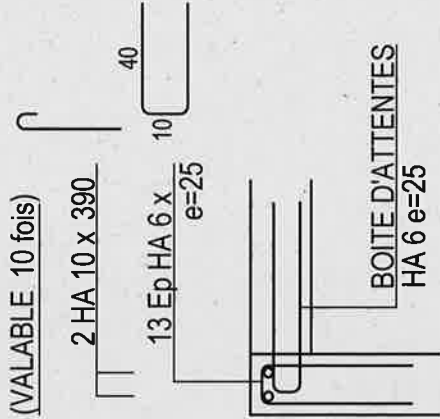

(VALABLE 5 fois)

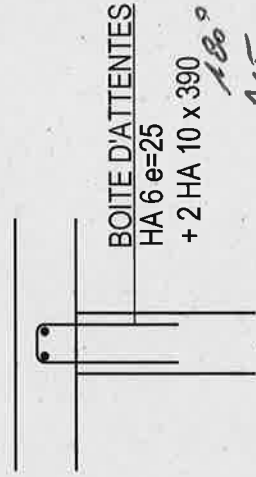


10/

130


115

POUTRE VOILE : PV1

ELEVATION

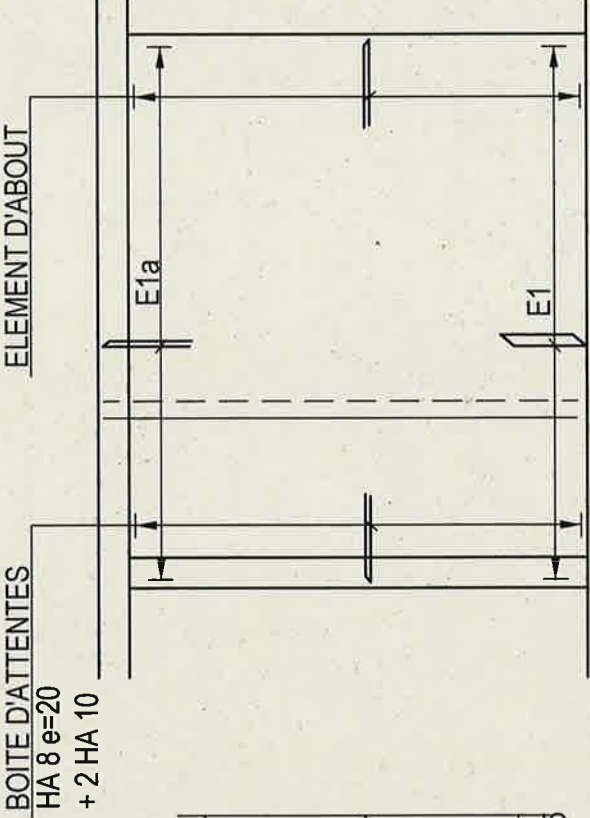


E1a Nombre: 1

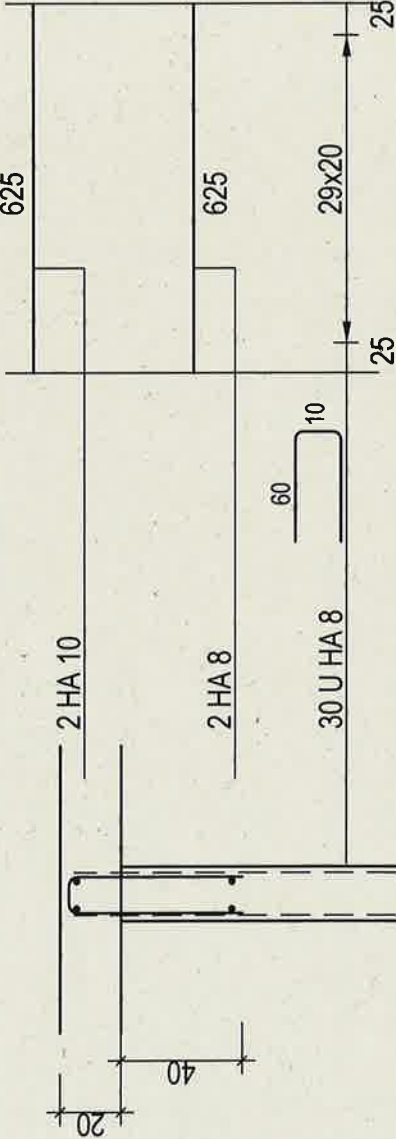

CHAQUE FACE
Pan ST25C A COUPER

Rec: 40 cm
Nombre: 2x3


E1 Nombre: 1

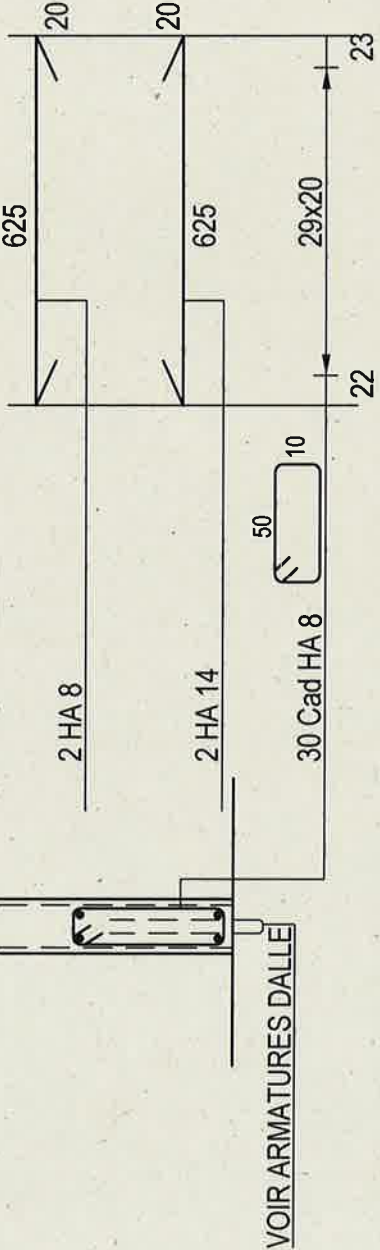

18°
AT
17/

POUTRE VOILE : PV2


ELEVATION

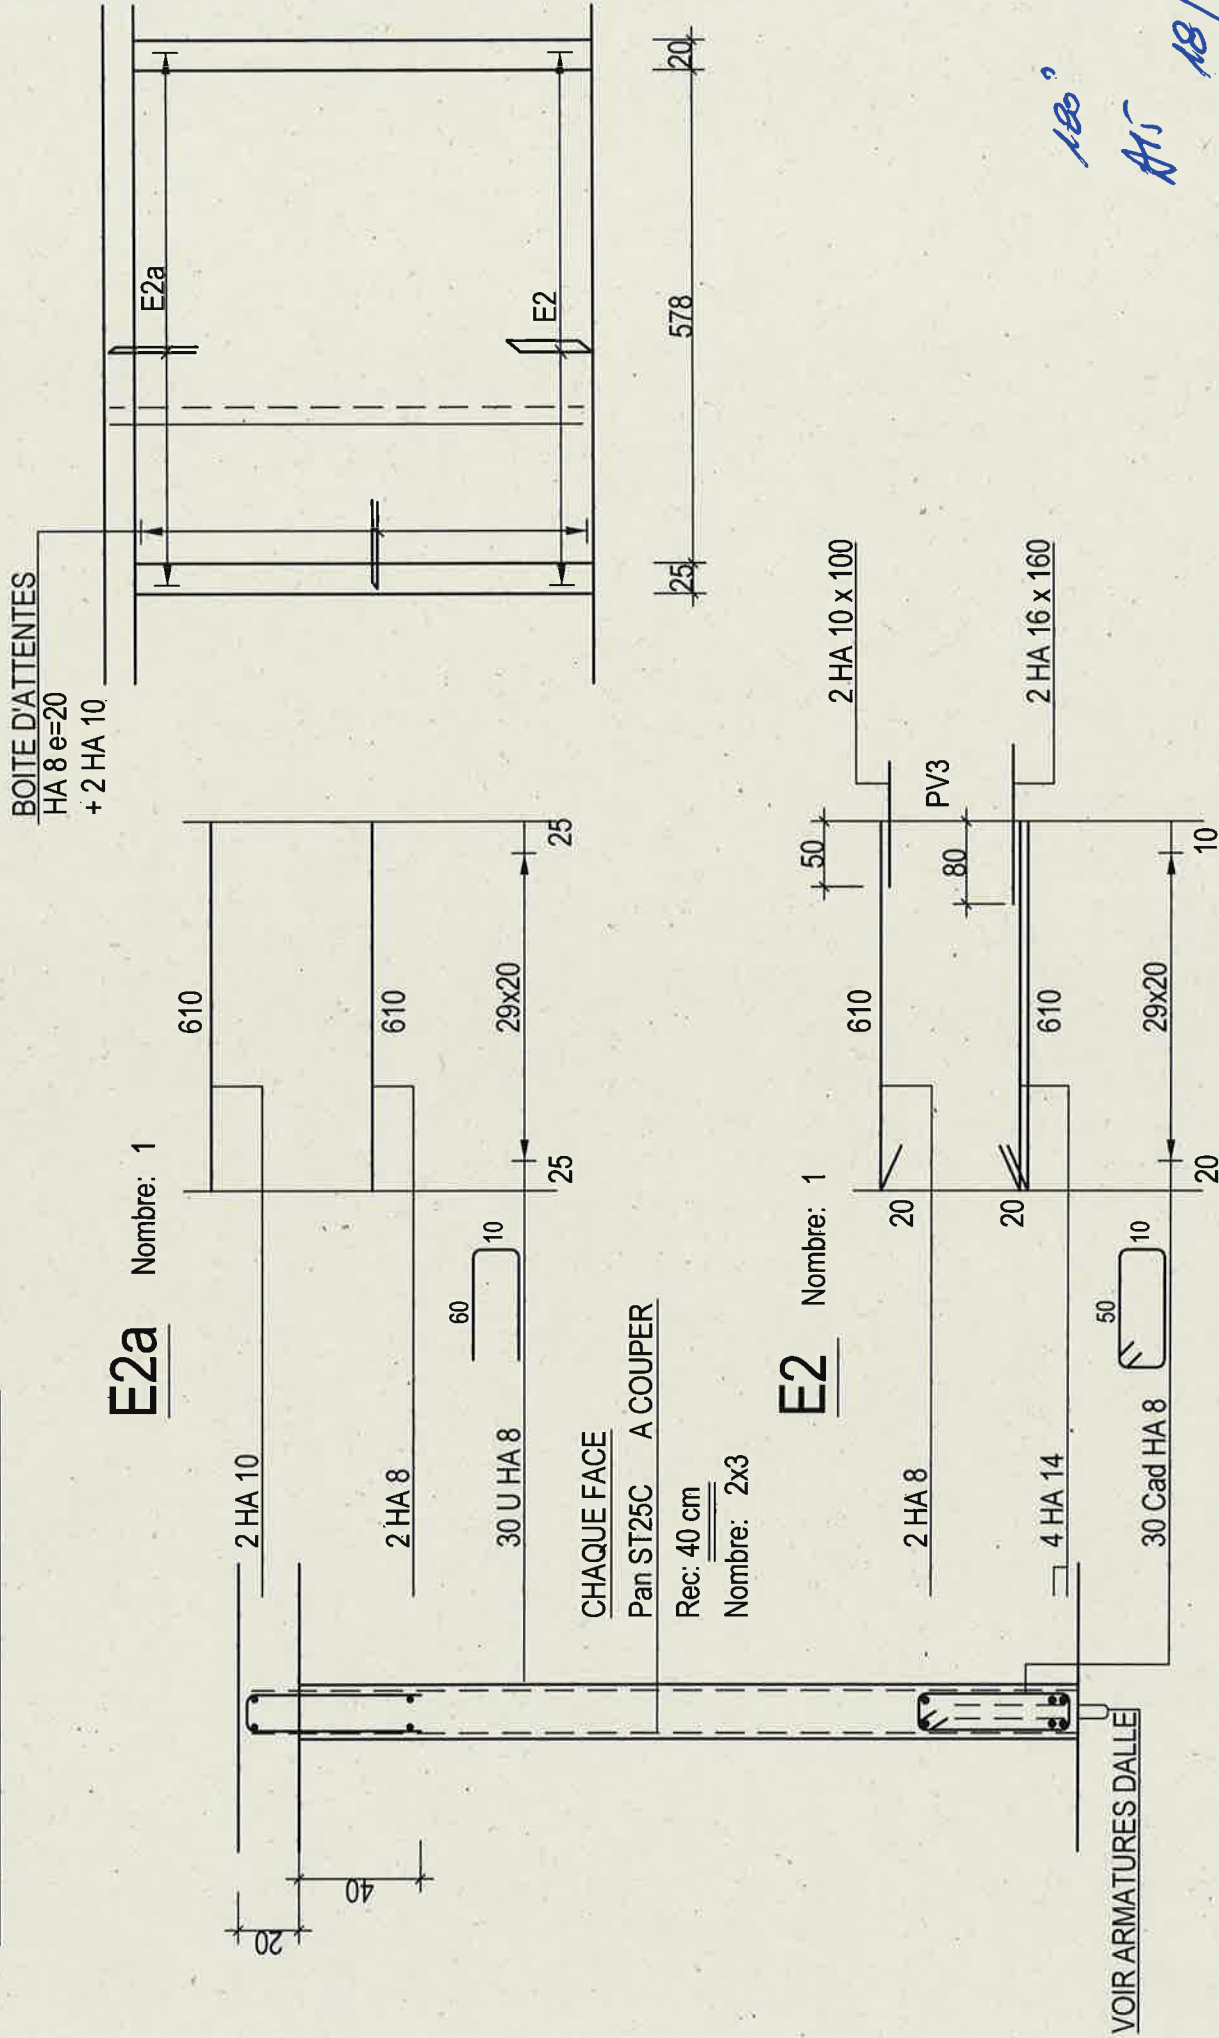

POUTRE VOILE : PV3

E3a

Nombre: 1

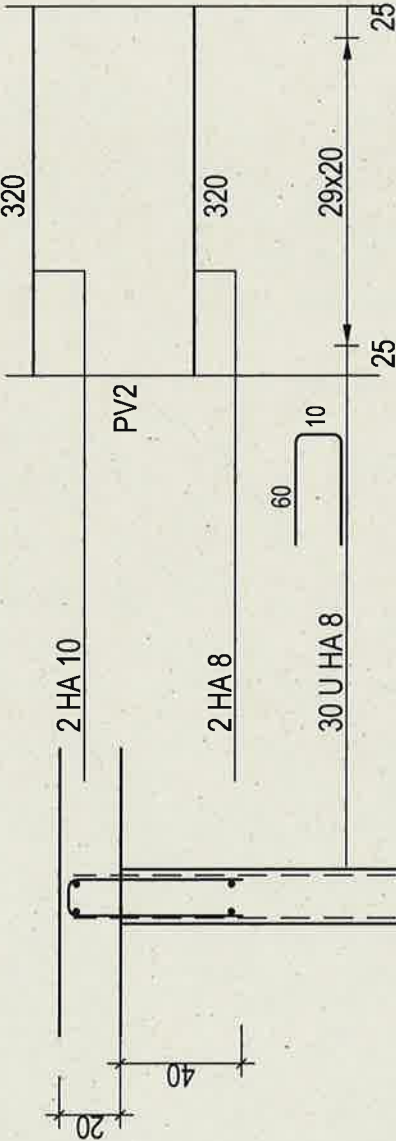

CHAQUE FACE


Pan ST25C A COUPER

Rec: 40 cm


Nombre: 2x3

E3

Nombre: 1

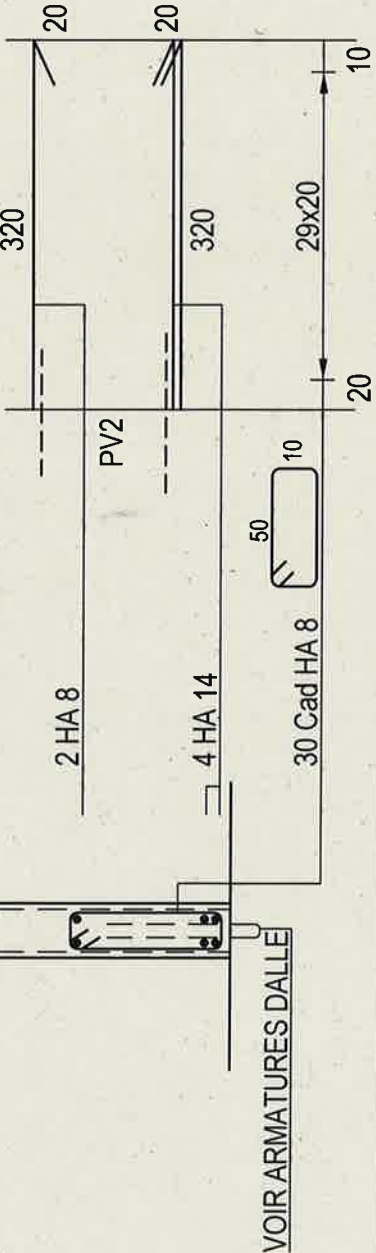

ELEVATION

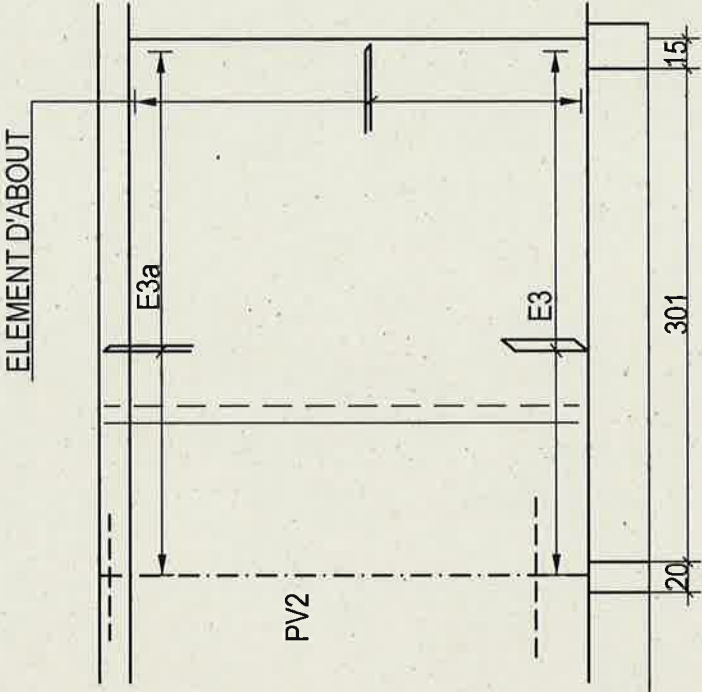


120°
A15
19/

POUTRE VOILE : PV4

ELEVATION


E4a

Nombre: 1

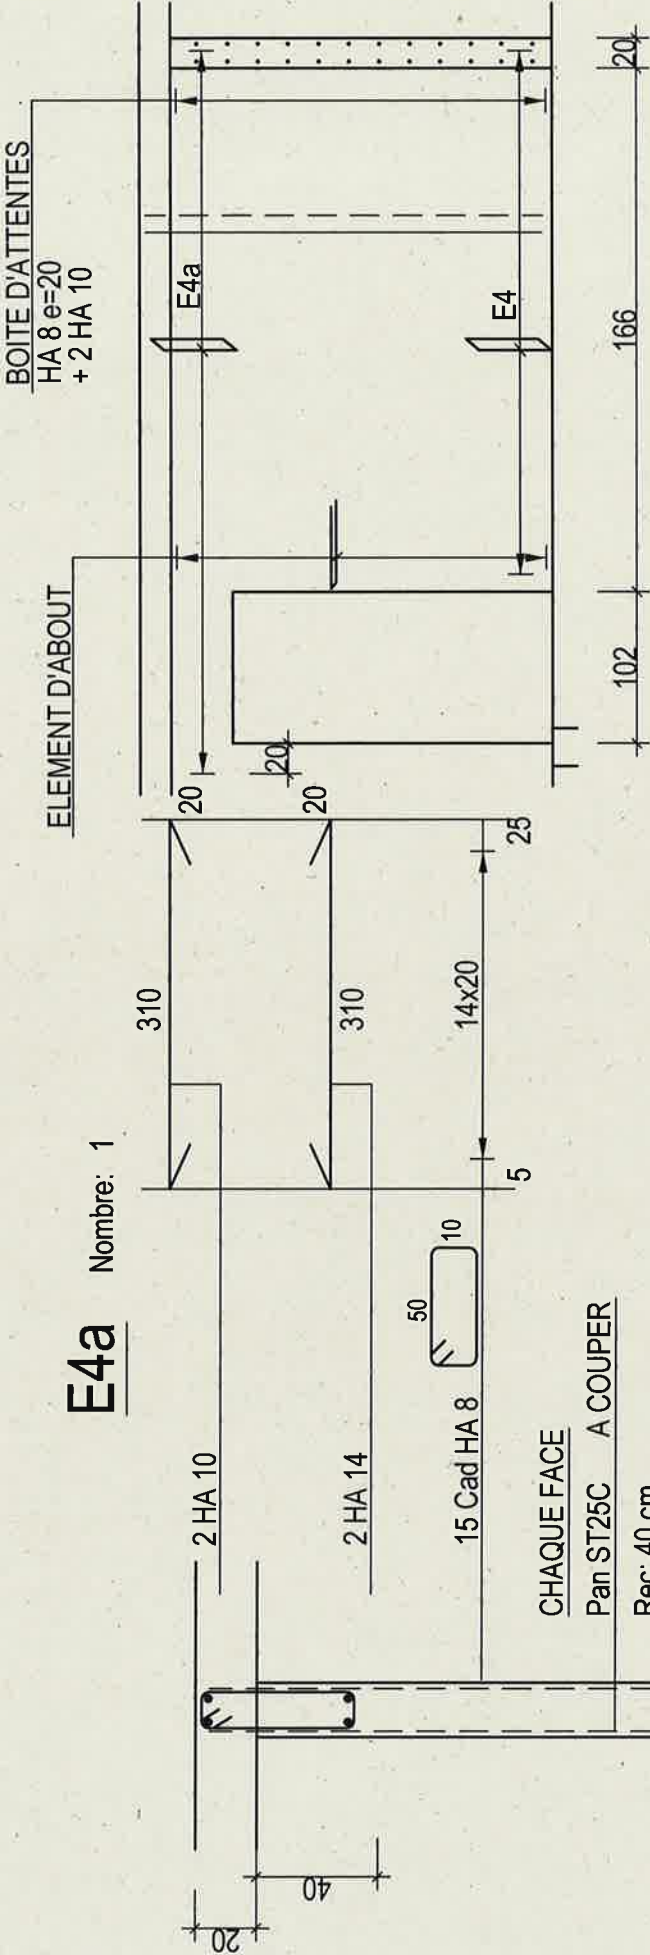

E4

Nombre: 1

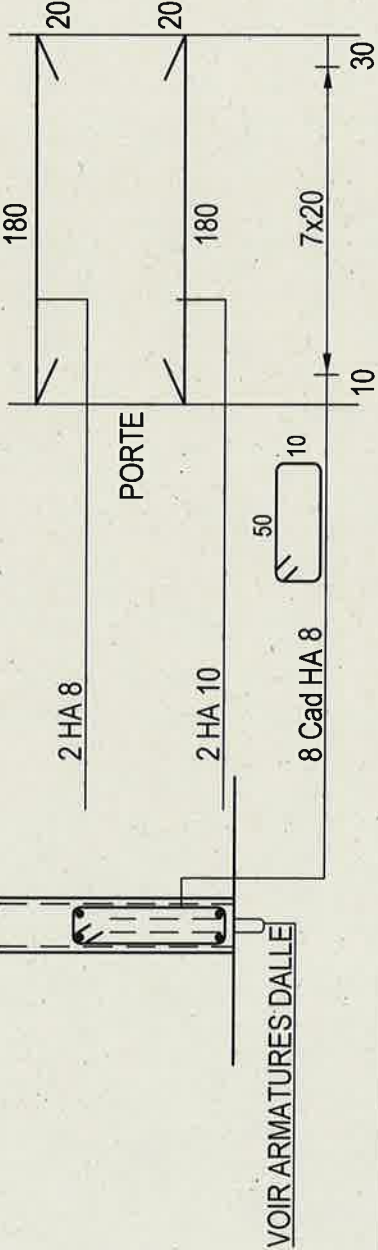


125°





415

20/

POUTRE VOILE : PV5 à PV.11

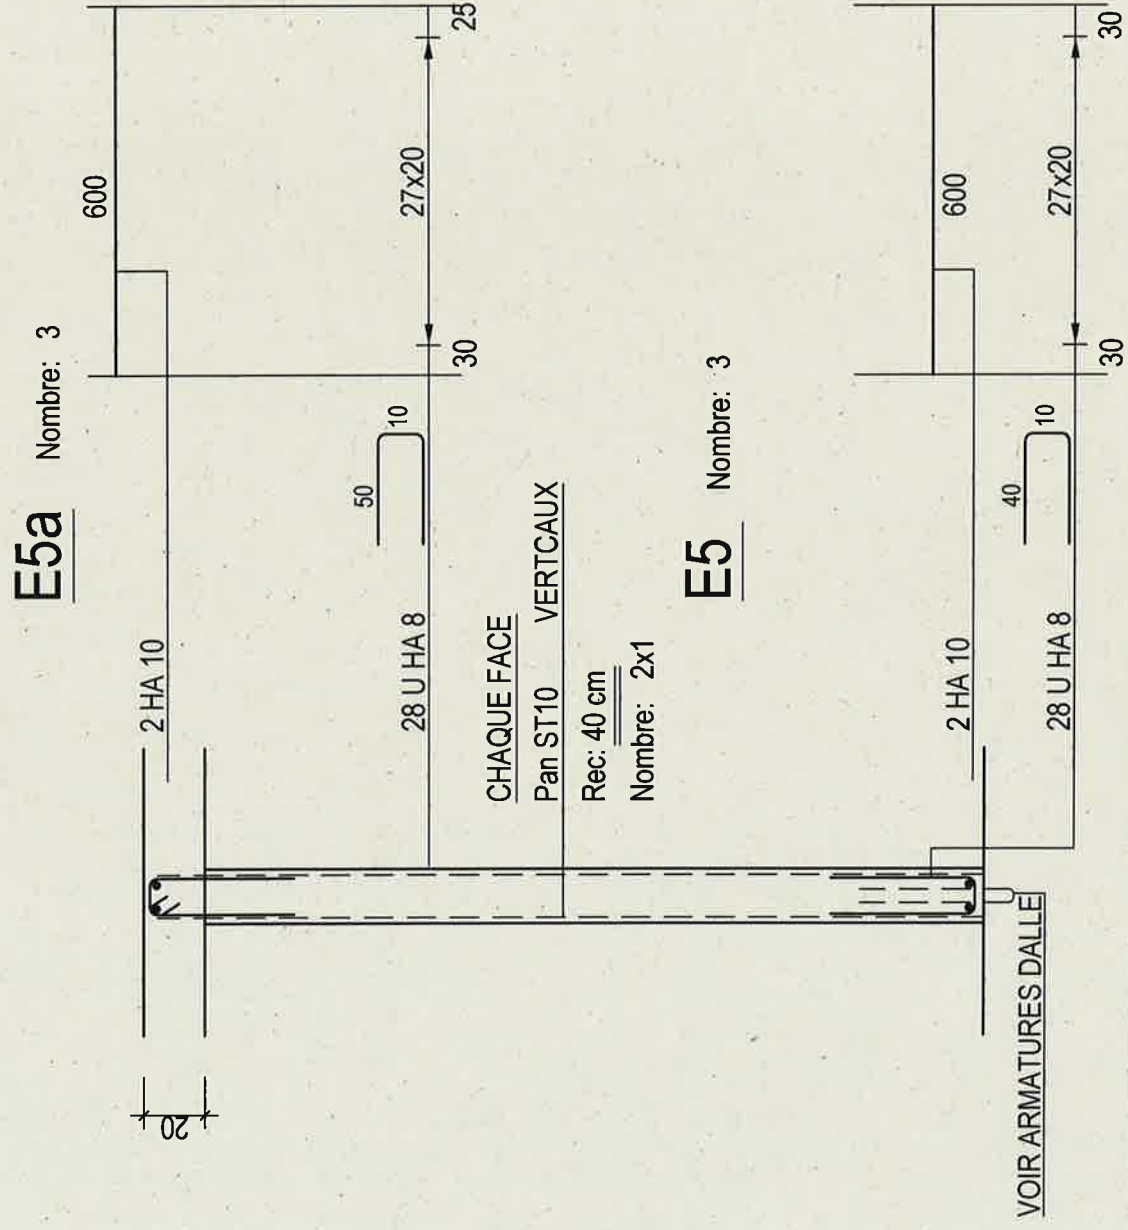


AFF: S.13.12.119	Bât: A	LA MULATIERE-69350 La Mulatiere CREATION de LOGEMENTS	BA au -4	Plan n° A 15	Page: 22
P1 à P17 20x80 			① 8 HA 12 x		
			②		
			③ 15 HA 6 x		
			④ 2x15 HA 6 x		
			⑤		
			⑥		
			⑦		
			⑧		
			⑨		
			⑩		
			⑪		
			⑫		
			⑬		12.3
			⑭		AR
			⑮		22/

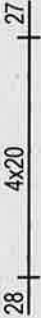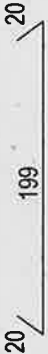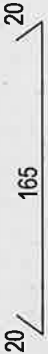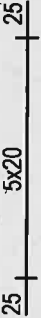AFF: S.13.12.119	Bât: A	LA MULATIERE-69350 La Mulatiere CREATION de LOGEMENTS	BA au -4	Plan n° A 15	Page: 23
<u>L</u> Nombre: 8  4 HA 10 5 Cad HA 6   	<u>La</u> Nombre: 2  4 HA 12 9 Cad HA 6   	<u>Lb</u> Nombre: 1  4 HA 10 7 Cad HA 6   	<u>LC</u> Nombre: 1  4 HA 10 6 Cad HA 6   	<i>1039</i> <i>A15</i> <i>23/</i>	

VENTILATIONS

COUPE HORIZONTALE

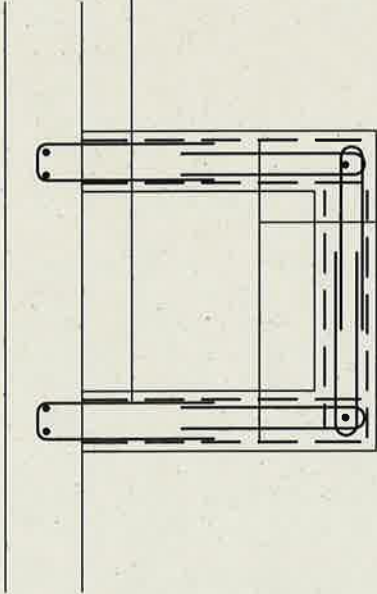


COUPE VERTICALE

BOITE D'ATTENTE

HA 8 e=20
+ 2 HA 10 FILANTS
Rec: 50 cm

E1 Nombre: 4
 1 HA 10 x 600

28 U HA 6

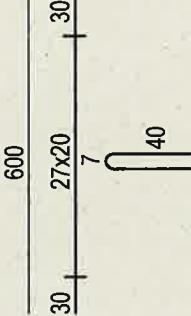

ChutePan MJ251C VERTICAUX
Rec: 40 cm

183°
A/15
26/