
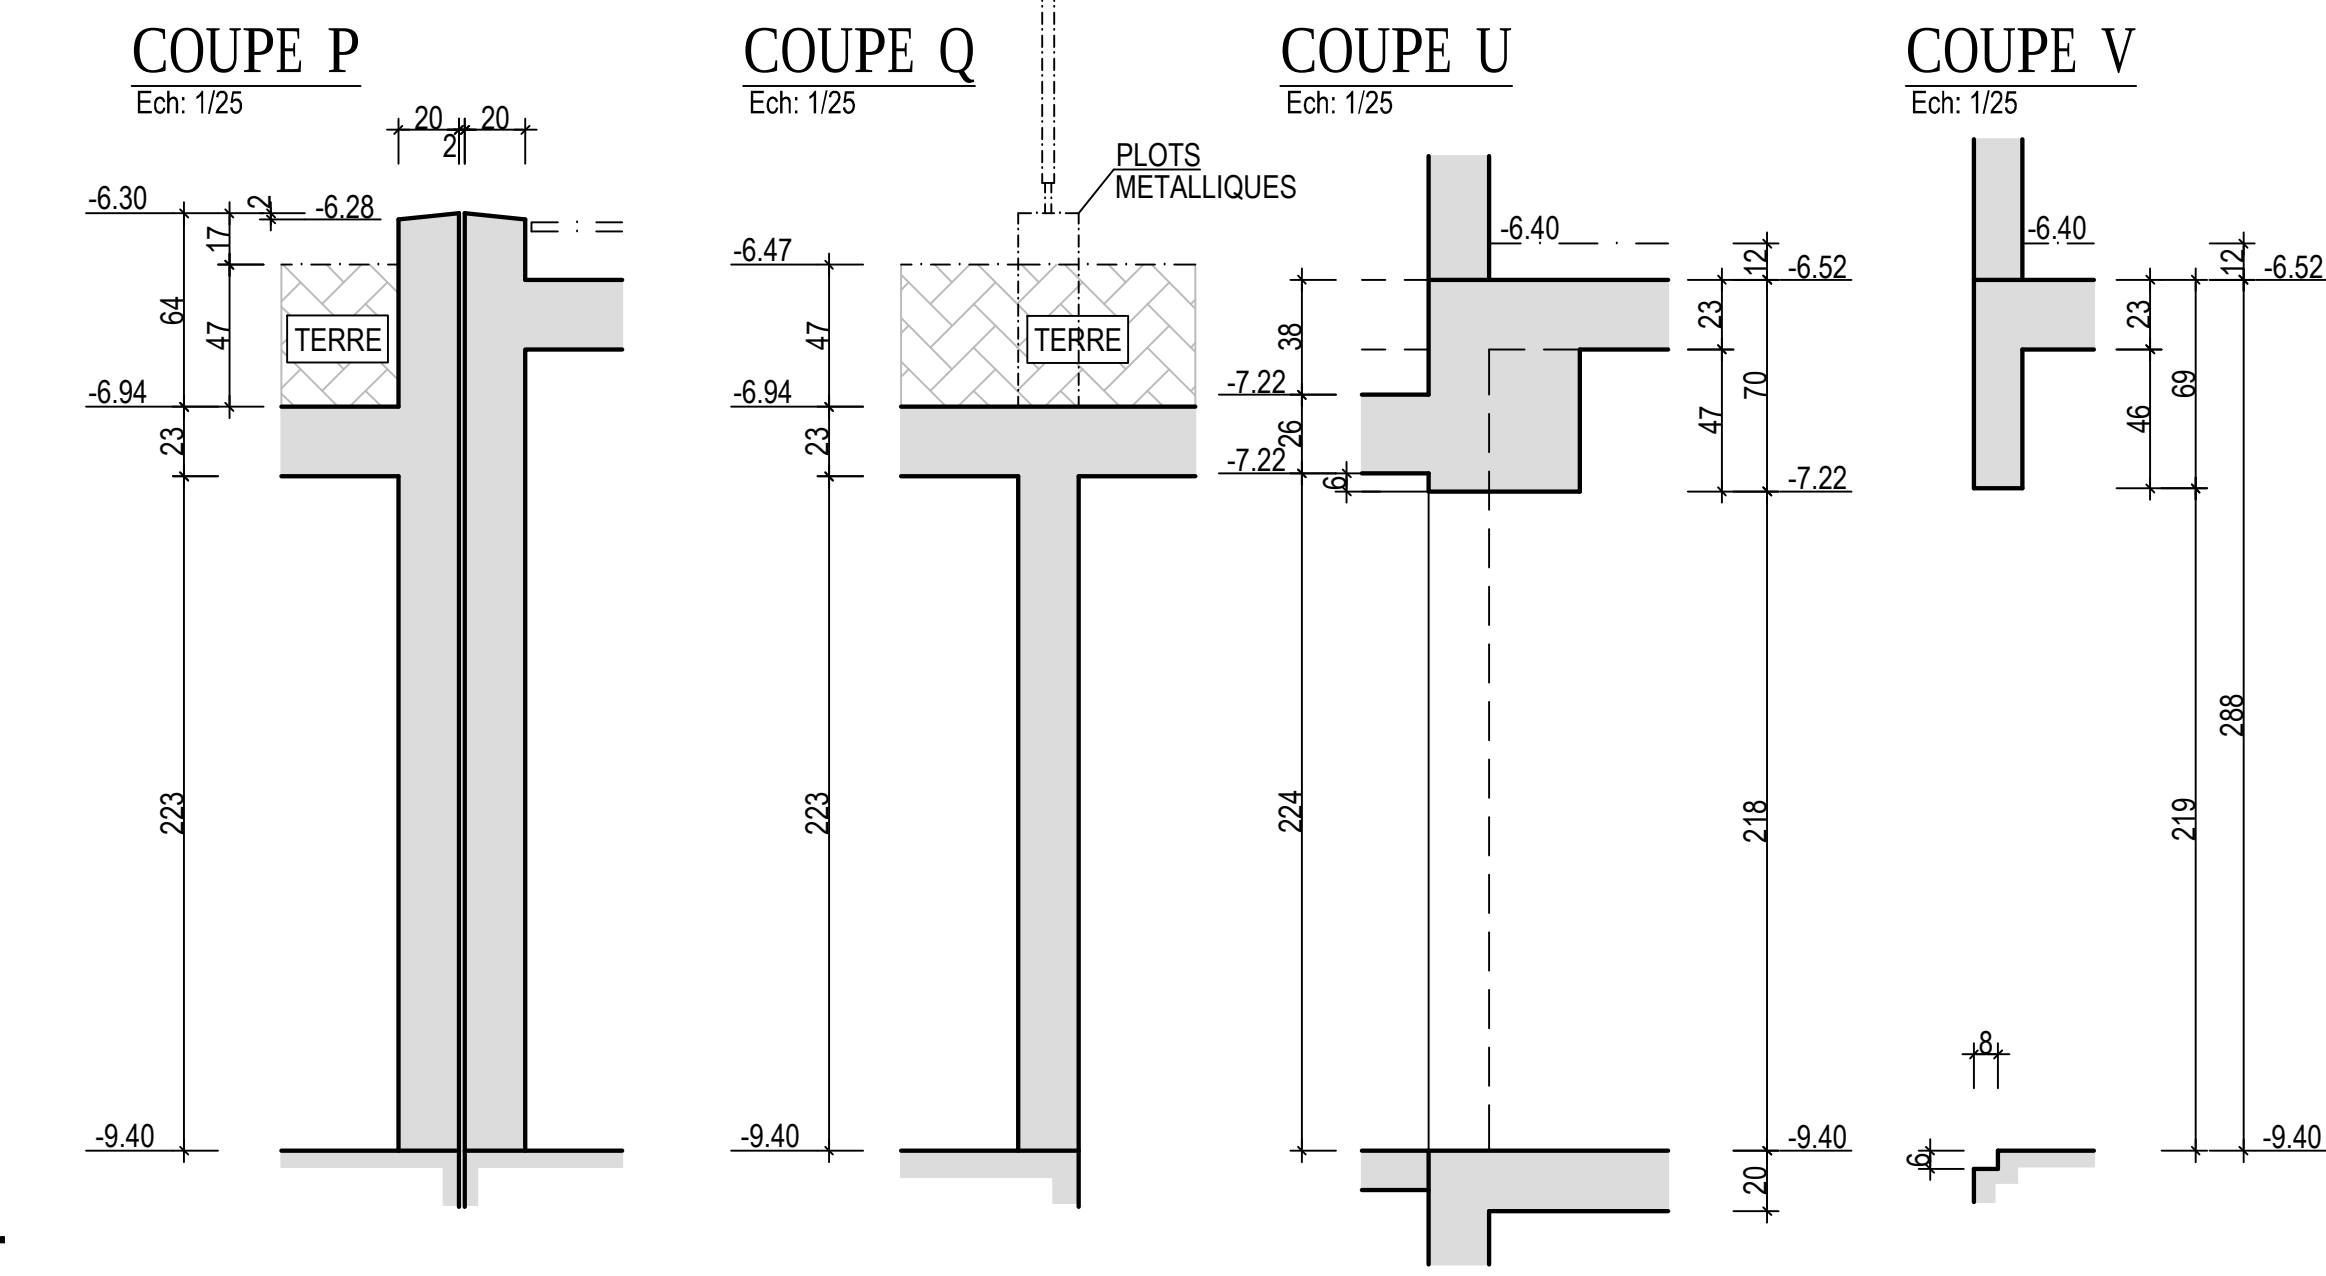
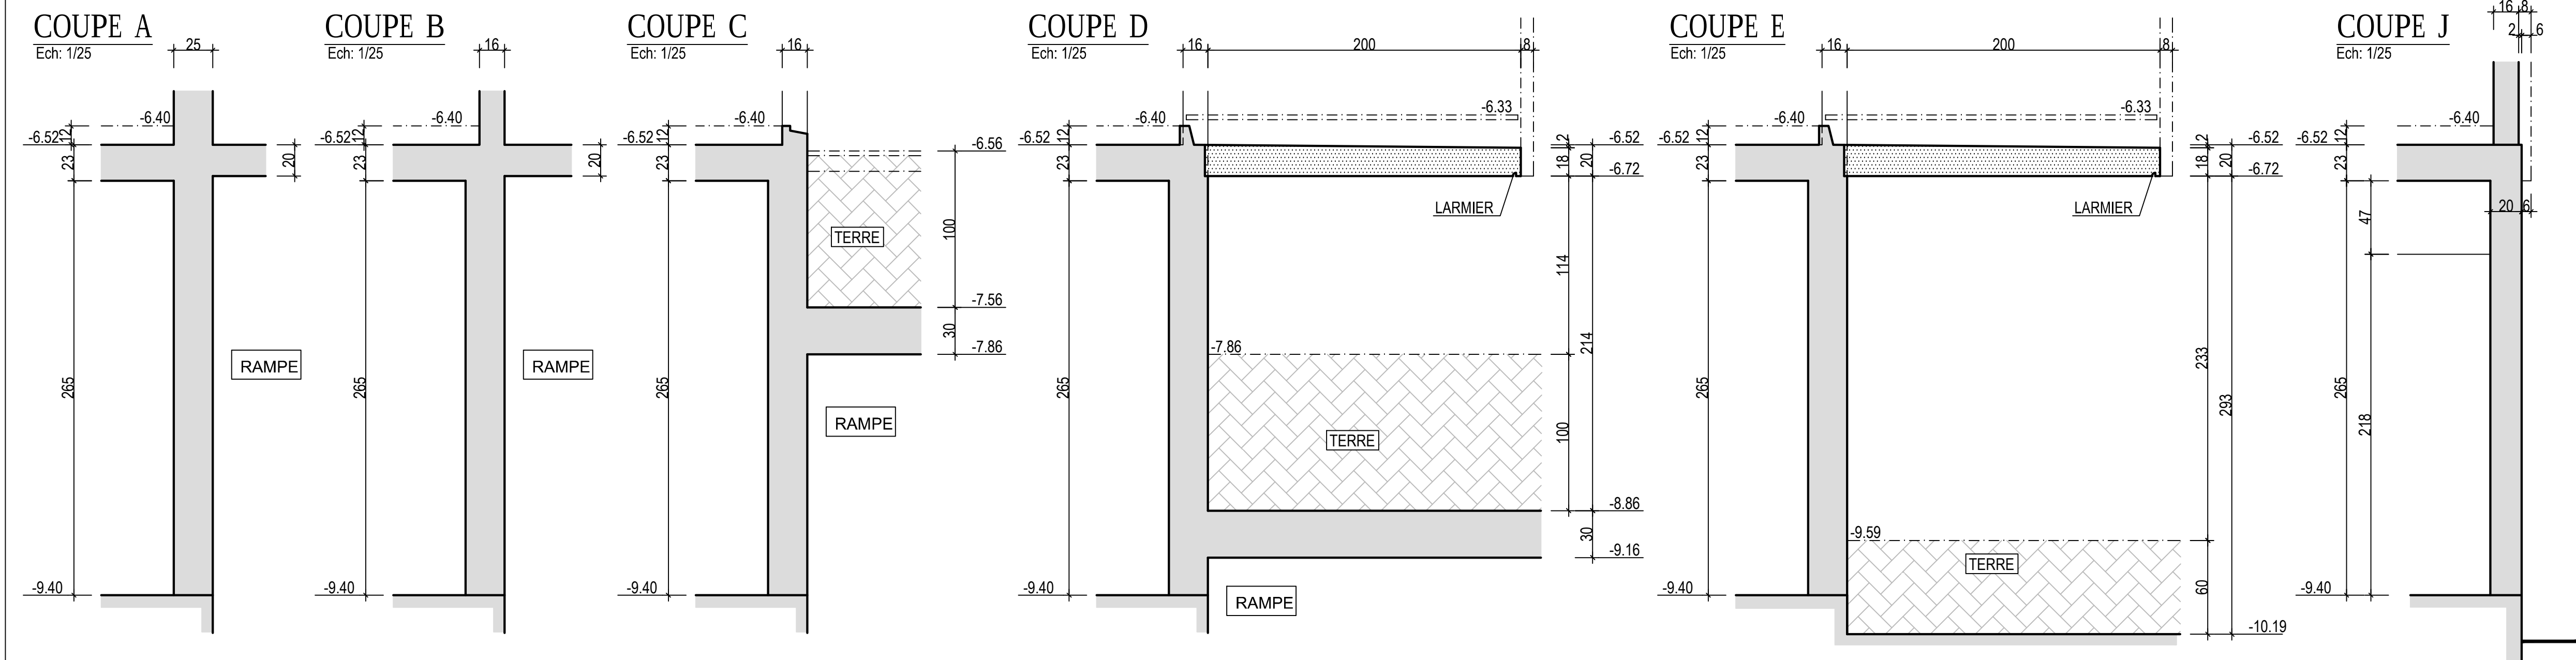
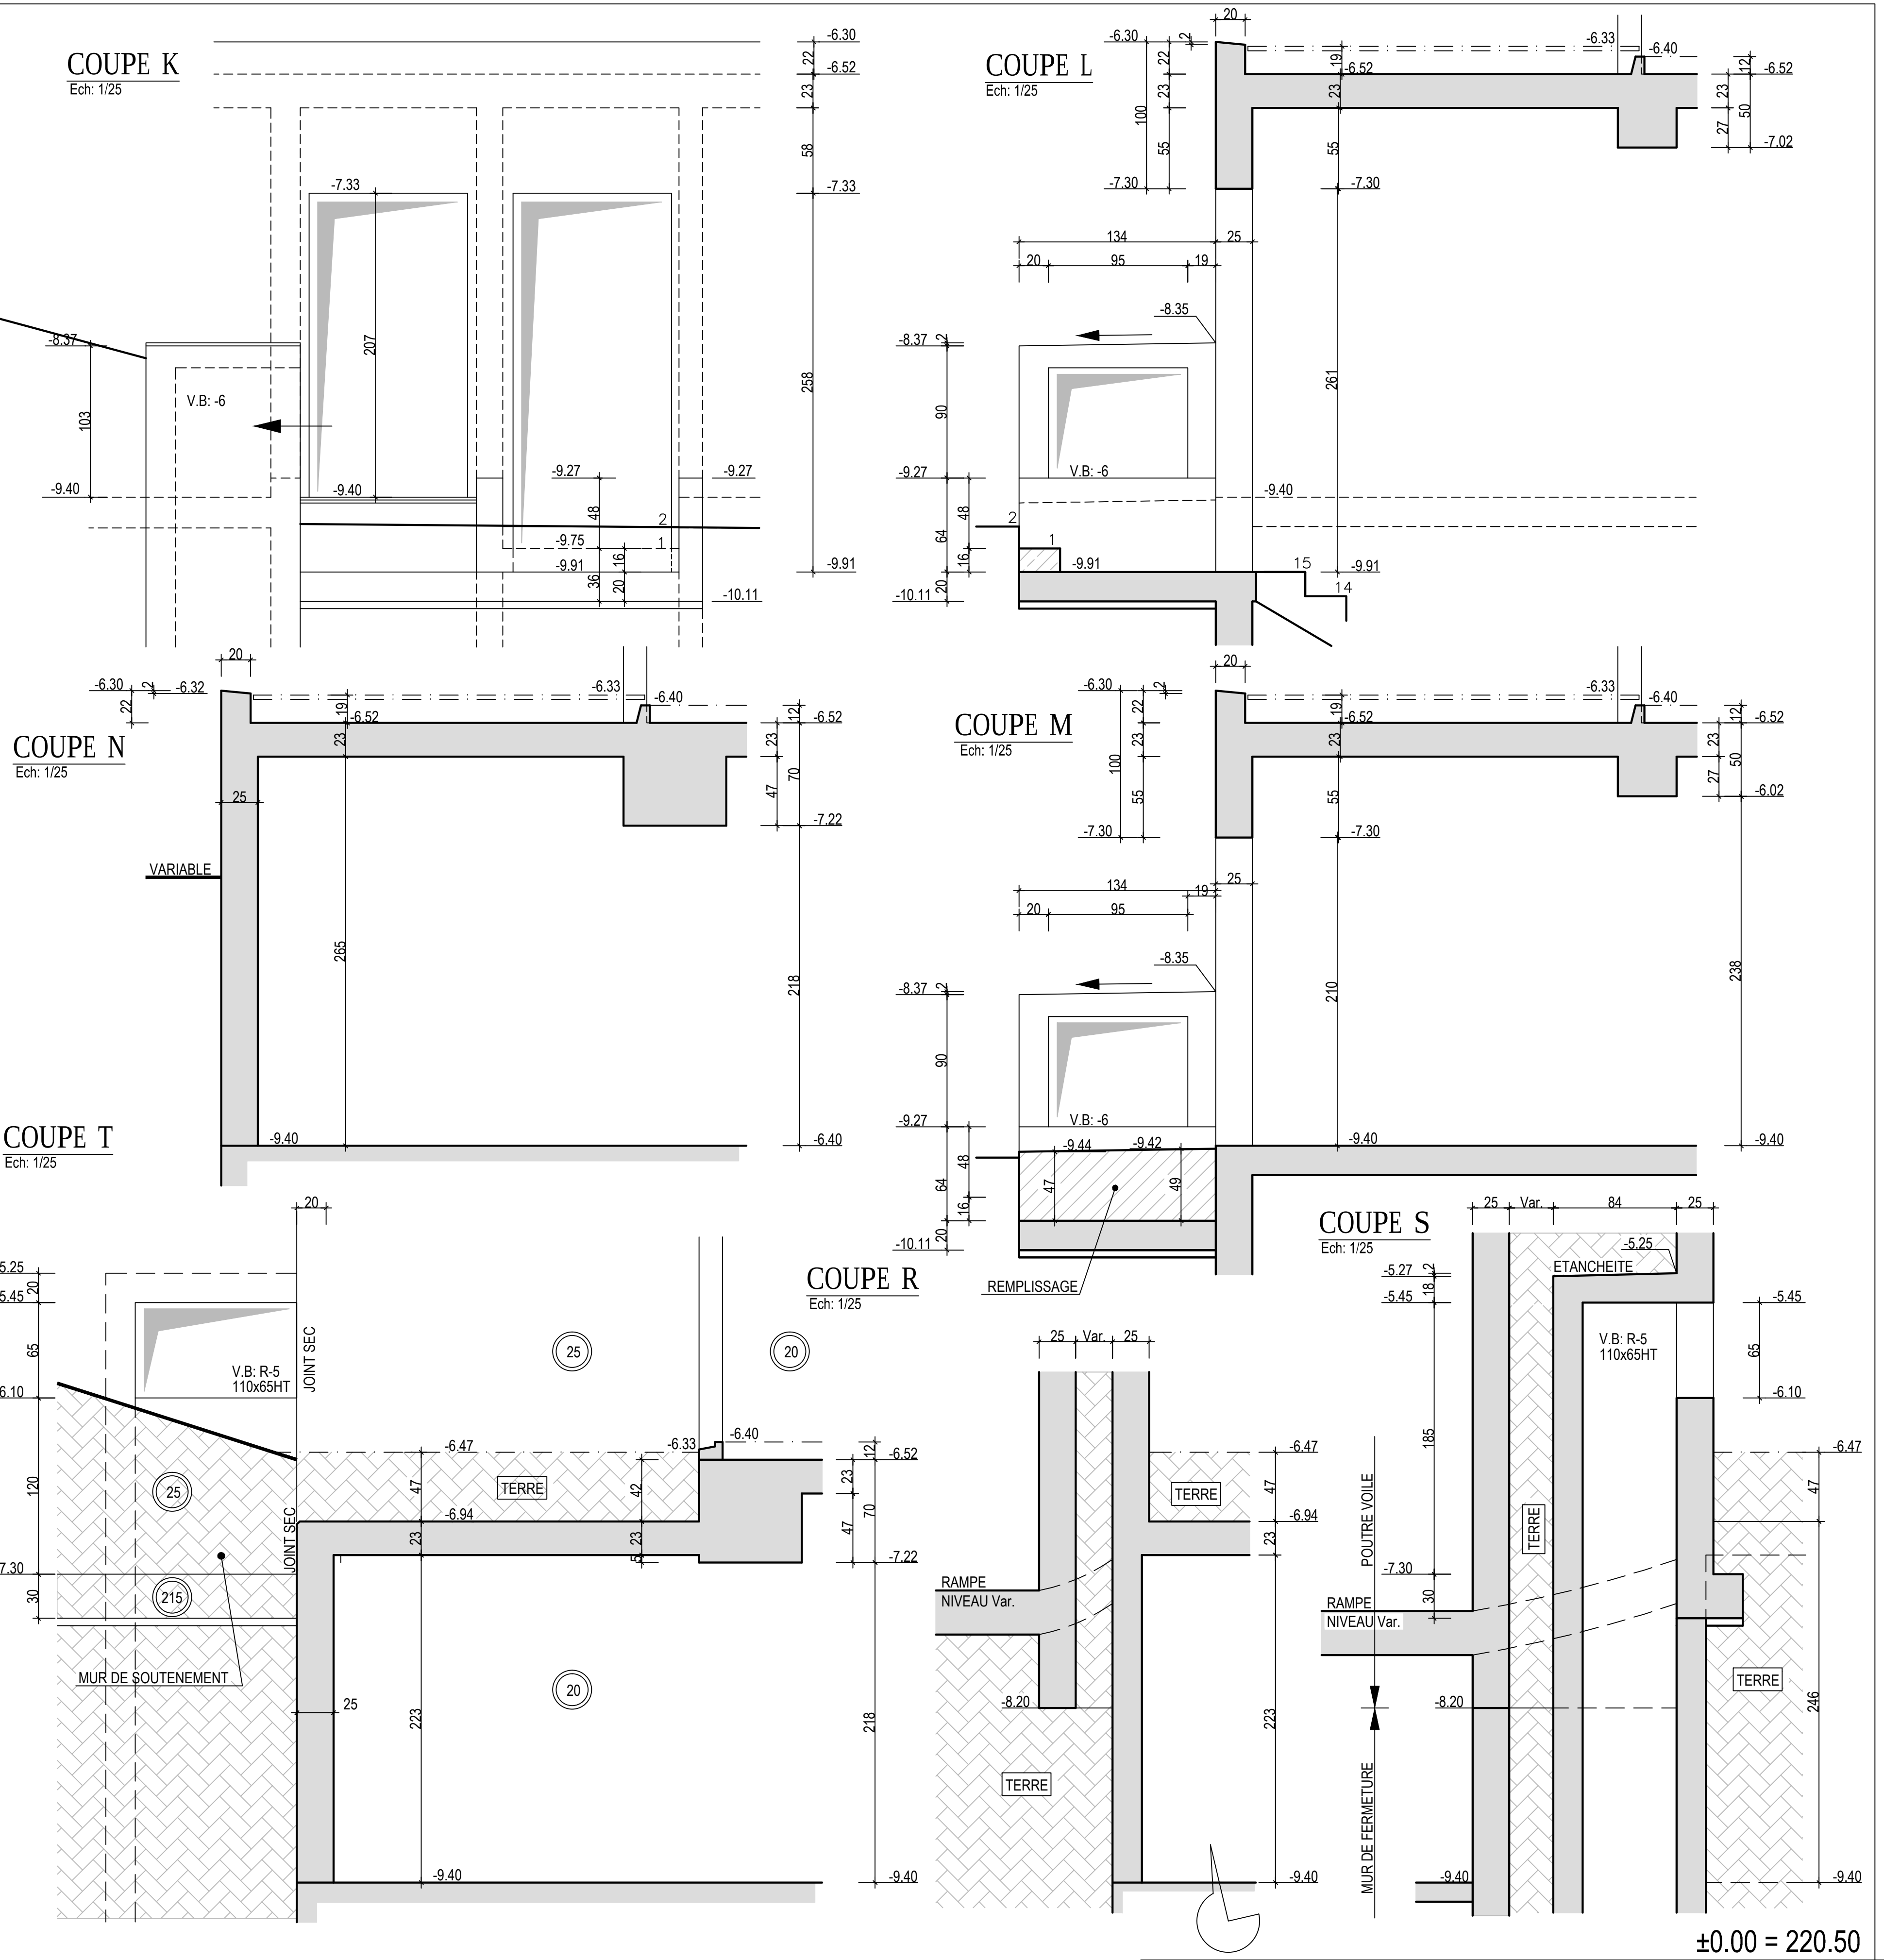


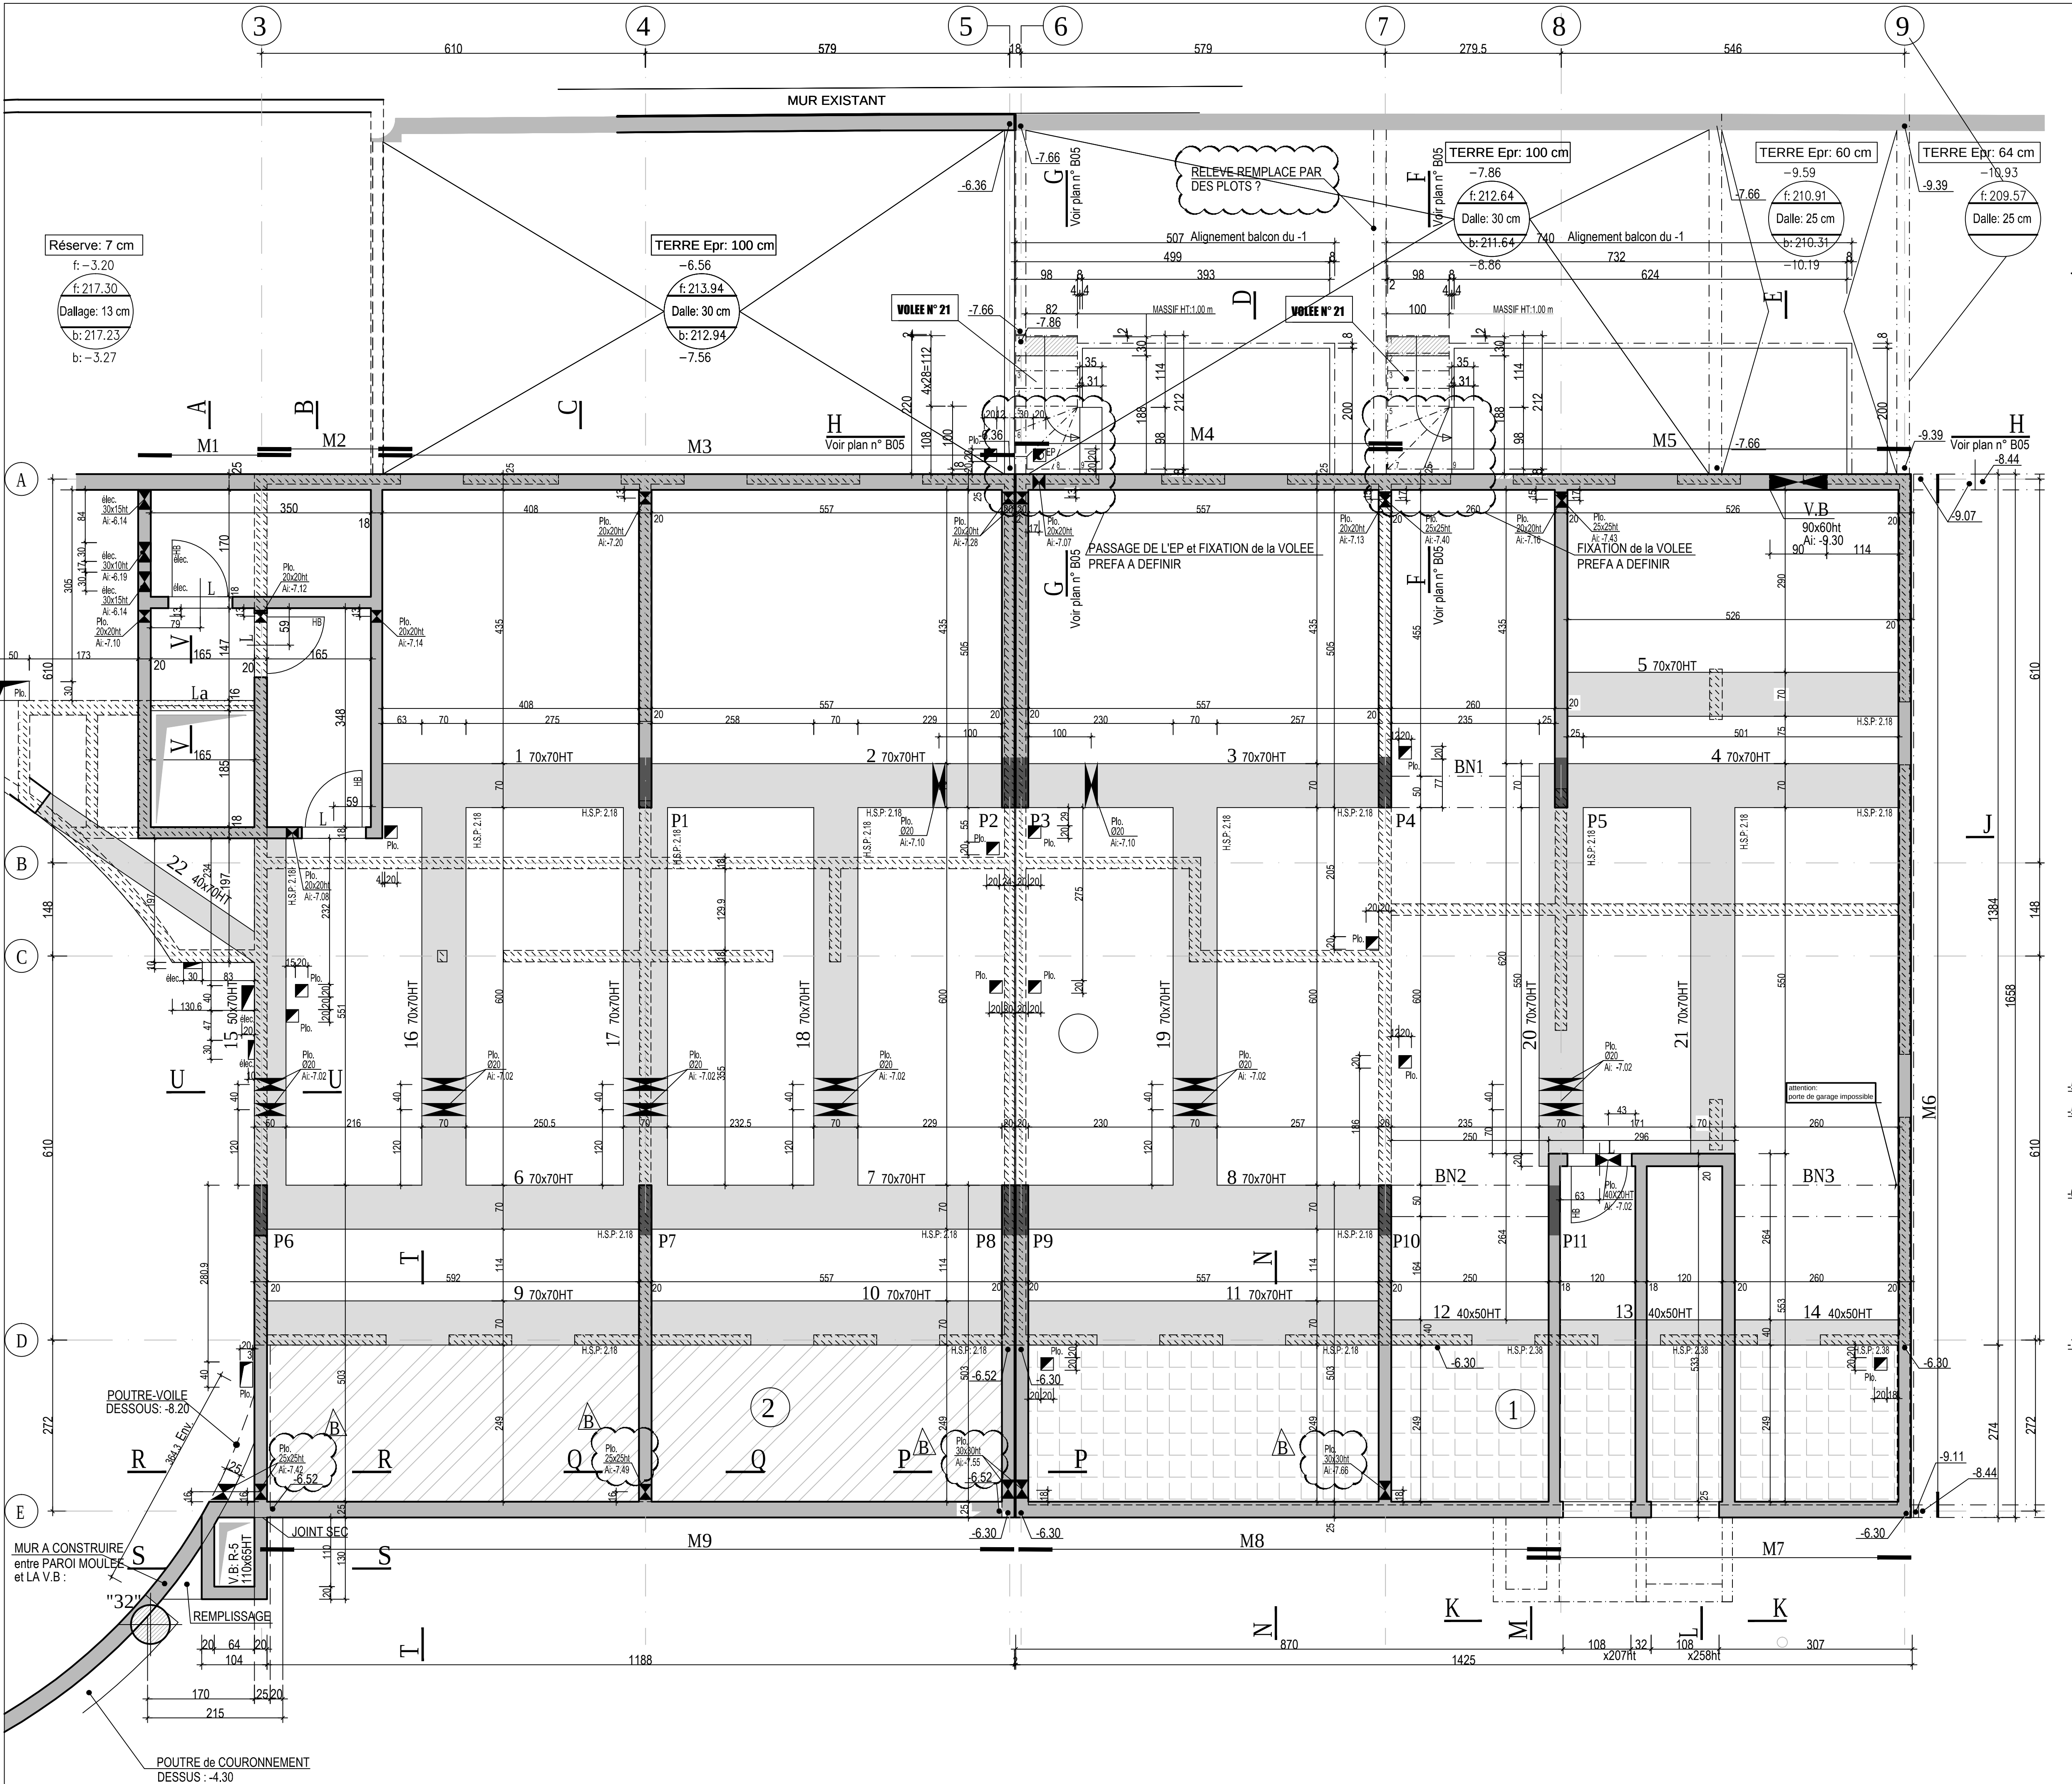

INDICE	DATE	MODIFICATIONS
A	08/12/2015	MODIFIE COUPE T
B	09/12/2015	MODIFIE: Ai réservations façade sud suivant B et supprimé les parements froissés.

NOAHO

Chemin de Fontanière - 69350 La Mulatière

Création de logements

Les entreprises réalisant les travaux devront tenir compte des derniers plans architecturaux lors de la réalisation des travaux. Les plans du Bât: A ne doivent servir qu'au corps d'état concerné et doivent être datés des plans d'exécution.

ARCHITECTE(S): ATELIER DE LA PASSERELLE
BET STRUCTURE: MATTE SAS
BET FLUIDES: PRELEM
ECONOMISTE: EXECO
BUREAU DE CONTRÔLE: Bureau VERITAS

MO DELEGUE: PSO Ingénierie
MODE: CSFS
OPC: ENTREPRISE(S): Fontanel-pbc

Bât: A

PLANCHER sur -3 entre files 3 et 9

Coffrage

DOE

Contrainte de sol: 8 dans ELS

Aciers HA (T) F4E500

Aciers Doux (B) F4E235

Aciers TS F4E 500

Béton t28 >= 25MPa

Enrobage = 3 cm

PLAN N° A19 B

DATE: 04/12/2015

MATTÉ

BUREAU D'ETUDES STRUCTURES ET FLUIDES

119 Boulevard Paul Marmont 91100 Evry-Courcouronnes

Tél. 01 72 44 52 07 Fax 01 72 44 26 59

E-mail: info@matté.fr

Dessiné par: J.B.O.

Contrôlé par: P.LIN.

Echelle: 1/500

Affaire N° 13.12.119