


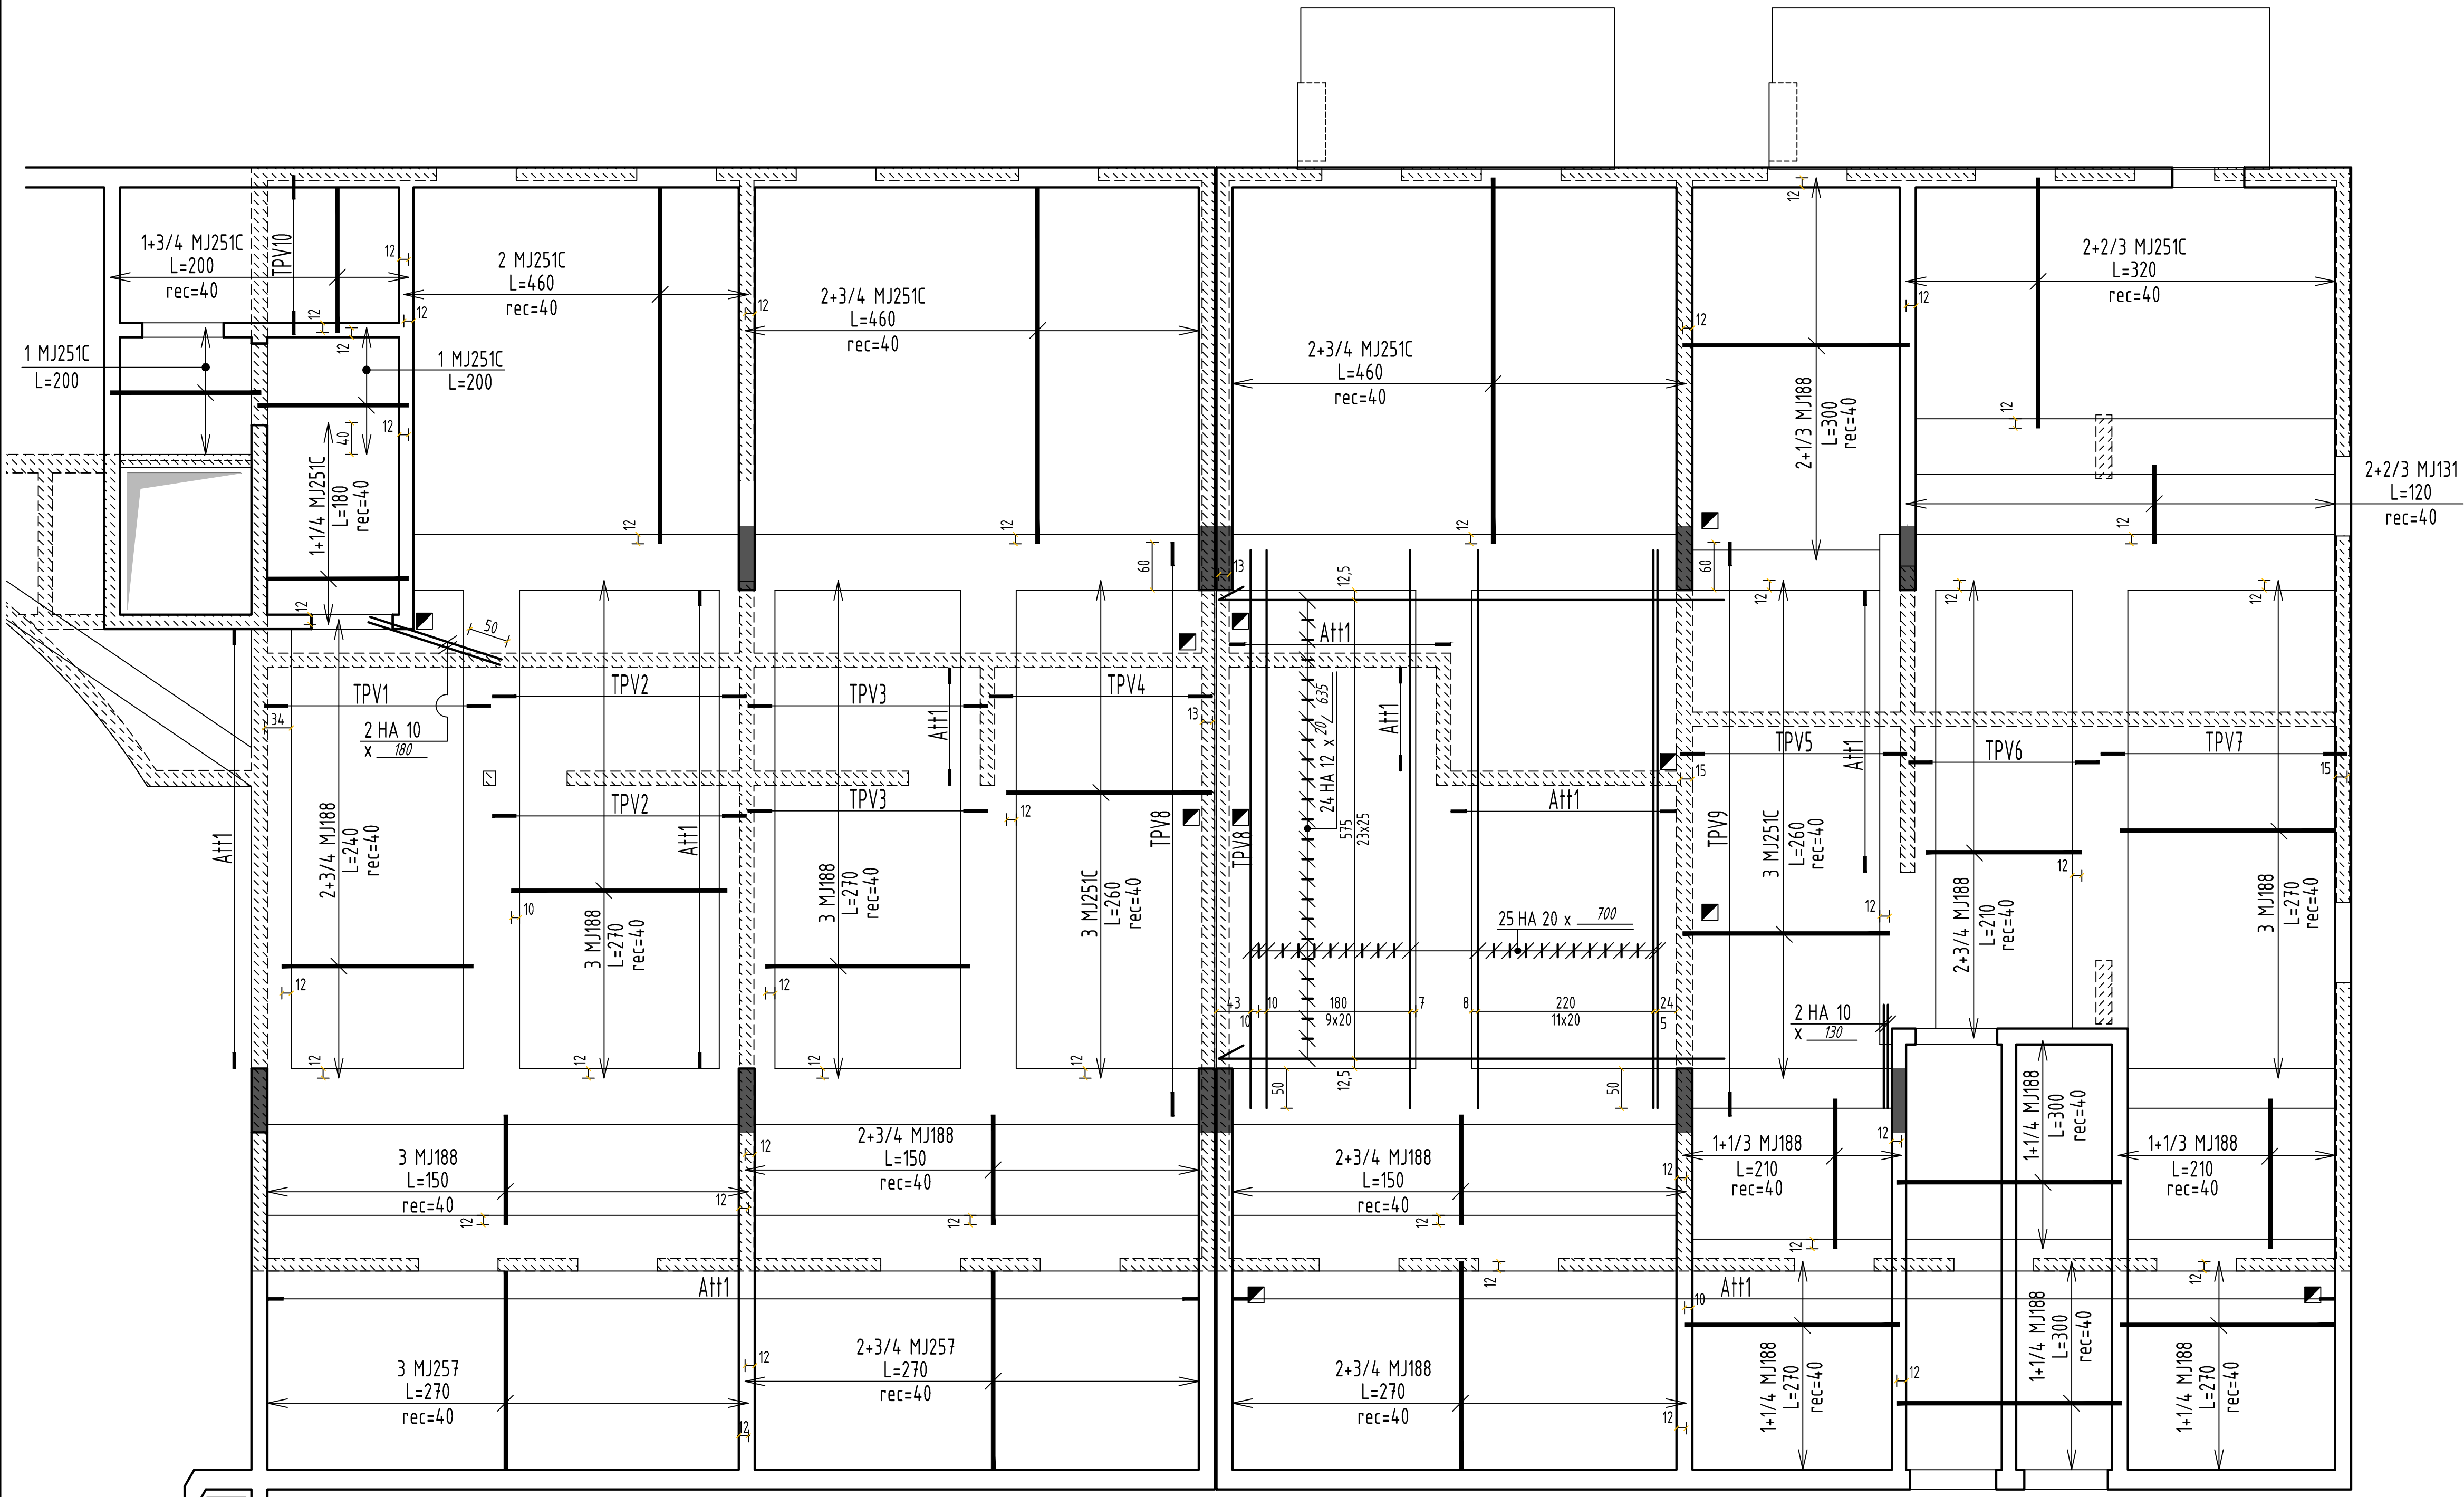


TREILLIS INF DES DALLES

Treillis	Lgr (cm)	Nbr
MJ131	120	3
MJ188	150	9
	210	6
	240	3
	270	14+1/2
	300	6
MJ251C	180	1+1/2
	200	4
	260	6
	320	3
	380	1
	460	8
MJ257	270	6




DETAIL D'ABOUTS DE CHAINAGES
INTERIEURS:

Position des épaves d'angles dans dalle 2 HA 14 x 100
à 90°
vues en plan

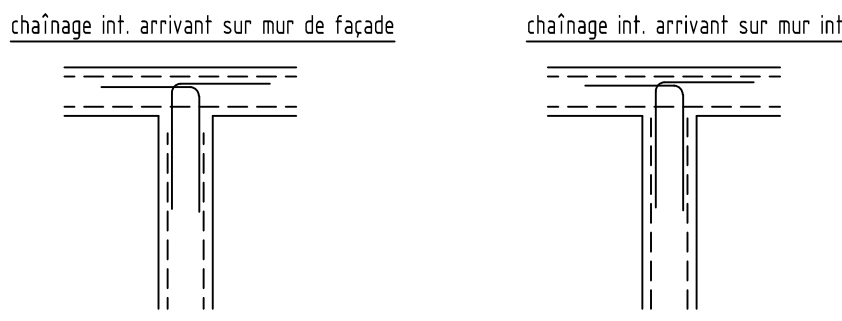

DETAIL D'ABOUTS DE CHAINAGES
EN ANGLE SUR FACADES:

Position des épaves d'angles dans dalle 2 HA 14 x 100
à 90°
coupe

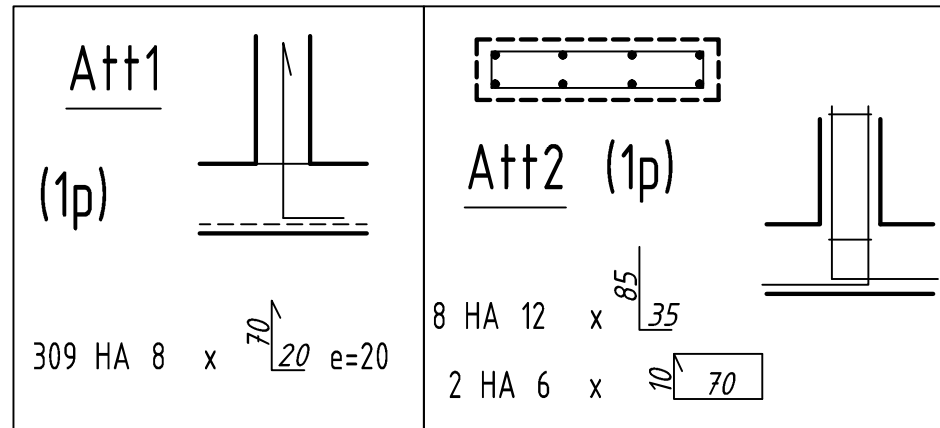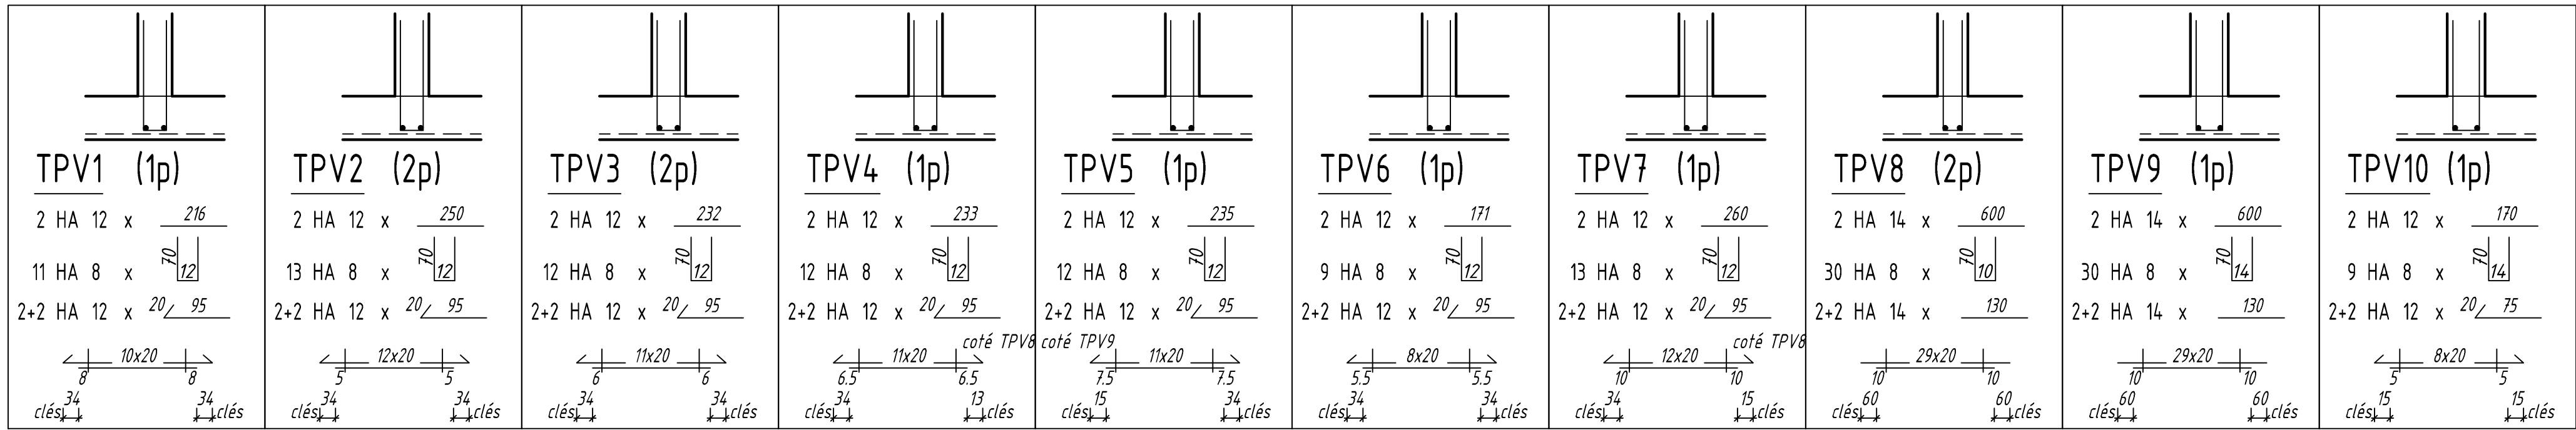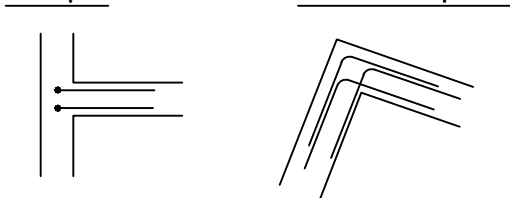

NOAHO

Chemin de Fontanière - 69350 La Mulatière

Création de logements

Les entreprises réalisant les travaux doivent tenir compte des derniers plans architectes lors de la réalisation des travaux.
Les plans du Bât MATTÉ ne doivent servir qu'au coup d'arrêt définitif et doivent être des plans d'exécution.

ARCHITECTES: ATELIER DE LA PASSERELLE

BET STRUCTURE: MATTÉ SAS

ECONOMISTE: EXECO

BUREAU DE CONTRÔLE: Bureau VERITAS

MO DELEGUE: MATTÉ SAS

MO: PRELEM

PSO Ingénierie: PSO Ingénierie

SUD EST COORDINATION: SUD EST COORDINATION

ENTREPRISES: Fontanel-pbc

Bât: A

PLANCHER sur -3 entre files 3 et 9

NAPPES INFÉRIEURES

Armatures des dalles

INDICE

DATE

MODIFICATIONS

MATTÉ

BUREAU D'ETUDES

STRUCTURES ET FLUIDES

119 BOULEVARD STRALINGHARD 69100 VILLEURBANNE

Tel: 04 72 44 10 87 Fax: 04 72 44 26 59

Email: bat@matté.fr

Designé par: J.B.O

Contrôlé par: P.LIN

Echelle: 1/50

EXE

Contrainte de sol: 8 bars EL5

Aciers HA (T) F4E500

Aciers Doux (D) F4E235

Aciers TS F4E 500

Béton b28 = 28MPa

Enrobage = 3 cm

PLAN N°

A22

0

DATE: 08/12/2015

Affaire N°

13.12.119