



PLANCHER sur -3

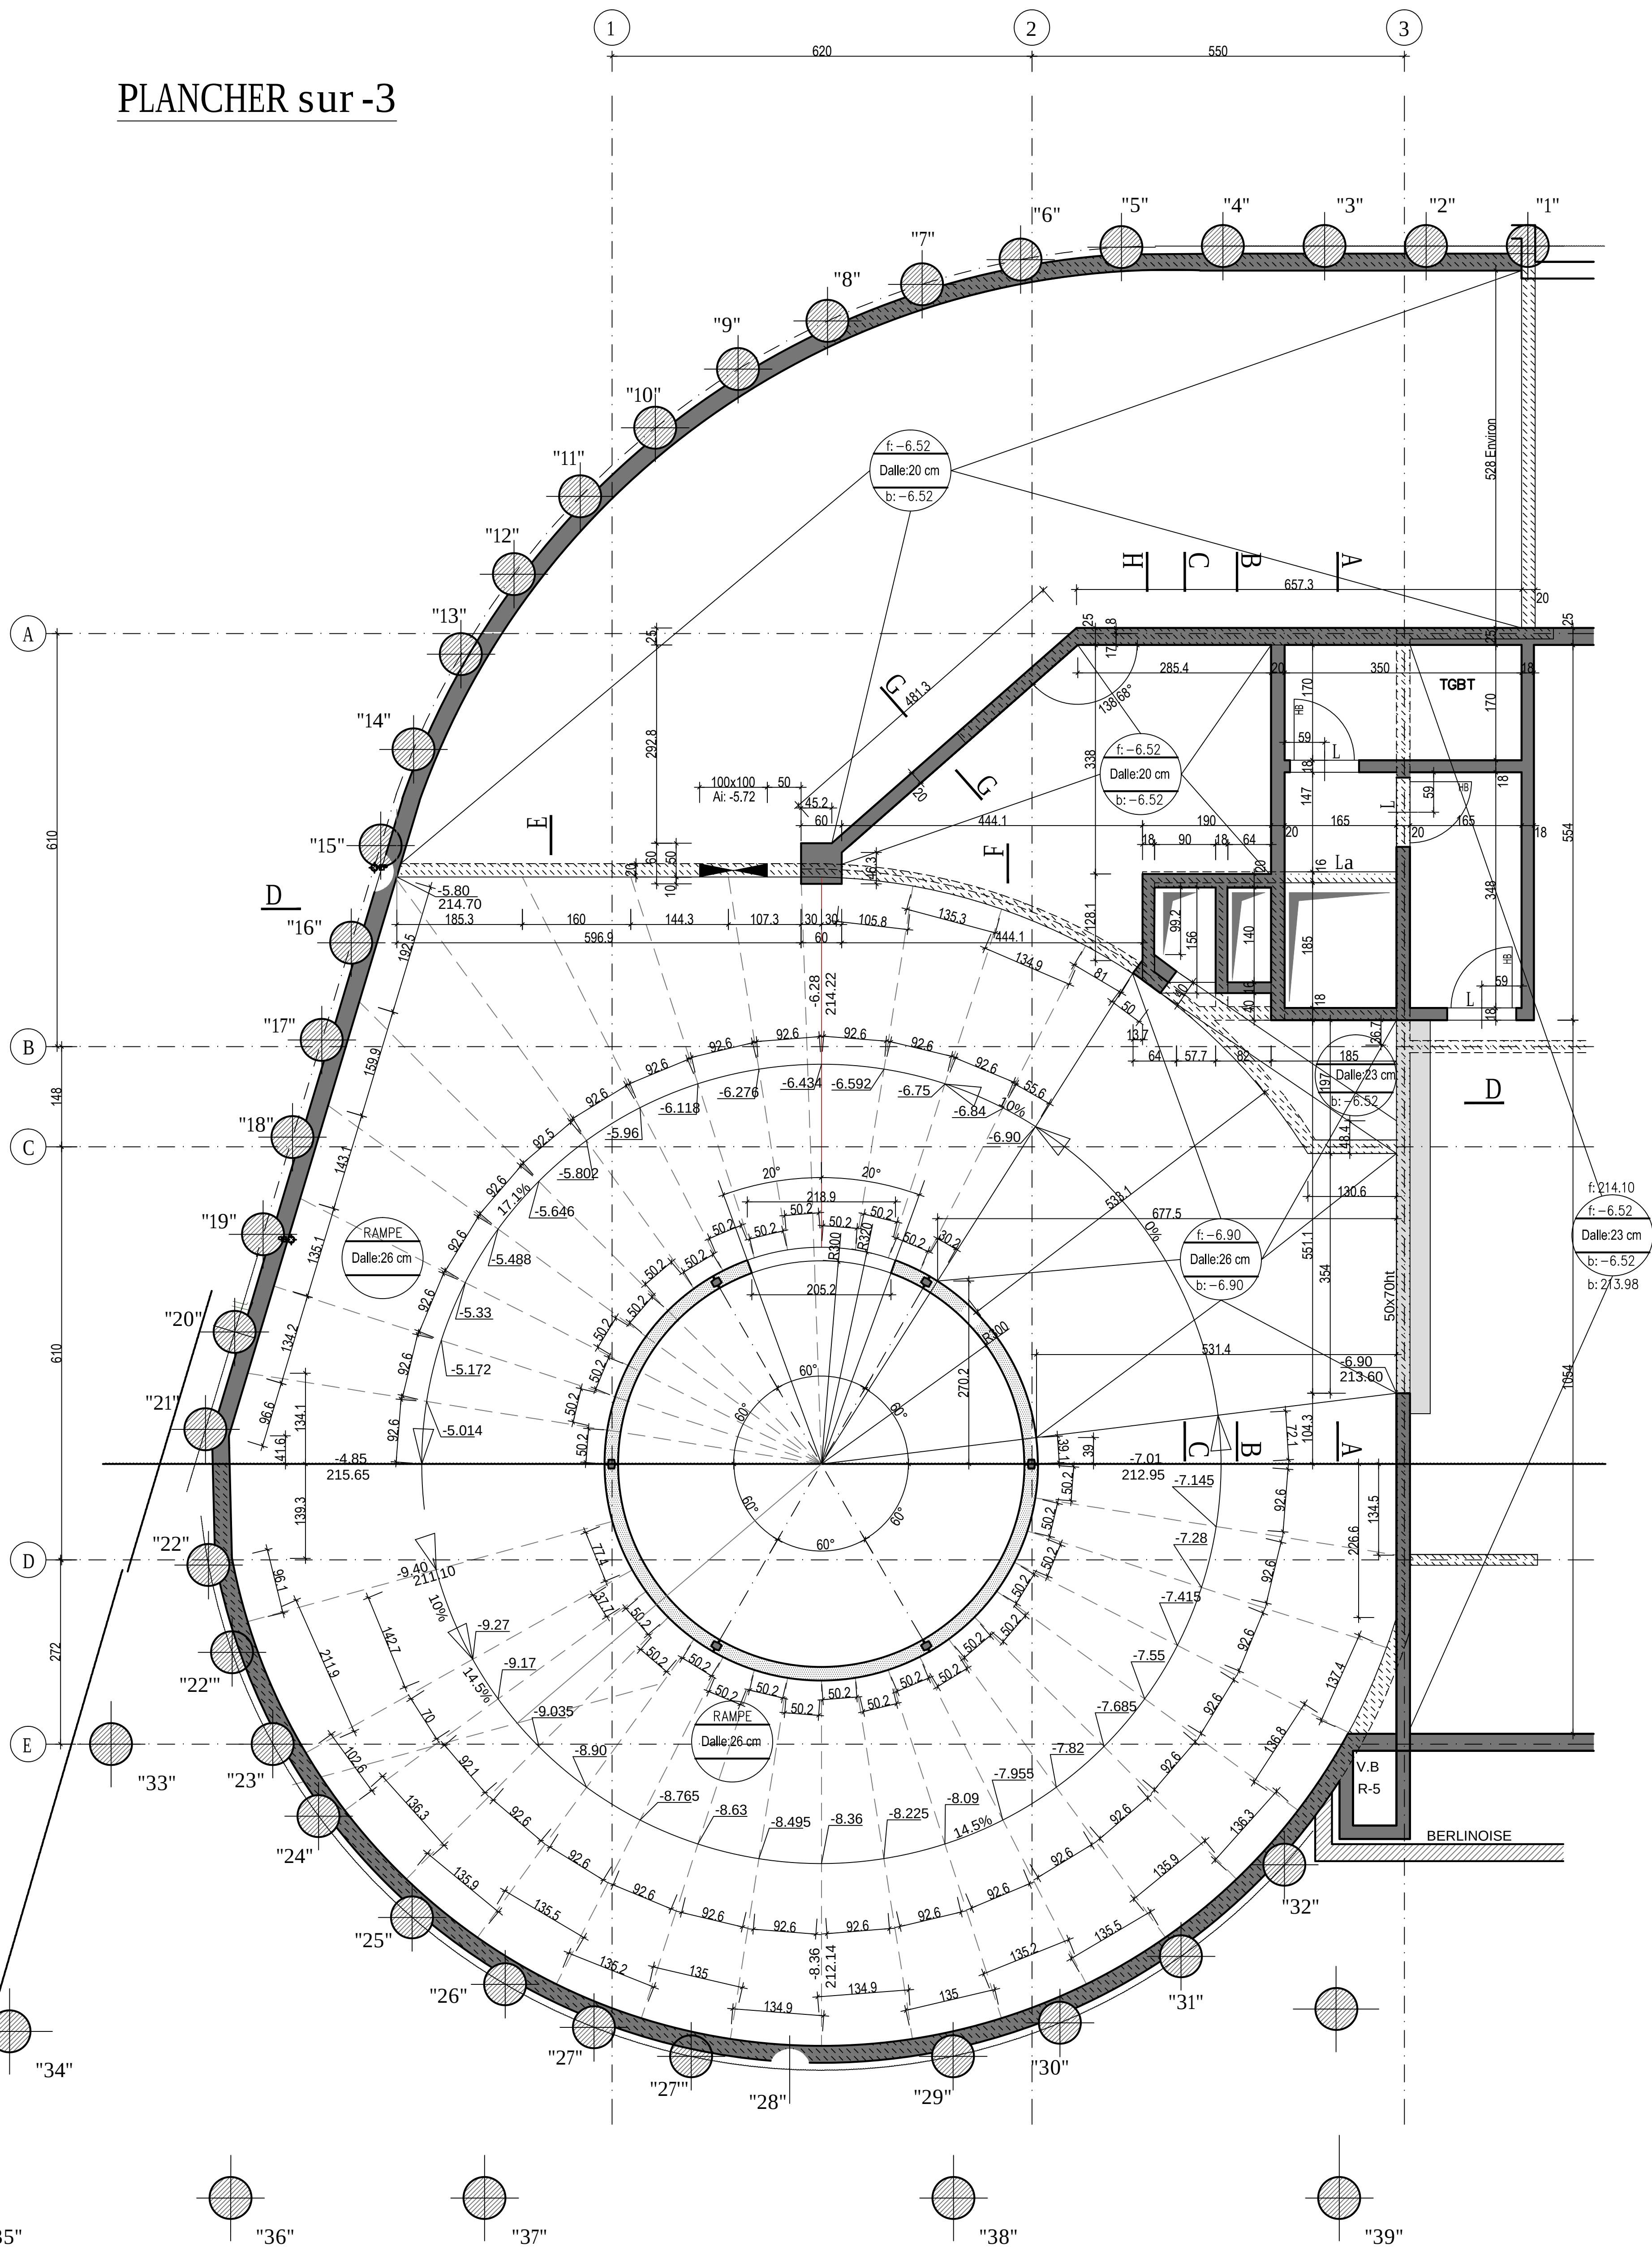

FONDATIONS au -3

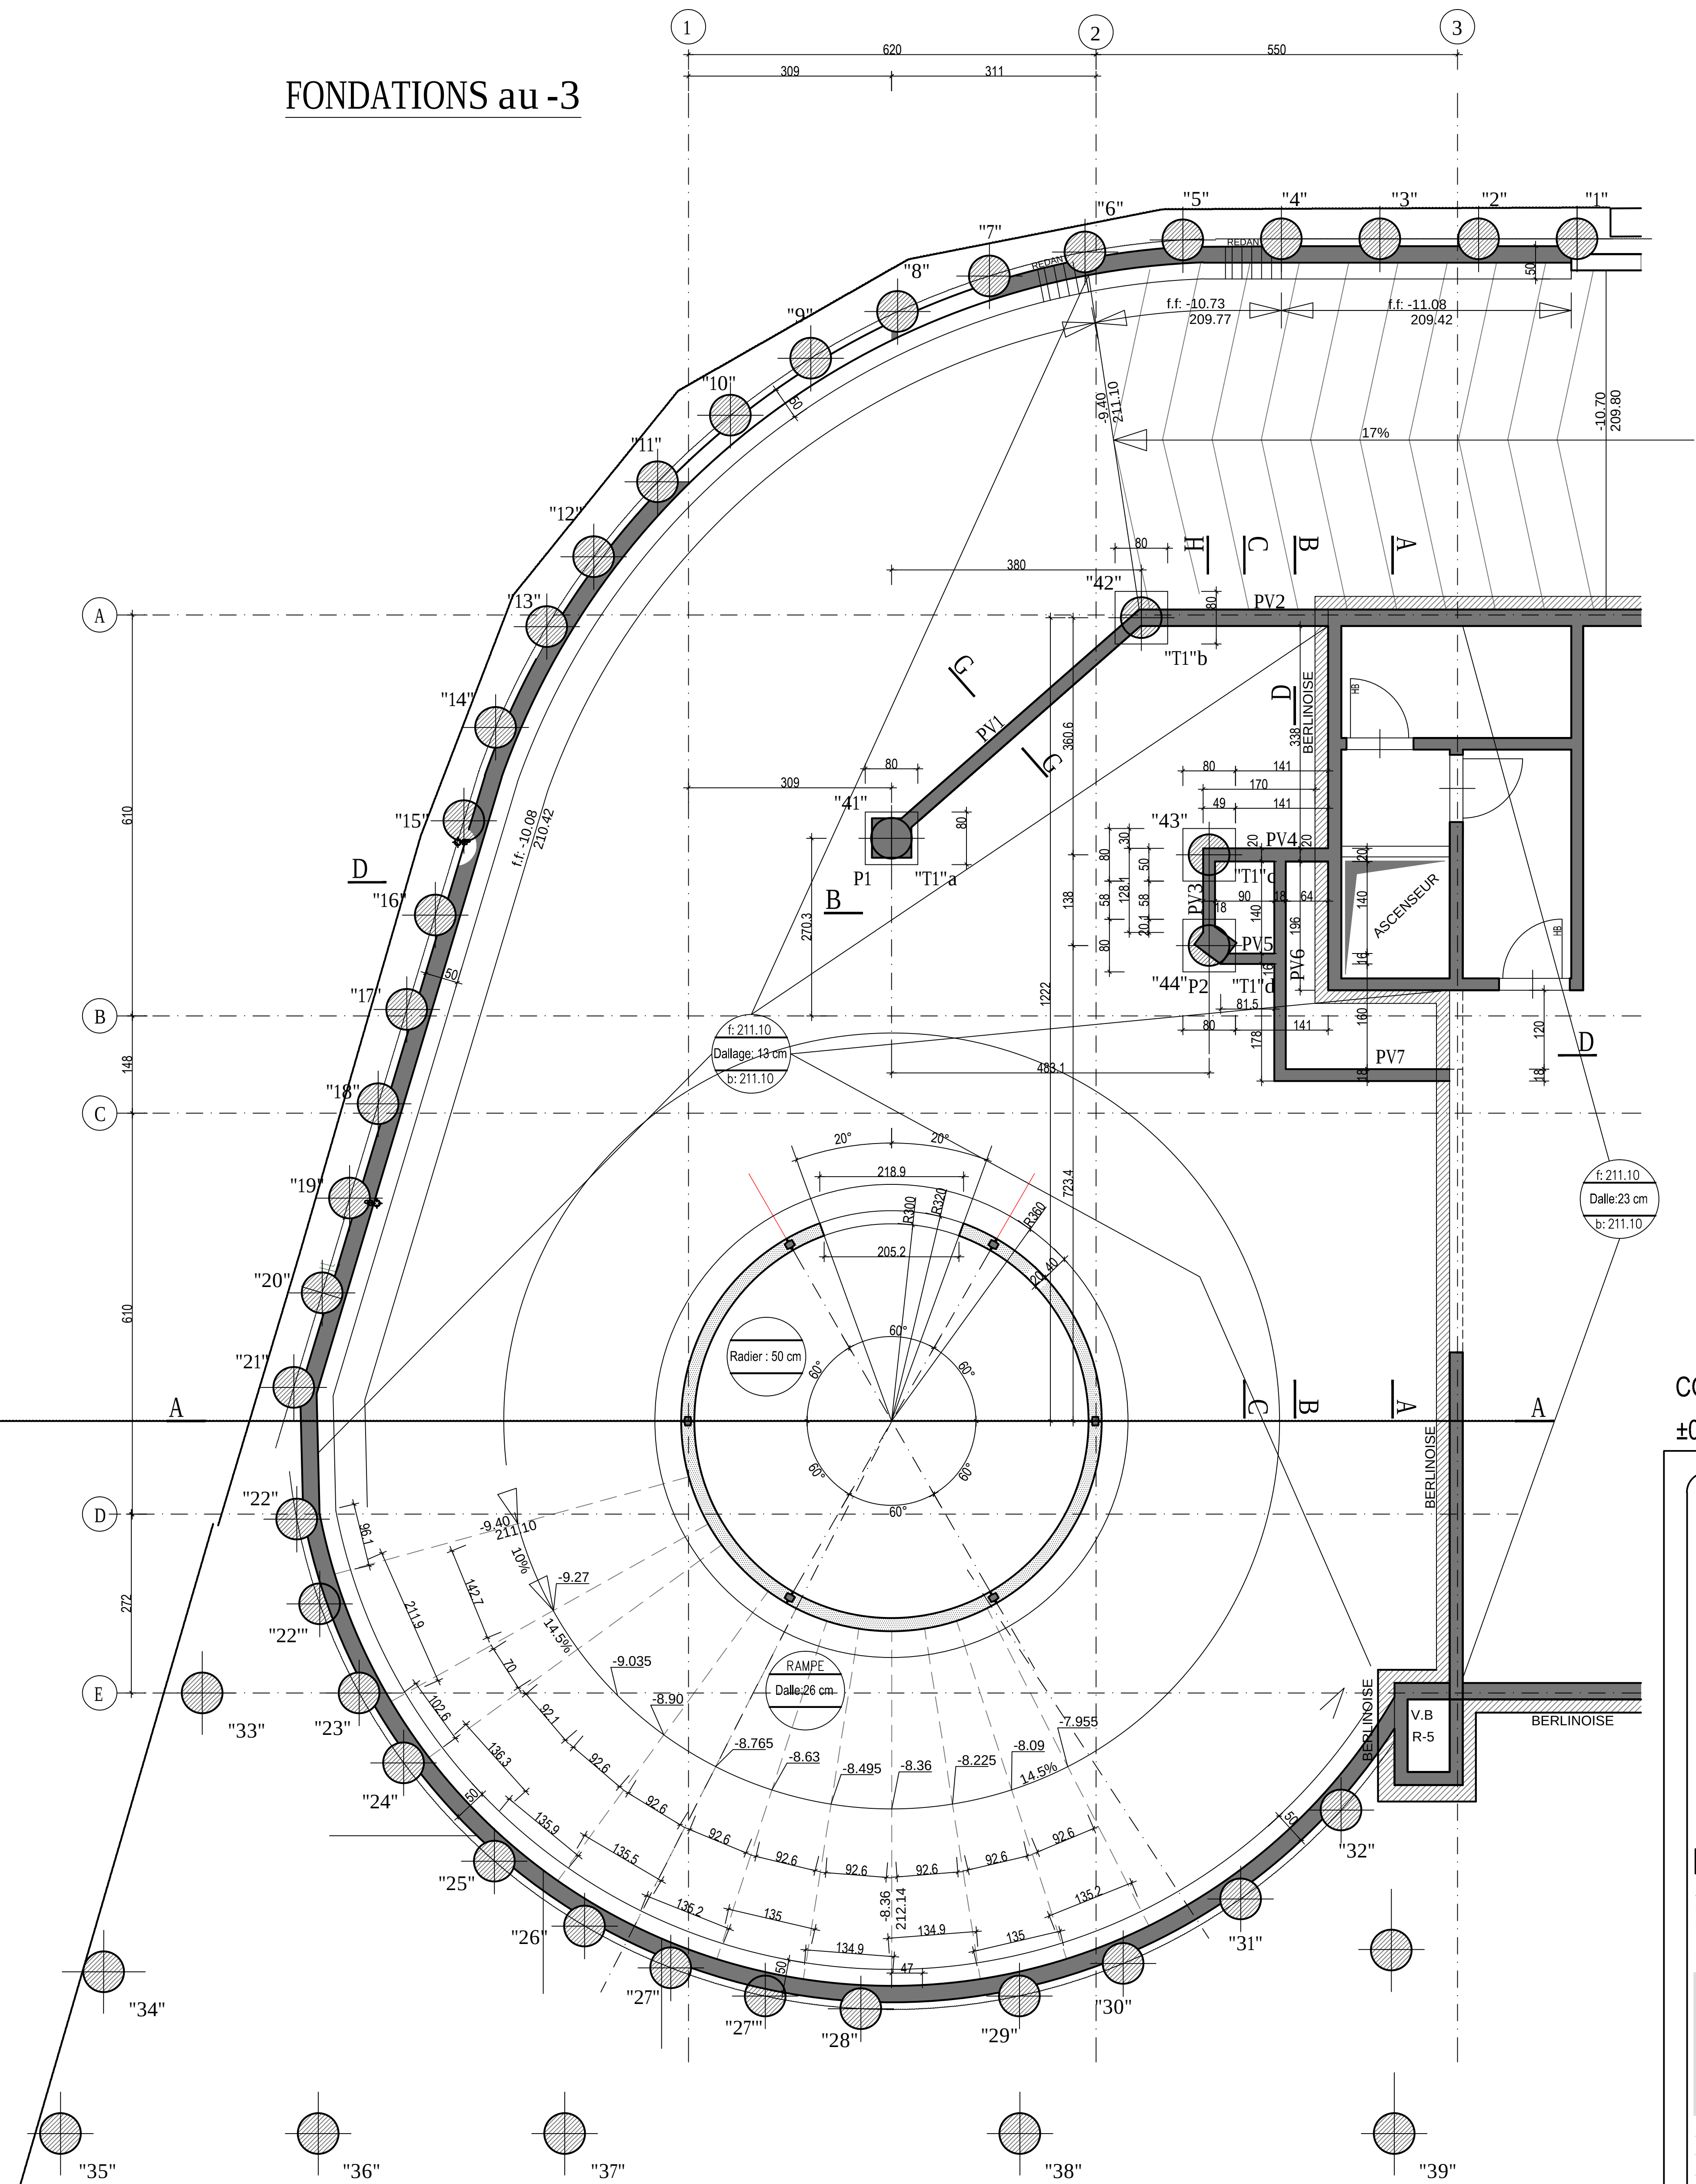

COUPES VOIR PLAN N° 26
±0.00 = 220.50

NOHAO

Chemin de Fontanière-69350 La Mulatière

Création de logements

Les entreprises réalisant les travaux devront tenir compte des derniers plans architecturaux lors de la réalisation des travaux.
Les plans du Bât MATTE ne doivent servir qu'au corps d'état concerné et doivent être des plans d'exécution.

ARCHITECTES: Atelier DE LA PASSERELLE

BET STRUCTURE: BET MATTE

BET FLUIDES: PRELEM

ECONOMISTE: EXECO

BUREAU DE CONTRÔLE: VERITAS

M.O. Délégue: .

M.O.: CSPPS

M.O.E.: PSO ingénierie

ENTREPRISES: SUD EST COORDINATION

Fontanel-poc

Bât A

PLANCHER sur -3 entre files 1 et 3

Vue en plan Coffrage

INDICE

DATE

MODIFICATIONS

A

08-01-2016

AJOUTER TROU D'HOMME

MATTÉ

BUREAU D'ETUDES

STRUCTURES ET FLUIDES

119 BOULEVARD STRAUBHOF 69100 VILLEURBANNE

Tel: 04 72 44 52 87 Fax: 04 72 44 26 59

E-mail: dm@matté.fr

Designé par: J. BONDETTI

Contrôle par: P. LIN

Ech:

DOE

Asses HA (T) F&E000

Asses D&U (B) F&E 235

Asses TS F&E 500

Bâton 628 = 200Pa

Enrobage = 3 cm

PLAN N° A25 A

DATE: 27-11-2015

Affaire N° S.13.12.118