

NOHAO

Chemin de Fontanière-69350 La Mulatière
Création de logements

Les entreprises réalisant les travaux devront tenir compte des derniers plans architecte lors de la réalisation des travaux
Les plans du be MATTE ne doivent servir qu'au corps d'état concerné et doivent être des plans d'exécution.

ARCHITECTE(S):	Atelier DE LA PASSERELLE	M.O. Délégué:	.
BET STRUCTURE:	BET MATTE	M.O.:	.
BET FLUIDES:	PRELEM	CSPS:	PSO ingénierie
ECONOMISTE:	EXECO	M.O.E.:	SUD EST COORDINATION
BUREAU DE CONTROLE:	VERITAS	ENTREPRISE(S):	Fontanel-pbc

Bât: A
BA au -3 entre files 1 et 3

DOE

INDICE	DATE	MODIFICATIONS
A	02-12-2015	AJOUTE PAGE 10

Aciers HA (T) FeE500
Aciers Doux (Ø) FeE 235
Aciers TS FeE 500
Béton fc28 >= 25MPa
Enrobage = 3 cm

PLAN N°
A27 A

DATE : 30-11-2015

MATTÉ



BUREAU D'ÉTUDES
STRUCTURES ET FLUIDES

119 BOULEVARD STALINGRAD 69100 VILLEURBANNE
Tél. 04 72 44 02 87 Fax 04 72 44 26 59
E-mail : bet@matte.fr



Dessiné par : J.BONDETTI
Contrôlé par : P. LIN
Ech :

Affaire N°
S.13.12.118



POUTRE VOILE : PV1

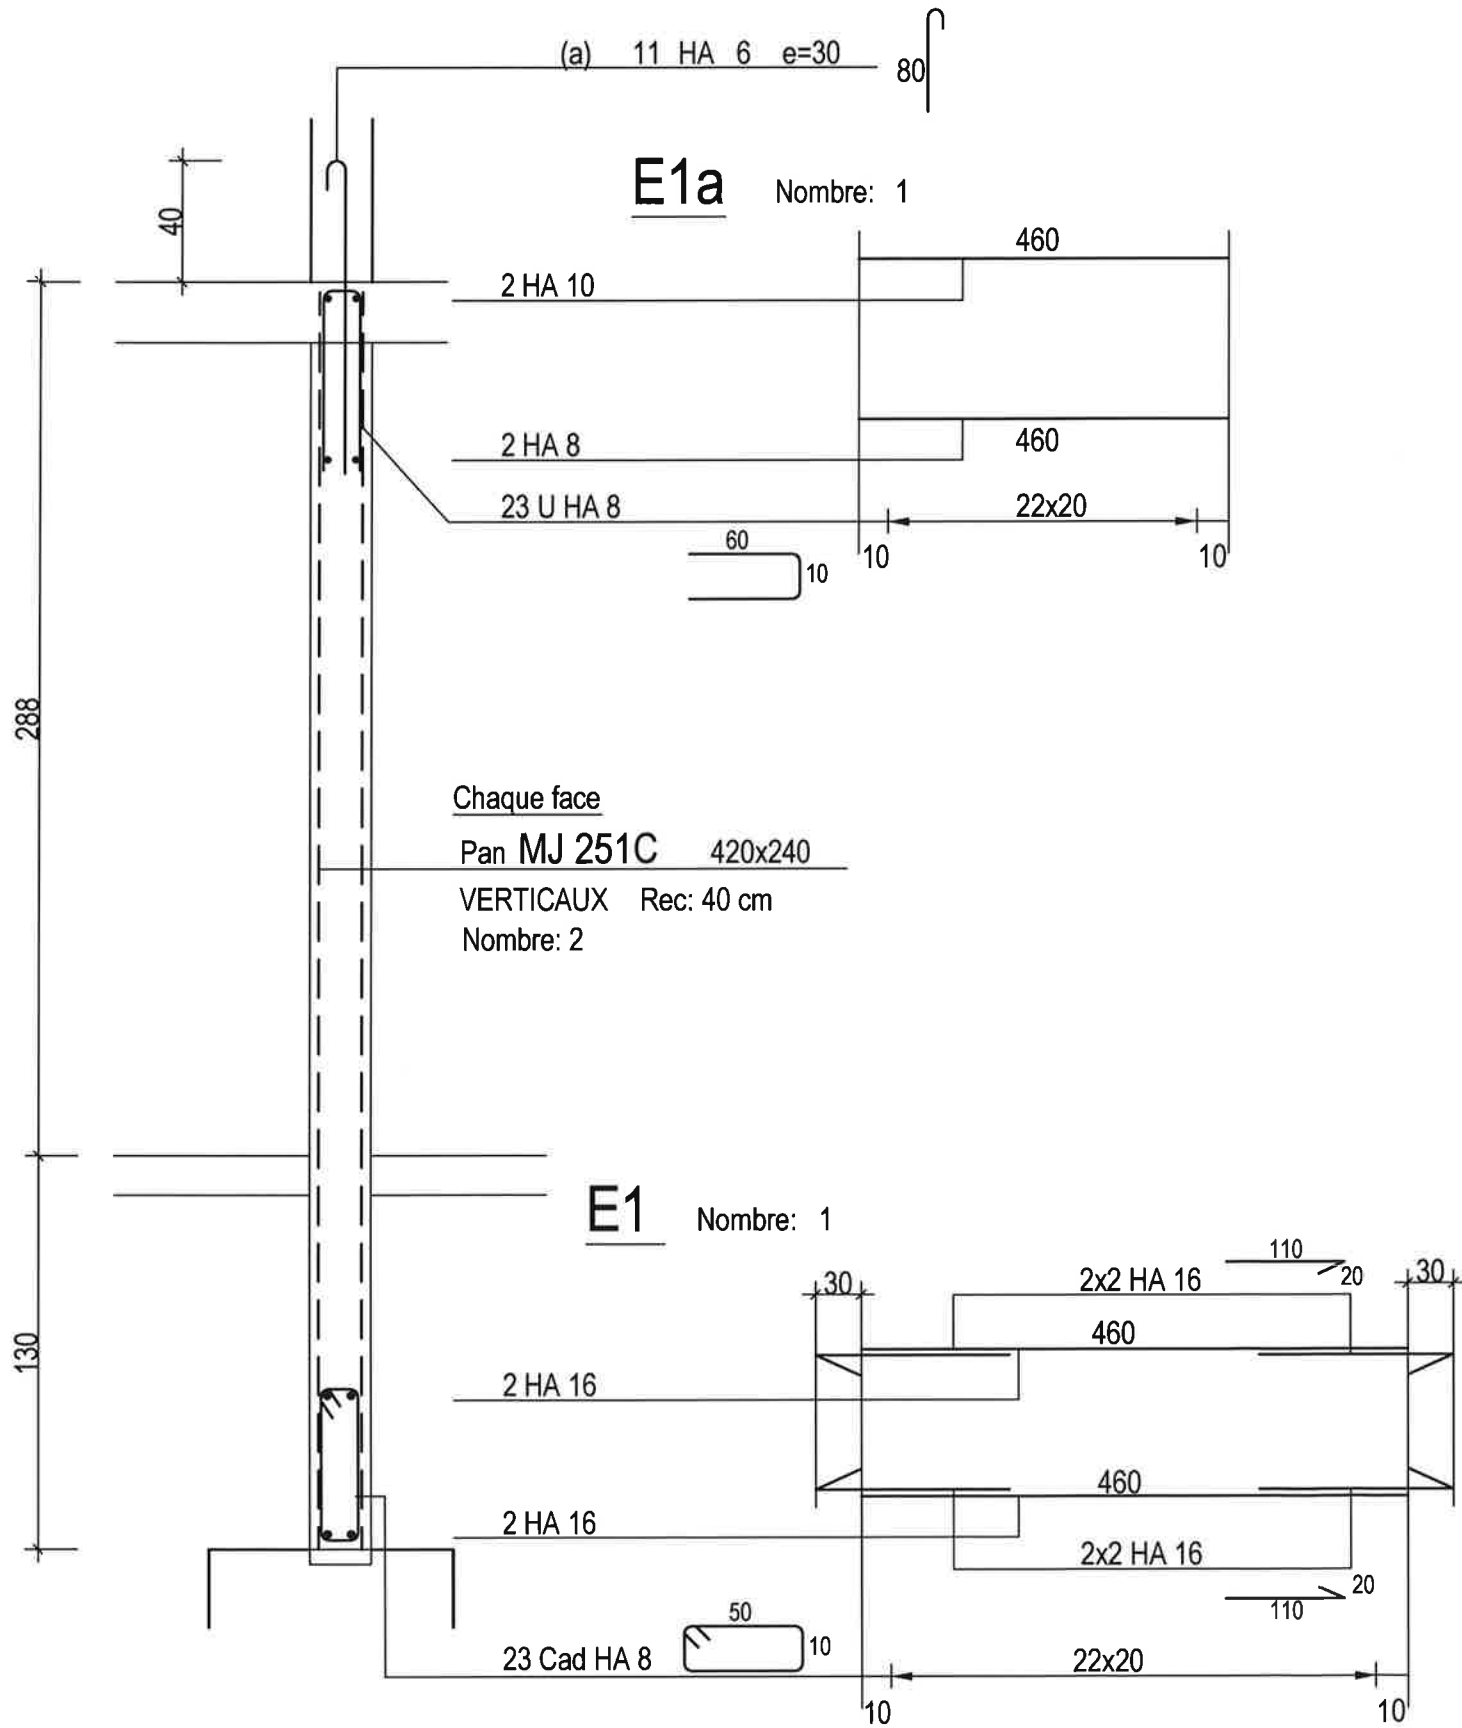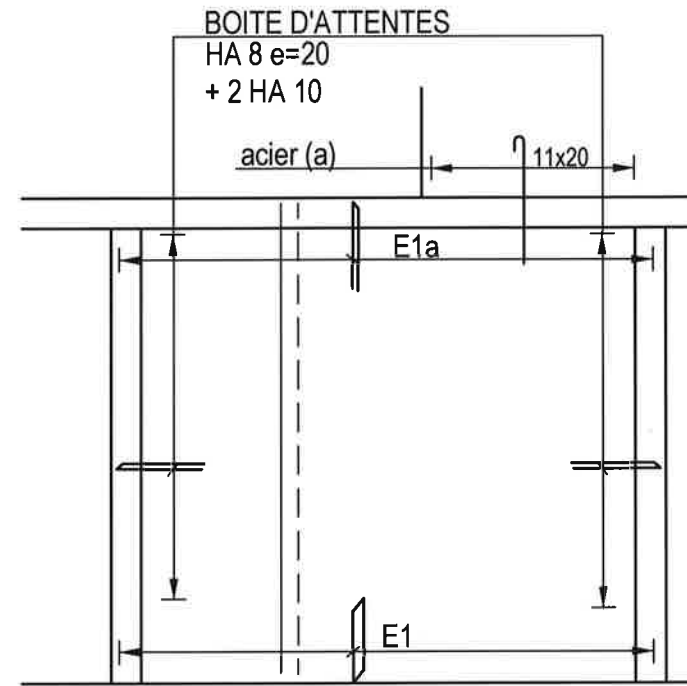ELEVATION



POUTRE VOILE : PV2

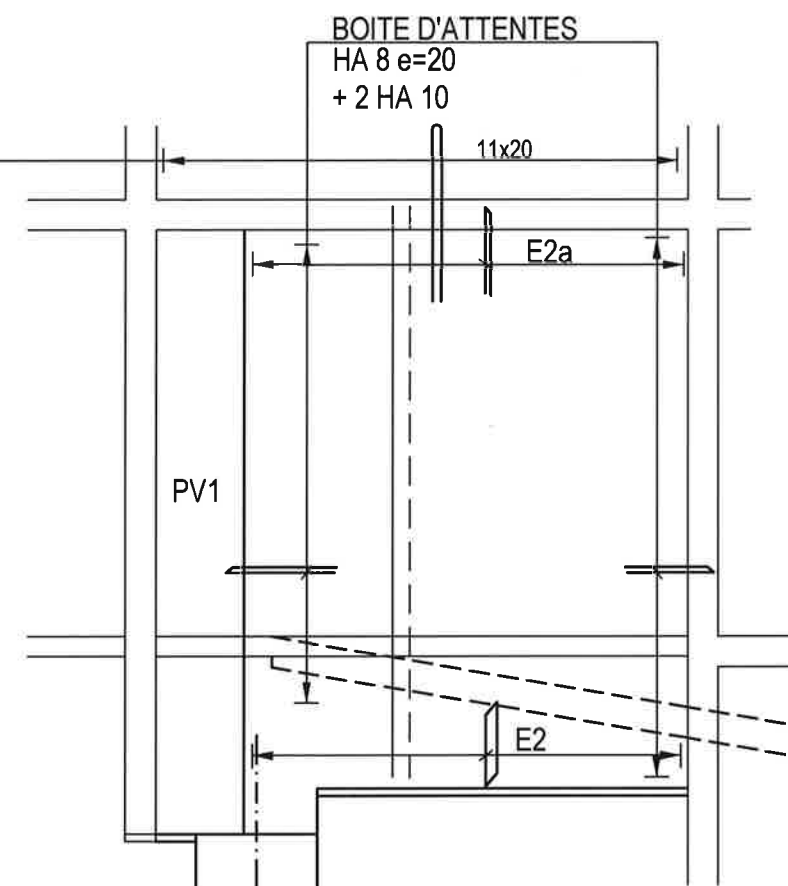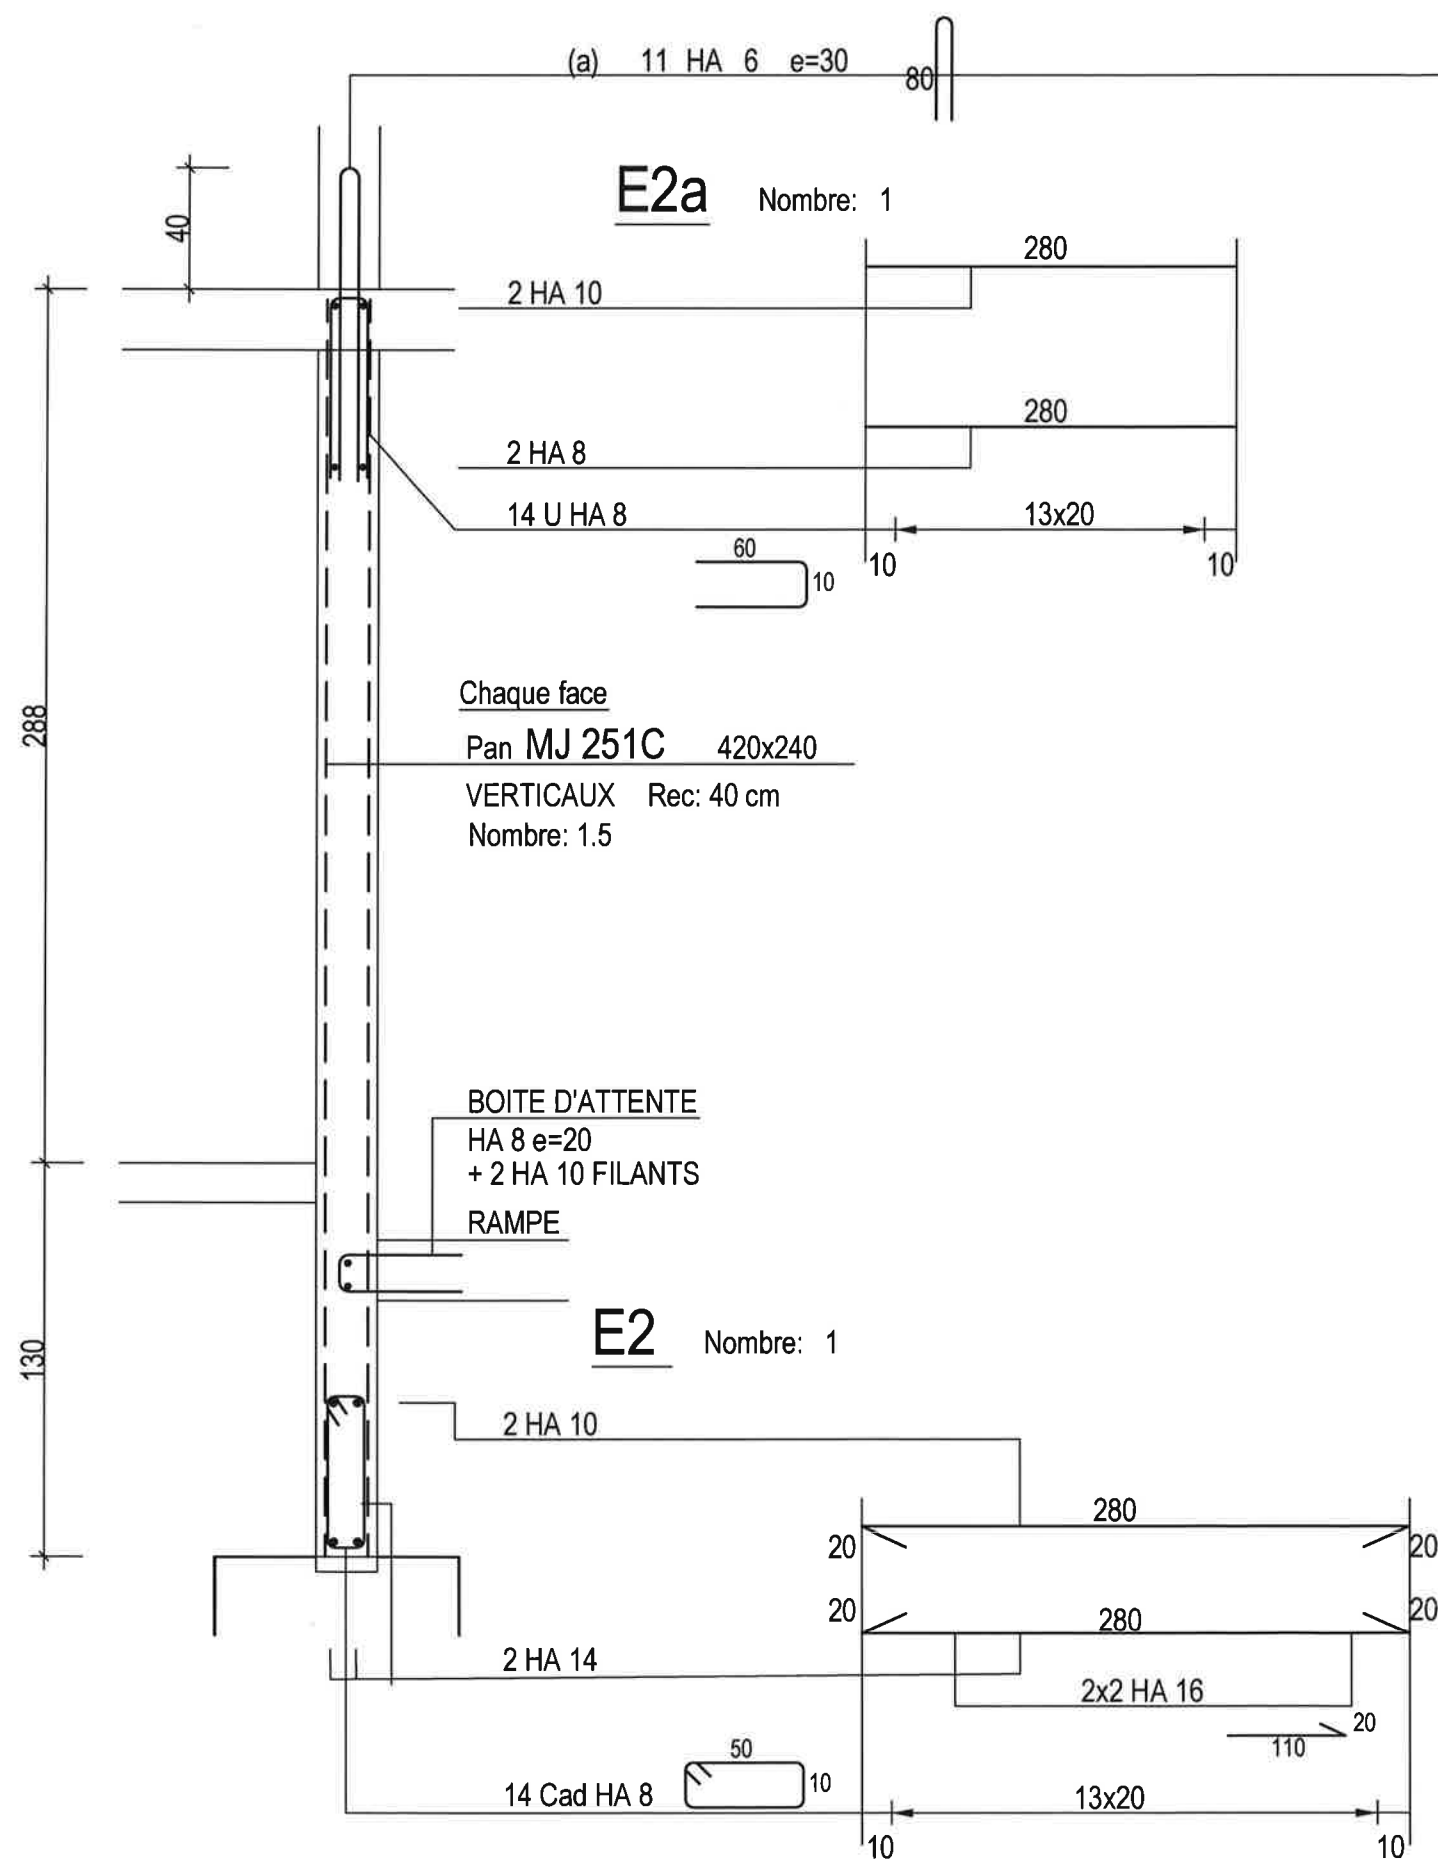



POUTRE VOILE : PV3

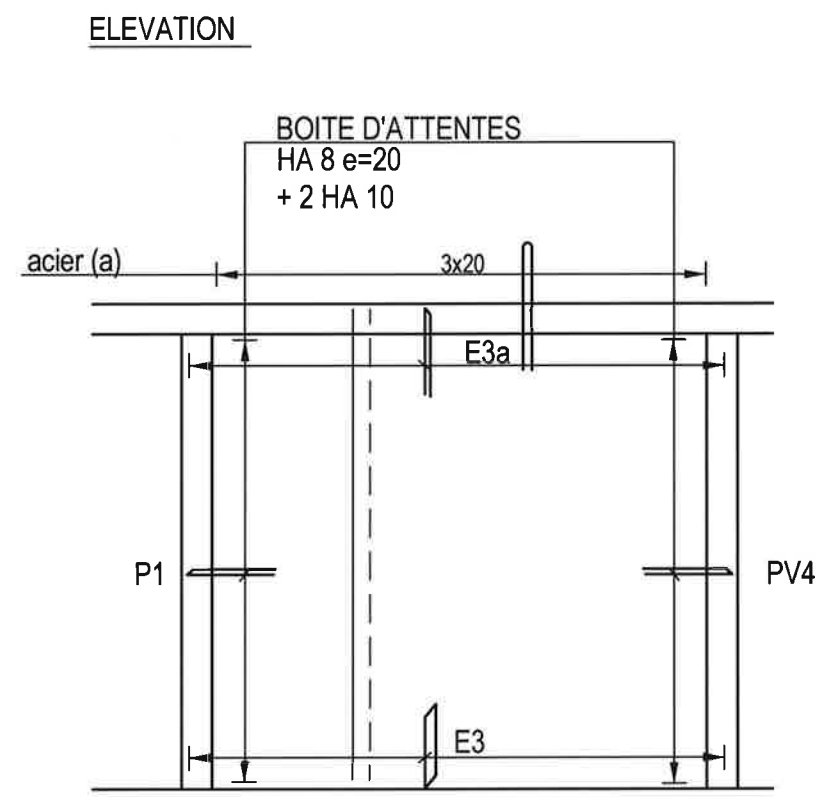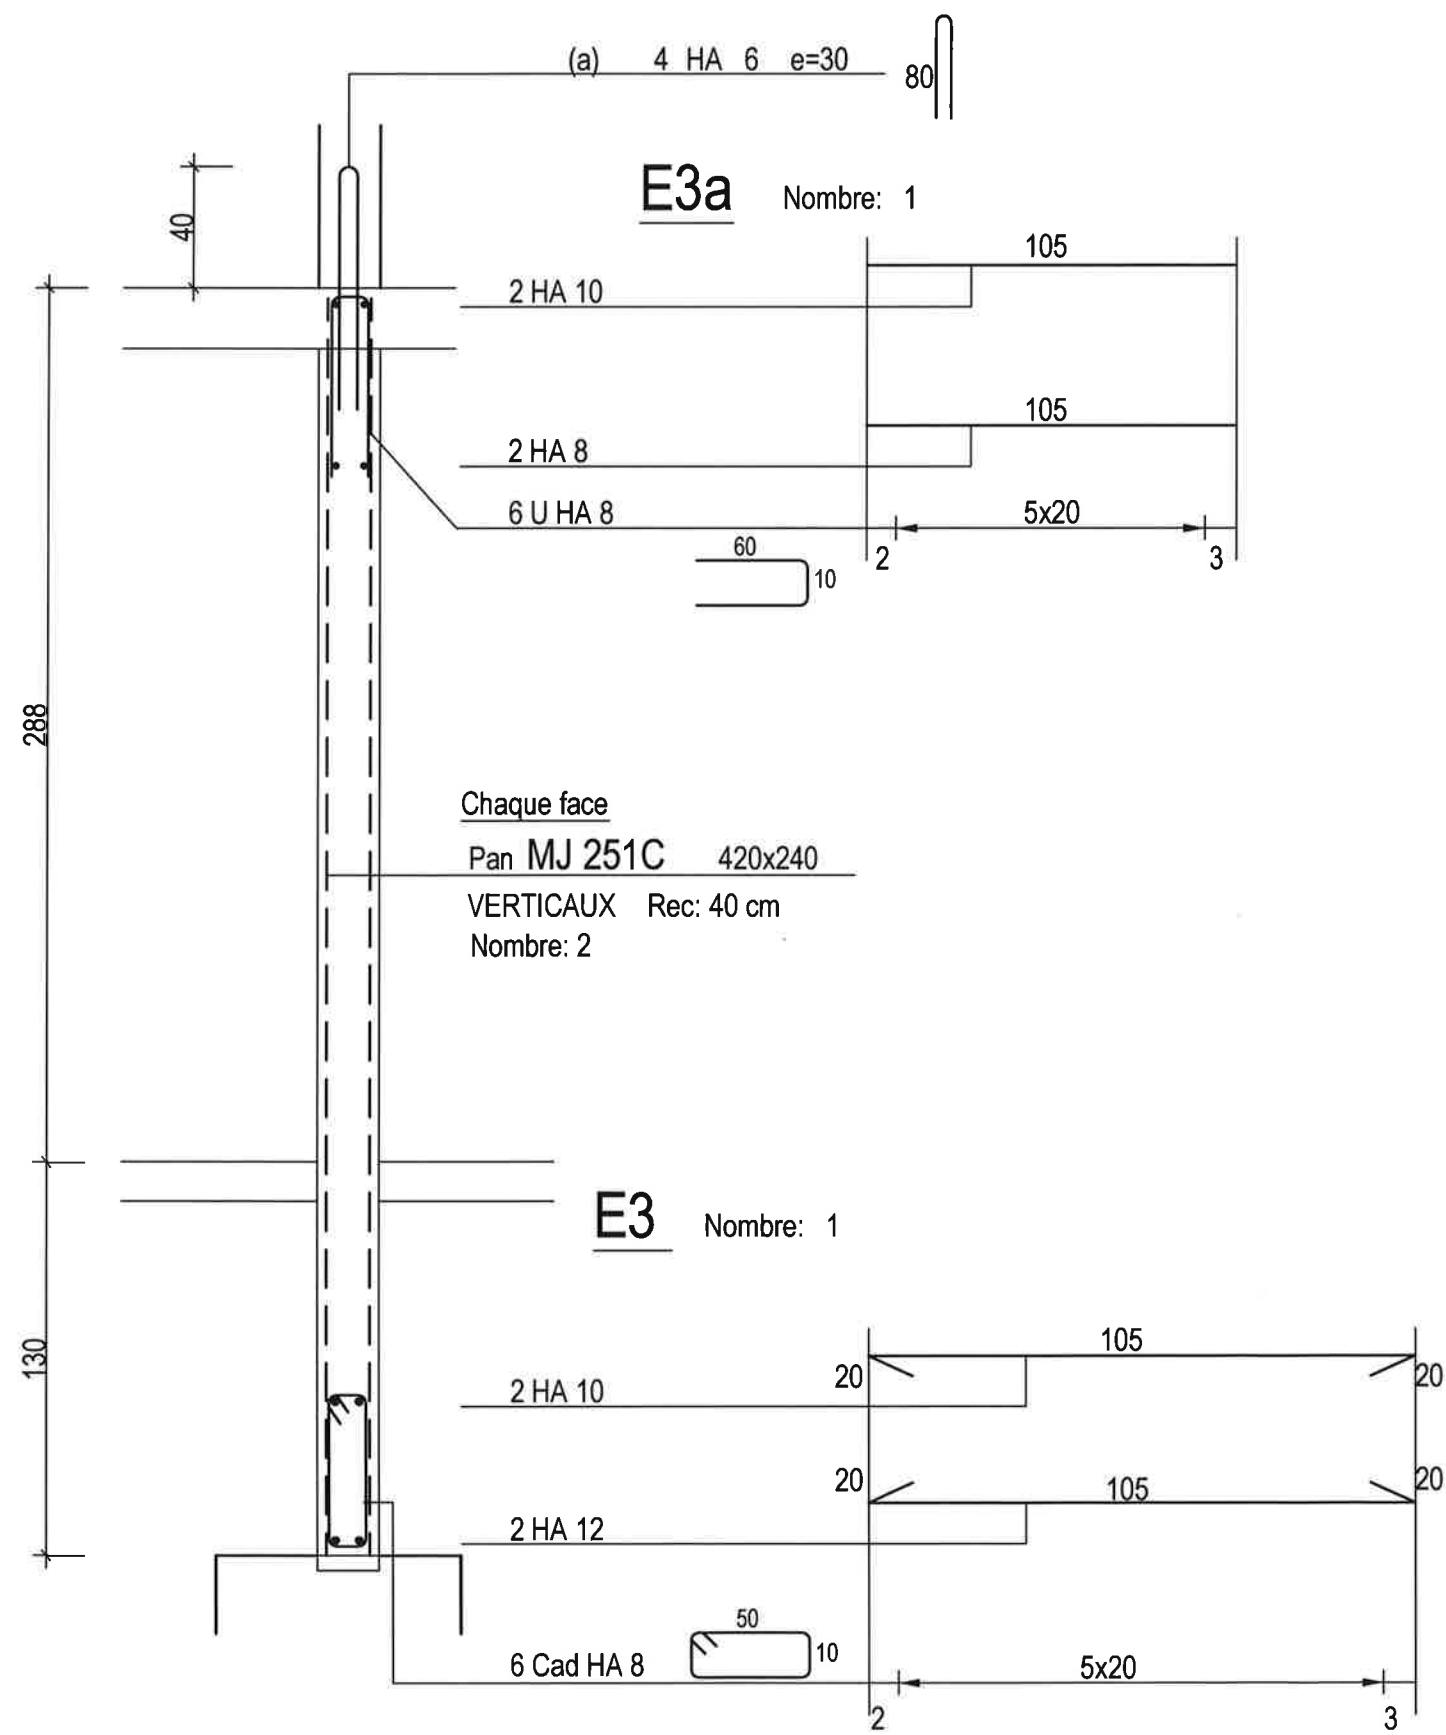


POUTRE VOILE : PV4

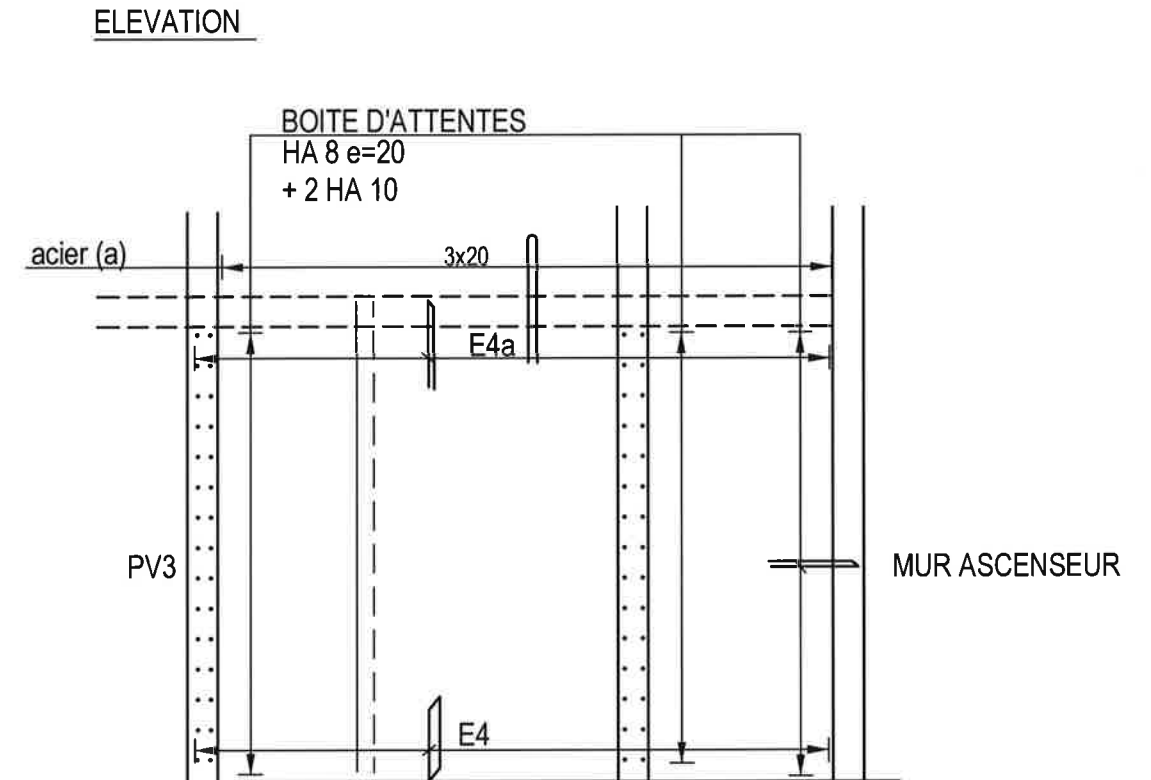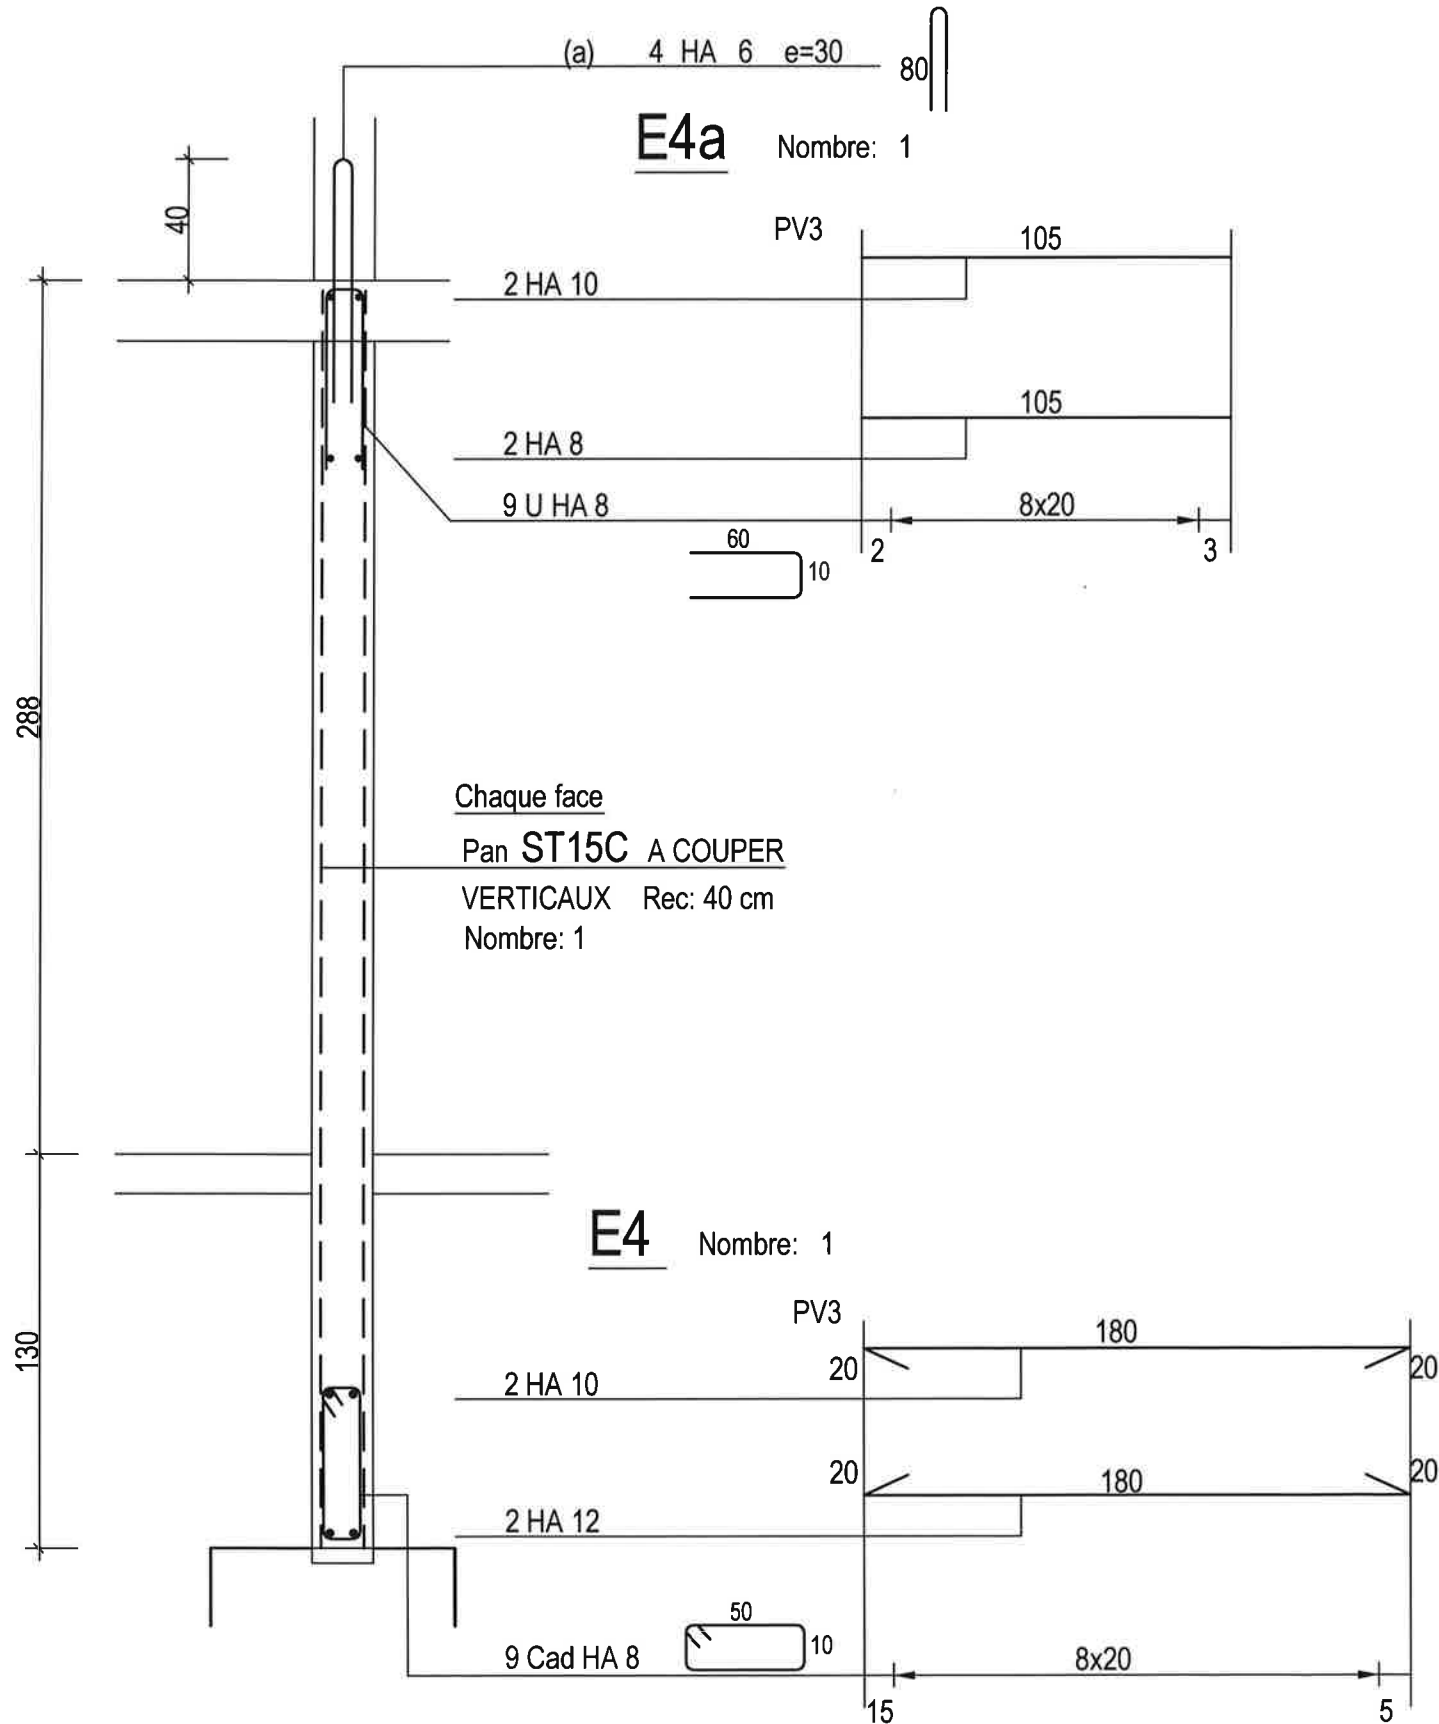


POUTRE VOILE : PV5

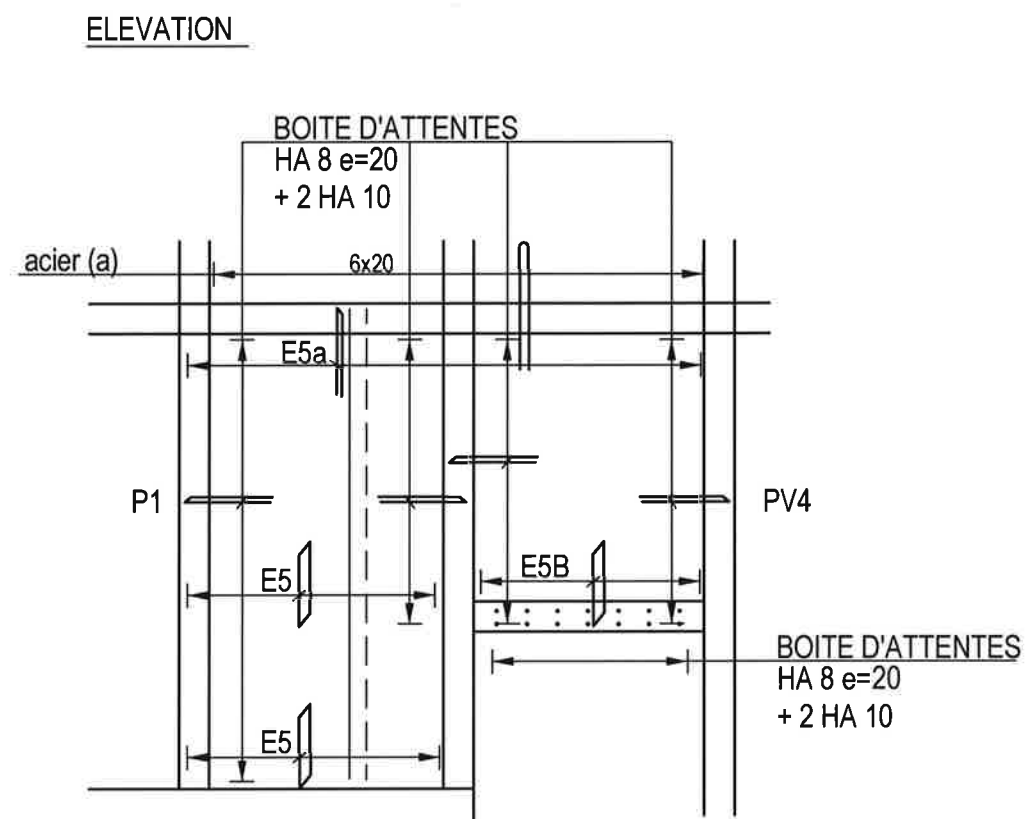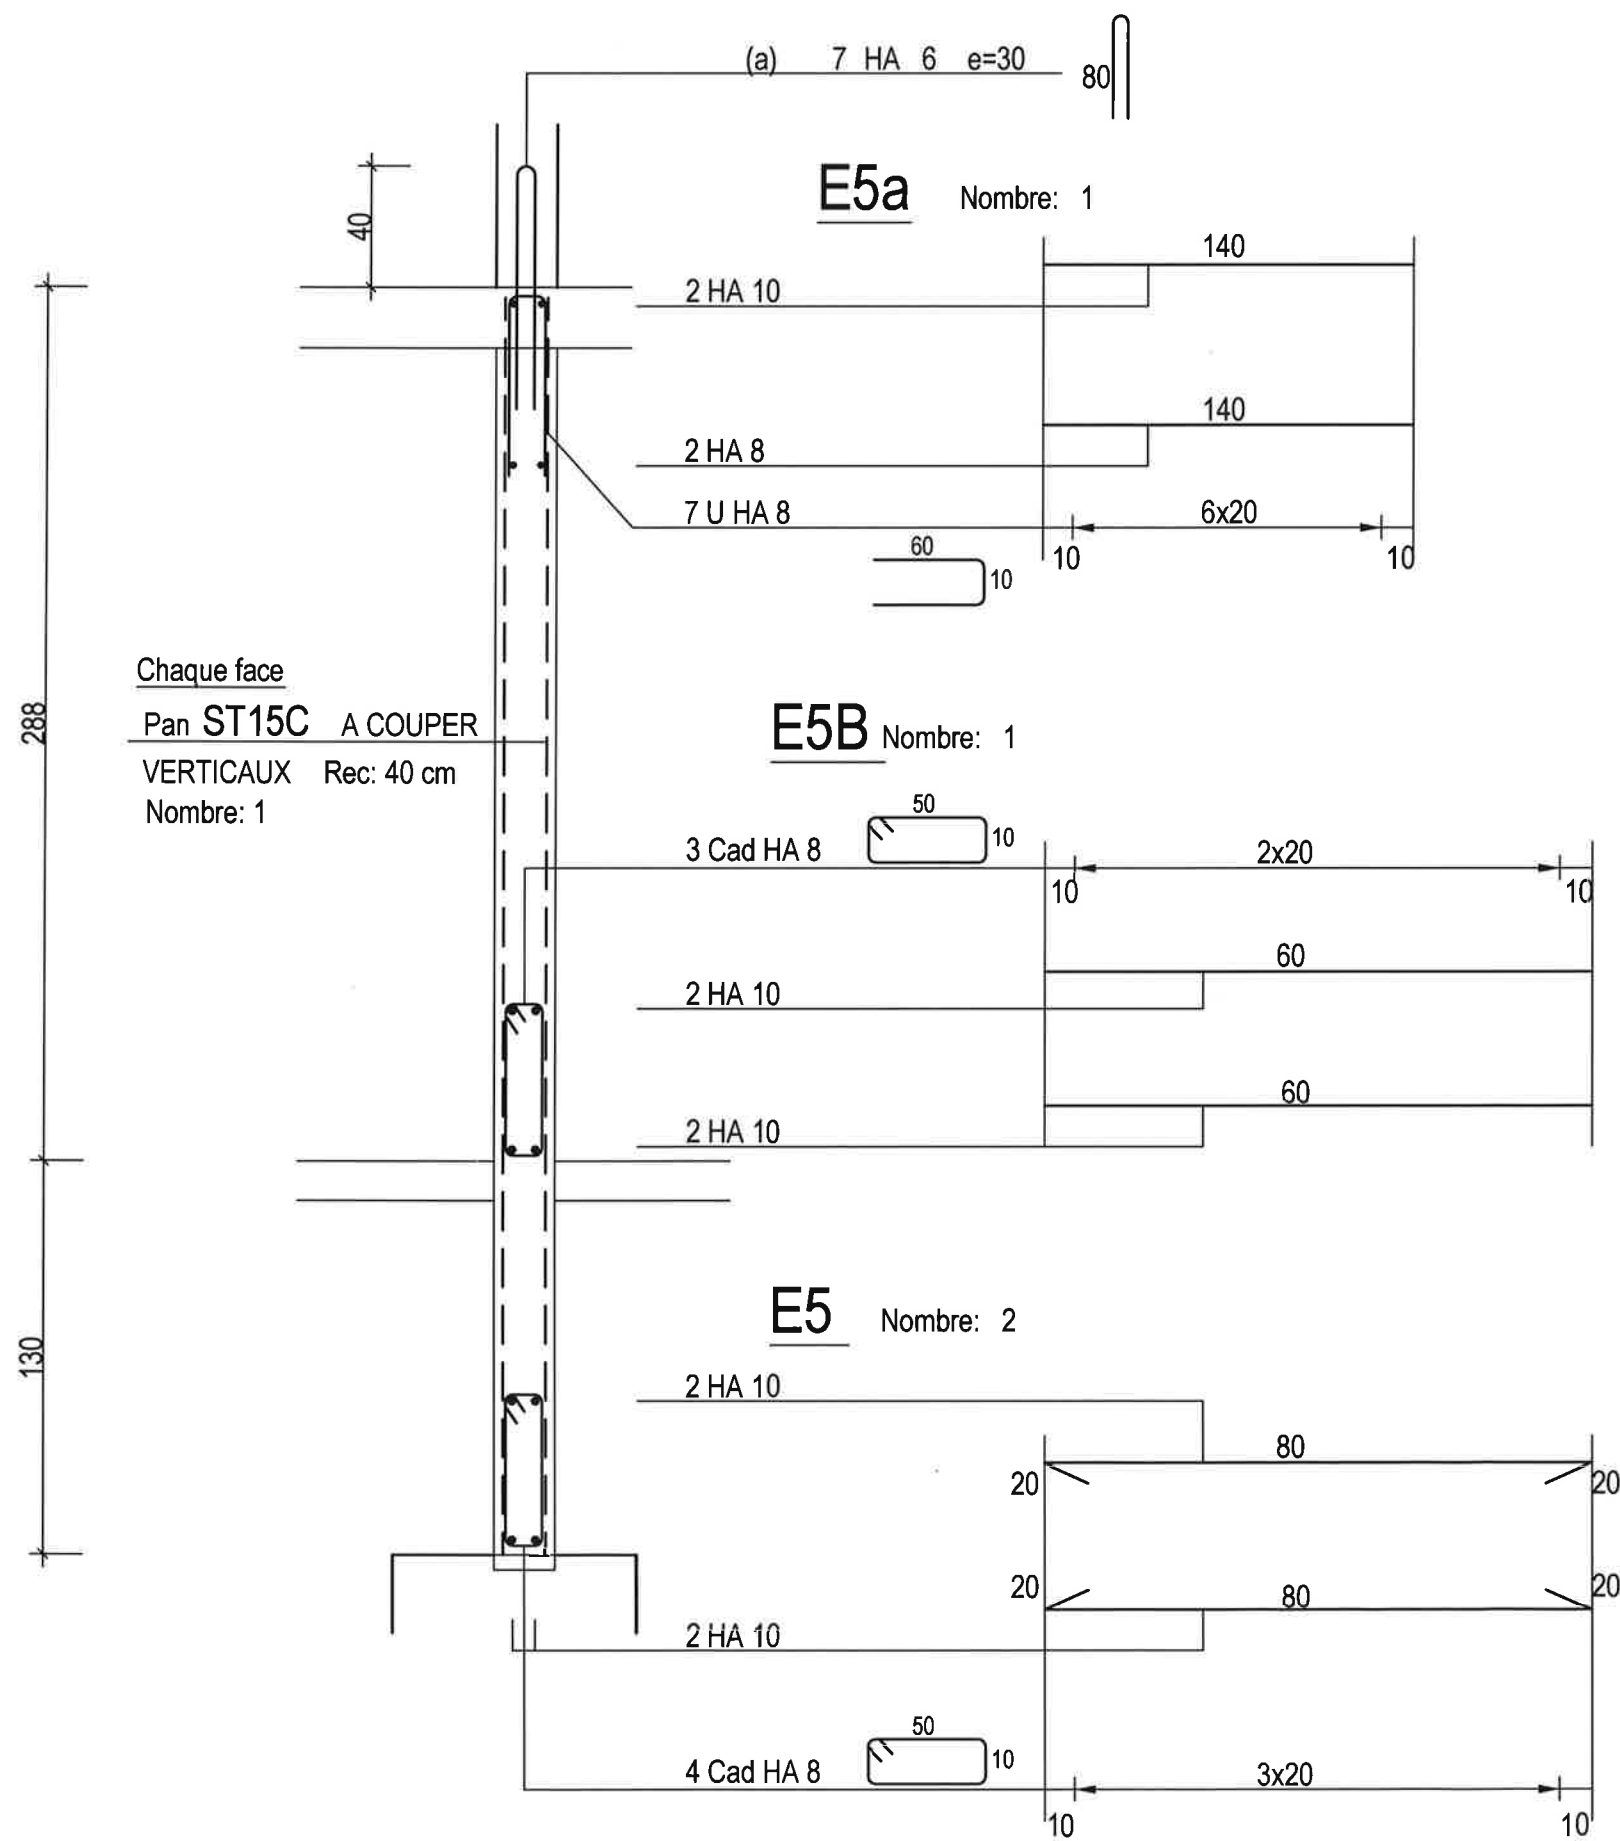



POUTRE VOILE : PV6

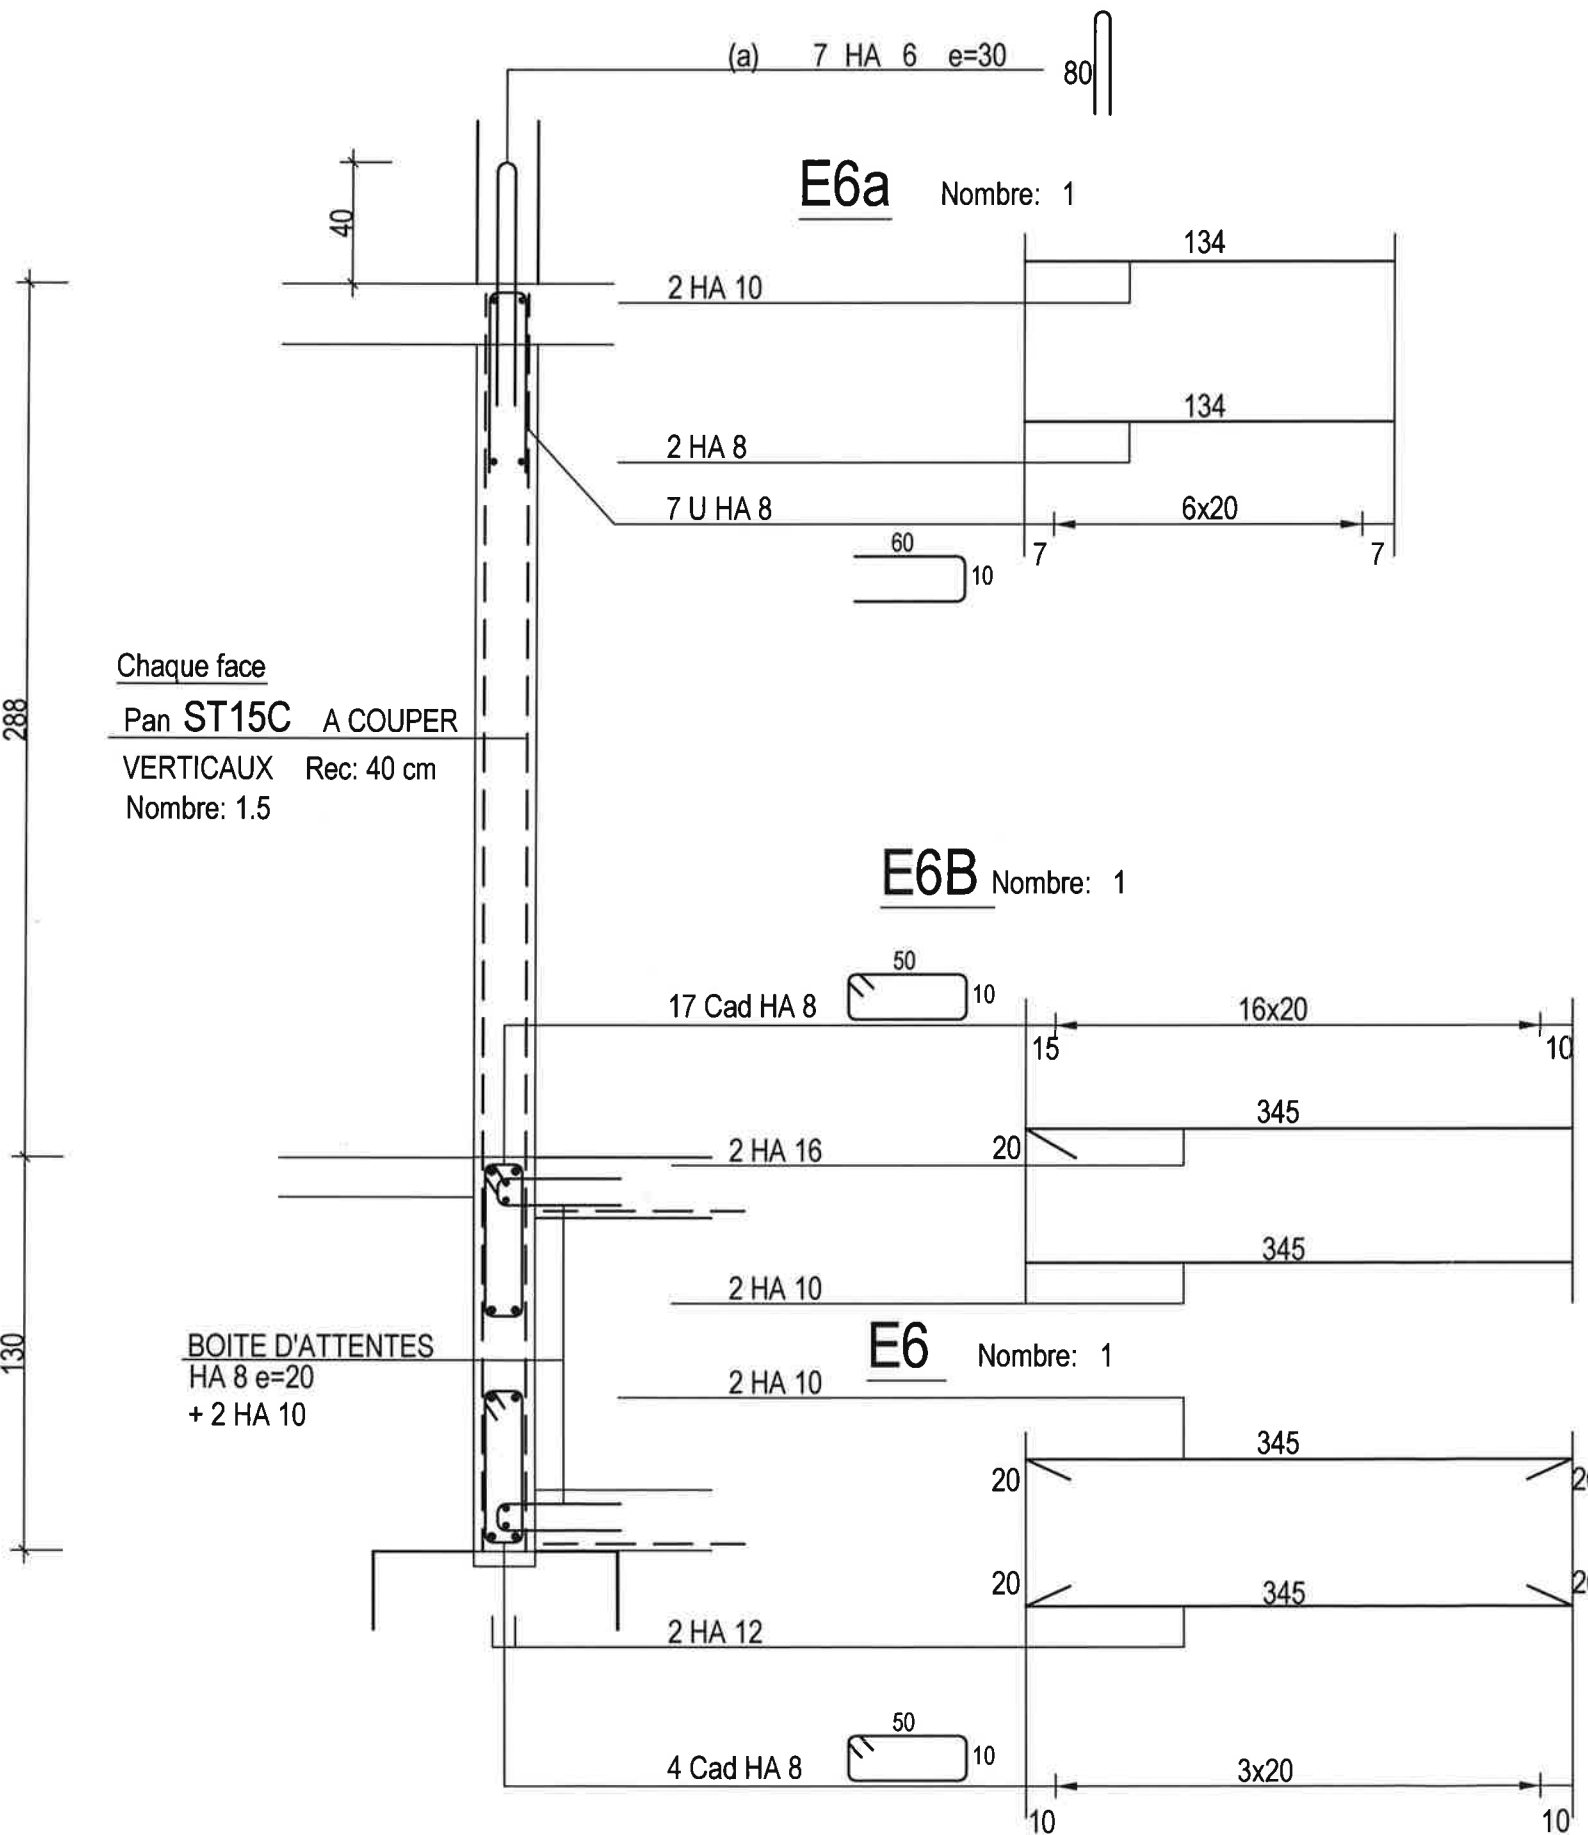

ELEVATION

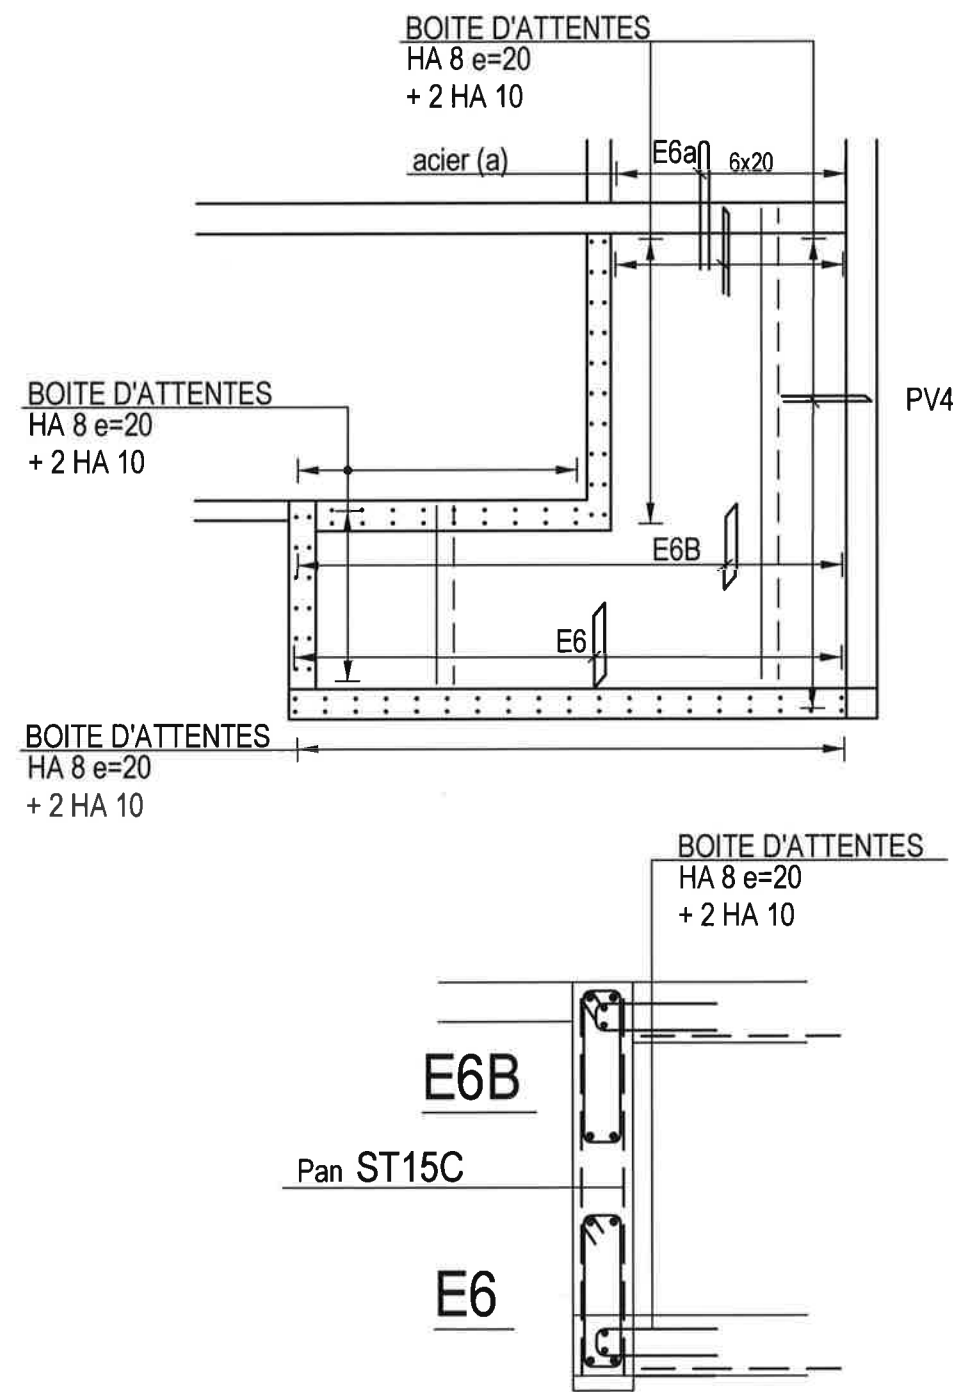


POUTRE VOILE : PV7

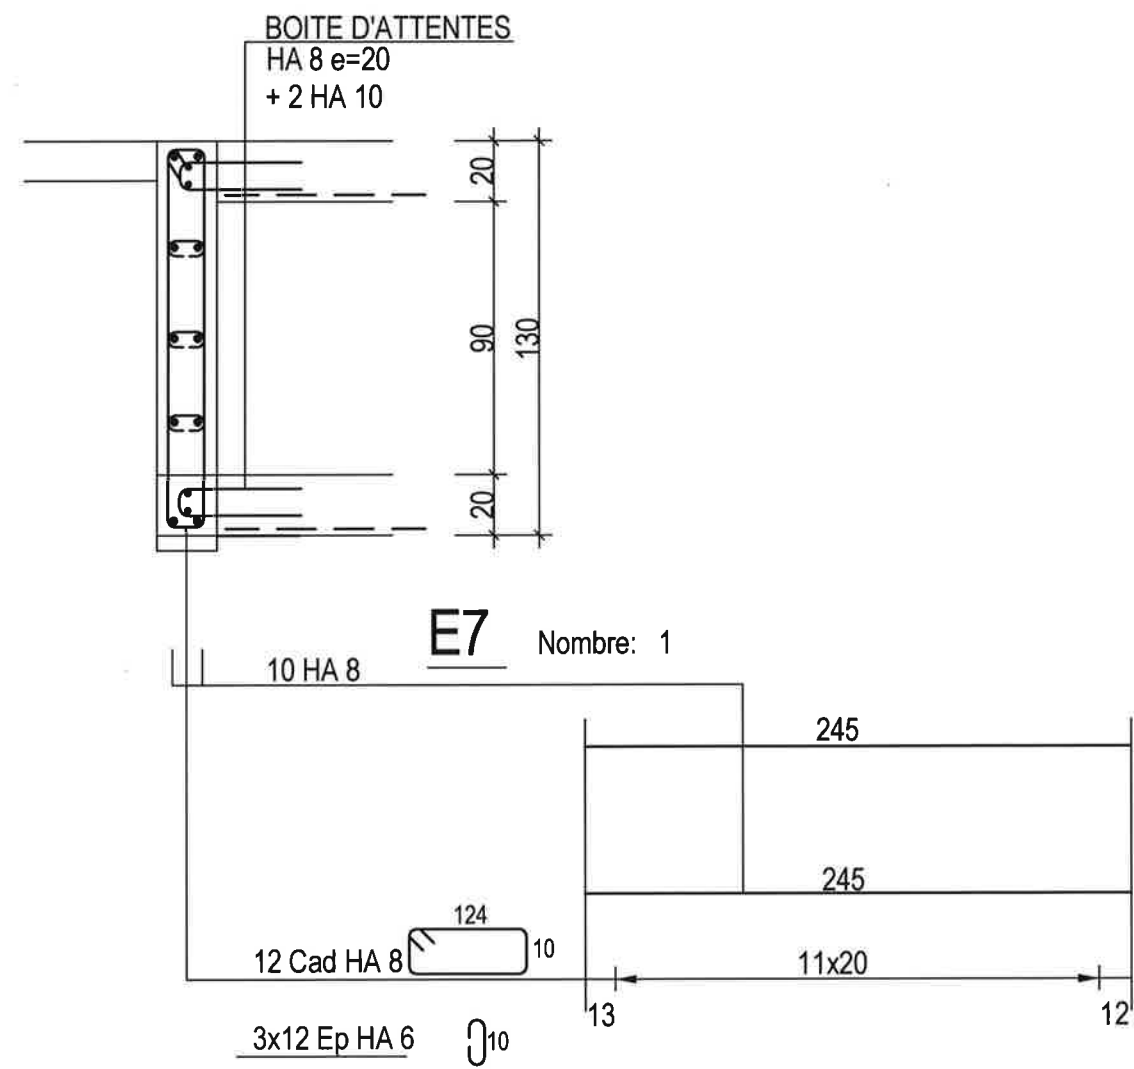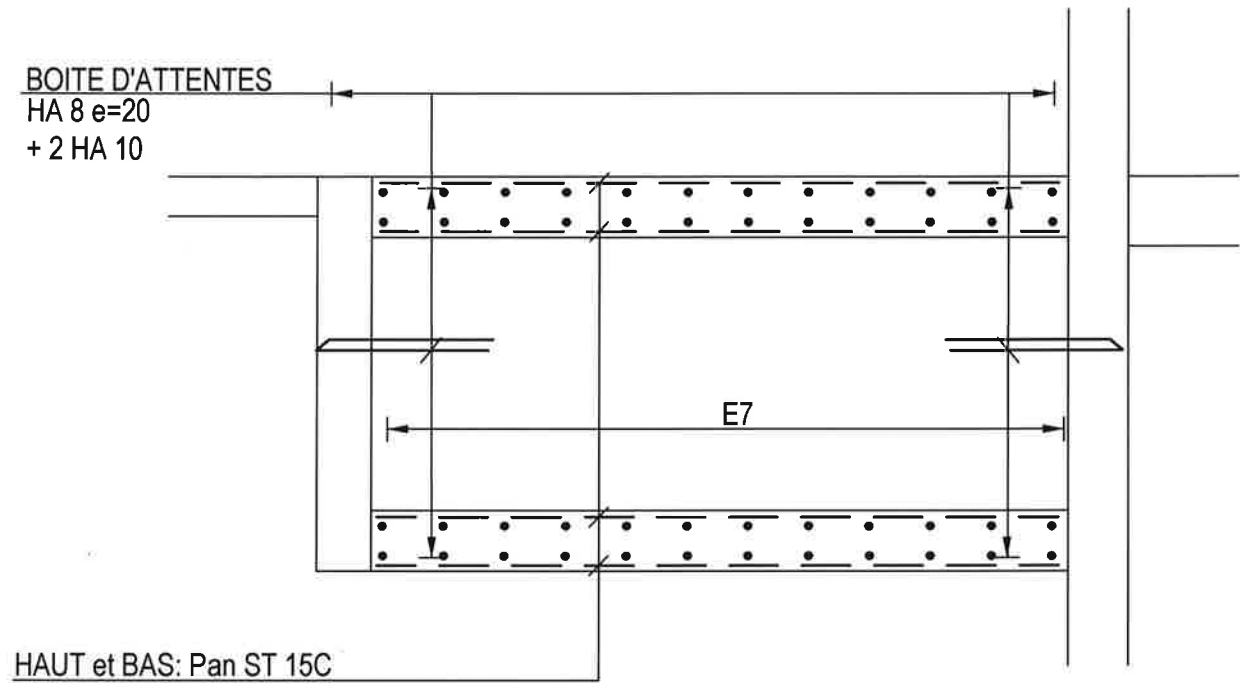

P1

Nombre: 1


60x60


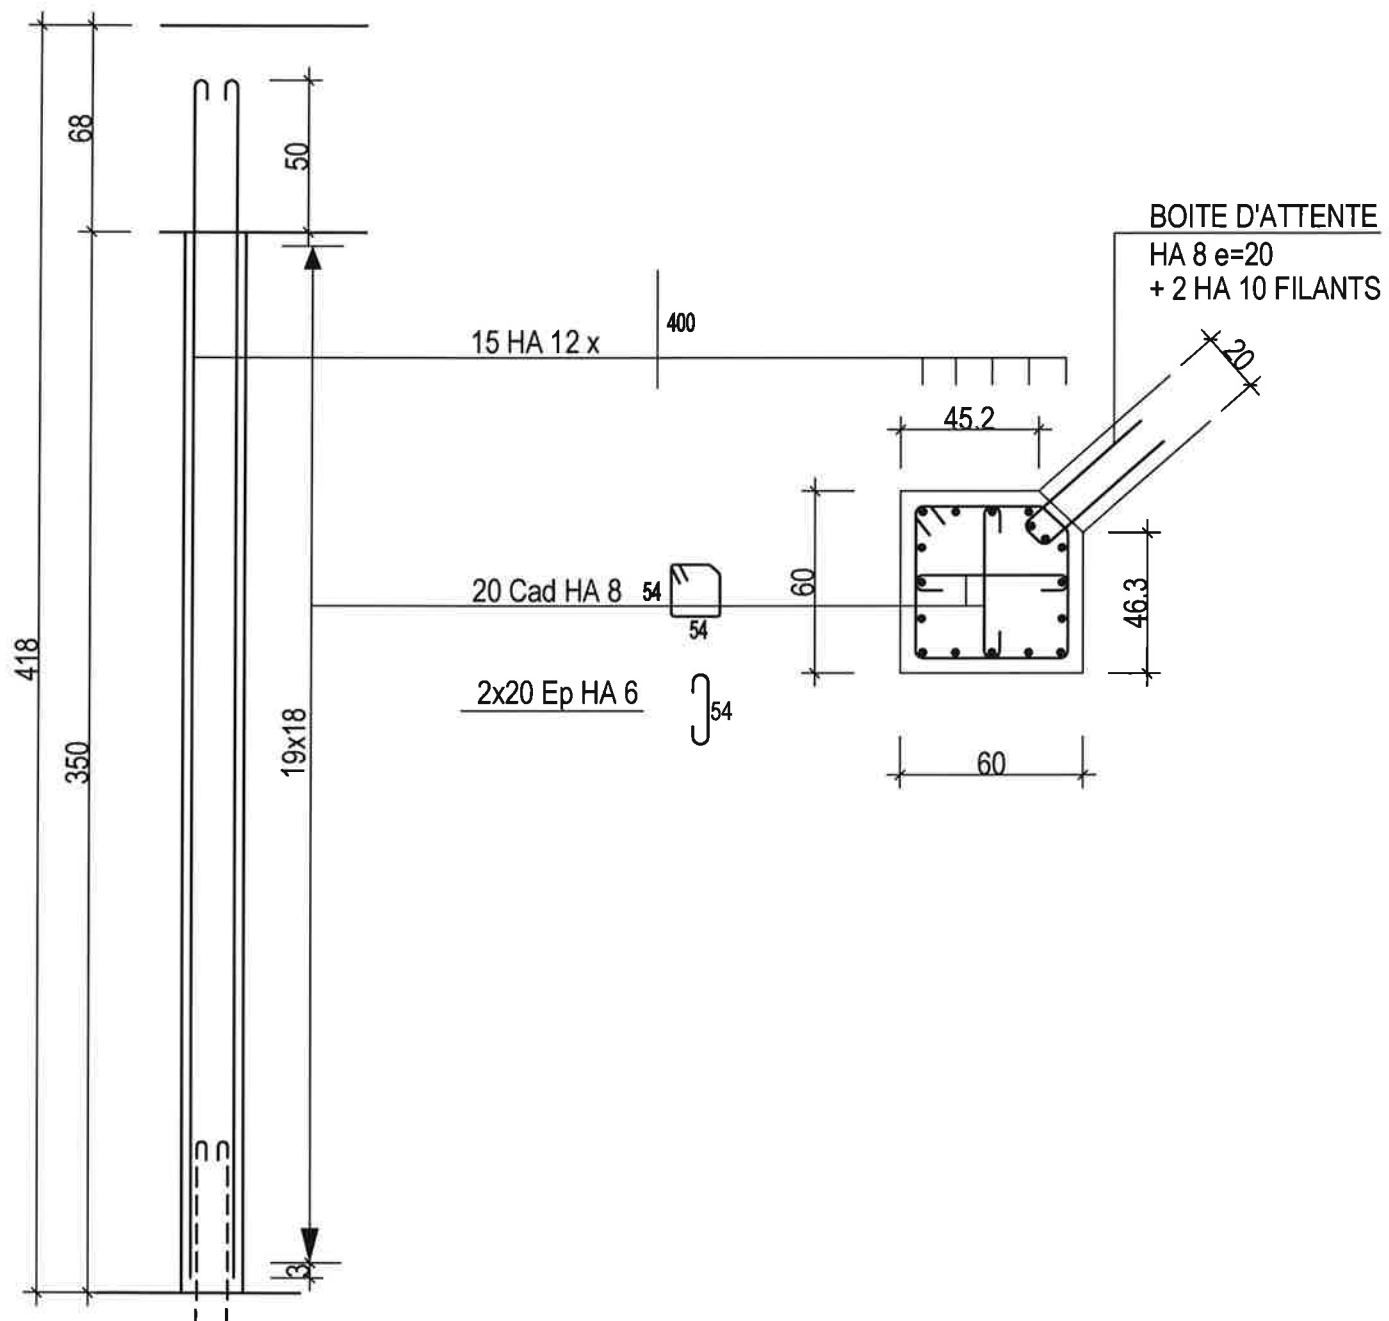



P2

Nombre: 1

50x40

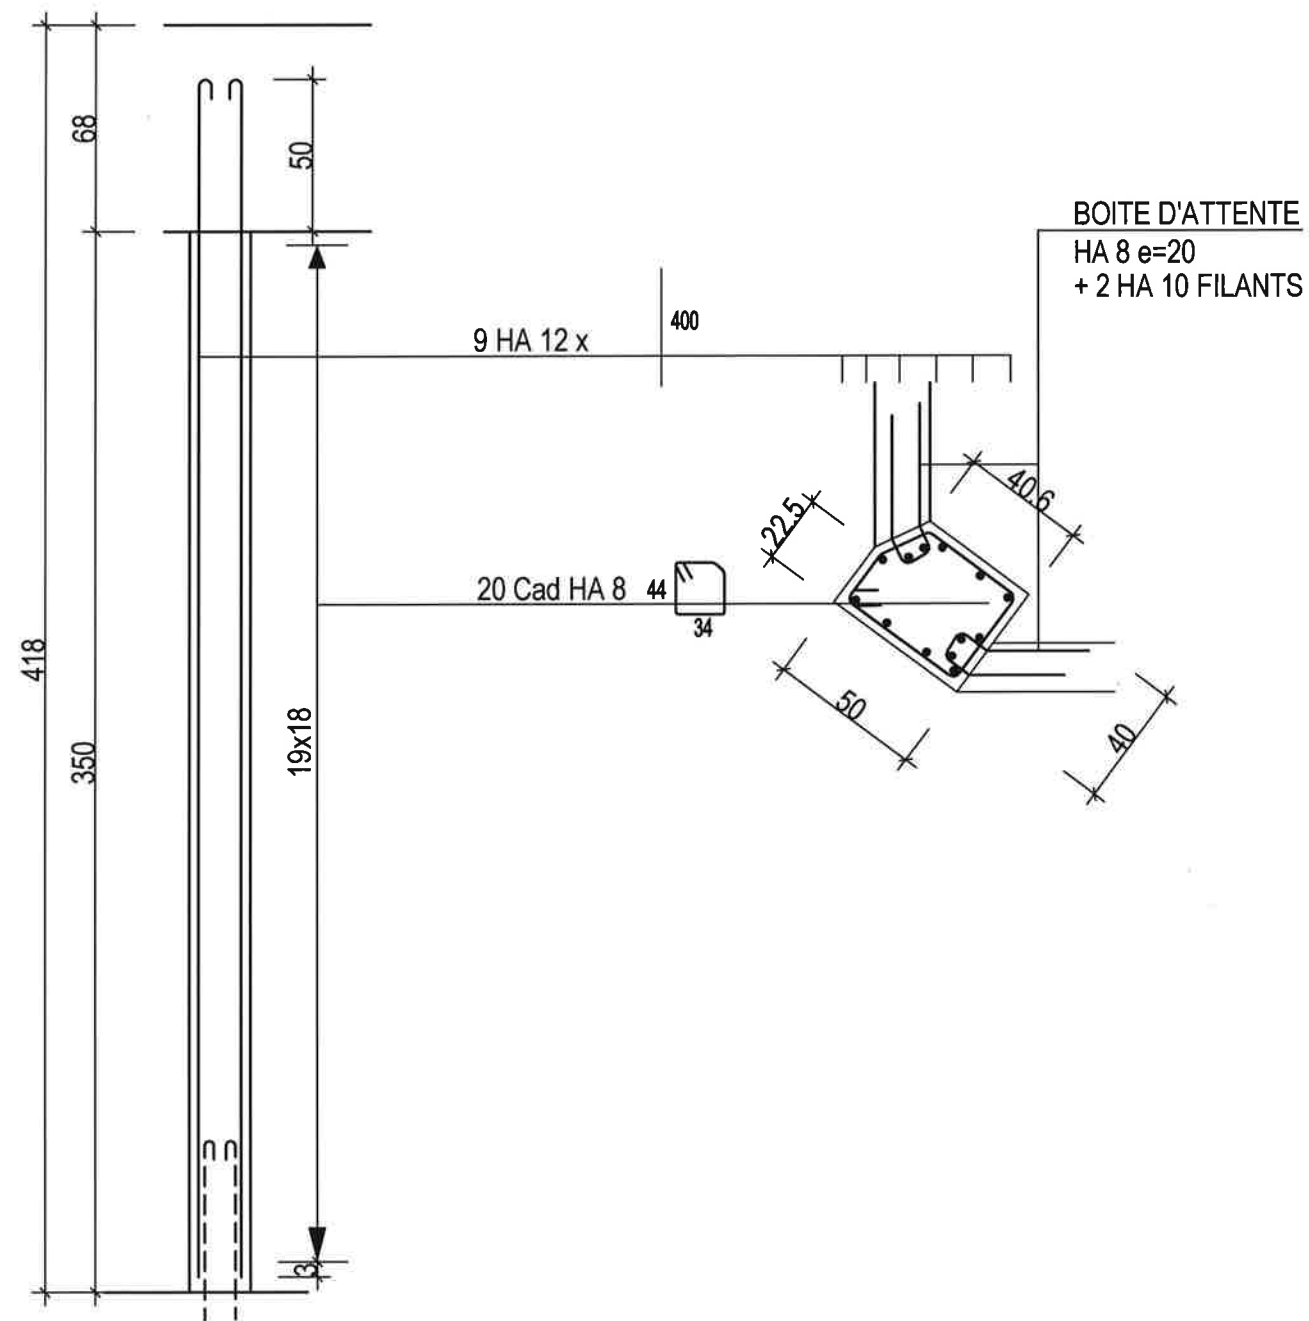

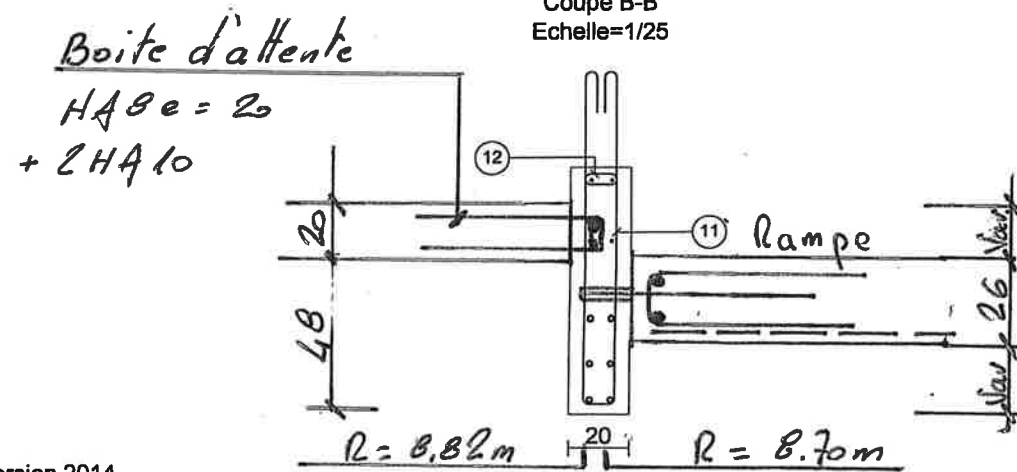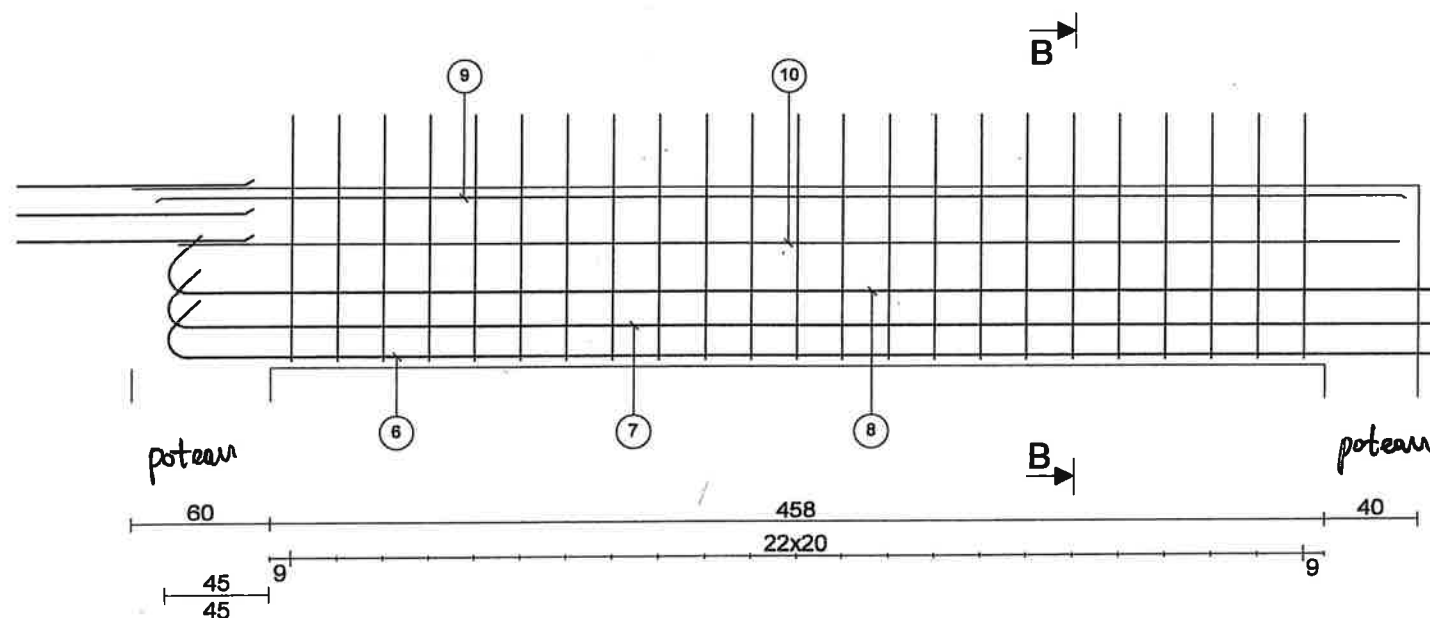

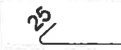	Barre	Lg	Forme
6	2HA16	599	 135° 573
7	2HA16	599	 135° 573
8	2HA16	599	 135° 573
9	2HA8	543	 543
10	2HA8	530	 530
11	23HA8	259	 110 11
12	23HA6	28	 11
	</		

DALLAGE

