



- Pan MJ 636 x 600 Nb: 4
x 530 Nb: 4
x 510 Nb: 1
x 270 Nb: 1
- Pan MJ 251C x 480 Nb: 1
x 360 Nb: 1
x 300 Nb: 1
- Pan MJ 188 x 90 Nb: 20
x 210 Nb: 5
- Pan ST15C 400x240 Nb: 5
- Pan ST50C 600x240 Nb: 1
- + COMMANDE MJ636 DE LA RAMPE VOIR COUPE TYPE RAMPE

ARMATURES INFERIEURES

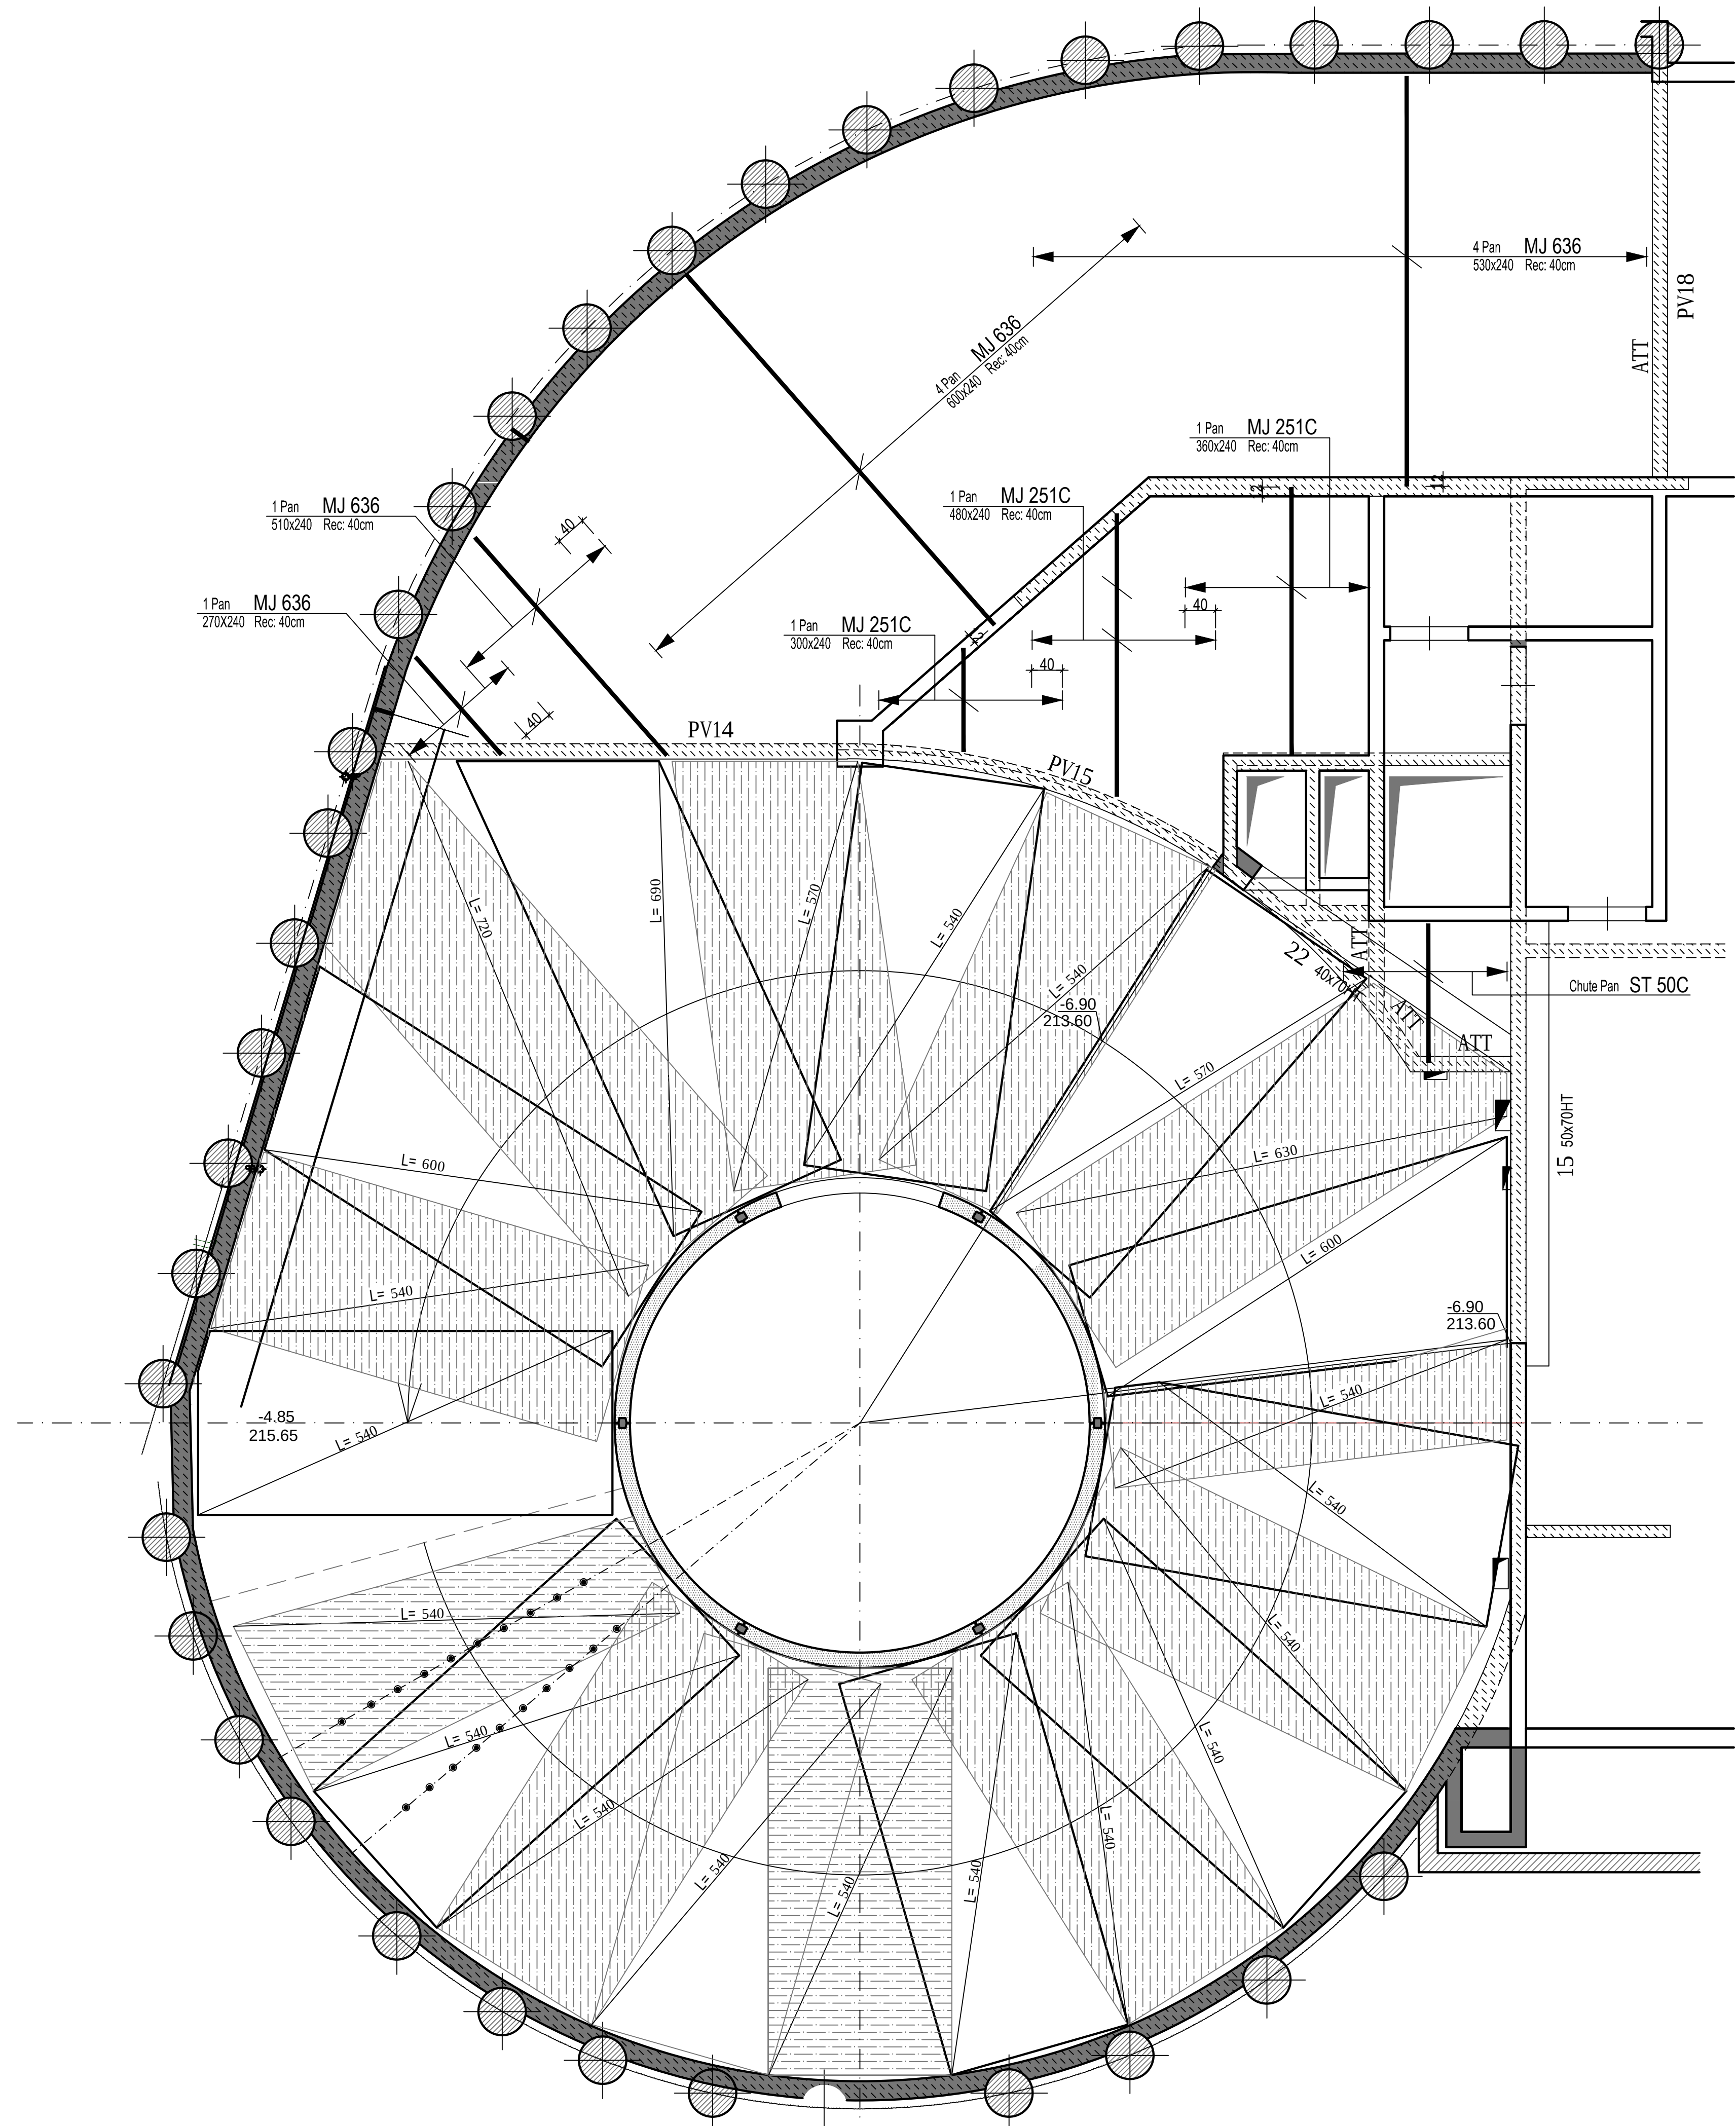


COUPE D

Ech: 1/25

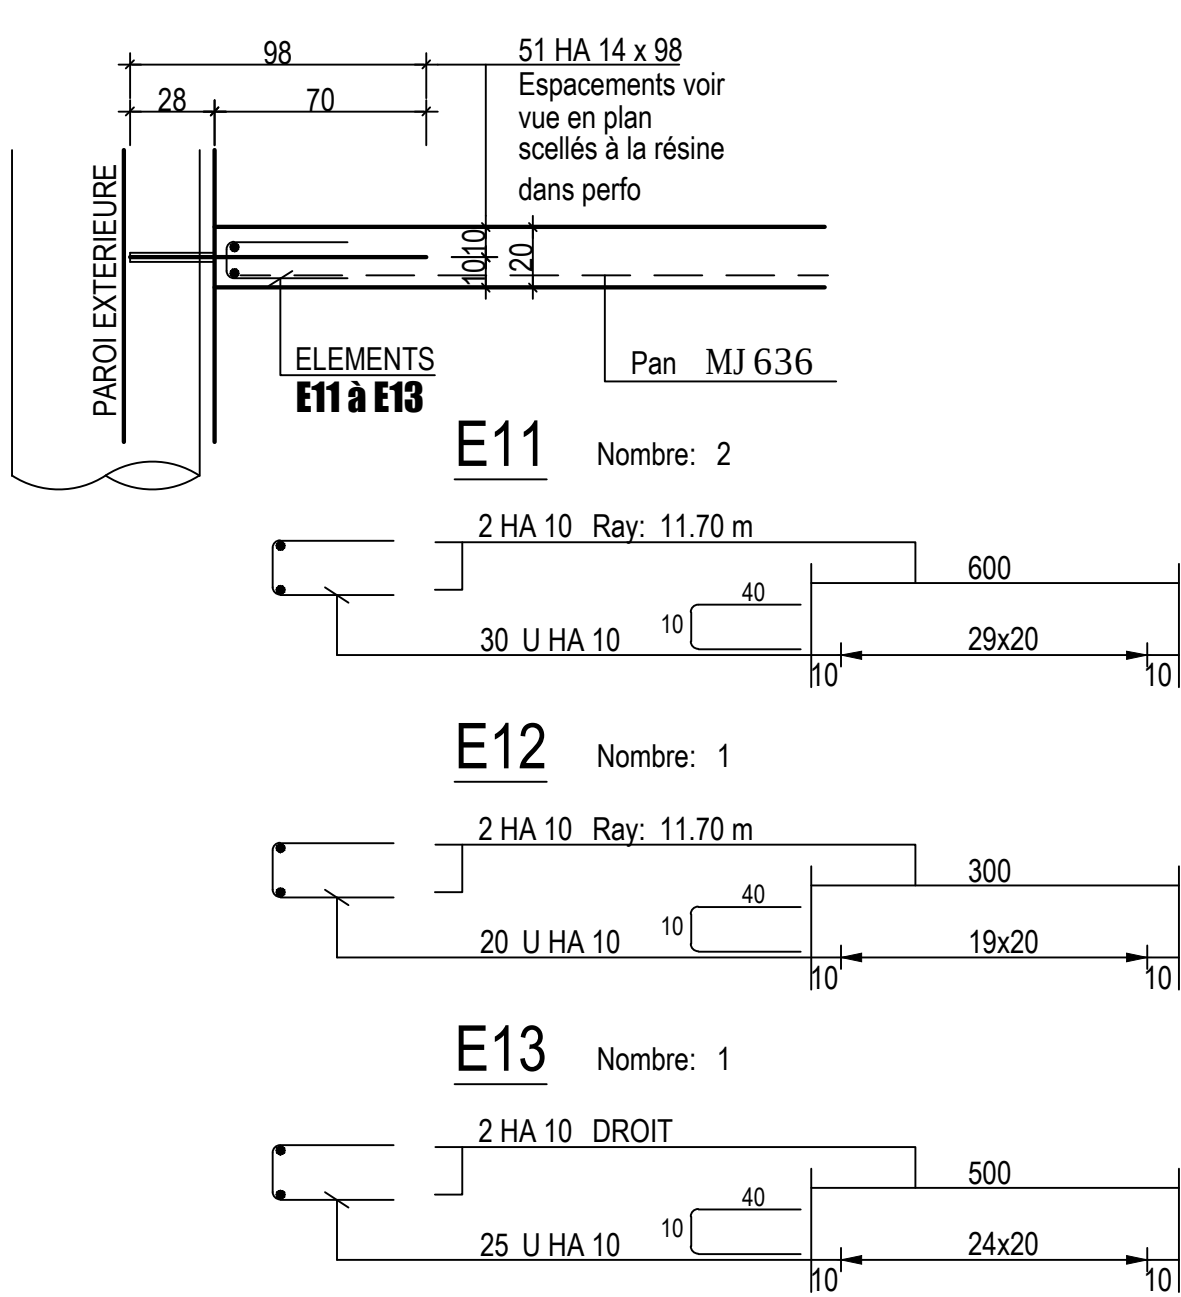


COUPE C

Ech: 1/25

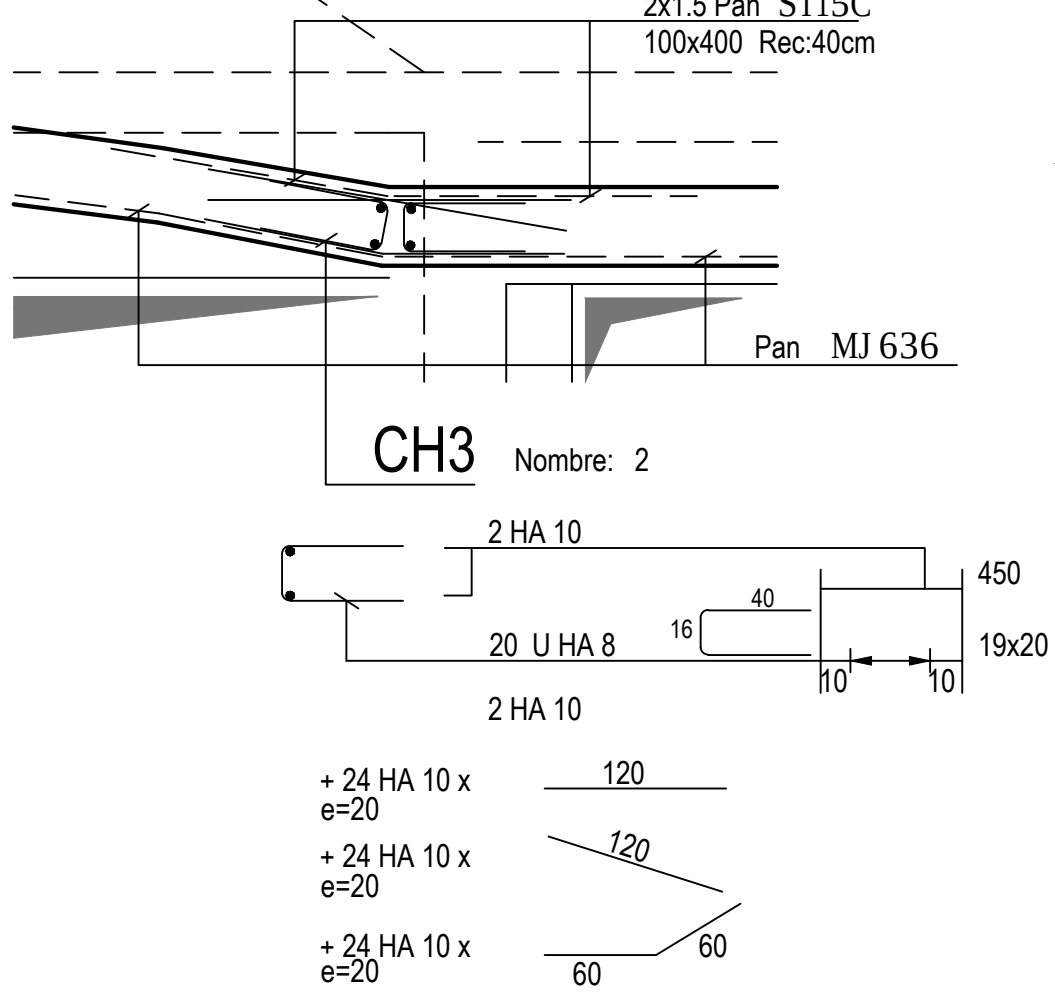


COUPE B

Ech: 1/25

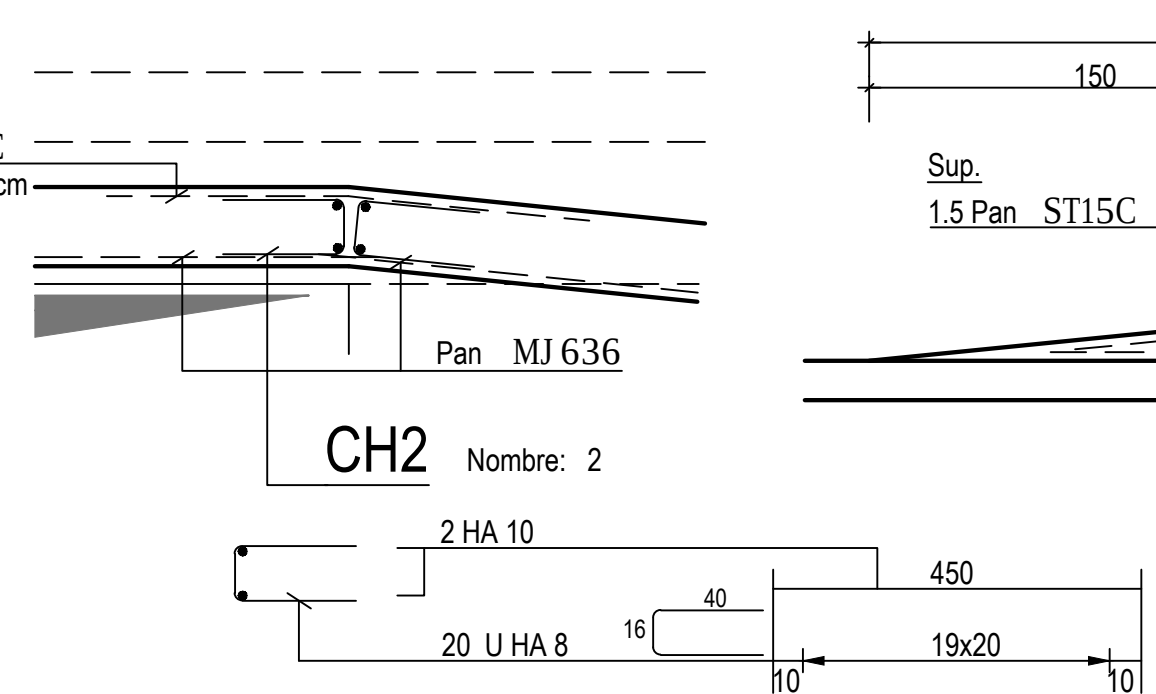


COUPE A

Ech: 1/25

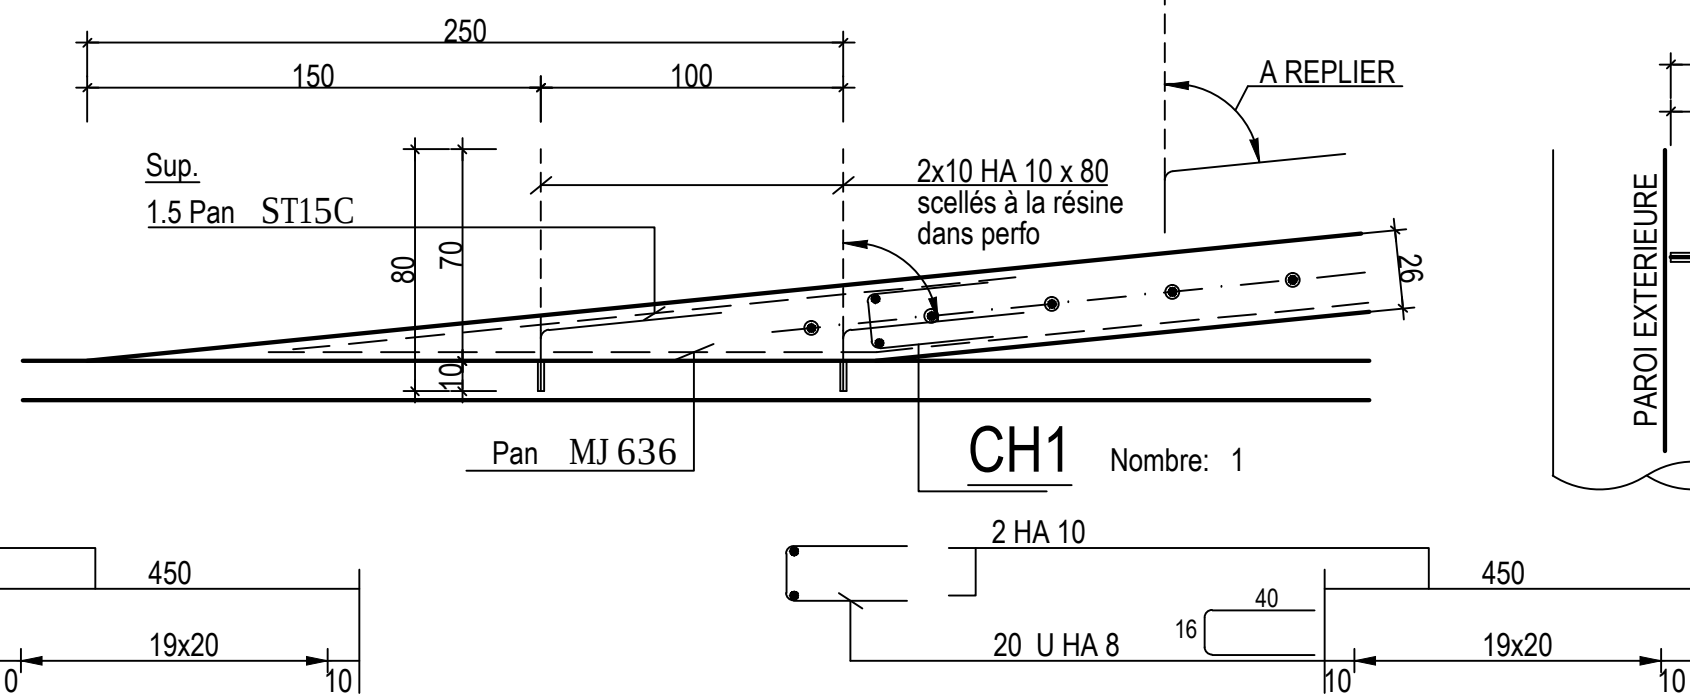

COUPE TYPE DALLE RAMPE

Ech: 1/25


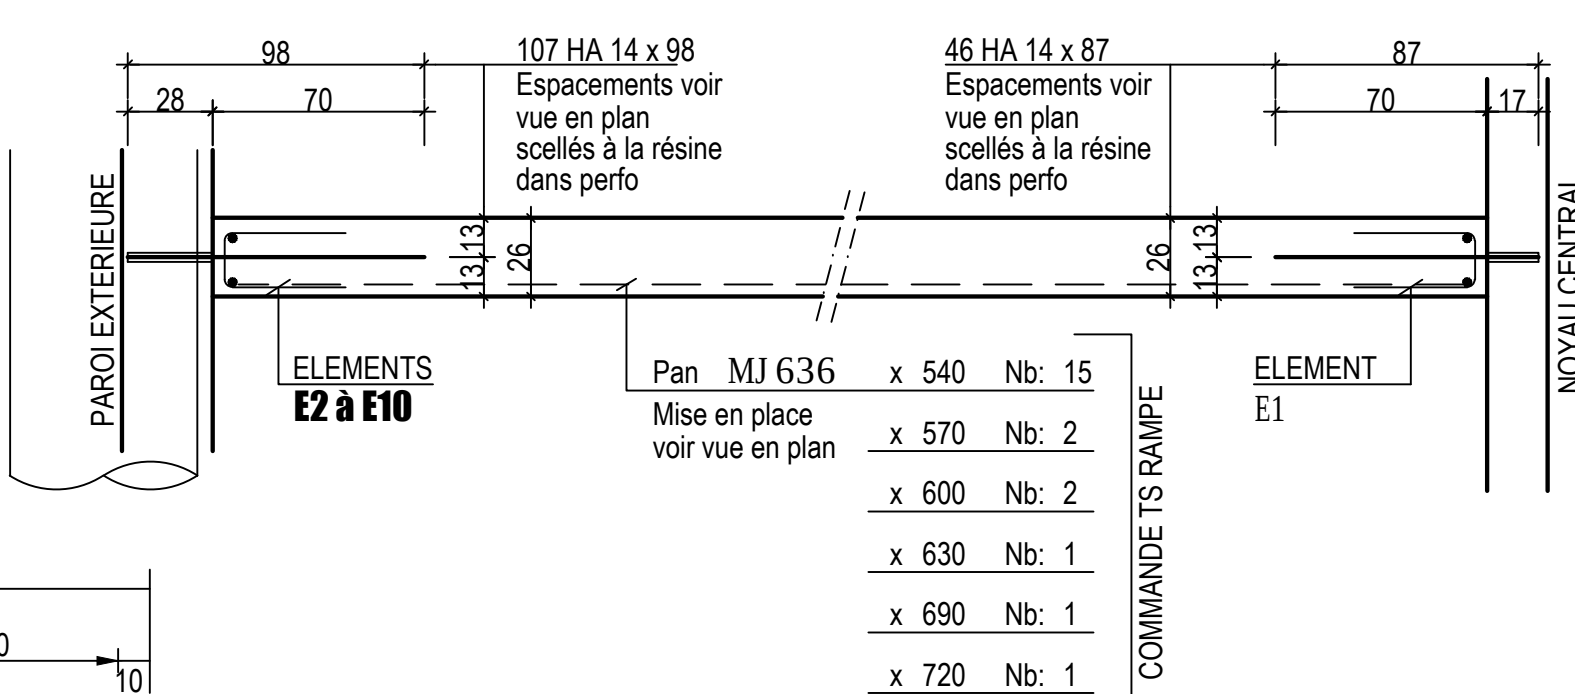


ARMATURES SUPERIEURES

+ PERFO

ATT

Nb: 2

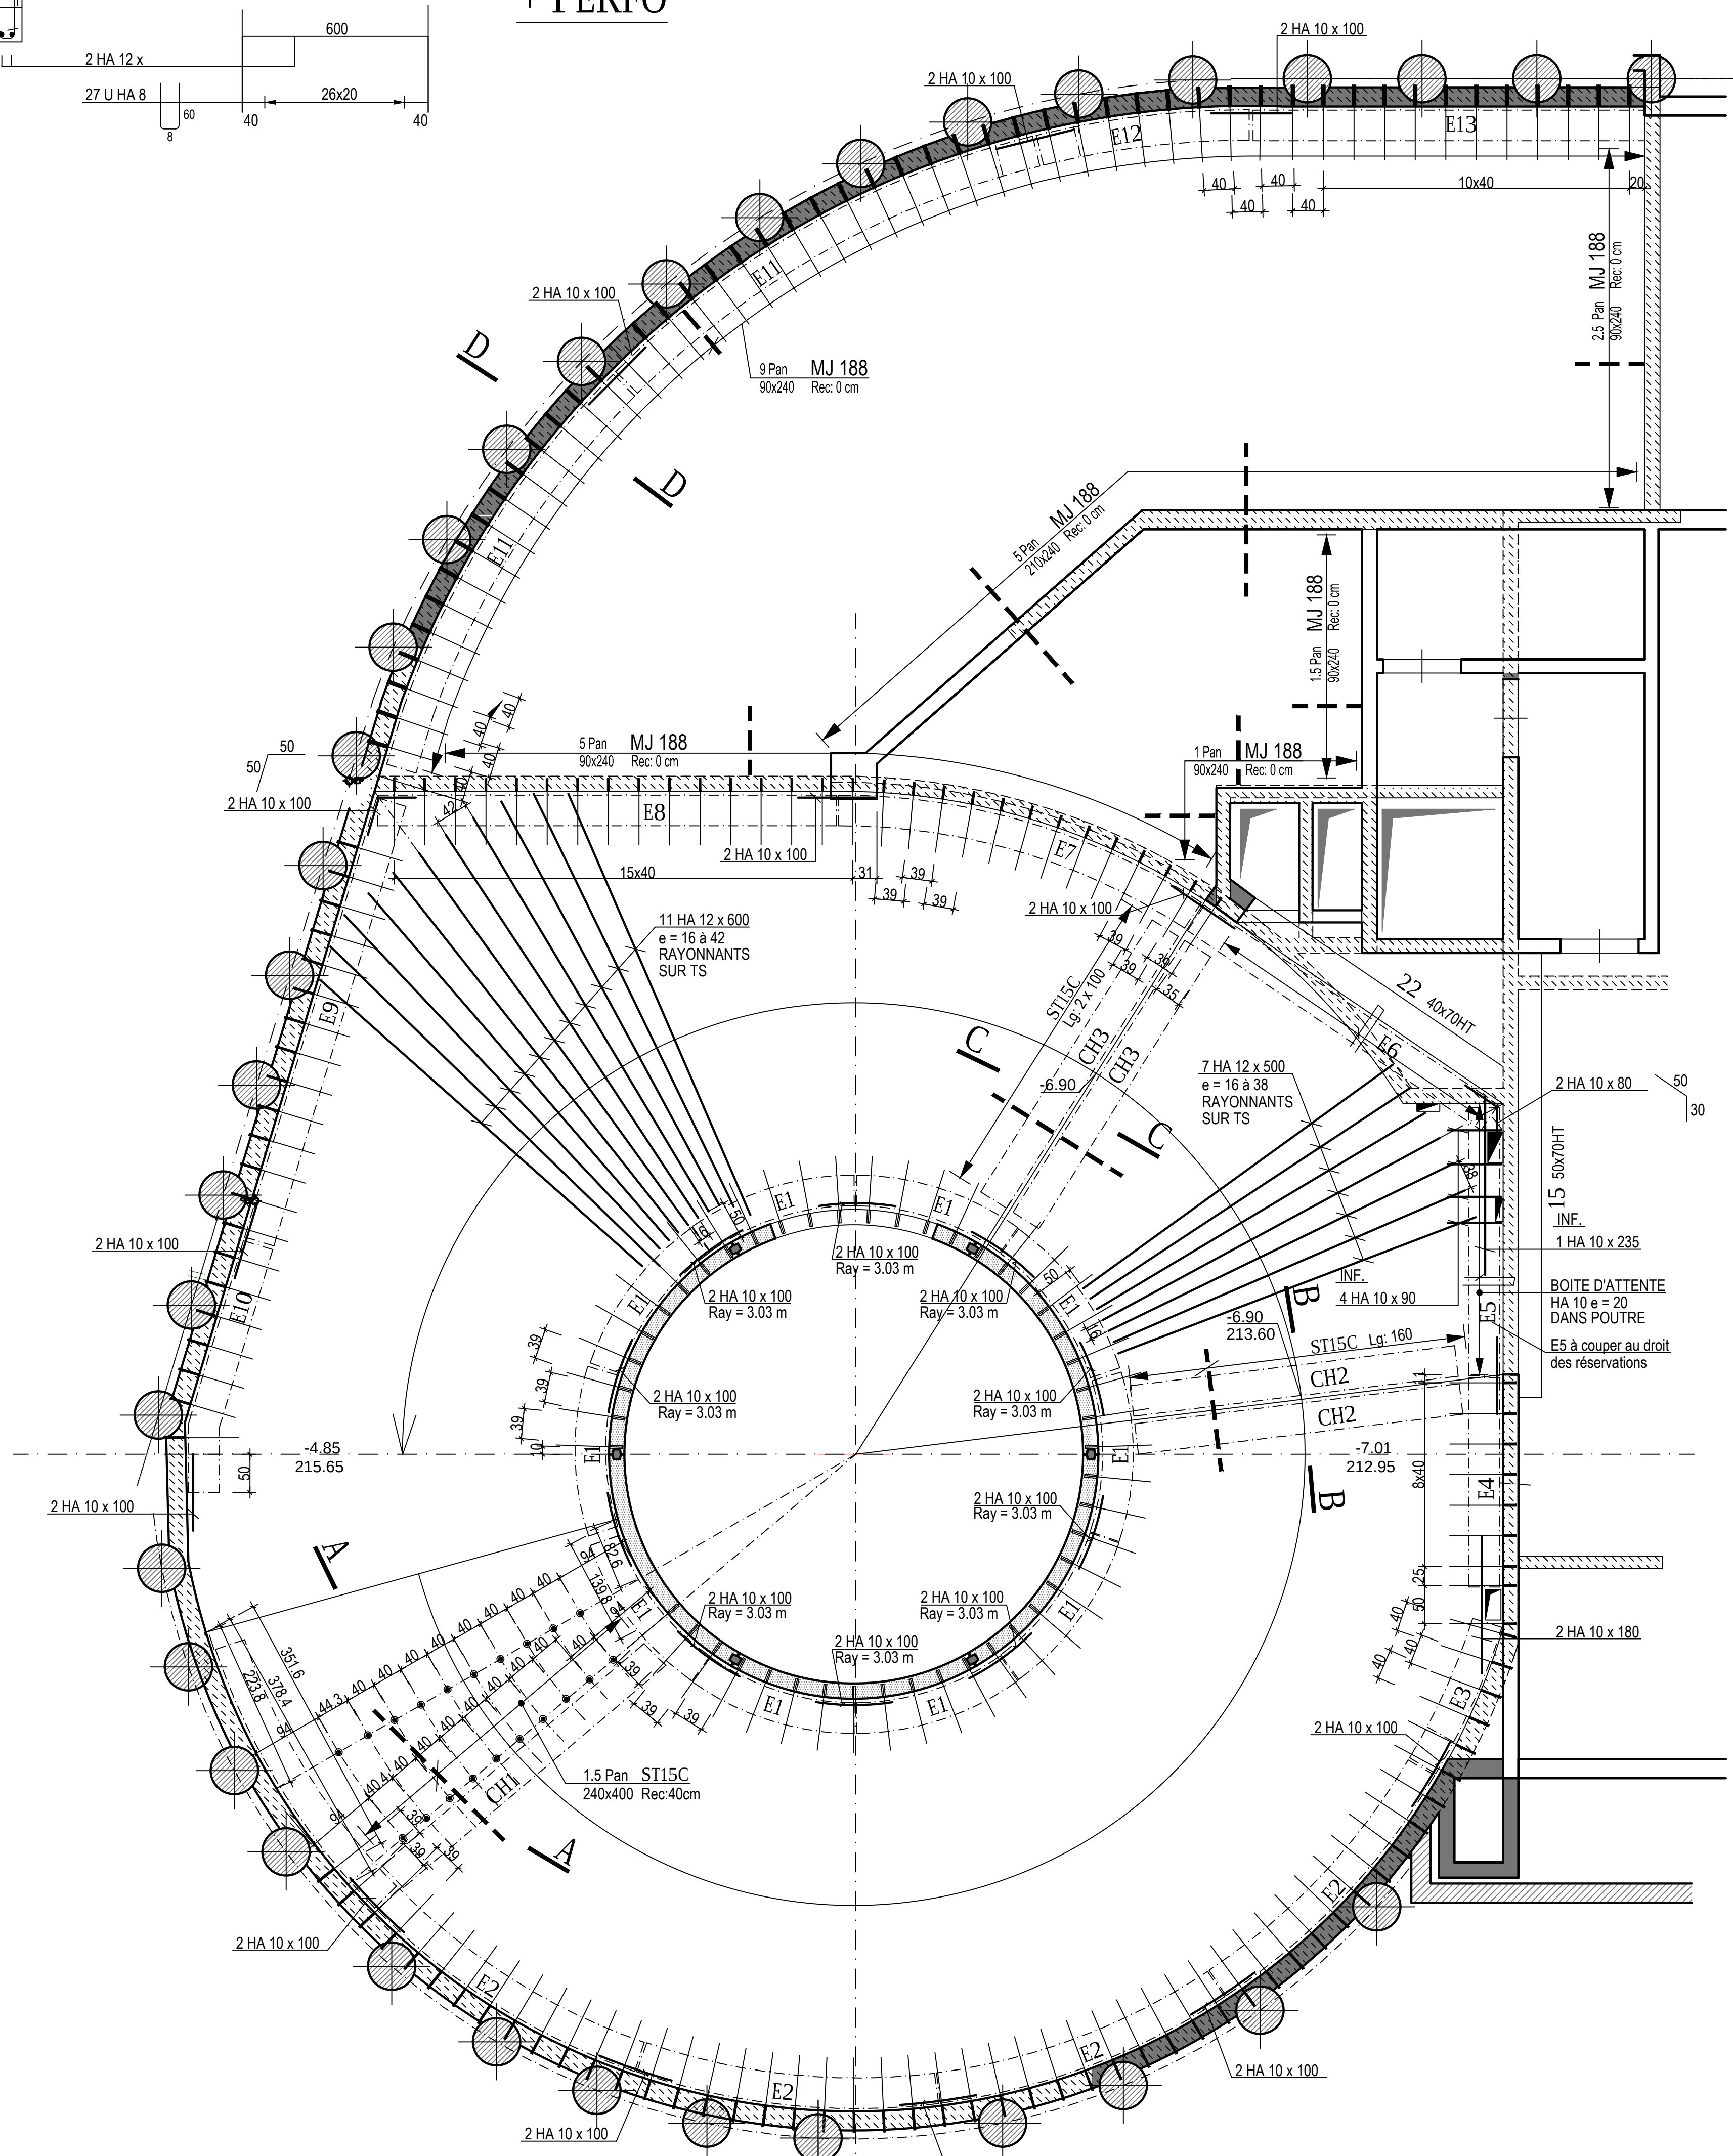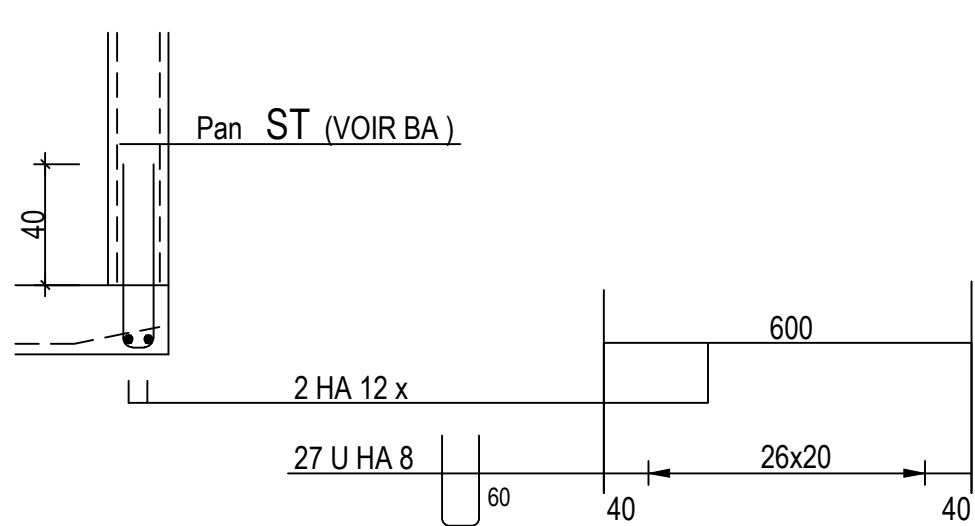

NOHAO

Chemin de Fontanière-69350 La Mulatière
Création de logements

Les entreprises réalisant les travaux devront tenir compte des données dans architecte lors de la réalisation des travaux
Les plans du Bât MATTE ne doivent servir qu'au corps d'état concerné et doivent être des plans d'exécution

ARCHITECTES: Atelier DE LA PASSERELLE M.O. Délégue: -
BET STRUCTURE: BET MATTE M.O. M.O. -
BET FLUIDES: PRELEM CSPS: PSO ingénierie
ECONOMISTE: EXECO M.O.E.: SUD EST COORDINATION
BUREAU DE CONTROLE: VERITAS ENTREPRISES: Fontanel-poc

Bât A
PLANCHER sur -3 entre files 1 et 3
ARMATURES DALLE

INDICE	DATE	MODIFICATIONS
A		

MATTÉ
BUREAU D'ETUDES
STRUCTURES ET FLUIDES
119 BOULEVARD STRAUBENHOFER 69100 VILLEURBANNE
Tél: 04 72 44 33 87 Fax: 04 72 44 35 59
E-mail: dm@matté.fr

Dessiné par: J.BONDETTI
Contrôle par: P.LIN
Ech:

DOE

PLAN N°
A28 A

DATE: 06-01-2016

Affaire N°
S.13.12.118