




DALLES

- FINI: -3.20/-217.30
DALLE BA Epr: 20 cm
DESSUS BRUT: -3.27
RESERVE: 7 cm
- 1 FINI: -3.27/-217.23
DALLE BA Epr: 23 cm
DESSUS BRUT: -3.27
RESERVE: 0 cm

RAMPE

- DALLE BA Epr: 26 cm
DESSUS BRUT: Voir vue en plan
RESERVE: 0 cm

SEUILS

DETAIL "1"

VUE DE DESSUS

Ech: 1/25

DETAIL "2"

VUE DE DESSUS

Ech: 1/25

NOAHO

Chemin de Fontanière - 69350 La Mulatière

Création de logements

Les entreprises réalisant les travaux devront tenir compte des derniers plans architecturaux lors de la réalisation des travaux.
Les plans du lot MATTE ne doivent servir qu'à titre de référence et ne doivent pas être utilisés pour la construction.

ARCHITECTES:	ATELIER DE LA PASSERELLE	MO DELEGUE:	MATTE SAS
SET STRUCTURE:	PRELEM	MO:	PSD Ingénierie
ECONOMISTE:	EXECO	CPR:	SUD EST COORDINATION
BUREAU DE CONTROL:	Bureau VERITAS	CPD:	ENTREPRISES: Fontaine-pbc

Bât: A

PLANCHER sur -2 entre files 1 et 9

Coffrage

DOE

Contrainte de sur: 8 bars ELS

PLAN N° A32 A

DATE: 17/12/2015

MATTÉ

BUREAU D'ETUDES

STRUCTURES ET FLUIDES

119 BOULEVARD STRAUSSHOFFER VILLEURBANNE

Tel: 04 72 44 52 87 Fax: 04 72 44 25 59

E-mail: info@matte.fr

Dessiné par: J.B.C

Contrôle par: P.L.M

Echelle: 1/50

Affaire N° 13.12.19