

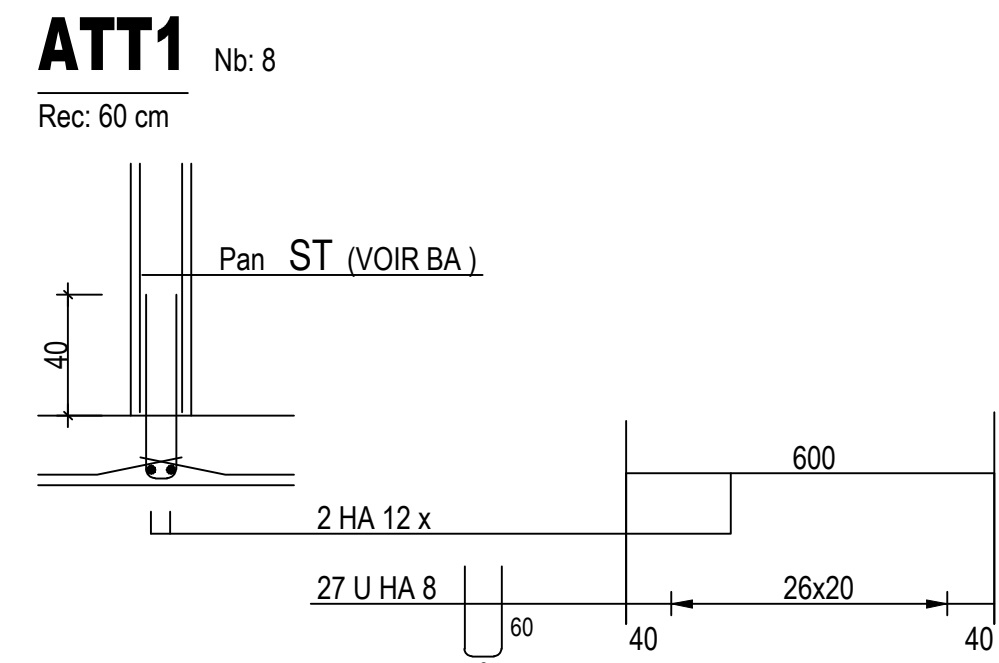
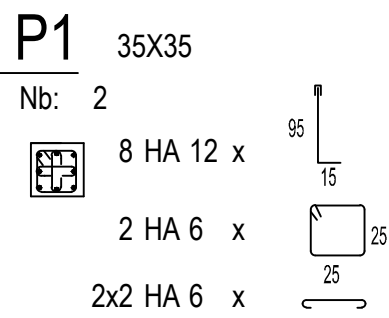
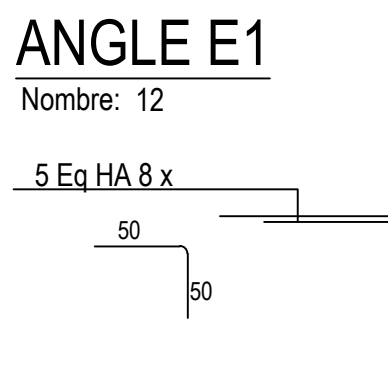


ATTENTES POTEAUX DANS SEMELLES




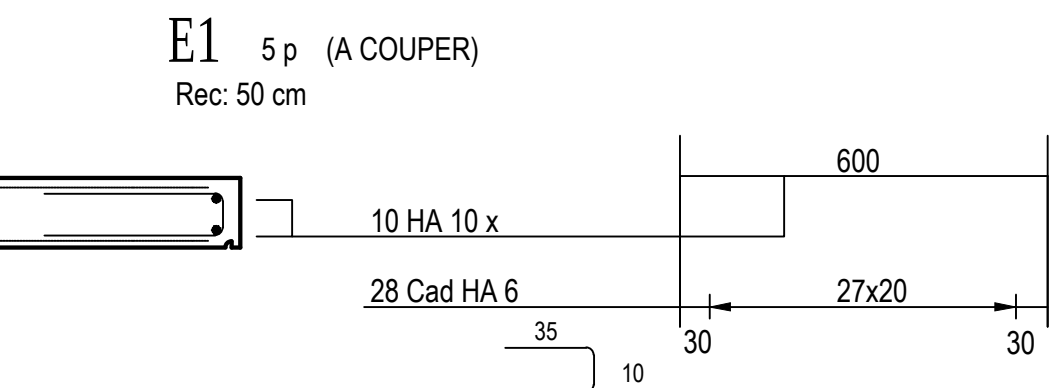


ATTENTES MURS DANS POUTRES

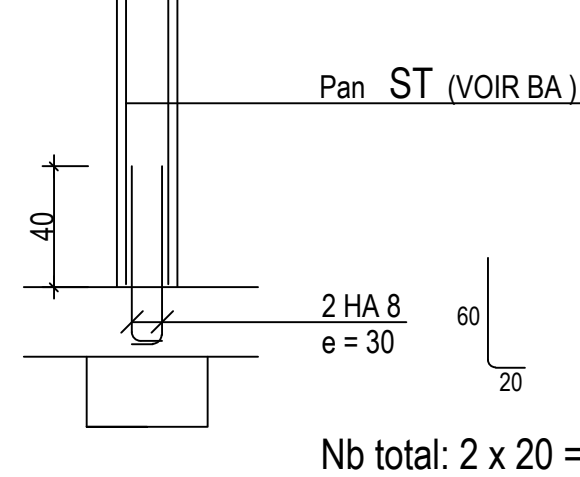


COUPE A

Ech: 1/25

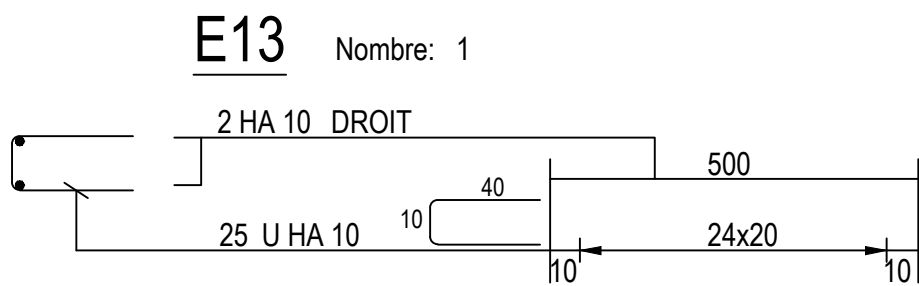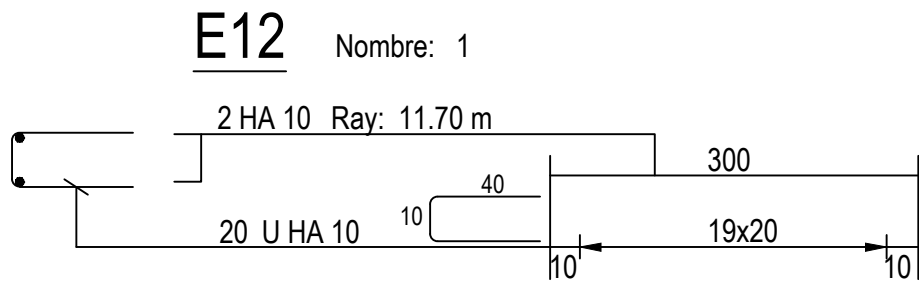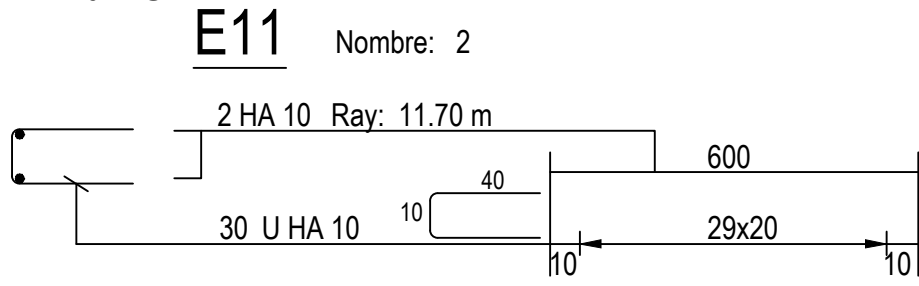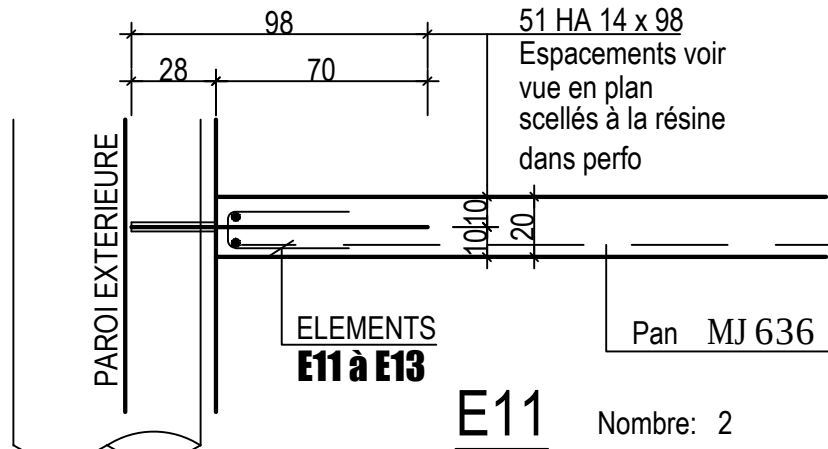

ARMATURES SUPERIEURES

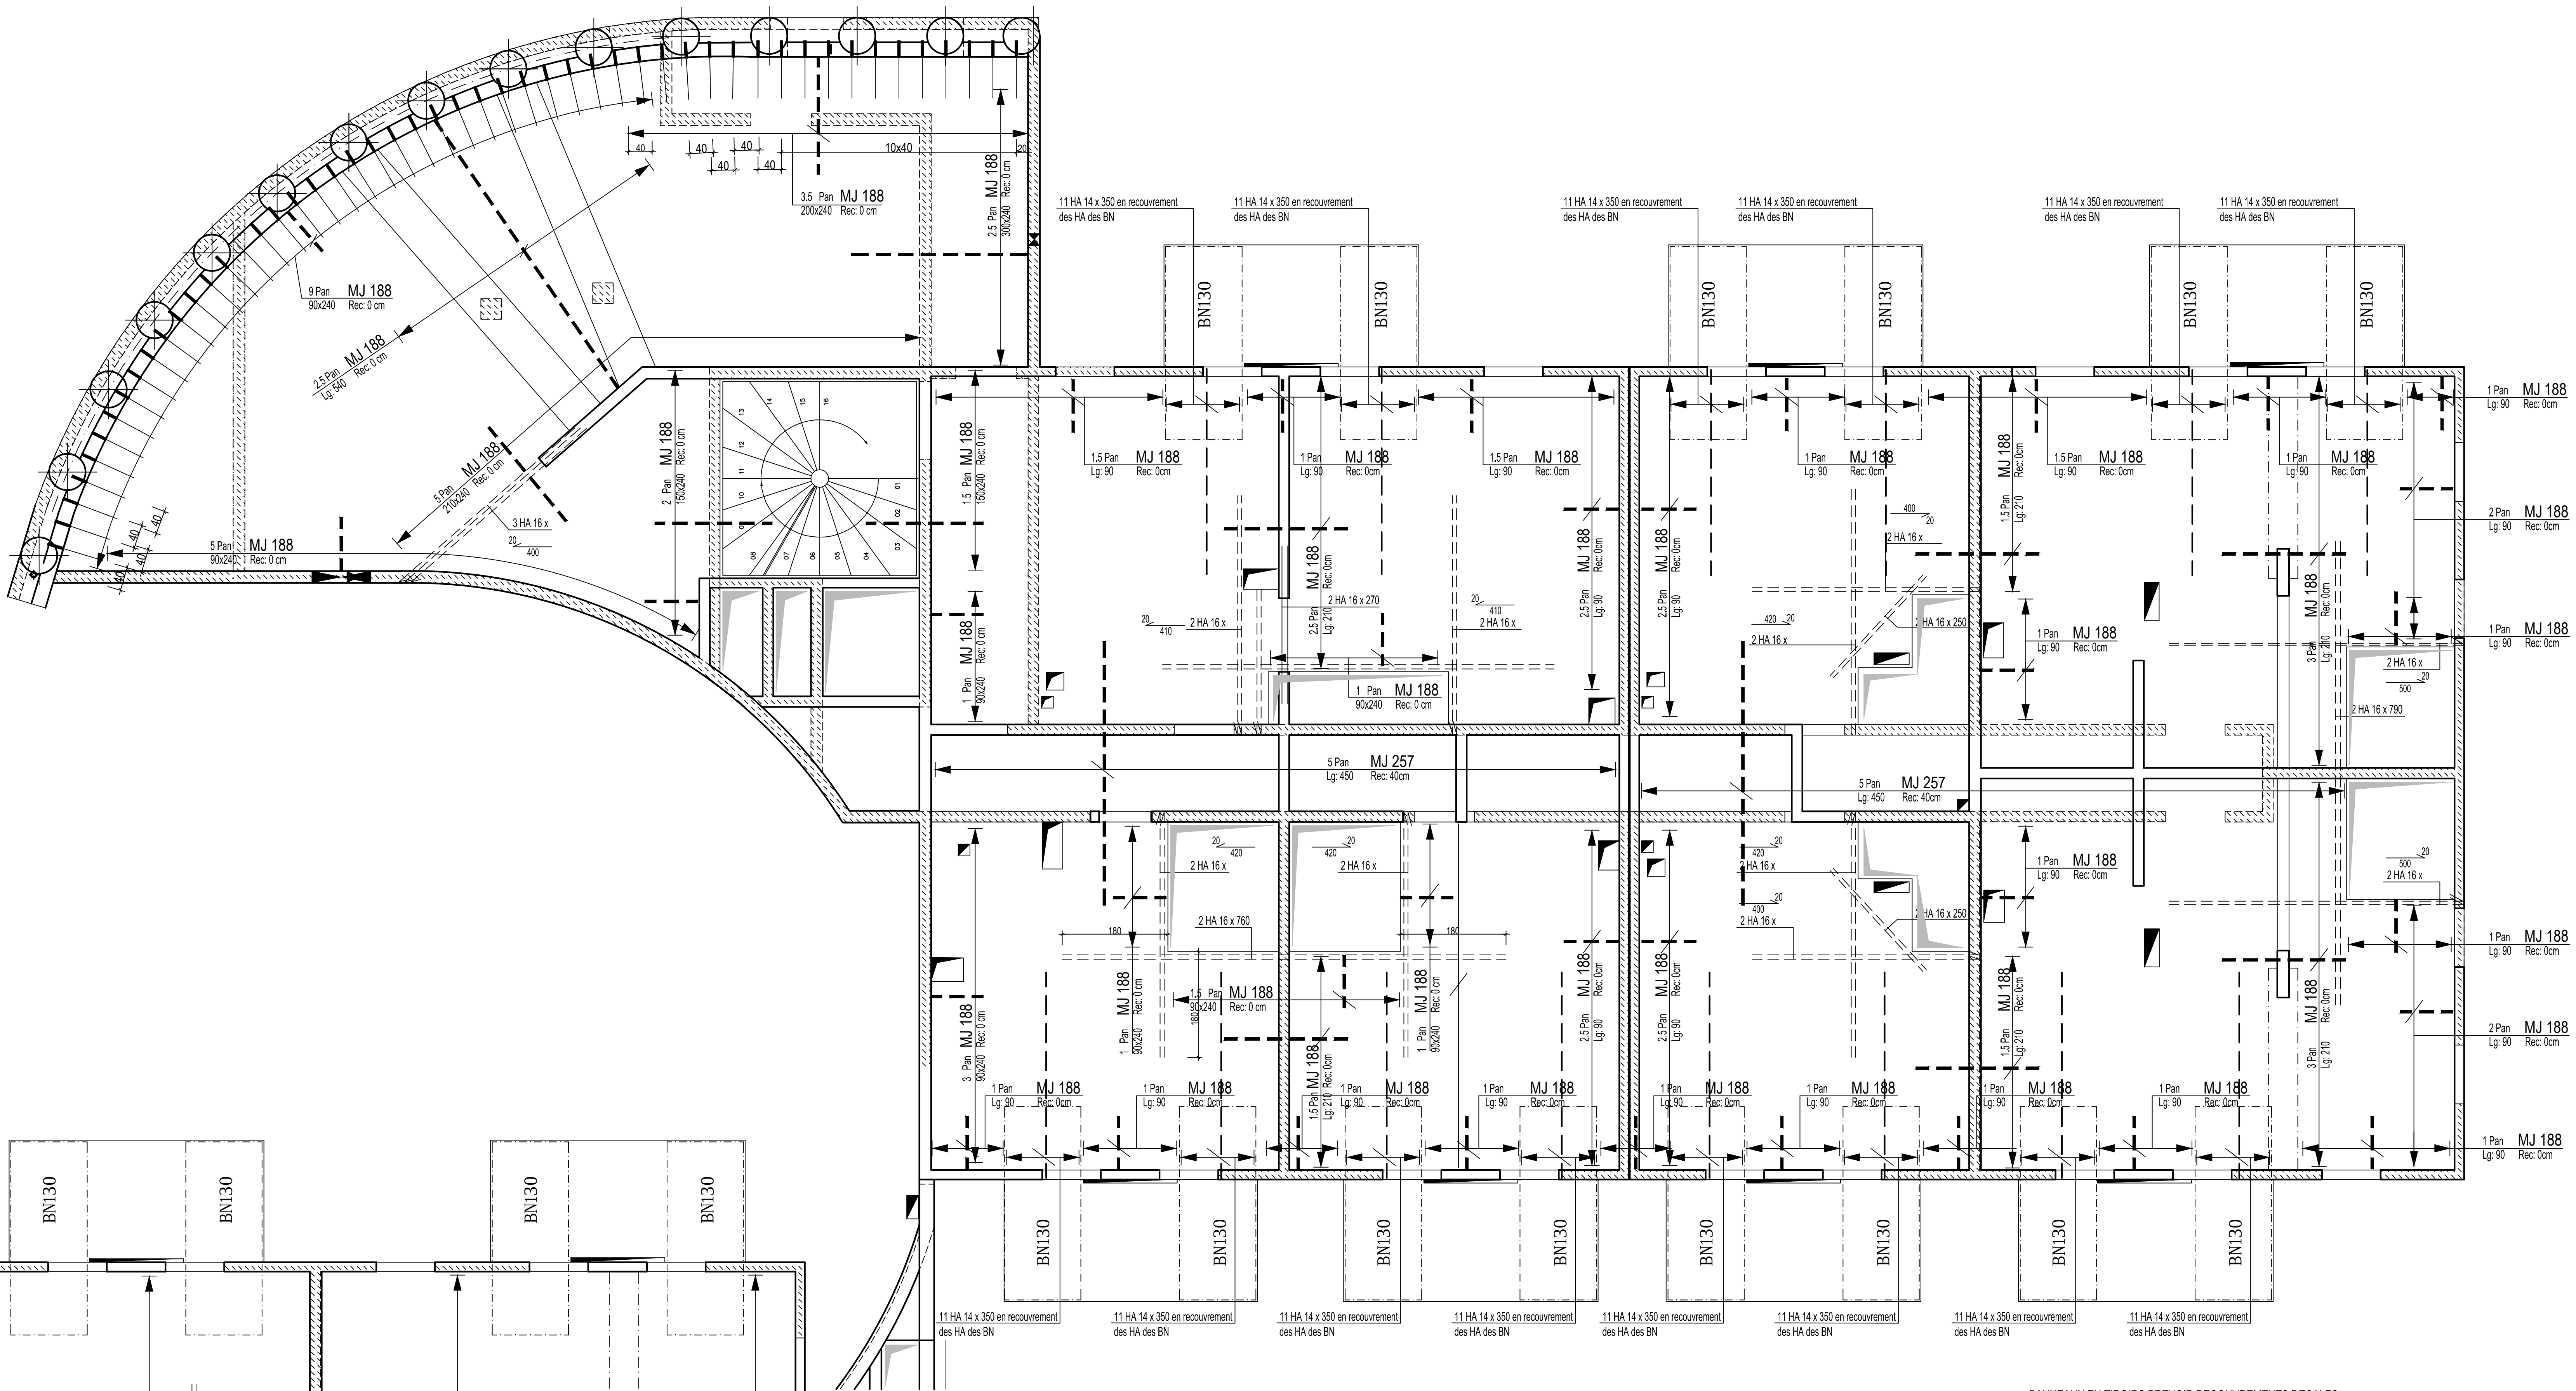


ARMATURES INFERIEURES




DETAIL D'ABOUTS DE CHAINAGES INTERIEURS:

Position des esquers d'angles dans dalle 2 HA 14 x 100
a des
vues en plan

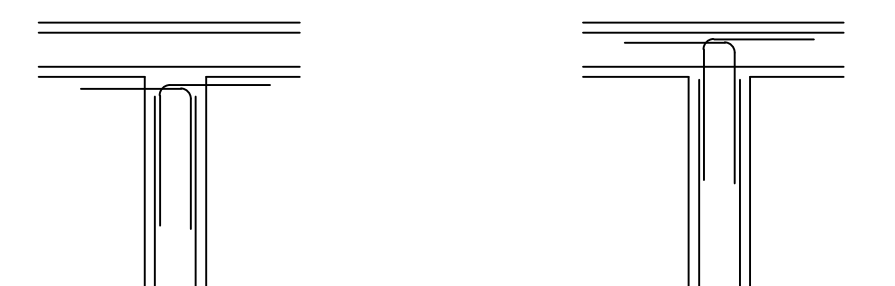


DETAIL D'ABOUTS DE CHAINAGES EN ANGLE SUR FACADES:


Position des esquers d'angles dans dalle 2 HA 14 x 100
a des
vues en plan

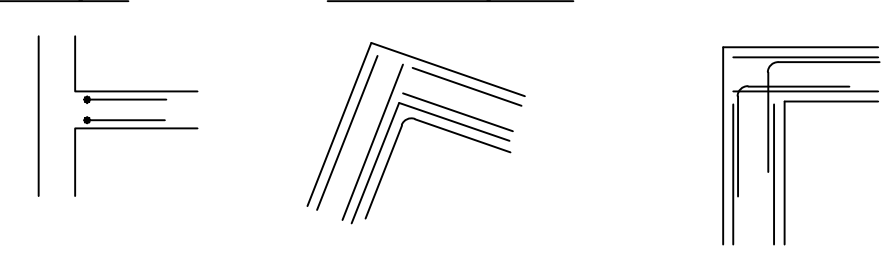

RENFORTS RESESERVATIONS JUSQU'A Ø200 mm

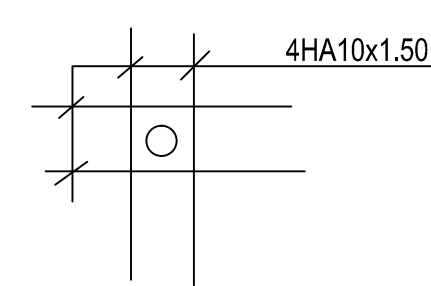

Principe de renfort aux droits des gaines:

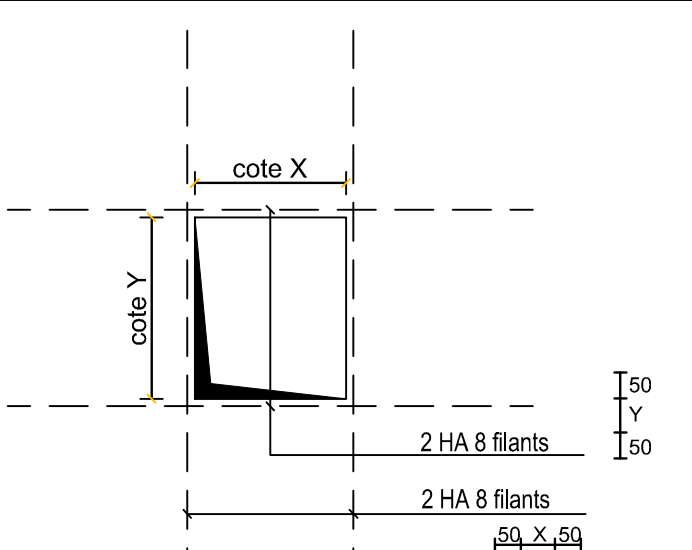

PANNEAUX EN TIROIRS PREVOIR RECOUVREMENTS DECALES

EX: 1er Lit: 3 panneaux
2ème Lit: 1/2+1/2 panneaux

NOAHO

Chemin de Fontanière - 69350 La Mulatière

Création de logements

Les entreprises réalisant les travaux devront tenir compte des derniers plans architecturaux lors de la réalisation des travaux.
Les plans du lot MATTE ne doivent servir qu'à titre de référence et ne sont pas à l'échelle.

ARCHITECTES:	ATELIER DE LA PASSERELLE	MO DELEGUE:	PSO Ingénierie
SET STRUCTURE:	MATTE SAS	NOE:	SUD EST COORDINATION
SET FLUIDES:	PRELEM	CSPR:	CPIC
ECONOMISTE:	EXECO	CPIC:	ENTREPRISES: Fontanel-pbc
BUREAU DE CONTROLE:	Bureau VERITAS		

Bât A
PLANCHER sur -2 entre files 1 et 9
ARMATURES DALLE

INDICE	DATE	MODIFICATIONS
A		
B		
C		

MATTE
BUREAU D'ETUDES
STRUCTURES ET FLUIDES
119 BOULEVARD STRAUSSHOFF 69100 VILLEURBANNE
Tél. 04 72 44 50 87 Fax 04 72 44 26 59
E-mail: info@matte.fr

Dessiné par: J.B.O.
Contrôlé par: P.L.M.
Echelle: 1/50

PLAN N°
A34_0
DATE: 11/01/2016

EXE
Contrainte de sur: 8 bars ELS
Aciers HA (T) FeE500
Aciers Dux (D) FeE235
Aciers TS FeE500
Béton C25-28MPa
Enrobé + 3 cm

Affaire N°
13.12.19