
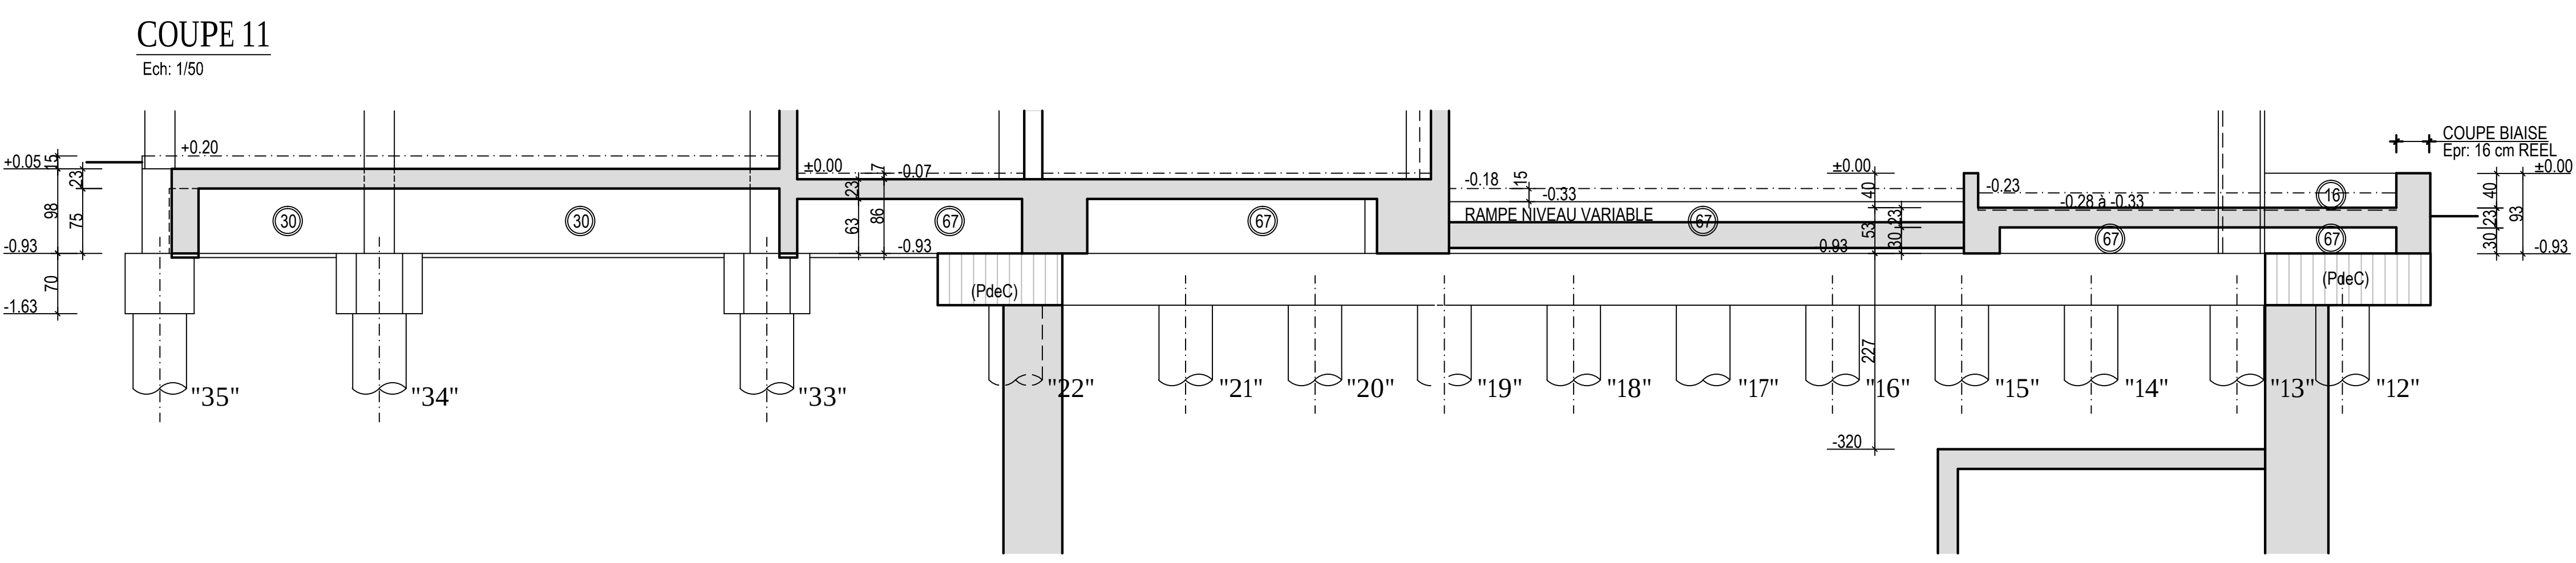
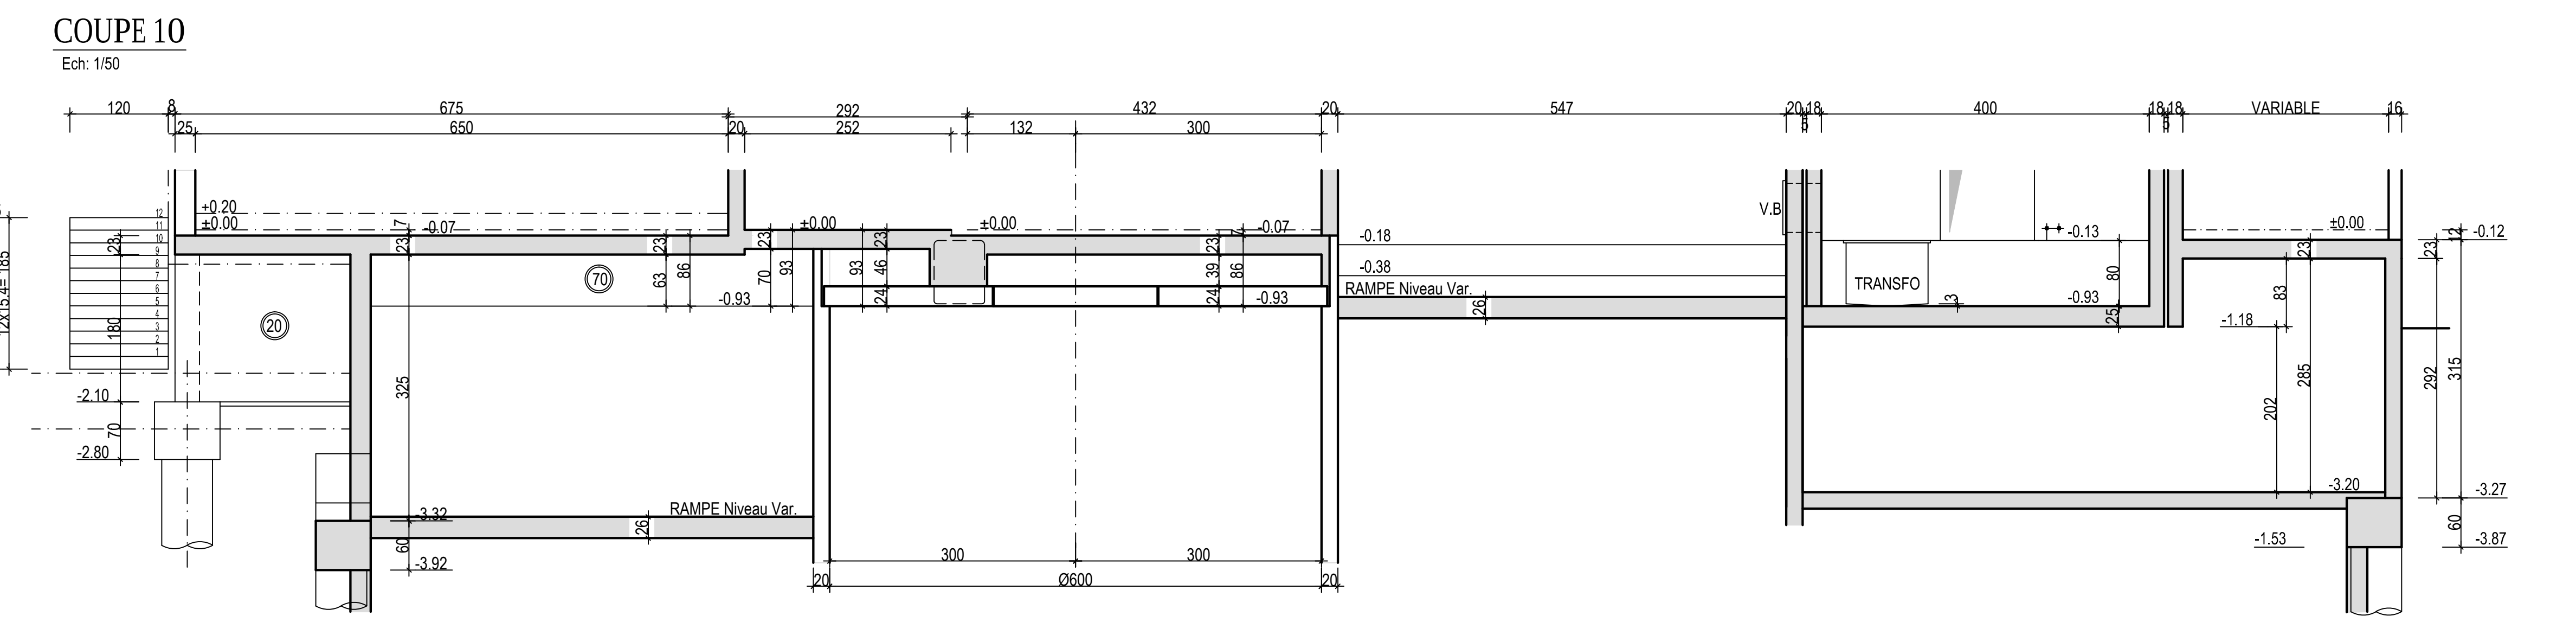
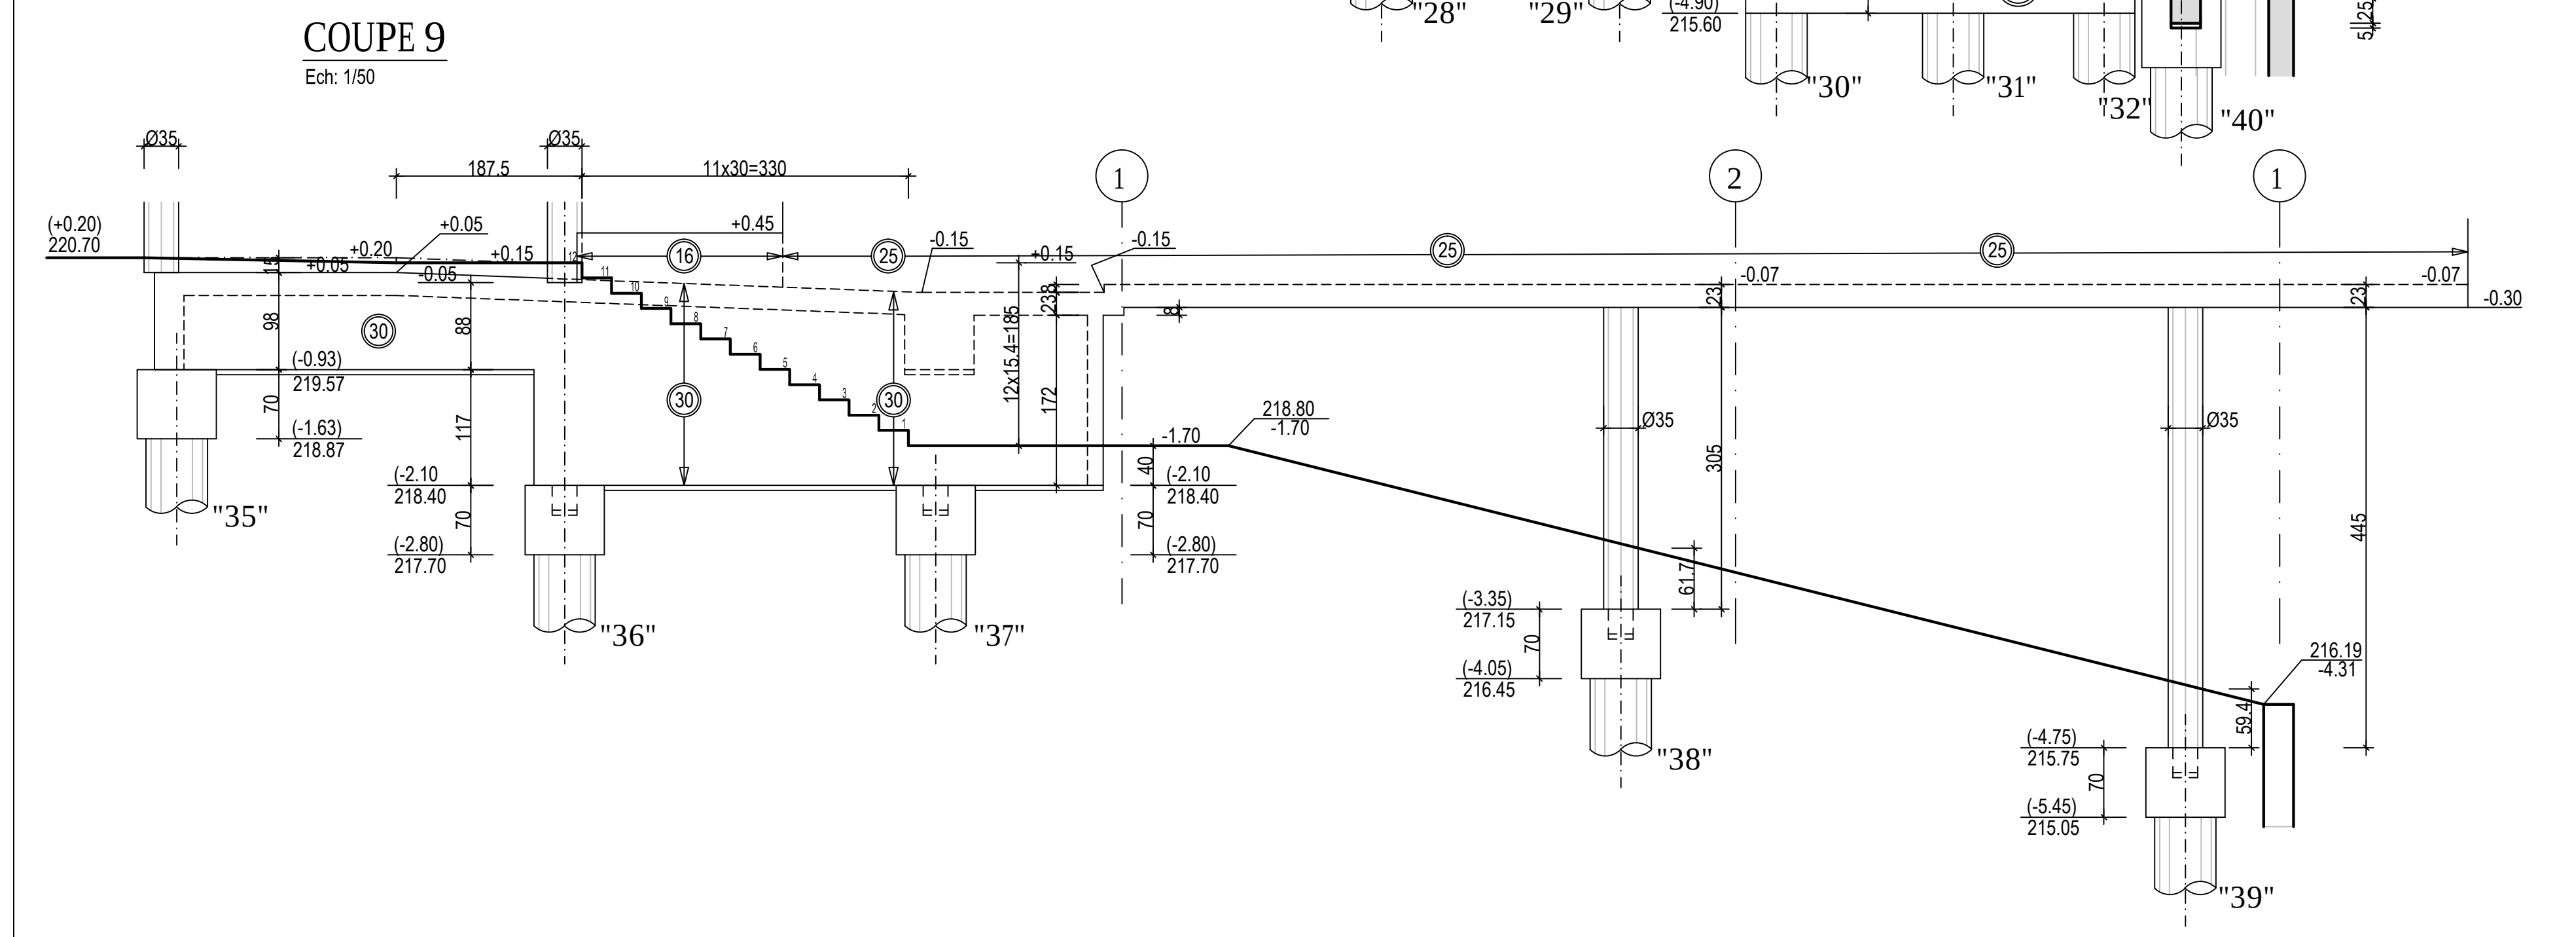
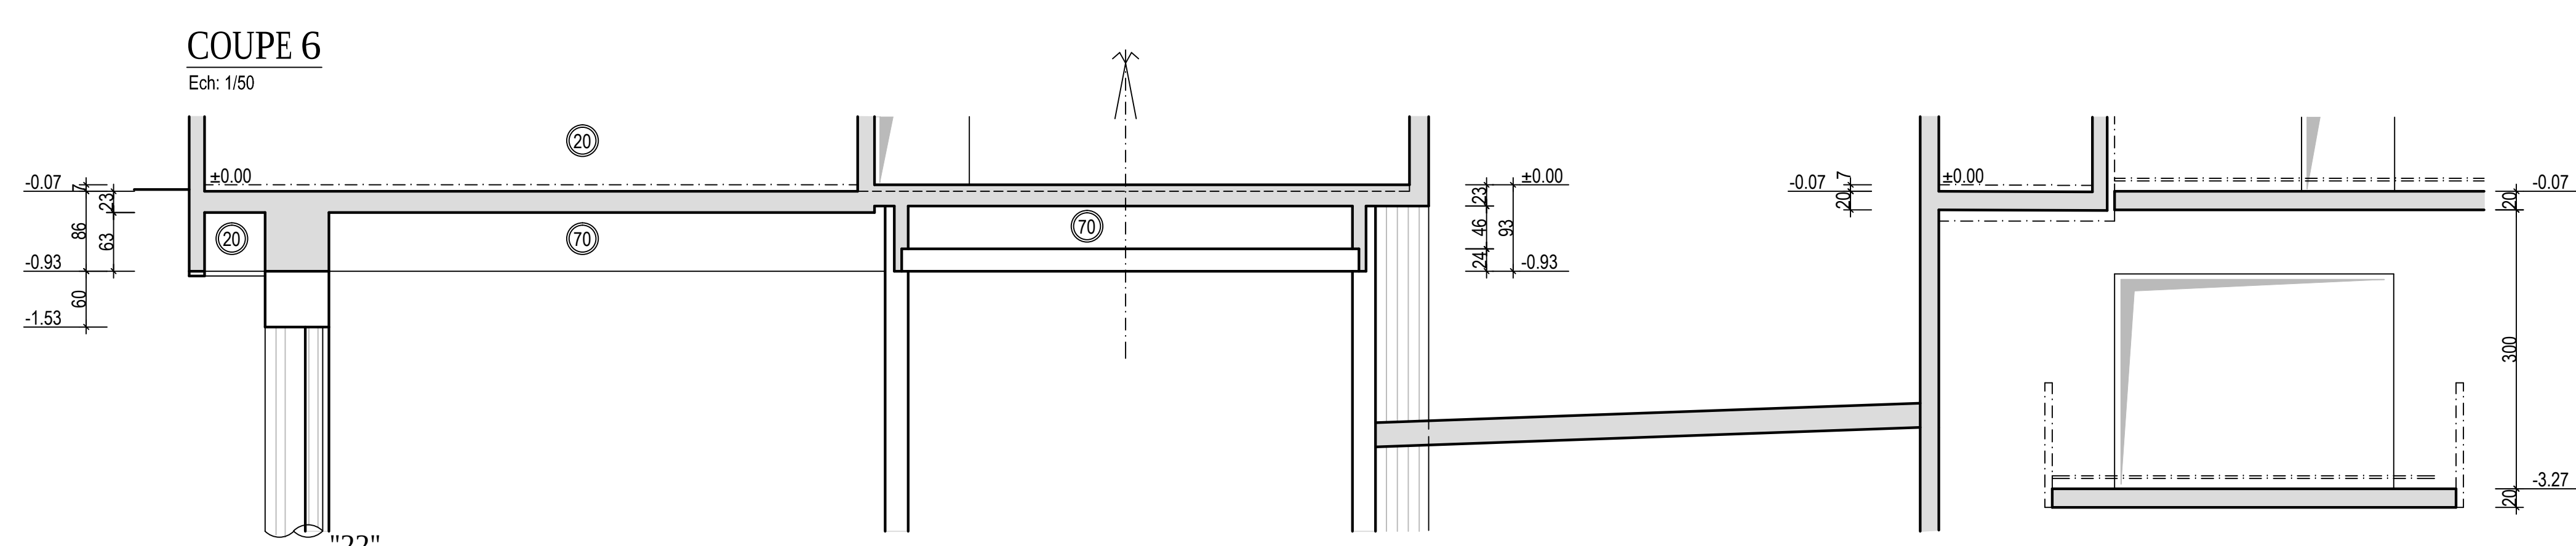
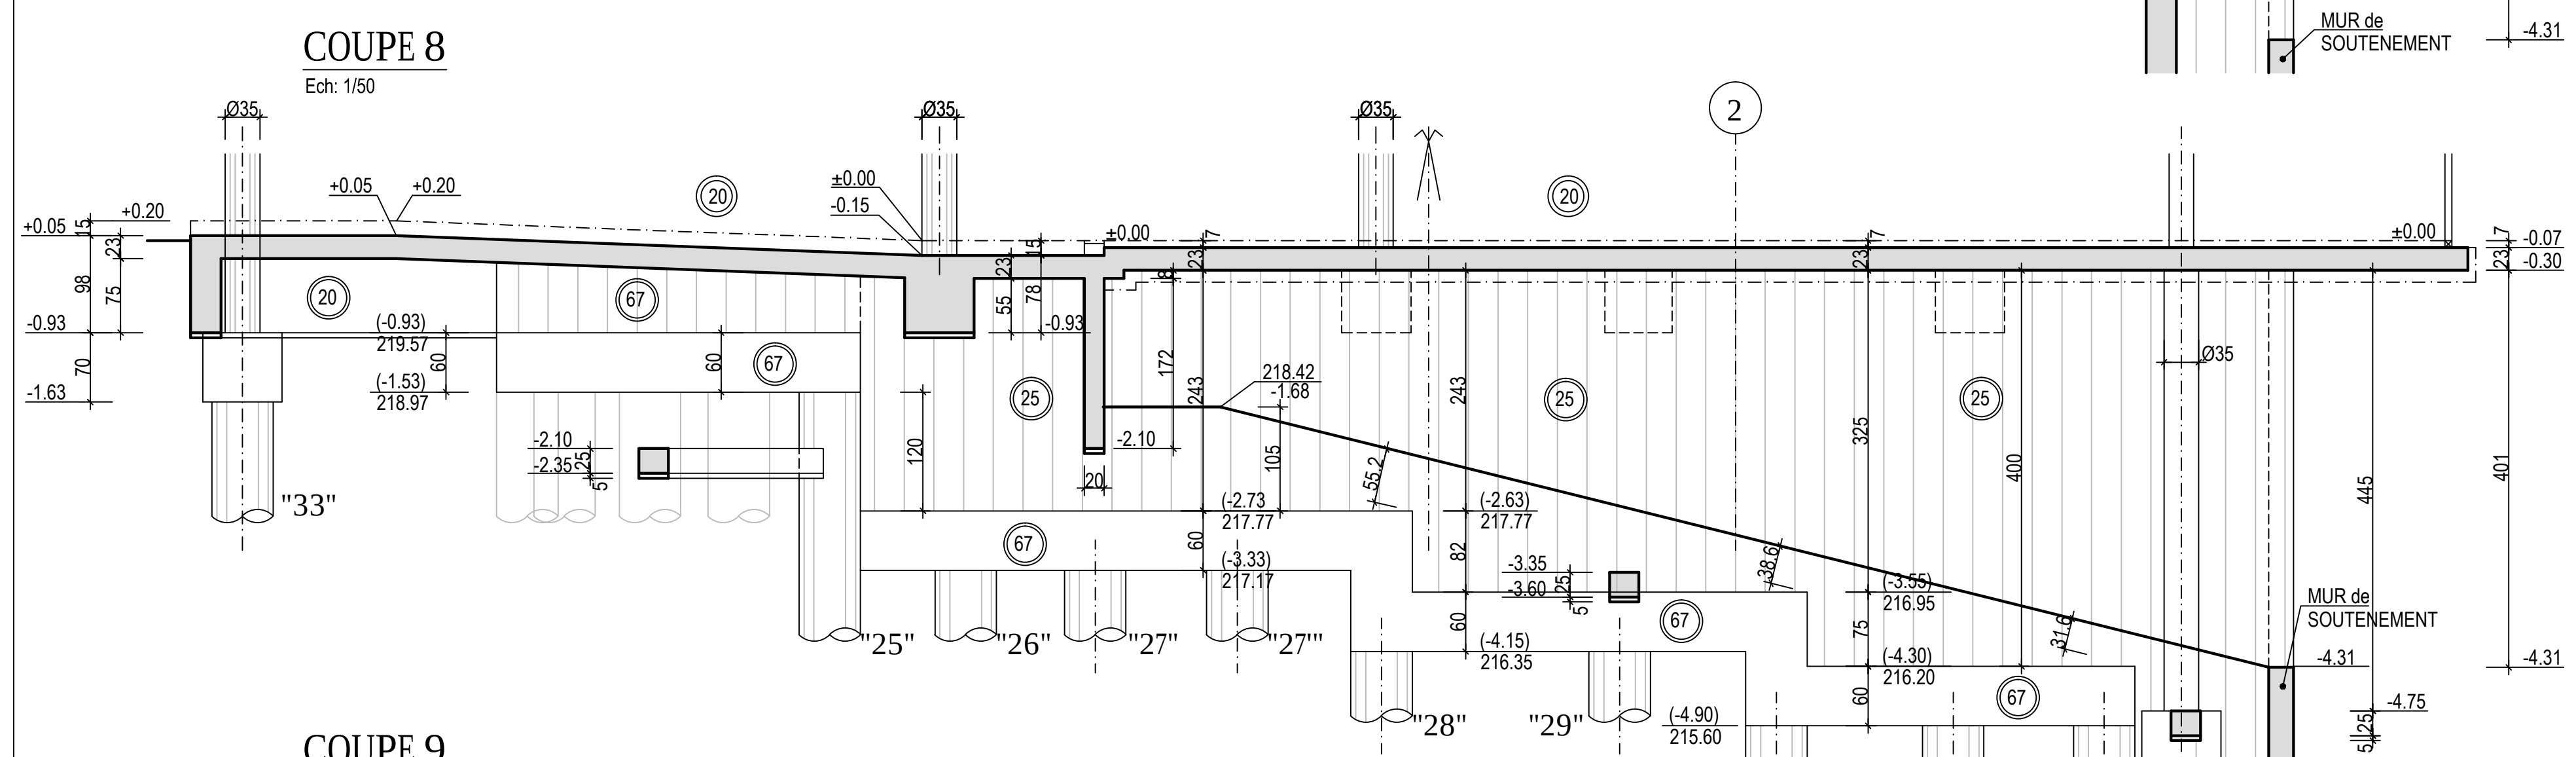
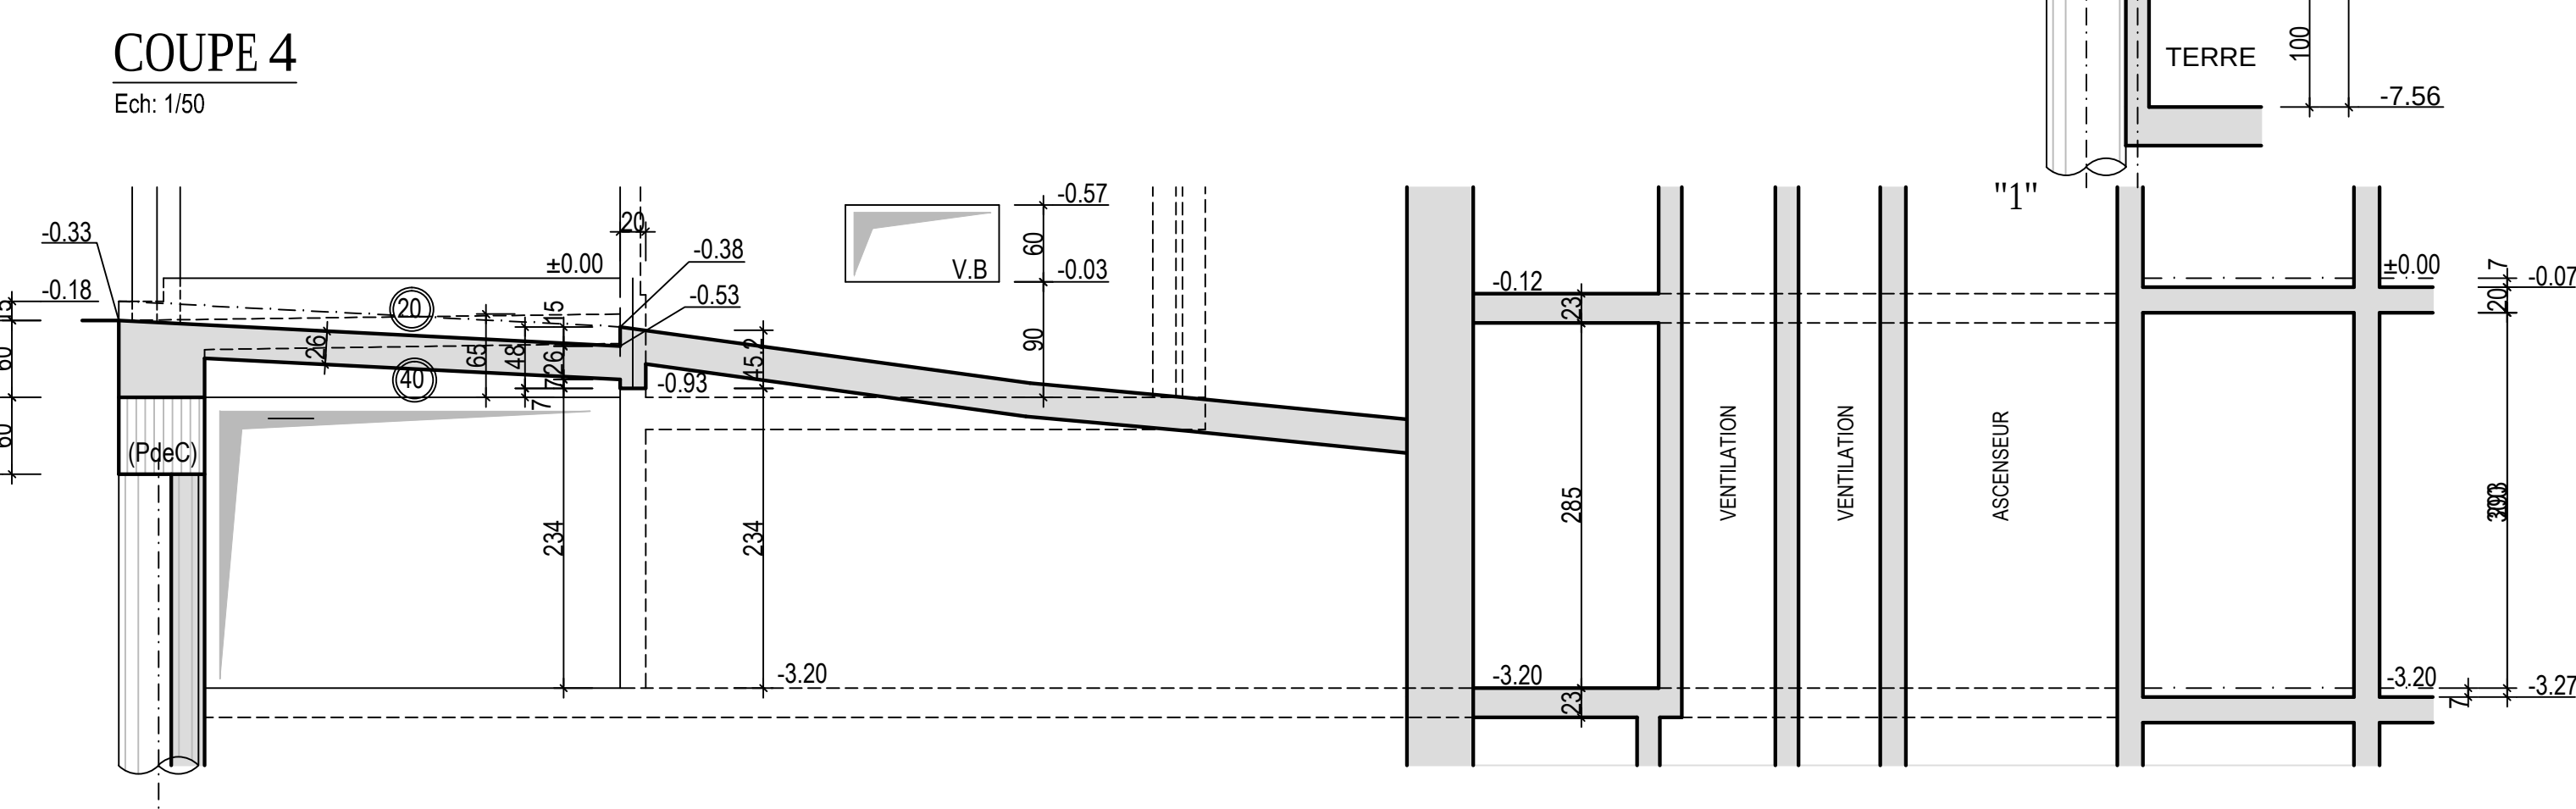
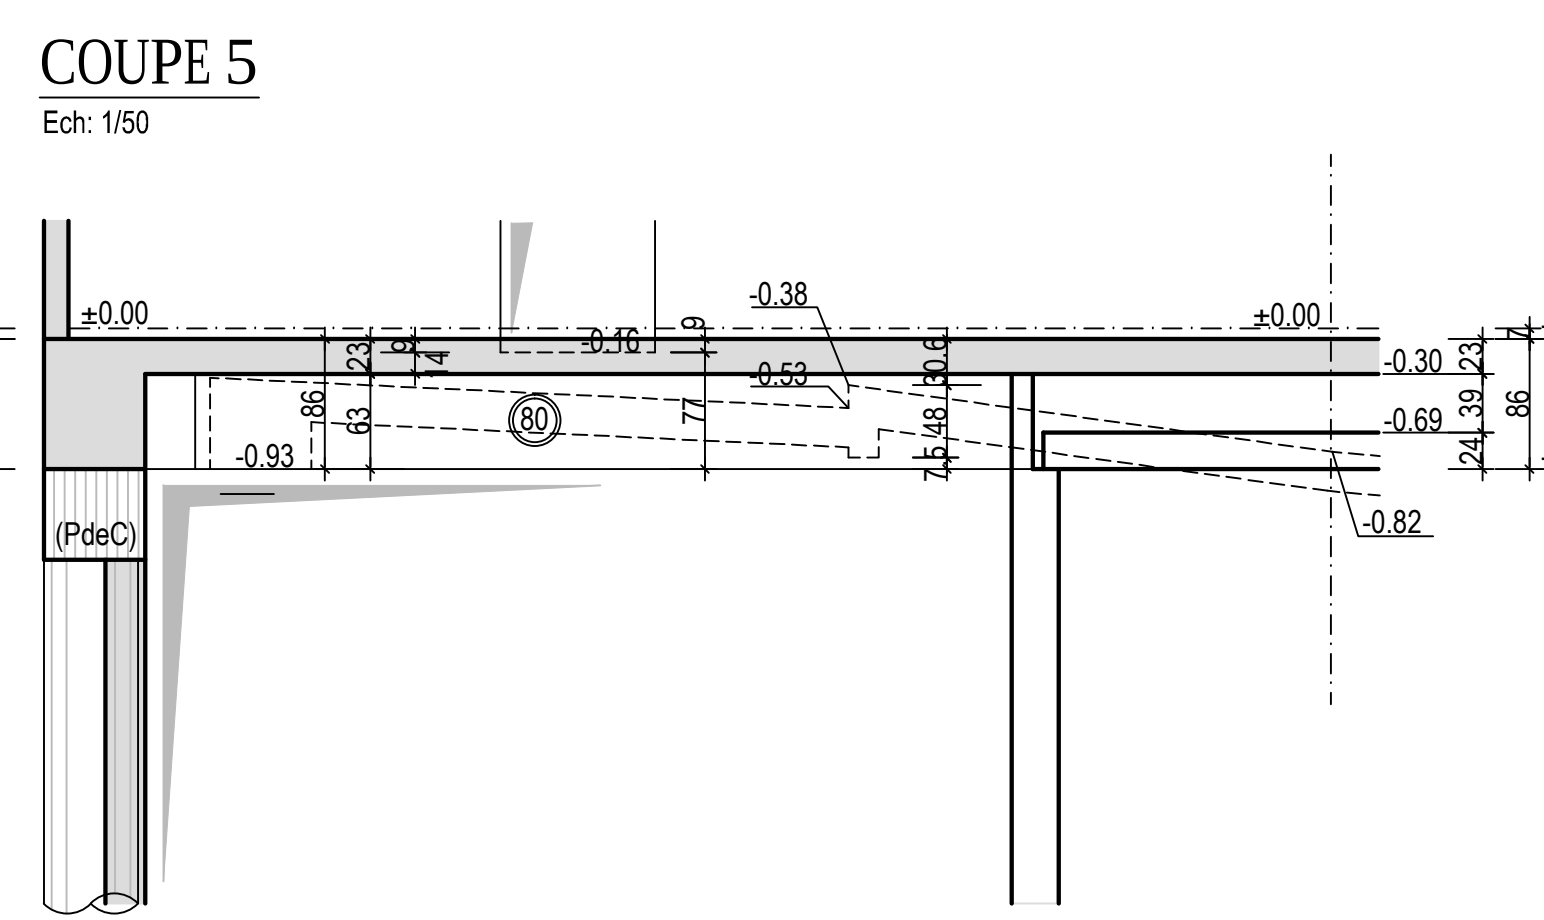
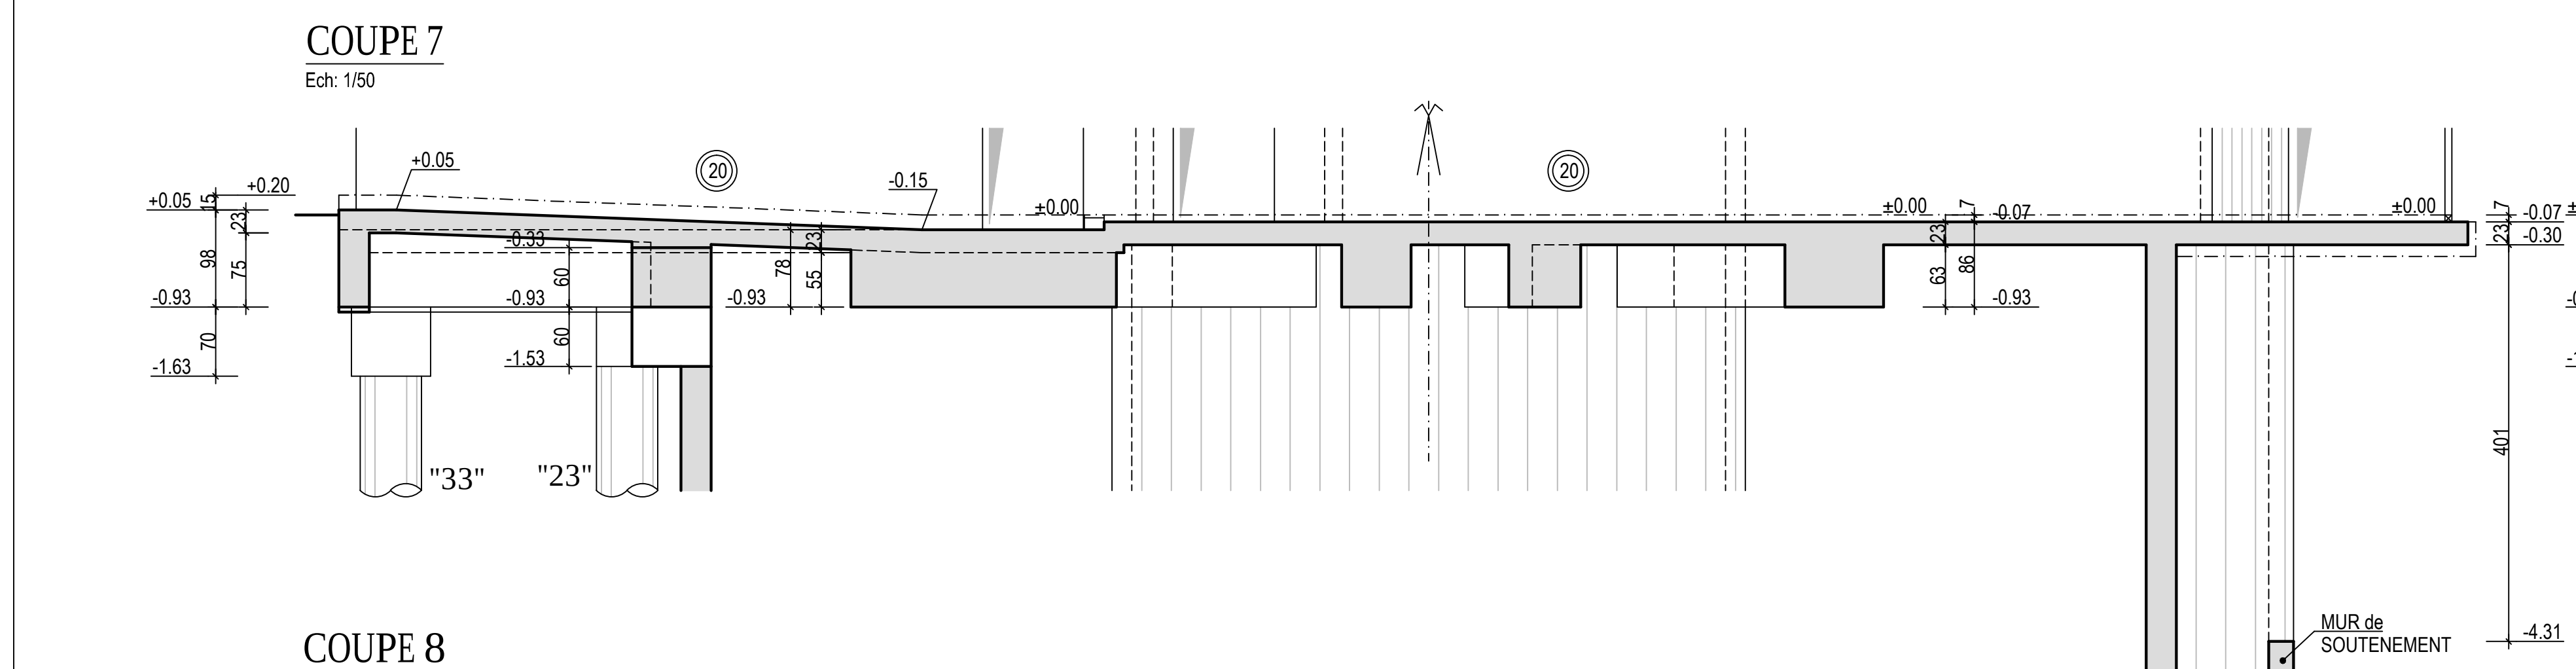
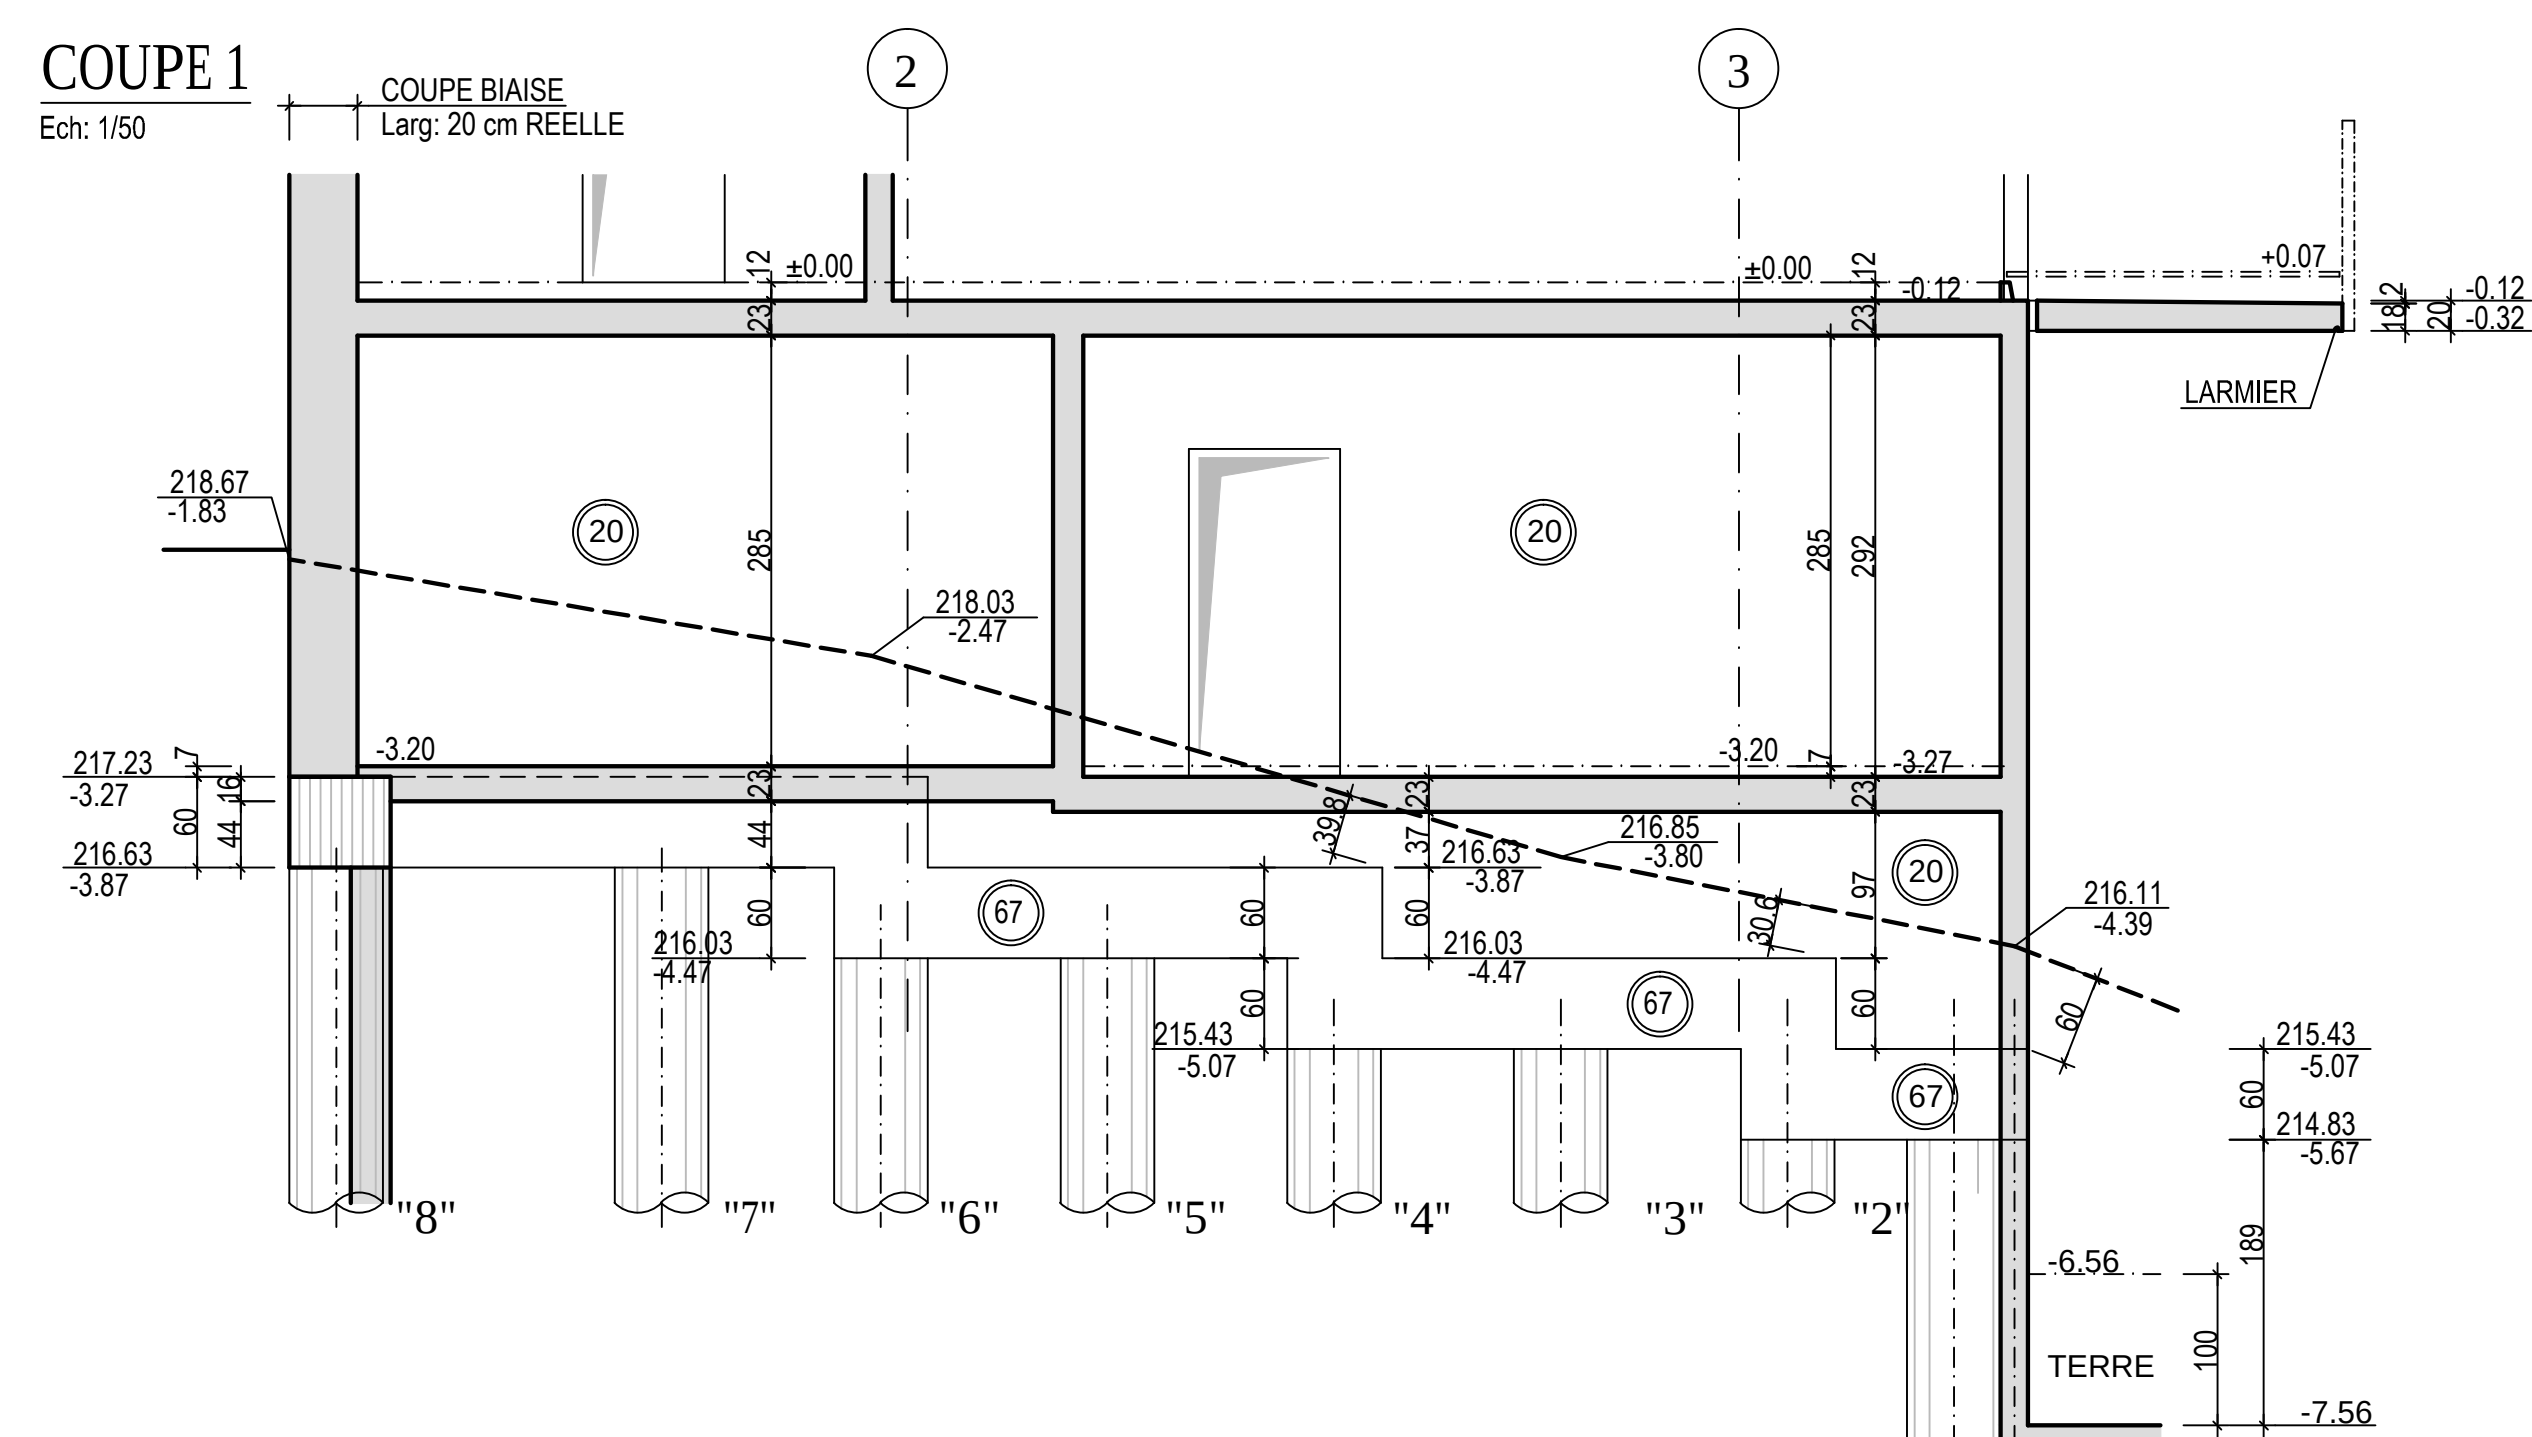
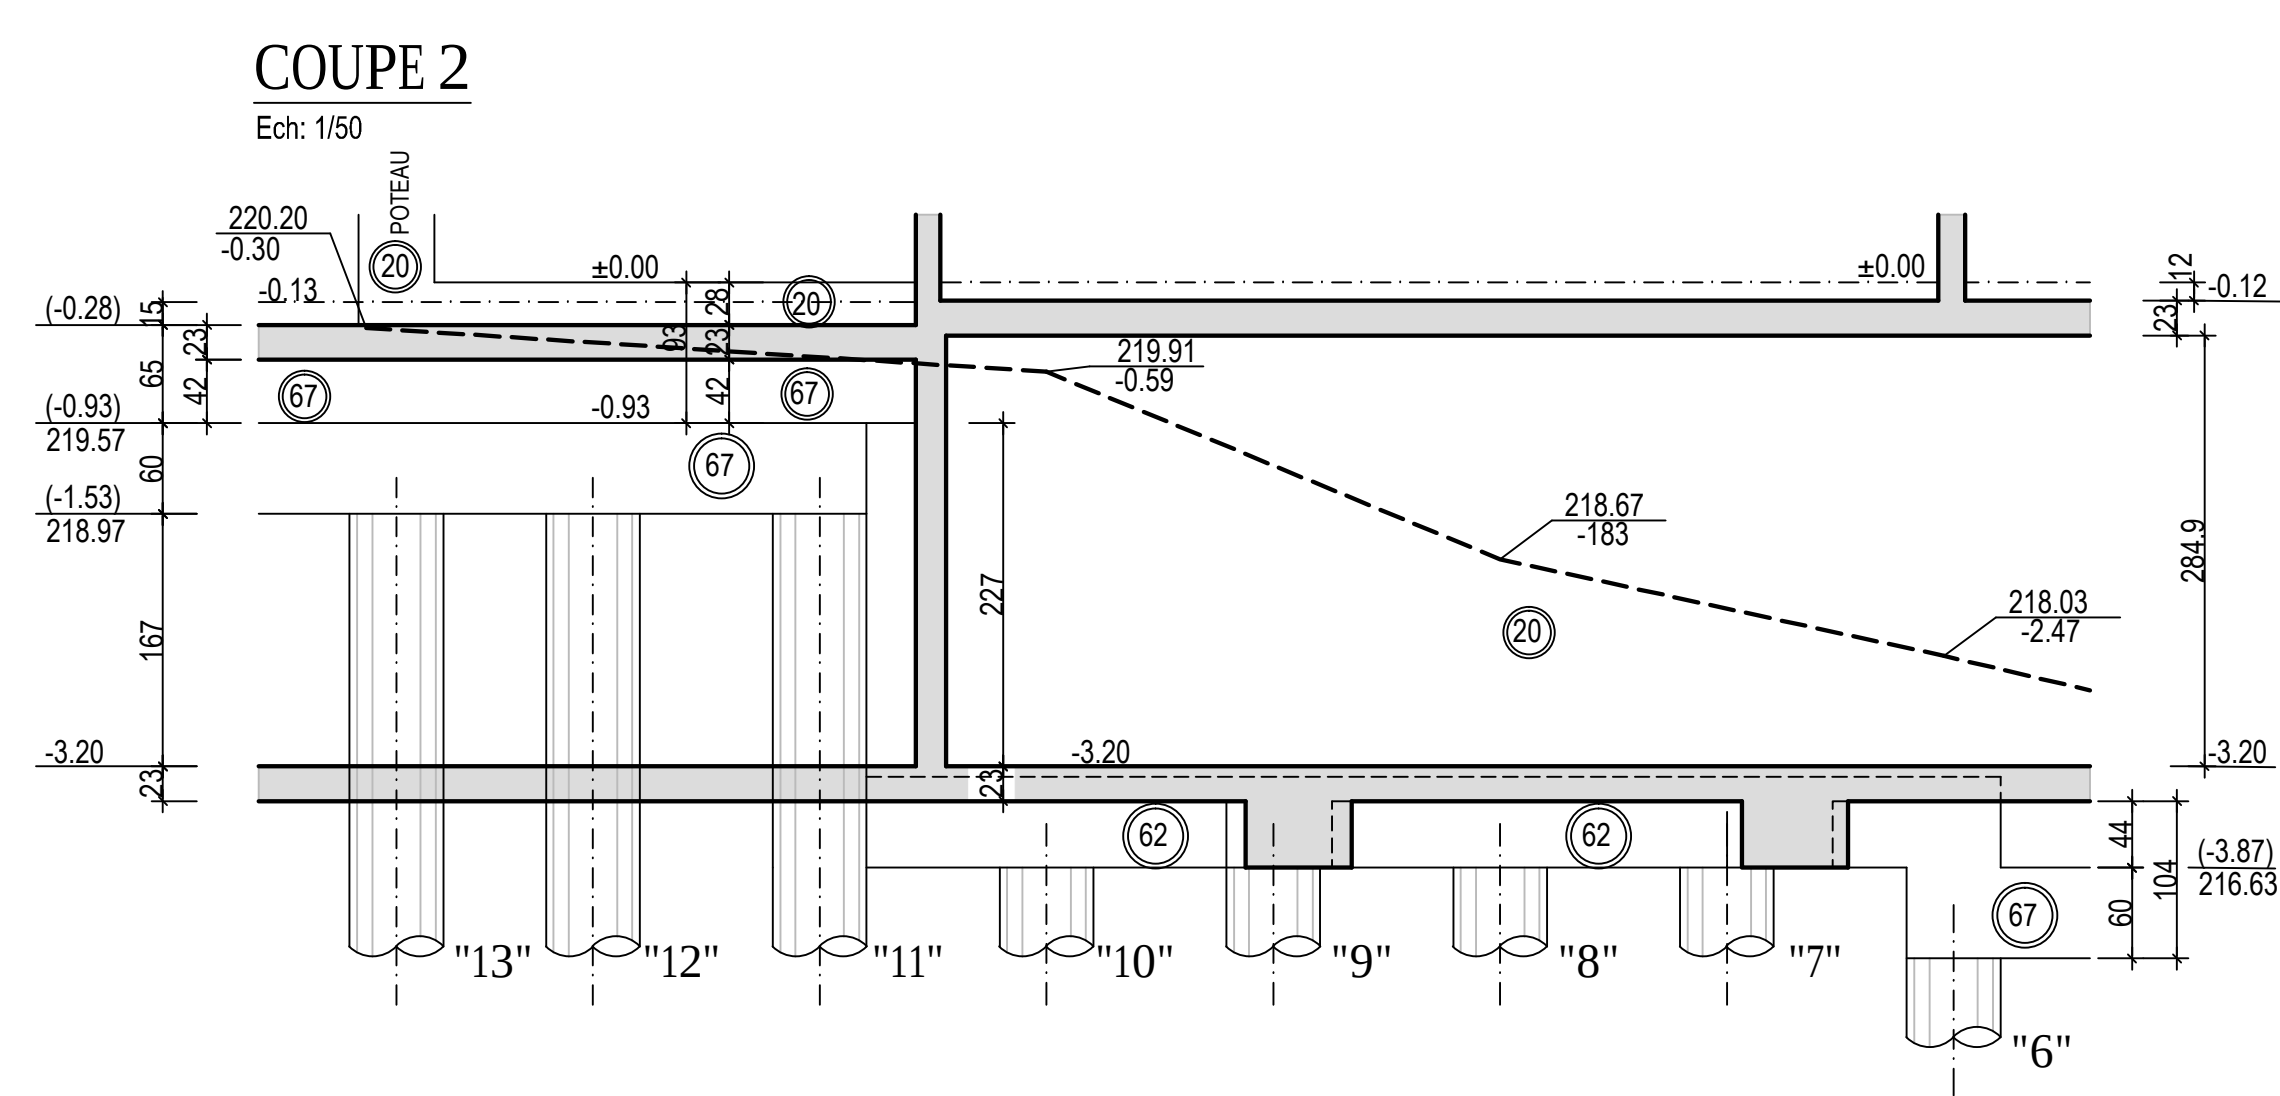


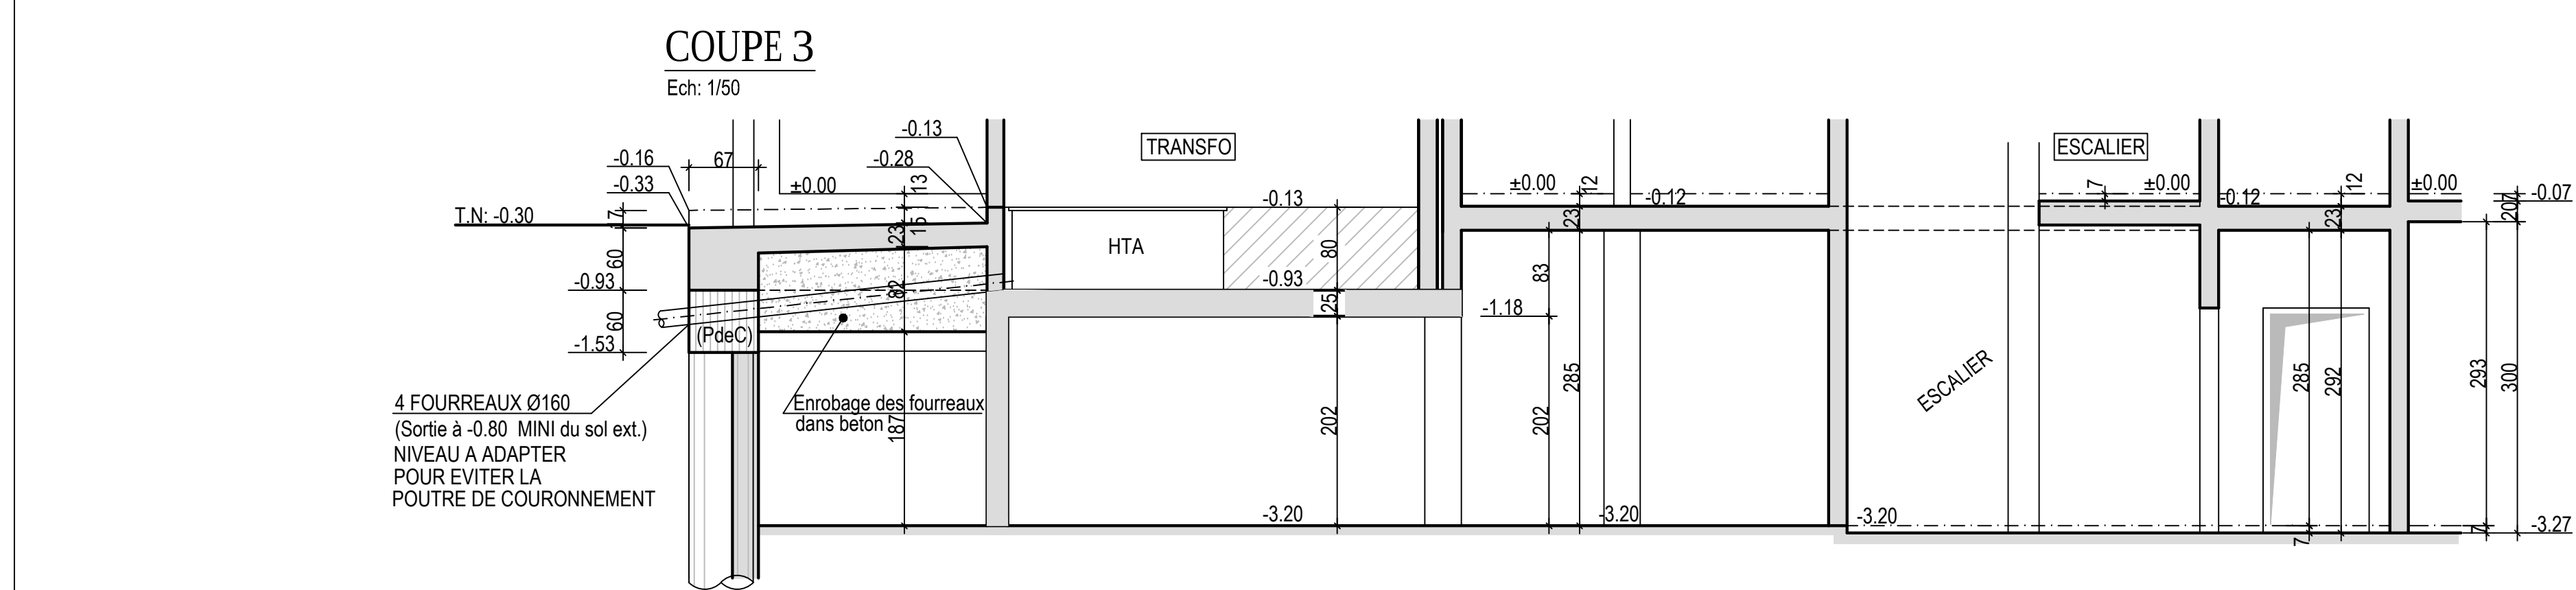

Rep.	Diamètre	Analysé	S.P.P.	
"1"	Ø62	214.83	-6.67	Sous poutre de couronnement
"2"	Ø62	214.83	-5.67	Sous poutre de couronnement
"3"	Ø62	215.43	-5.07	Sous poutre de couronnement
"4"	Ø62	215.43	-5.07	Sous poutre de couronnement
"5"	Ø62	216.03	-4.47	Sous poutre de couronnement
"6"	Ø62	216.03	-4.47	Sous poutre de couronnement
"7"	Ø62	216.63	-3.87	Sous poutre de couronnement
"8"	Ø62	216.63	-3.87	Sous poutre de couronnement
"9"	Ø62	216.63	-3.87	Sous poutre de couronnement
"10"	Ø62	216.63	-3.87	Sous poutre de couronnement
"11"	Ø62	218.97	-1.53	Sous poutre de couronnement
"12"	Ø62	218.97	-1.53	Sous poutre de couronnement
"13"	Ø62	218.97	-1.53	Sous poutre de couronnement
"14"	Ø62	218.97	-1.53	Sous poutre de couronnement
"15"	Ø62	218.97	-1.53	Sous poutre de couronnement
"16"	Ø62	218.97	-1.53	Sous poutre de couronnement
"17"	Ø62	218.97	-1.53	Sous poutre de couronnement
"18"	Ø62	218.97	-1.53	Sous poutre de couronnement
"19"	Ø62	218.97	-1.53	Sous poutre de couronnement
"20"	Ø62	218.97	-1.53	Sous poutre de couronnement
"21"	Ø62	218.97	-1.53	Sous poutre de couronnement
"22"	Ø62	218.97	-1.53	Sous poutre de couronnement
"23"	Ø62	218.97	-1.53	Sous poutre de couronnement
"24"	Ø62	218.97	-1.53	Sous poutre de couronnement
"25"	Ø62	218.97	-1.53	Sous poutre de couronnement
"26"	Ø62	217.17	-3.33	Sous poutre de couronnement
"27"	Ø62	217.17	-3.33	Sous poutre de couronnement
"28"	Ø62	216.35	-4.15	Sous poutre de couronnement
"29"	Ø62	216.35	-4.15	Sous poutre de couronnement
"30"	Ø62	215.60	-4.90	Sous poutre de couronnement
"31"	Ø62	215.60	-4.90	Sous poutre de couronnement
"32"	Ø62	215.60	-4.90	Sous poutre de couronnement
"33"	Ø62	218.87	-1.63	Sous tête de pieux Ø60x707H
"34"	Ø62	218.87	-1.63	Sous tête de pieux Ø60x707H
"35"	Ø62	218.87	-1.63	Sous tête de pieux Ø60x707H
"36"	Ø62	217.70	-2.80	Sous tête de pieux Ø60x707H
"37"	Ø62	217.70	-2.80	Sous tête de pieux Ø60x707H
"38"	Ø62	216.45	-4.05	Sous tête de pieux Ø60x707H
"39"	Ø62	215.05	-5.45	Sous tête de pieux Ø60x707H
"40"	Ø62	215.05	-5.45	Sous tête de pieux Ø60x707H
"41"	Ø72	210.07	-10.43	Sous tête de pieux Ø60x707H
"42"	Ø62	210.07	-10.43	Sous tête de pieux Ø60x707H
"43"	Ø62	210.07	-10.43	Sous tête de pieux Ø60x707H
"44"	Ø62	210.07	-10.43	Sous tête de pieux Ø60x707H

$$\pm 0.00 = 220.50$$

NOAHO
LE 180°
Chemin de Fontanière - 69350 La Mulatière
Création de logements

L'entreprise réalisant les travaux devra tenir compte des derniers plans architecturaux et de la réalisation des travaux. Les plans du MATTE ne doivent servir qu'au corps d'état complet et doivent être dans l'état d'évolution.