


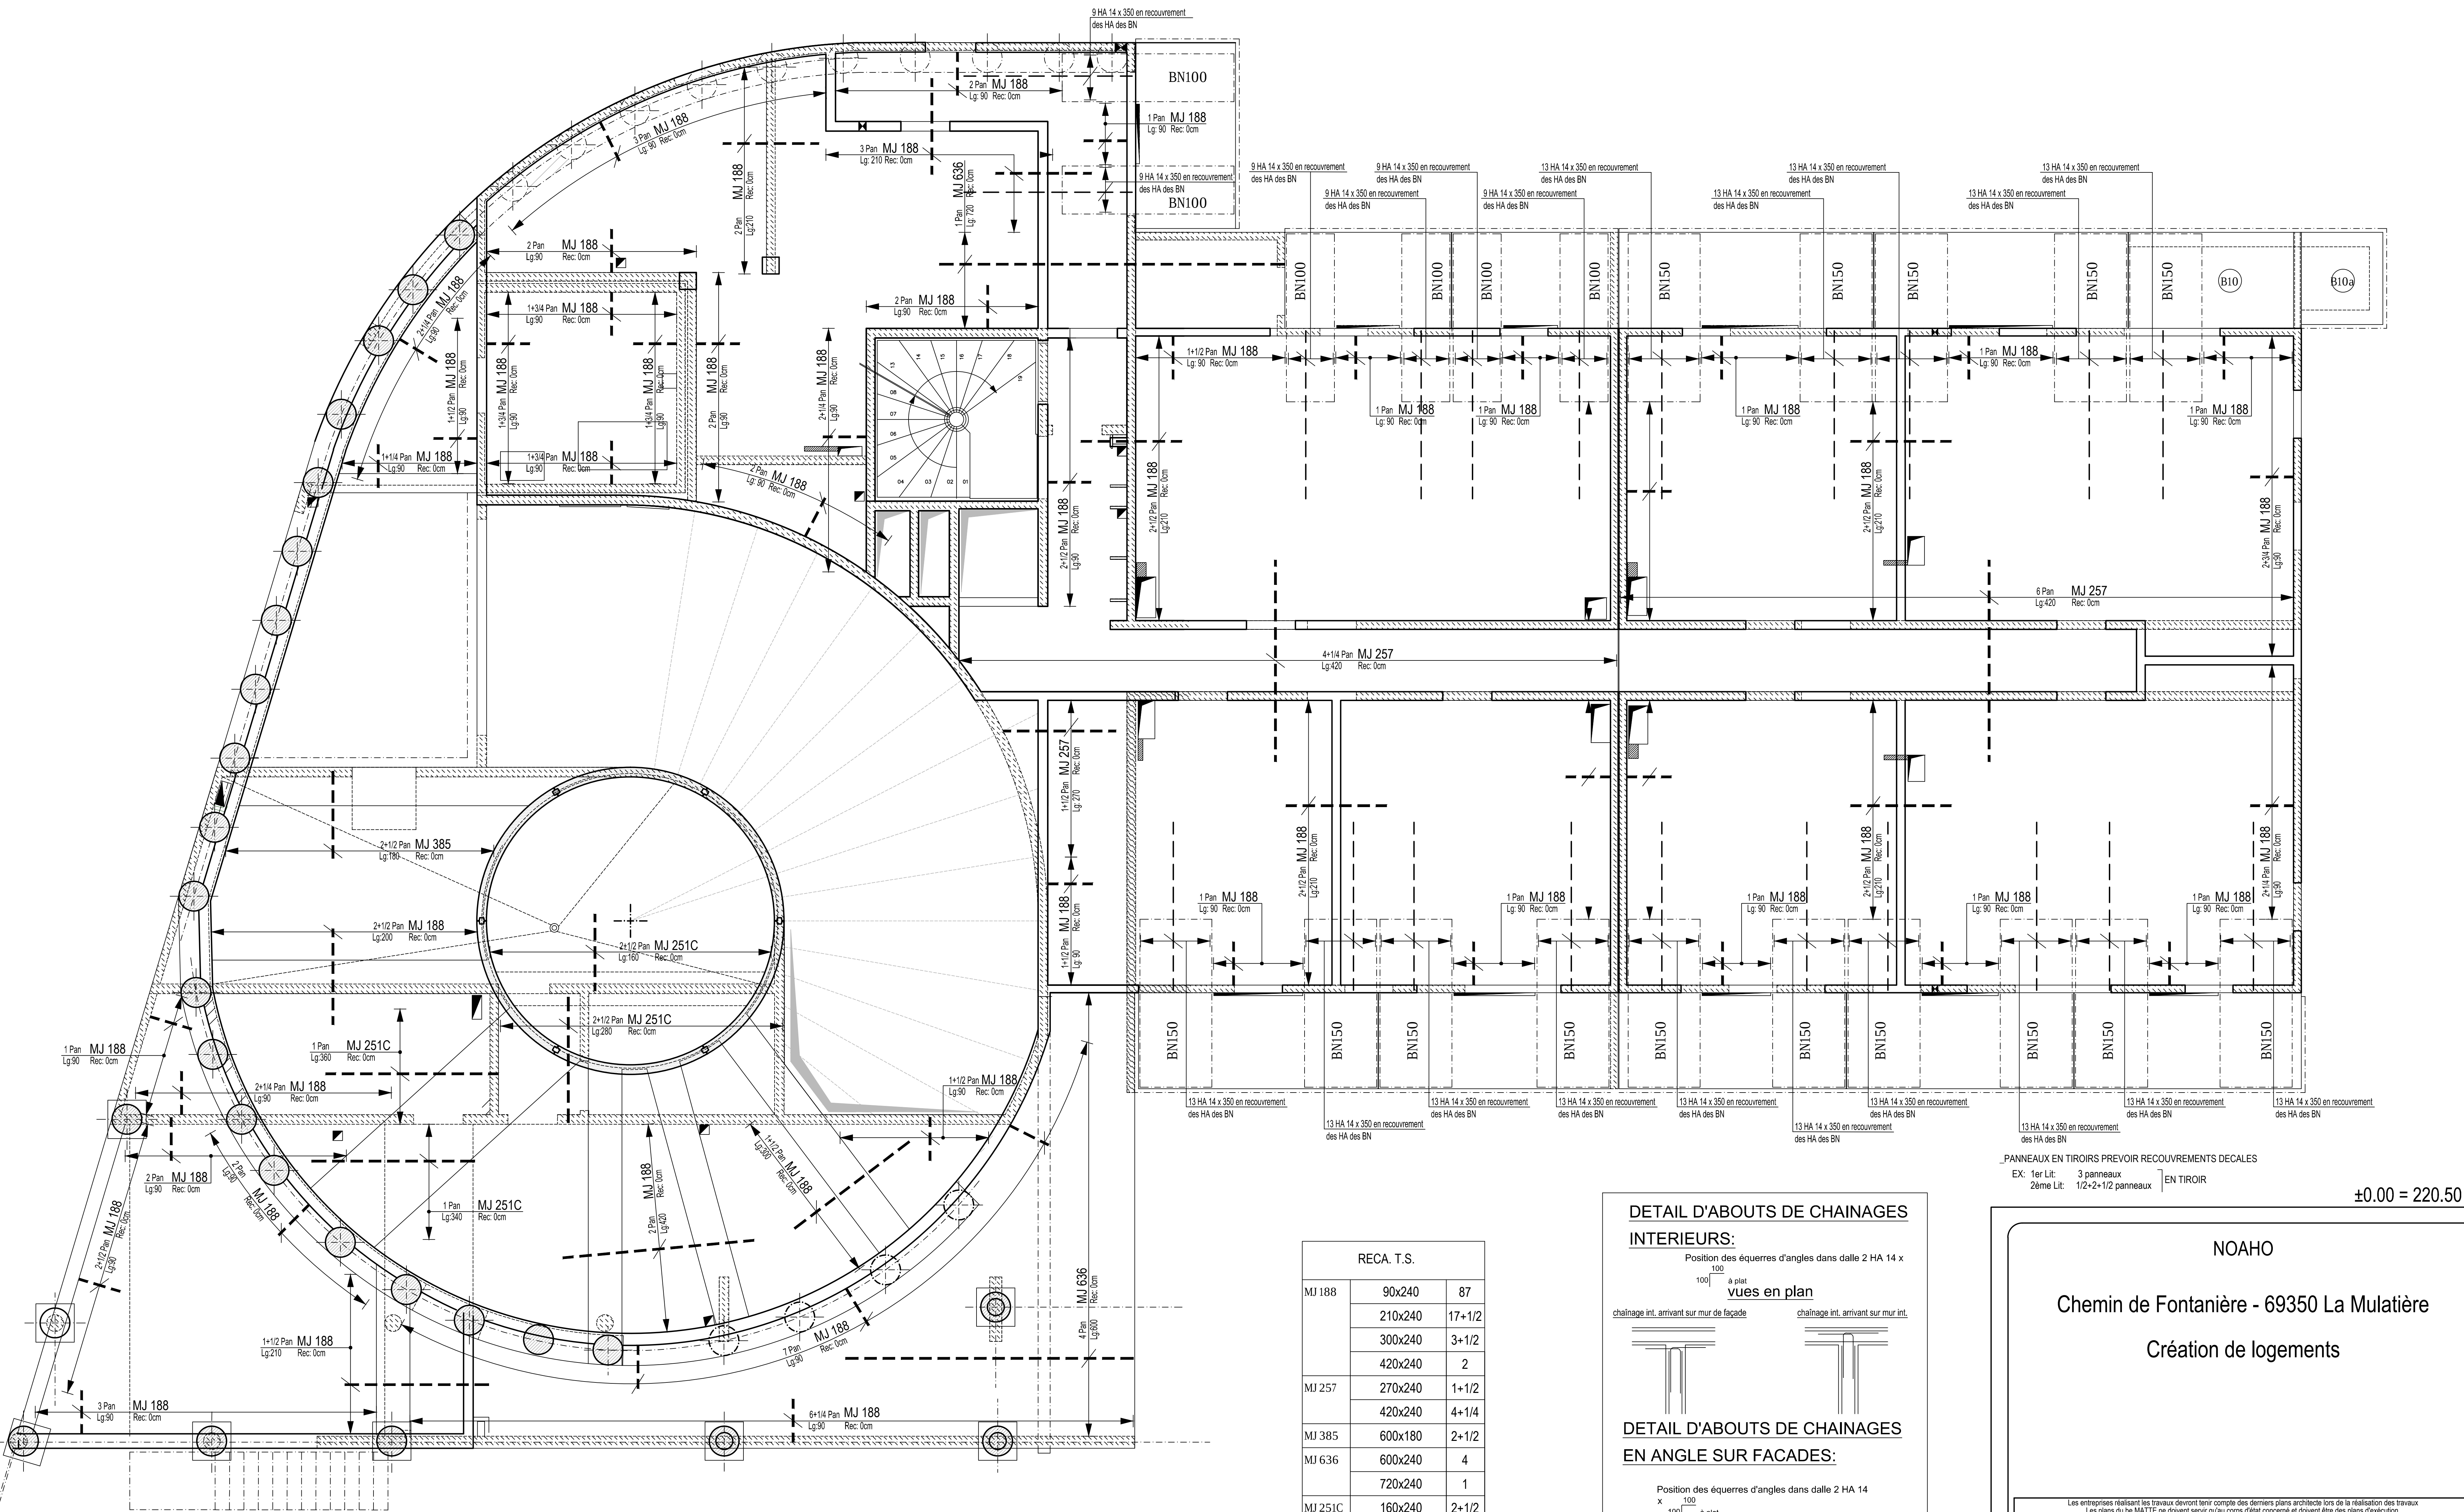


PANNEAUX EN TIROIRS PREVOIR RECouvreMENTS DECALES
EX: 1er Lit: 3 panneaux 2ème Lit: 1/2+2+1/2 panneaux EN TIROIR ±0.00 = 220.50

RECA. T.S.		
MJ 188	90x240	87
	210x240	17+1/2
	300x240	3+1/2
	420x240	2
MJ 257	270x240	1+1/2
	420x240	4+1/4
MJ 385	600x180	2+1/2
MJ 636	600x240	4
MJ 251C	720x240	1
	160x240	2+1/2
	280x240	2+1/2
	340x240	1
	360x240	1


DETAIL D'ABOUTS DE CHAINAGES
INTERIEURS:

Position des esquers d'angles dans dalle 2 HA 14 x 100
à plat
vues en plan

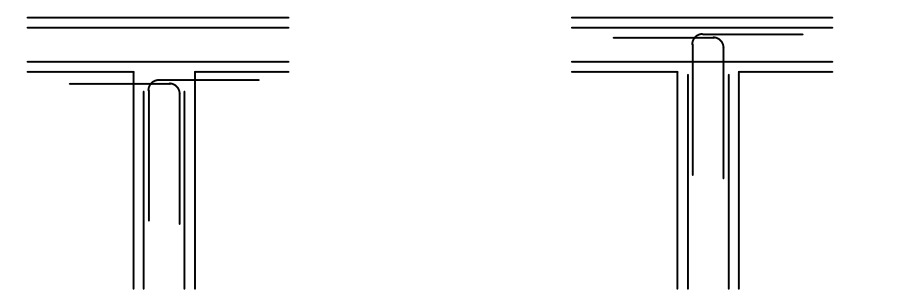


DETAIL D'ABOUTS DE CHAINAGES
EN ANGLE SUR FACADES:


Position des esquers d'angles dans dalle 2 HA 14 x 100
à plat
coupe vue en plan

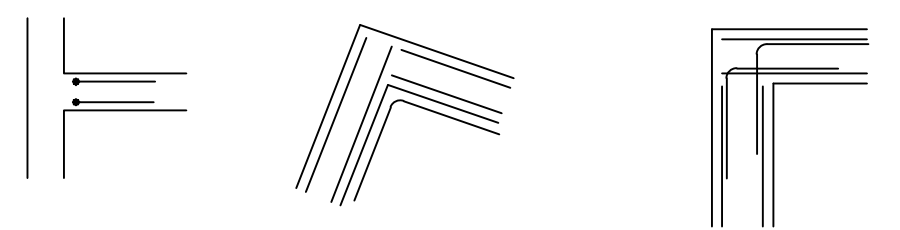

REINFORCING RESERVATIONS
JUSQU'A Ø200 mm

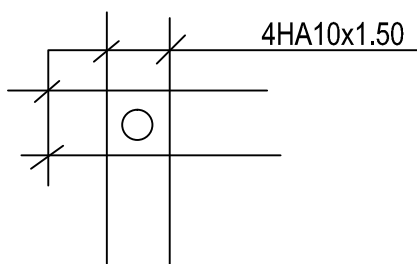

Principe de renfort aux droits des gaines:

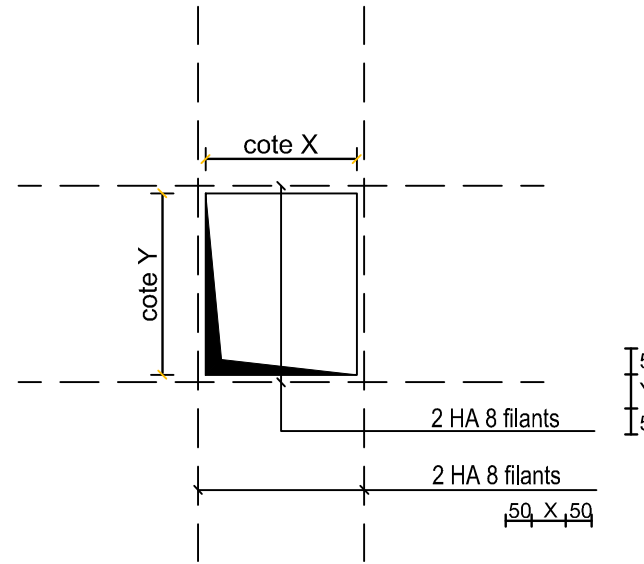

NAPPE INFERIEURE ET SUPERIEURE
NOTA: Ces renforts sont en complément des aciers mis sur la vue en plan

NOAHO

Chemin de Fontanière - 69350 La Mulatière

Création de logements

Les entreprises réalisant les travaux devront tenir compte des derniers plans architectes lors de la réalisation des travaux
Les plans du lot MATTE ne doivent pas être utilisés sans l'accord préalable de l'architecte et doivent être mis à jour d'urgence.

ARCHITECTES: ATELIER DE LA PASSERELLE MO. DELEGUE: PSD Ingénierie
BET STRUCTURE: MATTE SAS MOE: PSD Ingénierie
BET FLUIDES: PRELEM CSPS: SUD EST COORDINATION
ECONOMISTE: EXECO CPC:
BUREAU DE CONTROLE: Bureau VERITAS ENTREPREISES: Fontanel-pbc

Bât: A
PLANCHER sur -1 entre files 1 et 9
ARMATURES DALLE SUP

INDICE	DATE	MODIFICATIONS

MATTÉ
BUREAU D'ETUDES
STRUCTURES ET FLUIDES

119 BOULEVARD STALINGRAD 69100 VILLEURBANNE
Tel. 04 72 44 03 97 Fax 04 72 44 26 59
E-mail: matt@matte.fr

Dessiné par : J.B.O
Contrôle par : P.LIN
Echelle : 1/50"

DOE

Contenance de sol: 8 bars EL5
Aciers HA (T) FeE500
Aciers Doux (D) FeE235
Aciers TS FeE 400
Béton C20/25
Enrobage: 3 cm

PLAN N°
A39 0
DATE : 27/01/2016

Affaire N°
13.12.119