




±0.00 = 220.50

NOAHO
LE 180°
Chemin de Fontanière - 69350 La Mulatière

Création de logements

Les informations relatives aux travaux doivent être consultées des derniers plans approuvés par le Service des Travaux.
Les plans de MATTE ne doivent servir qu'à titre d'information et ne doivent pas être utilisés pour la construction.

ARCHITECTES: ATTELIER DE LA PASSERELLE
BUREAU D'ETUDES: MATTE SAS
BUREAU DE CONTRÔLE: Bureau VERITAS

MOULAGE: PSO Ingénierie
SUITE D'ORDINATION: PSO Ingénierie
ENTREPRISE: Fontaine

Bât A
PLANCHER SUR REZ
Coffrage

DOE
Contenu de sol 8 Bats ELS
Adress HA (T) FdE500
Adress Dca (S) FdE 235
Adress TS FdE 500
Séjour (S) = 200m²
Enlèvement 3 cm

INDEXE | DATE | MODIFICATIONS

A | 16/02/2016 | MODIFIE COUPES R.S.U et FdE

B | 16/02/2016 | COMPLETE

C | 03/03/2016 | DEPLACER POUTRE N°10

D | 08/04/2016 | MISE A JOUR REPERAGE

E | 14/04/2016 | MISE A JOUR FACADE OUEST

MATTE
BUREAU D'ETUDES
STRUCTURES ET FLUIDES

118 RUE ALFRED STALINGRAD 69100 VILLEURBANNE
TEL: 04 72 74 12 37 Fax: 04 72 74 12 38
E-mail: info@matte.fr

Dessiné par: J. BO
Contrôlé par: P. LIN
Echelle: 1/500

PLAN N°
A40 E

DATE: 28/01/2016

Affaire N°
13.12.118