


ARMATURES DALLE Epr: 40 cm

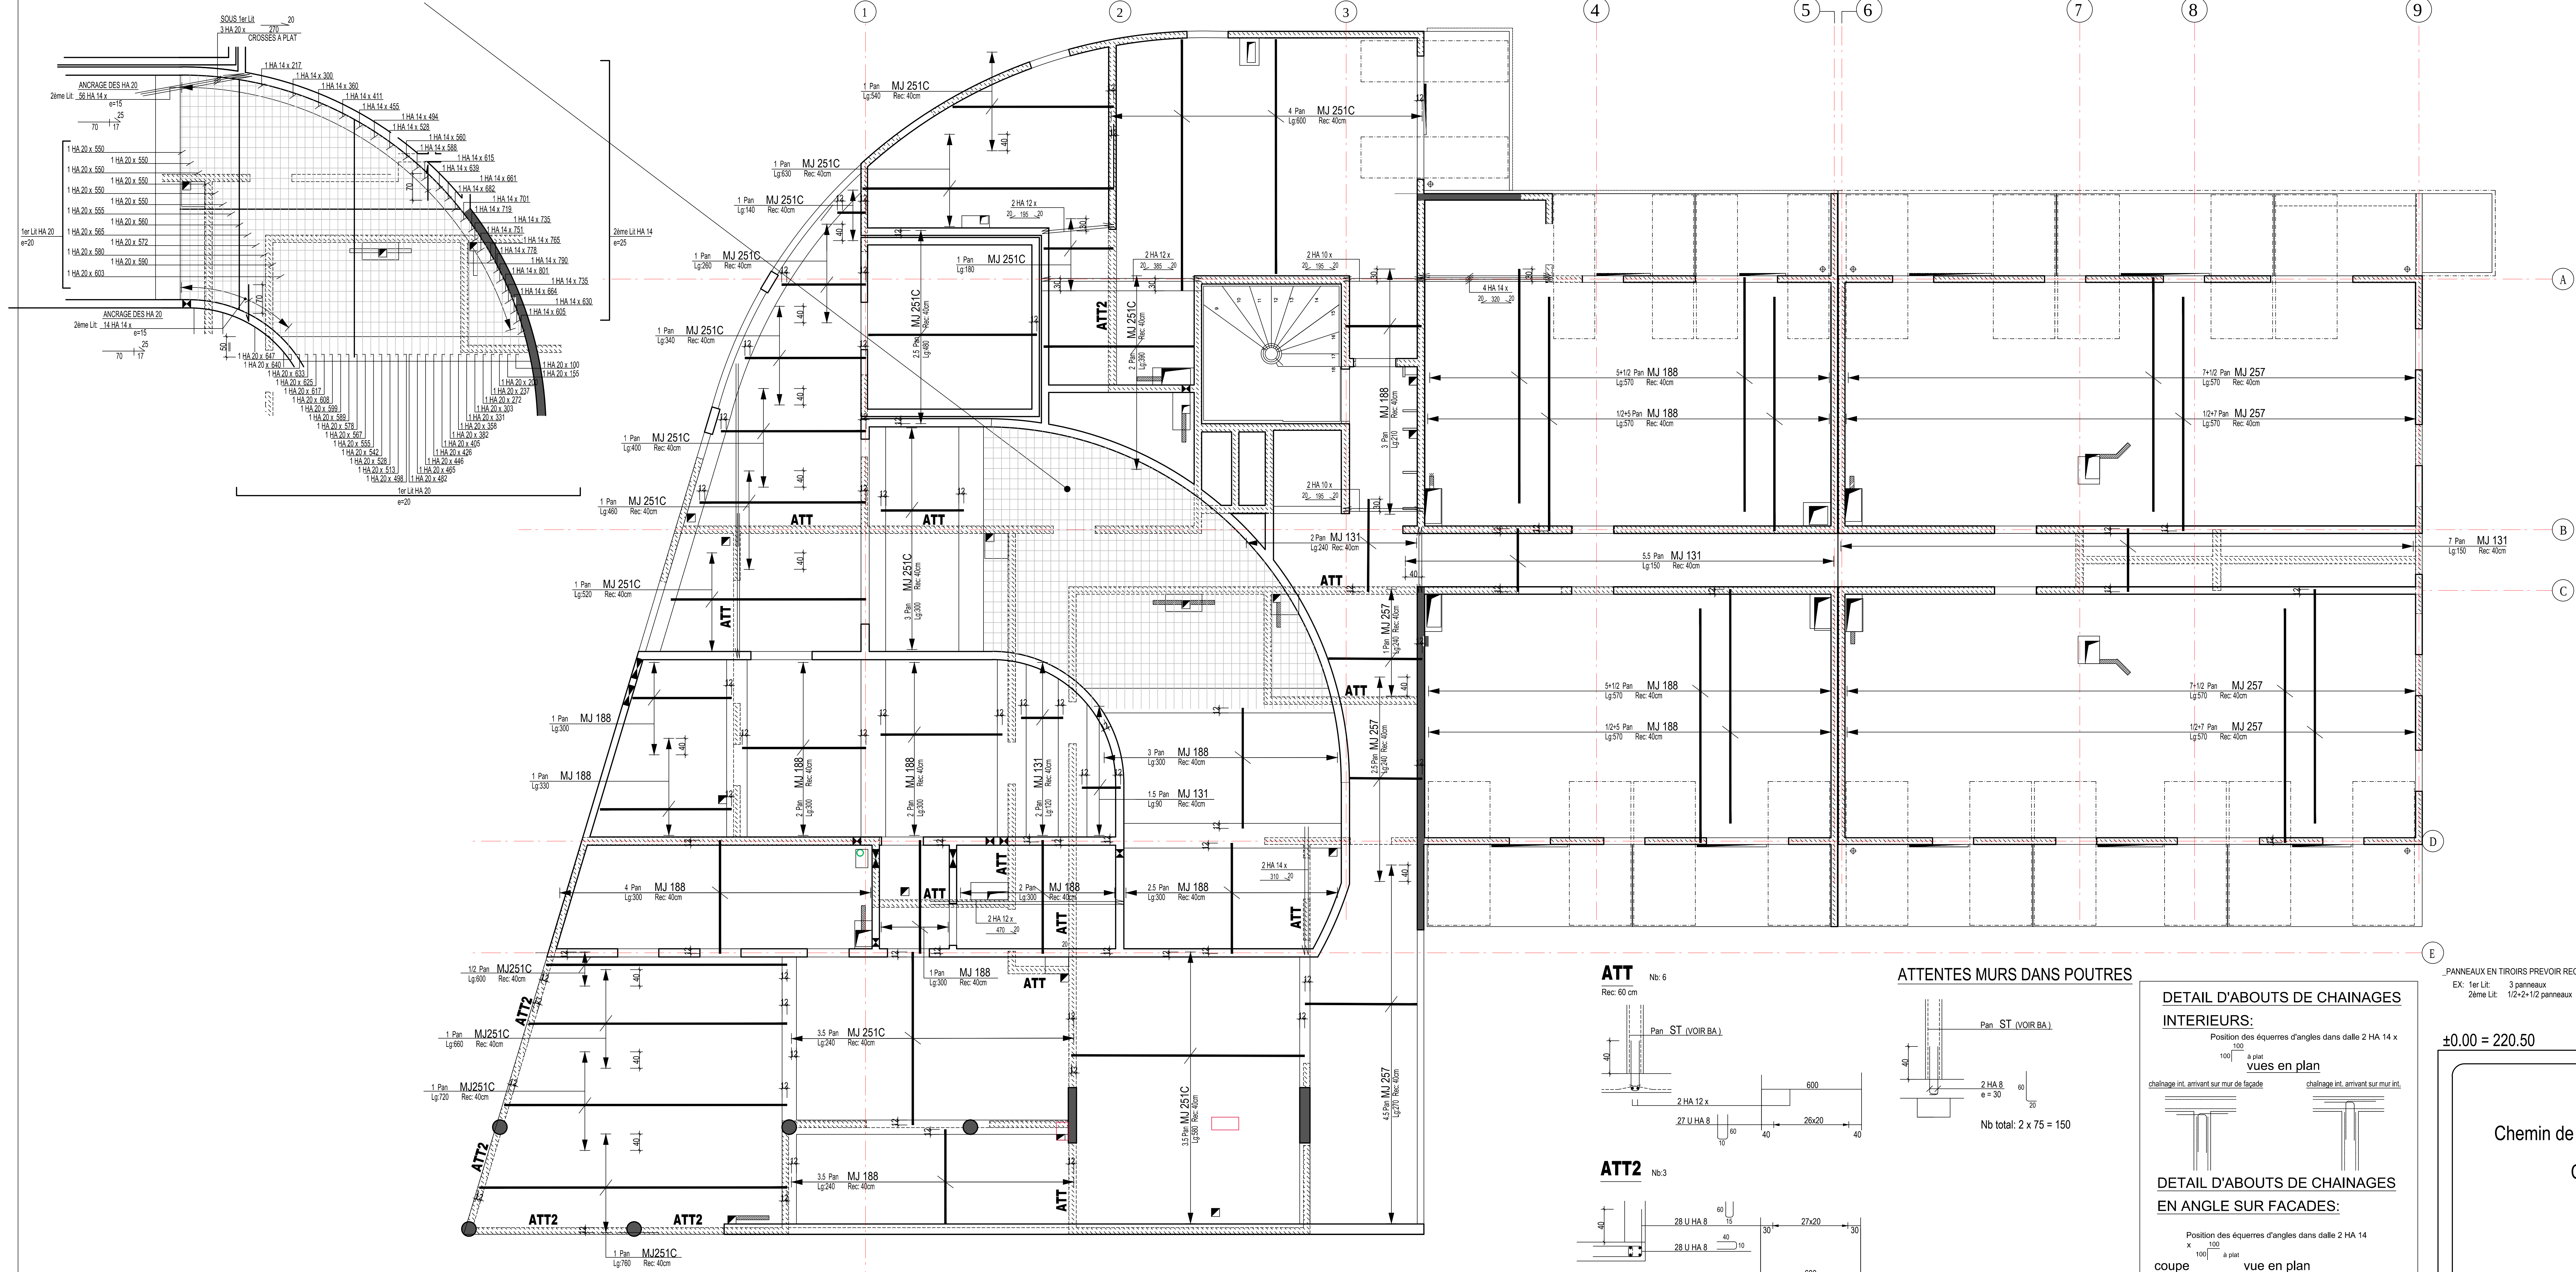

COMMANDE du 22/02/2016


RECA. T.S.		
MJ 131	90x240	2
	120x240	2
MJ 188	240x240	4
	300x240	18
	330x240	1
MJ 251C	140x240	1
	240x240	4
	260x240	1
	300x240	3
	340x240	1
	400x240	1
	460x240	1
	520x240	1
	580x240	4
	600x240	1
	660x240	1
	760x240	1

COMMANDE du 20/02/2016


RECA. T.S.		
MJ 131	150x240	13
	240x240	2
MJ 188	570x240	22
	210x240	3
MJ 257	570x240	30
	240x240	4
	270x240	5
MJ 251C	180x240	1
	350x240	2
	480x240	3
	540x240	1
	600x240	1
	630x240	1

PANNEAUX EN TIROIRS PREVOIR RECOURVEMENTS DECALES
EX: 1er Lit: 3 panneaux
2ème Lit: 1/2-2-1/2 panneaux EN TIROIR

±0.00 = 220.50

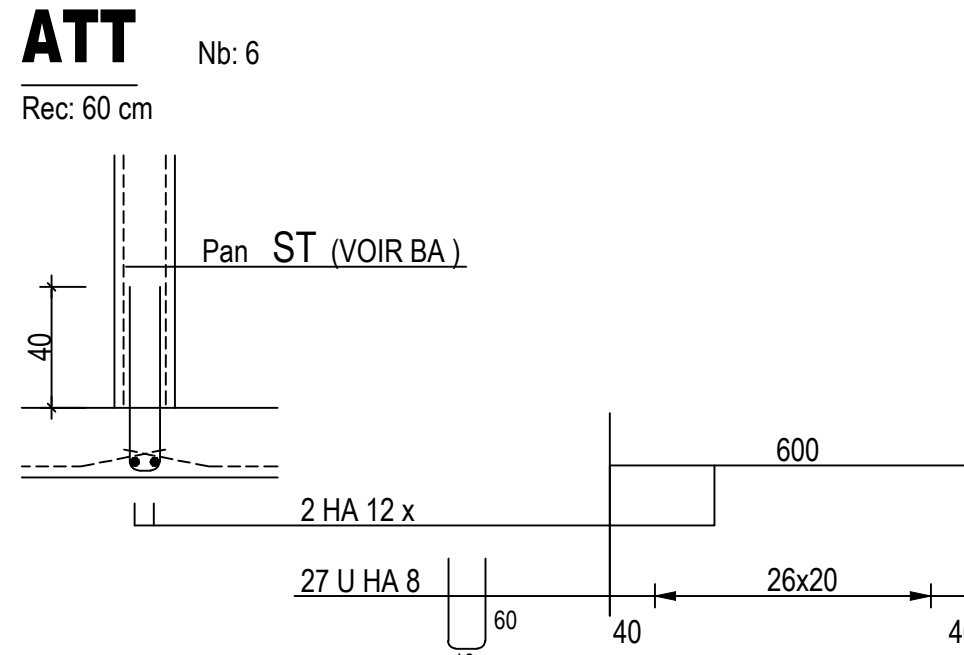


ATTENTES MURS DANS POUTRES

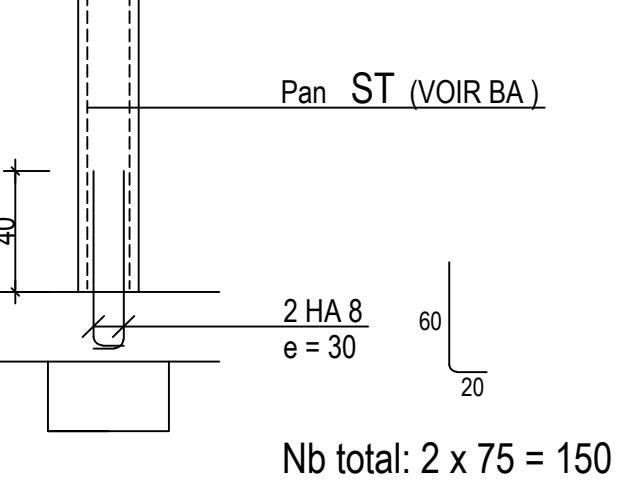




DETAIL D'ABOUTS DE CHAINAGES INTERIEURS:

Position des équerres d'angles dans dalle 2 HA 14 x 100 à plat
vues en plan

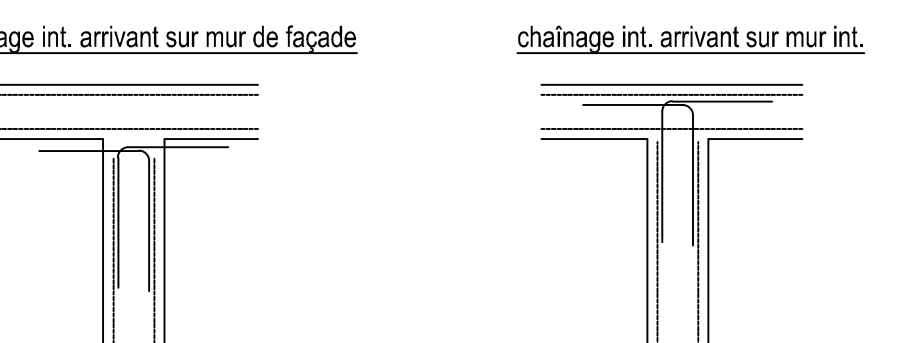


DETAIL D'ABOUTS DE CHAINAGES EN ANGLE SUR FACADES:


Position des équerres d'angles dans dalle 2 HA 14 x 100 à plat
coupe

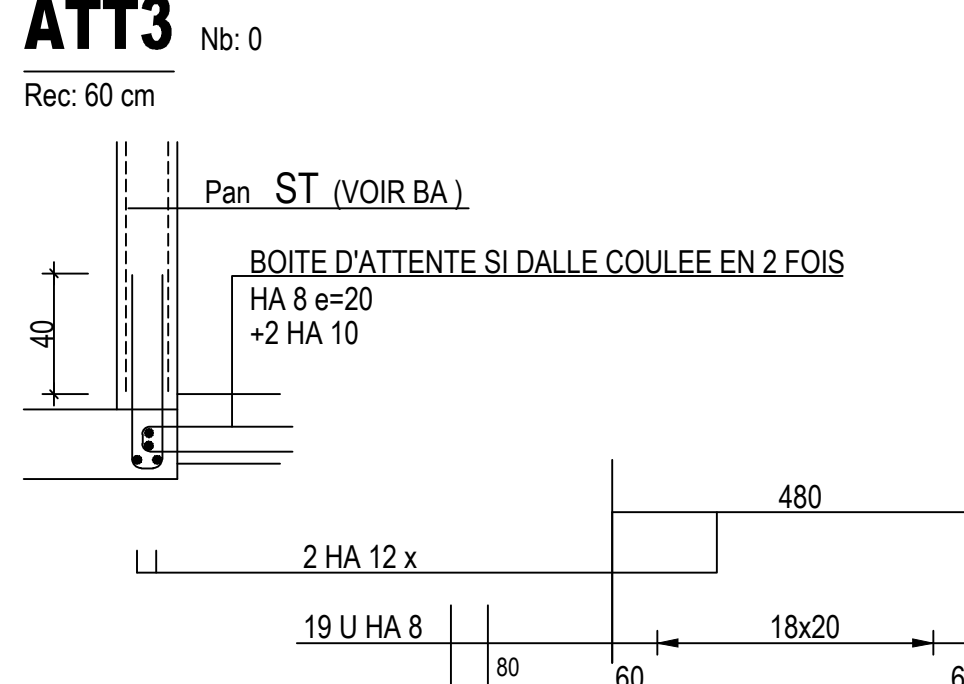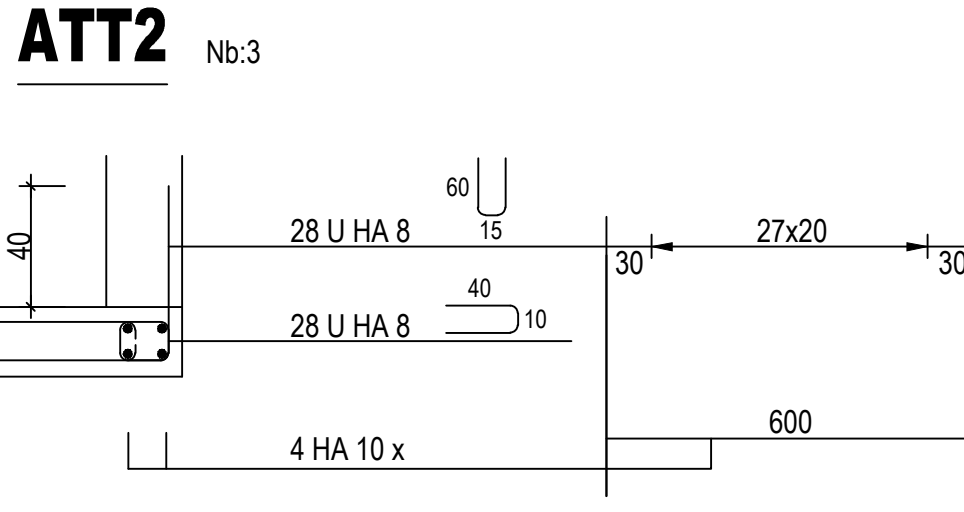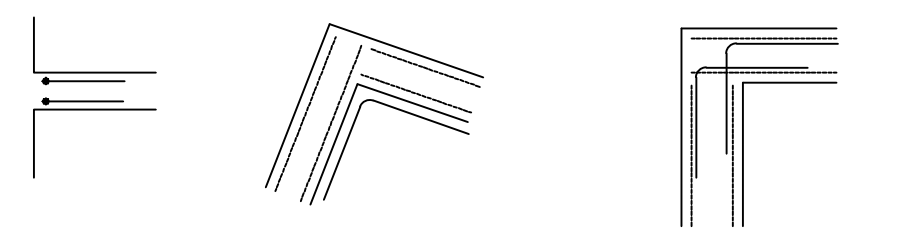

RENFORTS RESESERVATIONS JUSQU'A Ø200 mm

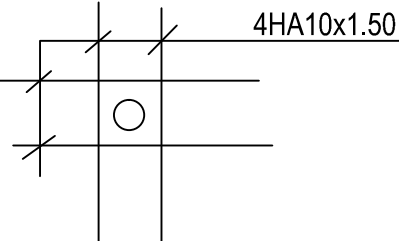

Principe de renfort aux droits des gaines:

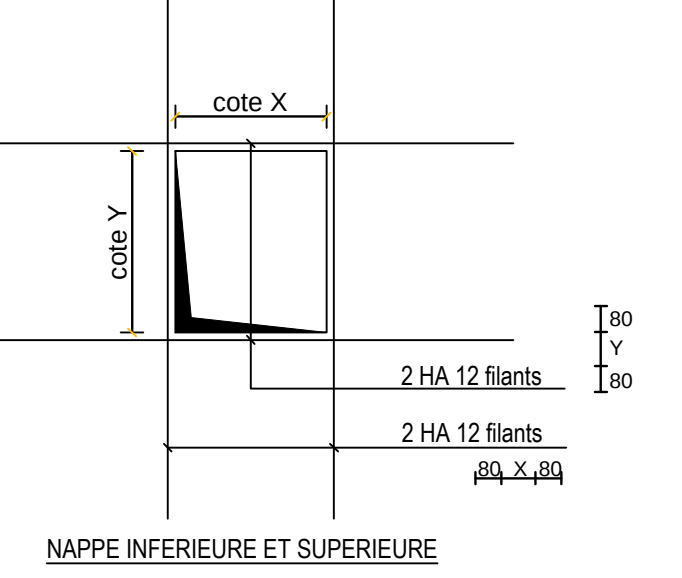

NOAHO
LE 180°
Chemin de Fontanière - 69350 La Mulatière
Création de logements

Les entreprises réalisant les travaux devront tenir compte des derniers plans architectes lors de la réalisation des travaux.
Les plans du Bâtiment ne doivent servir qu'à titre de référence et ne doivent pas être utilisés pour la réalisation des plans d'exécution.

ARCHITECTES:	ATELIER DE LA PASSERELLE	MO DELEGUE:	PSO Ingénierie
BET STRUCTURE:	MATTÉ SAS	MO:	CSPS
BET FLUIDES:	PRELEM	SUD EST COORDINATION	OPC:
ECONOMISTE:	EXECO	ENTREPRISES:	Fontanel
BUREAU DE CONTROLE:	Bureau VERITAS		

BâtA

PLANCHER SUR REZ

ARMATURES DALLES INFERIEURES

DOE

Commande de sol: 8 bords ELS

Aciers HA (T) FcE500

Aciers Dou (D) FcE235

Aciers TS FcE500

Béton f28 >= 20MPa

Enrobage > 3 cm

INDICE	DATE	MODIFICATIONS
A	22/02/2016	AJOUTE COMMANDE du 22/02/2016
B	02/03/2016	MISE A JOUR COMMANDE ARMATURES DALLE Epr: 40 cm

MATTÉ

BUREAU D'ETUDES

STRUCTURES ET FLUIDES

1119 BOULEVARD STANISLAS 69100 VILLEURBANNE

Tel: 04 72 44 02 87 Fax 04 72 44 26 59

E-mail: bat@matte.fr

Dessiné par: J. BO

Contrôlé par: P. LIN

Echelle: 1/50'

Plan N° A44 B

DATE: 19/02/2016

Affaire N° 13.12.118