


ARMATURES DALLE Epr: 40 cm

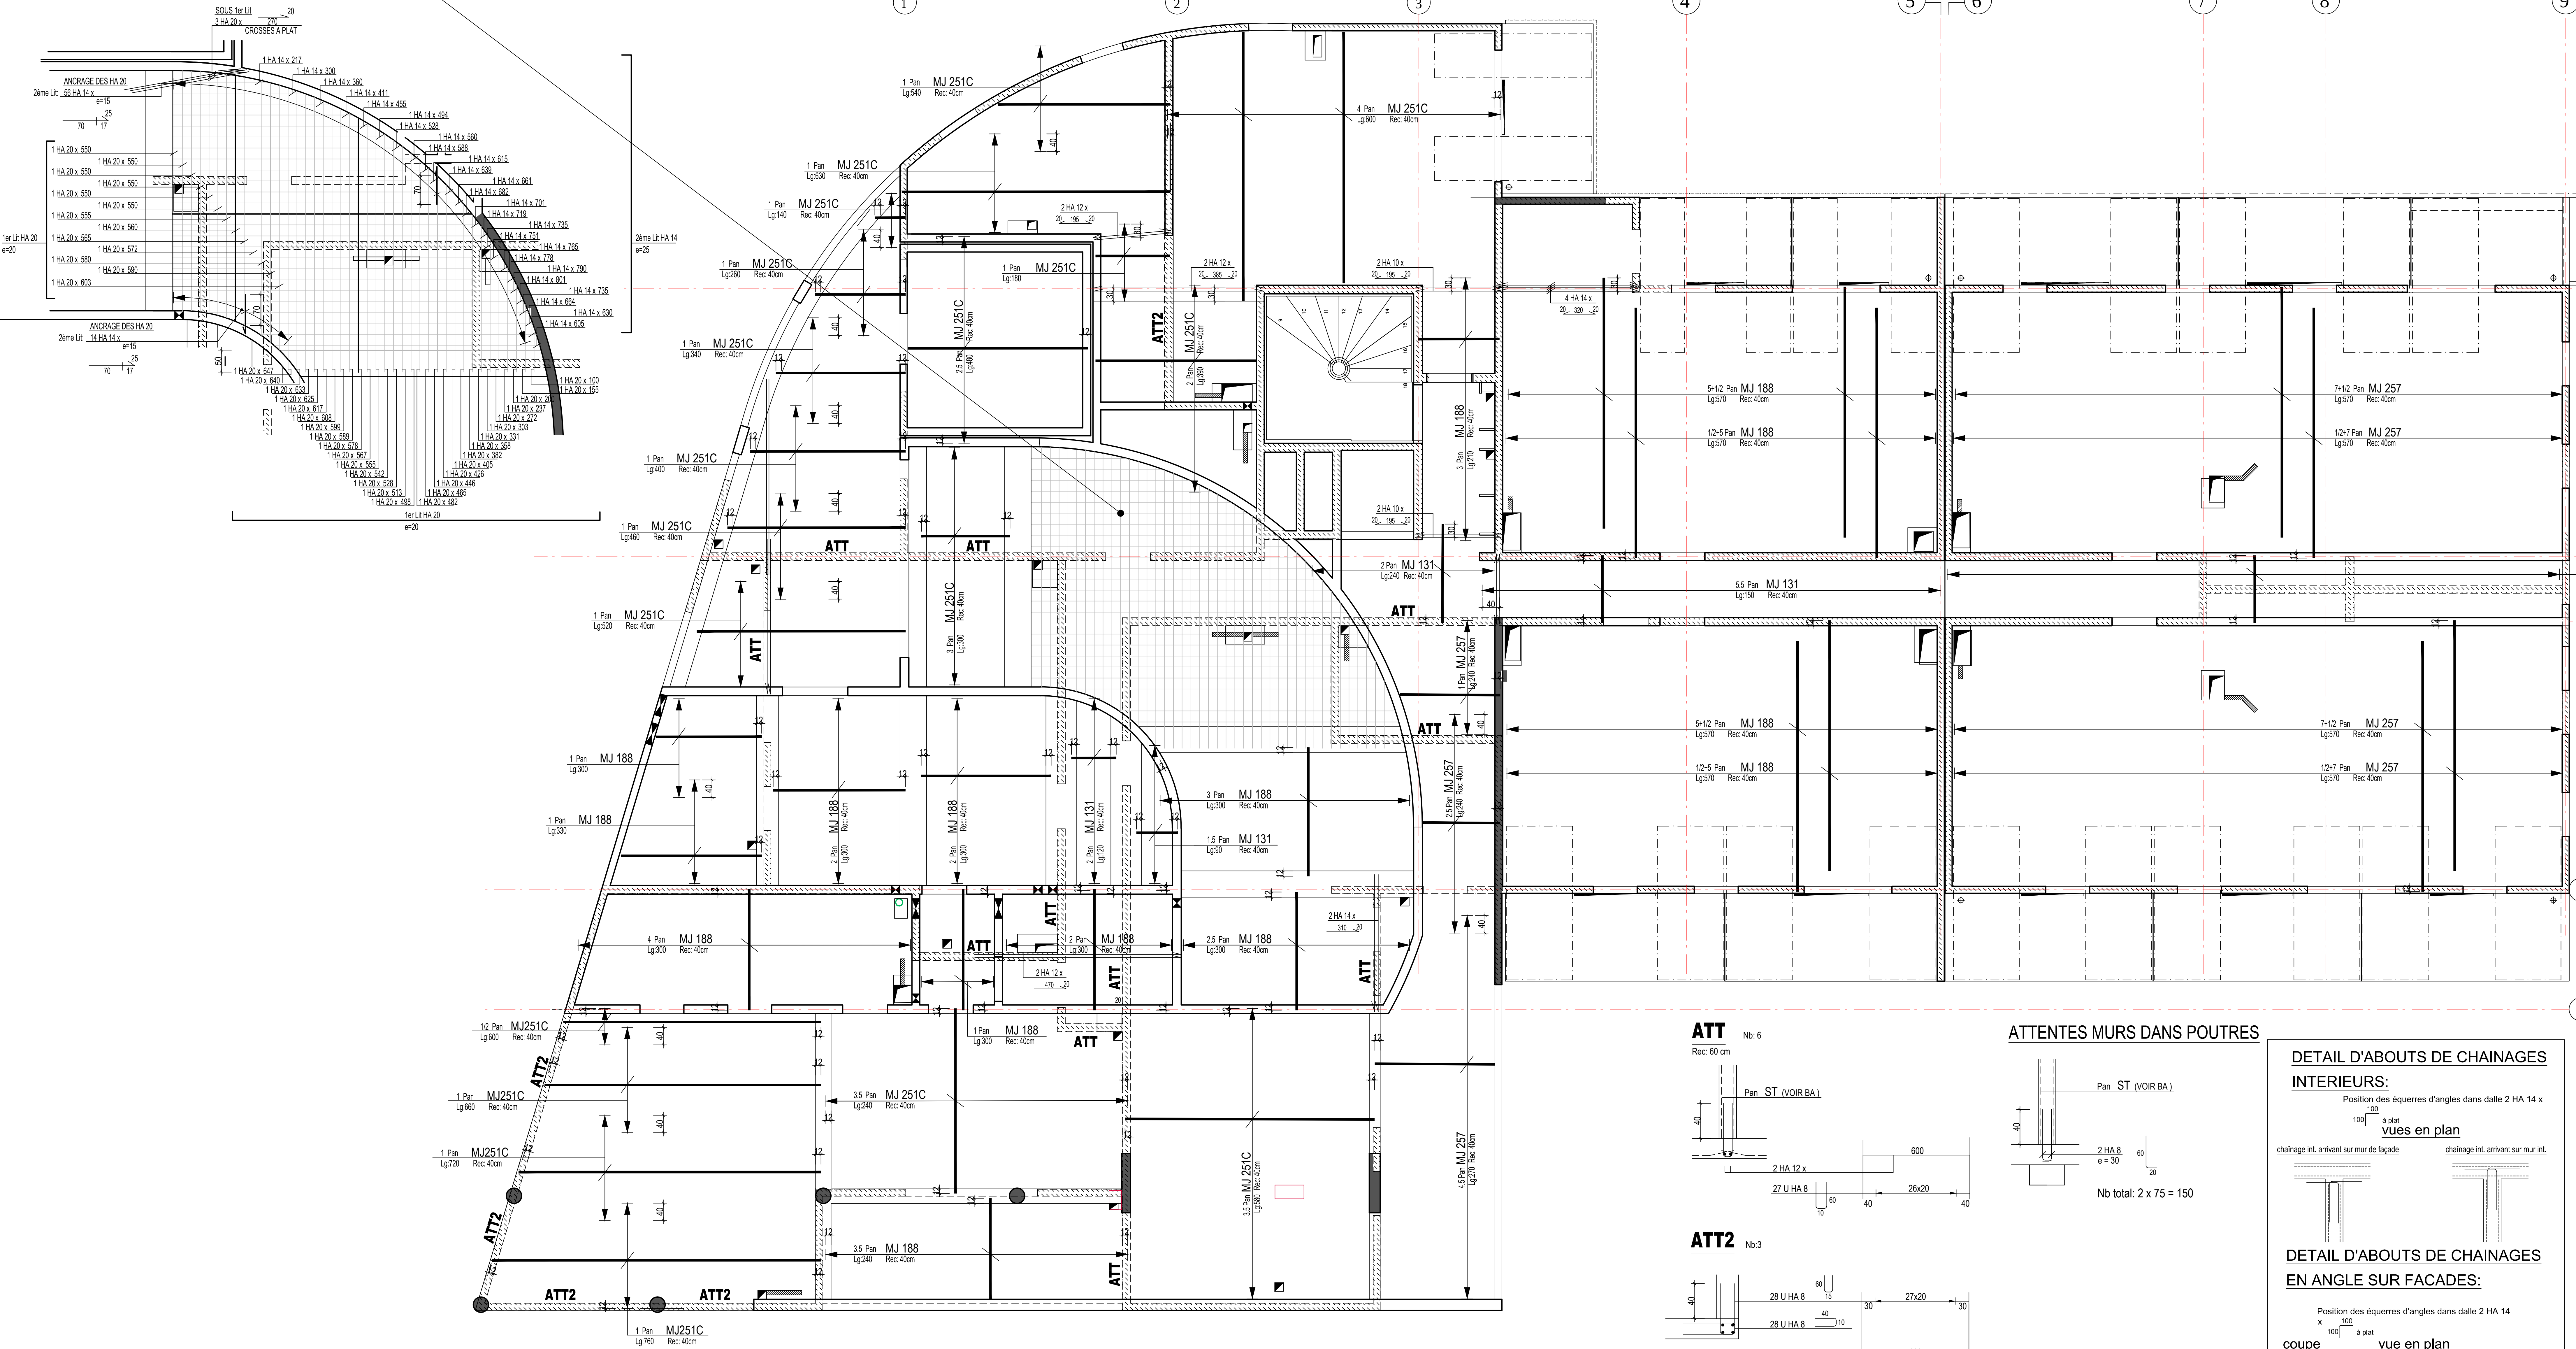

COMMANDE du 22/02/2016



RECA. T.S.		
MJ 131	90x240	2
	120x240	2
MJ 188	240x240	4
	300x240	18
	330x240	1
MJ 251C	140x240	1
	240x240	4
	260x240	1
	300x240	3
	340x240	1
	400x240	1
	460x240	1
	520x240	1
	580x240	4
	600x240	1
	660x240	1
	760x240	1

COMMANDE du 20/02/2016

RECA. T.S.		
MJ 131	150x240	13
	240x240	2
MJ 188	570x240	22
	210x240	3
MJ 257	570x240	30
	240x240	4
	270x240	5
MJ 251C	180x240	1
	350x240	2
	480x240	3
	540x240	1
	600x240	1
	630x240	1




PANNEAUX EN TIROIRS PREVOIR RECROUVREMENTS DECALES
EX: 1er Lit: 3 panneaux
2ème Lit: 1/2+2+1/2 panneaux

±0.00 = 220.50

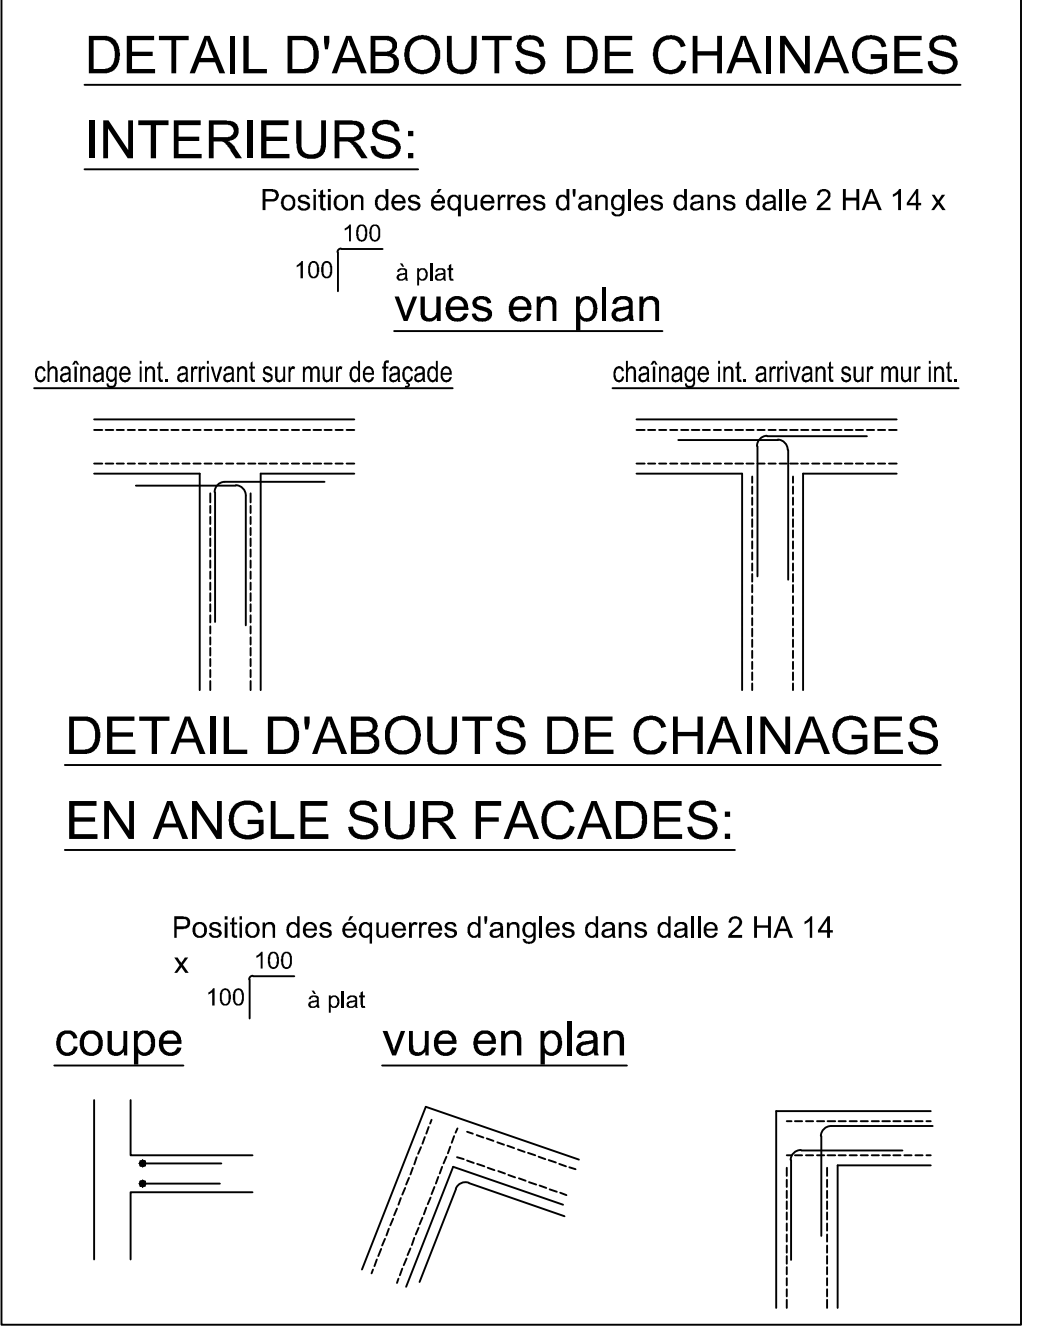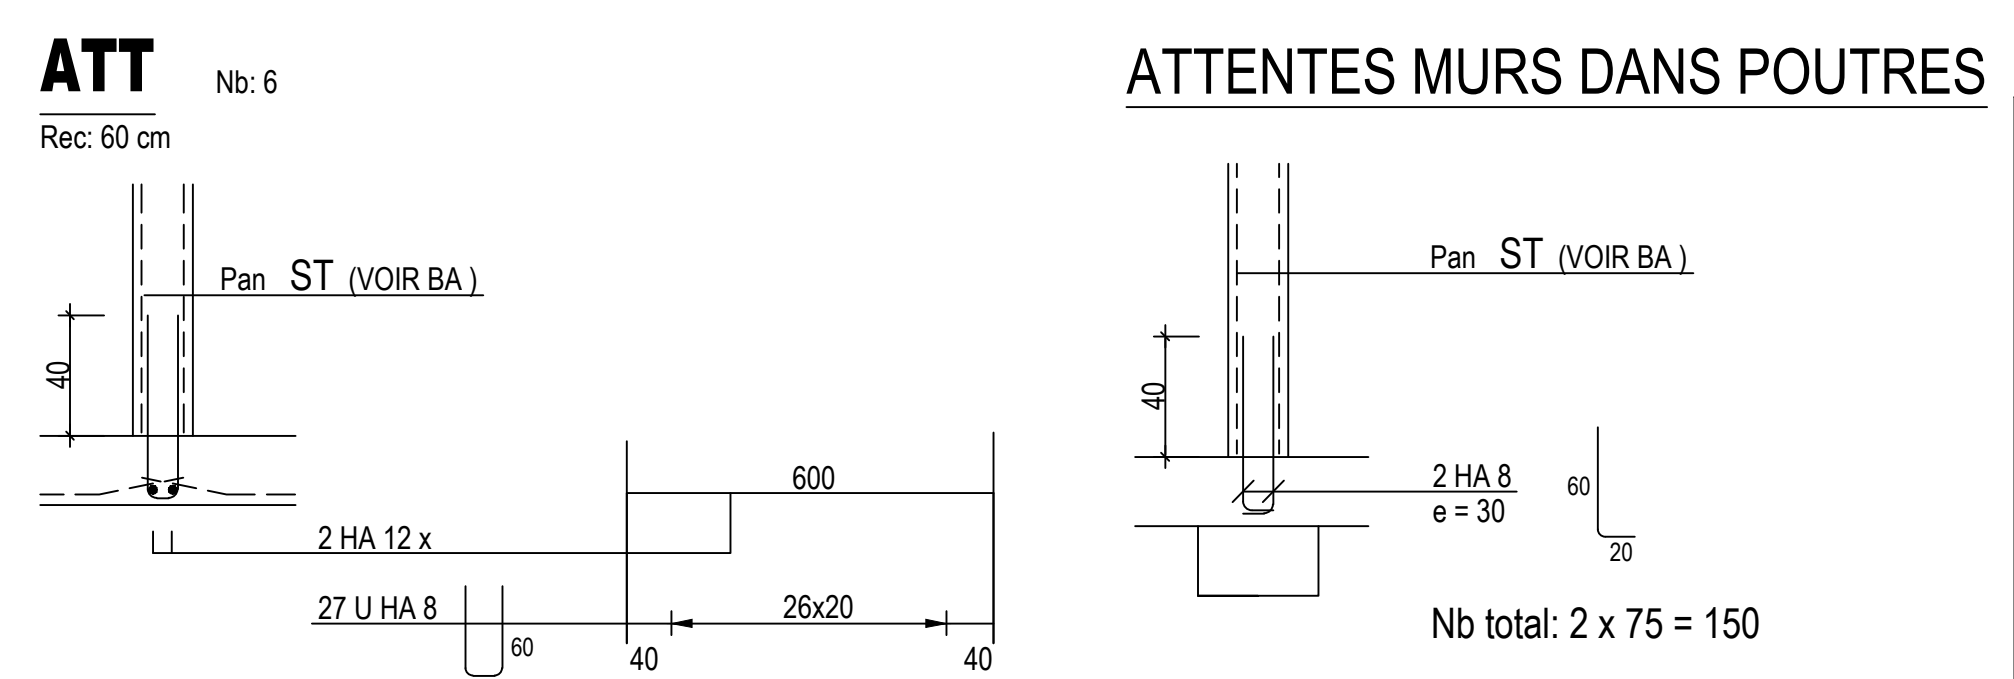

RENFORTS RESESERVATIONS
JUSQU'A Ø200 mm

Principe de renfort aux droits des gaines:

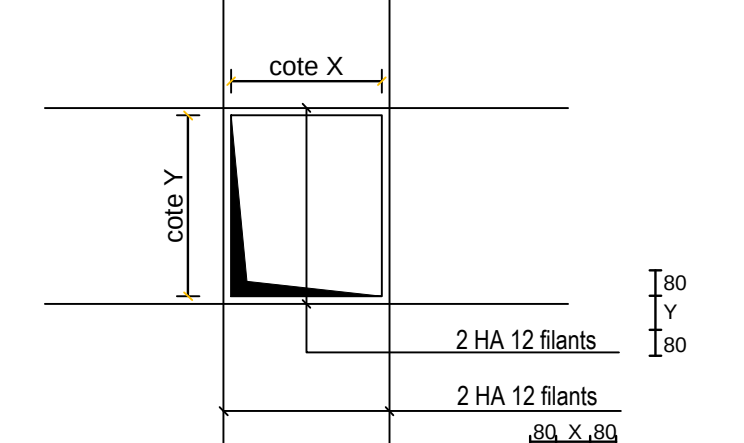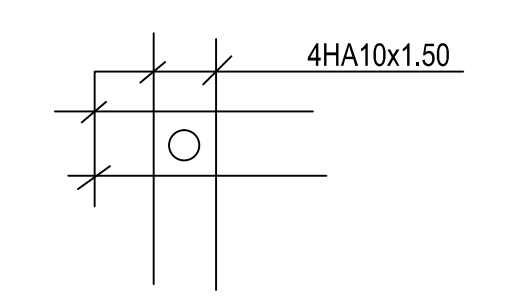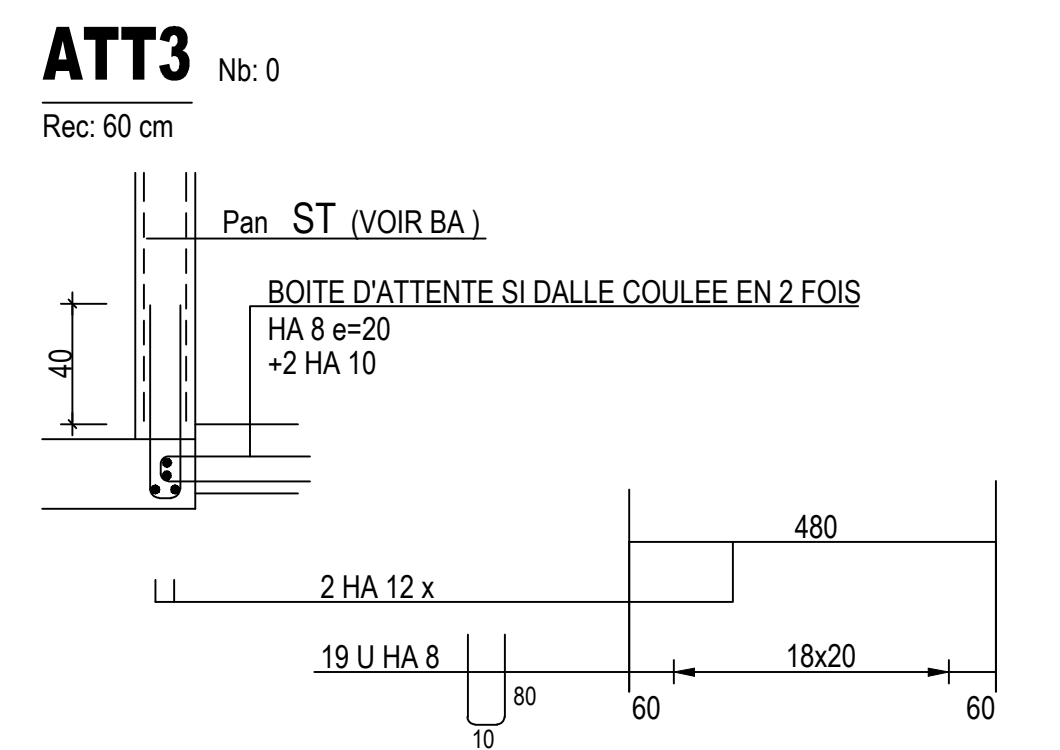

NOTA: Ces renforts sont en complément des autres mis sur la vue en plan

NOAHO

LE 180°

Chemin de Fontanière - 69350 La Mulatière

Création de logements

ATELIER DE LA PASSERELLE

BET STRUCTURE: MATTE SAS

BET FLUIDES: PRELEM

ECONOMISTE: EXECO

BUREAU DE CONTRÔLE: Bureau VERITAS

MO DELEGUE: PSD Ingénierie

MO: CSPE: SUD EST COORDINATION

OPC: ENTREPRISE(S): Fontanel

Bât A

PLANCHER SUR REZ

ARMATURES DALLES INFERIEURES

INDICE: A 22/02/2016 AJOUTE COMMANDE du 22/02/2016

DATE: 02/03/2016 MISE A JOUR COMMANDE ARMATURES DALLE Epr: 40 cm

MODIFICATIONS: A 22/02/2016 AJOUTE COMMANDE du 22/02/2016

DATE: 02/03/2016 MISE A JOUR COMMANDE ARMATURES DALLE Epr: 40 cm

MATTÉ

BUREAU D'ETUDES

STRUCTURES ET FLUIDES

119 BOULEVARD STALINGRAD 69100 VILLEURBANNE

Tel: 04 72 44 02 87 Fax: 04 72 44 28 55

E-mail: matt@matte.fr

DOE

Contrainte de sol: 8 bars ELS

Achers HA (T) FAE500

Achers Dow (Ø) FAE 205

Achers TS FAE 500

Béton C28+20MPa

Enrobé = 3 cm

PLAN N°

A44 B

DATE: 19/02/2016

Dessiné par: J BO

Contrôlé par: P LIN

Echelle: 1/150°

Affaire N°

13.12.118