


PLANCHER SUR REZ
ARMATURES SUPERIEURES

Aff: S.13.12.119 Bât A LA MULATIERE-69350 LA MULATIERE
REPRISE Plan n° A.100 0

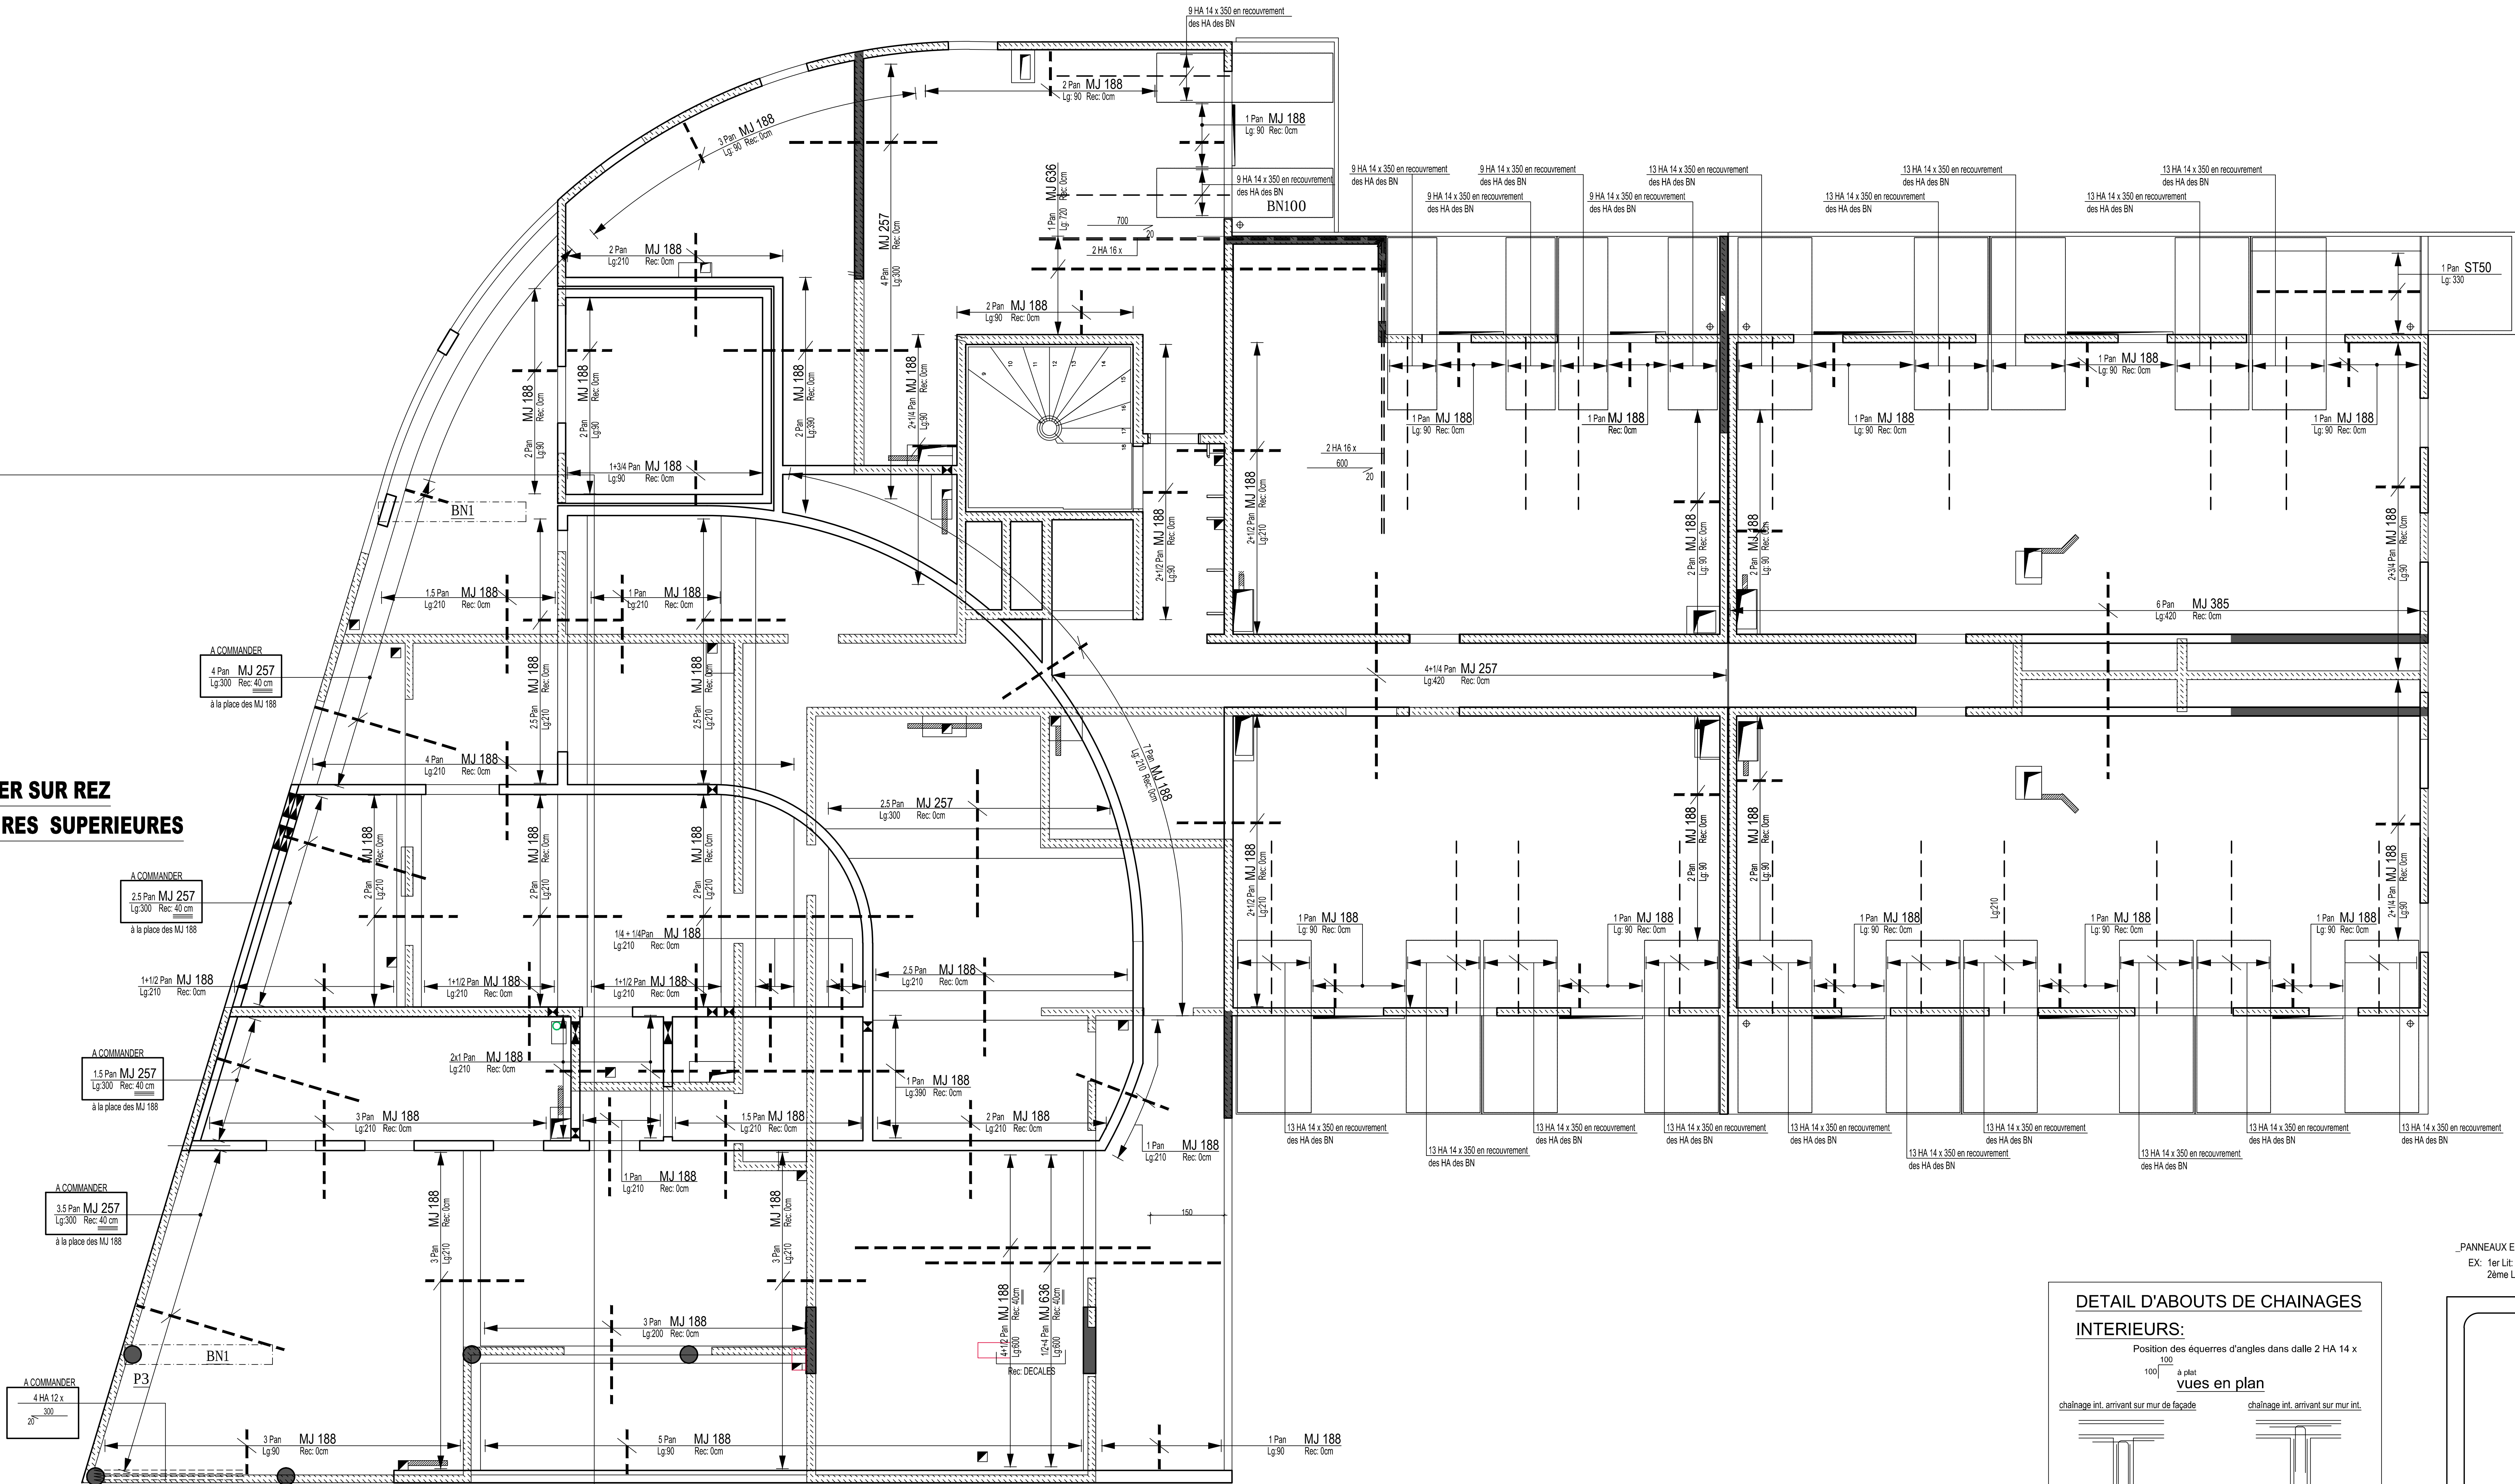

COMMANDE du 22/02/2016

RECA. T.S.		
MJ 188	90x240	26
	210x240	41
	390x240	3
	600x240	5
MJ 257	300x240	3
MJ 636	600x240	5

COMMANDE du 20/02/2016

RECA. T.S.		
MJ 188	90x240	40
	210x240	16
MJ 257	300x240	4
MJ 385	420x180	6
MJ 636	720x240	1

DETAIL D'ABOUTS DE CHAINAGES
INTERIEURS:



Position des équerres d'angles dans dalle 2 HA 14 x 100
à plat
vues en plan
chaînage int. arrivant sur mur de façade
chaînage int. arrivant sur mur int.

DETAIL D'ABOUTS DE CHAINAGES
EN ANGLE SUR FACADES:

Position des équerres d'angles dans dalle 2 HA 14 x 100
à plat
coupe
vue en plan

RENFORTS RESESERVATIONS
JUSQU'A Ø200 mm

Principe de renfort aux droits des gaines:

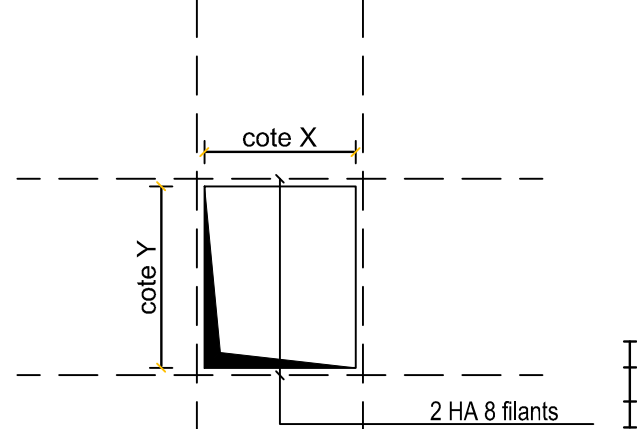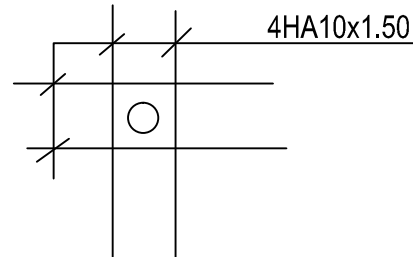

NAPPE INFÉRIEURE ET SUPÉRIEURE
NOTA: Ces renforts sont en complément des aciers mis sur la vue en plan

...Panneaux en Tiroirs prévoir recouvrements décalés
EX: 1er Lit: 3 panneaux
2ème Lit: 1/2-2+1/2 panneaux
EN TIROIR

±0.00 = 220.50

NOAHO
LE 180°
Chemin de Fontanière - 69350 La Mulatière
Création de logements

Les entreprises réalisant les travaux devront tenir compte des derniers plans architectes lors de la réalisation des travaux
Les plans du lot MATTE ne doivent servir qu'à des corps d'état concordés et doivent être des plans d'exécution

ARCHITECTES:	ATELIER DE LA PASSERELLE	MO DELEGUE:	PSO Ingénierie
BET STRUCTURE:	MATTE SAS	MO:	SUD EST COORDINATION
BET FLUIDES:	PRELEM	CPFS:	
ECONOMISTE:	EXECO	ENTREPRISES:	Fontanel
BUREAU DE CONTRÔLE:	Bureau VERITAS		

Bât A
PLANCHER SUR REZ
ARMATURES DALLE SUPERIEURE

DOE
Contrainte de sol: 8 bars ELS

INDICE	DATE	MODIFICATIONS
A	22/02/2016	AJOUTE COMMANDE DE LA FILE 1 à 3

Aciers HA (T) FdE500
Aciers Dux (R) FdE 235
Aciers TS FdE 500
Béton C28 >= 28MPa
Enrobage = 3 cm

PLAN N°
A45 A
DATE: 19/02/2016

MATTÉ
BUREAU D'ÉTUDES
STRUCTURES ET FLUIDES
119 BOULEVARD STALINGRAD 69100 VILLEURBANNE
Tél 04 72 44 02 87 Fax 04 72 44 26 55
E-mail: matt@orange.fr

Dessiné par: J BO
Contrôlé par: P LUN
Echelle: 1:100°

Affaire N°
13.12.118