




DALLES

- FINI+5.74+226.24
DALLE BA Epr. 20 cm
DESSUS BRUT+5.67
RESERVE: 7 cm
- FINI+5.74+226.24
DALLE BA Epr. 20 cm
DESSUS BRUT+5.67
RESERVE: 7 cm
- FINI+5.99+226.49
DALLE BA Epr. 20 cm
DESSUS BRUT+5.67
RESERVE: 32 cm
- FINI+6.02+226.52
DALLE BA Epr. 20 cm
DESSUS BRUT+5.67
RESERVE: 35 cm
- FINI+6.02+226.52
DALLE BA Epr. 20 cm
DESSUS BRUT+5.67
RESERVE: 35 cm

±0.00 = 220.50

NOAHO
LE 180°
Chemin de Fontanière - 69350 La Mulatière
Création de logements

Les informations relatives aux travaux doivent être consultées dans les documents suivants: Les plans de la MATTE ne doivent servir qu'à titre d'information et ne doivent pas être utilisés pour la construction.

ARCHITECTE:	ATELIER DE LA PASSERELLE	MOULAGE:	PSO Ingénierie
RESTRUCTURE:	MATTE SAS	NOUVEAU:	SUD EST COORDINATION
RETRAVAIL:	PRELEM	CPPS:	ENESCO
ACCOMMODER:	ENESCO	ENTREPRISE:	Fontanel

Bât A
PLANCHER SUR 1er
Coffrage

DOE
Conteneur de sol 8 Bars ELS
Aciers HA (T) FeE500
Aciers Doss (H) FeE235
Aciers T5 FeE 600
Sécher 120 = 200Pa
Enrobage = 3 cm

INDICE	DATE	MODIFICATIONS
A	03/03/2016	COMPLÈTE ZONE entre E1 et 3
B	04/03/2016	AJOUT COUPE 71 INCORPORER POSITION PORTE FILE D3 et MODIFIE COUPE R
C	08/04/2016	MISE A JOUR REPERAGE PREFE

MATTE
BUREAU D'ETUDES
STRUCTURES ET FLUIDES
110 RUE DU 14 JUILLET 69100 VILLEURBANNE
Tél: 04 72 74 82 07 Fax: 04 72 74 82 09
E-mail: info@matte.fr

Dessiné par: J.B.O.
Contrôlé par: P.L.N.
Echelle: 1/500

PLAN N°
A46 C
DATE: 28/02/2016

Affaire N°
13.12.118