

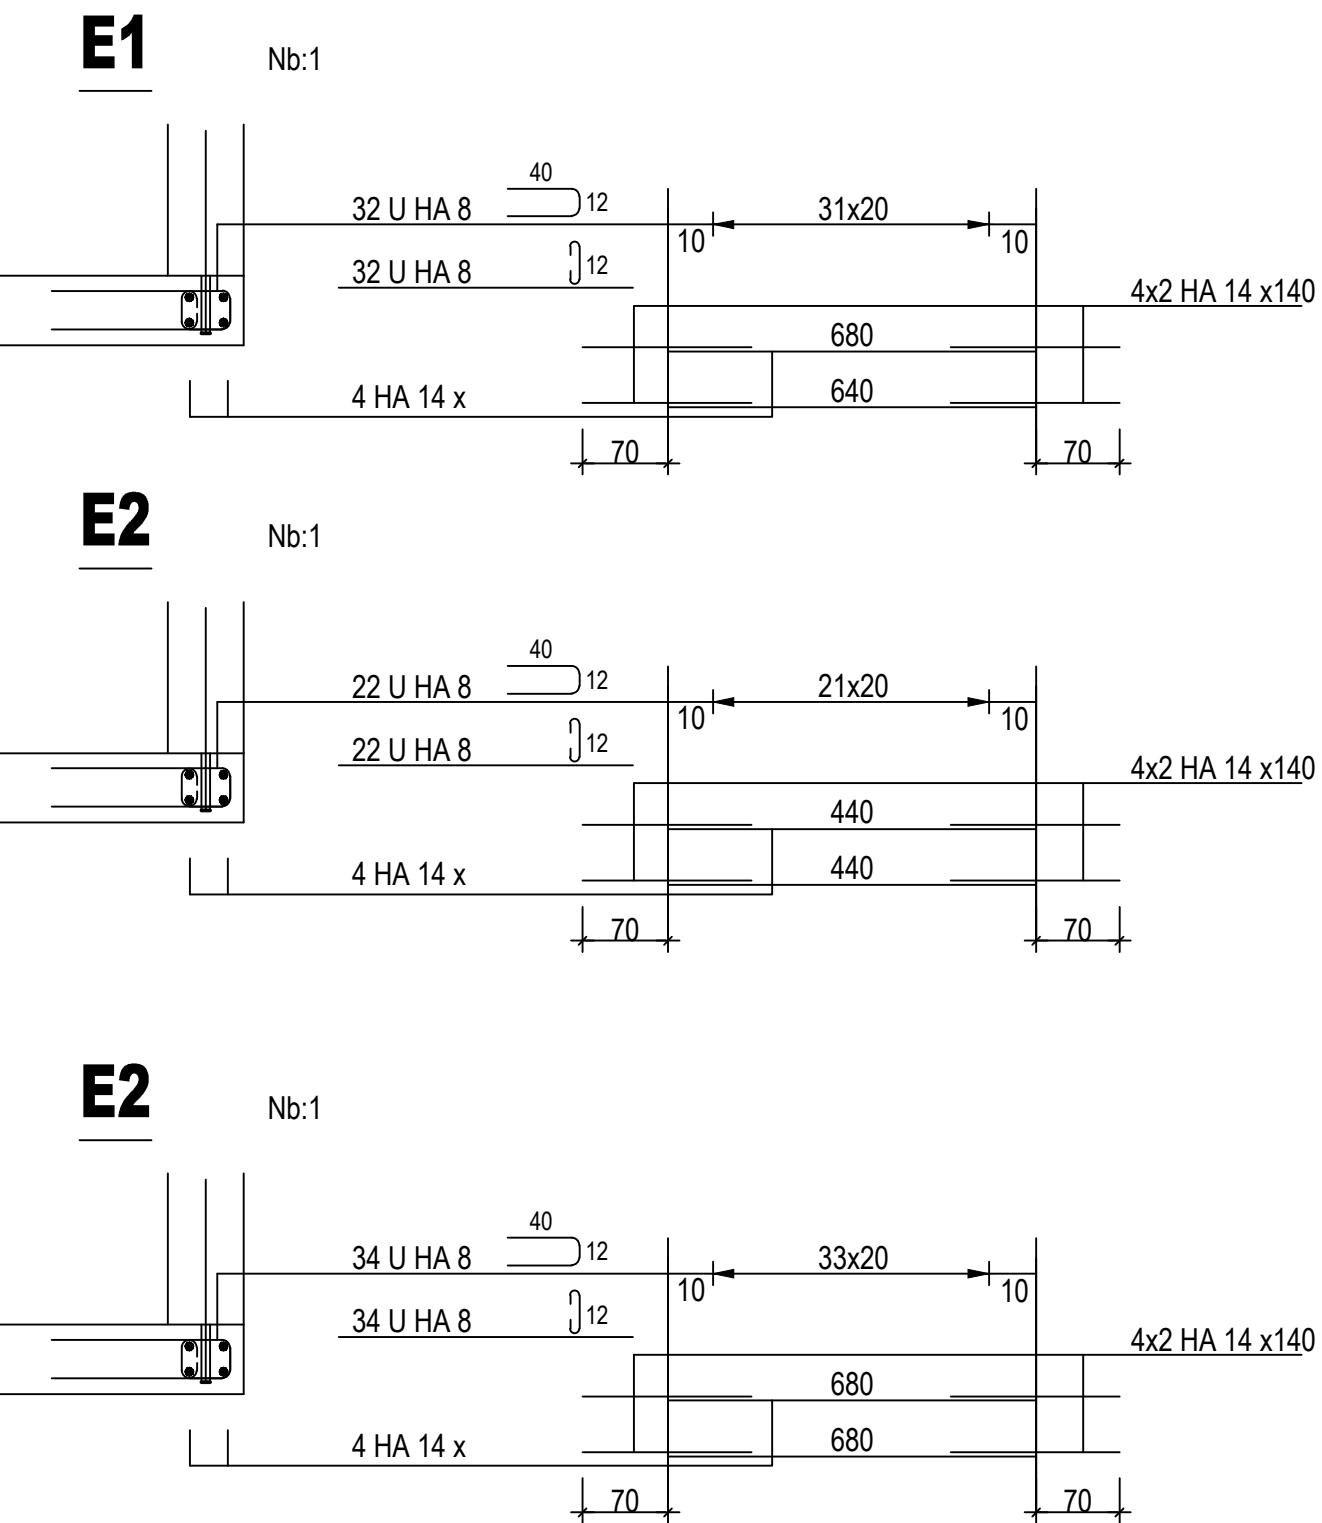
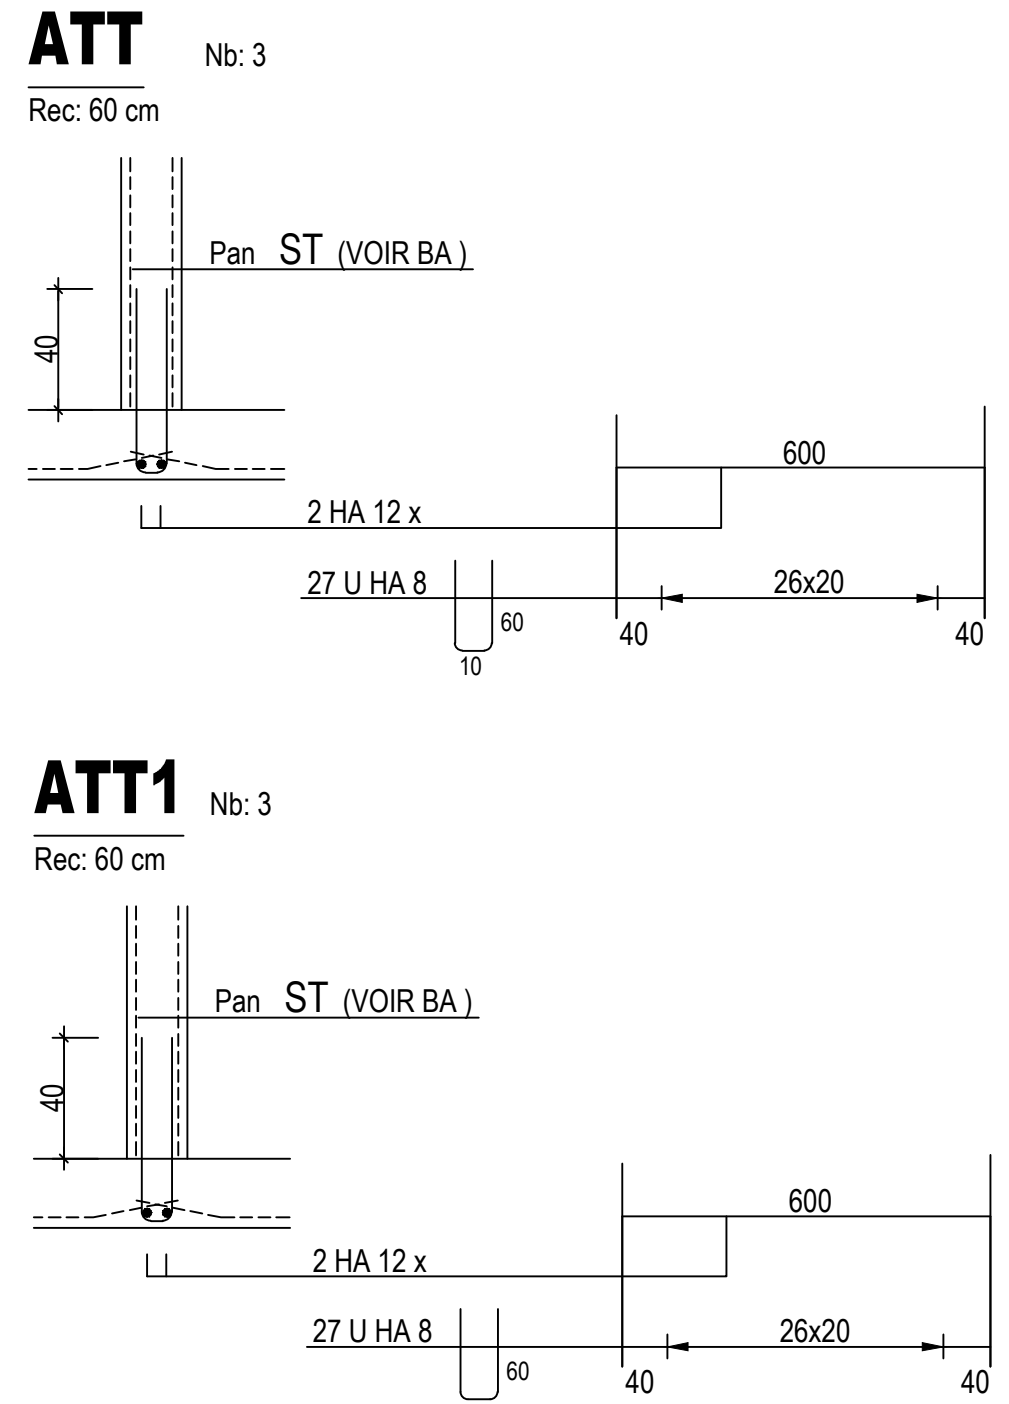


RELEVES

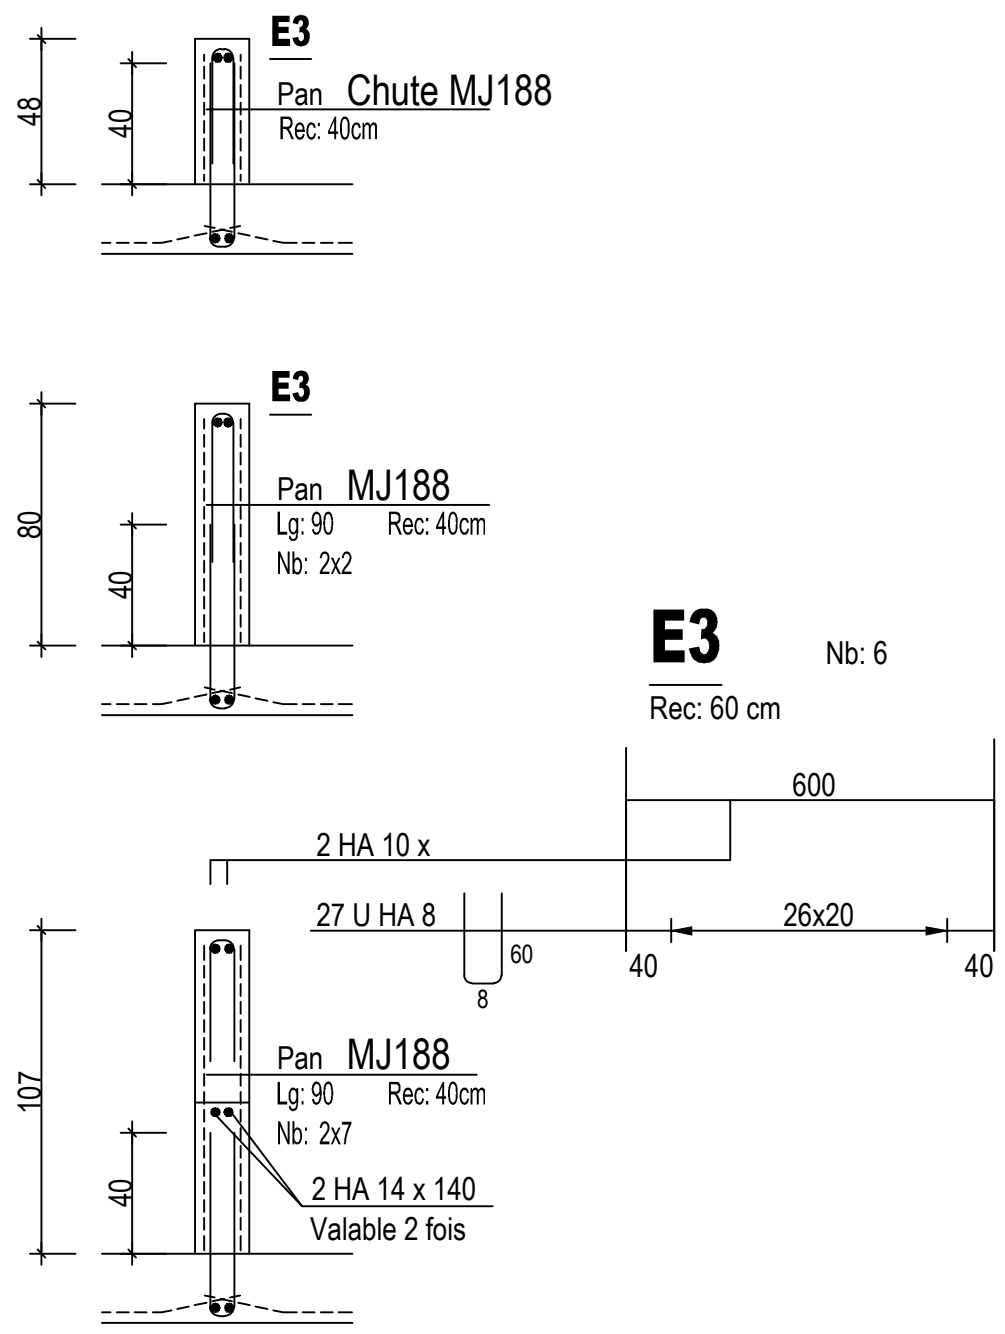



DETAIL D'ABOUTS DE CHAINAGES
INTERIEURS:

Position des équerres d'angles dans dalle 2 HA 14 x
x 100 a plat
vues en plan
chainage int. arrivant sur mur de façade chainage int. arrivant sur mur int.

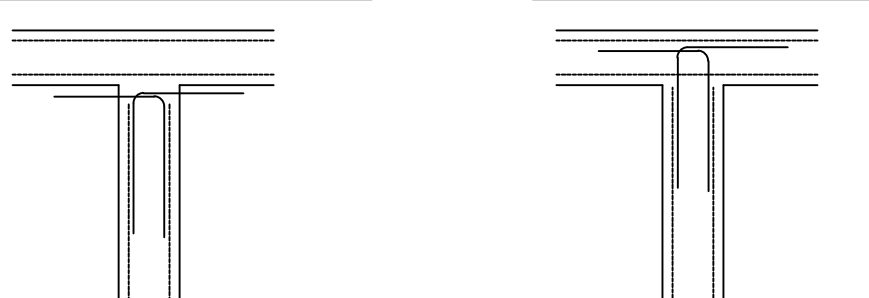

DETAIL D'ABOUTS DE CHAINAGES
EN ANGLE SUR FACADES:

Position des équerres d'angles dans dalle 2 HA 14
x 100 a plat
coupe vue en plan

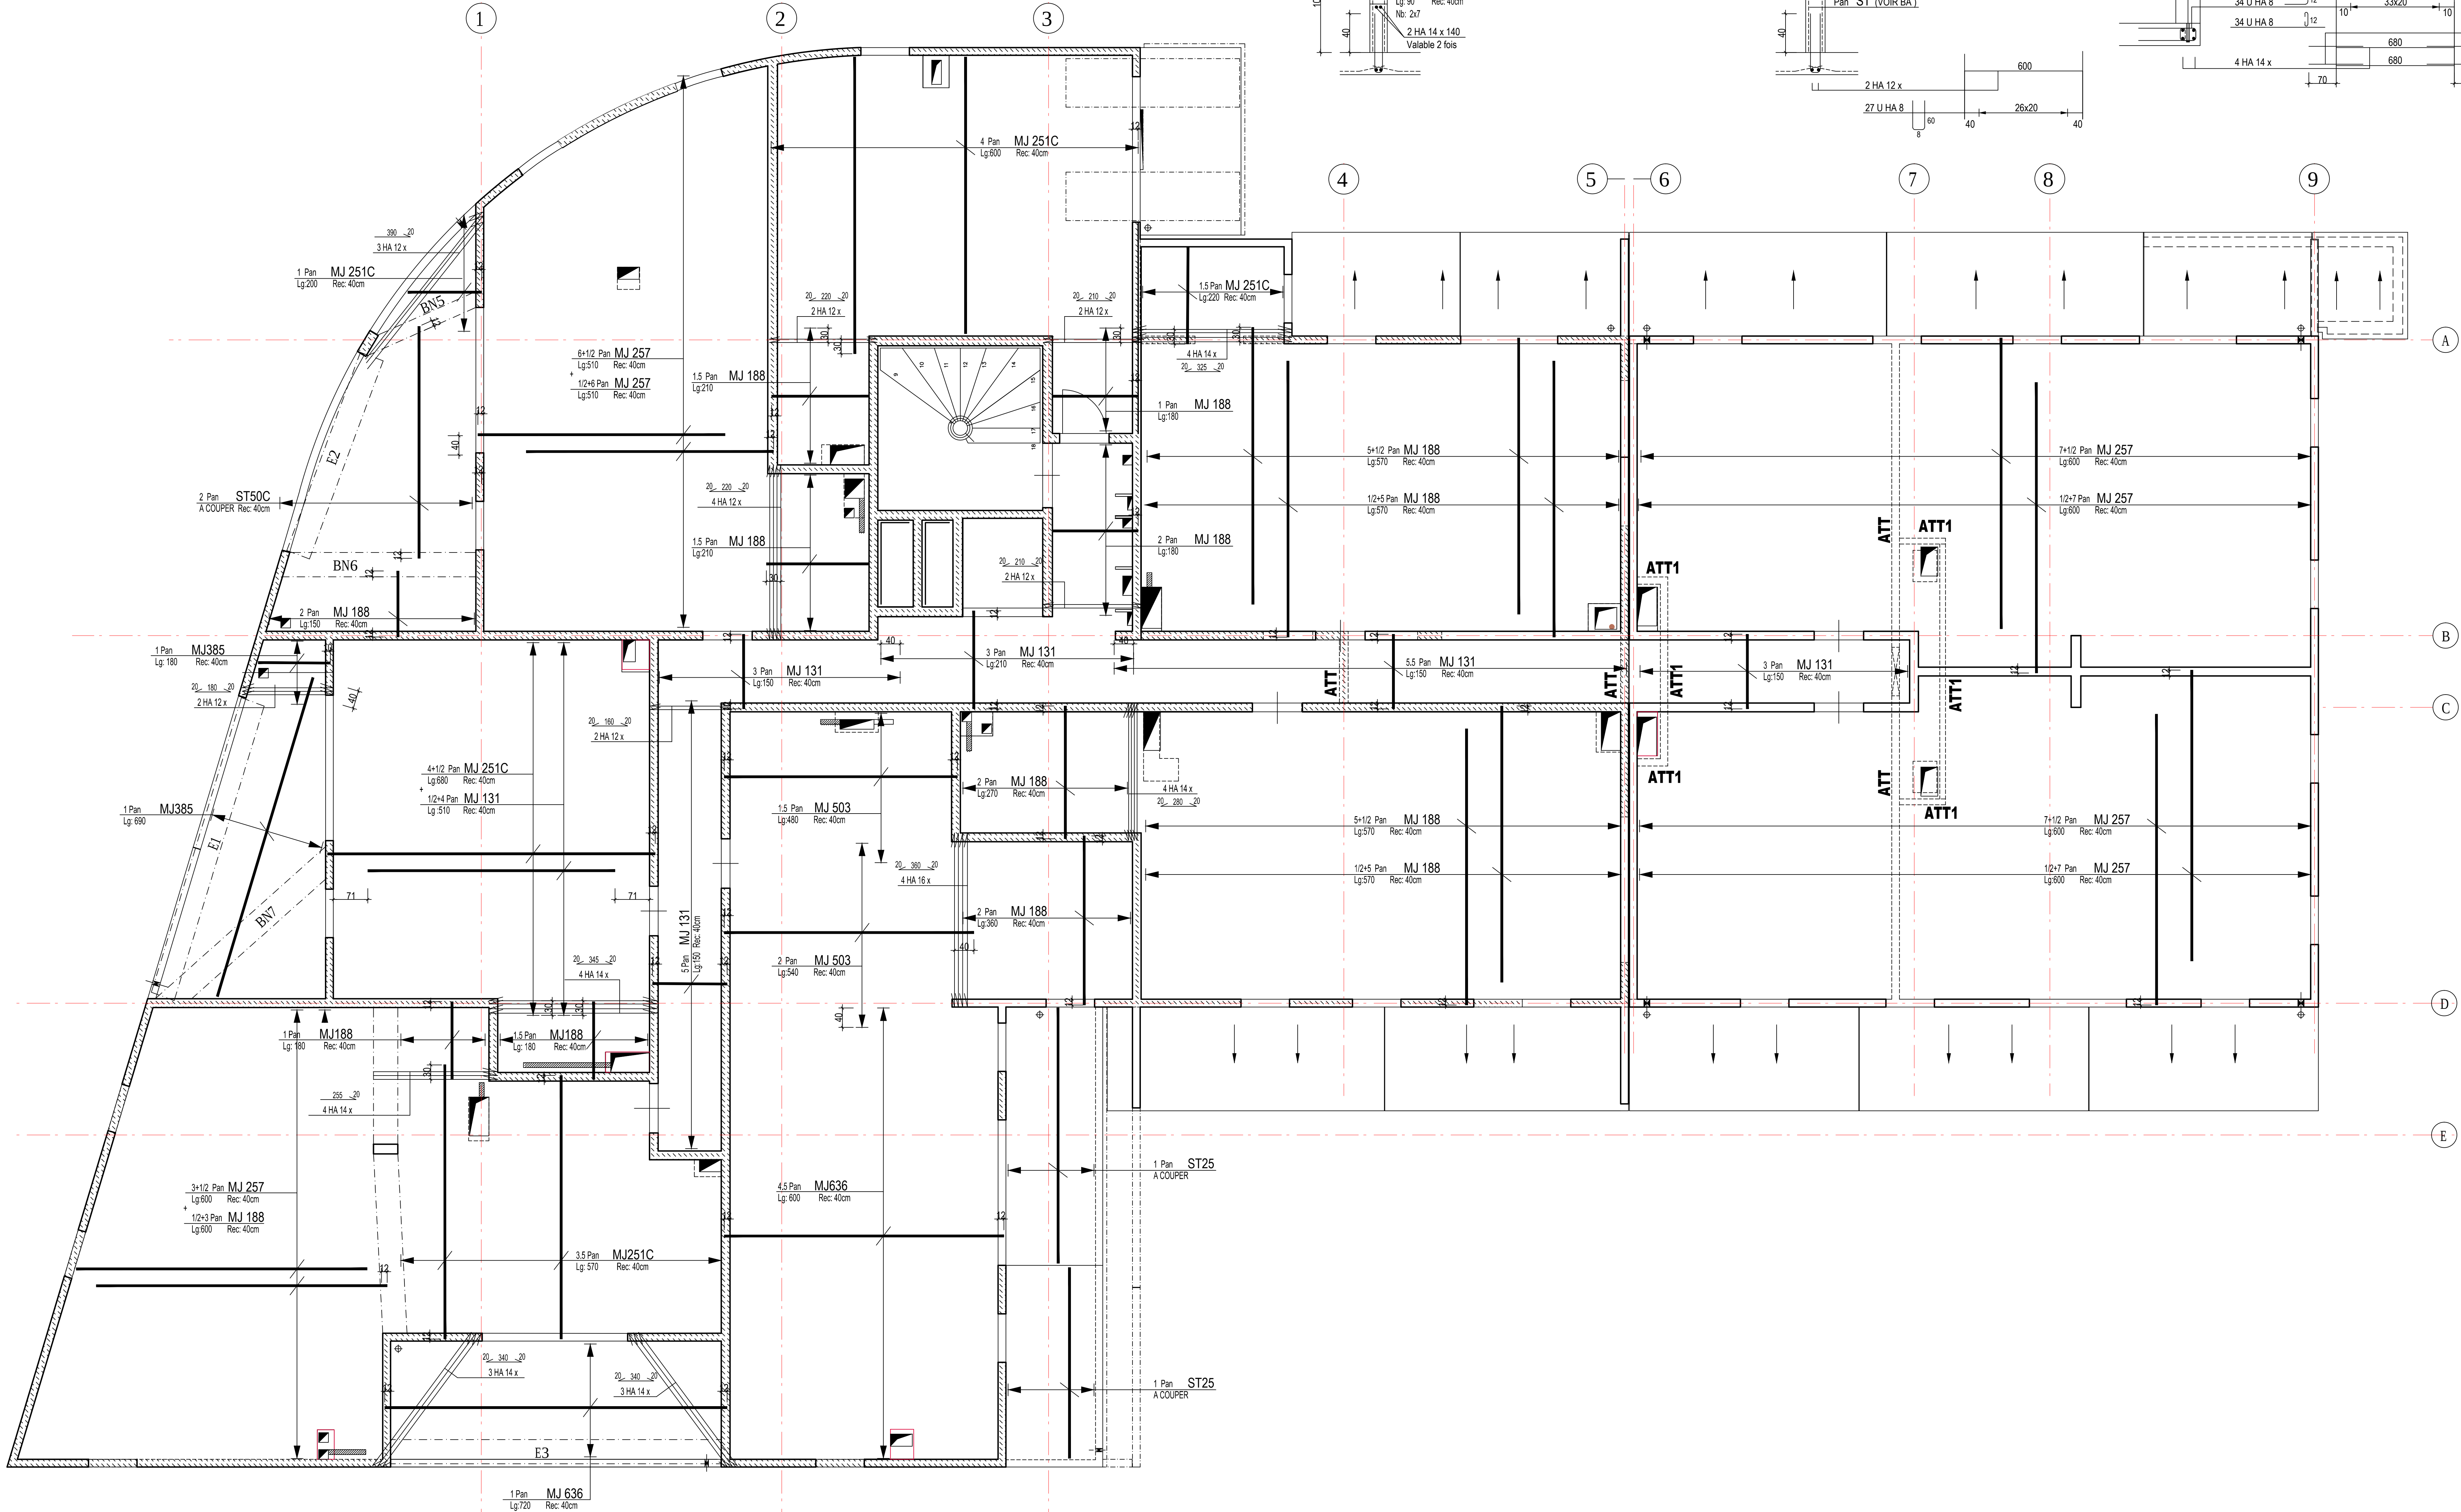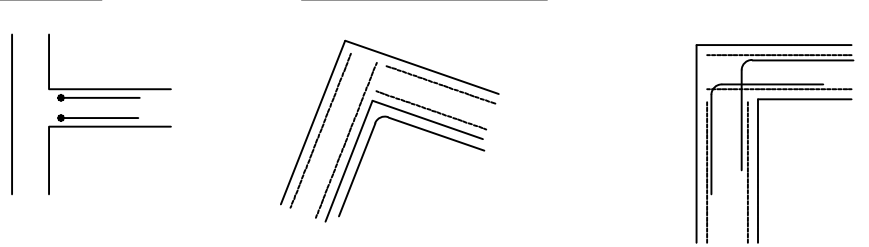

RECA. T.S.			
ST 25	600x240	2	
ST 50C	600x240	4	

RECA. T.S.		
MJ 131	150x240	17
	210x240	5
MJ 188	180x240	6
	210x240	6
	270x240	2
	360x240	2
	570x240	22
MJ 257	600x240	37
MJ 385	180x240	1
	690x240	1
MJ 503	480x240	2
	540x240	2
MJ 636	600x240	5
	720x240	1
MJ 251C	200x240	1
	220x240	2
	500x240	4
	570x240	4
	680x240	5

PANNEAUX EN TIROIRS PREVOIR RECouvreMENTS DECALES
EX: 1er Lit: 3 panneaux
2ème Lit: 1/2+2+1/2 panneaux EN TIROIR

NOAHO
LE 180°
Chemin de Fontanière - 69350 La Mulatière
Création de logements

Les entreprises réalisant les travaux devront tenir compte des derniers plans architecturaux lors de la réalisation des travaux.
Les plans du Bât A et B doivent servir de base pour la construction et doivent être des plans d'exécution.

ARCHITECTES:	ATELIER DE LA PASSERELLE	MO DELEGUE:	PSO Ingénierie
BET STRUCTURE:	MATTE SAS	MOE:	SUD EST COORDINATION
BET FLUIDES:	PRELEM	CSPS:	
ECONOMISTE:	EXECO	CPC:	
BUREAU DE CONTROLE:	Bureau VERITAS	ENTREPRISES:	Fontanel

Bât A
PLANCHER SUR 1er
ARMATURES DALLE INFÉRIEURES

INDICE	DATE	MODIFICATIONS

MATTE
BUREAU D'ETUDES
STRUCTURES ET FLUIDES
119 BOULEVARD STALINGRAD 69100 VILLEURBANNE
Tel: 04 72 44 02 87 Fax: 04 72 44 26 59
Email: info@matte.fr

DOE
Contrainte de sol: 8 bars ELS
Aciers HA (T) FeE500
Aciers Doux (D) FeE235
Aciers TS FeE500
Béton f28 >= 25MPa
Enrobage = 3 cm

PLAN N°
A48 0
DATE: 10/03/2016

Affaire N°
13.12.118