


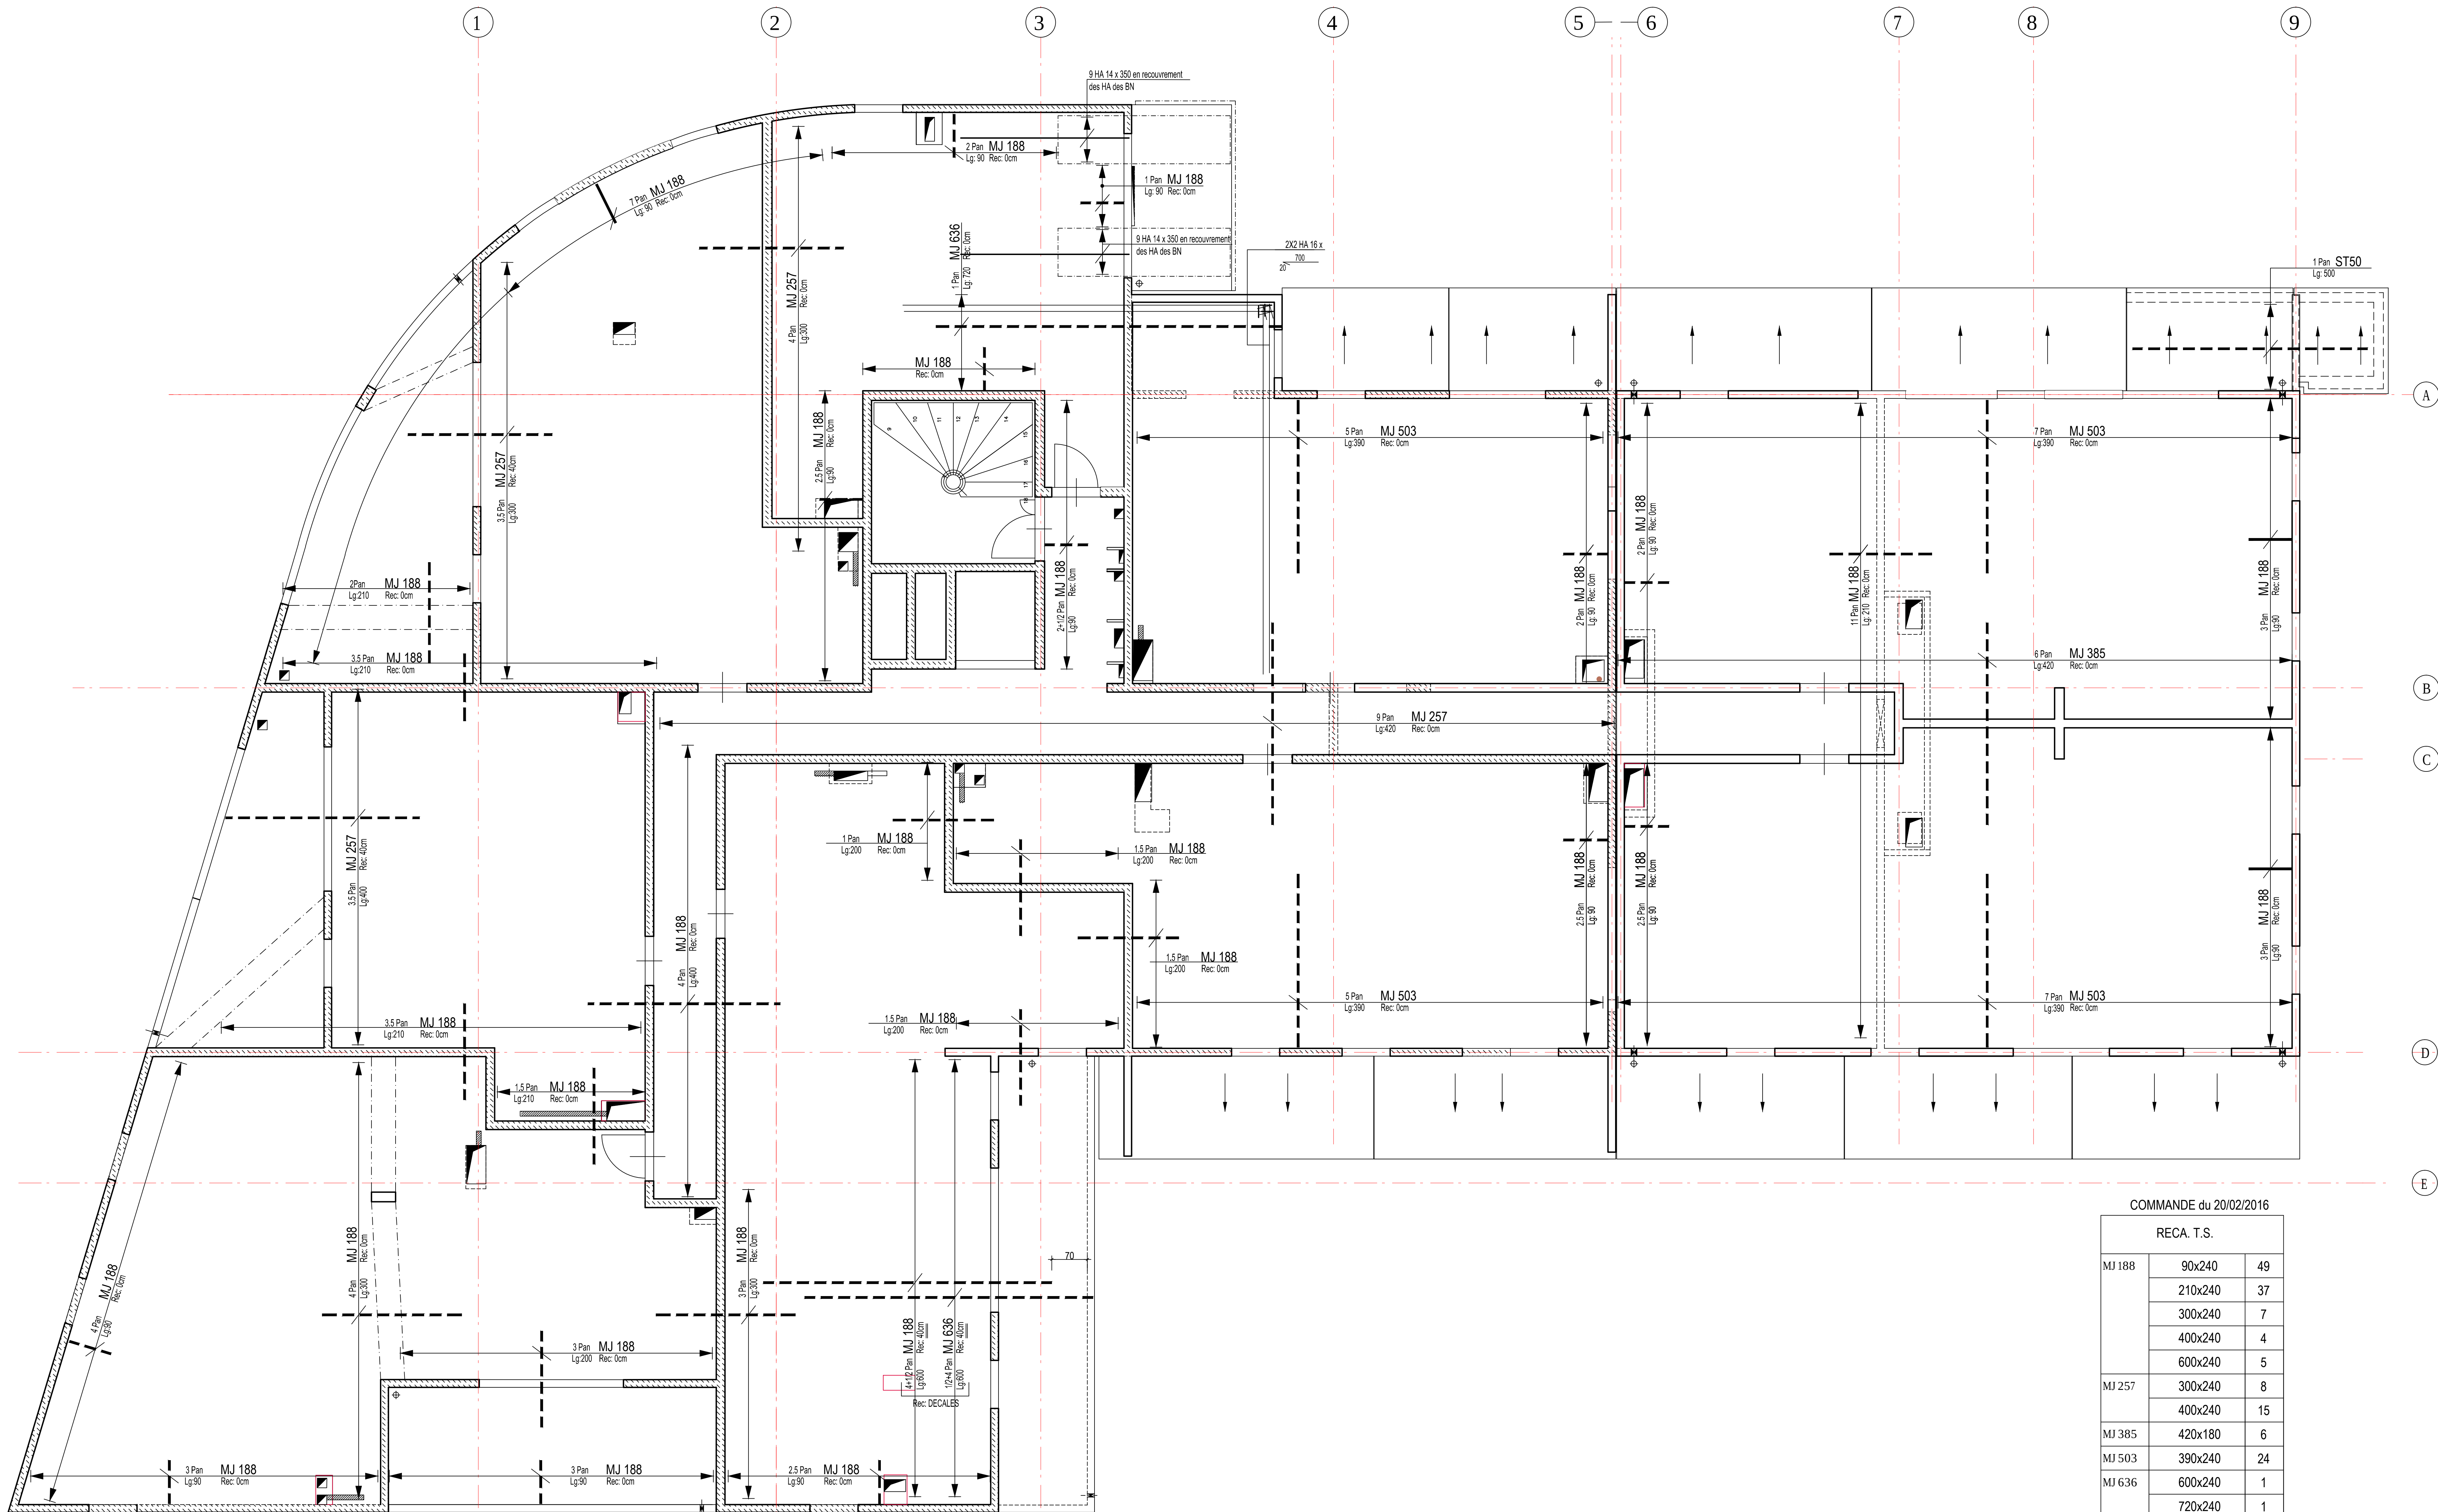

DETAIL D'ABOUTS DE CHAINAGES

INTERIEURS:

Position des équerres d'angles dans dalle 2 HA 14 x 100
à plat
vues en plan

chainage int. arrivant sur mur de façade chainage int. arrivant sur mur int.




DETAIL D'ABOUTS DE CHAINAGES


EN ANGLE SUR FACADES:

Position des équerres d'angles dans dalle 2 HA 14 x 100
à plat

coupe vue en plan

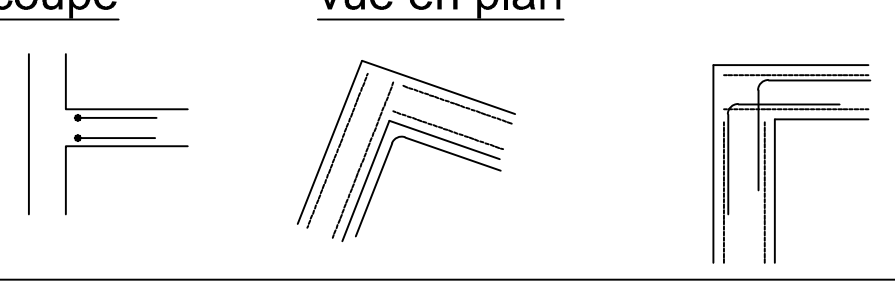


Principe de renfort aux droits des gaines:

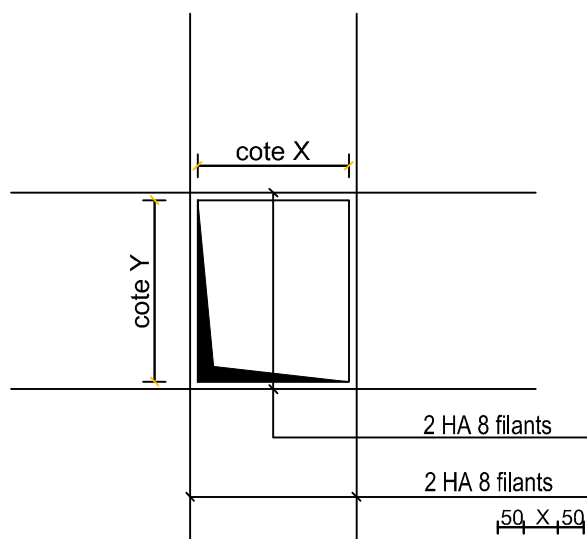

NAPPE INFÉRIEURE ET SUPÉRIEURE

NOTA: Ces renforts sont en complément des autres mis sur la vue en plan

RENFORTS RESESERVATIONS
JUSQU'A Ø200 mm

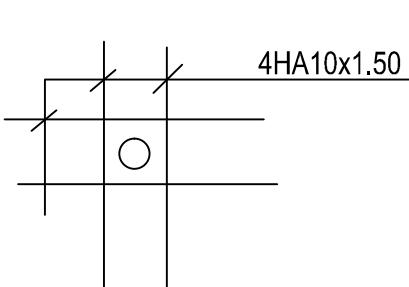

NOAHO

LE 180°

Chemin de Fontanière - 69350 La Mulatière

Création de logements

Les entreprises réalisant les travaux devront tenir compte des derniers plans architectes lors de la réalisation des travaux.
Les plans du Bât MATTÉ ne doivent servir qu'au corps d'état concerné et doivent être des plans d'exécution.

ARCHITECTES: ATELIER DE LA PASSERELLE
SET STRUCTURE: MATTÉ SAS
SET FLUIDES: PRELEM
ECONOMISTE: EXECO
BUREAU DE CONTRÔLE: Bureau VERITAS

MO DELEGUE: PSD Ingénierie
NOE: CSFR
OPC: Fontanel
ENTREPRISES: Fontanel

BâtA
PLANCHER SUR 1er
ARMATURES DALLE SUPERIEURES

INDICE	DATE	MODIFICATIONS

MATTÉ
BUREAU D'ETUDES
STRUCTURES ET FLUIDES
119 BOULEVARD STRANDBERG VILLEURBANNE
Tél: 04 72 44 32 87 Fax 04 72 44 36 59
E-mail: bat@matté.fr

Dessiné par: J.B.O.
Contrôlé par: P.LIN
Echelle: 1/50'

DOE

Commande de sol: 8 bars ELS

Acière HA (T) FeE500

Acière Dux (D) FeE235

Acière TS FeE 500

Béton C28 > 25MPa

Enrobage: e = 3 cm

PLAN N°
A49 0

DATE: 10/03/2016

Affaire N°
13.12.118

COMMANDE du 20/02/2016

RECA. T.S.		
MJ 188	90x240	49
	210x240	37
	300x240	7
	400x240	4
	600x240	5
MJ 257	300x240	8
	400x240	15
MJ 385	420x180	6
MJ 503	390x240	24
MJ 636	600x240	1
	720x240	1

ST 50	600x240	1
-------	---------	---