

 


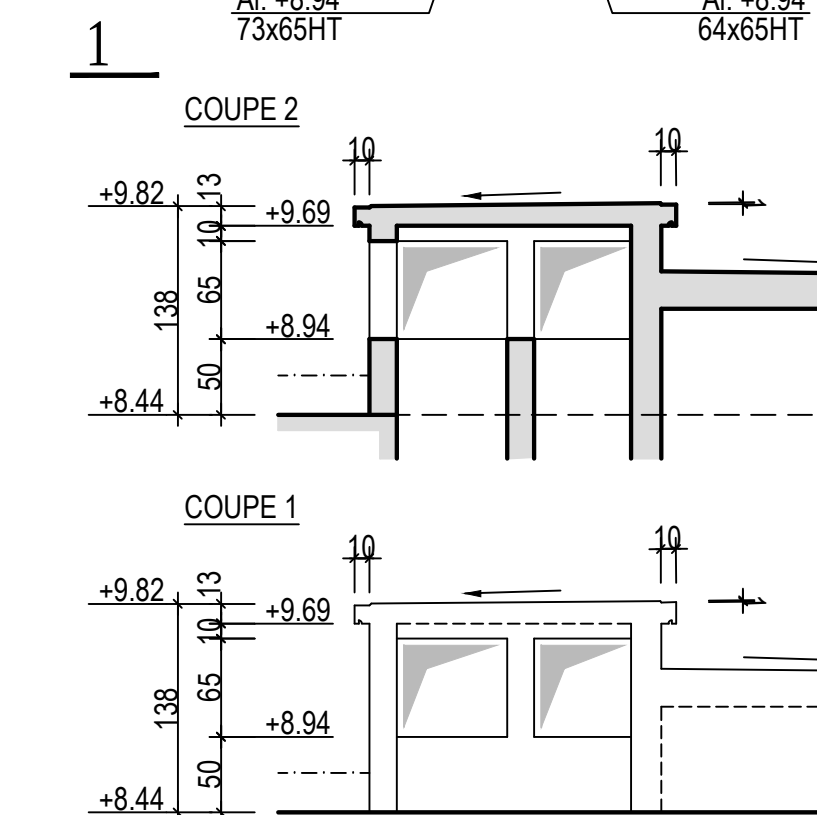

DETAIL "1" VENTILATIONS

Ech: 1/50

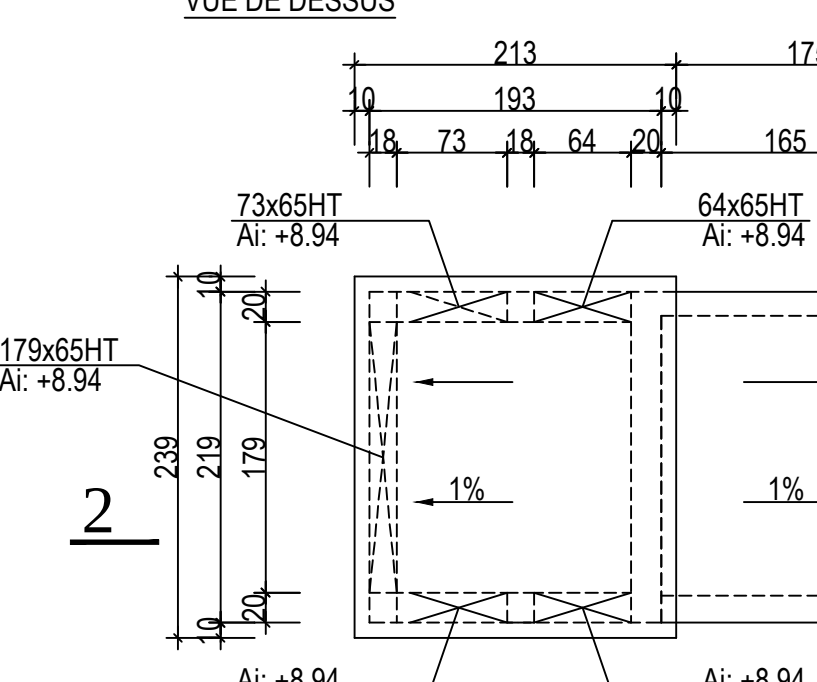

DALLE

- FINI: +8.70-229.20
- DALLE BA Epr: 20 cm
- DESSUS BRUT: +8.44
- RESERVE: 26 cm

±0.00 = 220.50

NOAHO

LE 180°

Chemin de Fontanière - 69350 La Mulatière

Création de logements

Les entreprises dessinant les plans doivent leur copier des formes plans et les faire lire de la notation des plans

Les plans du lot MATTE ne doivent servir qu'à des fins de consultation et ne doivent pas être utilisés

ARCHITECTES: BUREAU DE CONCEPTION

ATELIER DE LA PASSERELLE

RET STRUCTURE: MATTE SAS

RET FLUIDES: PRELEM

RECONSTRUCTION: CPIC

BUREAU DE CONCEPTION: Bureau VERITAS

MO DELEVUE: MOE

PSD Ingénierie

SUD EST COORDINATION

ENTREPRISE: Fontanel

BâtA

PLANCHER SUR 2ème

Coffrage

DOE

Contrainte de sol: 8 bars EL5

INDEXE

DATE

MODIFICATIONS

A

14/03/2016

MISE A JOUR DETAIL 7

B

15/03/2016

MISE A JOUR OUVERTURE FACADE NORD

C

26/03/2016

AJOUTER RESERVATIONS FILE S

D

14/04/2016

MISE A JOUR DETAIL "1" COUPES SUR VENTILATIONS

MATTE

BUREAU D'ETUDES

STRUCTURES ET FLUIDES

188 MOULOUERIE ETAL NOAHO 69350 VILLEURBANNE

Tel: 04 72 44 12 37 Fax: 04 72 44 20 00

E-mail: info@matte.fr

Dessiné par: J.BG

Contrôlé par: J.P.LN

Echelle: 1/500

PLAN N°

A50 D

DATE: 11/03/2016

Affaire N°

13.12.118