



RENFORTS RESESERVATIONS
JUSQU'A Ø200 mm

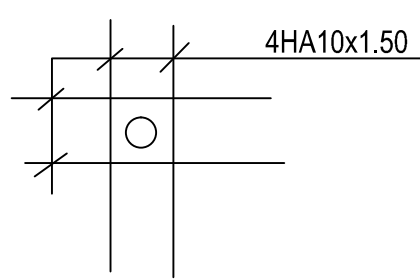


Principe de renfort aux droits des gaines:

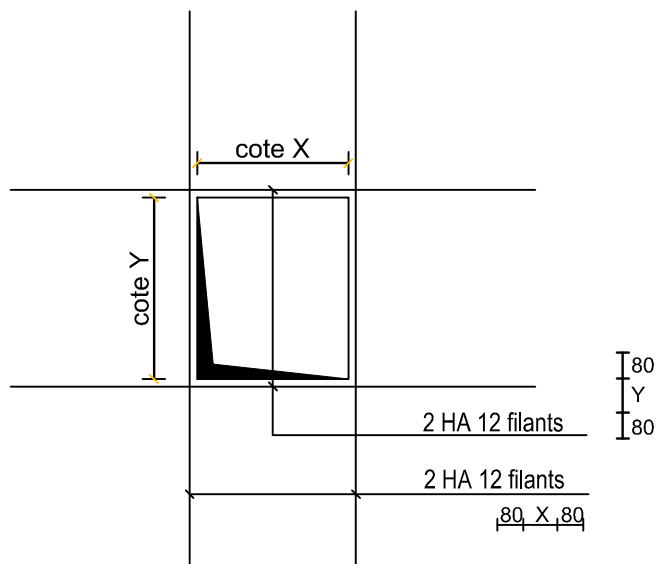

NAPPE INFERIEURE ET SUPERIEURE
NOTA: Ces renforts sont en complément des aciers mis sur la vue en plan




DETAIL D'ABOUTS DE CHAINAGES
INTERIEURS:

Position des équerres d'angles dans dalle 2 HA 14 x 100
à plat
vues en plan
chainage int. arrivant sur mur de façade chainage int. arrivant sur mur int.

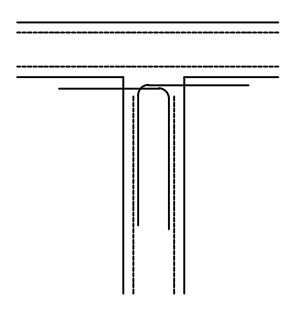

DETAIL D'ABOUTS DE CHAINAGES
EN ANGLE SUR FACADES:

Position des équerres d'angles dans dalle 2 HA 14 x 100
à plat
coupe vue en plan

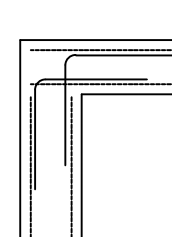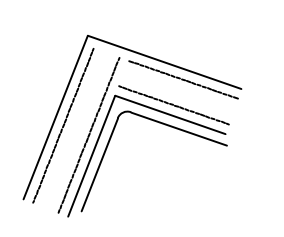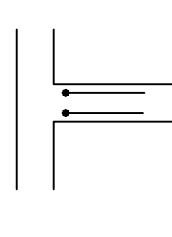

RECA. T.S.		
ST 40C	600x240	1

RECA. T.S.		
MJ 131	120x240	1
	150x240	15
	210x240	3
	510x240	5
MJ 188	180x240	6
	210x240	3
	270x240	2
	570x240	22
	600x240	4
	510x240	13
MJ 257	600x240	4
	540x240	2
MJ 503	480x240	2
	600x240	5
MJ 636	240x240	1
	360x240	2
	570x240	4
	600x240	4
	680x240	5

PANNEAUX EN TIROIRS PREVOIR RECOUVREMENTS DECALES
EX: Tier Lit. 3 panneaux
2ème Lit. 1/2x2+1/2 panneaux] EN TIROIR

±0.00 = 220.50

NOAHO

LE 180°

Chemin de Fontanière - 69350 La Mulatière

Création de logements

Les entreprises réalisant les travaux devront tenir compte des derniers plans architectes lors de la réalisation des travaux
Les plans du bt MATTE ne doivent servir qu'au corps d'état concerné et doivent être des plans d'exécution

ARCHITECTES: ATELIER DE LA PASSERELLE
SET STRUCTURE: MATTE SAS
BET FLUIDES: PRELEM
ECONOMISTE: EXECO
BUREAU DE CONTROLE: Bureau VERITAS
MO DELEGUE: PSO Ingénierie
MSE: CSPS
SUD EST COORDINATION
OPC:
ENTREPREISES: Fontanel

BâtA
PLANCHER SUR 2ème
ARMATURES DALLE INFERIEURES

INDICE	DATE	MODIFICATIONS

MATTÉ

BUREAU D'ETUDES
STRUCTURES ET FLUIDES

119 BOULEVARD STALINGRAD 69100 VILLEURBANNE
Tél. 04 72 44 12 87 Fax 04 72 44 26 59
E-mail: mat@matte.fr

Dessiné par: J. BO
Contrôlé par: P. LUN
Echelle: 1/150°

DOE

Contrainte de sol: 8 bars ELS

Aciers HA (T) FdE500

Aciers Dux (O) FdE 235

Aciers TS FdE 500

Béton f28 >= 25MPa

Enrobage = 3 cm

PLAN N°
A52 0

DATE: 14/03/2016

Affaire N°
13.12.118