



RENFORTS RESESERVATIONS
JUSQU'A Ø200 mm

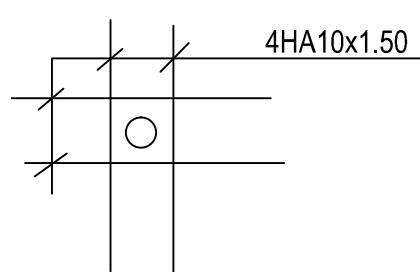

Principe de renfort aux droits des gaines:

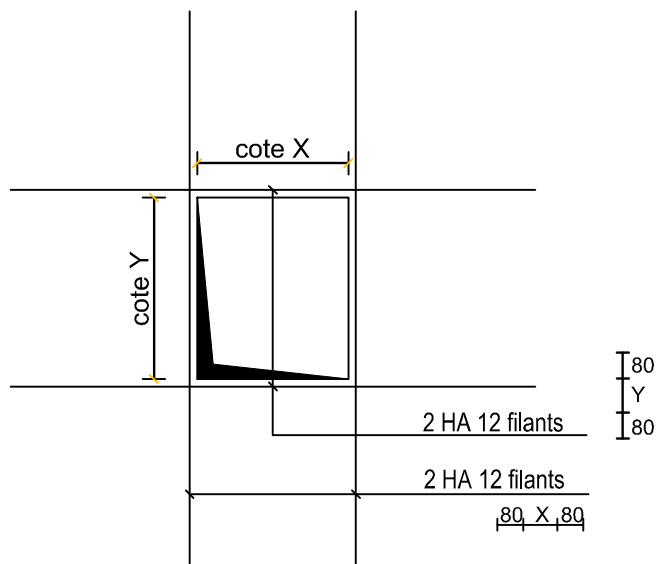

NOTA: Ces renforts sont en complément des aciers mis sur la vue en plan

DETAIL D'ABOUTS DE CHAINAGES

INTERIEURS:


Position des équerres d'angles dans dalle 2 HA 14 x 100
à plat
vues en plan
chainage int. arrivant sur mur de façade chainage int. arrivant sur mur int.



DETAIL D'ABOUTS DE CHAINAGES


EN ANGLE SUR FACADES:

Position des équerres d'angles dans dalle 2 HA 14 x 100
à plat
coupe vue en plan

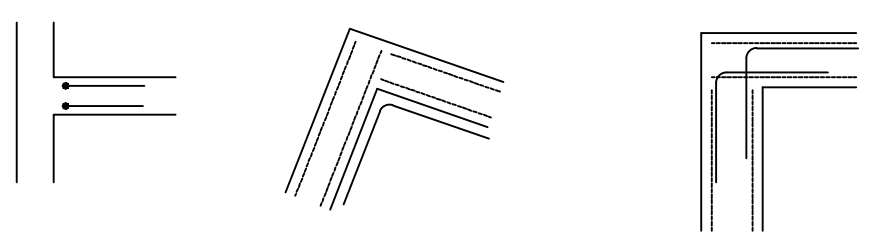

RECA. T.S.		
ST 40C	600x240	1

RECA. T.S.		
MJ 188	90x240	55
	180x240	8
	200x240	1
	270x240	16
	400x240	4
MJ 257	300x240	5
	400x240	9

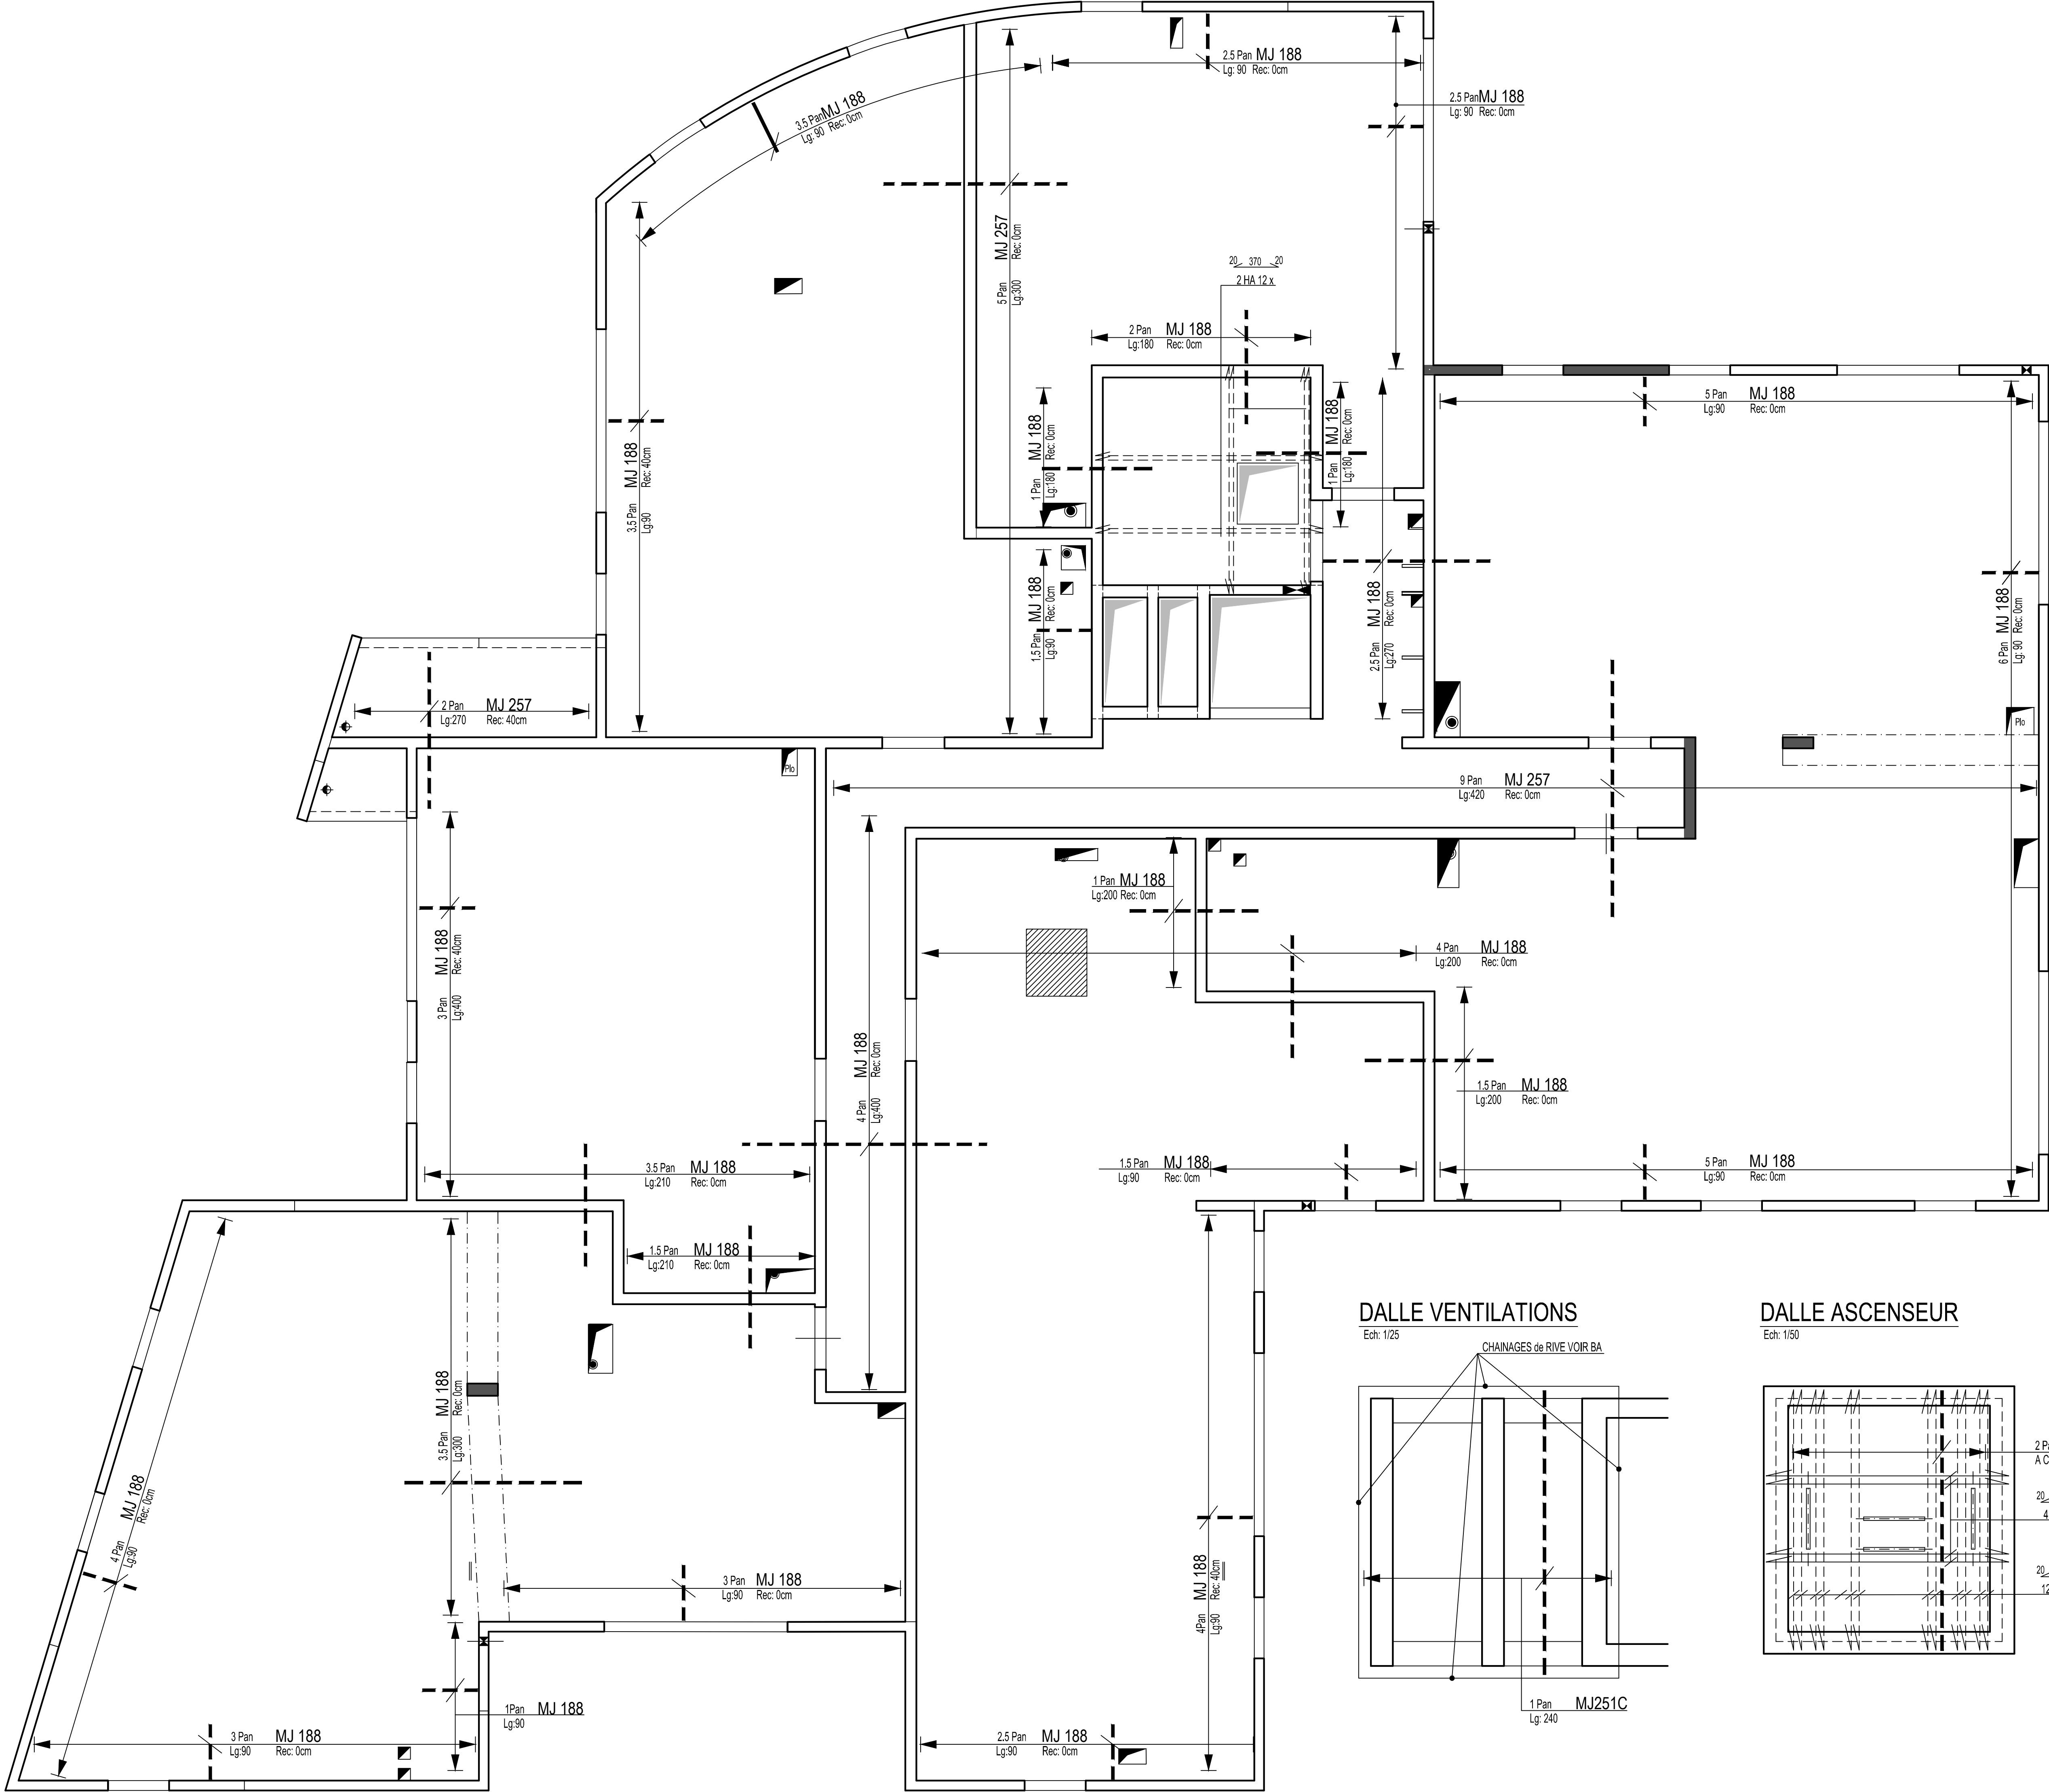

±0.00 = 220.50

NOAHO
LE 180°
Chemin de Fontanière - 69350 La Mulatière
Création de logements

Les entreprises réalisant les travaux devront tenir compte des derniers plans architectes lors de la réalisation des travaux Les plans du bt MATTE ne doivent servir qu'au corps d'état concerné et doivent être des plans d'exécution.		
ARCHITECTES:	ATELIER DE LA PASSERELLE	MO DELEGUE:
SET STRUCTURE:	MATTE SAS	MEC:
BET FLUIDES:	PRELEM	CSPS:
ECONOMISTE:	EXECO	OPC:
BUREAU DE CONTROLE:	Bureau VERITAS	ENTREPRISES:

Bât A
PLANCHER SUR 2ème
ARMATURES DALLE SUPERIEURES

DOE

Contrainte de sol 8 bars ELS
Aciers HA (T) FeE500
Aciers Doux (D) FeE235
Aciers TS FeE500
Béton C20/25 B50/60
Enrobage = 3 cm

INDICE	DATE	MODIFICATIONS


MATTE
BUREAU D'ETUDES
STRUCTURES ET FLUIDES
119 RUE LEONARD ETLINGHARDT 69100 VILLEURBANNE
Tél. 04 72 44 12 87 Fax 04 72 44 26 59
E-mail: mat@matte.fr

Dessiné par : J. BO
Contrôle par : P. LUN
Echelle : 1/150°

PLAN N°
A53 0
DATE : 14/03/2016
Affaire N°
13.12.118

DALLE VENTILATIONS

Ech: 1/25

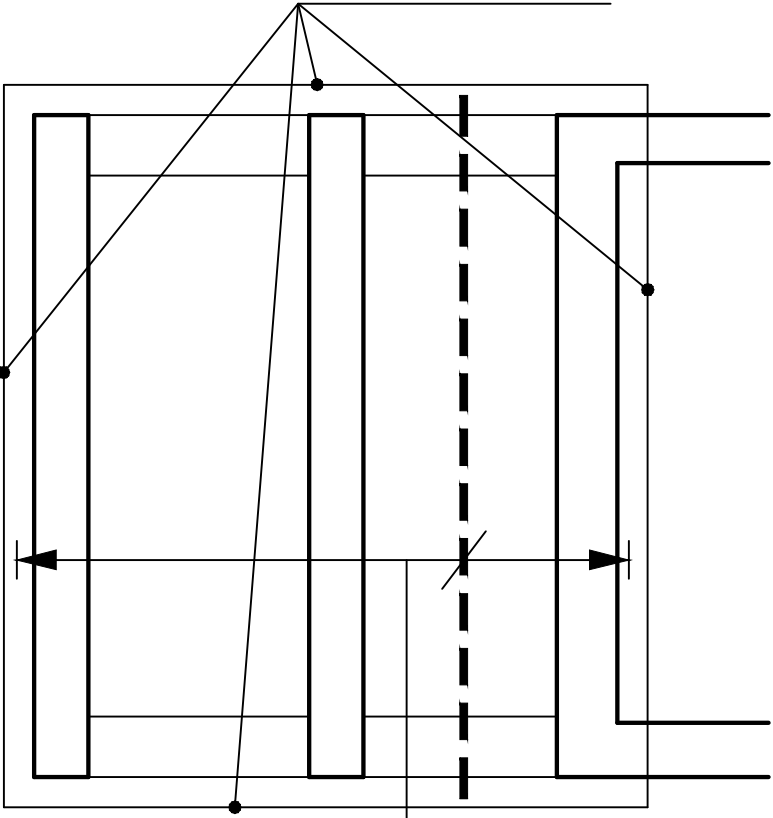

DALLE ASCENSEUR

Ech: 1/50

