

NOAHO

rmatures

Chemin de Fontanière - 69350 La Mulatière

Création de logements

Les entreprises réalisant les travaux devront tenir compte des derniers plans architecte lors de la réalisation des travaux
Les plans du be MATTE ne doivent servir qu'au corps d'état concerné et doivent être des plans d'exécution.

ARCHITECTE(S): ATELIER DE LA PASSERELLE MO DELEGUE:
BET STRUCTURE: MATTE SAS MOE: PSO Ingénierie
BET FLUIDES: PRELEM CSPS: SUD EST COORDINATION
ECONOMISTE: EXECO OPC:
BUREAU DE CONTROLE: Bureau VERITAS ENTREPRISE(S): Fontanel

Bât:A Files 1 et 5,6

ESCALIERS EXTERIEURS FACADE SUD

Coffrage Armatures

INDICE	DATE	MODIFICATIONS

MATTÉ
BUREAU D'ÉTUDES
STRUCTURES ET FLUIDES

119 BOULEVARD STALINGRAD 69100 VILLEURBANNE
Tél. 04 72 44 02 87 Fax 04 72 44 26 59
E-mail : bet@matte.fr

Dessiné par : J.BO
Contrôlé par : P.LIN
Echelle : 1/50°

DOE

Contrainte de sol: bars ELS

Aciers HA (T) FeE500
Aciers Doux (Ø) FeE 235
Aciers TS FeE 500
Béton fc28 >= 25MPa
Enrobage = 3 cm

PLAN N°
A54 0


DATE : 07/06/2016

Affaire N°
13.12.118

ESCALIER FILES 5,6 et 7 FACADE SUD

VUE EN PLAN VOLEES PREFE


Ech: 1/25

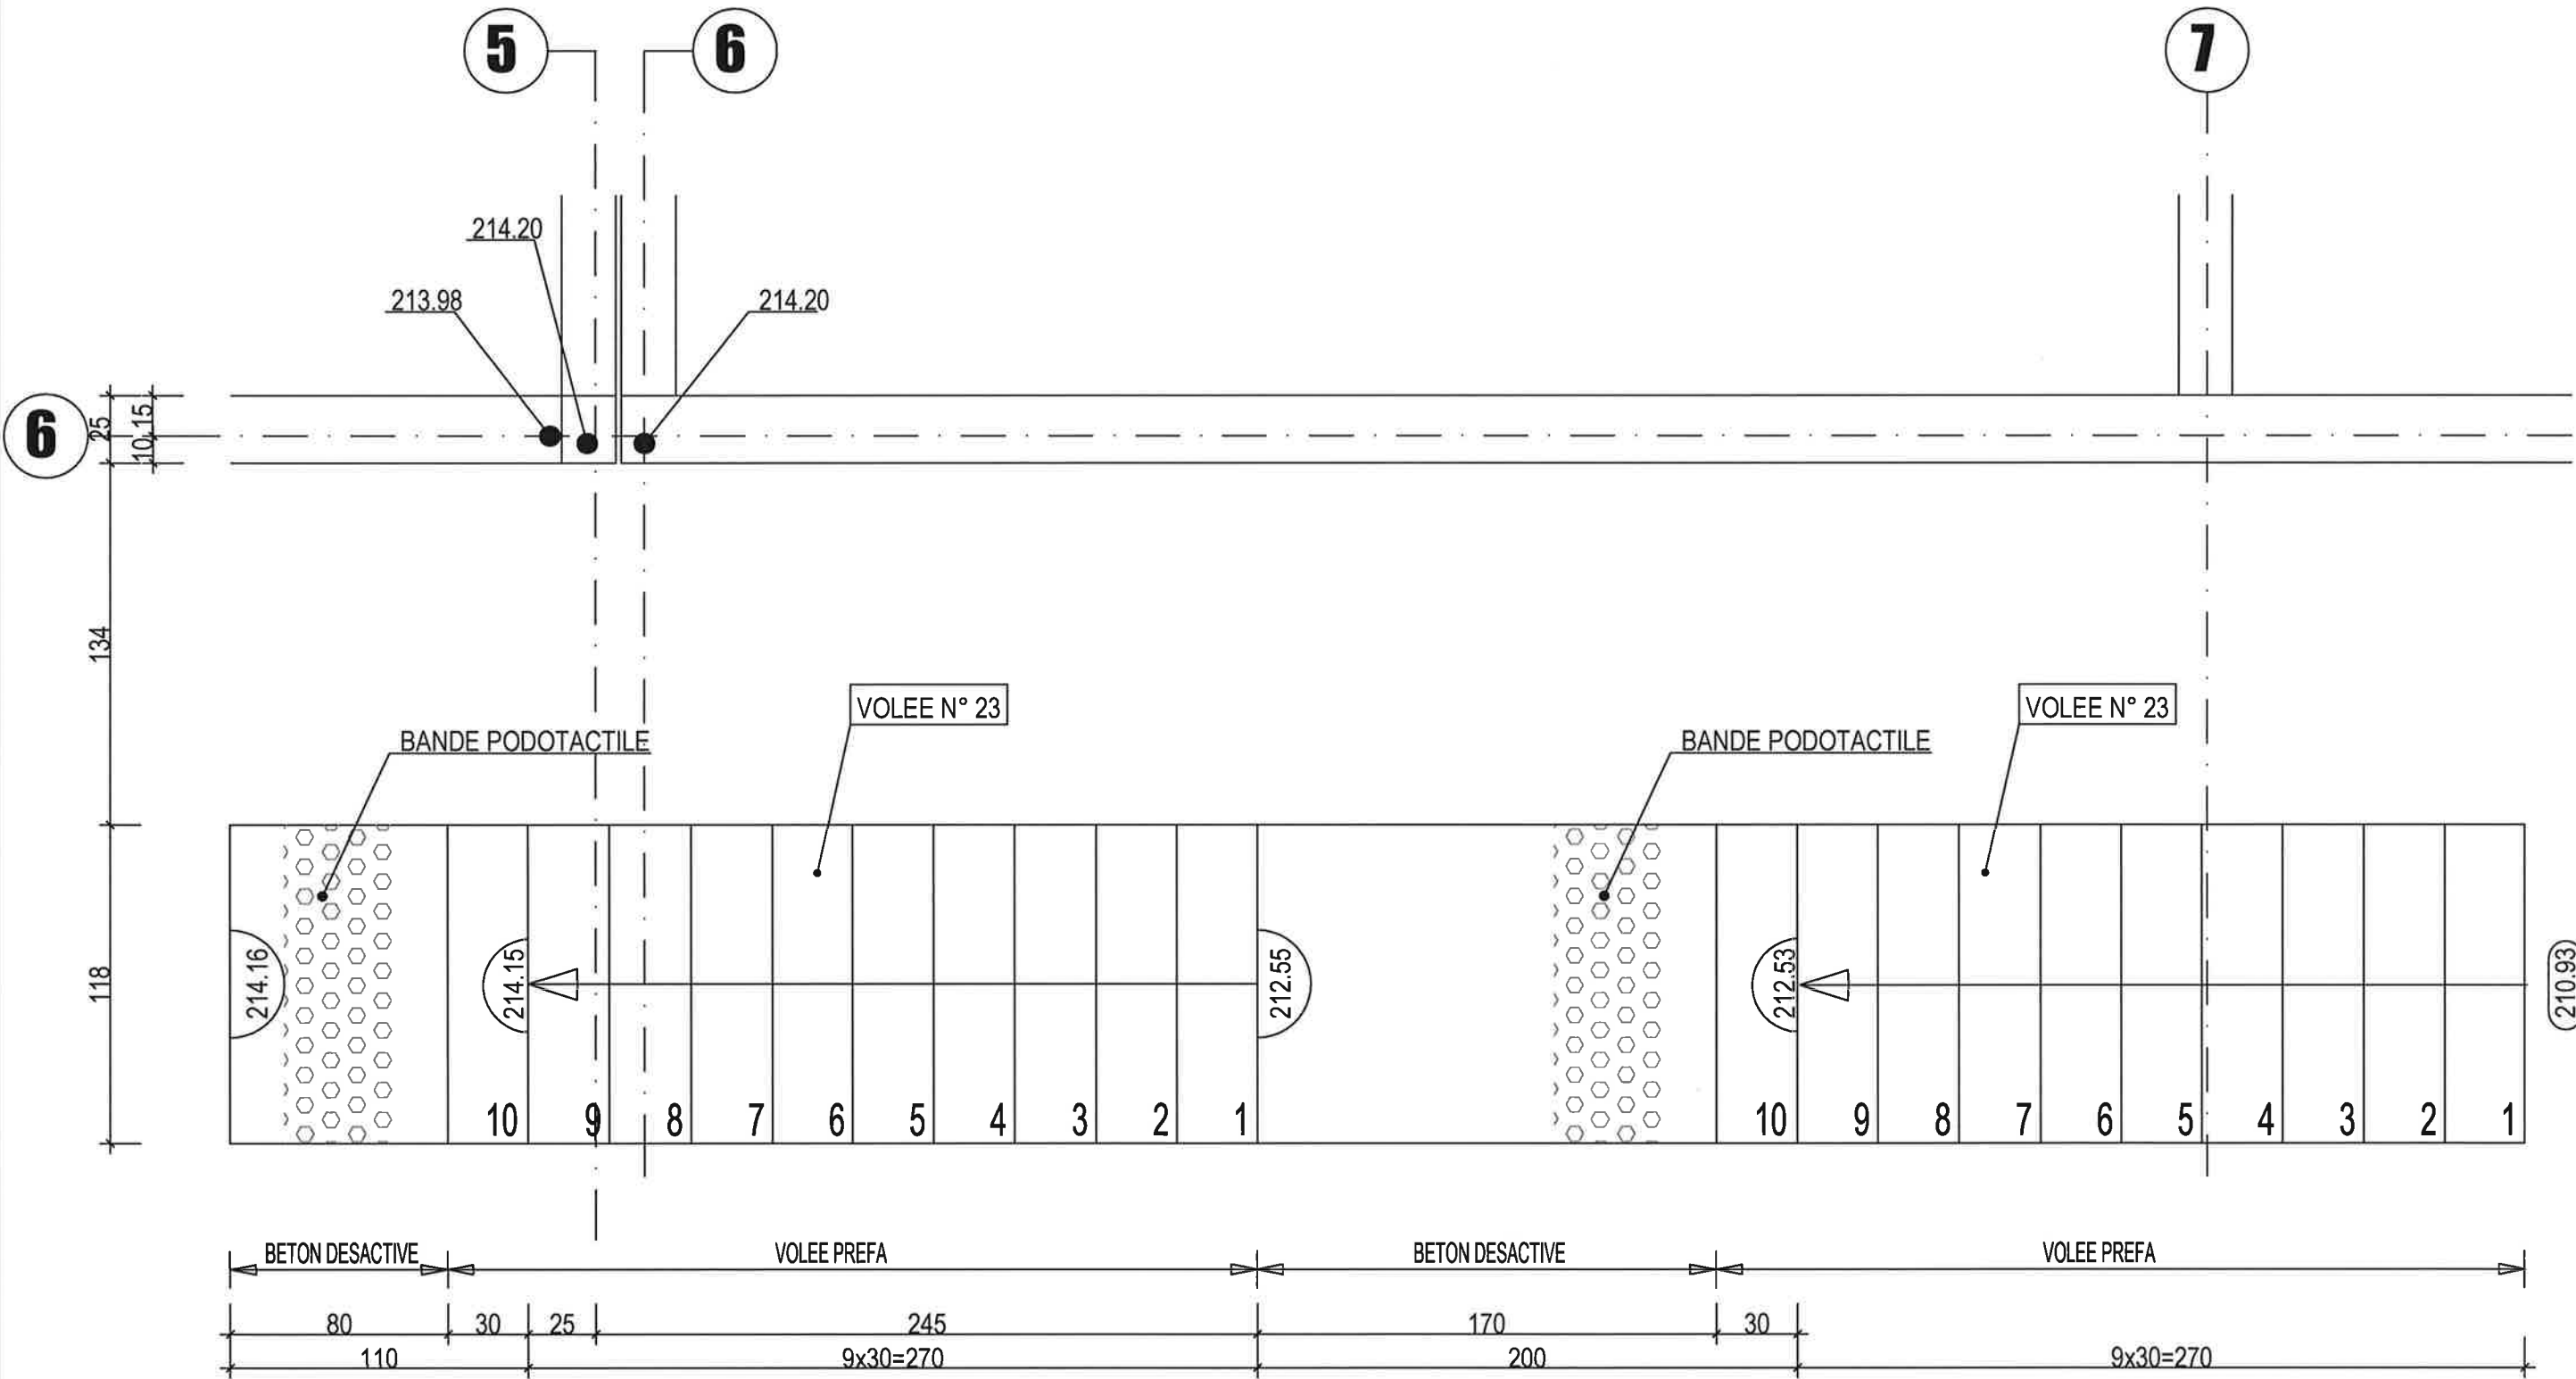


ESCALIER FILES 5,6 et 7 FACADE SUD

COUPE

Ech: 1/25

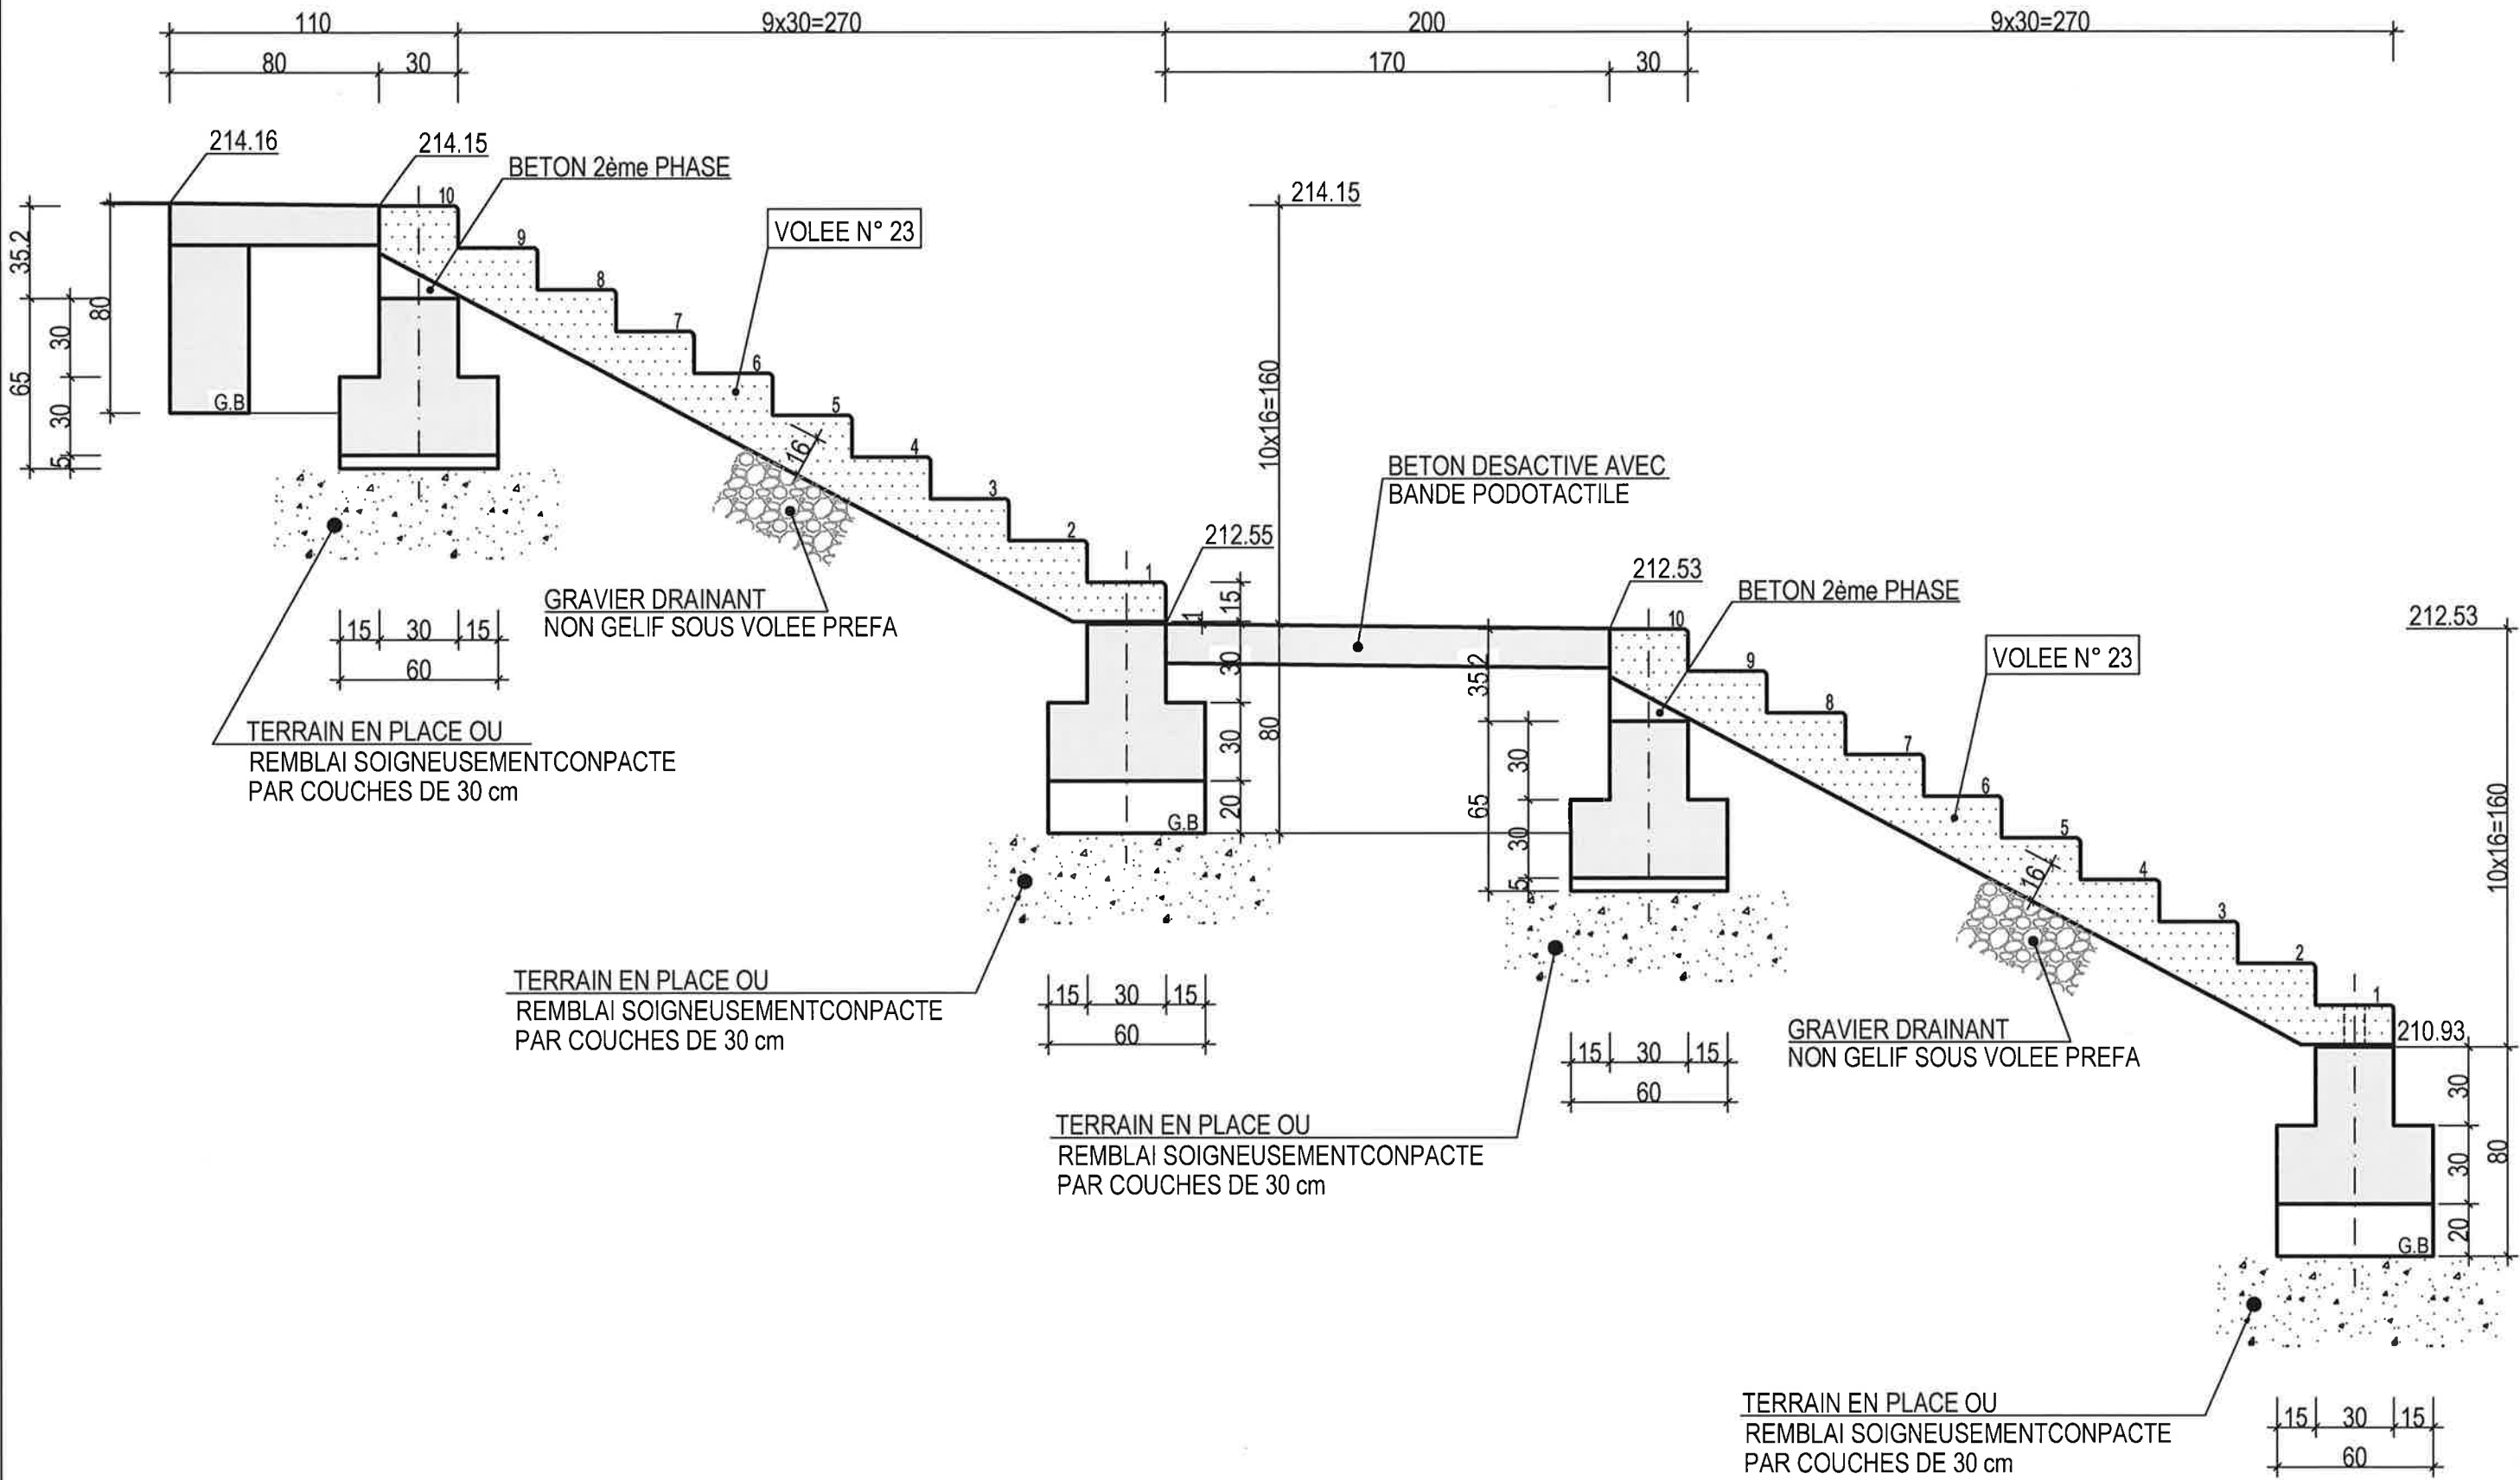


S1 2 p

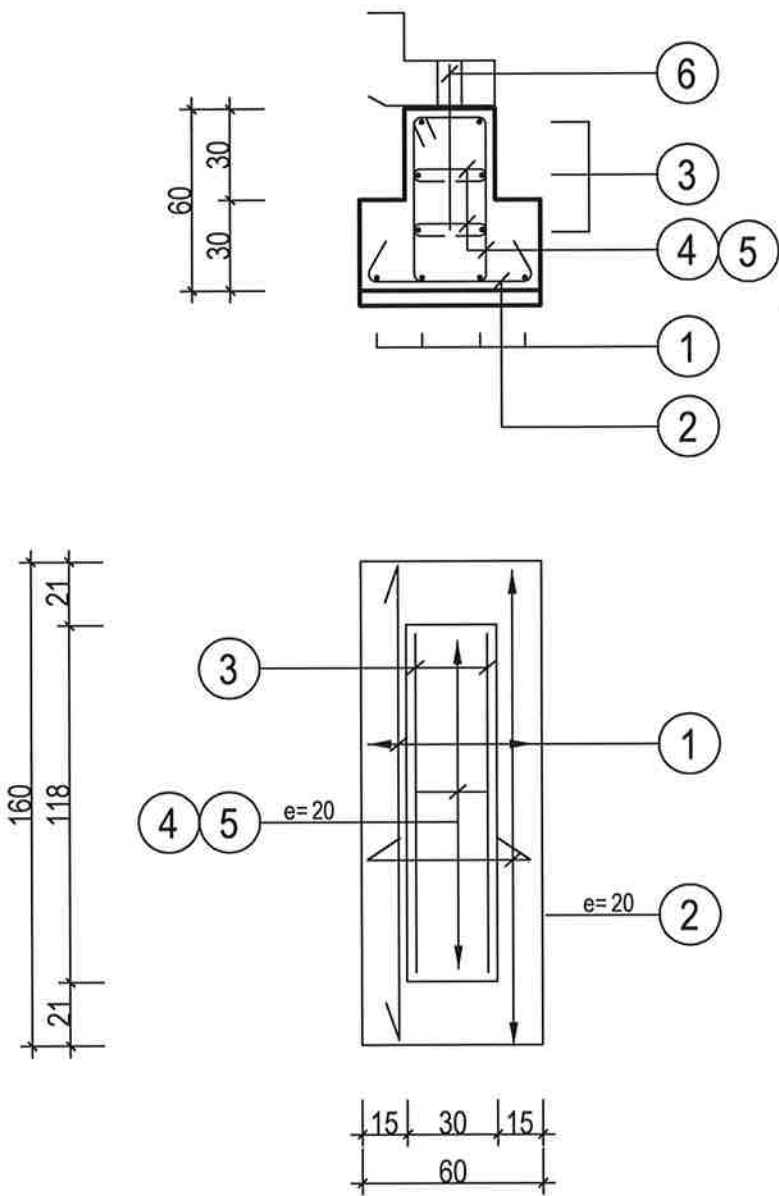

①	4 HA 10 x	
②	8 HA 10 x	
③	6 HA 10 x	110
④	6 HA 8 x	
⑤	2X6 HA 6 x	
⑥	2 HA 14 x	65
⑦		
⑧		
⑨		
⑩		
⑪		
⑫		
⑬		
⑭		
⑮		

S1a 2 p

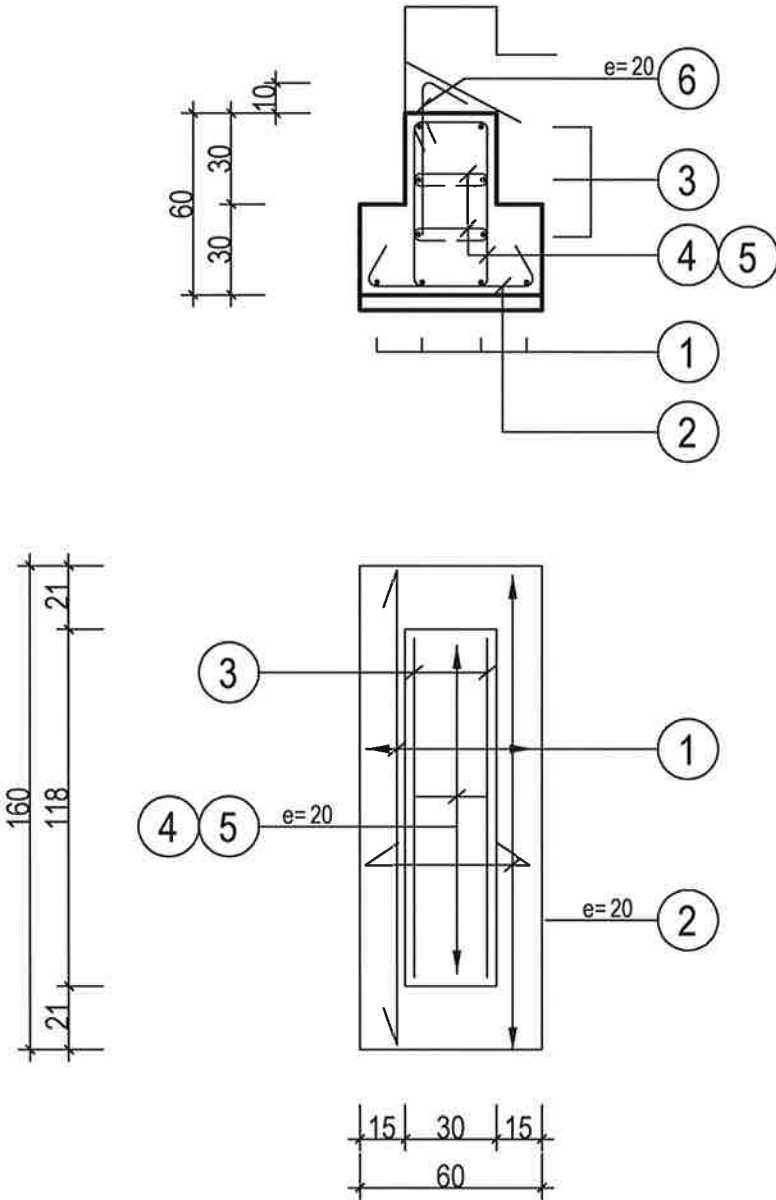


①	4 HA 10 x	
②	8 HA 10 x	
③	6 HA 10 x	
④	6 HA 8 x	
⑤	2X6 HA 6 x	
⑥	6 HA 8 x	
⑦		
⑧		
⑨		
⑩		
⑪		
⑫		
⑬		
⑭		
⑮		

ESCALIER FILE 1 FACADE SUD

VUE EN PLAN FONDATIONS


Ech: 1/25

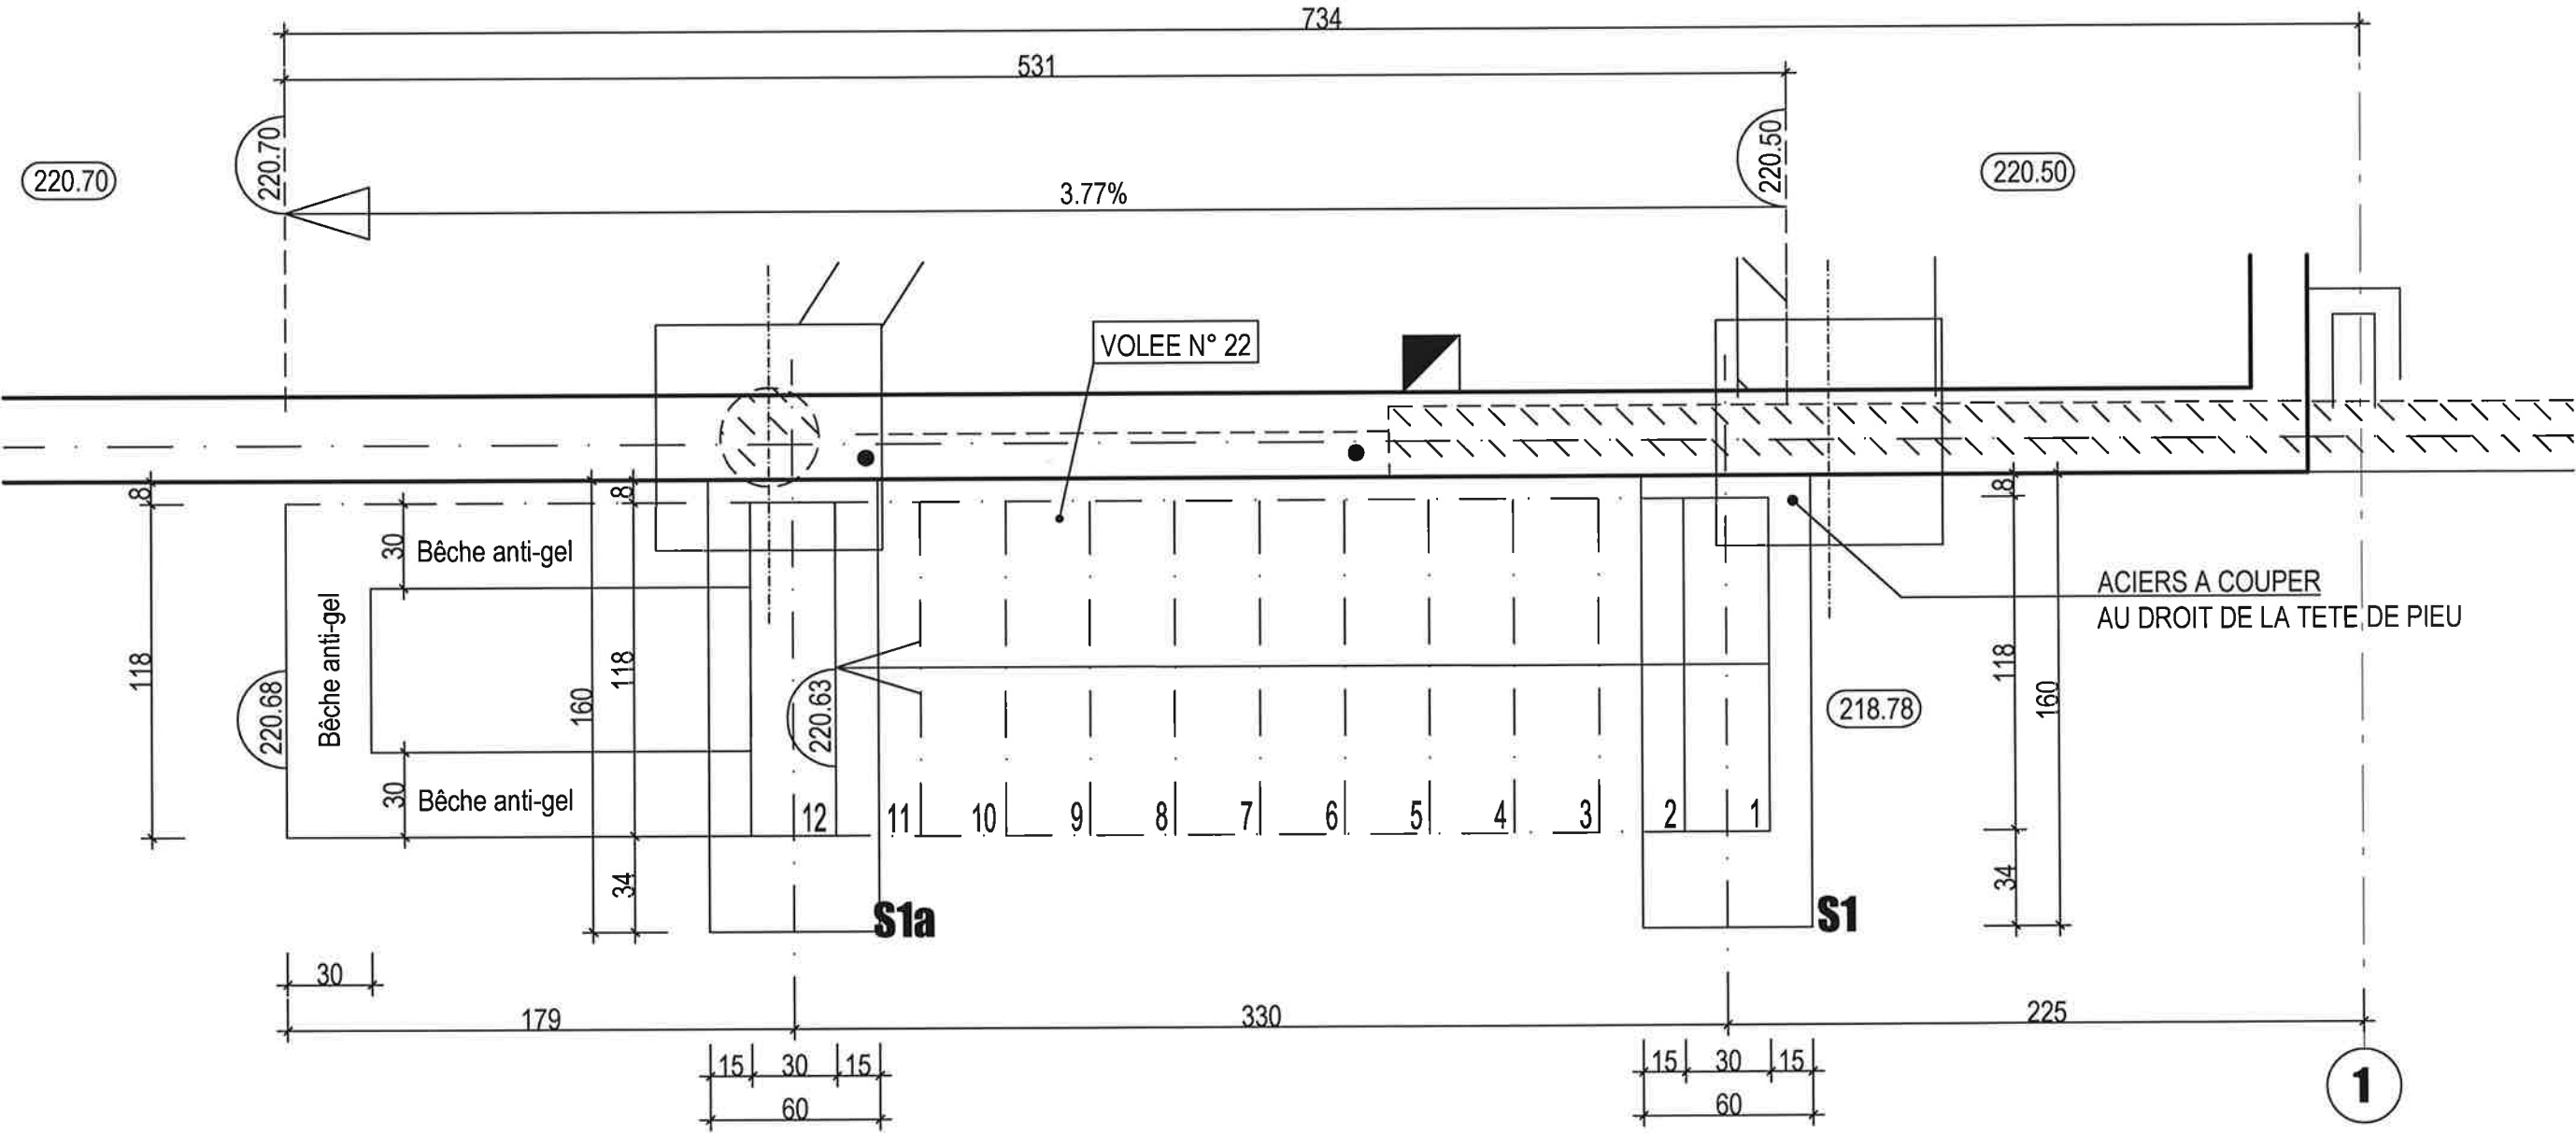

ESCALIER FILE 1 FACADE SUD


VUE EN PLAN VOLEES PREFABRIQUEES

Ech: 1/25

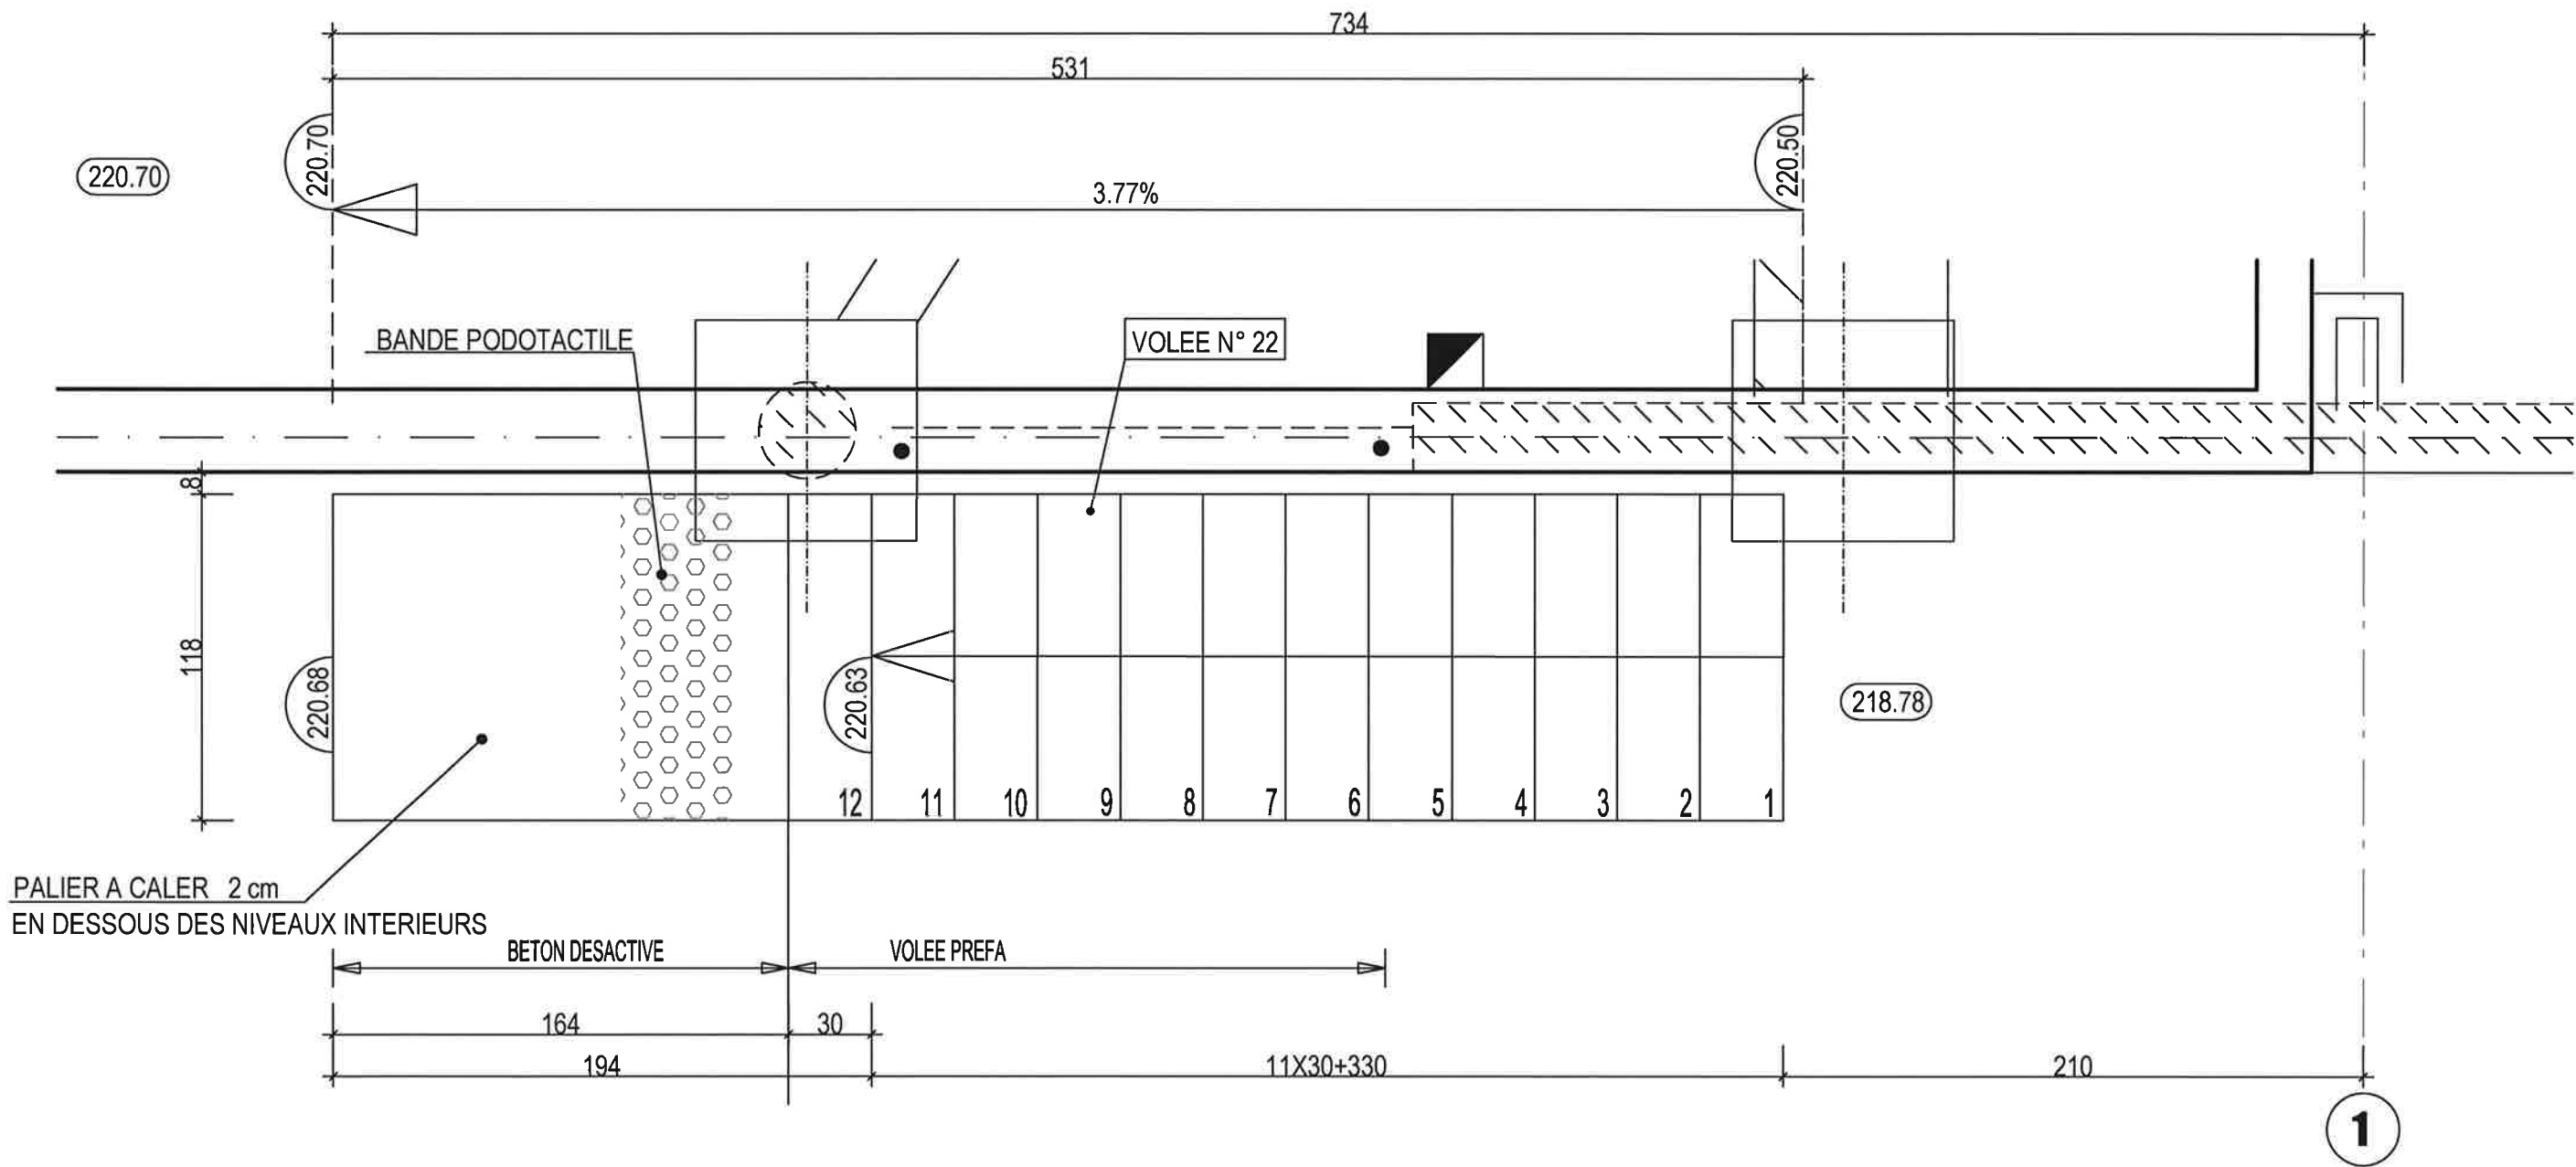




ESCALIER FILE 1 FACADE SUD

1

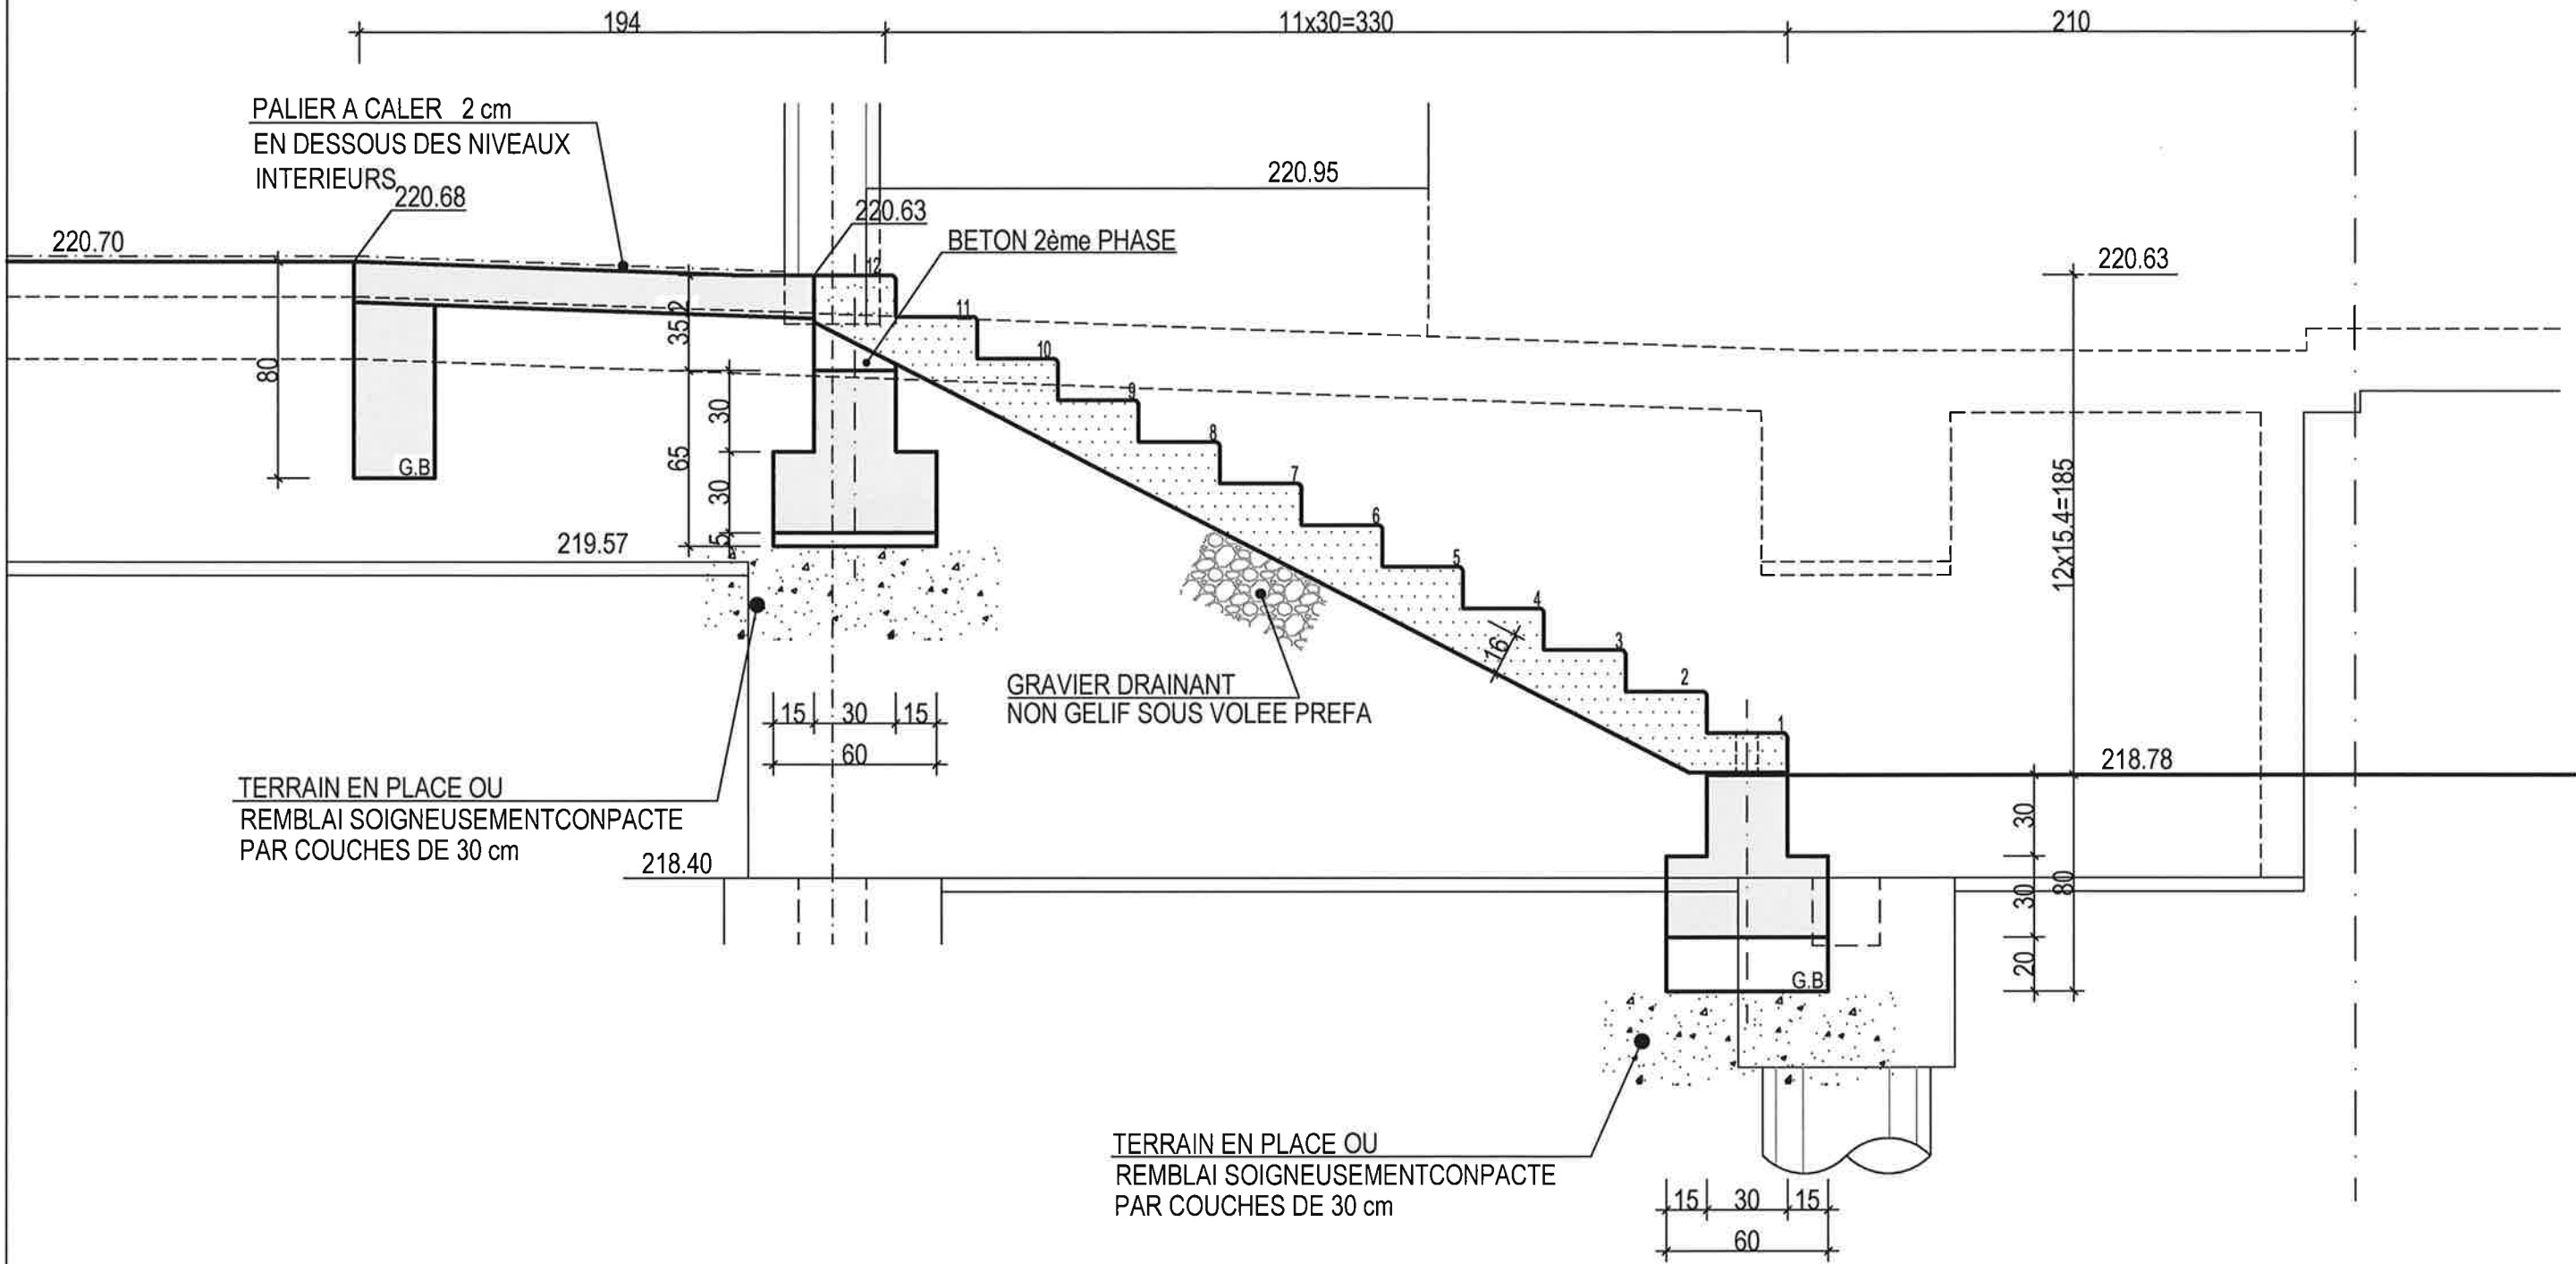


S1 2 p

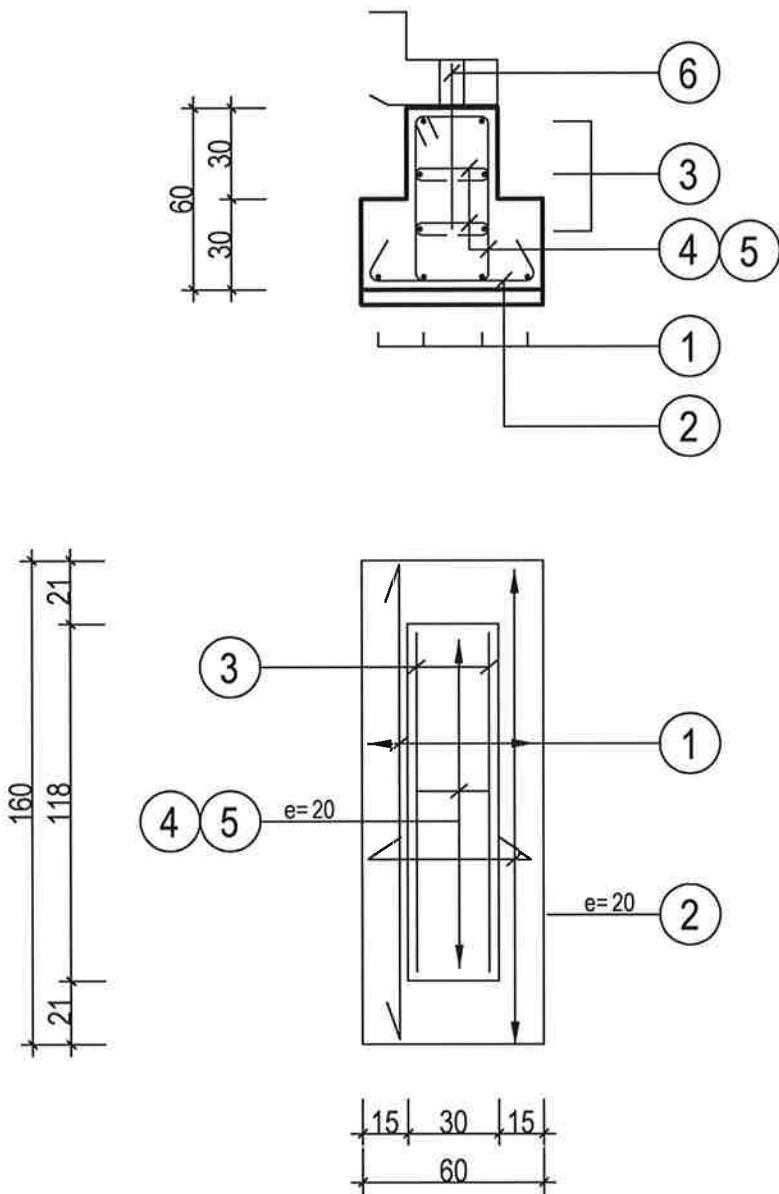

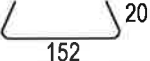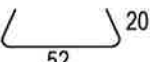①	4 HA 10 x	 20 152
②	8 HA 10 x	 20 52
③	6 HA 10 x	110
④	6 HA 8 x	 24 54
⑤	2X6 HA 6 x	 24
⑥	2 HA 14 x	65
⑦		
⑧		
⑨		
⑩		
⑪		
⑫		
⑬		
⑭		
⑮		

S1a 2 p

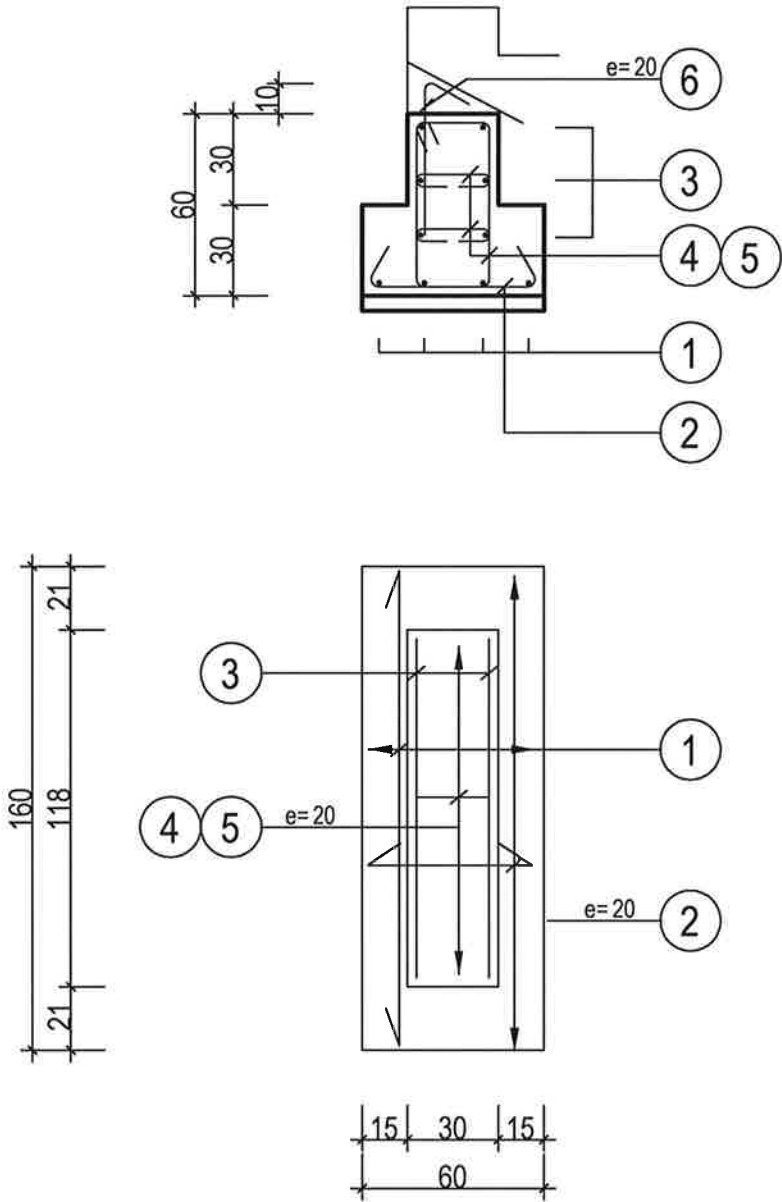

①	4 HA 10 x	
②	8 HA 10 x	
③	6 HA 10 x	
④	6 HA 8 x	
⑤	2X6 HA 6 x	
⑥	6 HA 8 x	
⑦		
⑧		
⑨		
⑩		
⑪		
⑫		
⑬		
⑭		
⑮		