



ATTENTES POTEAUX DANS SEMELLES


ATP30

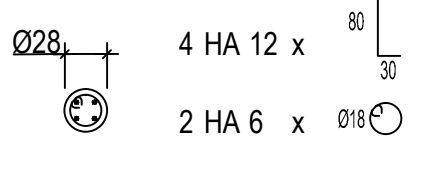


ATP31

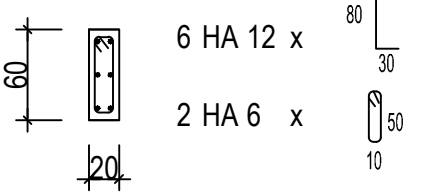


ATP32 à ATP34

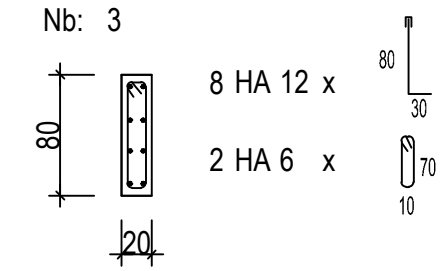


ATTENTES MURS DANS POUTRES

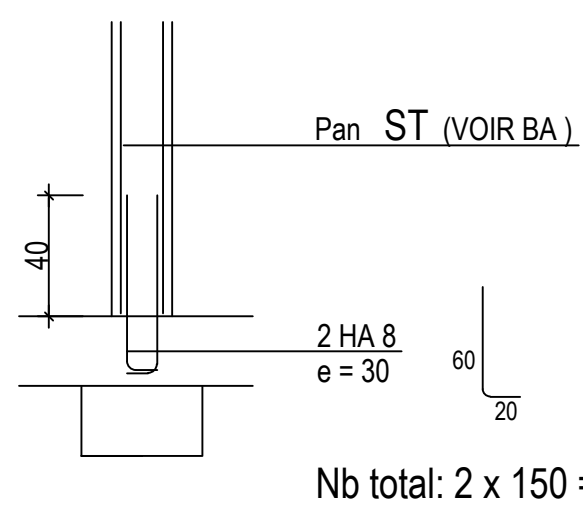


ATT Nb: 5

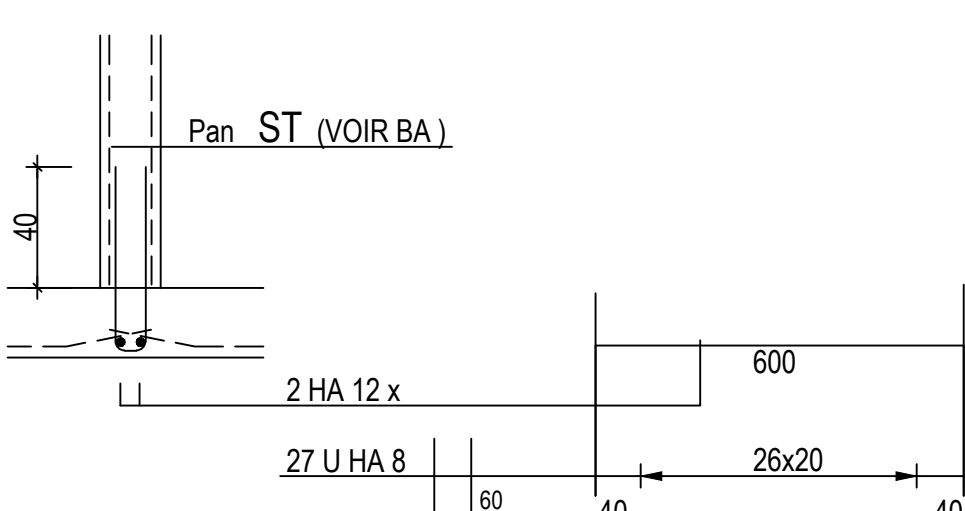

CH1 Nb: 4

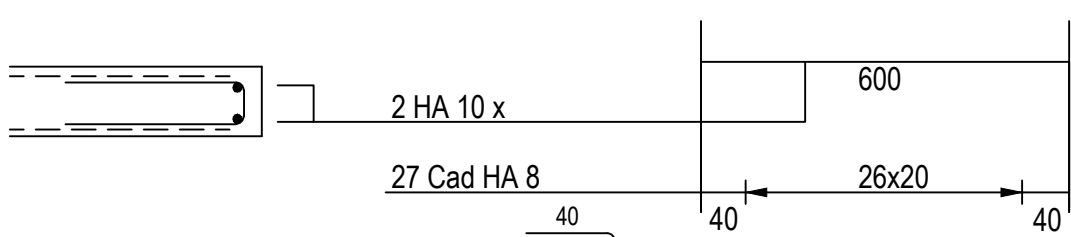


CH2 Nb: 1

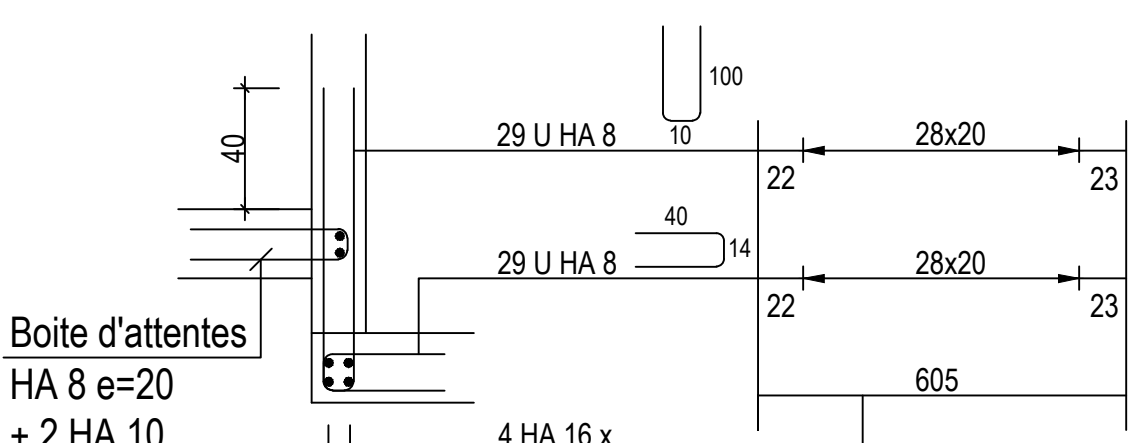


Boite d'attentes
HA 8 e=20
+ 2 HA 10

CH3 Nb: 1

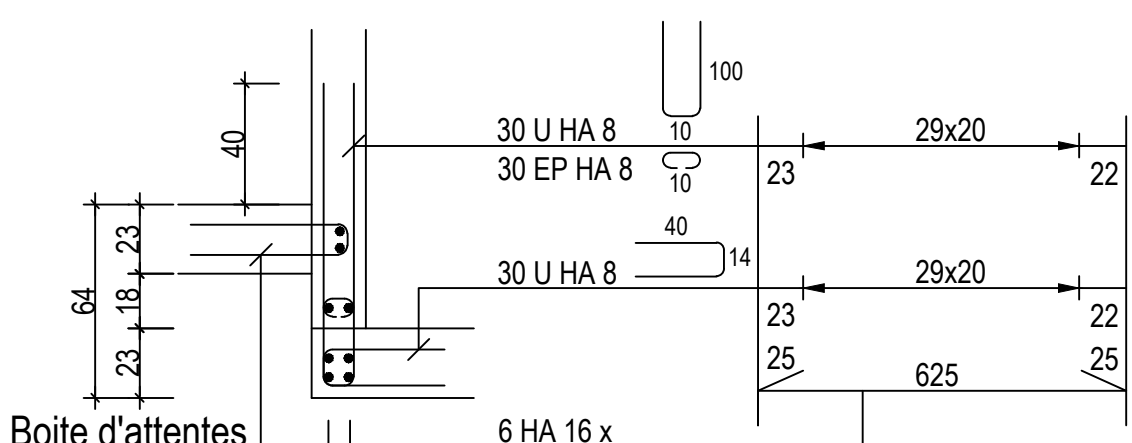

Boite d'attentes
HA 8 e=20
+ 2 HA 10

CH4 Nb: 1

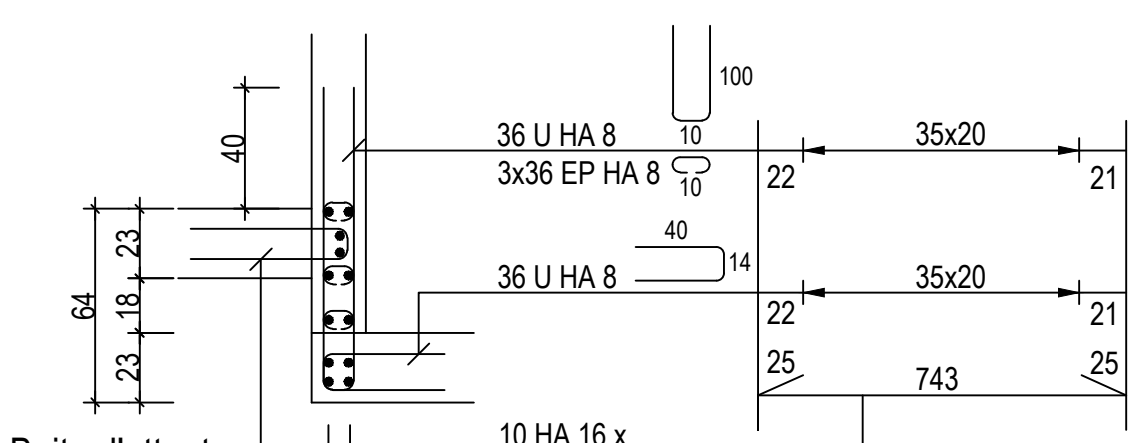


Boite d'attentes
HA 8 e=20
+ 2 HA 10

DETAIL D'ABOUTS DE CHAINAGES

INTERIEURS:


Position des équerres d'angles dans dalle 2 HA 14 x
à pas 100

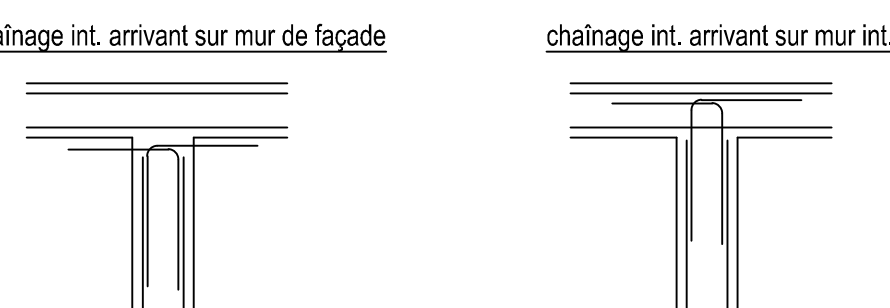

DETAIL D'ABOUTS DE CHAINAGES


EN ANGLE SUR FACADES:

Position des équerres d'angles dans dalle 2 HA 14
x 100 à pas 100

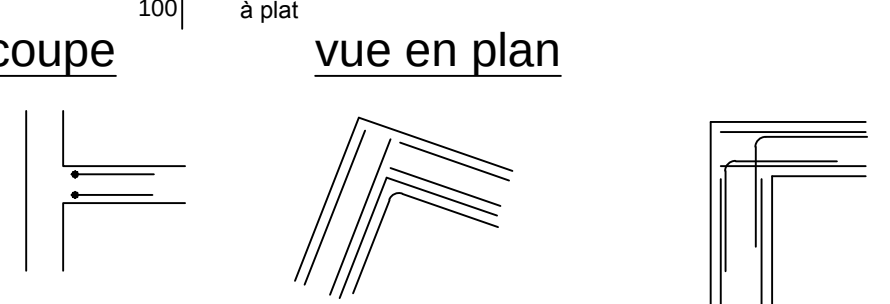

RECA. T.S.			RESTE
MJ 251C	240x120	3	0.
	240x140	1	0
	240x200	14+3/4	3
	240x220	9+1/2	9
	240x240	6	6
	240x260	2+3/4	0
	240x280	2+1/2	2+1/2
	240x360	3	0
	240x440	5+1/4	5+1/4
	240x480	19+3/4	5
MJ 257	240x500	3+3/4	3+3/4
	240x520	3	3
MJ 335	240x540	4+1/4	0
	240x600	8+1/4	5
MJ 257	240x620	2+3/4	0
	240x600	33+1/4	7
MJ 335	240x600	7+3/4	7+3/4

Principe de renfort aux droits des gaines:

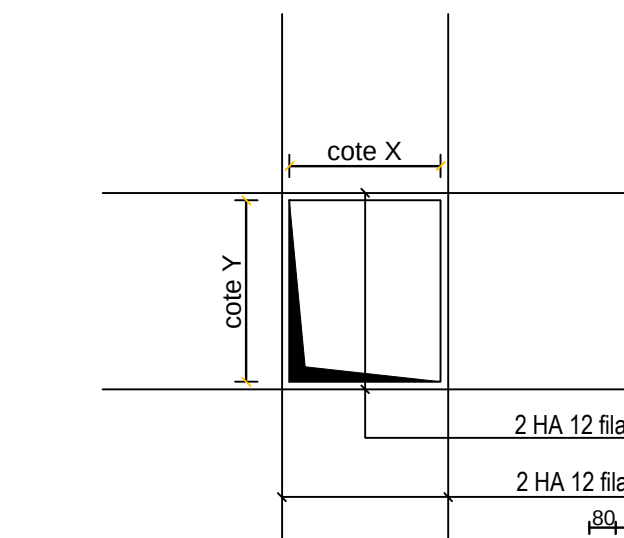


NOTA: Ces renforts sont en complément des aciers mis sur la vue en plan

PANNEAUX EN TIROIRS PREVOIR RECOURVEMENTS DECALES

EX: 1er Lit: 3 panneaux
2ème Lit: 1/2+2+1/2 panneaux

Renforts réservations

Jusqu'à Ø200 mm

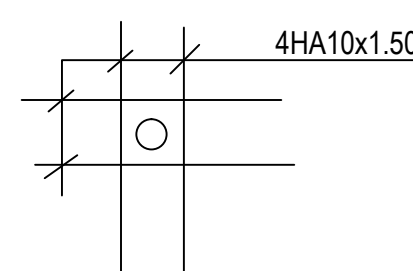

NOAHO

Chemin de Fontanière - 69350 La Mulatière

Création de logements

Les entreprises réalisant les travaux devront tenir compte des derniers plans architectes lors de la réalisation des travaux Les plans du Bâtiment ne doivent pas être coupés d'éléments et doivent être des plans d'exécution		
ARCHITECTES:	ATELIER DE LA PASSERELLE	MISE EN ŒUVRE:
BET STRUCTURE:	MATTE SAS	MO:
RET FLUIDES:	PRELEM	CSRS:
ECONOMISTE:	EXECO	OPC:
BUREAU DE CONTRÔLE:	Bureau VERITAS	ENTREPRISES:

Bât: B

PLANCHER sur -6
ARMATURES DALLE INFERIEURES

INCOE	DATE	MODIFICATIONS
A	21/10/2015	MAJ nombre CH2, CH3 et ATT
B	04/11/2015	MISE A JOUR COMMANDE TS

MATTE
BUREAU D'ETUDES
STRUCTURES ET FLUIDES
119 BOULEVARD STALINGRAD 69100 VILLEURBANNE
Tel: 04 72 44 02 87 Fax: 04 72 44 28 59
E-mail: bat@matte.fr

Dessiné par: JBO
Contrôle par: P.LIN
Echelle: 1/50°

Affaire N°
13.12.119

DOE

Contraintes de sol: 8 bars EL5

Aciers HA (T) FeE500

Aciers Doux (B) FeE235

Aciers TS FeE500

Béton f28 = 25MPa

Enrobage: 3 cm

PLAN N°
B12 B

DATE: 09/10/2015