

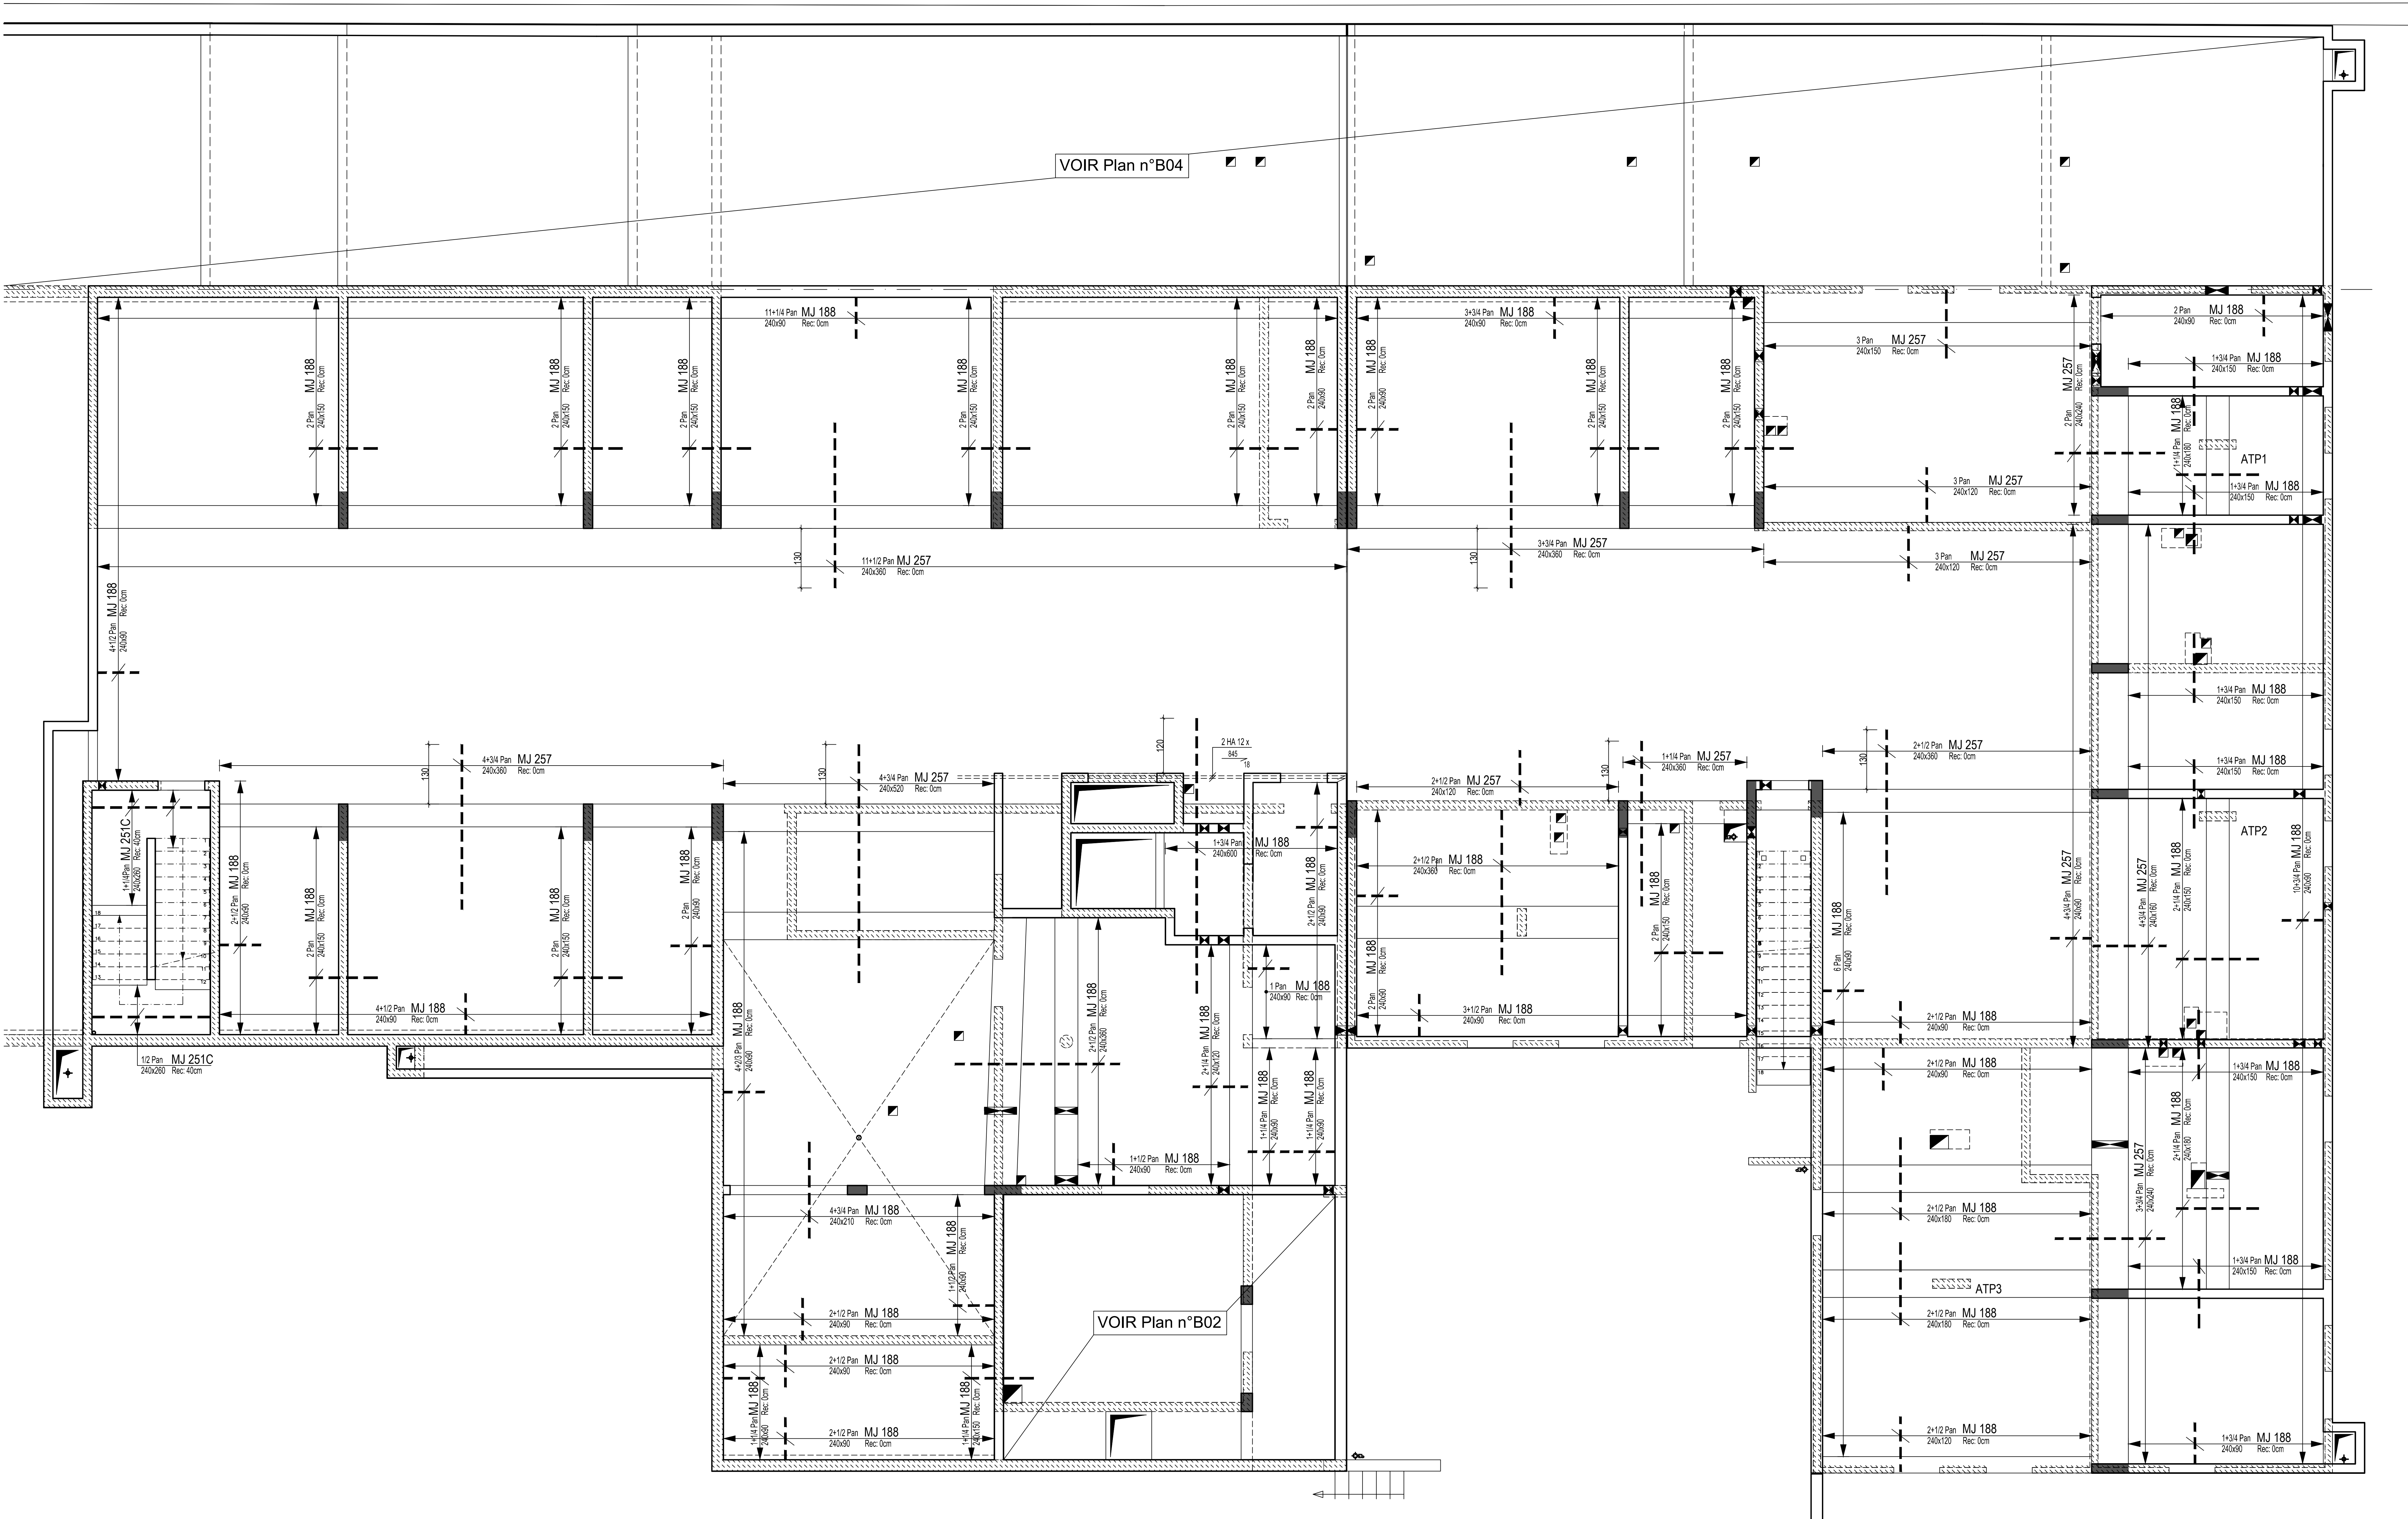


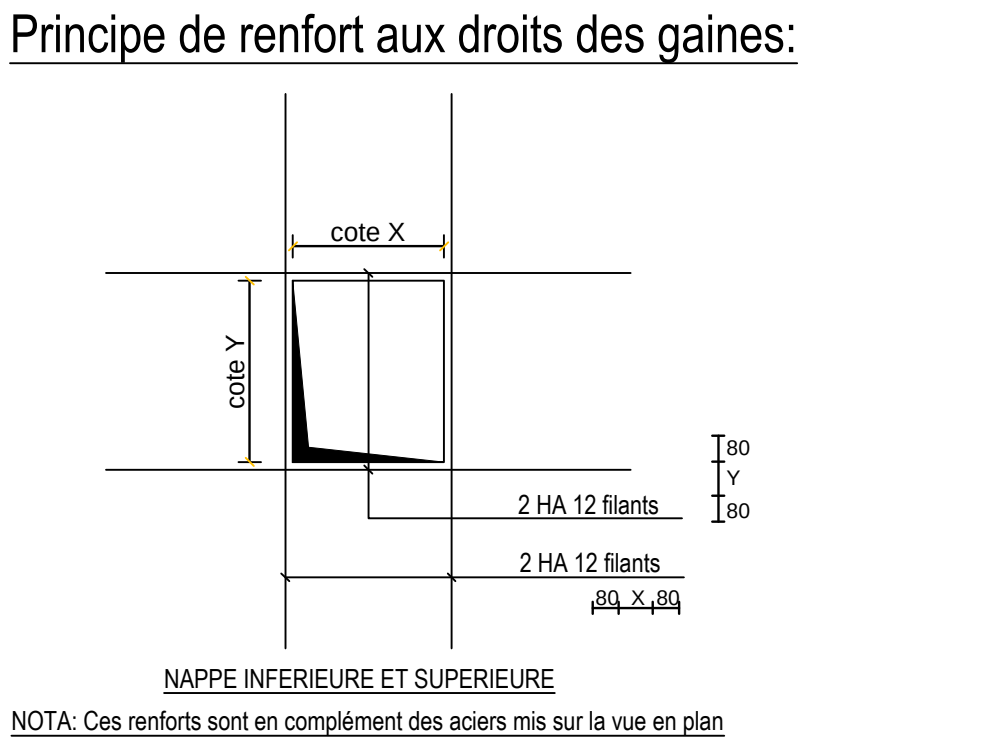

DETAIL D'ABOUTS DE CHAINAGES
INTERIEURS:
Position des équerres d'angles dans dalle 2 HA 14 x 100 à plat
vues en plan
chainage int. arrivant sur mur de façade chainage int. arrivant sur mur int.

DETAIL D'ABOUTS DE CHAINAGES
EN ANGLE SUR FACADES:
Position des équerres d'angles dans dalle 2 HA 14 x 100 à plat
coupe **vue en plan**

RECA. T.S.			RESTE
MJ 188	240x90	82	0
	240x120	4+3/4	0
	240x150	30+1/2	0
	240x180	10+3/4	7
	240x210	4+3/4	0
	240x360	5	0
MJ 257	240x600	1+3/4	0
	240x90	4+3/4	0
	240x120	8+1/2	0
	240x150	7+3/4	0
	240x240	5+3/4	0
	240x360	23+3/4	8
MJ 251C	240x260	1+3/4	0

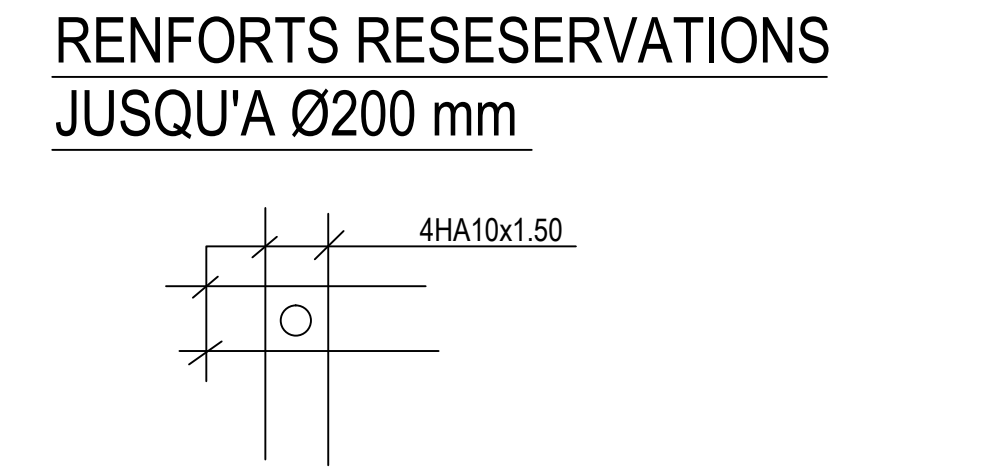

PANNEAUX EN TIROIRS PREVOIR RECOURVEMENTS DECALES
EX: 1er Lit: 3 panneaux
2ème Lit: 1/2+1/2 panneaux EN TIROIR

NOAHO
Chemin de Fontanière - 69350 La Mulatière
Création de logements

Les entreprises réalisant les travaux devront tenir compte des derniers plans architectes lors de la réalisation des travaux
Les plans de la MATTE ne doivent servir qu'à des corps d'élaboration et doivent être des plans d'exécution.

ARCHITECTES:	ATELIER DE LA PASSERELLE	MATTE S.A.S.	MO: SELOUCHE	PSO Ingénierie
BET STRUCTURE:	PRELEM	EXECO	CSRS:	SUD EST COORDINATION
RET FLUIDES:	EXECO	EXECO	OPC:	
ECONOMISTE:	Bureau VERITAS		ENTREPRISES:	Fontanel-gbc

Bât: B
PLANCHER sur -6
ARMATURES DALLE SUPERIEURES

DOE
Comptes de sol 8 bars EL5
Aciers HA (T) FeE500
Aciers Doux (B) FeE235
Aciers TS FeE500
Béton f28 = 25MPa
Enrobage = 3 cm

INDICE	DATE	MODIFICATIONS
A	04/11/2015	MISE A JOUR COMMANDE TS

MATTÉ
BUREAU D'ETUDES
STRUCTURES ET FLUIDES
119 BOULEVARD STALINGRAD 69100 VILLEURBANNE
Tel. 04 72 44 02 67 Fax 04 72 44 28 59
E-mail: bat@matte.fr

Dessiné par : J.B.O
Contrôle par : P.LIN
Echelle: 1/50'

PLAN N° B13 A
DATE: 09/10/2015

Affaire N° 13.12.119