

 


TABLEAU SEMELLES ISOLEES


Repère	Long. x Larg.	HT
S1	150 x 240	55
S2	120 x 240	55
S3		
S4	160 x 240	60
S5	110 x 400	50
S6	150 x 150	40

TABLEAU SEMELLES FILANTES


Repère	Larg.	HT
SF 50	50	30
SF 60		
SF 70	70	35
SFe 70	70	35

COUPES TYPES SEMELLES FILANTES

INTERIEURES

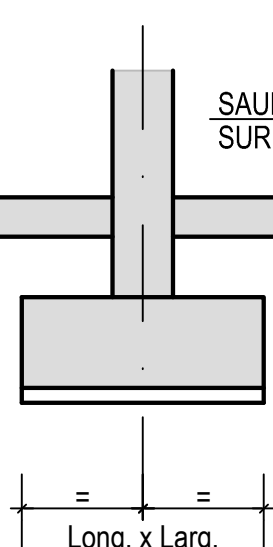


RIVES

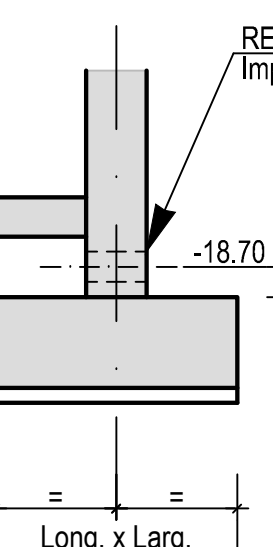

COUPES TYPES SEMELLES ISOLEES

PORTEAUX ou MURS

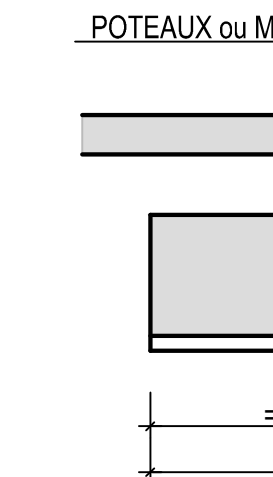

±0.00 = 220.50

NOAHO

Chemin de Fontanière - 69350 La Mulatière

Création de logements

Les emprises réalisant les travaux devront tenir compte des derniers plans architecte lors de la réalisation des travaux.
Les plans du DE MATTE ne doivent servir qu'au corps d'état concerné et doivent être des plans d'exécution.

ARCHITECTES: MATE SAS

ATTELIER DE LA PASSERELLE

MISE: MATE SAS

BET STRUCTURE: PRELEM

ECONOMISTE: EXECO

BUREAU DE CONTROLE: BUREAU VERITAS

MO DELEGUE: PSO Ingénierie

CSFS: SUD EST COORDINATION

GPC: ENTREPRENEUR: Fontanel-abc

Bât: B

FONDACTIONS

Cofrage

DOE

Contenance de sol 8 bars EL5

Aciers HA (T) FeE500

Aciers Doux (U) FeE235

Aciers TS FeE 500

20m TS2 ±20Pa

Enrobage ±3 cm

INDICE

DATE

MODIFICATIONS

A

30/08/2015

Maj regard rétention, ajout fosse hydrocarbure

B

03-09-2015

AJOUTE SURVERSES TYPE "A"

C

09/10/2015

MISE A JOUR SUIVANT C (Position mur pignon avec rampe)

D

15/10/2015

MISE A JOUR FOSSE ASCENSEUR et CUNETTES

MATTÉ

BUREAU D'ETUDES

STRUCTURES ET FLUIDES

119304 LEVANT STALABRIS - 69100 VILLEURBANNE

Tel: 04 72 44 02 87 Fax: 04 72 44 26 69

E-mail: mat@matte.fr

Destiné par: J.B.O

Contrôlé par: S. BARRIERE

Echelle: 1/50'

PLAN N°

B01 D

DATE: 28/07/2015

Affaire N°

13.12.118