

NOHAO

Chemin de Fontanière-69350 La Mulatière

Création de logements

Les entreprises réalisant les travaux devront tenir compte des derniers plans architecte lors de la réalisation des travaux
Les plans du be MATTE ne doivent servir qu'au corps d'état concerné et doivent être des plans d'exécution.

ARCHITECTE(S): Atelier DE LA PASSERELLE
BET STRUCTURE: BET MATTE
BET FLUIDES: PRELEM
ECONOMISTE: EXECO
BUREAU DE CONTROLE: VERITAS

M.O. Délégué: .
M.O.: .
CSPS: PSO ingénierie
M.O.E.: SUD EST COORDINATION
ENTREPRISE(S): Fontanel-pbc

Bât: B

FONDATIONS

Armatures

DOE

INDICE	DATE	MODIFICATIONS
A	31/07/2015	AJOUTE PAGES 15 à 31
B	30/08/2015	MODIFIE POSITION REGARG DANS FOSSE
C	09/10/2015	MISE A JOUR NIVEAUX(Modif. hauteur poutre 50 et poteau

Aciers HA (T) FeE500
Aciers Doux (Ø) FeE 235
Aciers TS FeE 500
Béton fc28 >= 25MPa
Enrobage = 3 cm

PLAN N°
B02 C

DATE : 29-07-2015

MATTÉ
BUREAU D'ÉTUDES
STRUCTURES ET FLUIDES

119 BOULEVARD STALINGRAD 69100 VILLEURBANNE

Tél. 04 72 44 02 87 Fax 04 72 44 26 59

E-mail : bet@matte.fr

Dessiné par : J.BONDETTI
Contrôlé par : P. LIN
Ech :

Affaire N°
S.13.12.118

AFF: S.13.12.118		Bât: B	LA MULATIERE-69350 LaMulatiere CREATION de LOGEMENTS		FONDATIONS au -6		Plan n° B 02	Page: 2									
S2 120X240x55ht																	
<table><tr><th colspan="2">Nombres</th></tr><tr><td>Entre axes 8 à 15</td><td>Entre axes 16 à 18</td></tr><tr><td>2</td><td>11</td></tr></table>					Nombres		Entre axes 8 à 15	Entre axes 16 à 18	2	11	VOIR ATTENTES POTEAUX 55				1	7 HA 14 x	
					Nombres												
Entre axes 8 à 15	Entre axes 16 à 18																
2	11																
2	14 HA 14 x																
240 120 e=17 1 2					3												
					4												
					5												
AFF: S.13.12.118		Bât: B	LA MULATIERE-69350 LaMulatiere CREATION de LOGEMENTS		FONDATEIONS au -6		Plan n° B 02	Page: 6						
SF50 Rec: 50 cm <table><tr><th colspan="2">Nombres</th></tr><tr><td>Entre axes 8 à 15</td><td>Entre axes 16 à 18</td></tr><tr><td>11</td><td>19</td></tr></table>									Nombres		Entre axes 8 à 15	Entre axes 16 à 18	11	19
Nombres														
Entre axes 8 à 15	Entre axes 16 à 18													
11	19													
①	4 HA 8 x						600							
②	22 HA 8 x						52	20						
③	22 HA 8 x						70	10						
④														
⑤														
⑥														
⑦														
⑧														
⑨														
⑩														
⑪														
⑫														
⑬														
⑭														
⑮														

AFF: S.13.12.118

Bât: B

LA MULATIERE-69350 La Mulatiere
CREATION de LOGEMENTS

FONDATIONS au -6

Plan n° B 02

Page: 7

SF70

Rec: 50 cm

Nombres	
Entre axes 8 à 15	Entre axes 16 à 18
4	0


A replier au droit des ouvertures

Dimensions: 40, 35, 21 x 25, 27 x 20, 6, 28, 38, 30, 70

Callouts: 1, 2, 3

1	6 HA 8 x	600
2	28 HA 10 x	62 20
3	28 HA 8 x	70 10
4		
5		
6		
7		
8		
9		
10		
11		
12		
13		
14		
15		

AFF: S.13.12.118		Bât: B	LA MULATIERE-69350 LaMulatiere CREATION de LOGEMENTS	FONDACTIONS au -6		Plan n° B 02	Page: 8				
SF70a Rec: 50 cm											
Nombres <table><tr><td>Entre axes 8 à 15</td><td>Entre axes 16 à 18</td></tr><tr><td>2</td><td>1</td></tr></table>								Entre axes 8 à 15	Entre axes 16 à 18	2	1
Entre axes 8 à 15	Entre axes 16 à 18										
2	1										
①	6 HA 8 x						600				
②	28 HA 10x						 20 62				
③	2x28 HA 8 x						70  10				
④											
⑤											
⑥											
⑦											
⑧											
⑨											
⑩											
⑪											
⑫											
⑬											
⑭											
⑮											

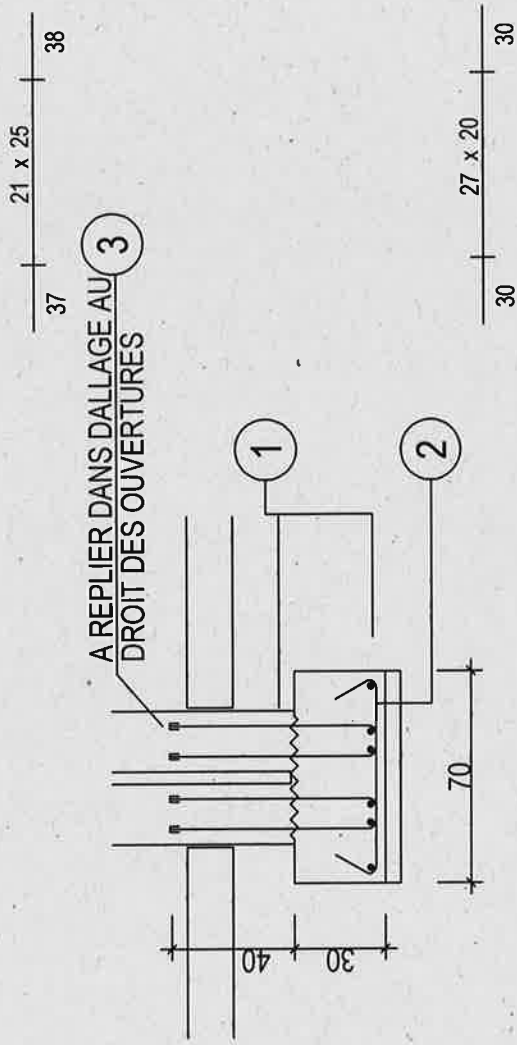

A REPLIER DANS DALLAGE AU DROIT DES OUVERTURES

AFF: S.13.12.118

Bât: B

LA MULATIERE-69350 La Mulatiere
CREATION de LOGEMENTS

FONDATIONS au -6

Plan n° B 02

Page: 9

SFe70

Rec: 50 cm

Nombres	
Entre axes 8 à 15	Entre axes 16 à 18
24	7



①	4 HA 10x	600
②	46 HA 12x	20 62 110
③	23 HA 10x	80
④		
⑤		
⑥		
⑦		
⑧		
⑨		
⑩		
⑪		
⑫		
⑬		
⑭		
⑮		

ANGLES SEMELLES FILANTES


Rec: 40 cm

Nombres	
Entre axes 8 à 15	Entre axes 16 à 18
5	1

Nombres	
Entre axes 8 à 15	Entre axes 16 à 18
12	11

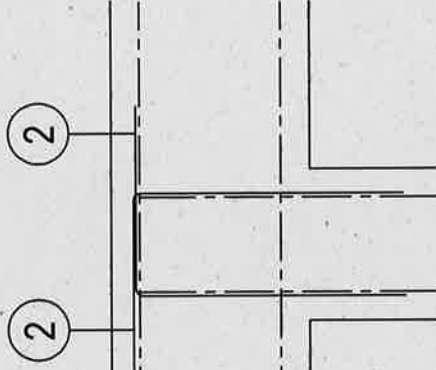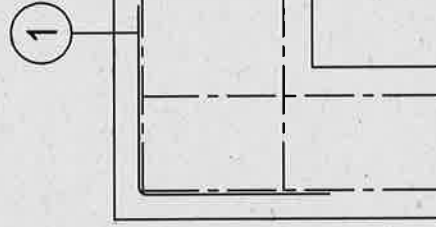


LIAISON SEMELLES ISOLEES et FILANTES

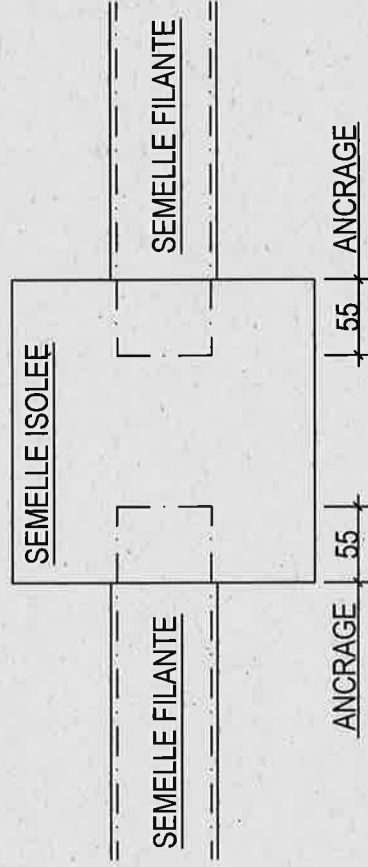

ATTENTES POTEAUX DANS SEMELLESentre axes 8 et 15


P1 P2 P3 P4 P5 P6
P9 P10 P12 P17

20x80

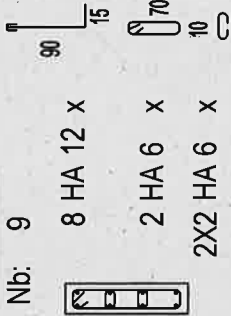


P4 P11

25x80

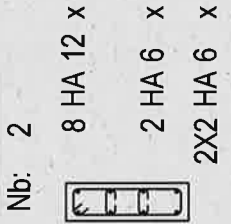


P16

20x43

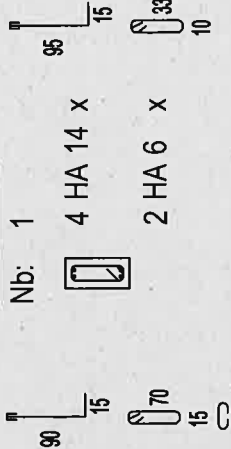


P18

20x50

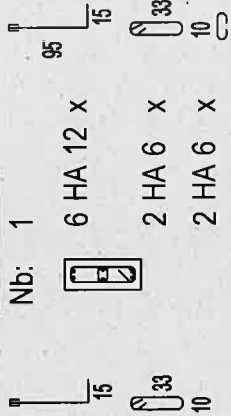


P19 P20

25x40

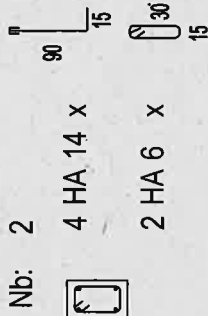


P21

25x50

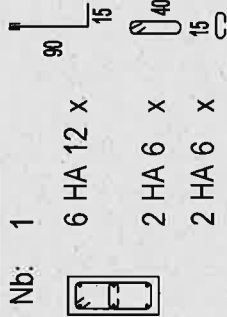


Attentes murs dans semelles isolees

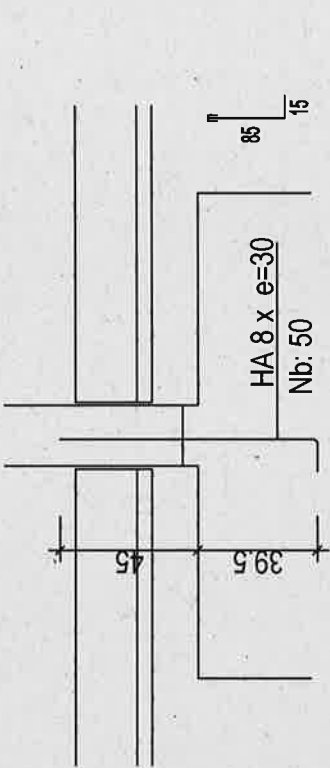

ANGLES et ABOUTS VOILES

Nb: 42

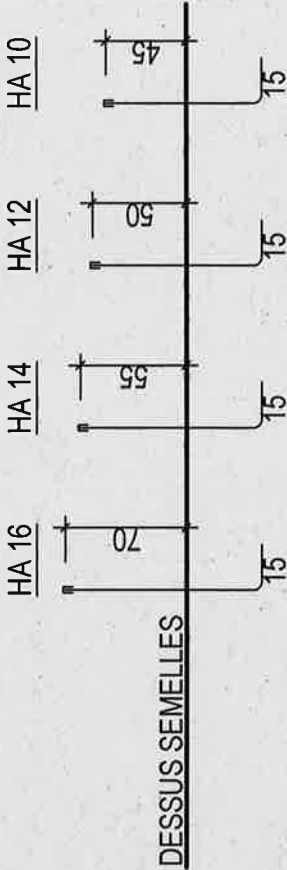

ATTENTES POTEAUX DANS SEMELLES entre axes 16 et 18


P7 P8 P13 P22 P23 P24

P25 P26 P27 P28


P4 P15

P14


20x80

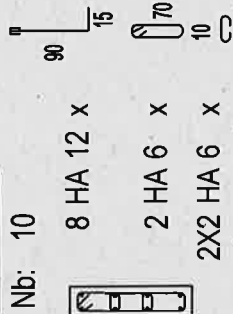


25x80

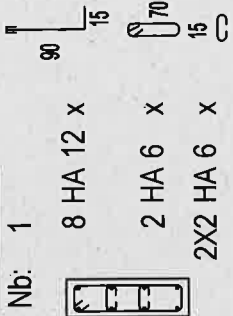



20x100

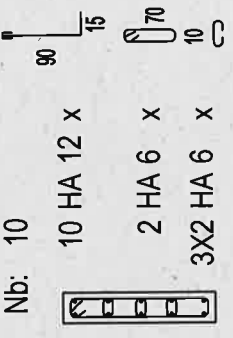

Attentes murs dans semelles isolees

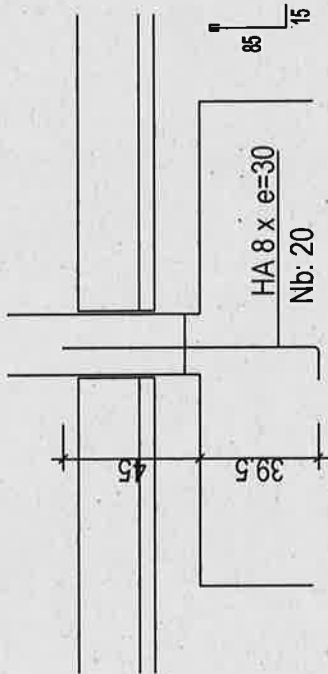


ANGLES et ABOUTS VOILES

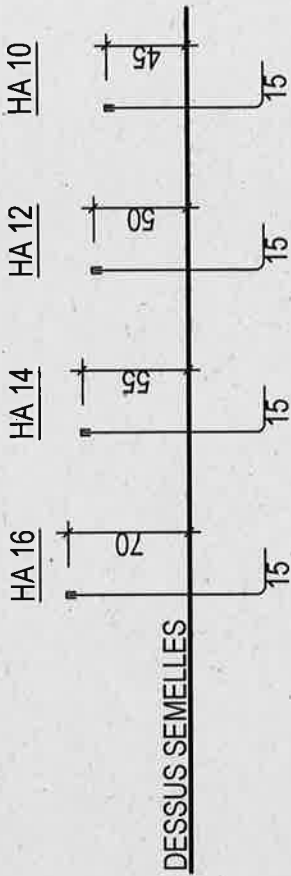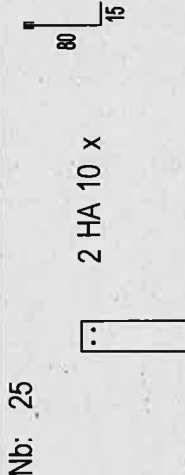


FOSSE ASCENSEUR

ANGLES (VALABLE 4 fois)

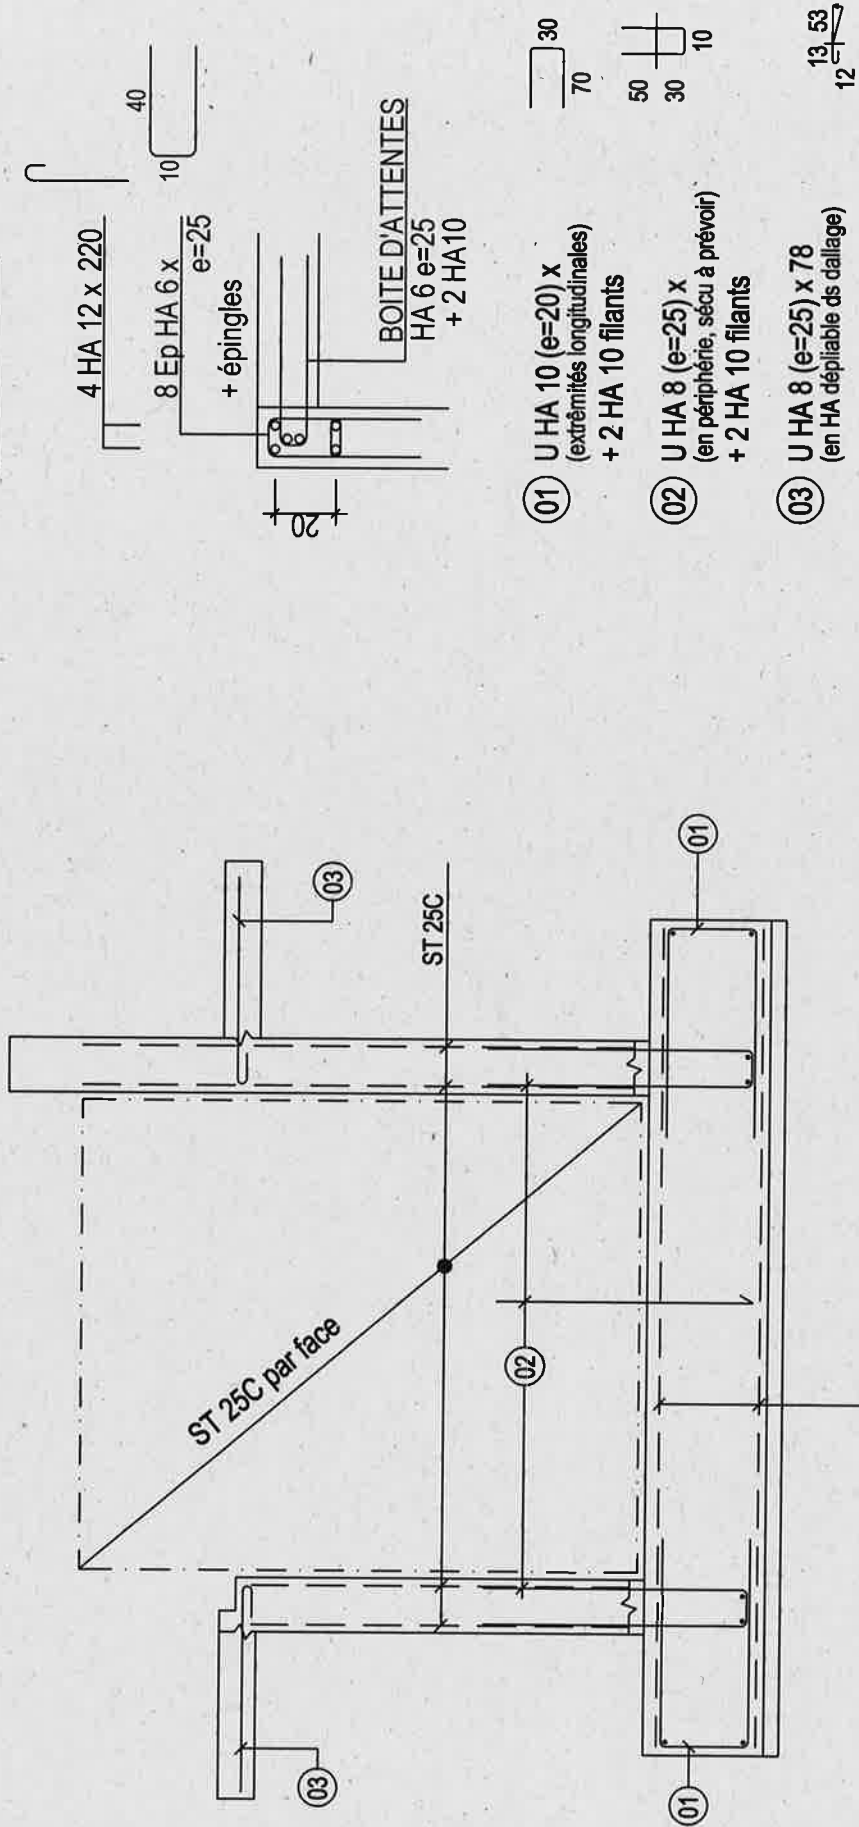

DALLAGE

JOINTS SCIÉS

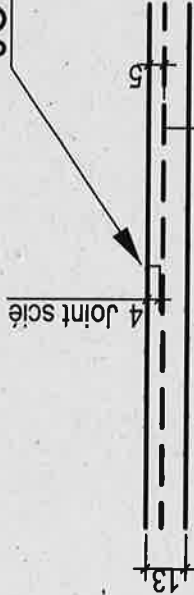

Pan ST 15C 400X240


Rec:30 cm MINI

Nombres	
Entre axes 8 à 15	Entre axes 16 à 18
70	65


(Nb: INDICATIF A CONFIRMER PAR LE DALLAGISTE)

RADIER

VUE EN PLAN

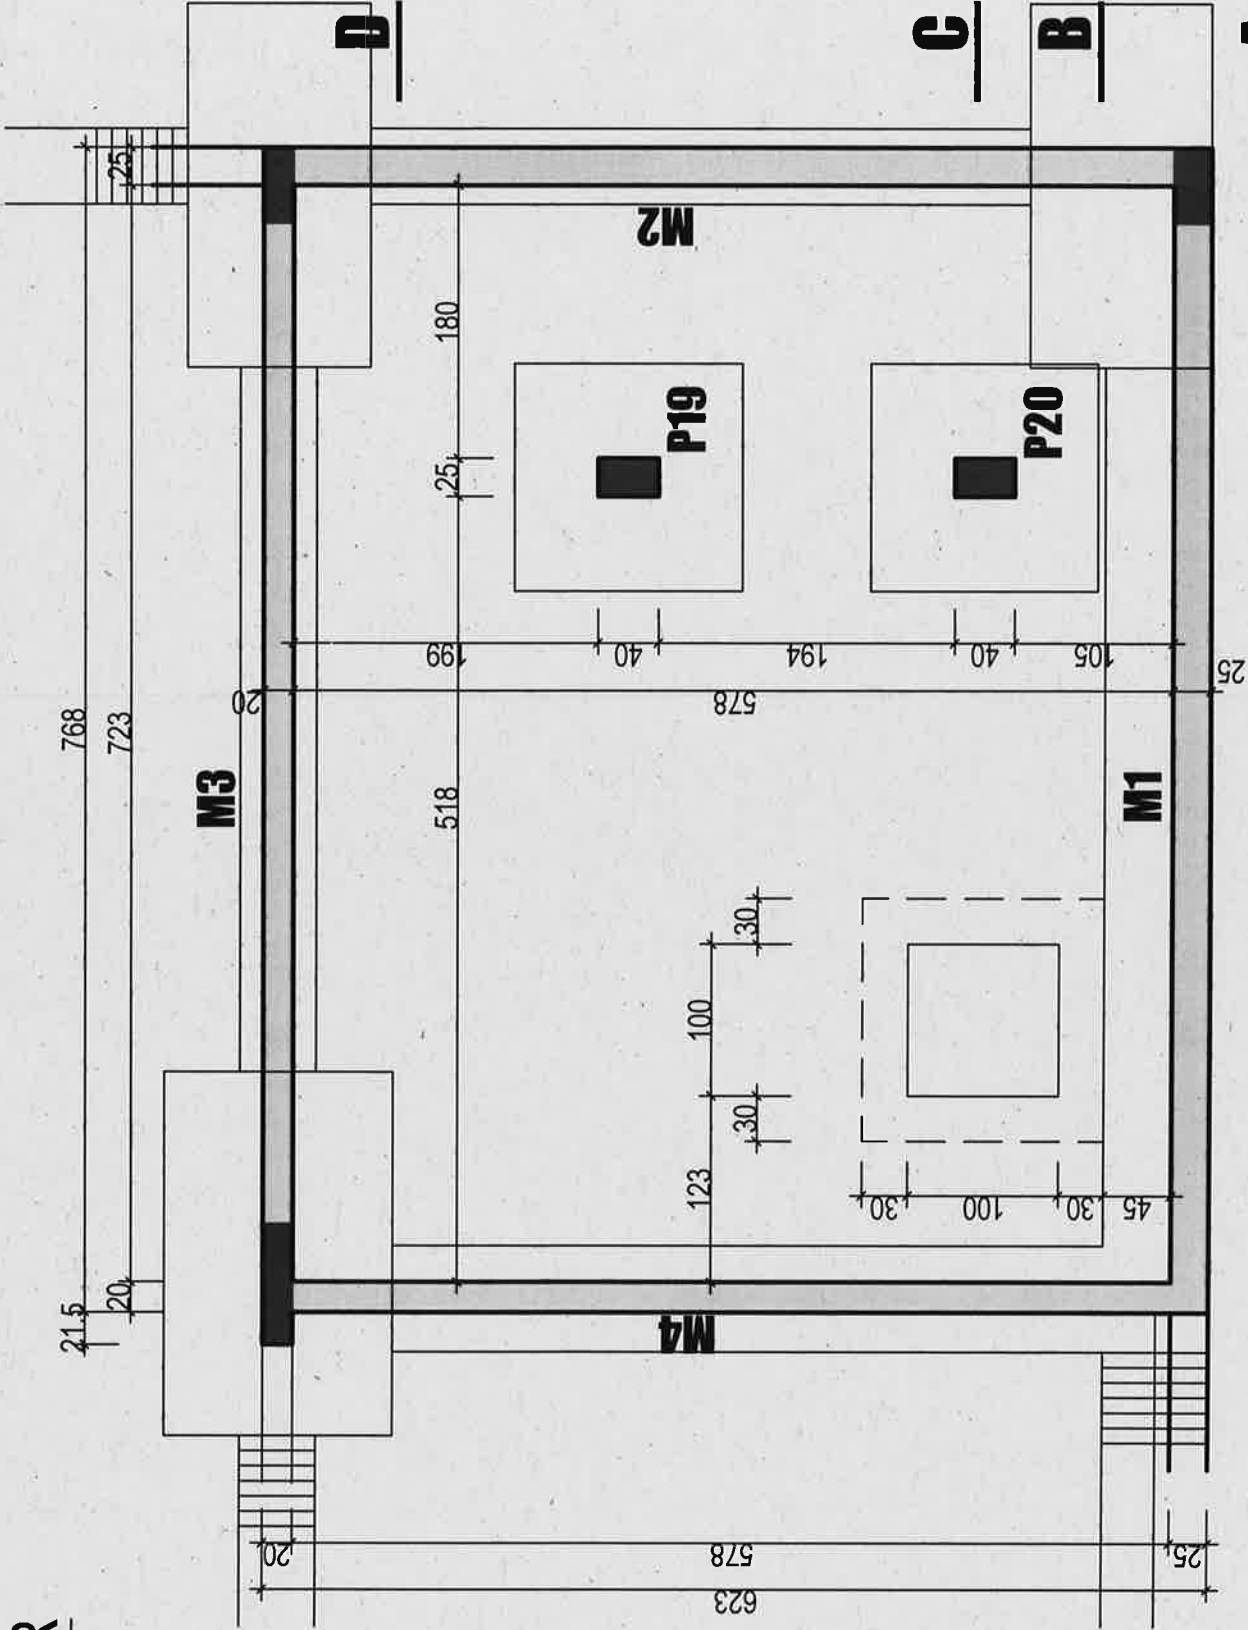


A FOSSE

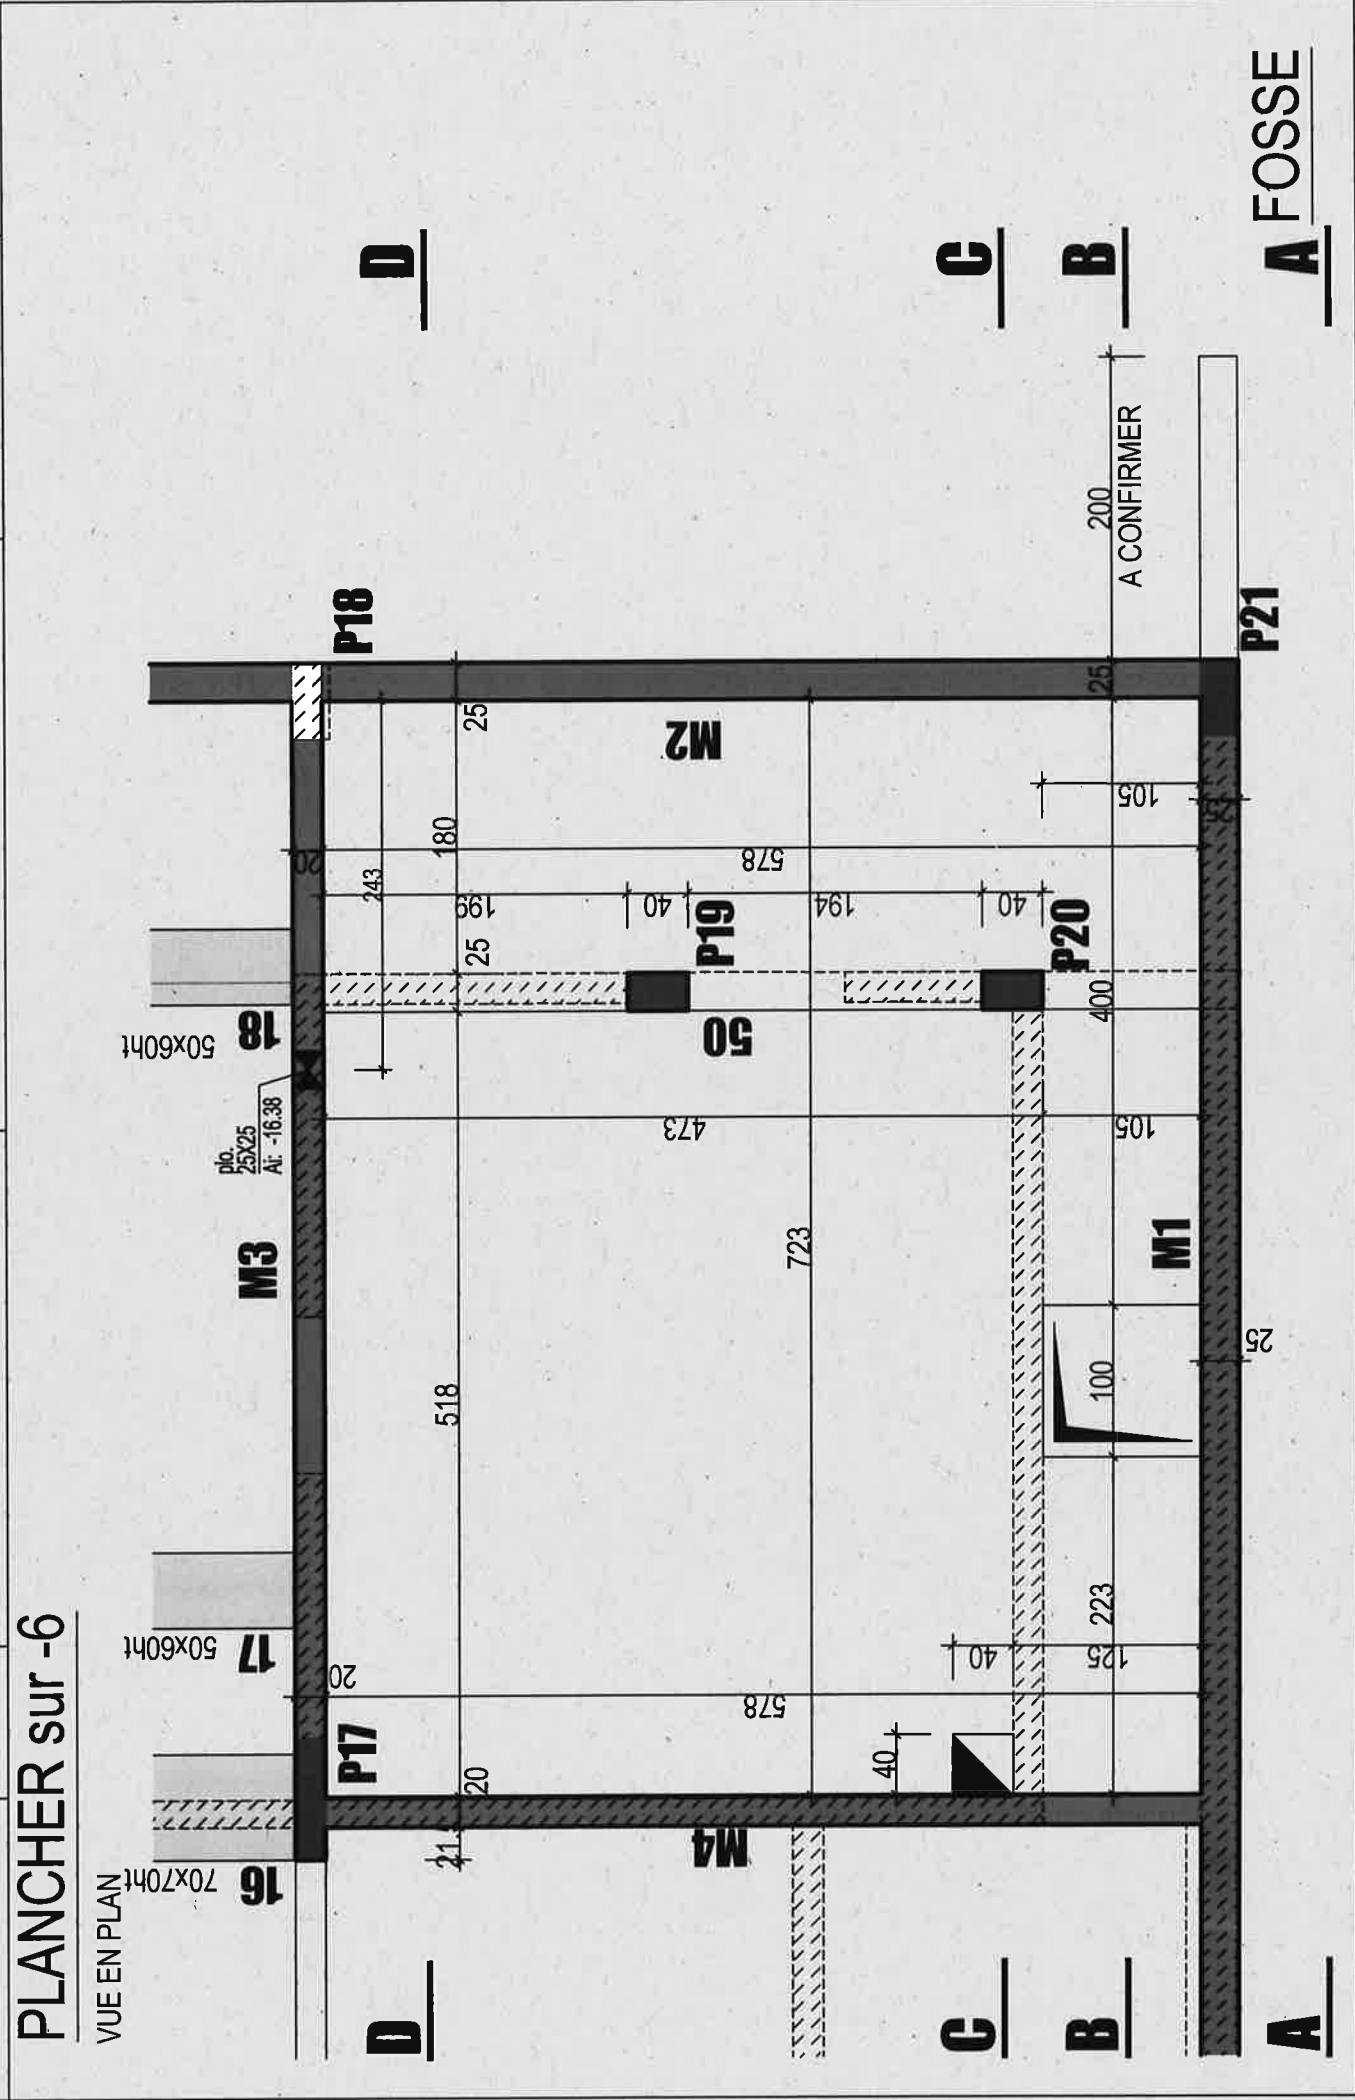


COUPE A

Ech: 1/50

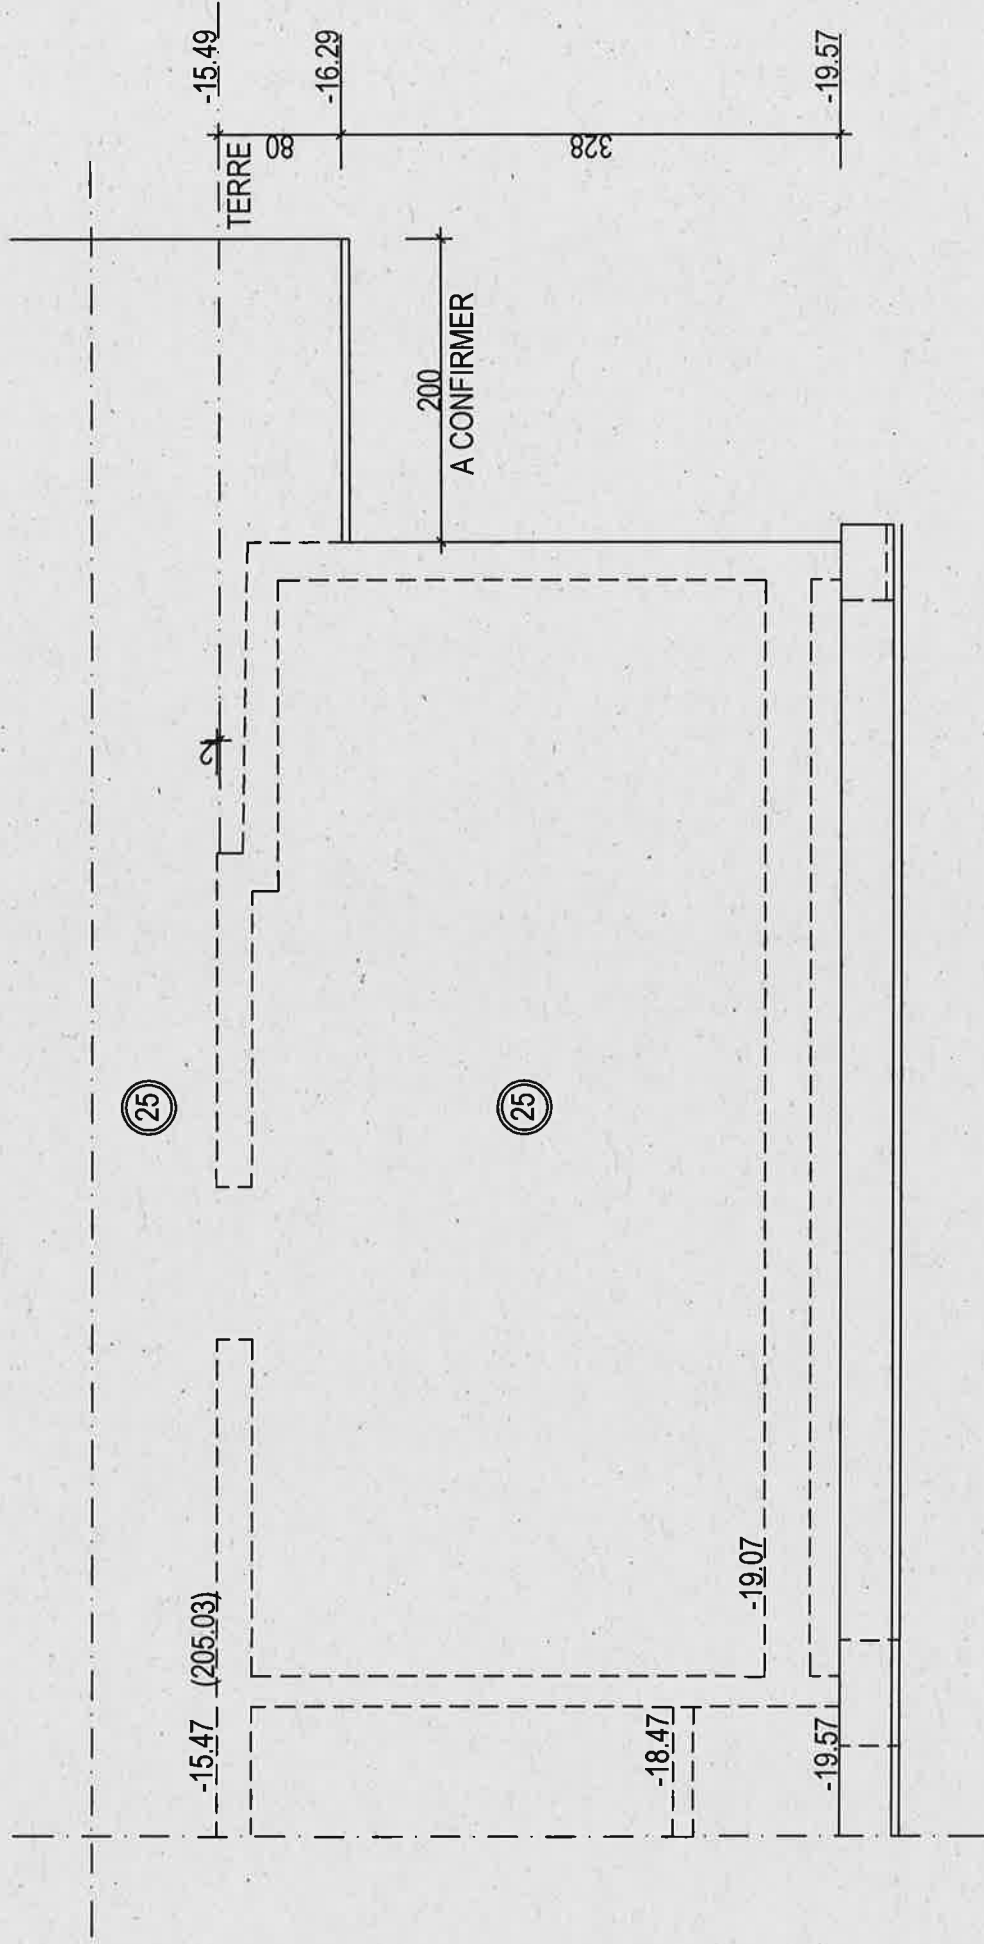

COUPE B


Ech: 1/50

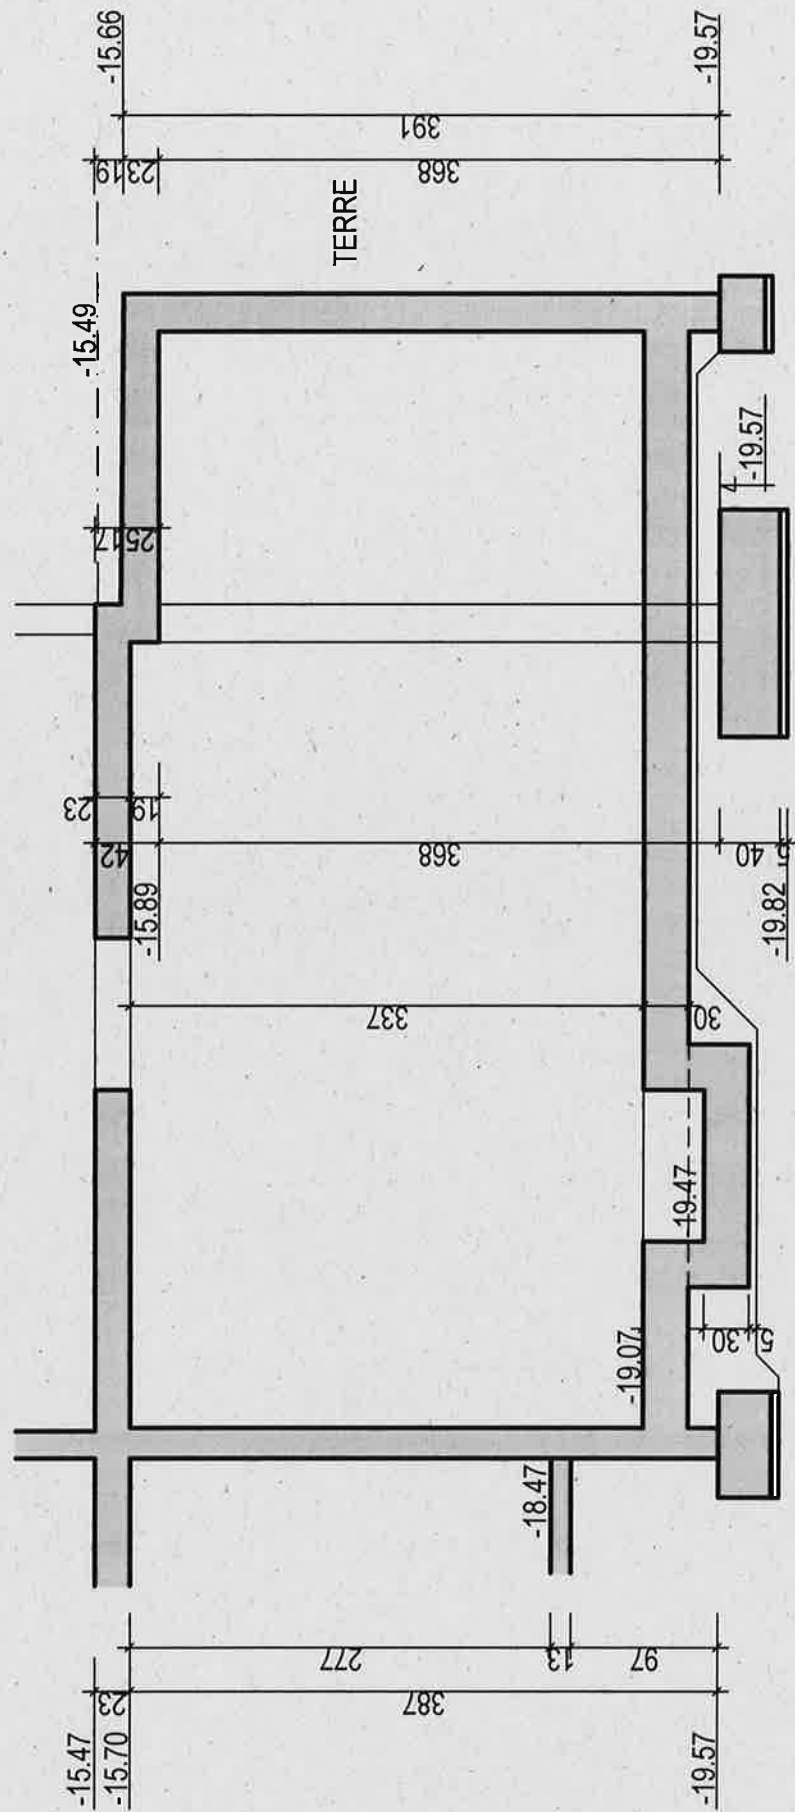

FOSSE

COUPE C


Ech: 1/50

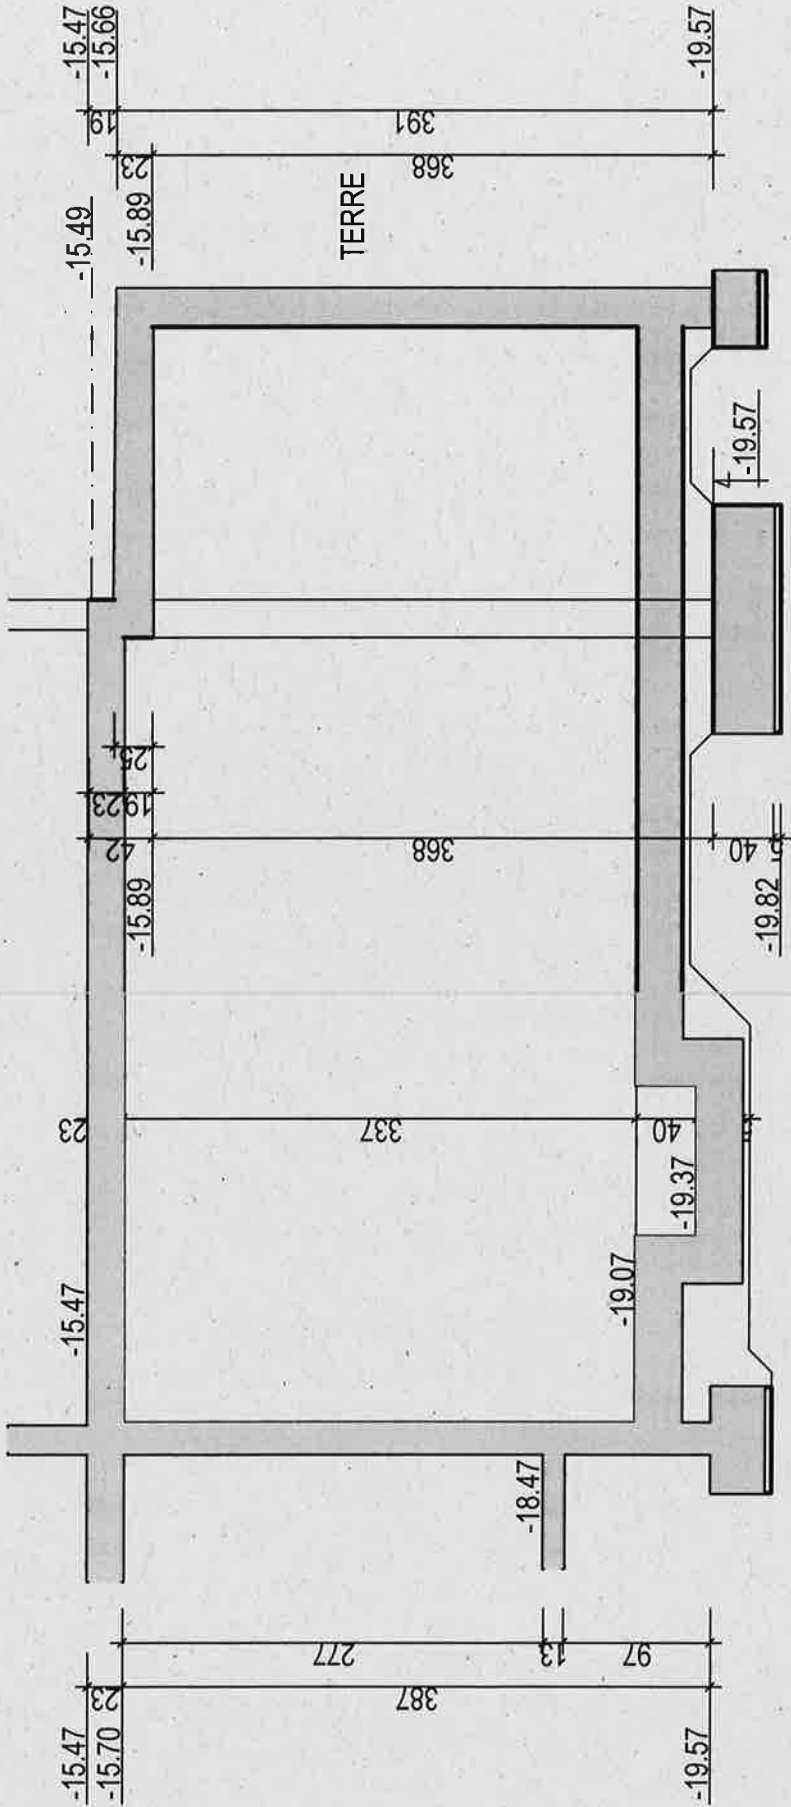



FOSSE

COUPE D

Ech: 1/50

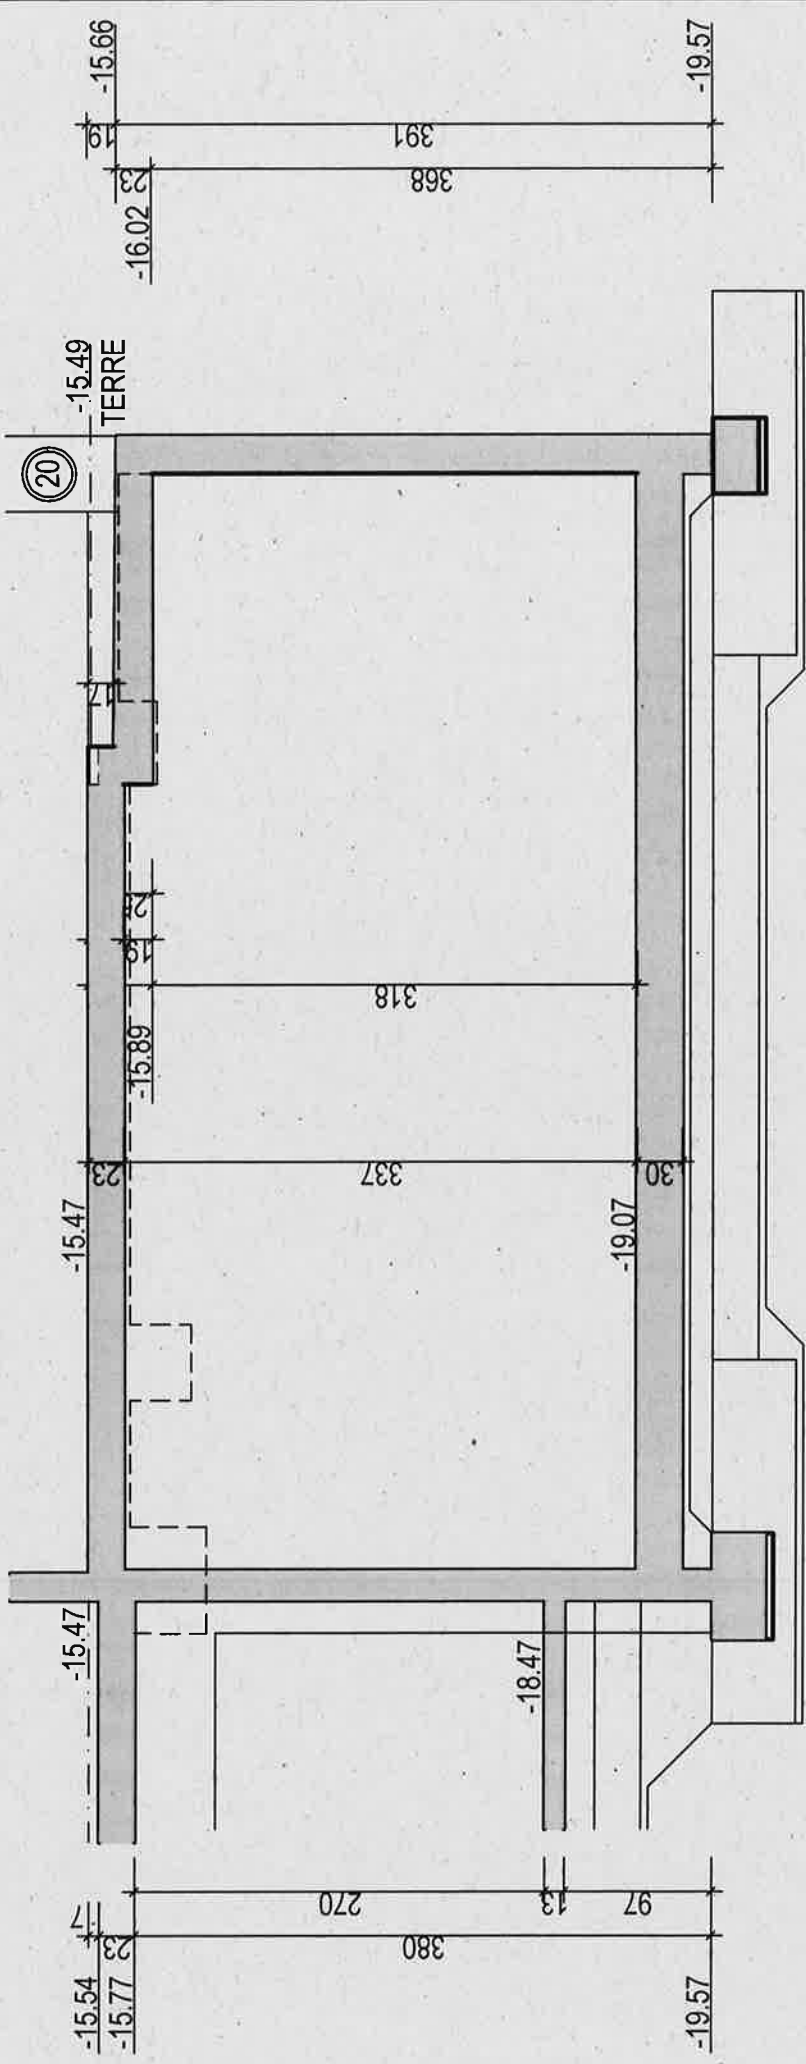


FOSSE

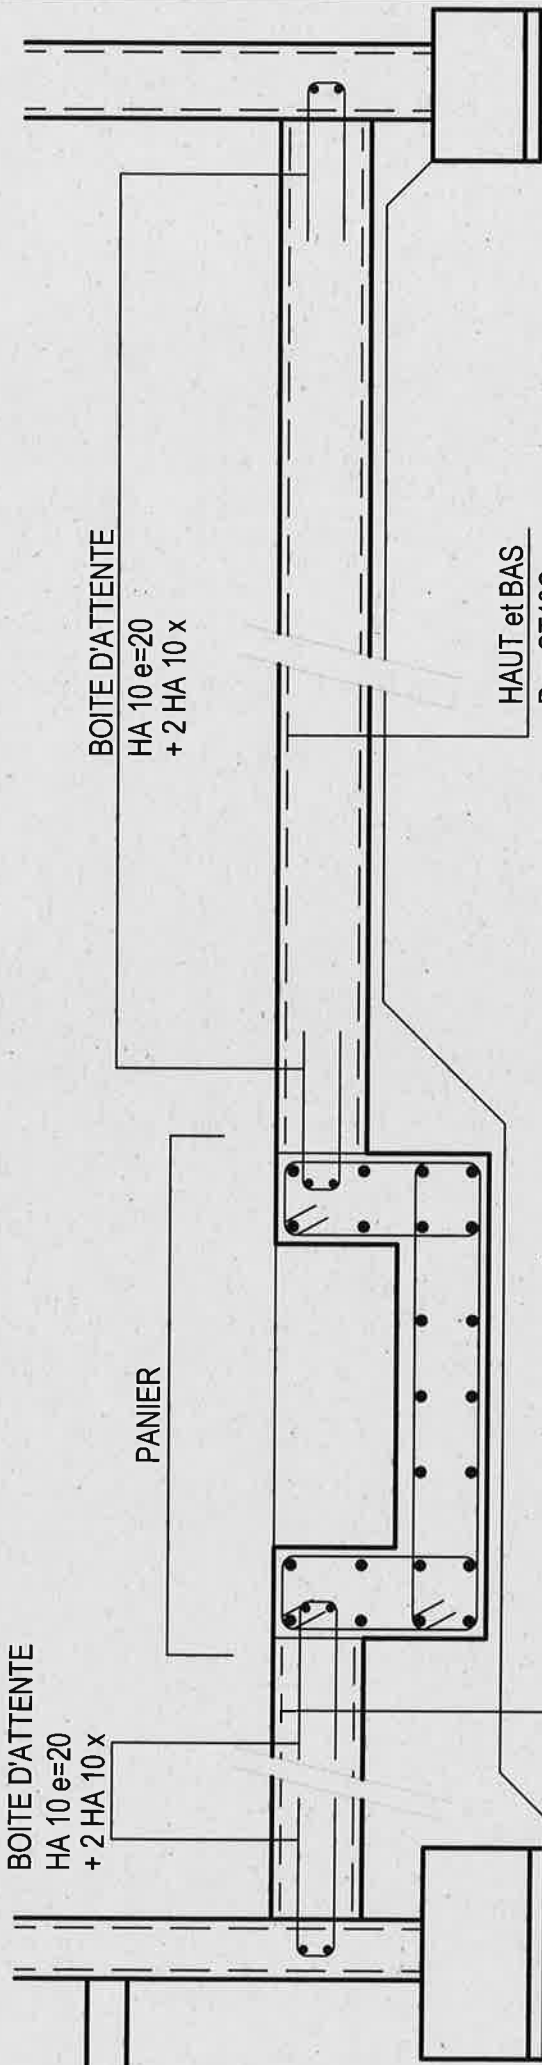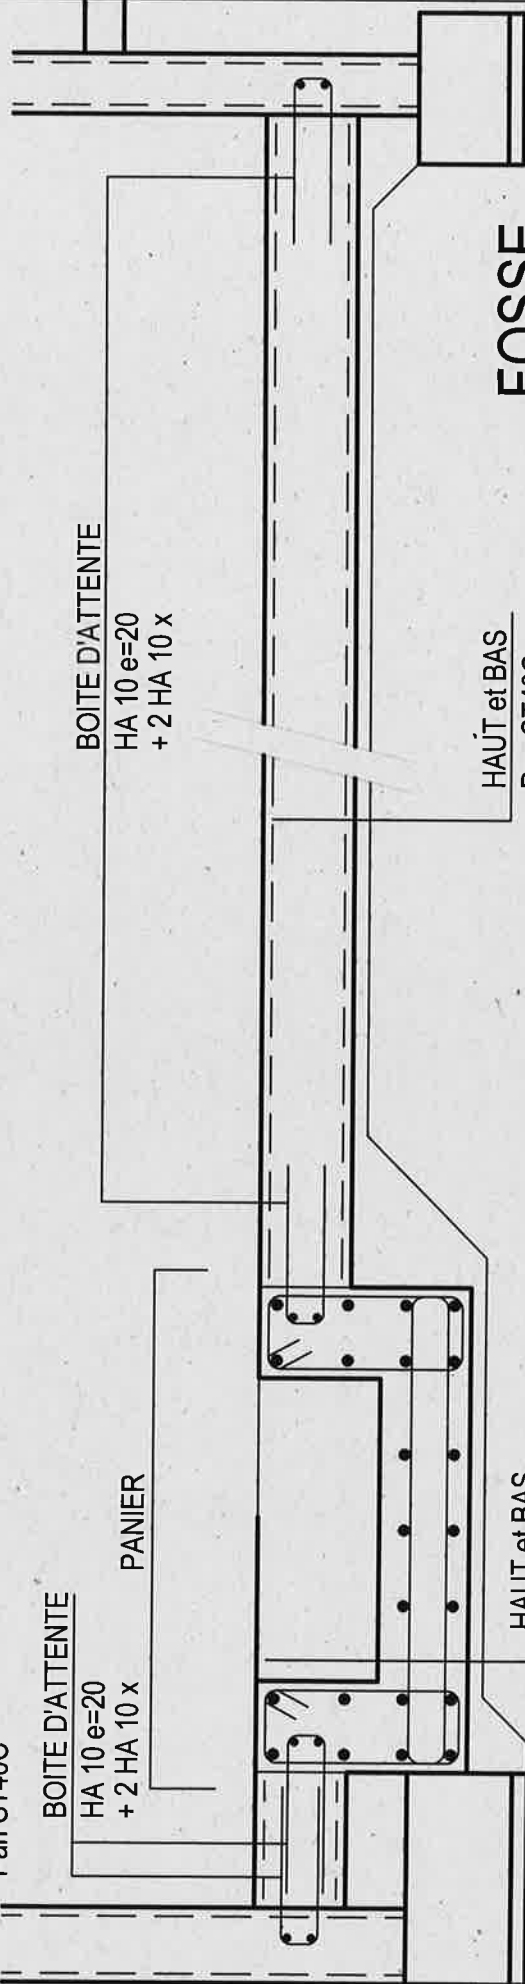AFF: S.13.12.118	Bât: B	LA MULATIERE-69350 La Mulatiere CREATION de LOGEMENTS	FONDATIONS au -6	Plan n° B 02	Page: 21
RADIER					
VUE EN PLAN					
					
FOSSE					
					


PANIER REGARD

Nombre: 1

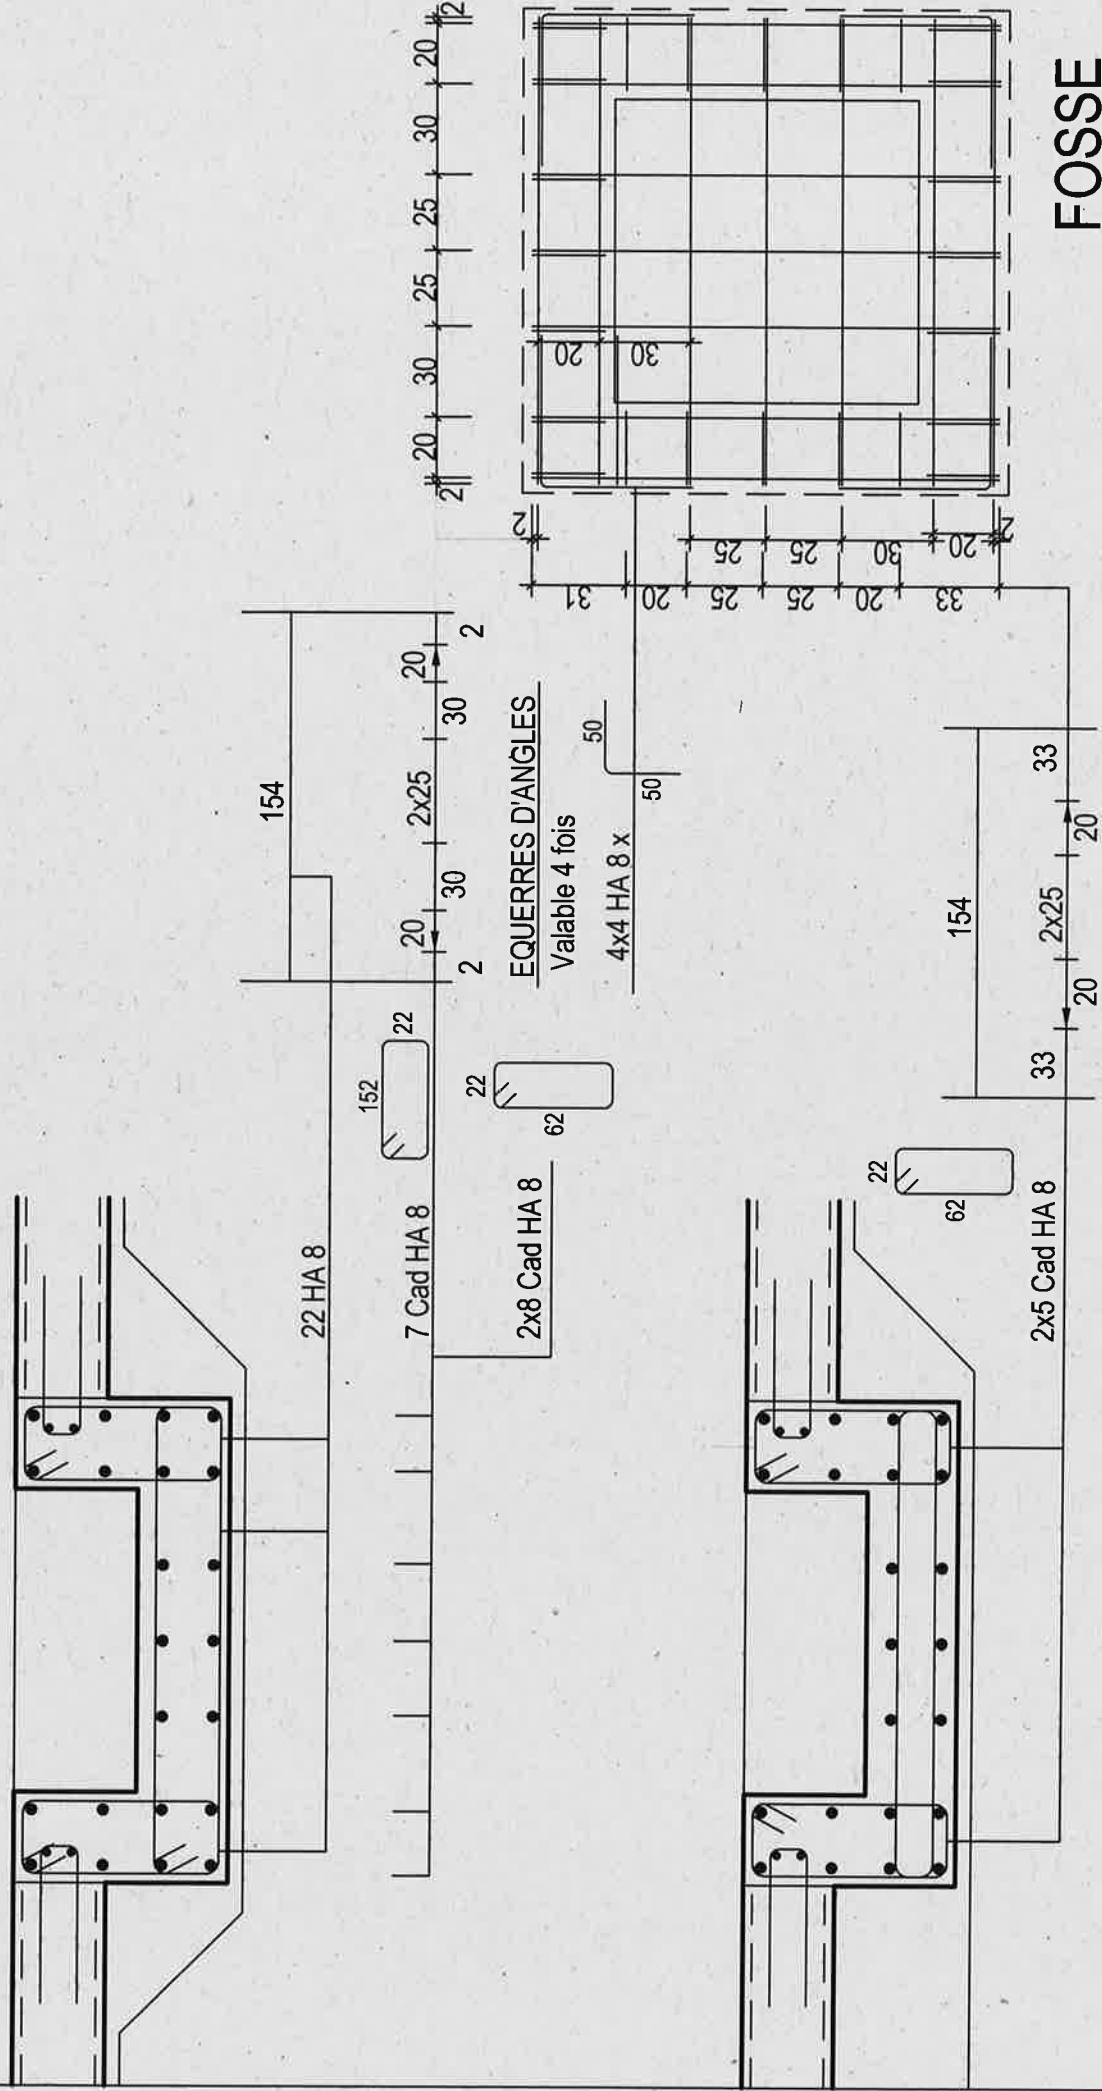


RADIER

ARMATURES DALLE

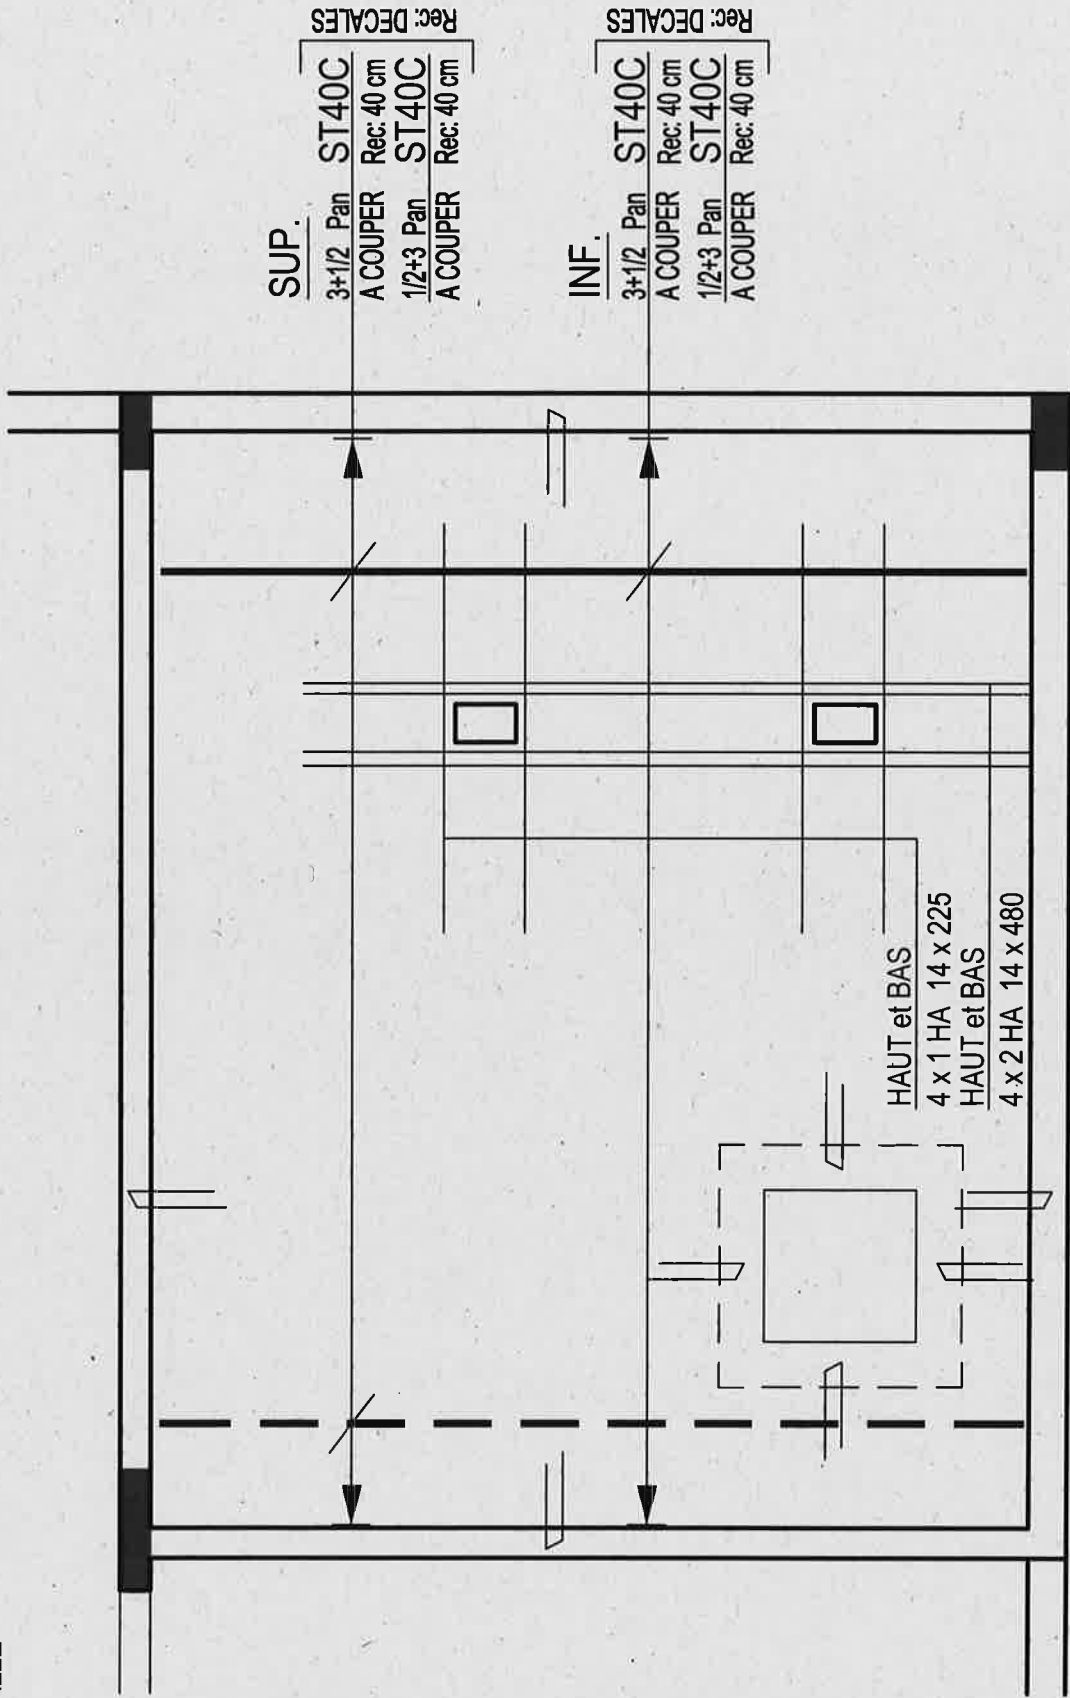

FOSSE

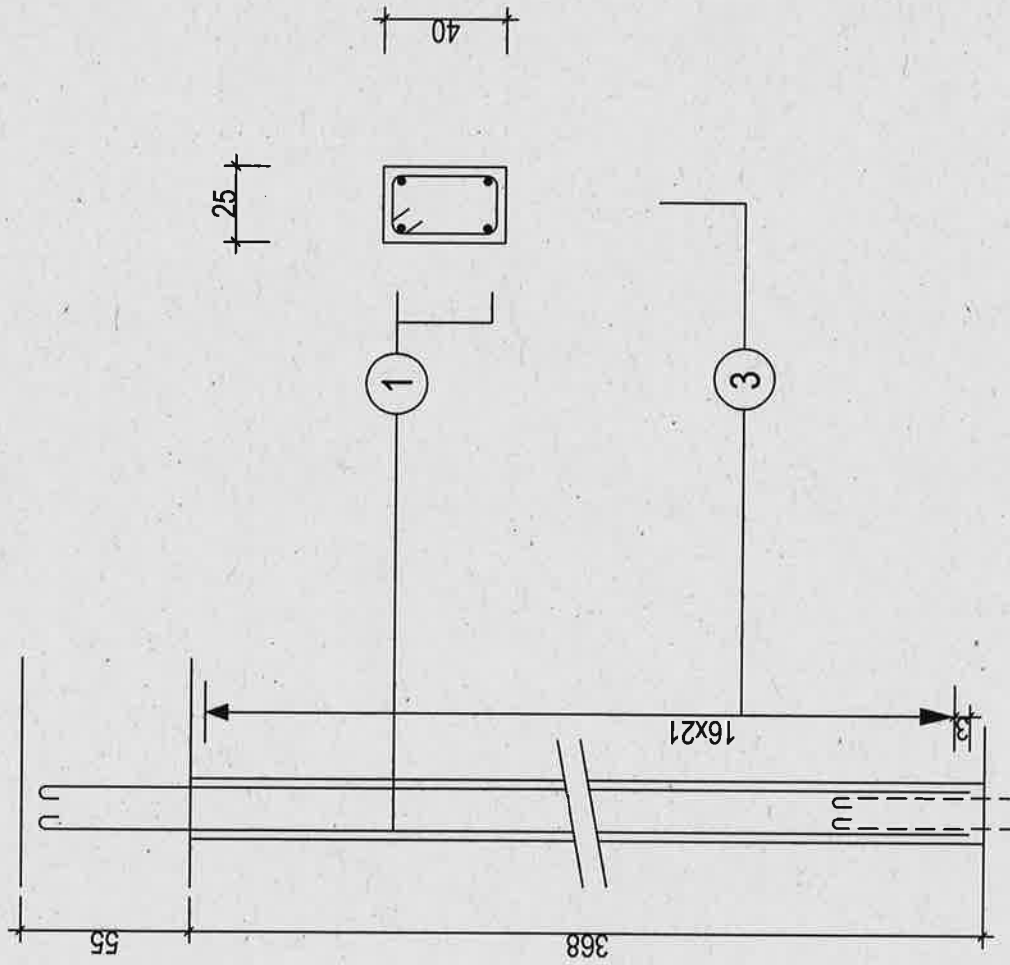AFF: S.13.12.118	Bât: B	LA MULATIERE-69350 LaMulatiere CREATION de LOGEMENTS	FONDATIONS au -6	Plan n° B 02	Page: 26
P19 Nombre: 1		P20 Nombre: 1			
25x40					
		①	4 HA 14 x	C 395	
		②			
		③	17 HA 6 x	34 19	
		④			
		⑤			
		⑥			
		⑦			
		⑧			
		⑨			
		⑩			
		⑪			
		⑫			
		⑬			
		⑭			
		⑮			

AFF: S.13.12.118		Bât: B	LA MULATIERE-69350 LaMulatiere CREATION de LOGEMENTS		FONDACTIONS au -6		Plan n° B 02		Page: 27						
P21 Nombre: 1 25x50					BOITE D'ATTENTE HA 10 e=20 + 2 HA 10 x 370 328 50 17x18 3 34 17										
1	6 HA 12 x	C		370											
2															
3	18 HA 6 x	34		17											
4	18 HA 6 x	J17													
5															
6															
MURS

M1

M2

M3

M3

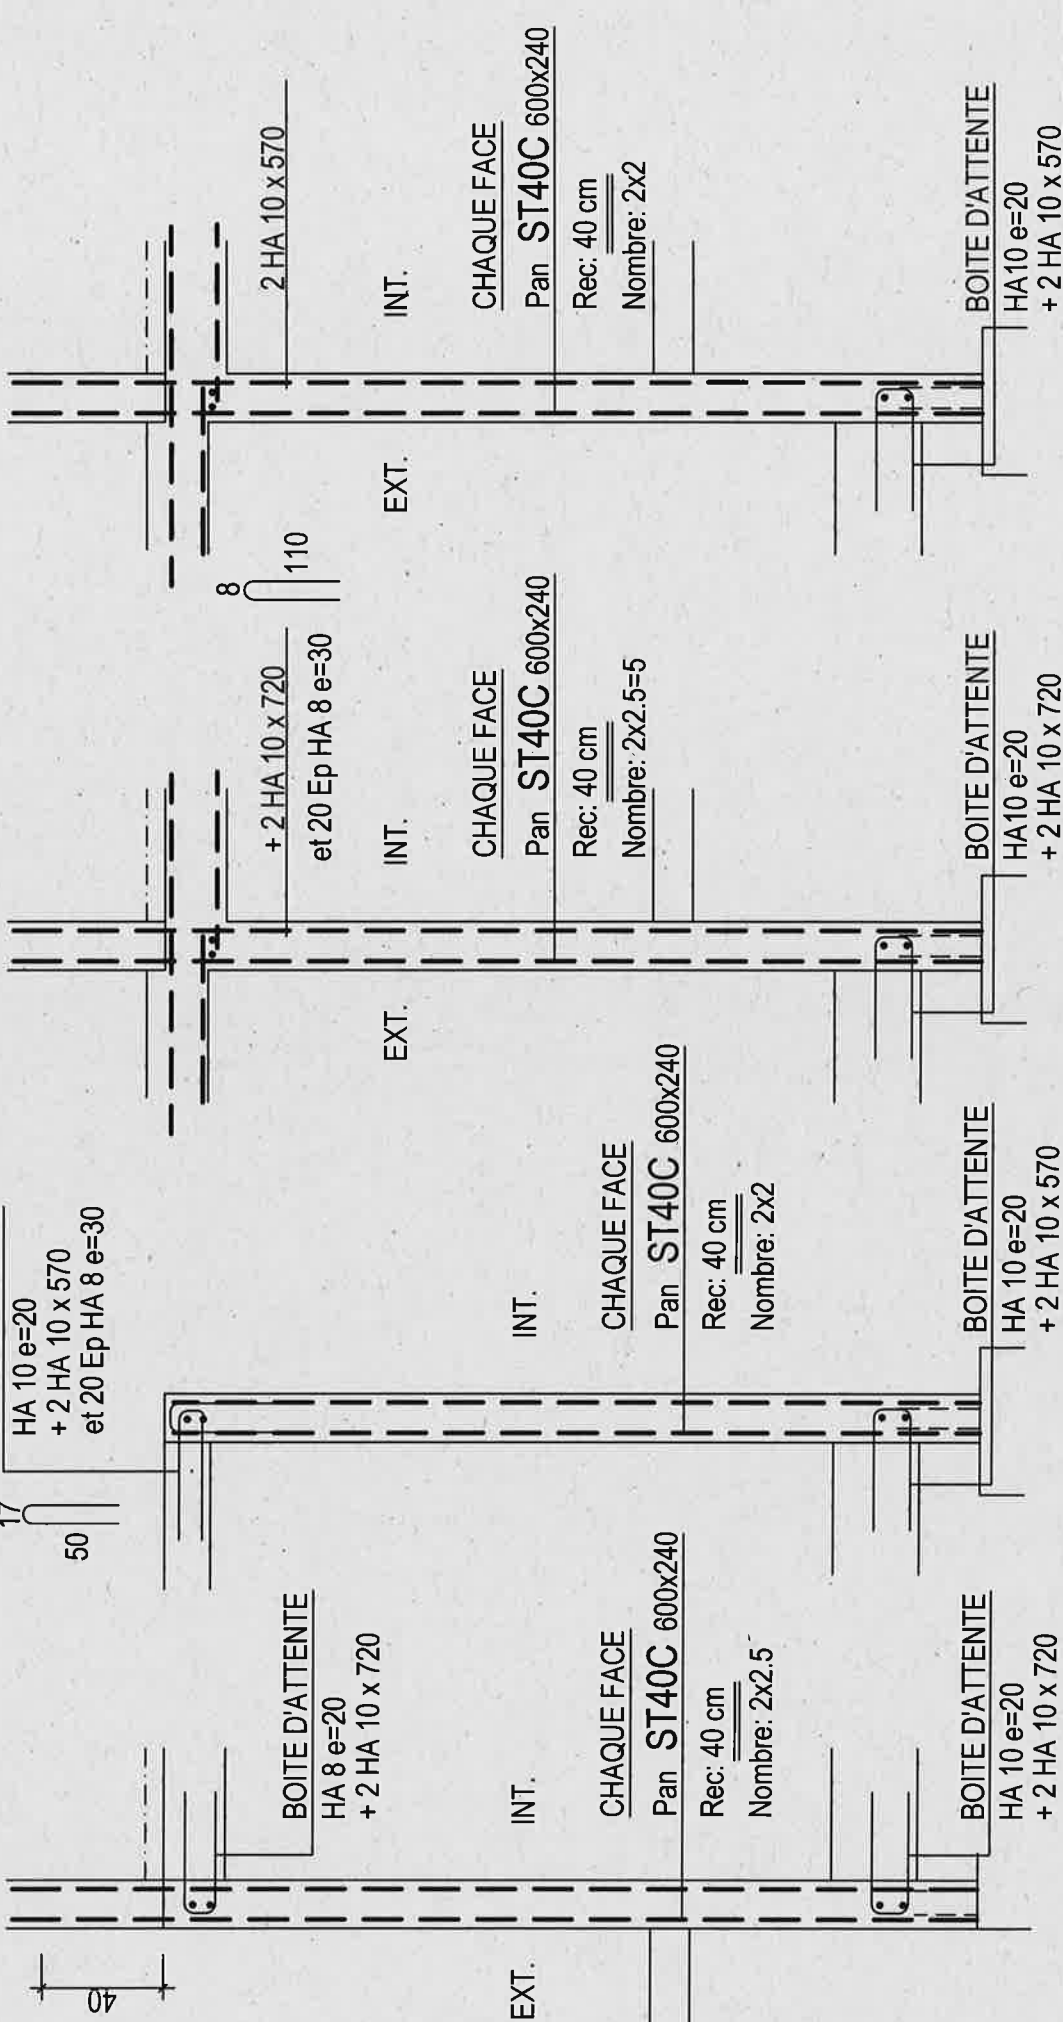

FOSSE

Bât: B	LA MULATIERE-69350 La Mulatiere CREATION de LOGEMENTS	FONDACTIONS au -6	Plan	B 02	Page: 29
--------	--	-------------------	------	------	----------

<

