

NOHAO

Chemin de Fontanière-69350 La Mulatière

Création de logements

Les entreprises réalisant les travaux devront tenir compte des derniers plans architecte lors de la réalisation des travaux
Les plans du be MATTE ne doivent servir qu'au corps d'état concerné et doivent être des plans d'exécution.

ARCHITECTE(S): Atelier DE LA PASSERELLE M.O. Délégué: .
BET STRUCTURE: BET MATTE M.O.: .
BET FLUIDES: PRELEM CSPS: PSO ingénierie
ECONOMISTE: EXECO M.O.E.: SUD EST COORDINATION
BUREAU DE CONTROLE: VERITAS ENTREPRISE(S): Fontanel-pbc

Bât: B

MURS RAMPE NORD

ARMATURES

DOE

INDICE	DATE	MODIFICATIONS
A		

Aciers HA (T) FeE500
Aciers Doux (Ø) FeE 235
Aciers TS FeE 500
Béton fc28 >= 25MPa
Enrobage = 3 cm

PLAN N°
B03 0

DATE : 30-10-2015

MATTÉ

BUREAU D'ÉTUDES
STRUCTURES ET FLUIDES

119 BOULEVARD STALINGRAD 69100 VILLEURBANNE

Tél. 04 72 44 02 87 Fax 04 72 44 26 59

E-mail : bet@matte.fr

Dessiné par : J.BONDETTI


Contrôlé par : P. LIN

Ech :


Affaire N°
S.13.12.118

MS1


COUPE

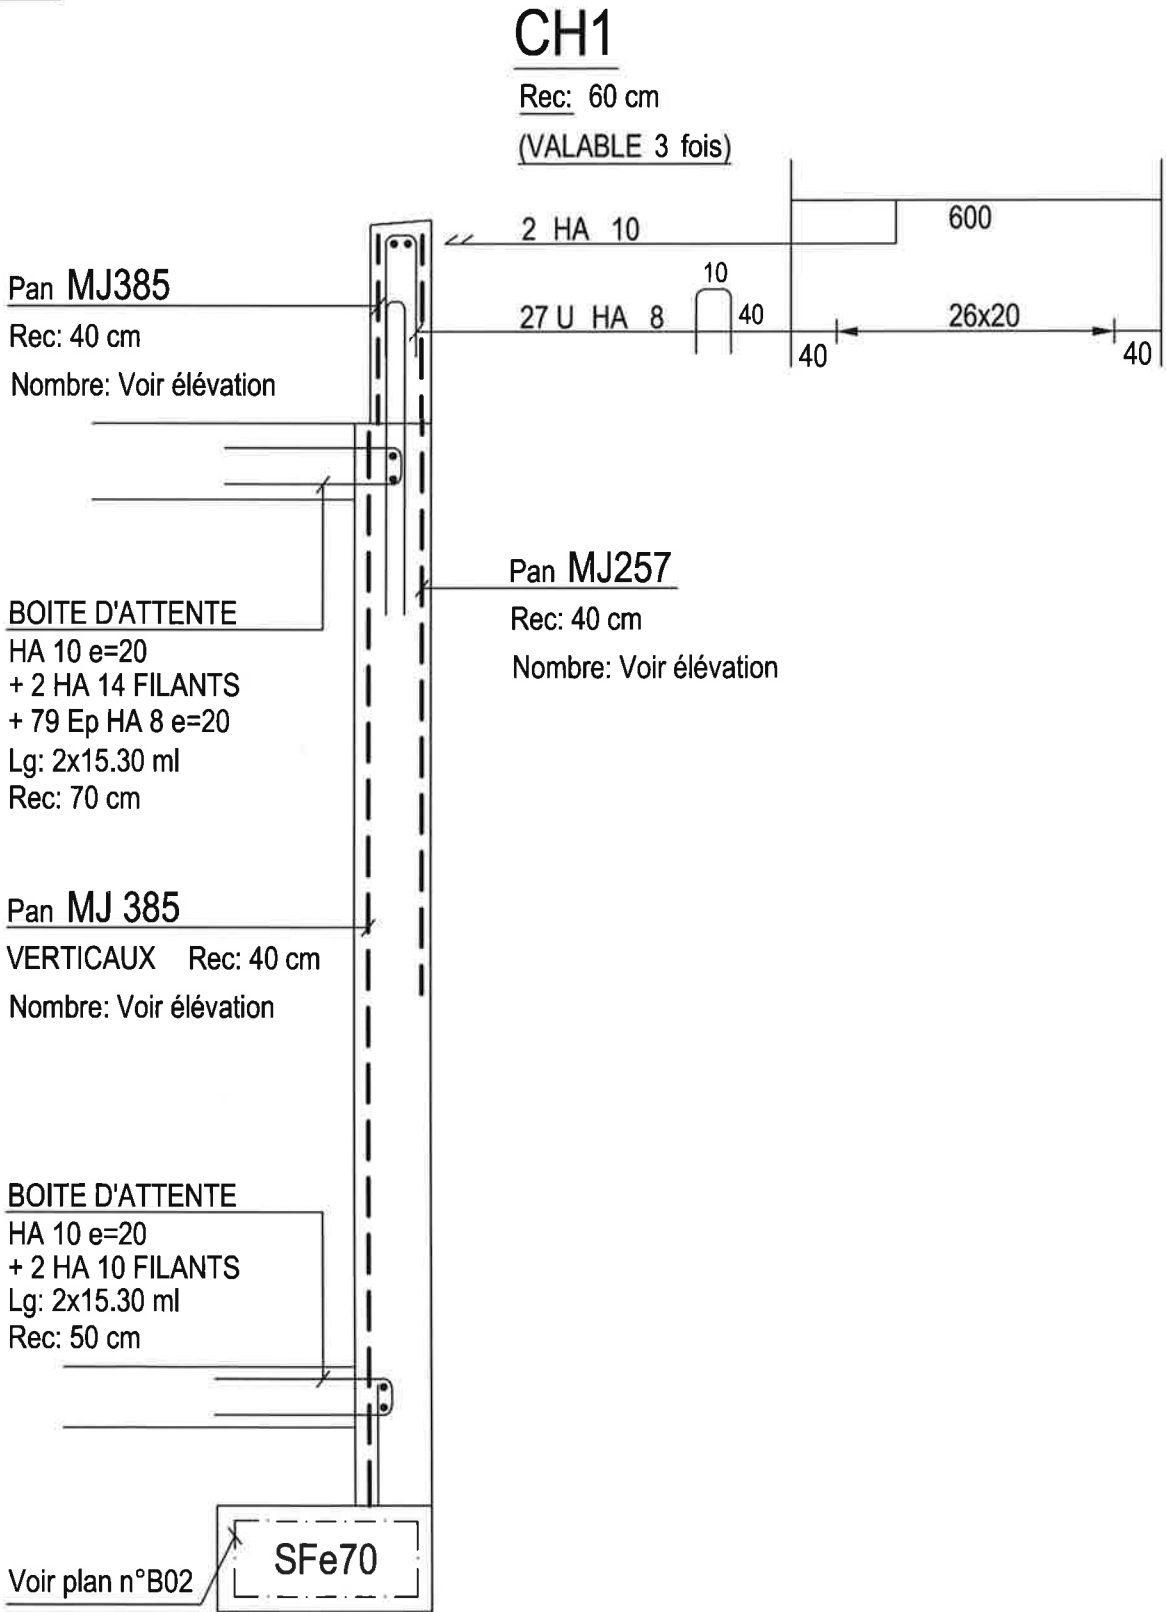

ARMATURES TETES DE MURS

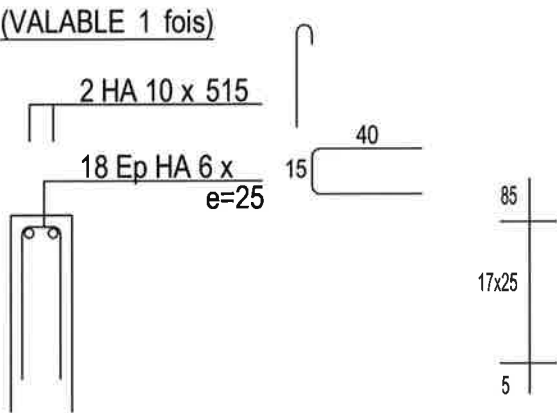


MS1
ELEVATION

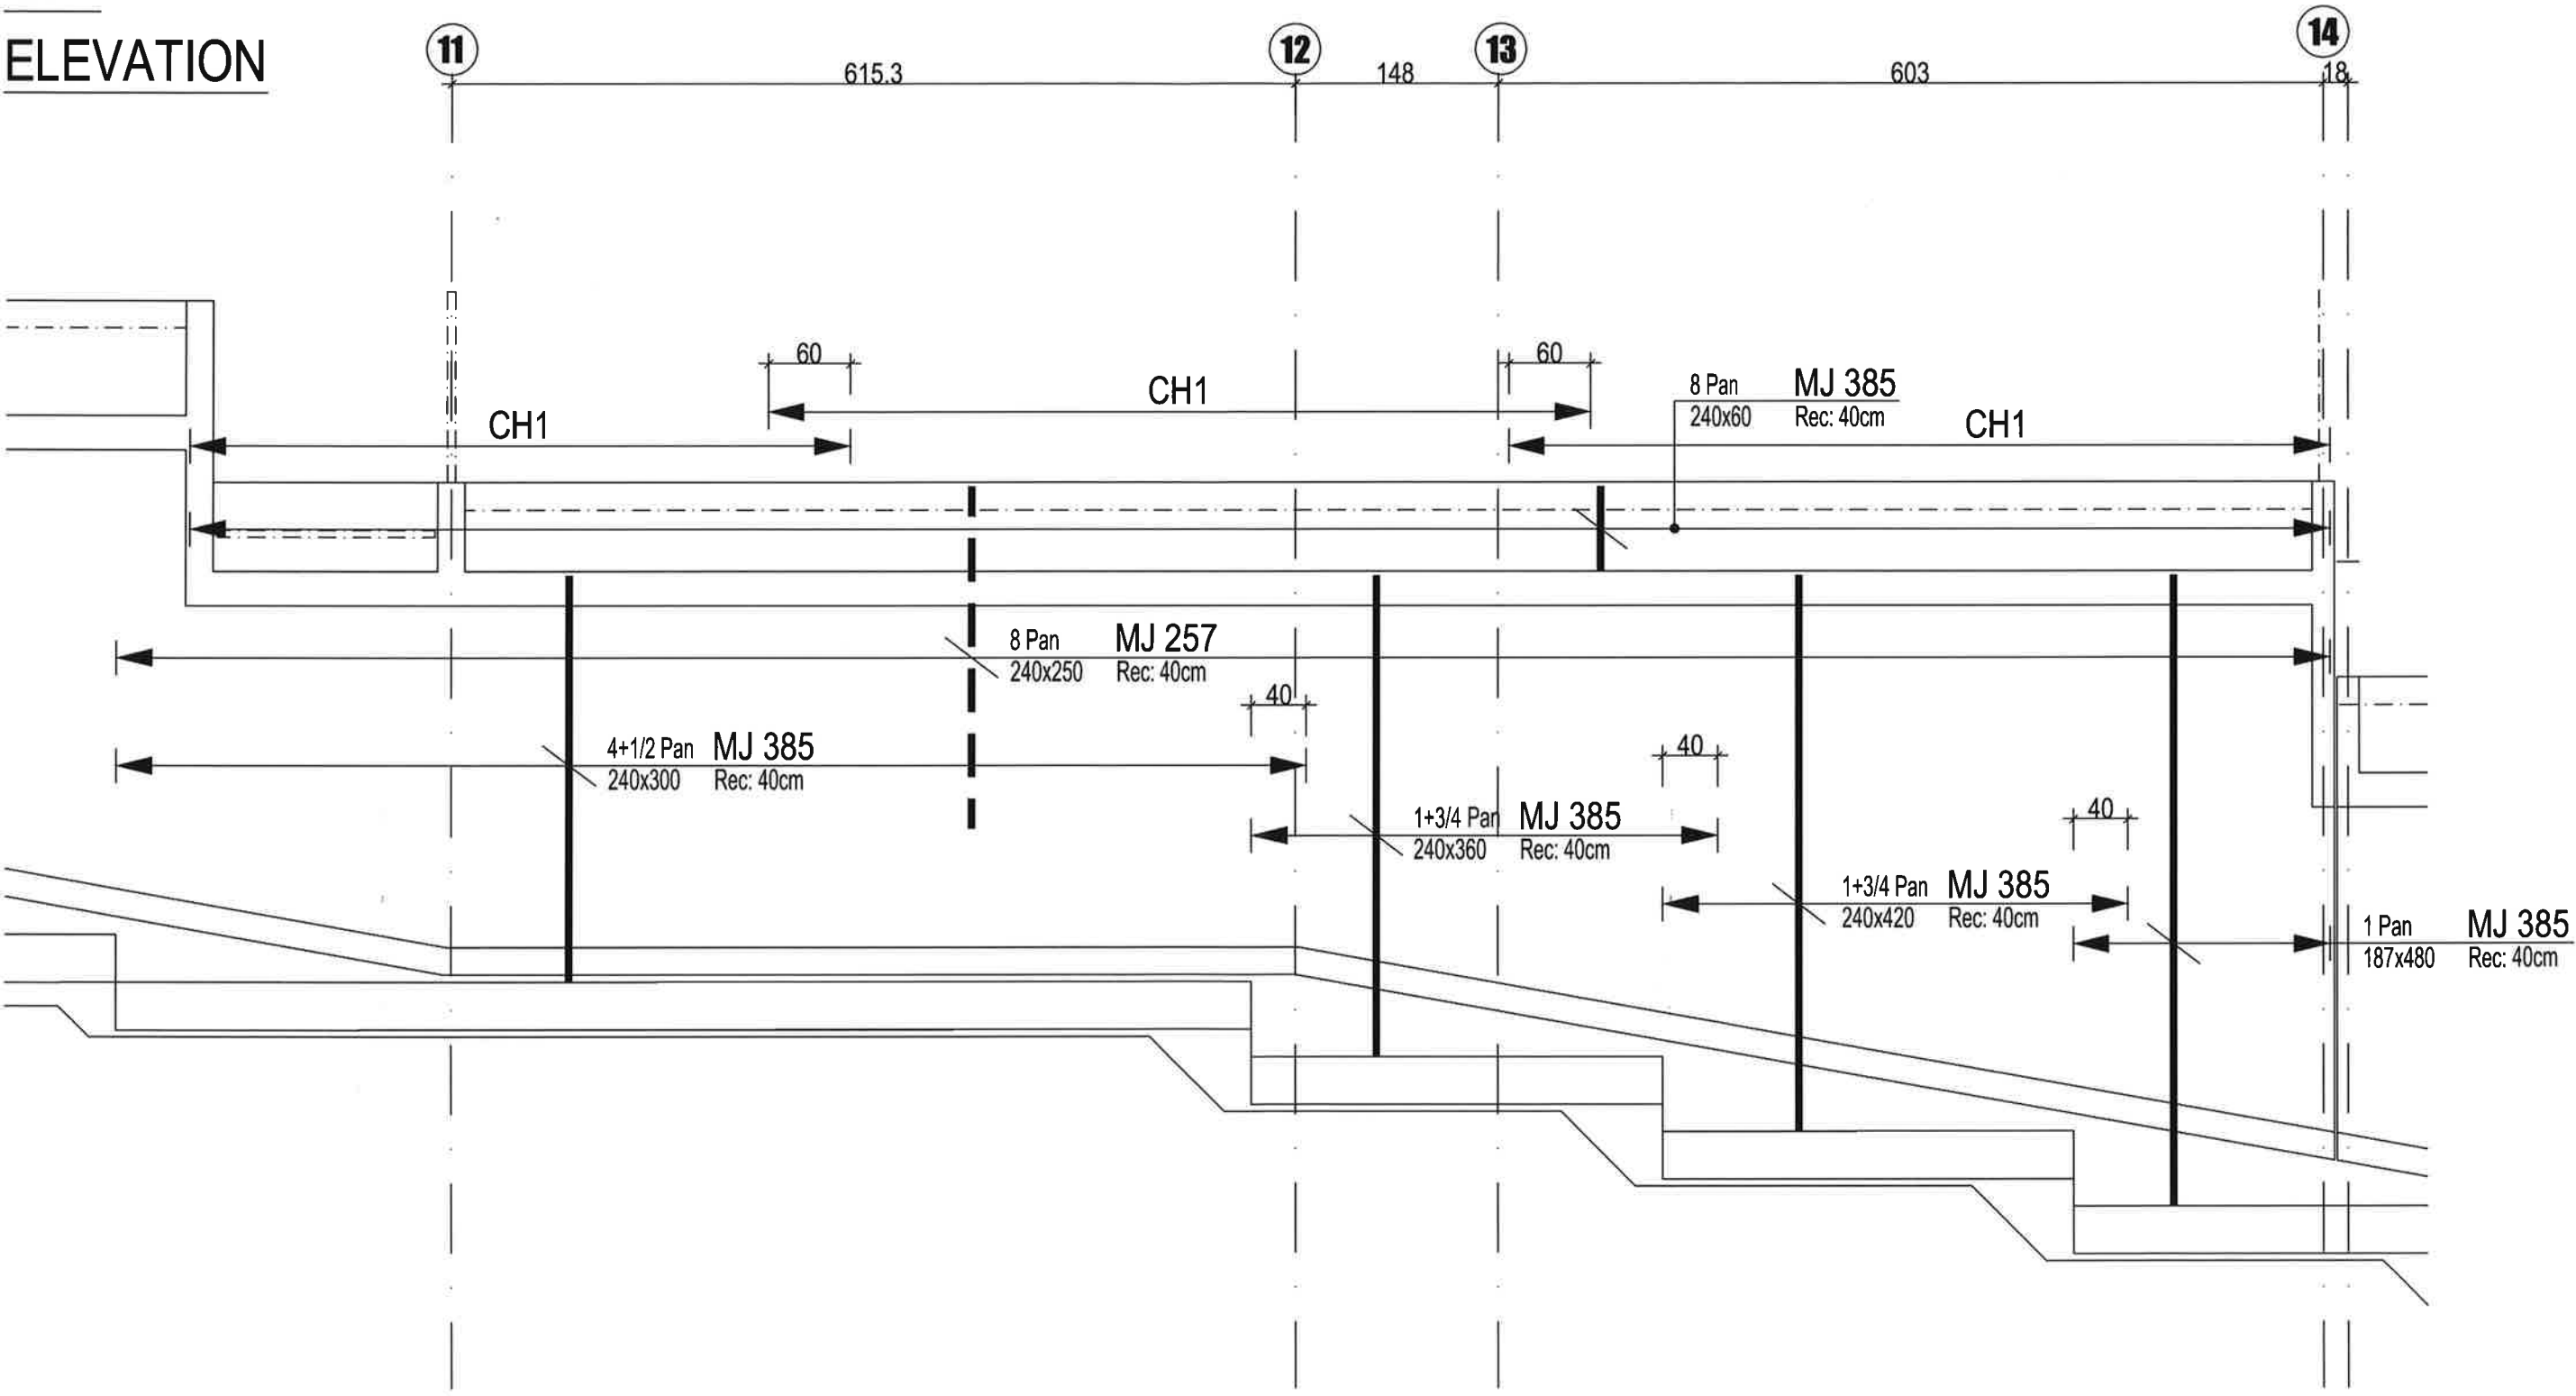


MS2 + MS3 + MS3a

ELEVATION

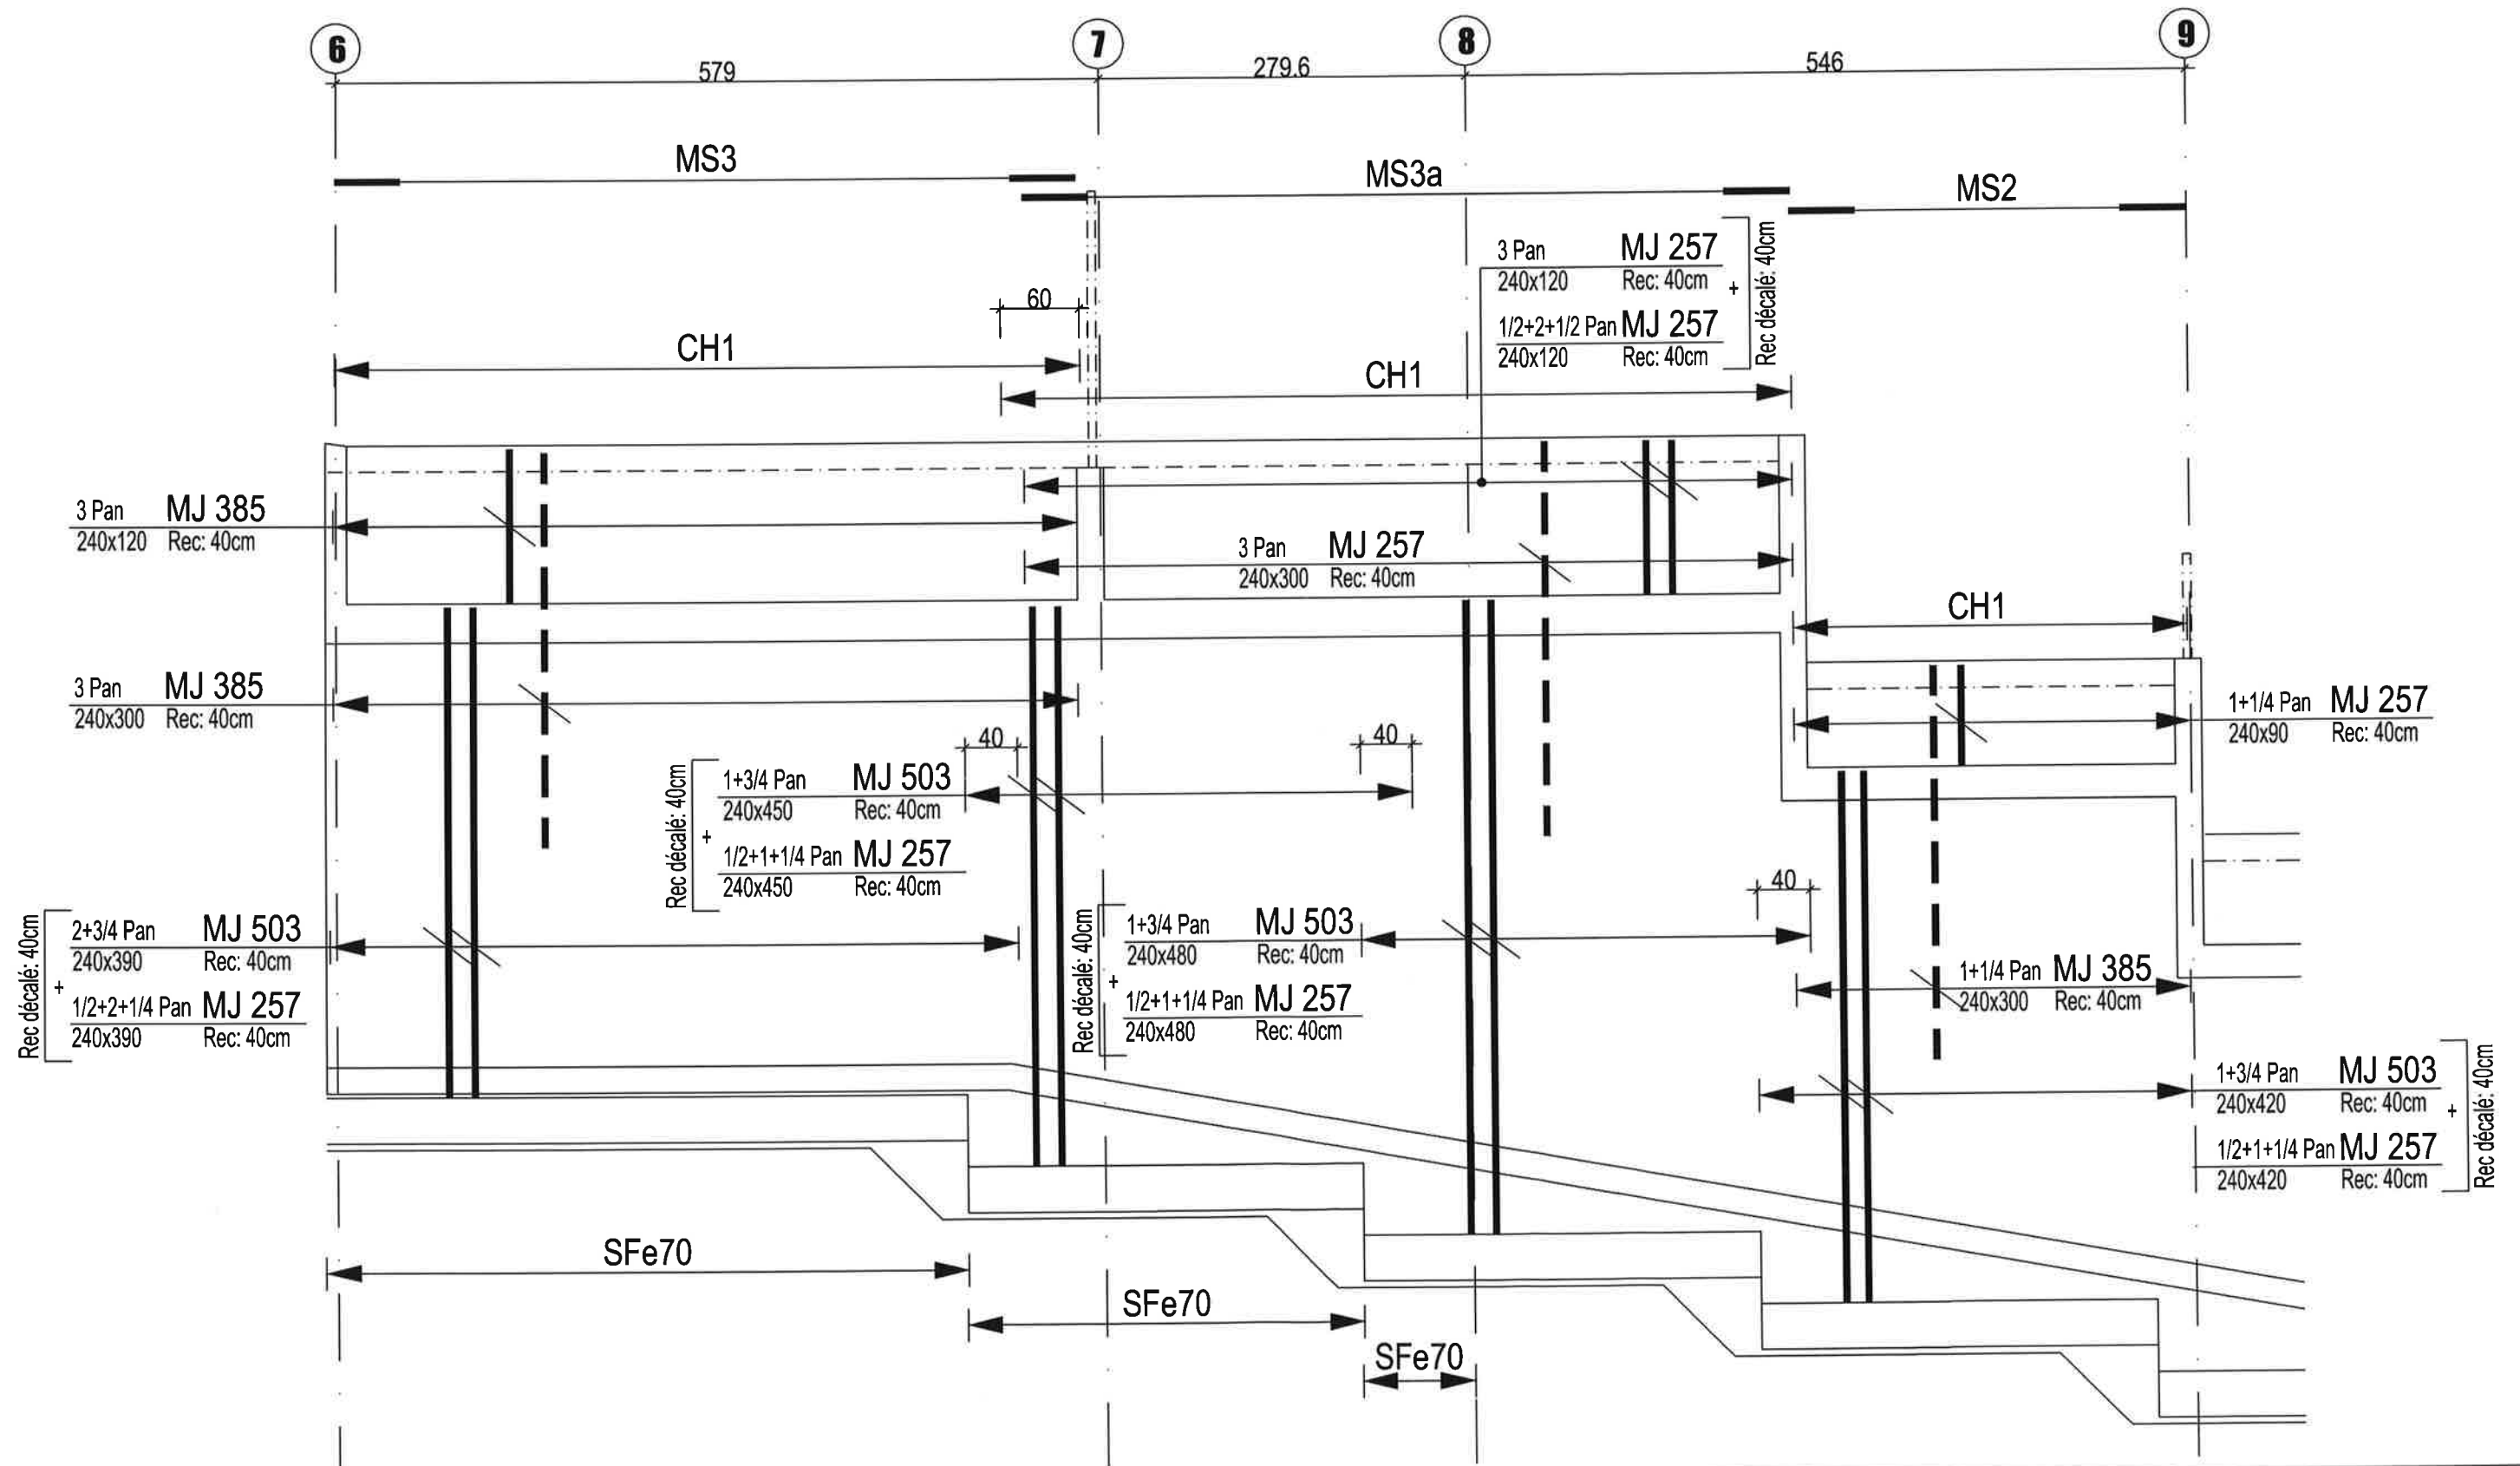


MS2

COUPE

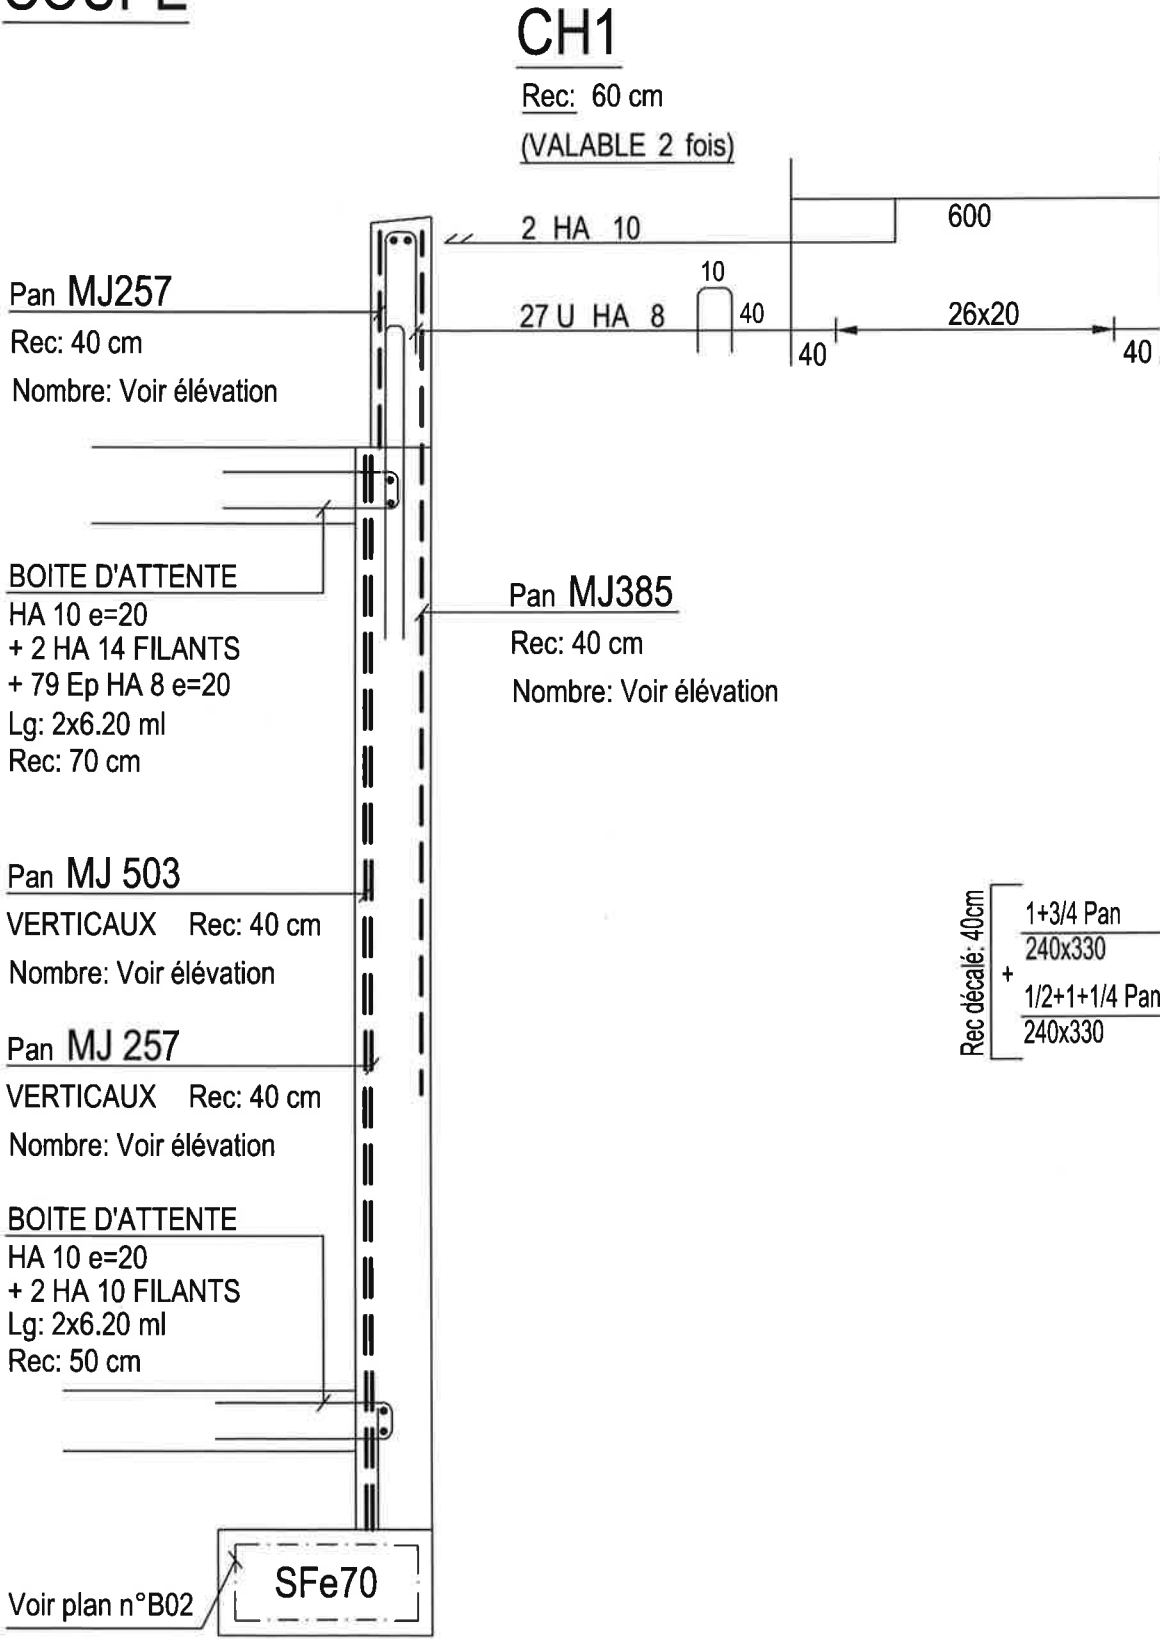


ELEVATION

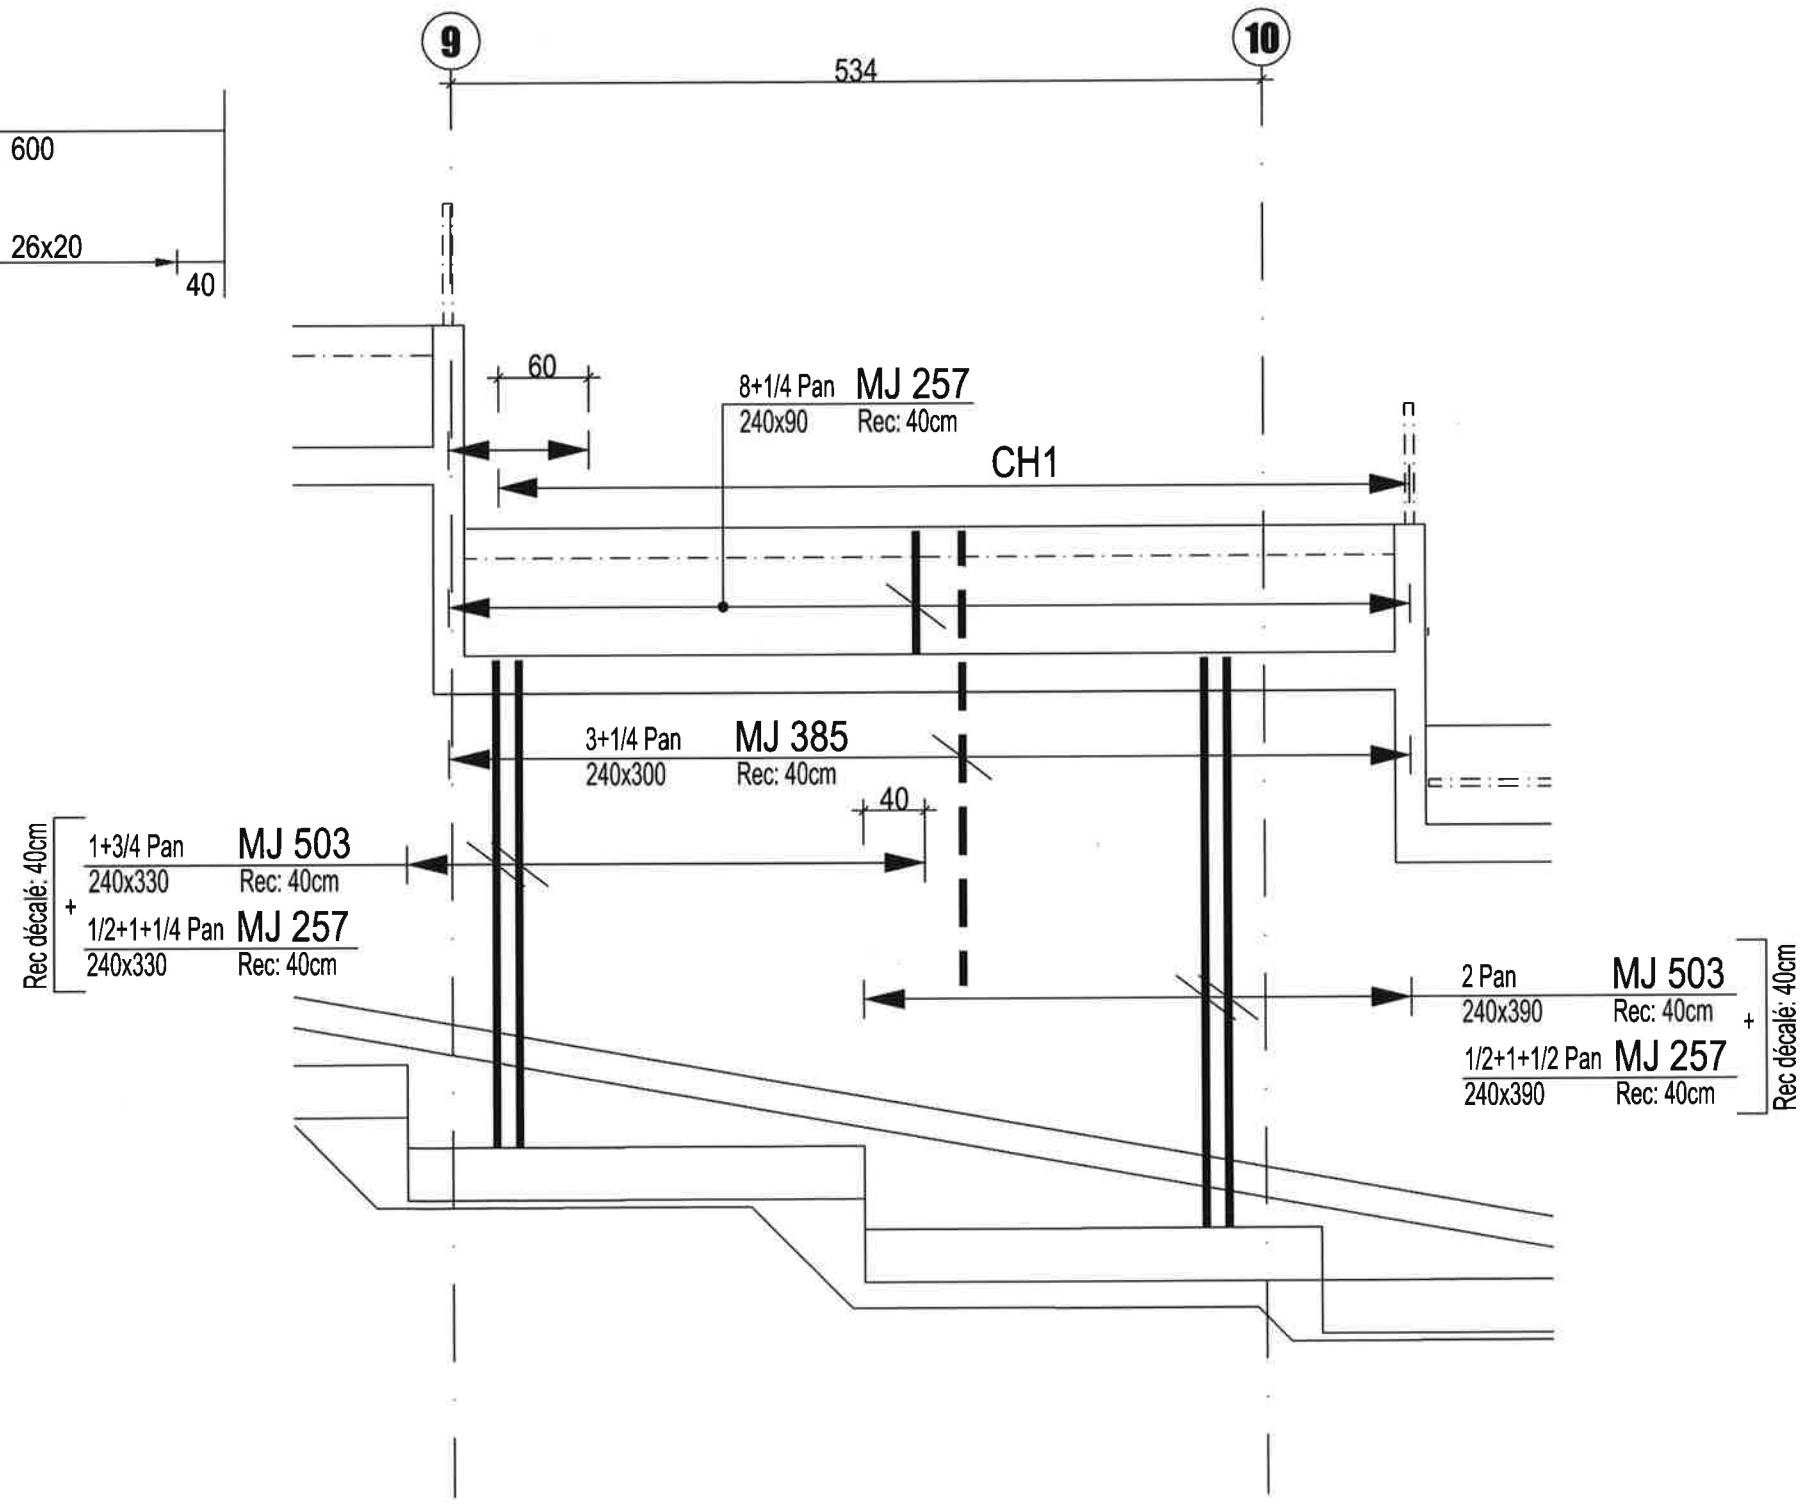


MS3

COUPE

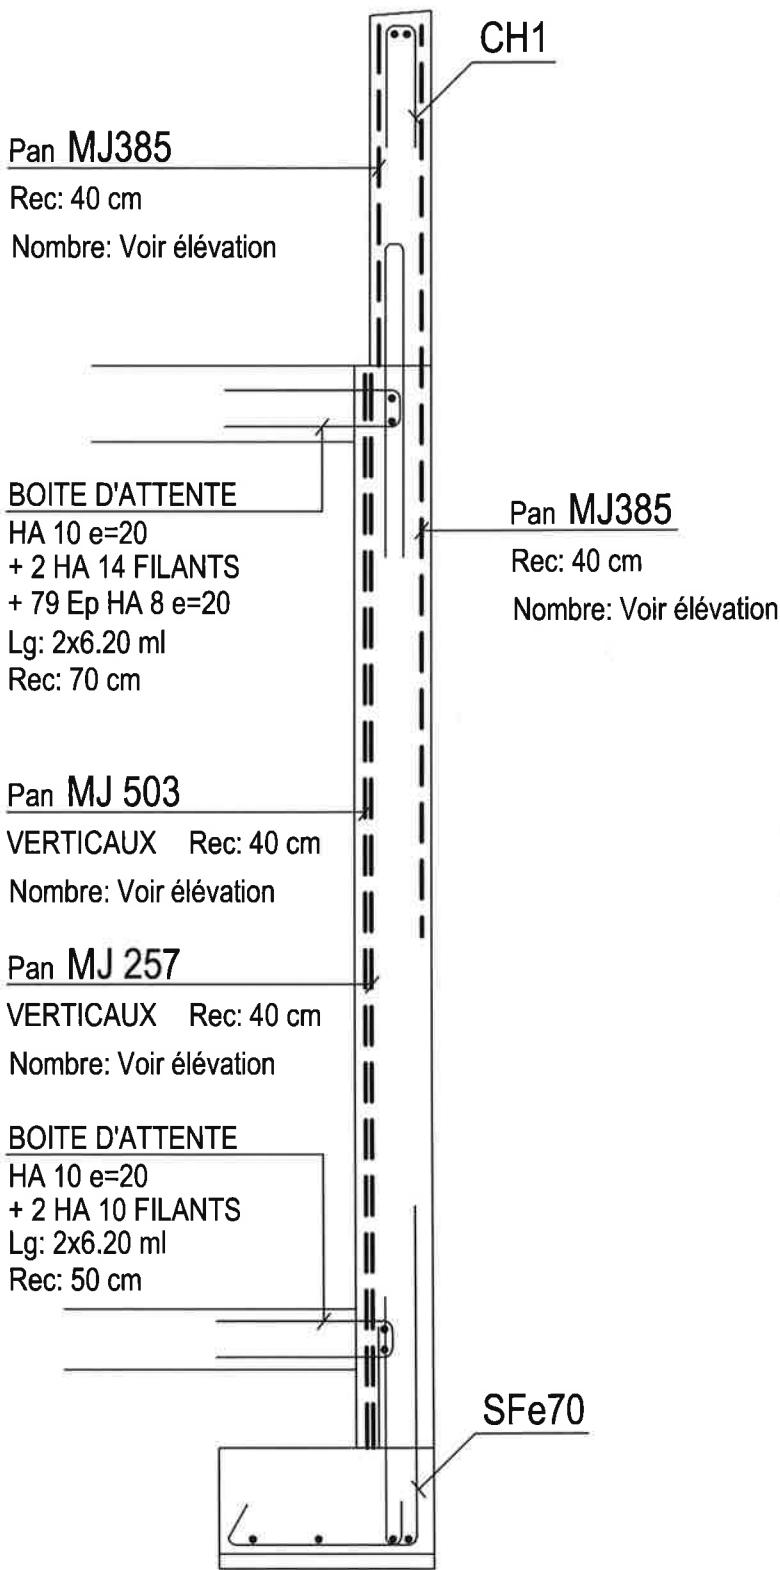


MS3a

COUPE

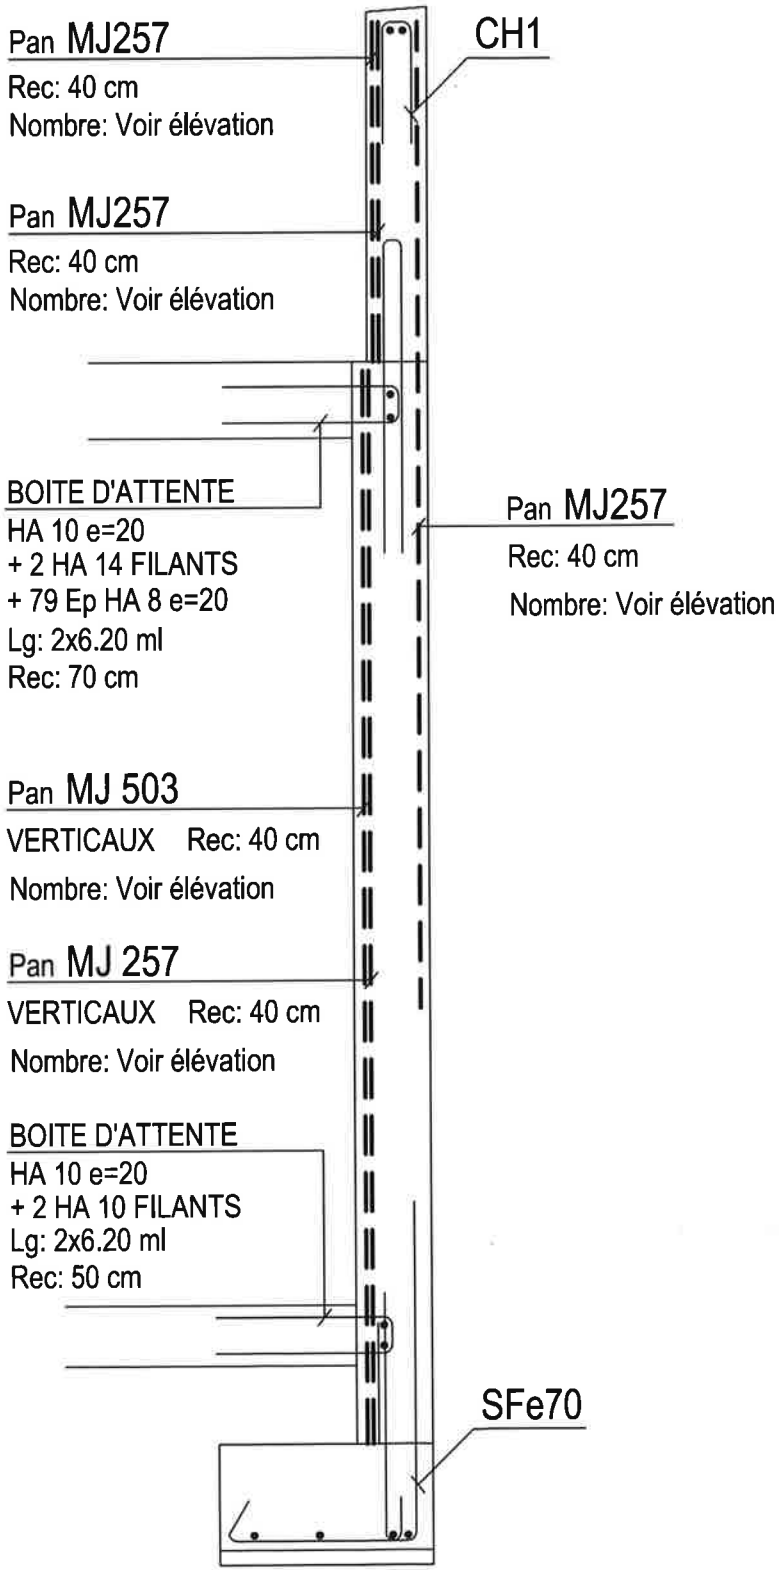


CH1

Rec: 60 cm
(VALABLE 3 fois)

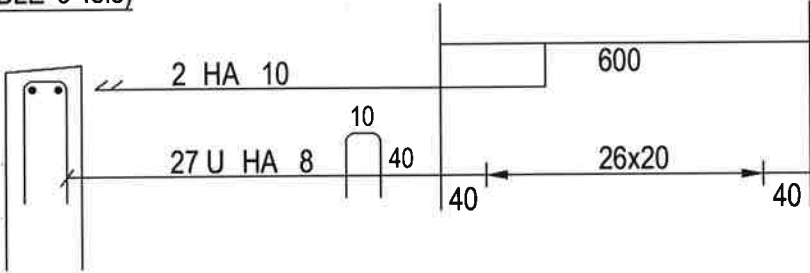


SFe70

Rec: 50 cm
Nombre: 2

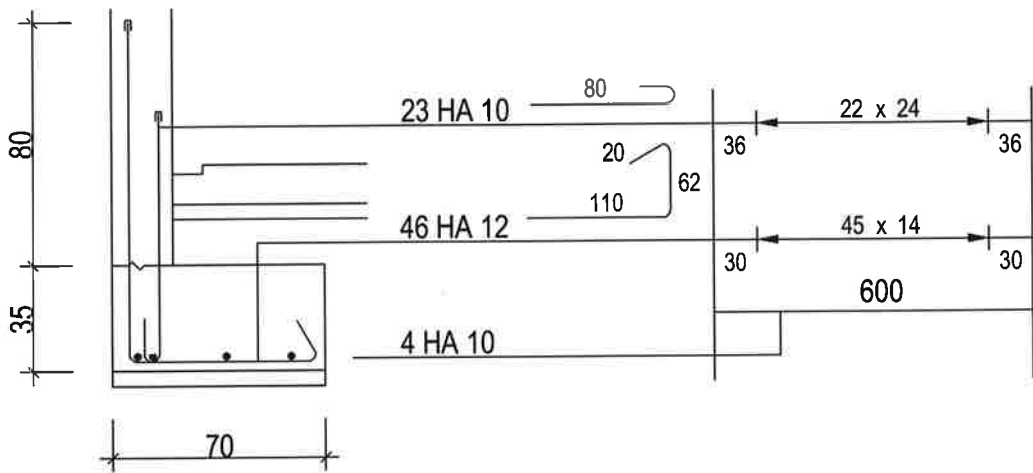

ARMATURES TETES DE MURS

(VALABLE 1 fois)

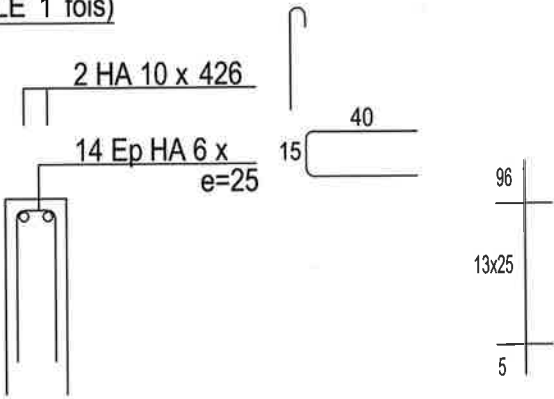

MS4

COUPE

Pan MJ385

Rec: 40 cm

Nombre: Voir élévation

BOITE D'ATTENTE

HA 10 e=20

+ 2 HA 14 FILANTS

+ 79 Ep HA 8 e=20

Lg: 2x14.20 ml

Rec: 70 cm

Pan MJ 503

VERTICAUX Rec: 40 cm

Nombre: Voir élévation

Pan MJ 503

VERTICAUX Rec: 40 cm

Nombre: Voir élévation

BOITE D'ATTENTE

HA 10 e=20

+ 2 HA 10 FILANTS


Lg: 2x14.20 ml

Rec: 50 cm

CH1

Rec: 60 cm

(VALABLE 2 fois)

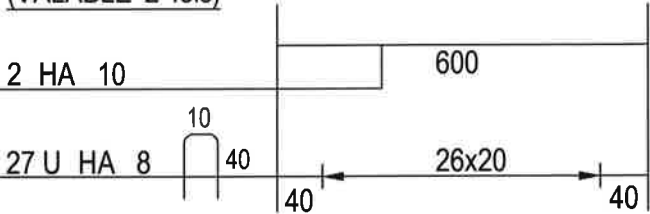

Pan MJ385


Rec: 40 cm

Nombre: Voir élévation


SFe70

Rec: 50 cm

Nombre: 2

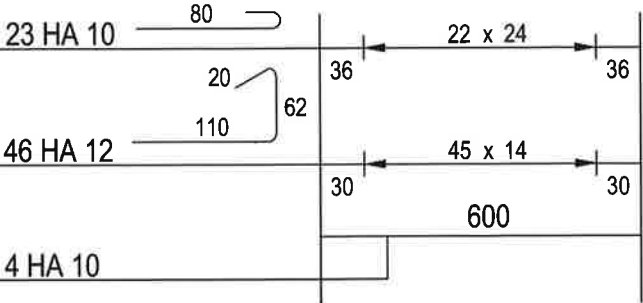

ARMATURES TETES DE MURS

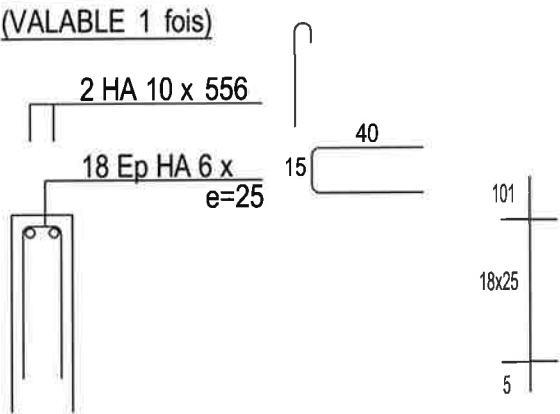

MS4

ELEVATION

