



COUPE G

Ech. 1/25

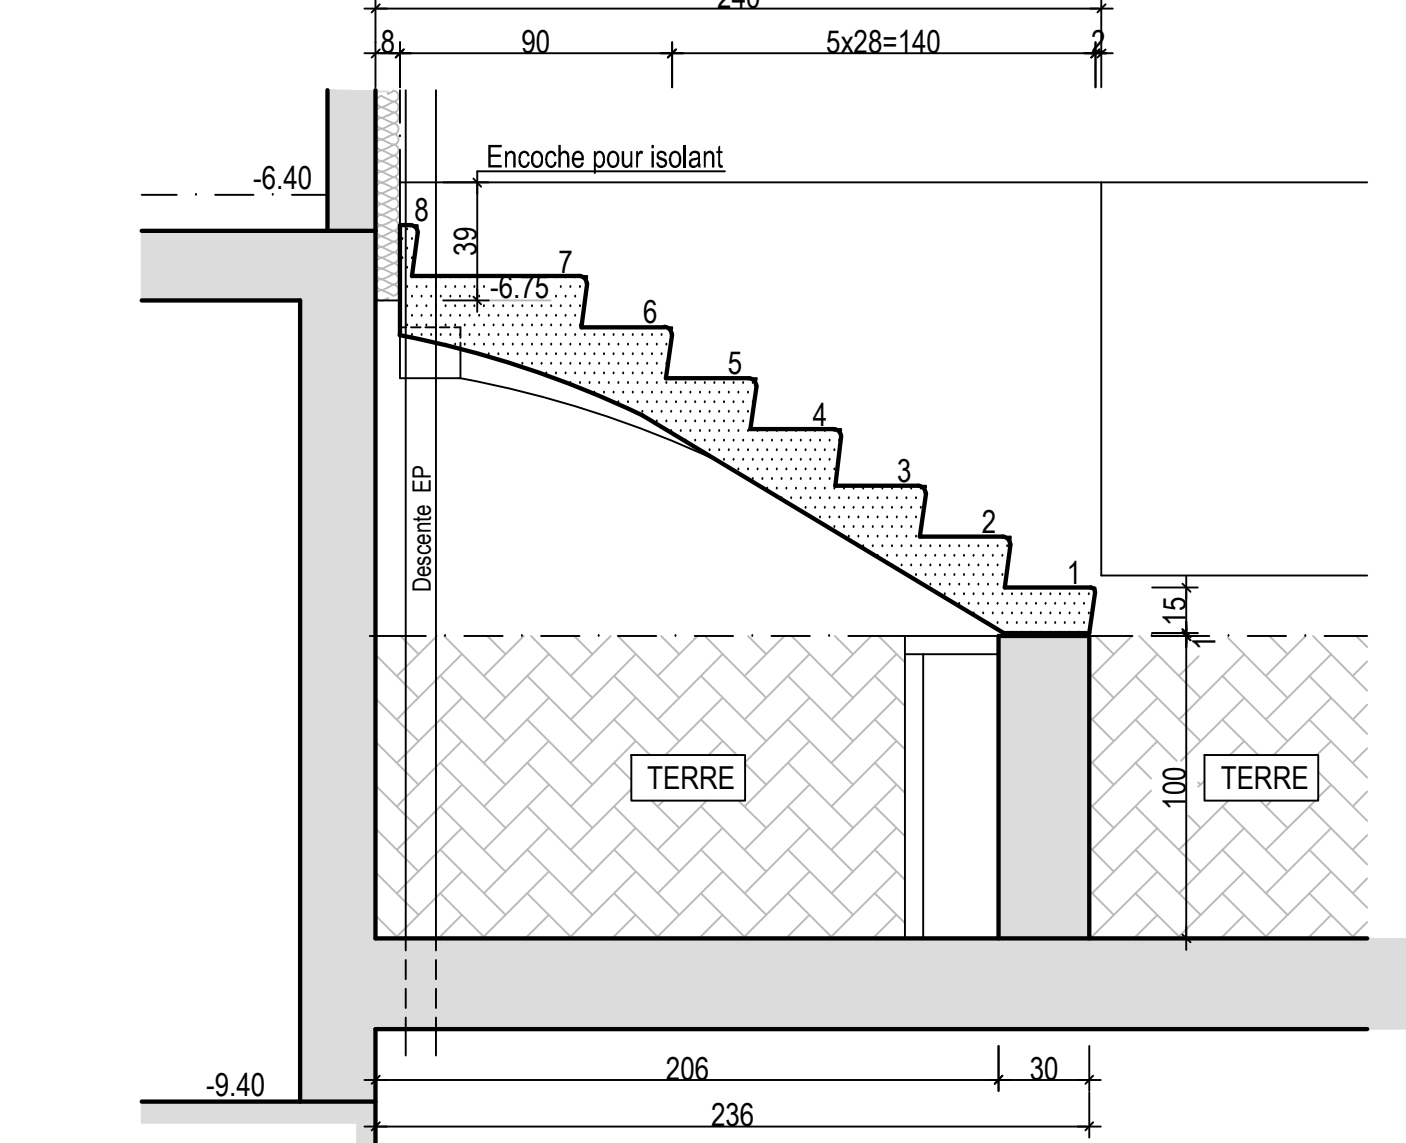


COUPE F

Ech. 1/25

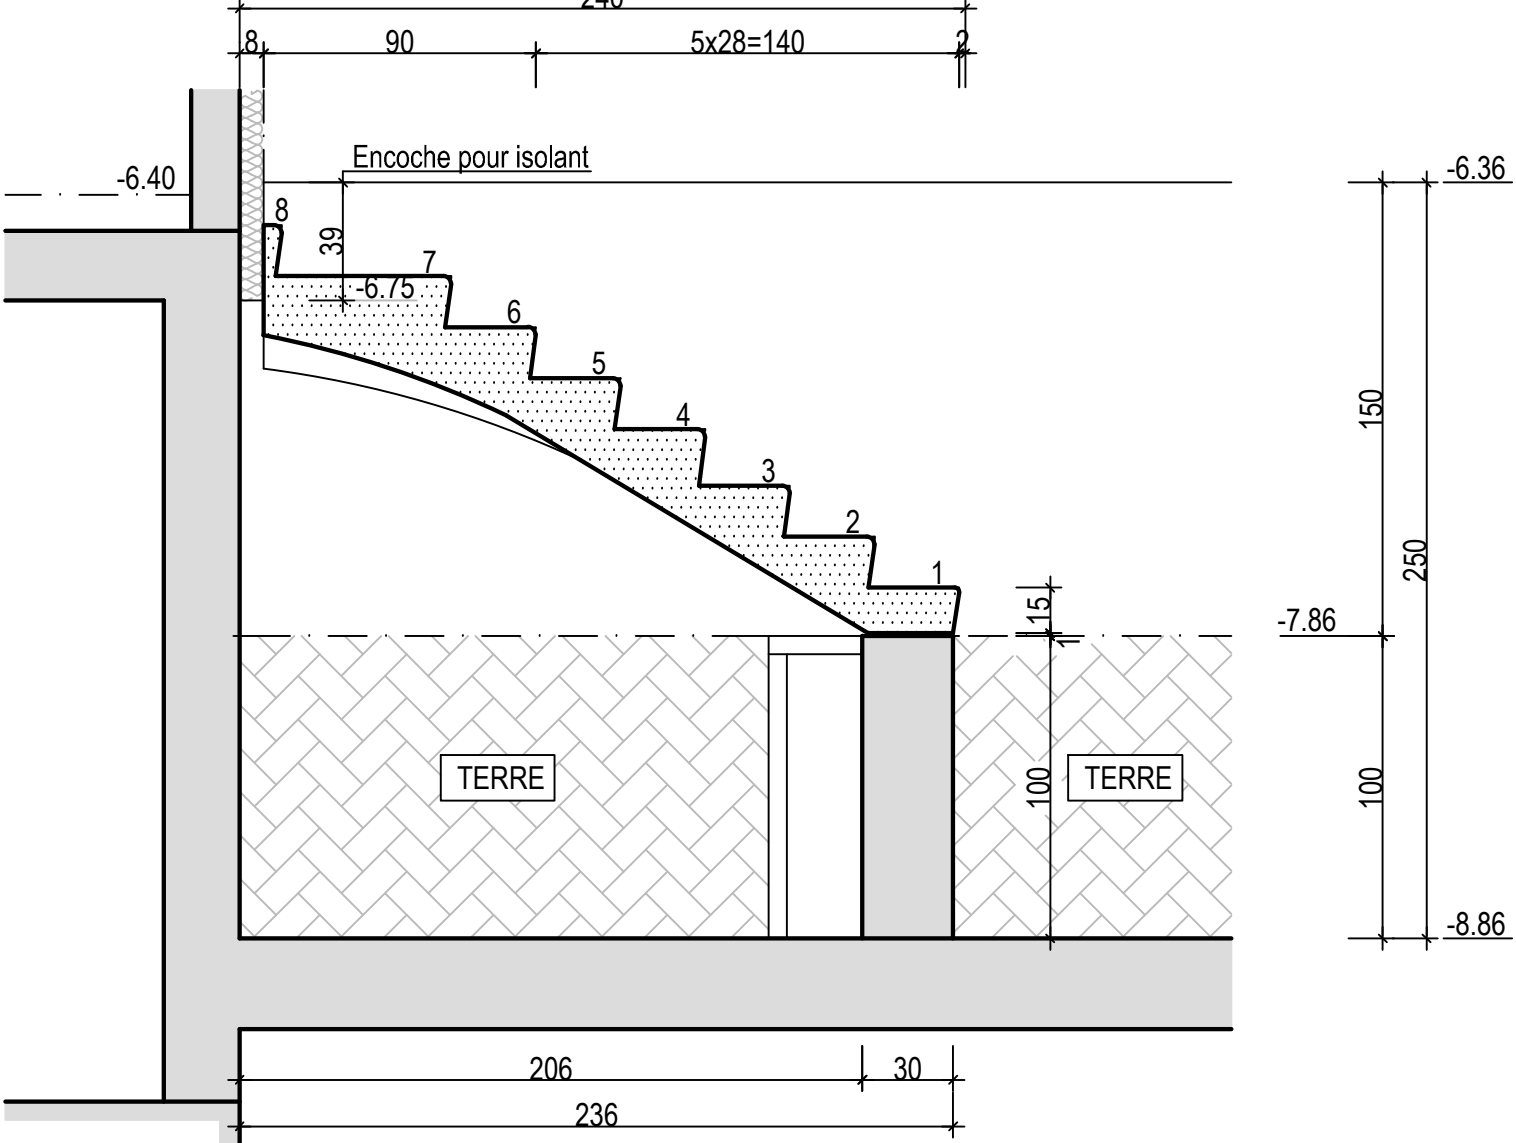


COUPE E

Ech. 1/25

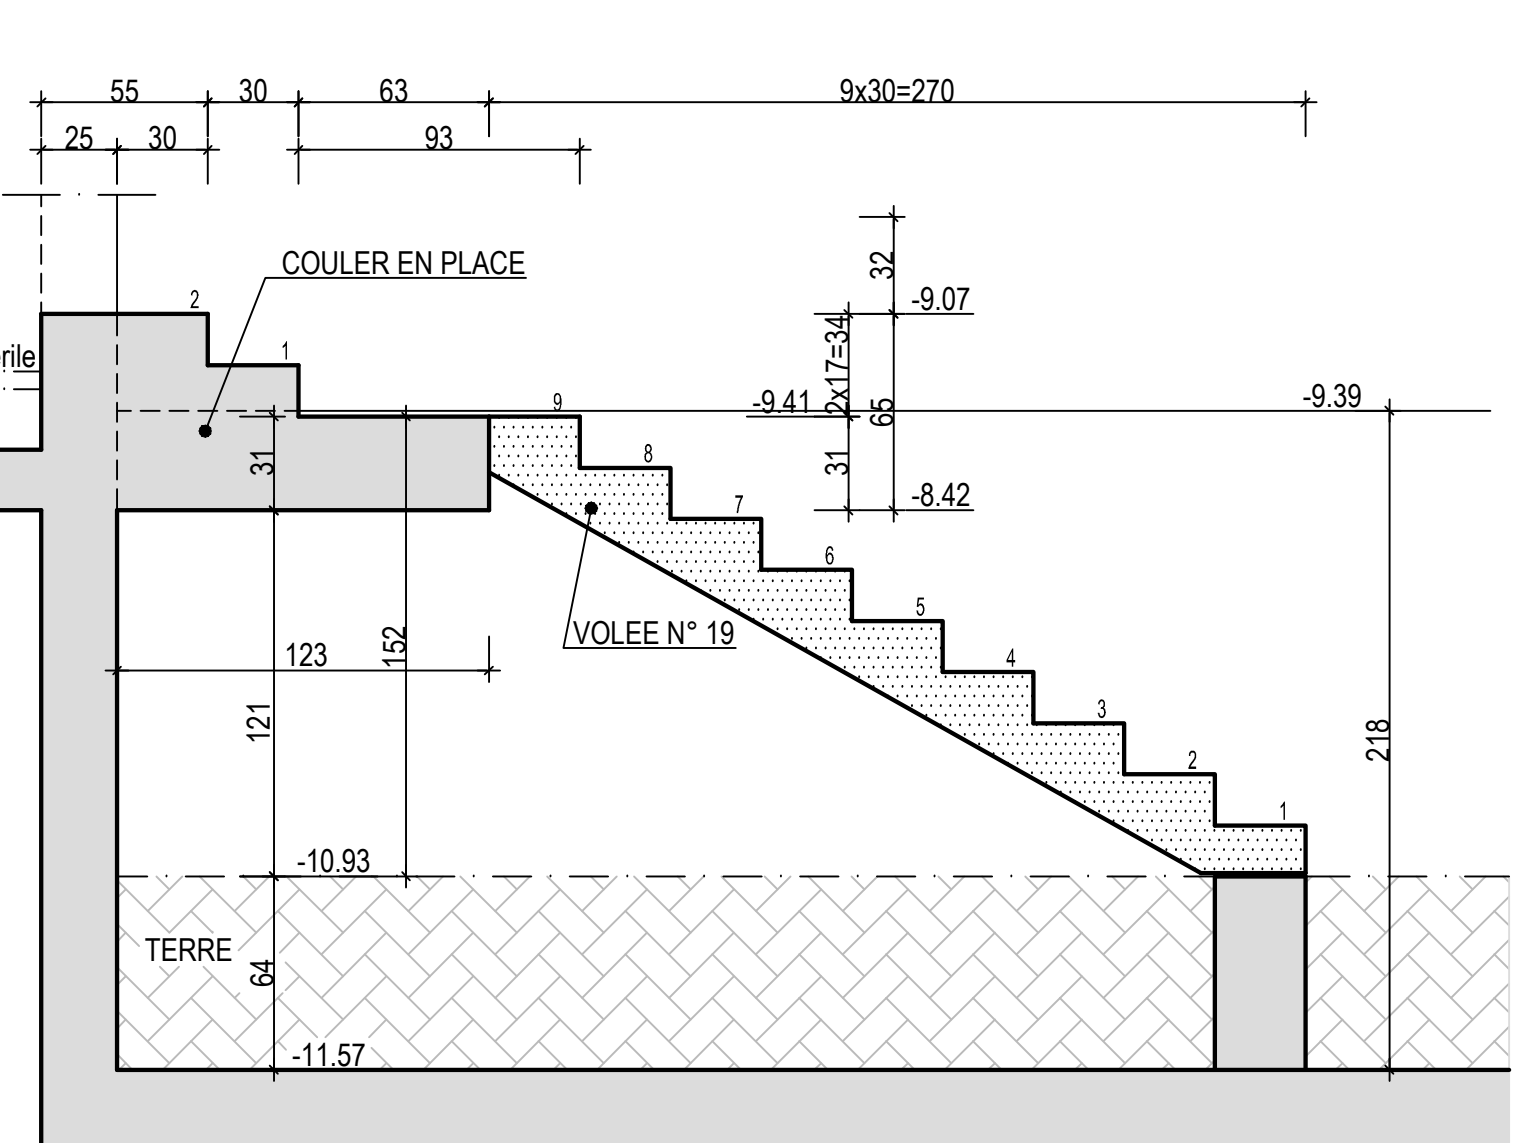


COUPE D

Ech. 1/25

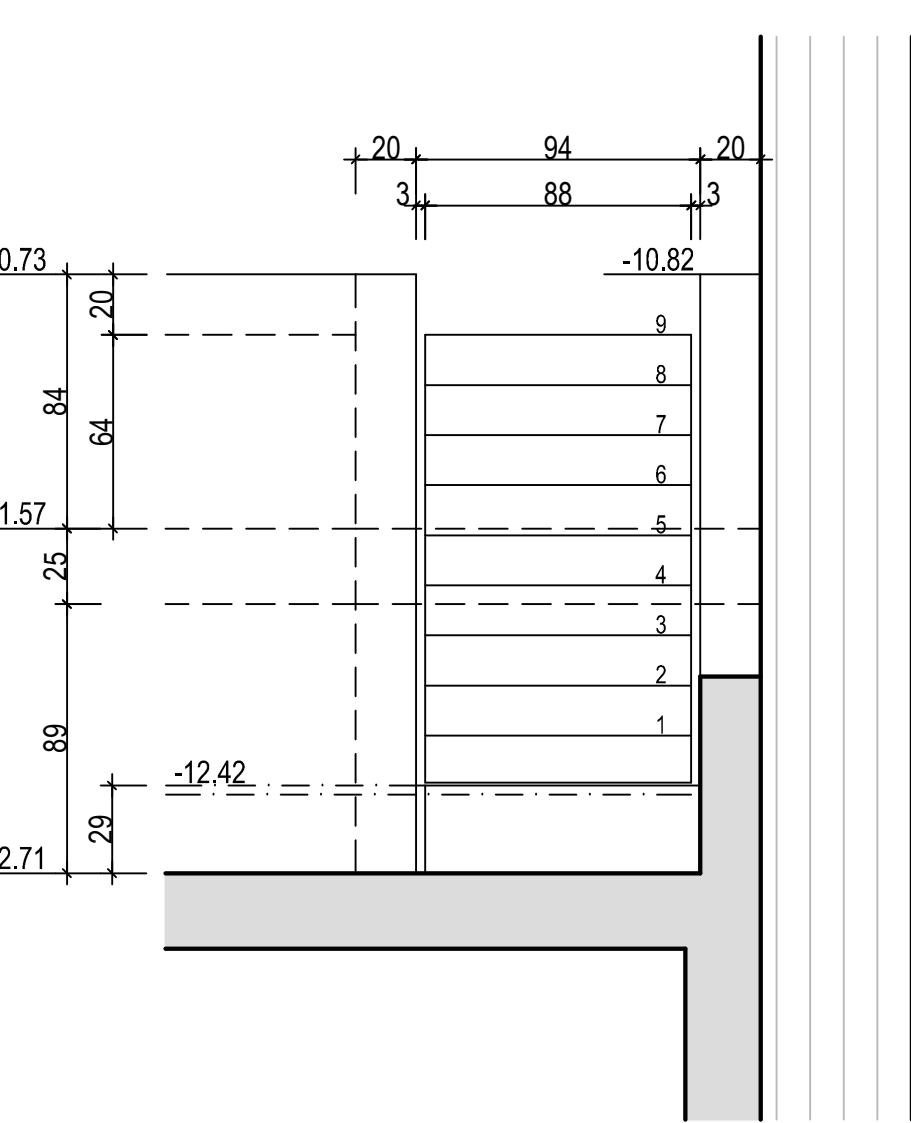


COUPE B

Ech. 1/25

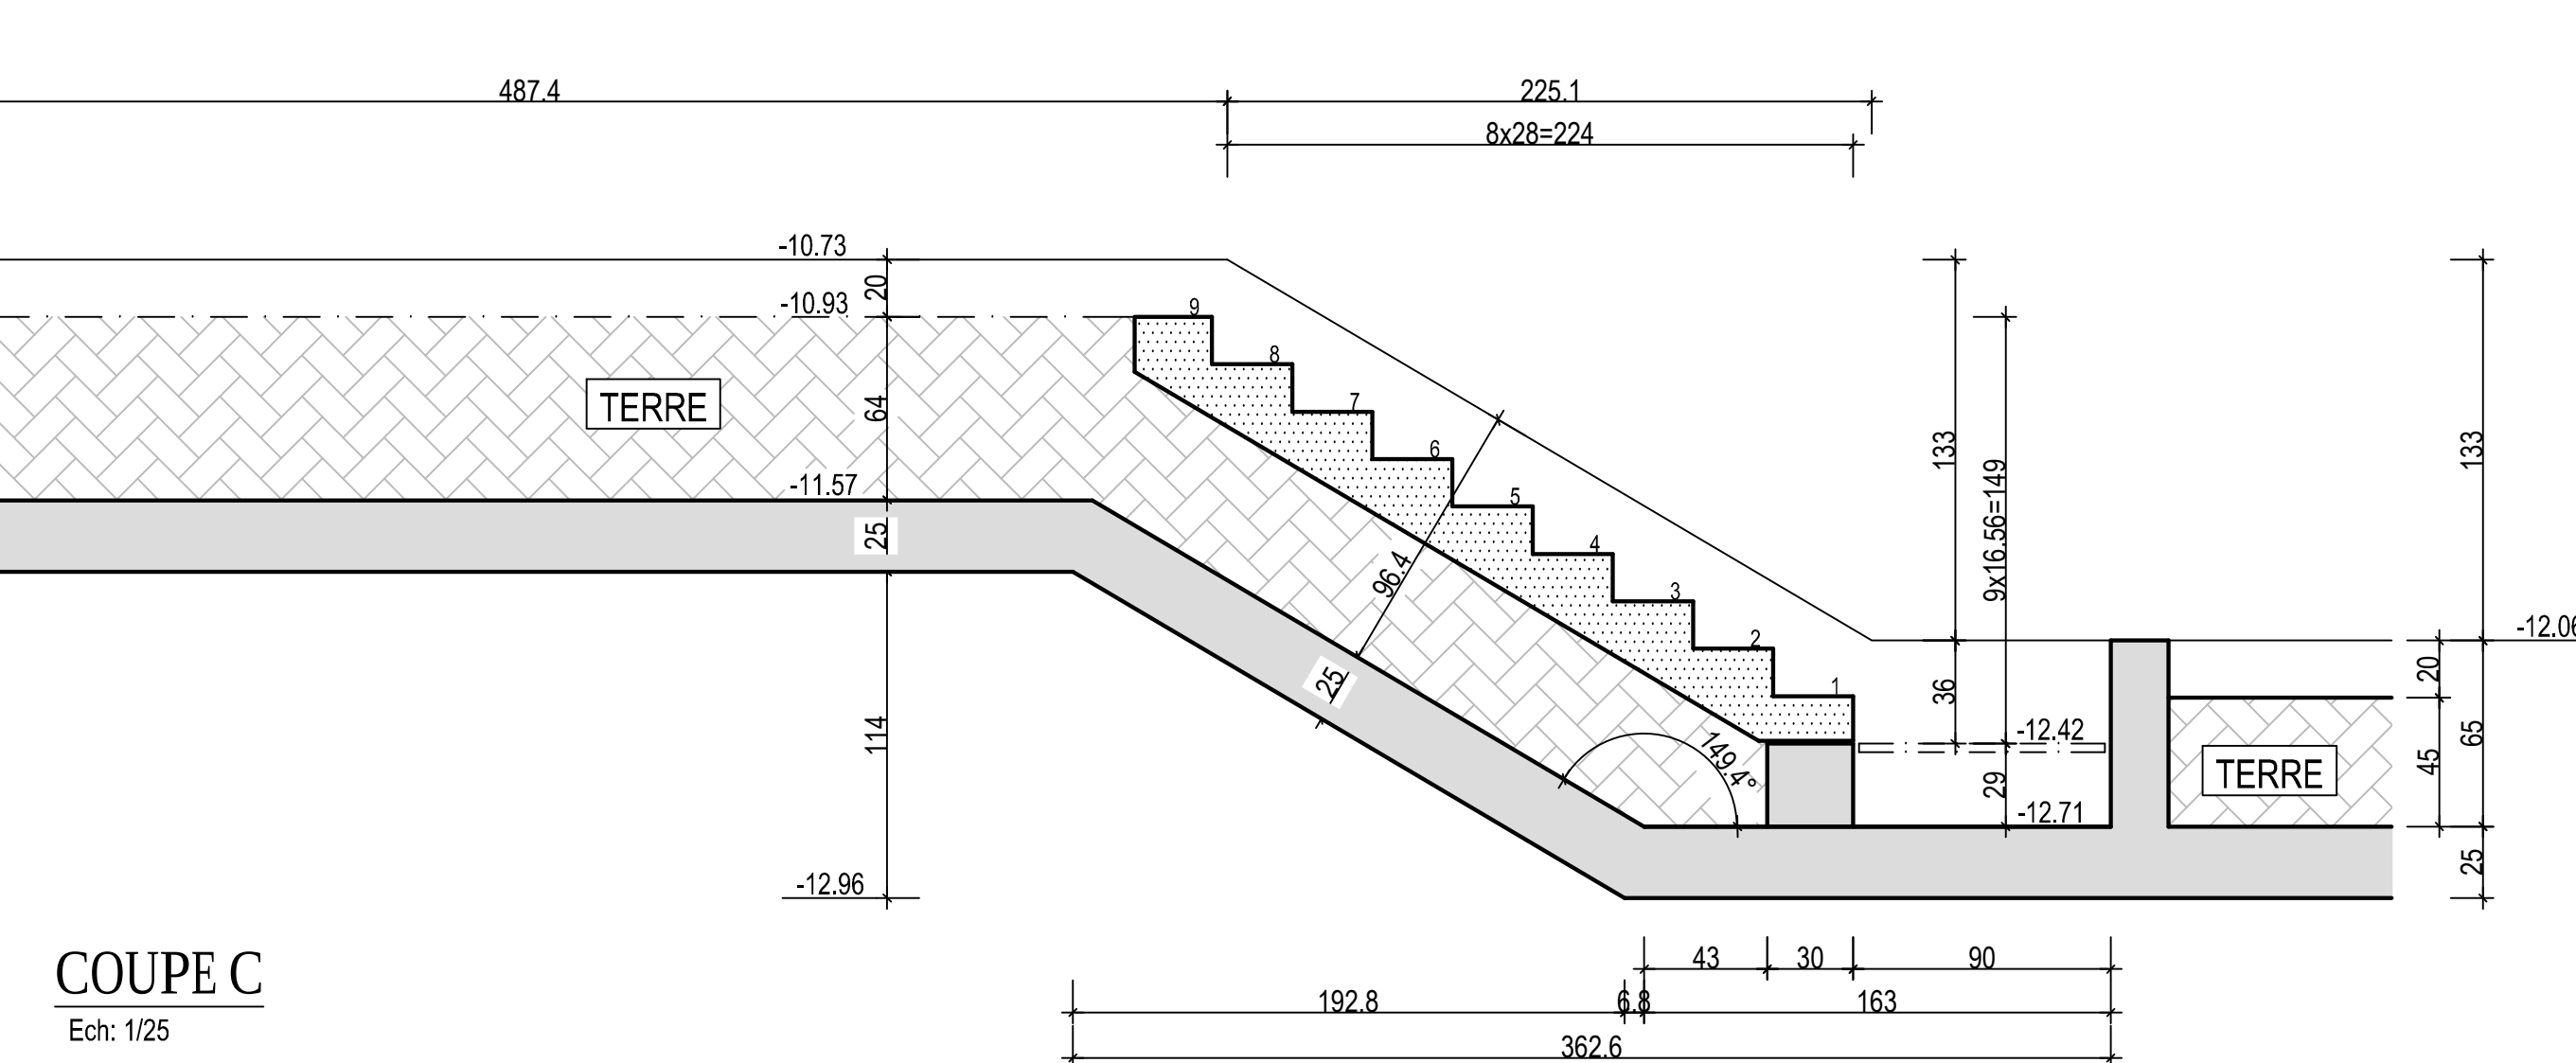


COUPE C

Ech. 1/25

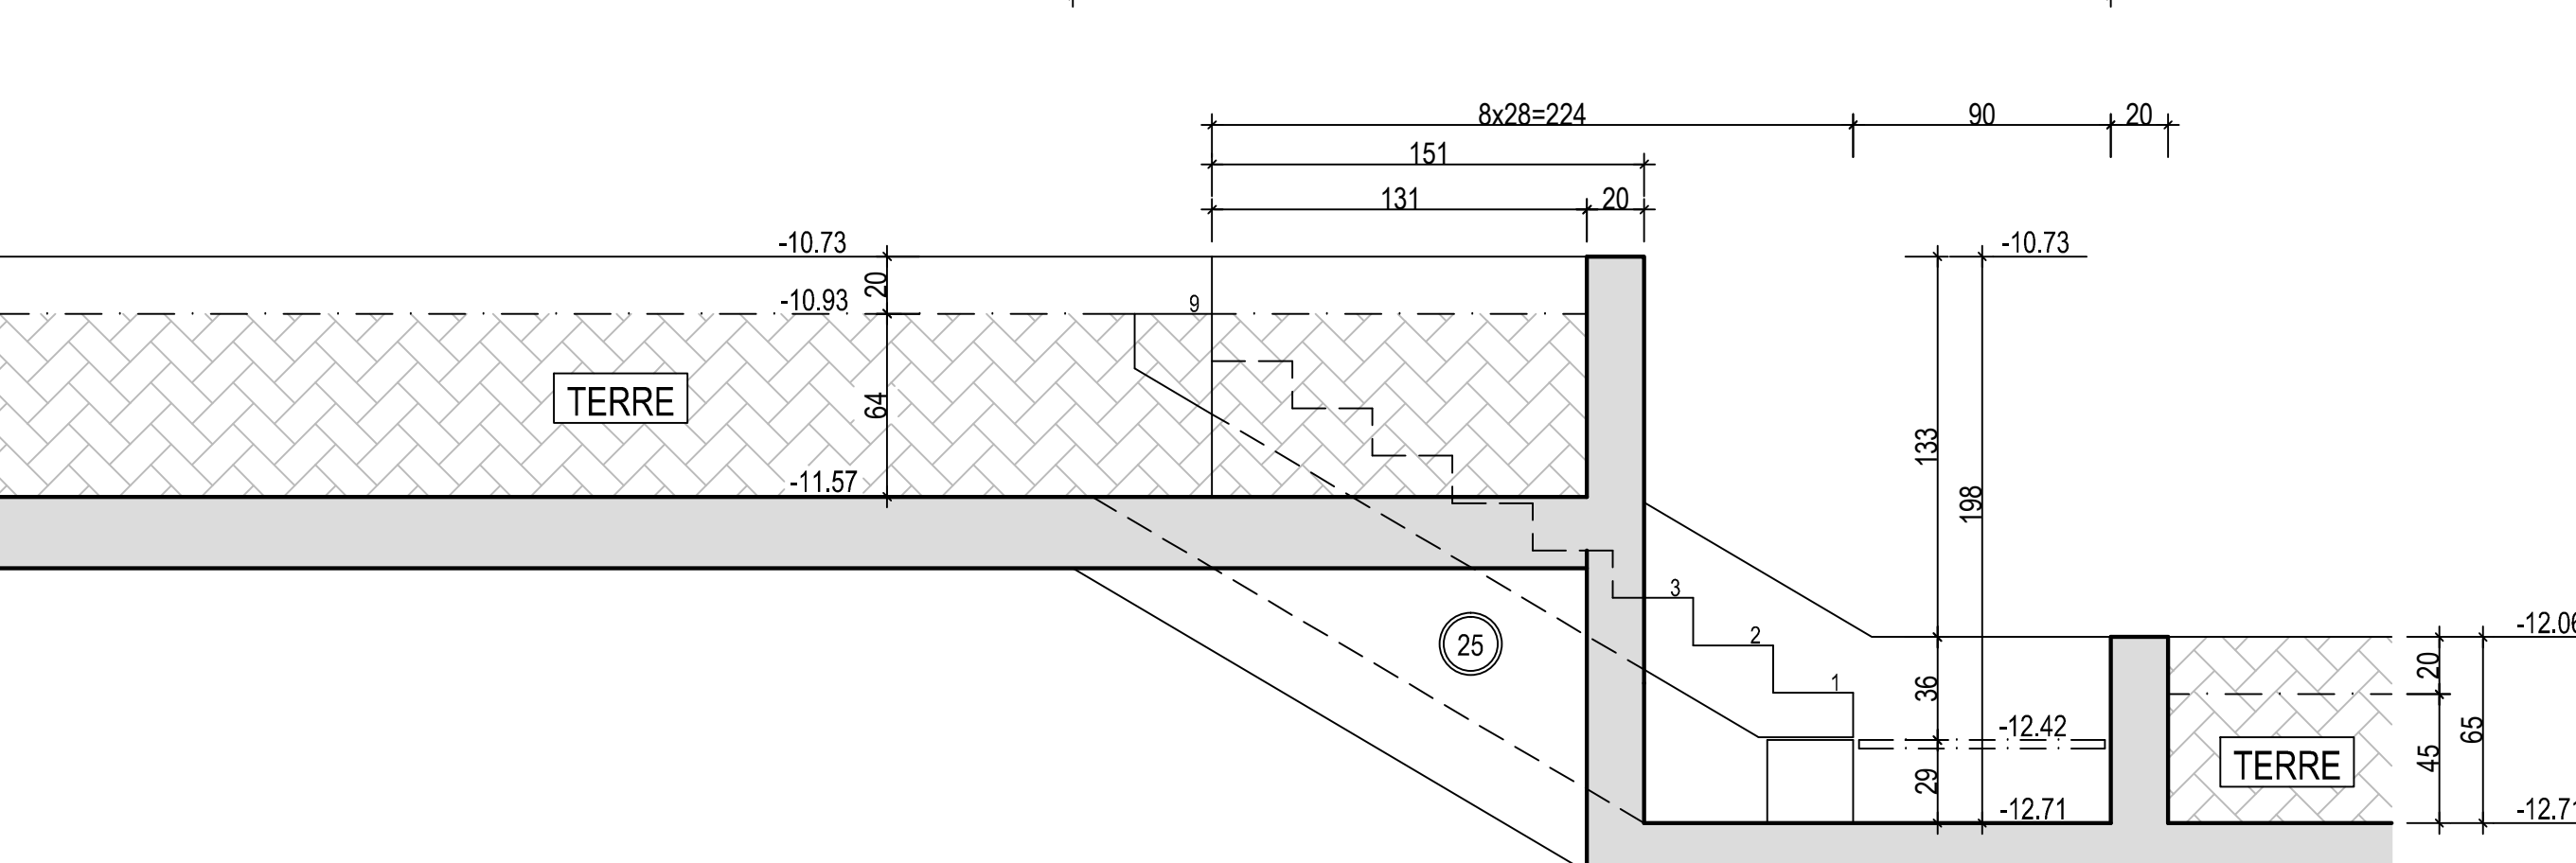



COUPE A

Ech. 1/25

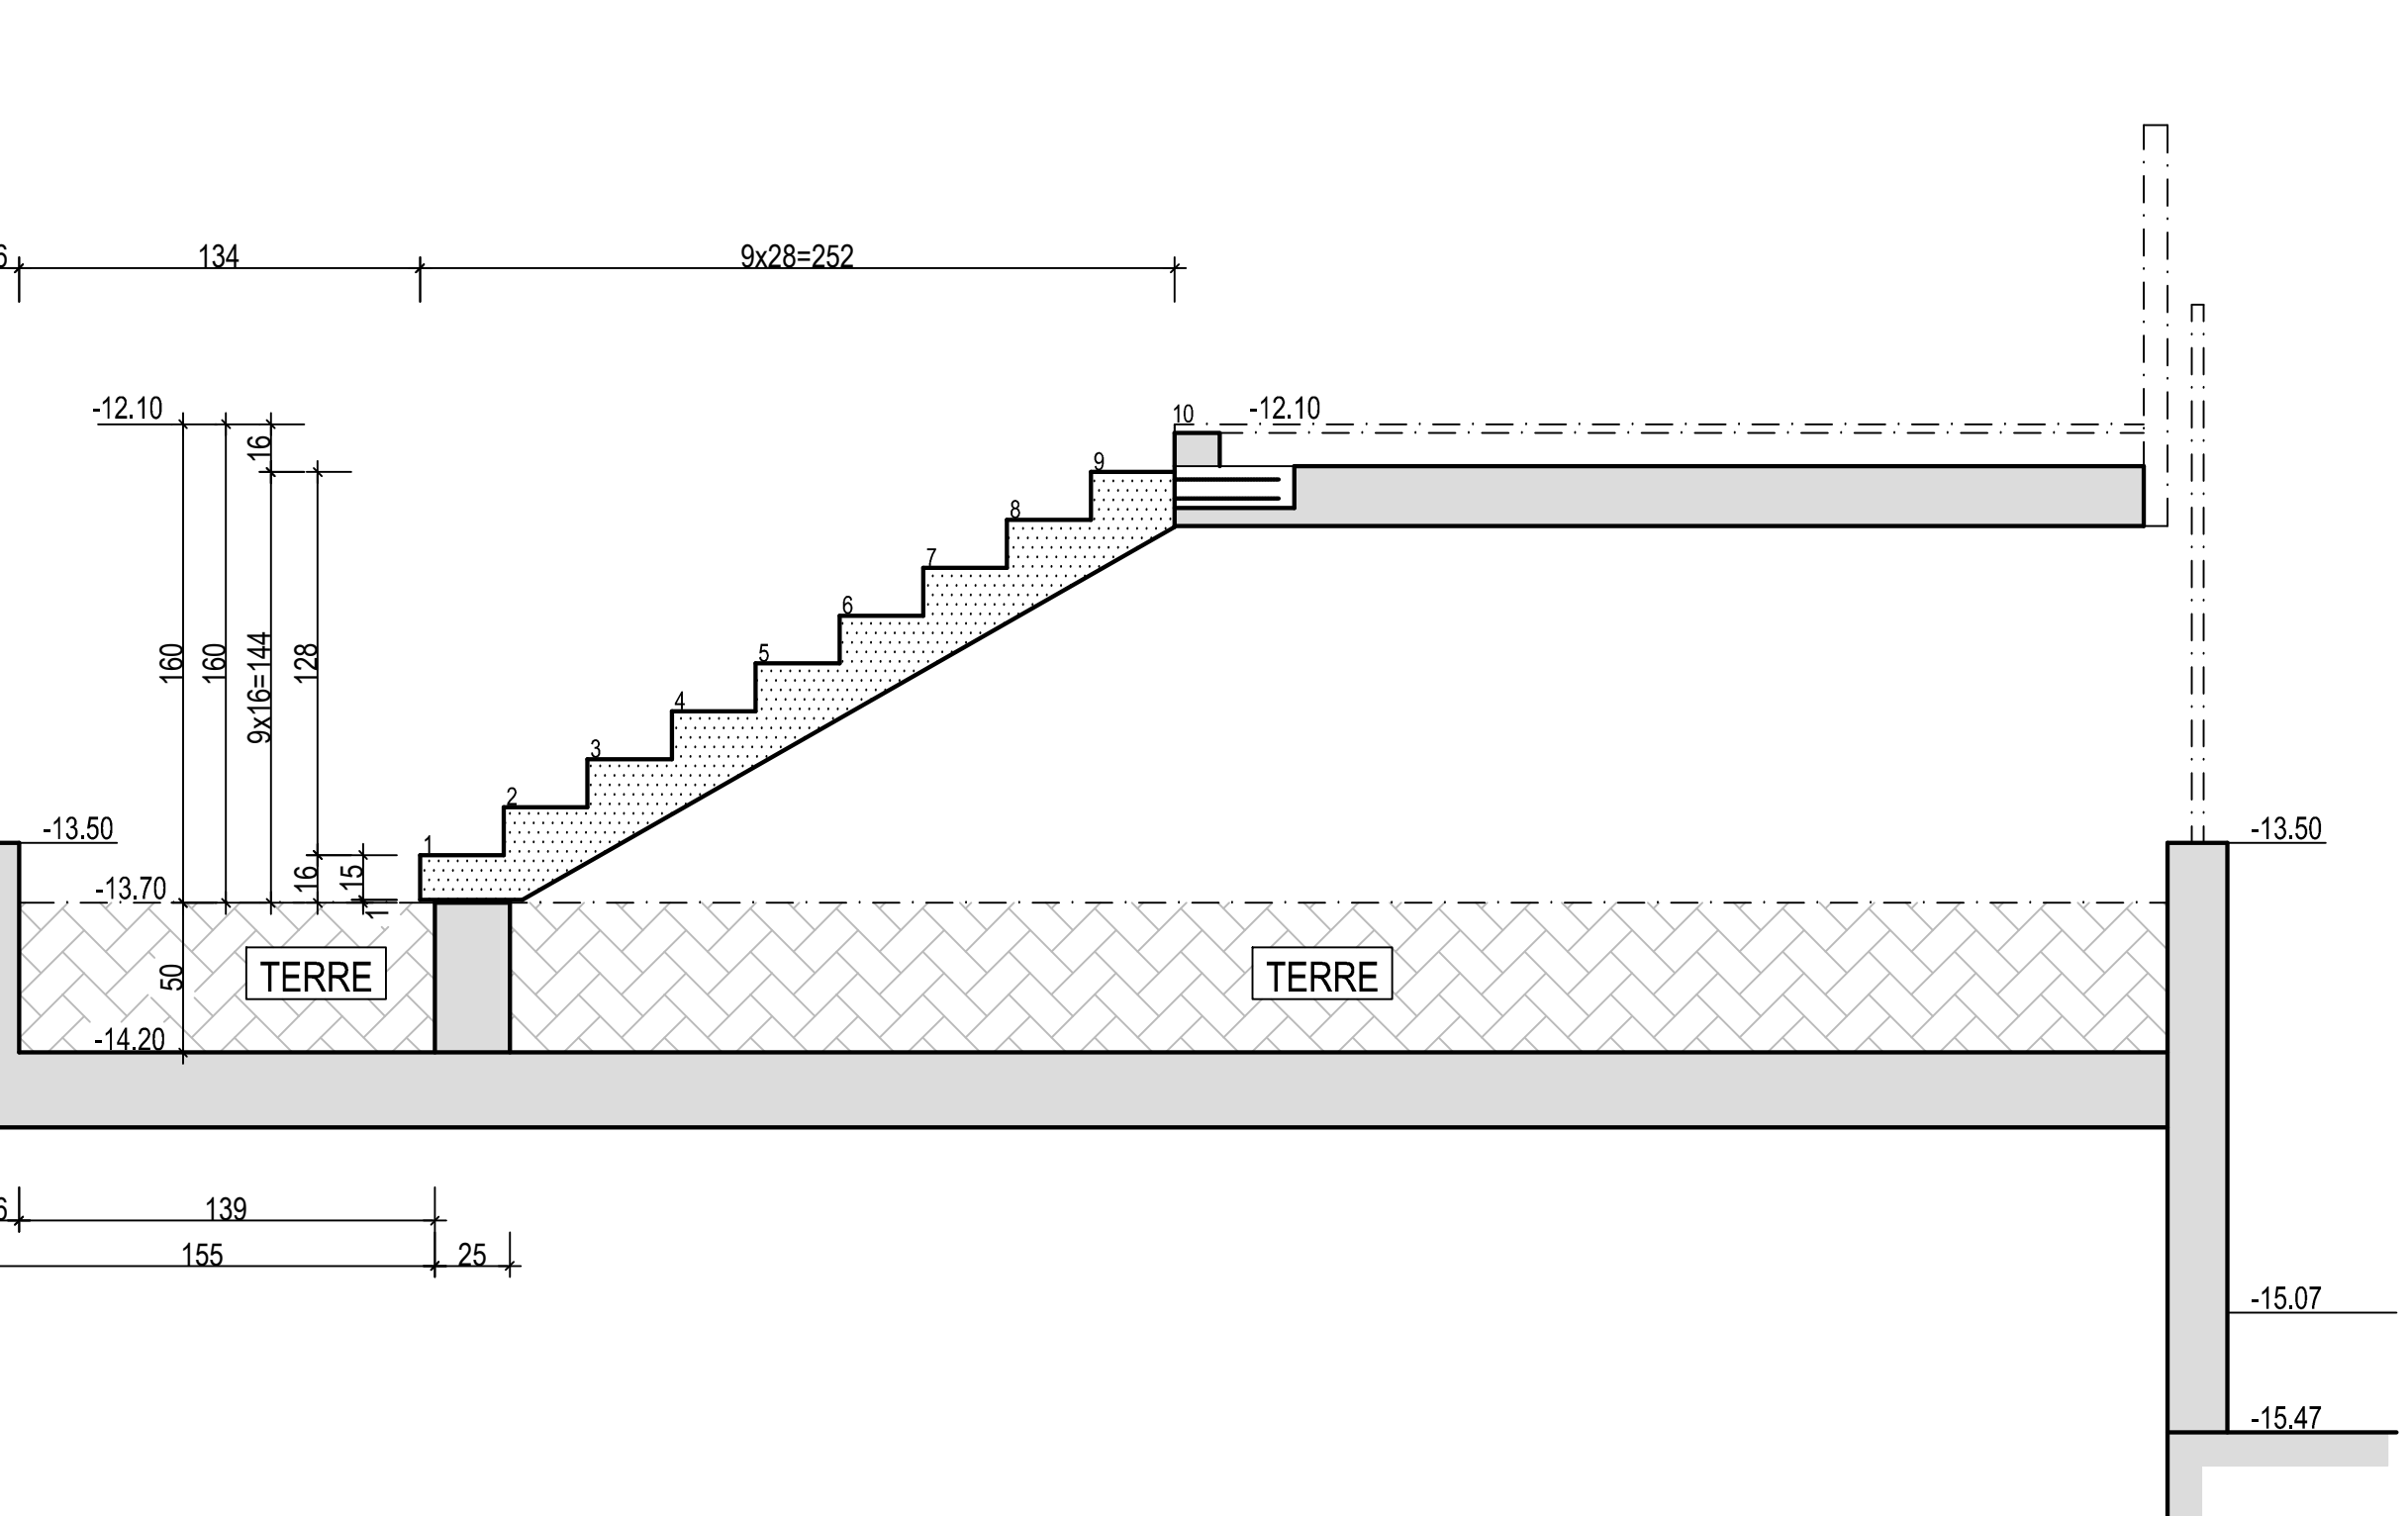

COUPE H

Ech. 1/25

 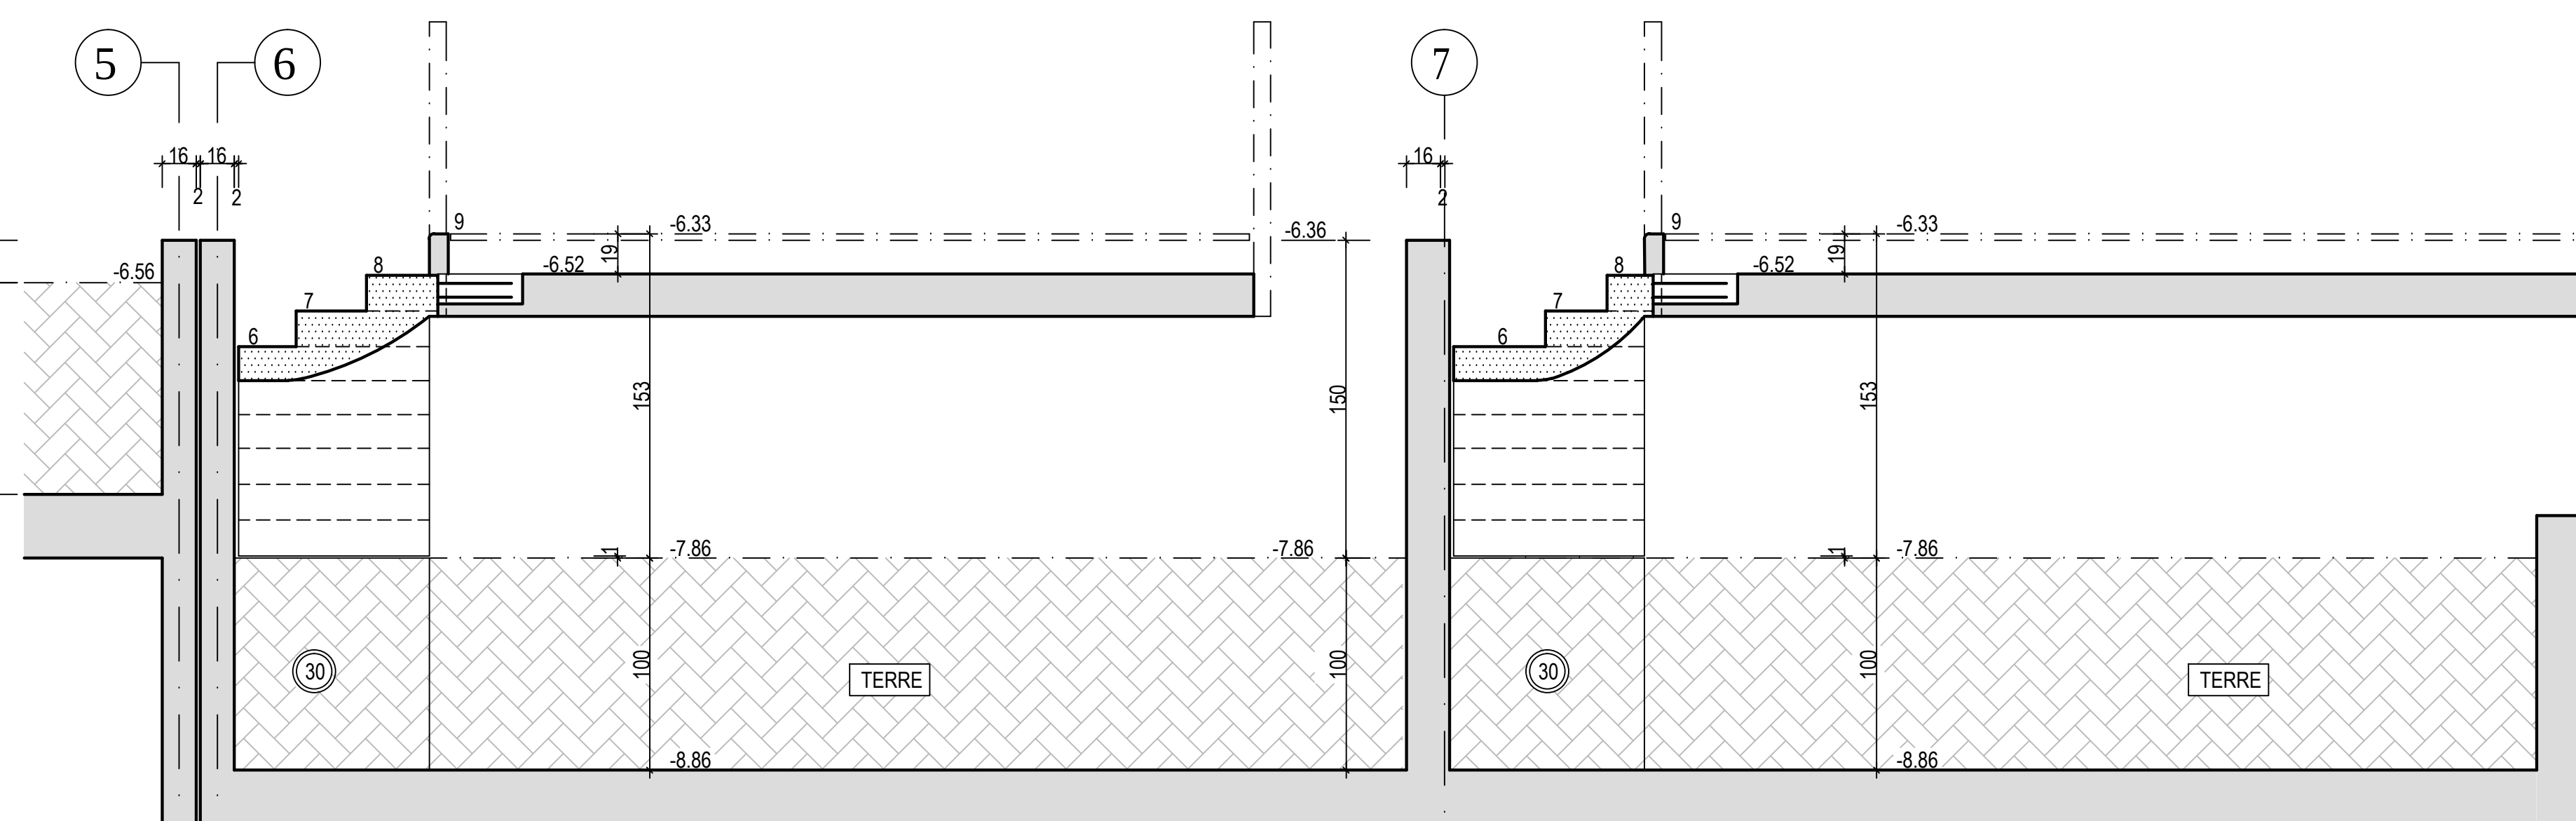

±0.00 = 220.50

NOAHO

Chemin de Fontanière - 69350 La Mulatière

Création de logements

Les entreprises réalisant les travaux devront tenir compte des données techniques inscrites dans les plans d'exécution. Les plans de la MATTE ne doivent servir qu'à des fins d'information.

ARCHITECTES: BUREAU VERITAS
BET FLUIDES: PRELEMI
BET FONDATIONS: EXECO
BUREAU DE CONTRÔLE: Bureau VERITAS
MO DELEGUE: MATTE SAS
MO: PRELEMI
MO: EXECO
PSO Ingénierie
SUITE EST COORDINATION
SUITE EST COORDINATION
ENTREPRISE: Fontanière-ebc

Bât: A et B
ESCALIER SUR RAMPE NORD
POSITION DES MASSIFS BA

INDICE: A 30/11/2015 AJOUTE ESCALIERS
B 4/12/2015 MISE A JOUR COUPES B et C
C 08/12/2015 MISE A JOUR COUPES B et C
D 15/12/2015 MISE A JOUR ESCALIERS FILE 6 et 7
E 17/12/2015 MISE A JOUR ESCALIER FILE 16

MATTE
BUREAU D'ETUDES
STRUCTURES ET FLUIDES
39 RUE DE LA PAIX 69001 LYON
Tél: 04 72 44 82 00 Fax: 04 72 44 26 09
E-mail: matte@matte.fr

Dessiné par: J.B.O.
Contrôlé par: P.LIN
Echelle: 1/500

Affaire N°
13.12.119