

NOAHO

Chemin de Fontanière - 69350 La Mulatière

Création de logements

Les entreprises réalisant les travaux devront tenir compte des derniers plans architecte lors de la réalisation des travaux
Les plans du be MATTE ne doivent servir qu'au corps d'état concerné et doivent être des plans d'exécution.

ARCHITECTE(S):	ATELIER DE LA PASSERELLE	MO DELEGUE:	
BET STRUCTURE:	MATTE SAS	MOE:	PSO Ingénierie
BET FLUIDES:	PRELEM	CSPS:	SUD EST COORDINATION
ECONOMISTE:	EXECO	OPC:	
BUREAU DE CONTROLE:	Bureau VERITAS	ENTREPRISE(S):	Fontanel-pbc

Bât: B

BALCONS

Coffrage

DOE

Contrainte de sol:

Aciers HA (T) FeE500
Aciers Doux (Ø) FeE 235
Aciers TS FeE 500
Béton fc28 >= 25MPa
Enrobage = 3 cm

PLAN N°

B06 A

DATE : 2/11/2015

MATTÉ

BUREAU D'ÉTUDES

STRUCTURES ET FLUIDES

119 BOULEVARD STALINGRAD 69100 VILLEURBANNE

Tél. 04 72 44 02 87 Fax 04 72 44 26 59

E-mail : bet@matte.fr

Dessiné par : J.BO

Contrôlé par : P.LIN

Echelle : 1/50°

Affaire N°

13.12.119


PLANCHER sur -5

A

B1


1 p

Poids: 6500 Kg

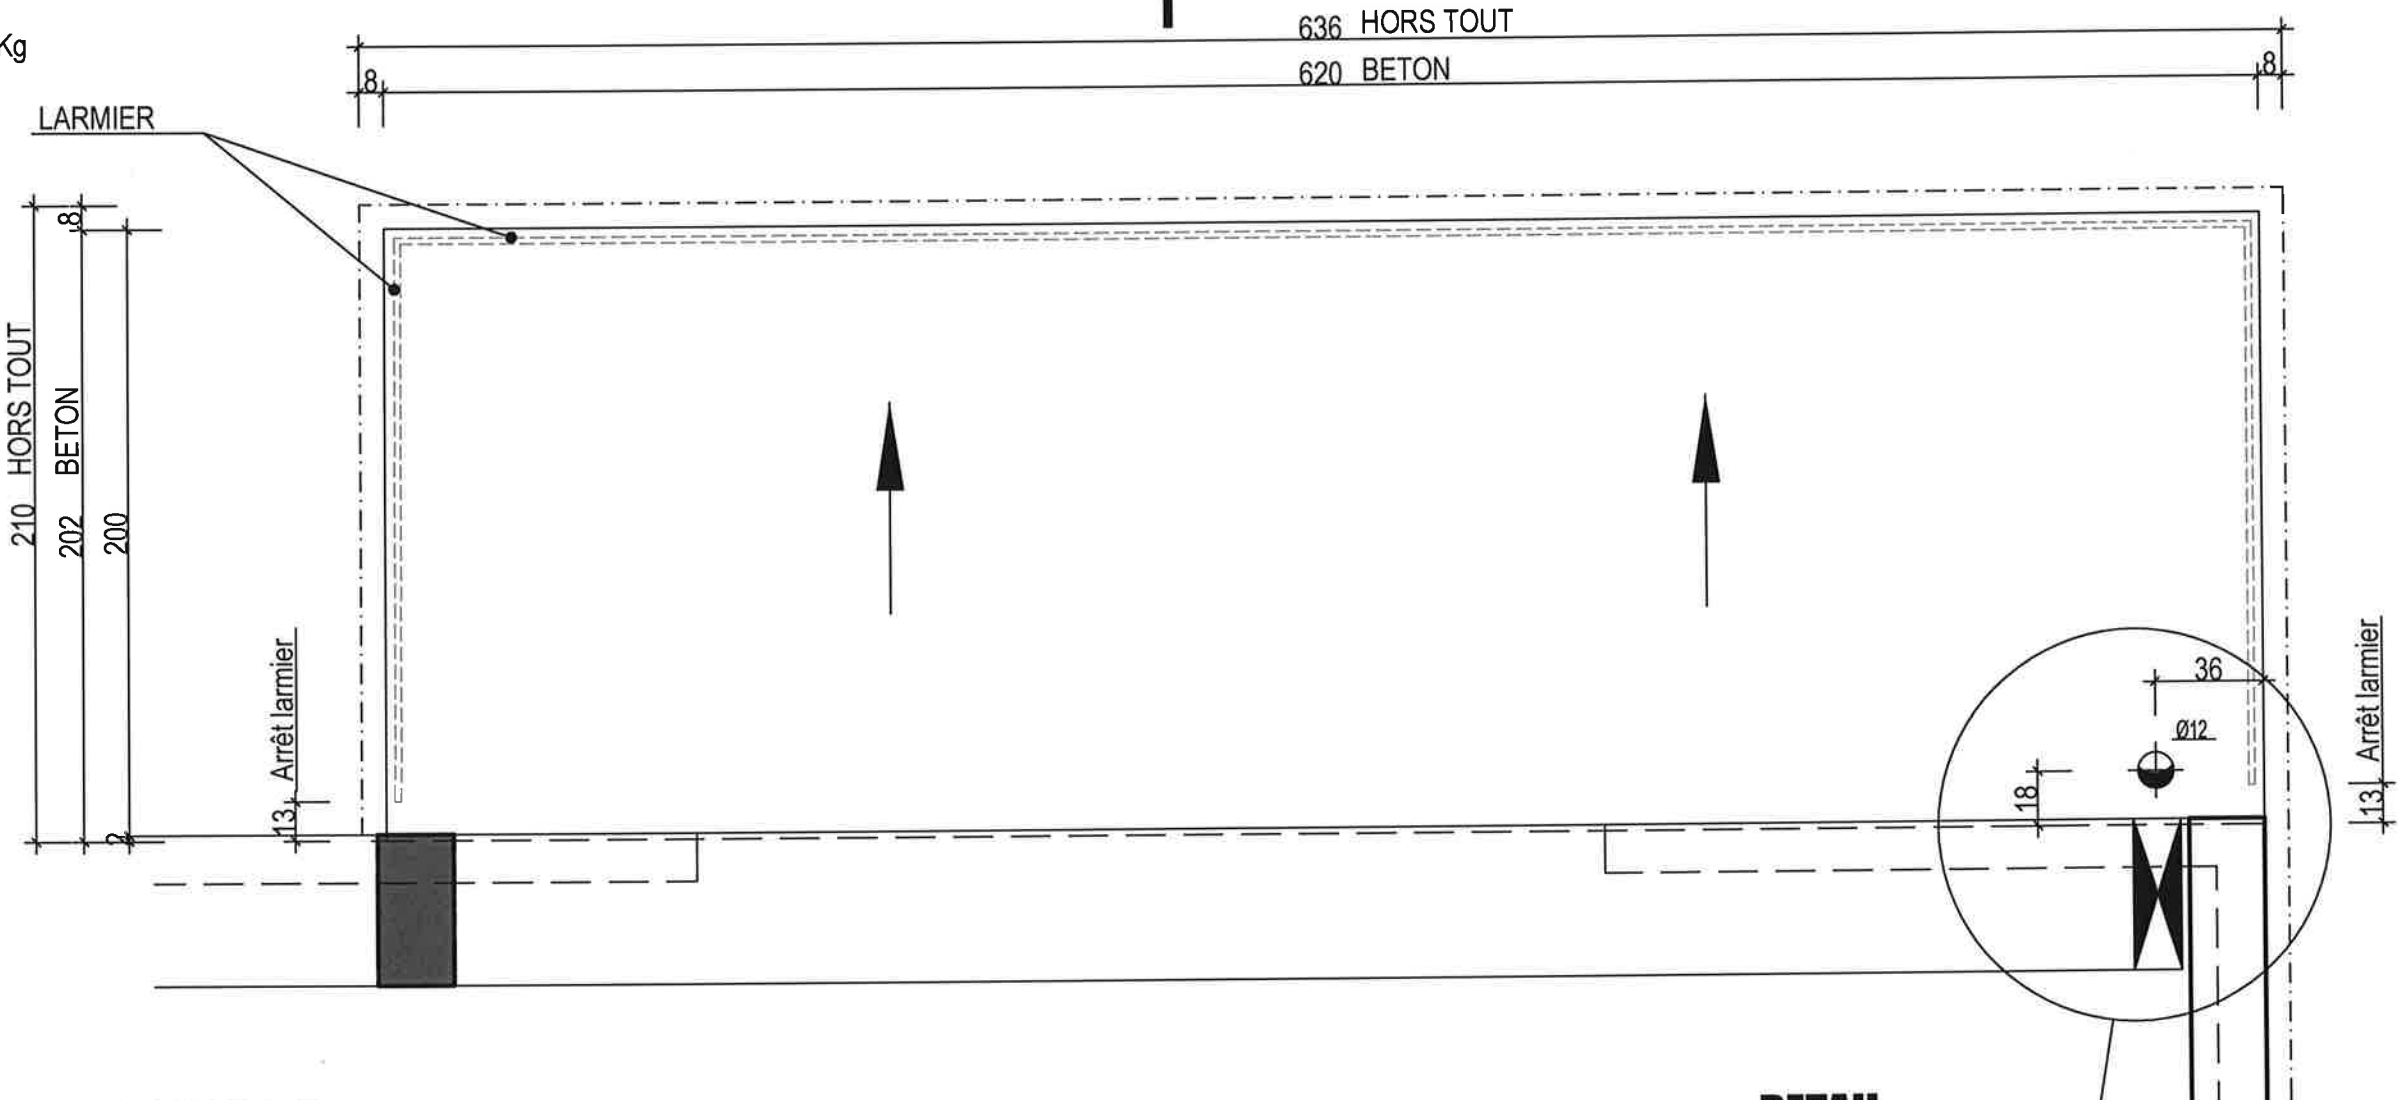


COUPE A

Ech: 1/25

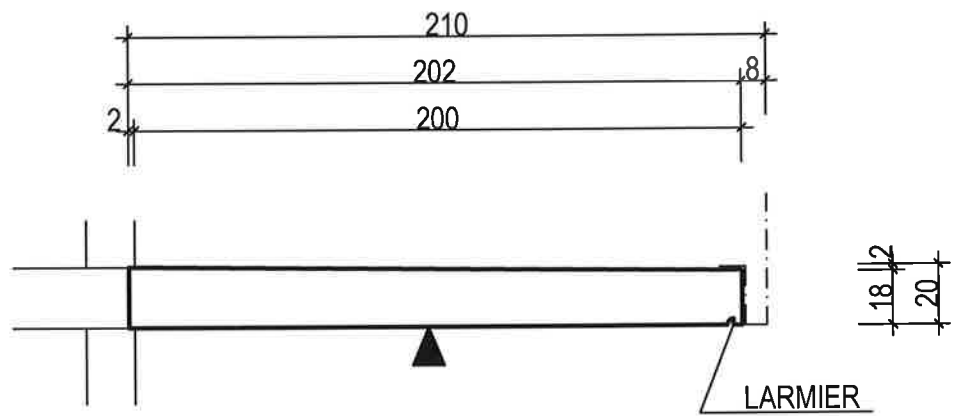

DETAIL vue de dessus

Ech: 1/25

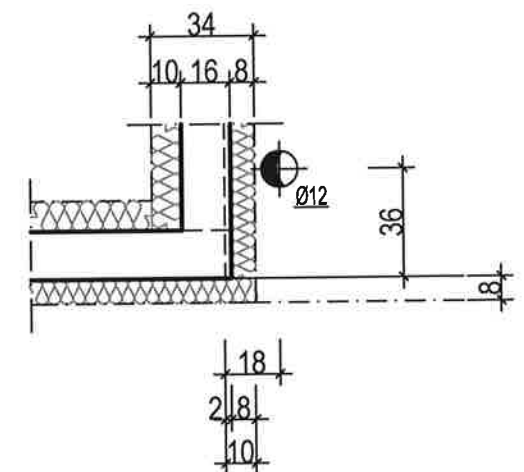


B2

Poids: 4800 Kg

	Entre files 10 et 14	Entre files 14 et 19
Plancher sur +2	0	0
Plancher sur +1	0	0
Plancher sur REZ	0	0
Plancher sur -1	0	0
Plancher sur -2	1	1
Plancher sur -3	1	0
Plancher sur -4	0	0
Plancher sur -5	0	5



COUPE A

Ech: 1/25

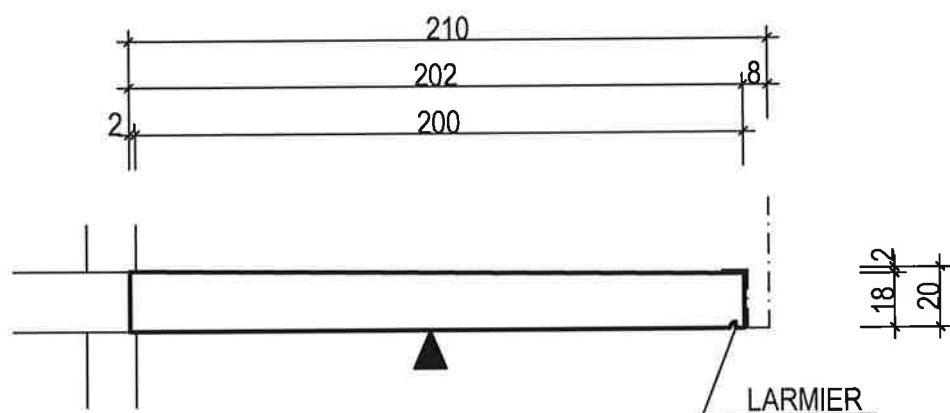

COUPE B

Ech: 1/25

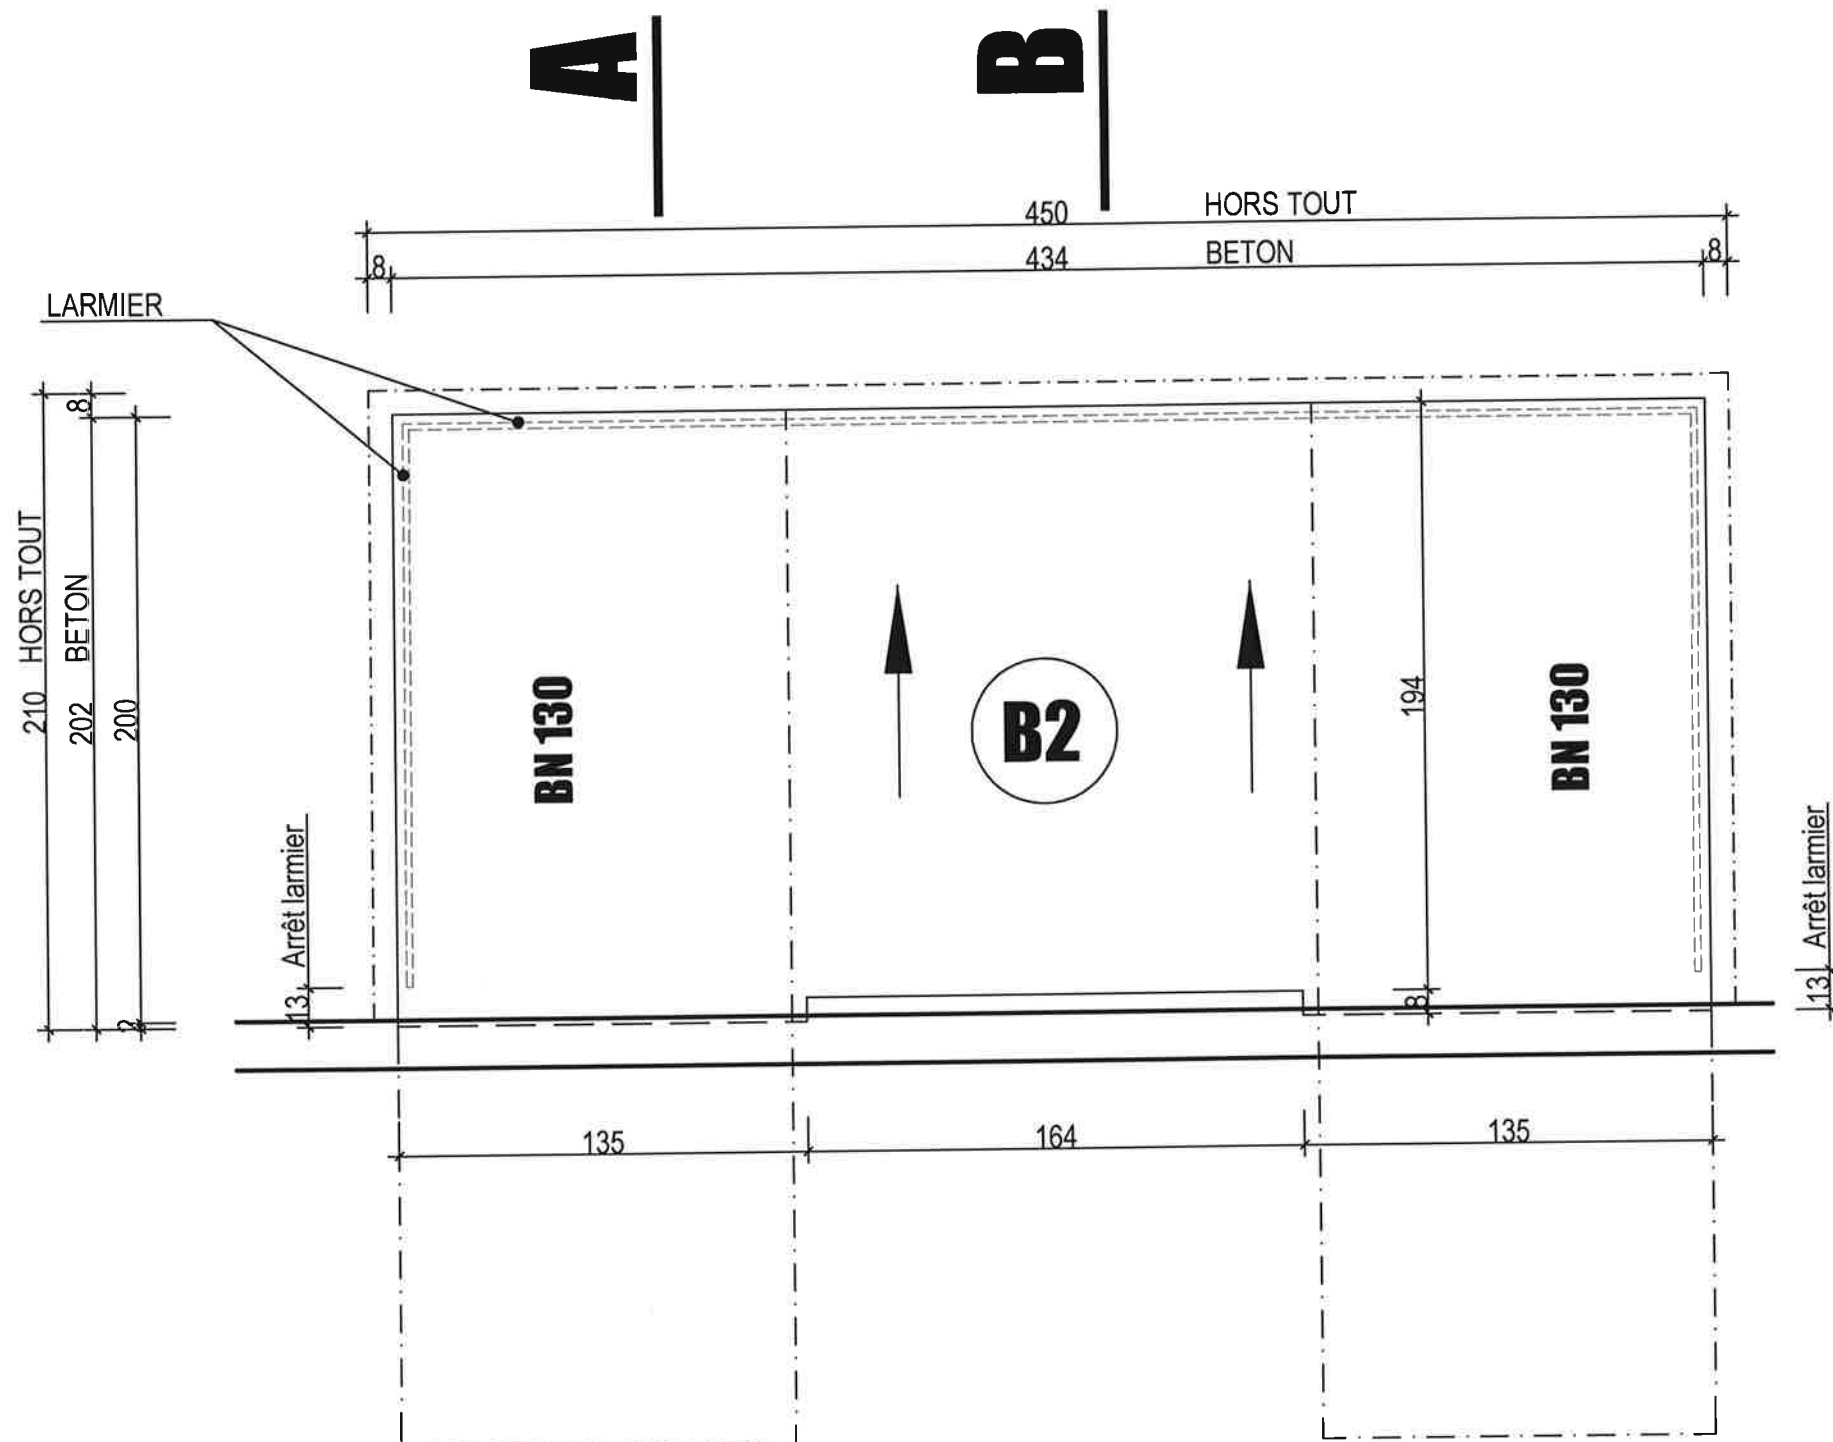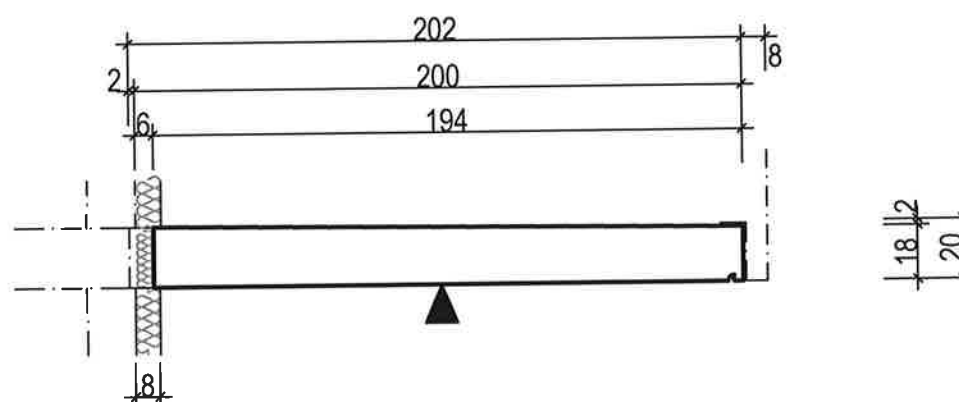


B3


Poids: 4800 Kg

	Entre files 10 et 14	Entre files 14 et 19
Plancher sur +2	0	0
Plancher sur +1	0	0
Plancher sur REZ	0	0
Plancher sur -1	0	0
Plancher sur -2	0	0
Plancher sur -3	0	0
Plancher sur -4	0	0
Plancher sur -5	0	1


LARMIER

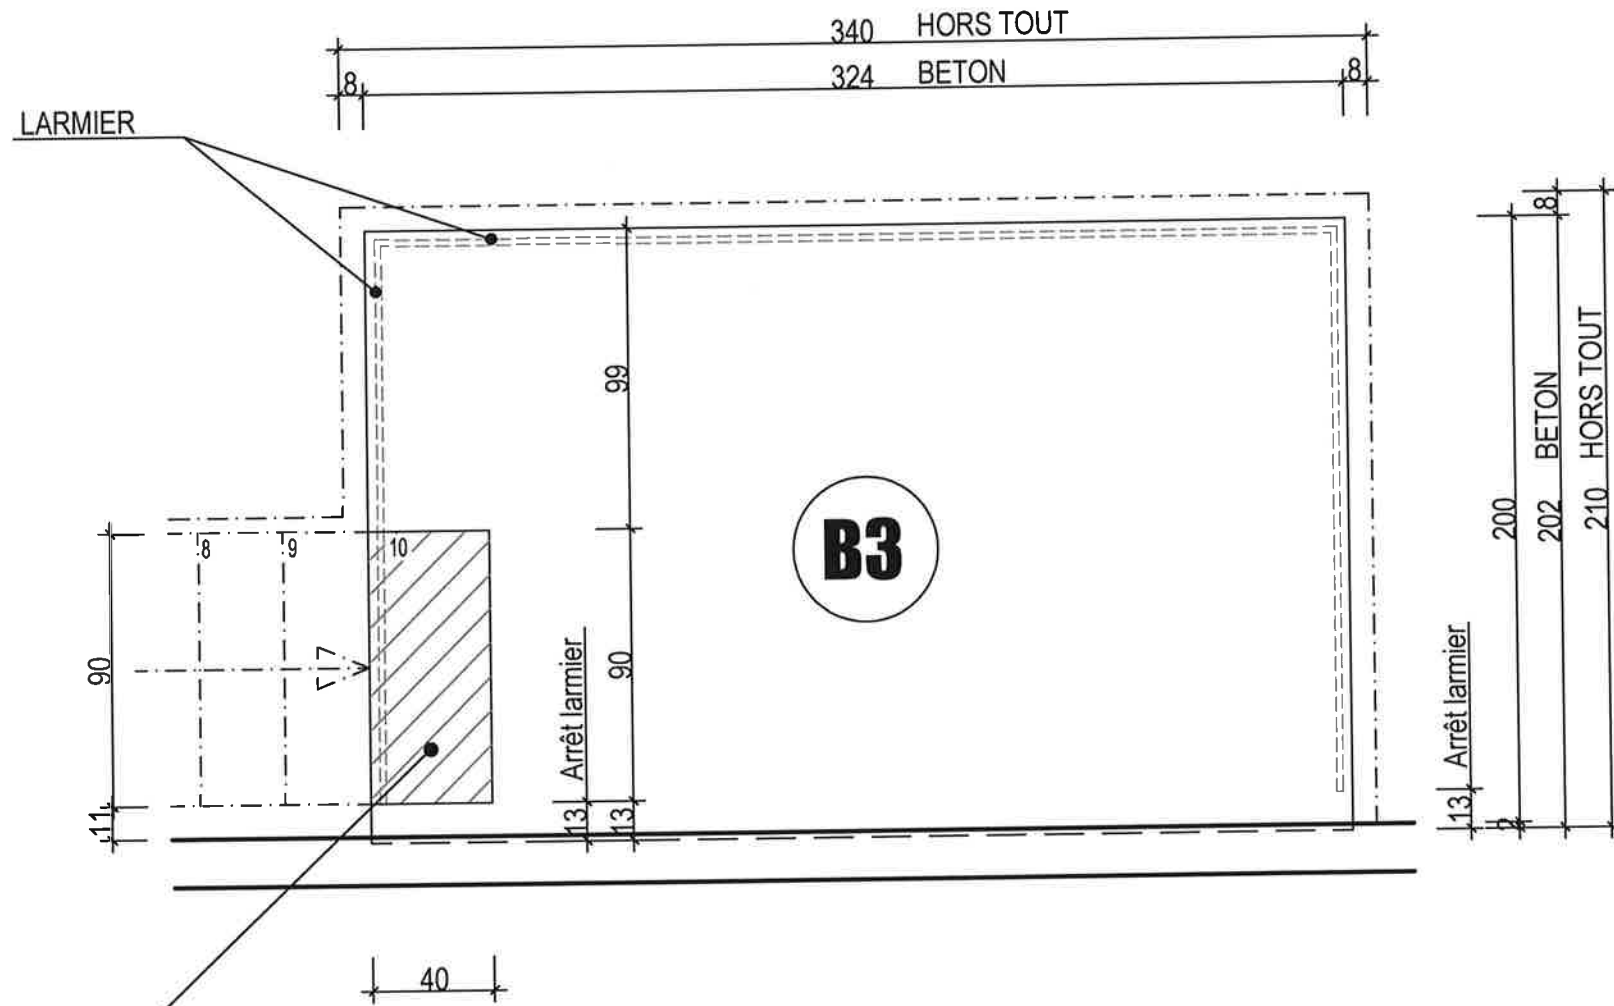**DETAIL D'ARRIVEE**

Ech: 1/10

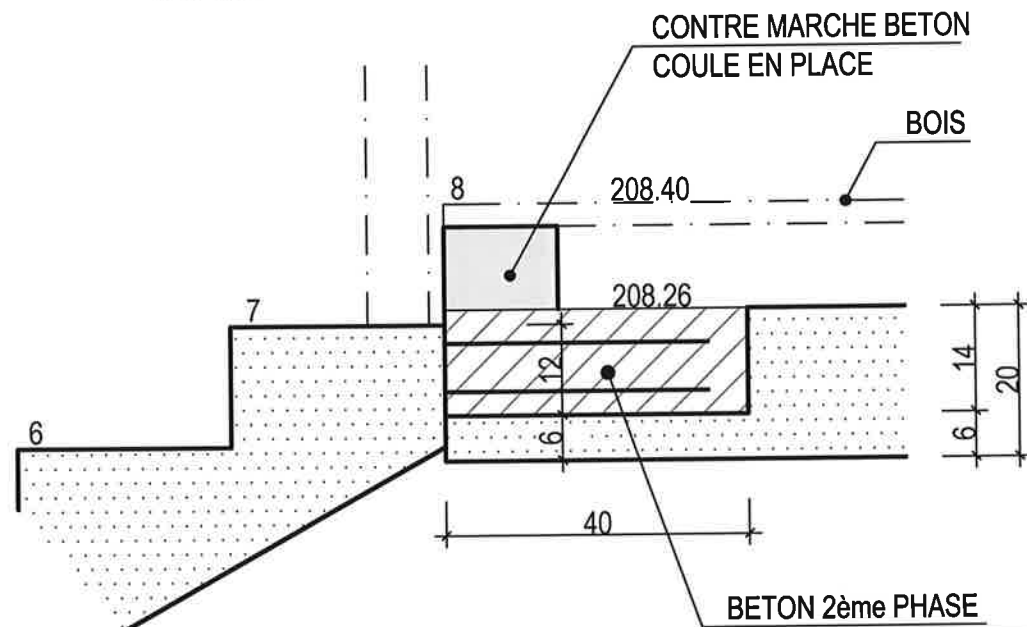**COUPE A**

Ech: 1/25

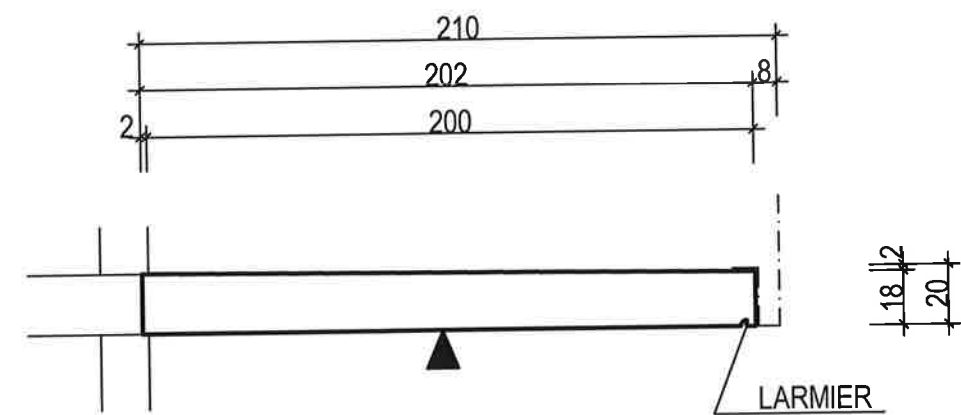


B4

Poids: 3700 Kg

	Entre files 10 et 14	Entre files 14 et 19
Plancher sur +2	0	0
Plancher sur +1	0	0
Plancher sur REZ	0	0
Plancher sur -1	0	0
Plancher sur -2	0	0
Plancher sur -3	0	0
Plancher sur -4	0	1
Plancher sur -5	0	0



COUPE A

Ech: 1/25

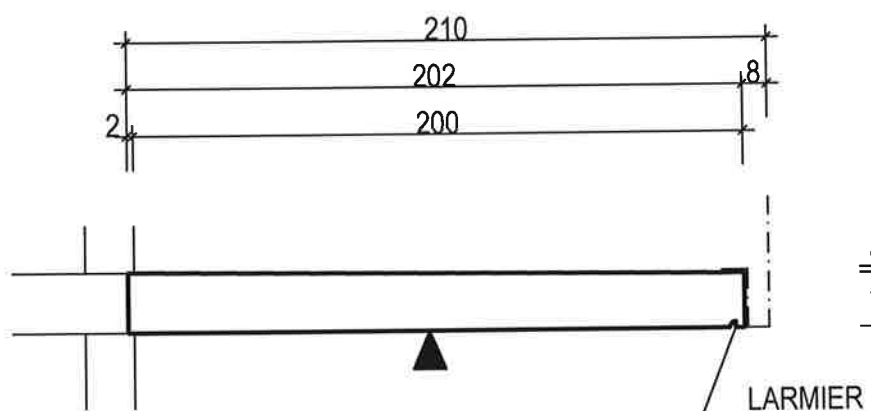


COUPE B

Ech: 1/25

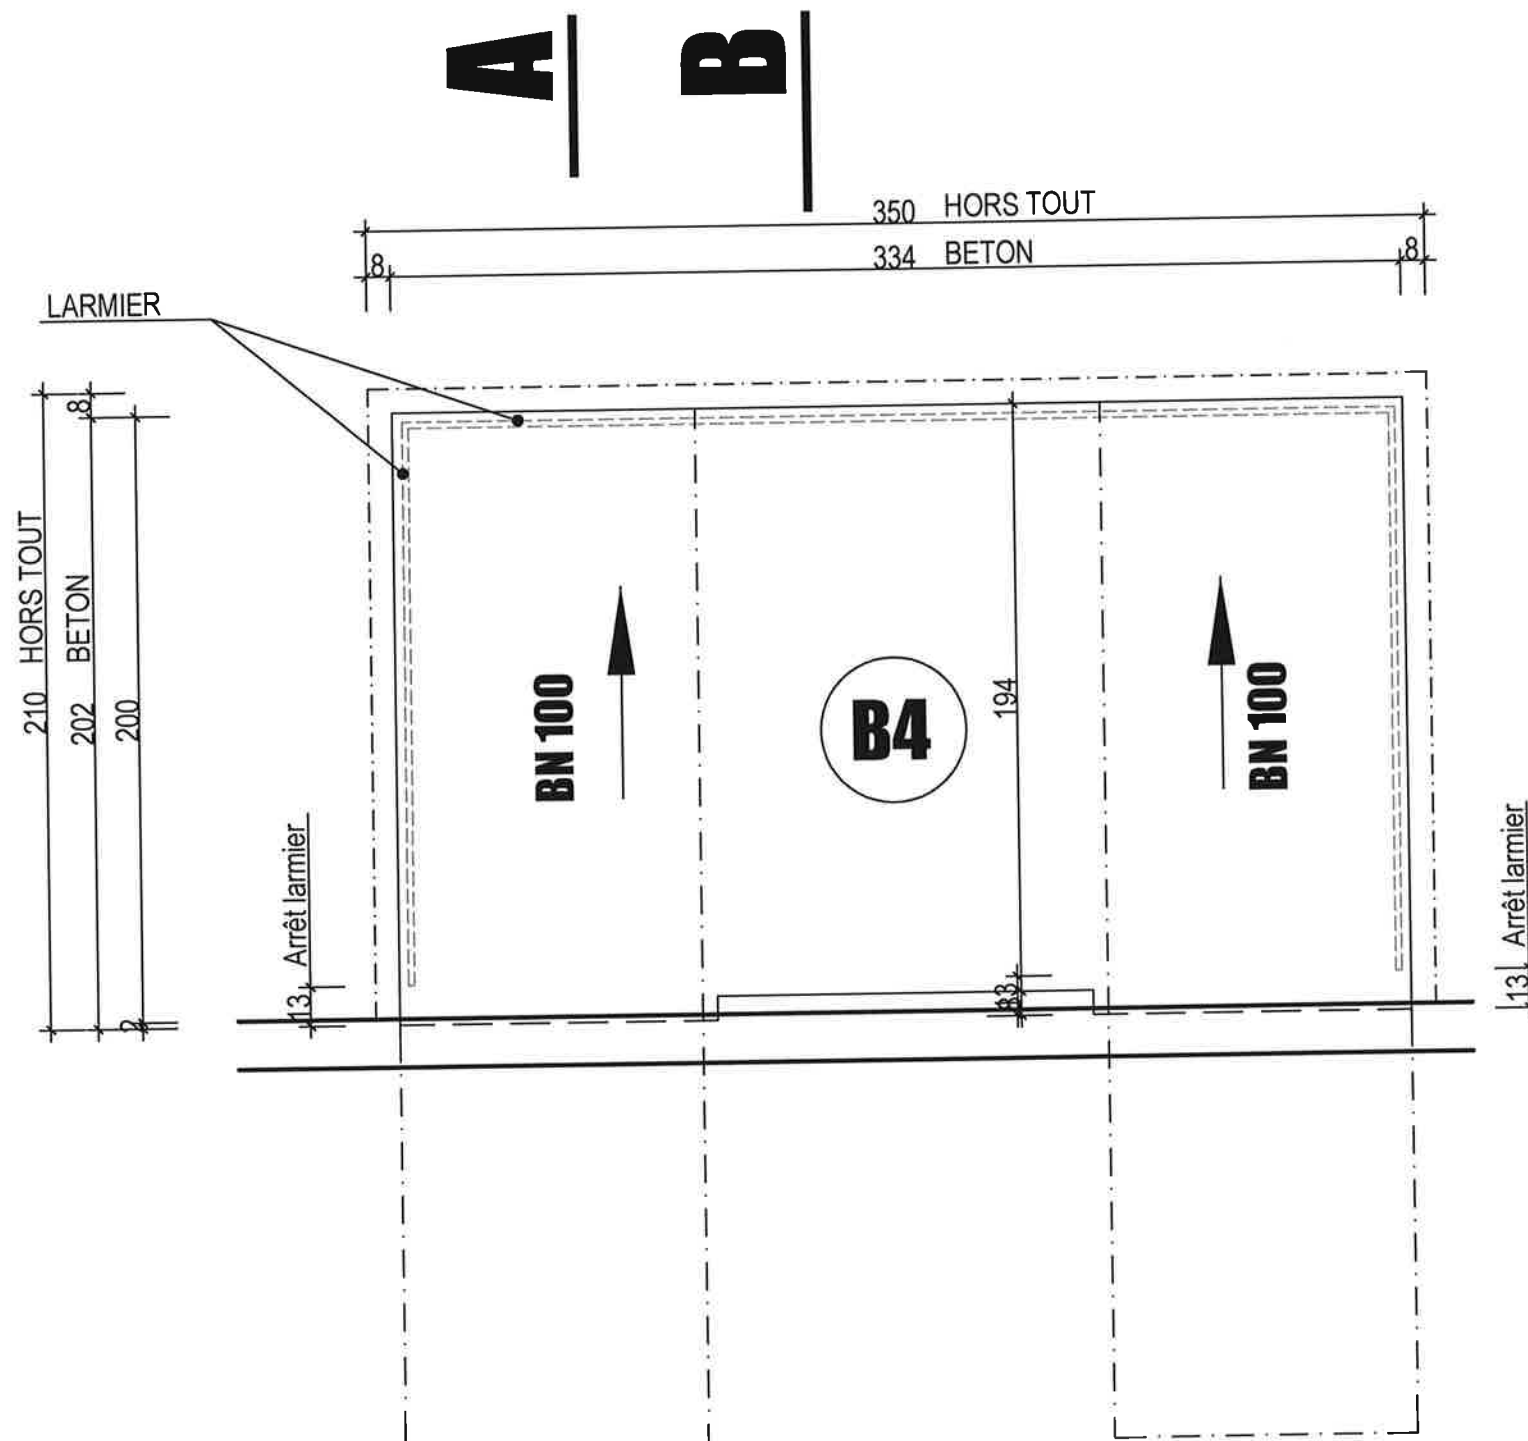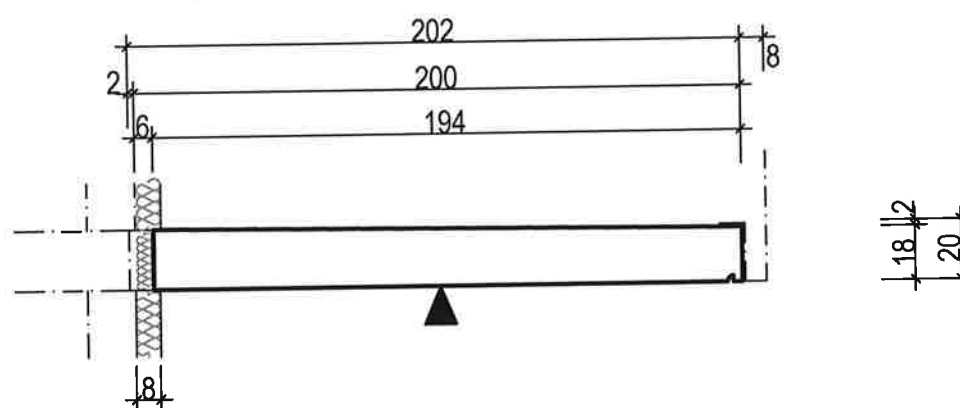

Vue en plan


Ech: 1/50

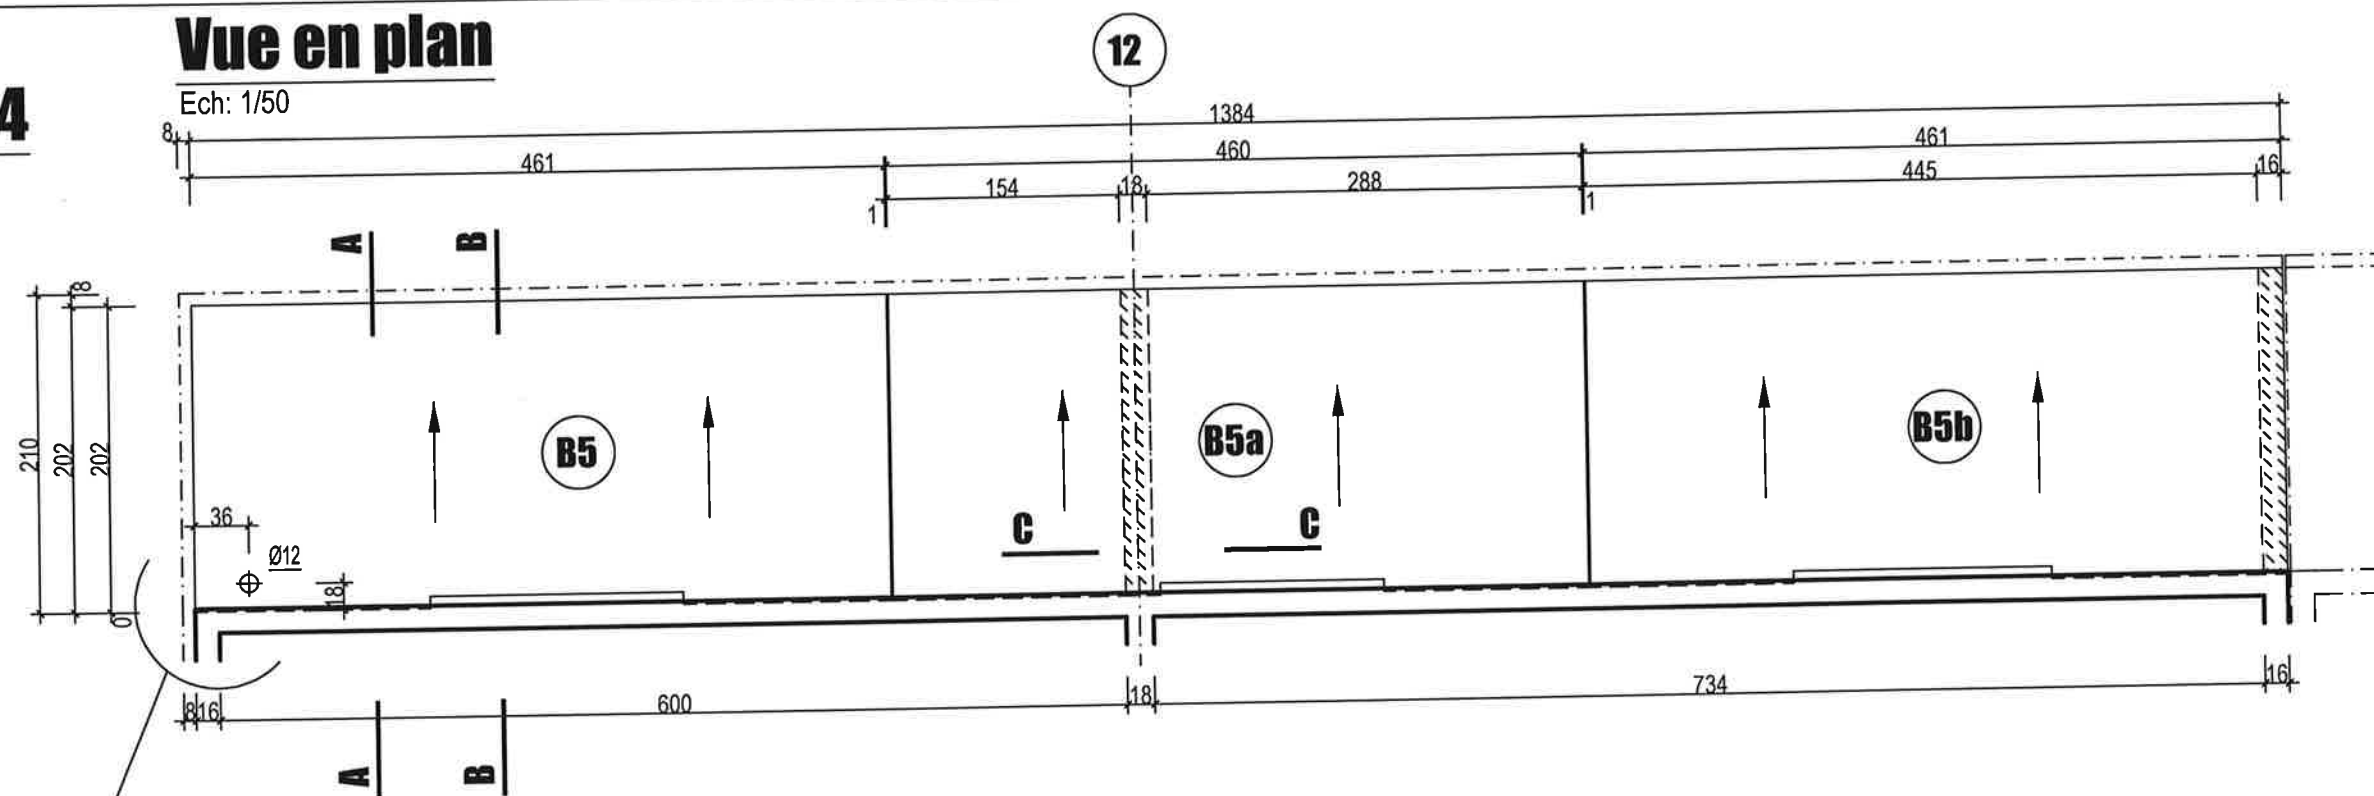

DETAIL

Ech: 1/10

GARDE-CORPS
VERRE

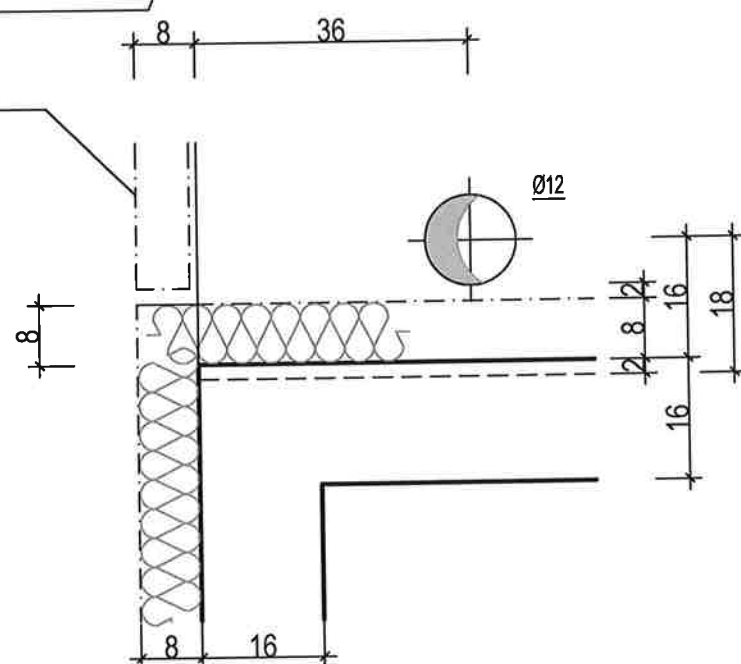


COUPE C

Ech: 1/25


BALCON PREFAB

MUR de REFEND

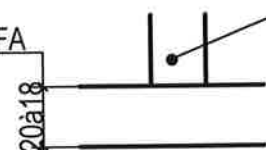


COUPE A

Ech: 1/25

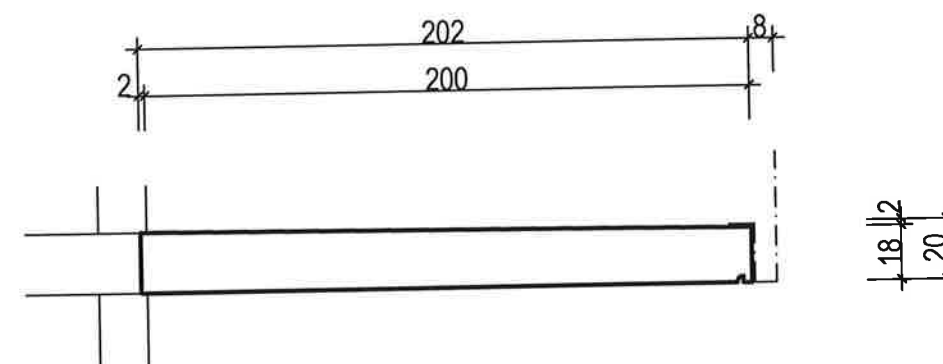

COUPE B

Ech: 1/25


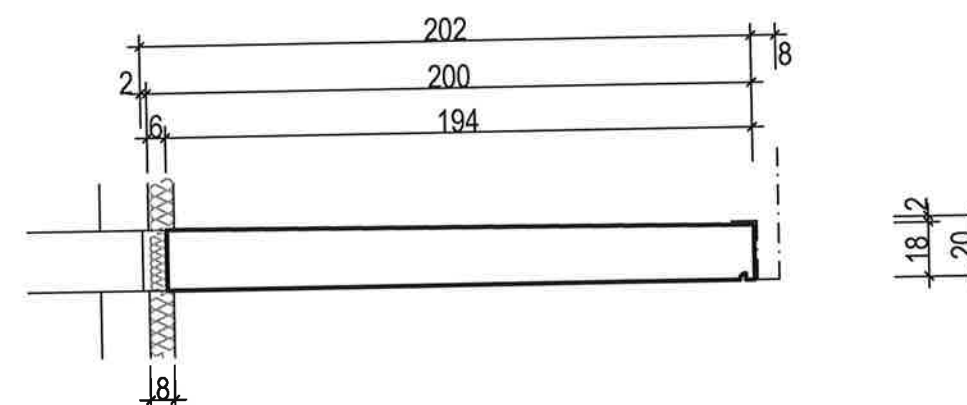


B5 1 p

Poids: 4850 Kg


DETAIL

Ech: 1/10

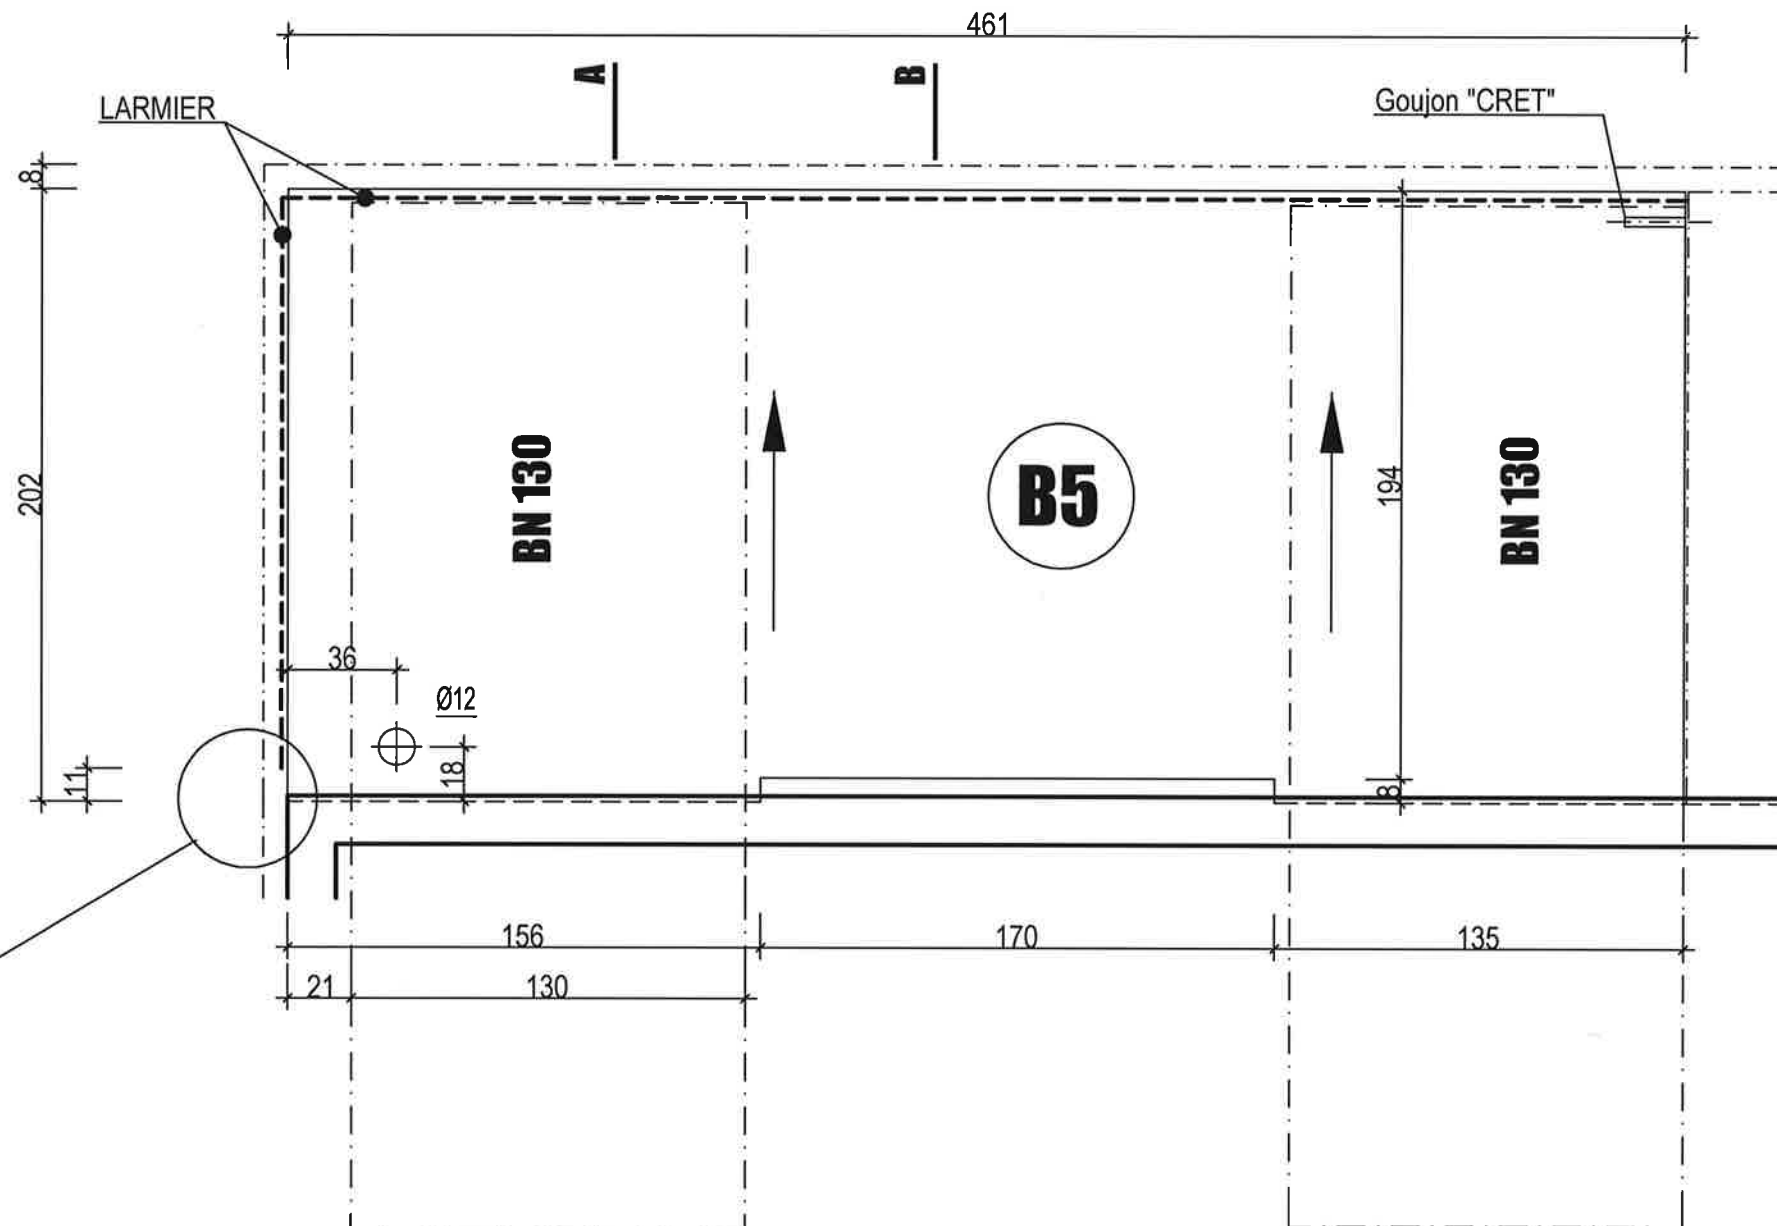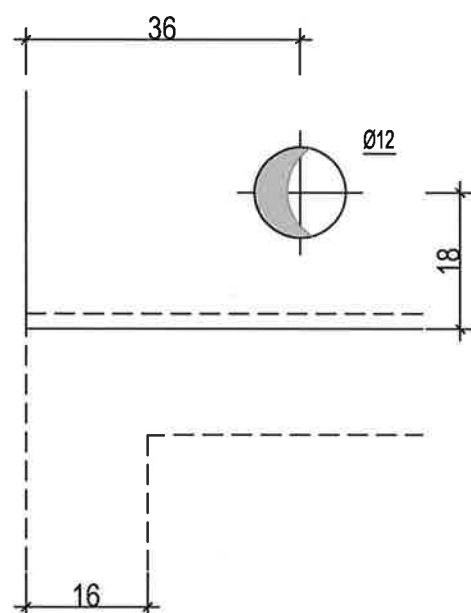


COUPE A

Ech: 1/25

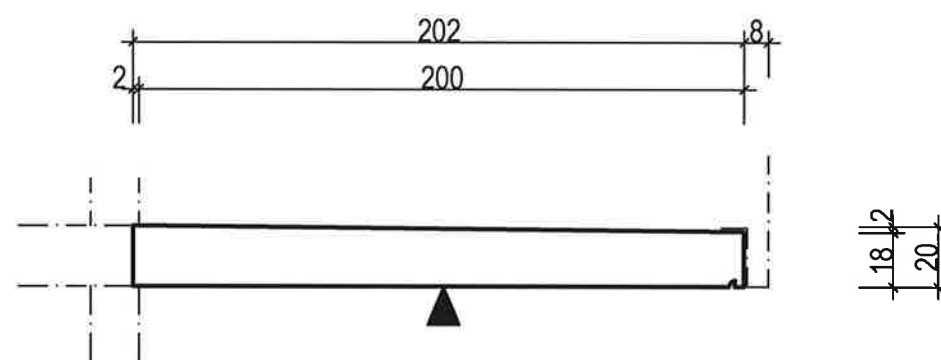

COUPE B


Ech: 1/25

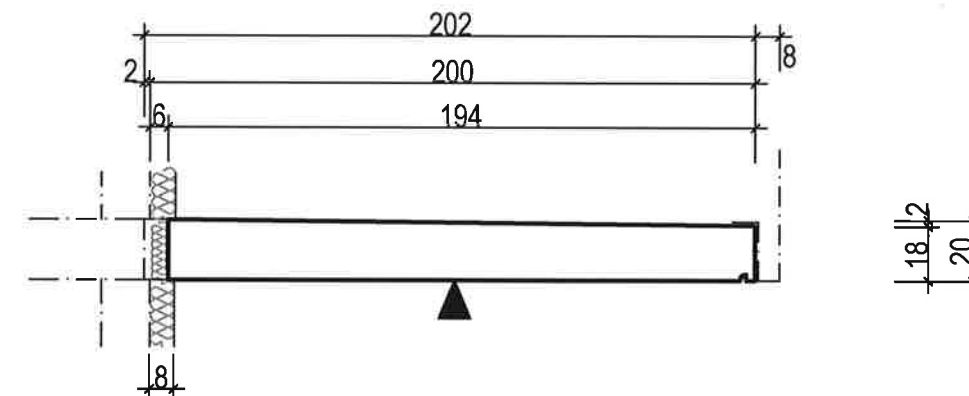

B5a


1 p

Poids: 4850 Kg

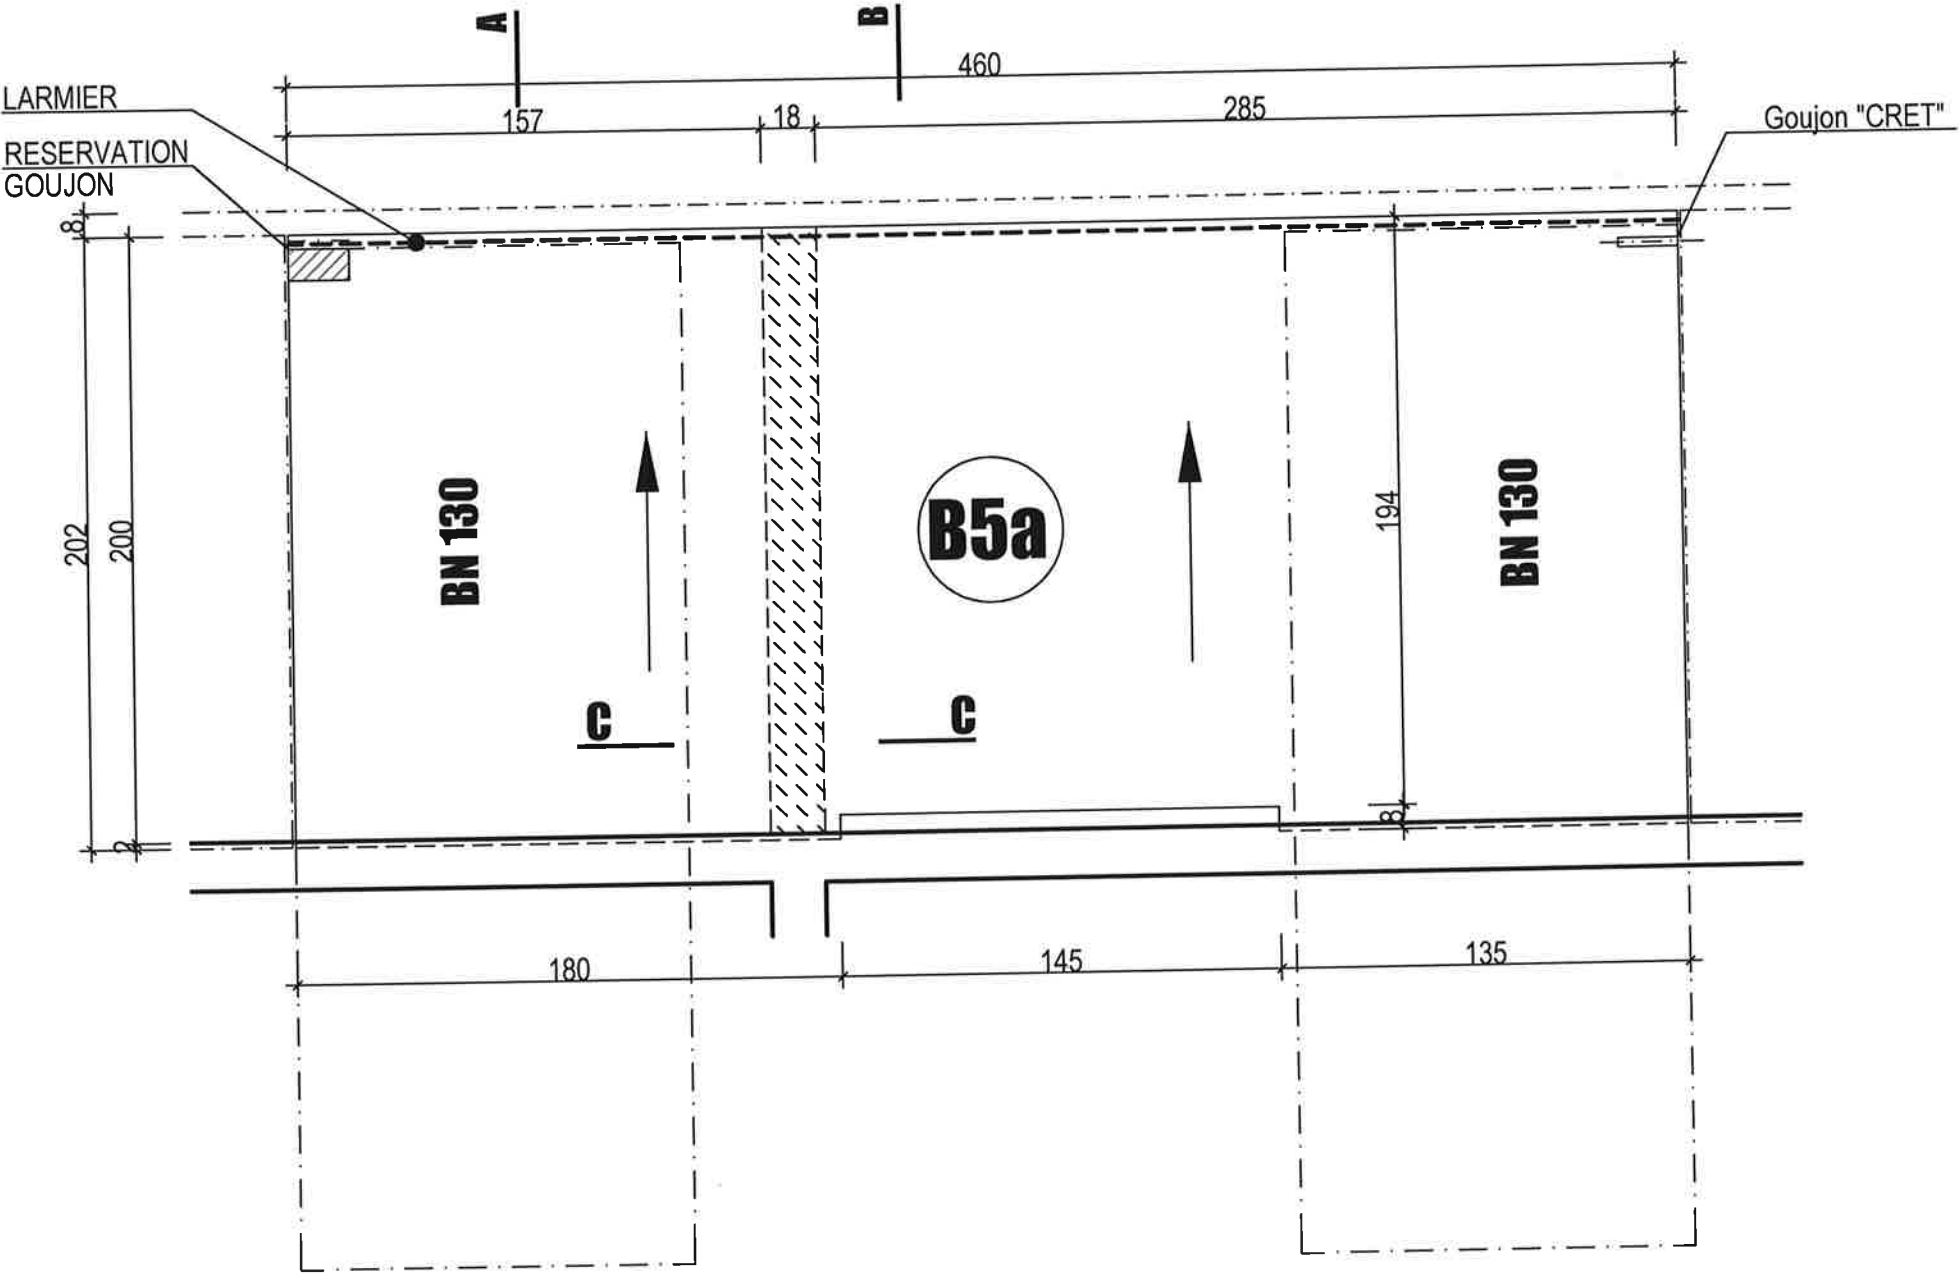


COUPE C

Ech: 1/10

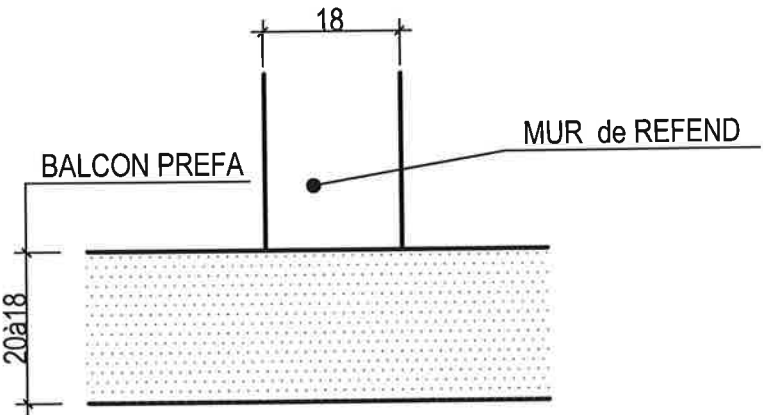



COUPE A

Ech: 1/25

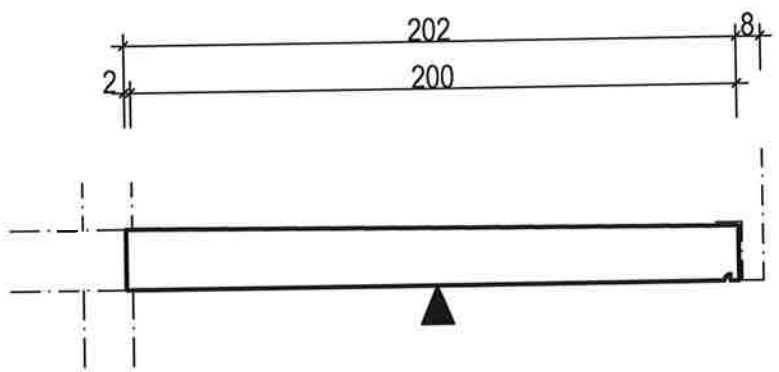

COUPE B

Ech: 1/25

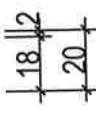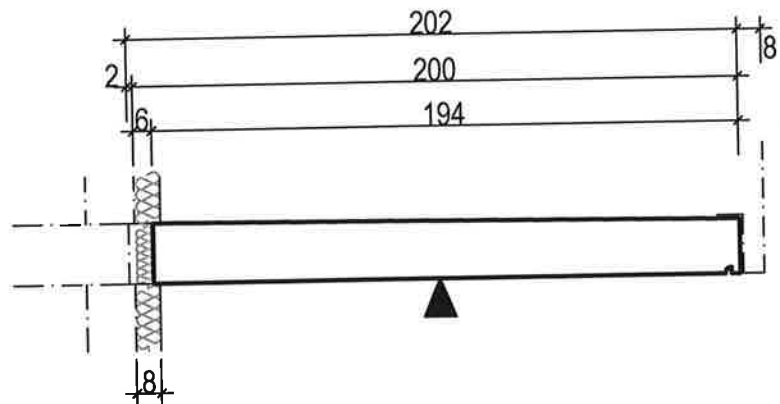

B5b

1 p

Poids: 4850 Kg

LARMIER
RESERVATION
GOUJON

Goujon "CRET"

BN 130

B5b

BN 130

C

C

COUPE C




Ech: 1/10

COUPE A

Ech: 1/25

COUPE B


Ech: 1/25

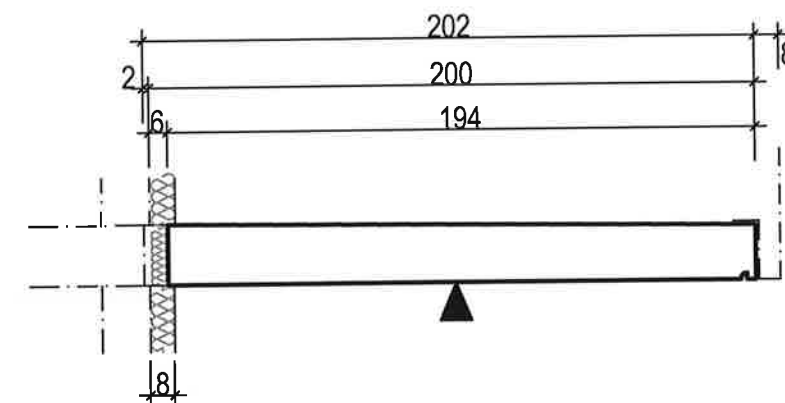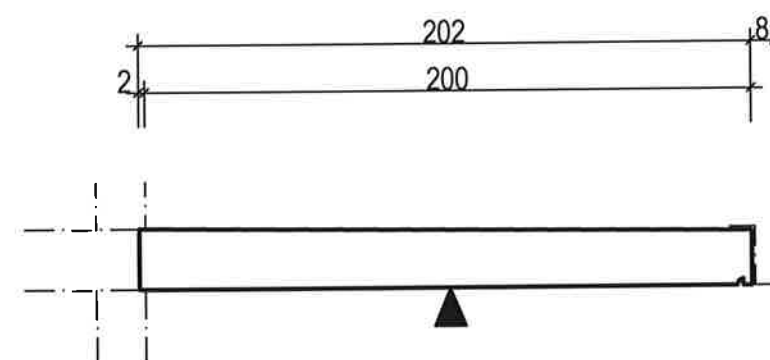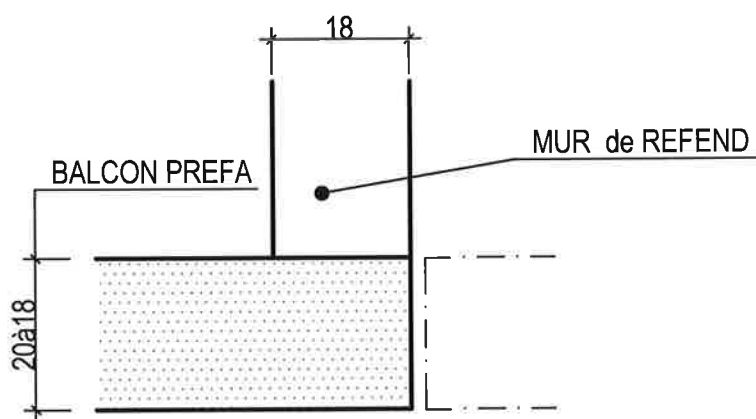

PLANCHER sur -3

Vue en plan


Ech: 1/50

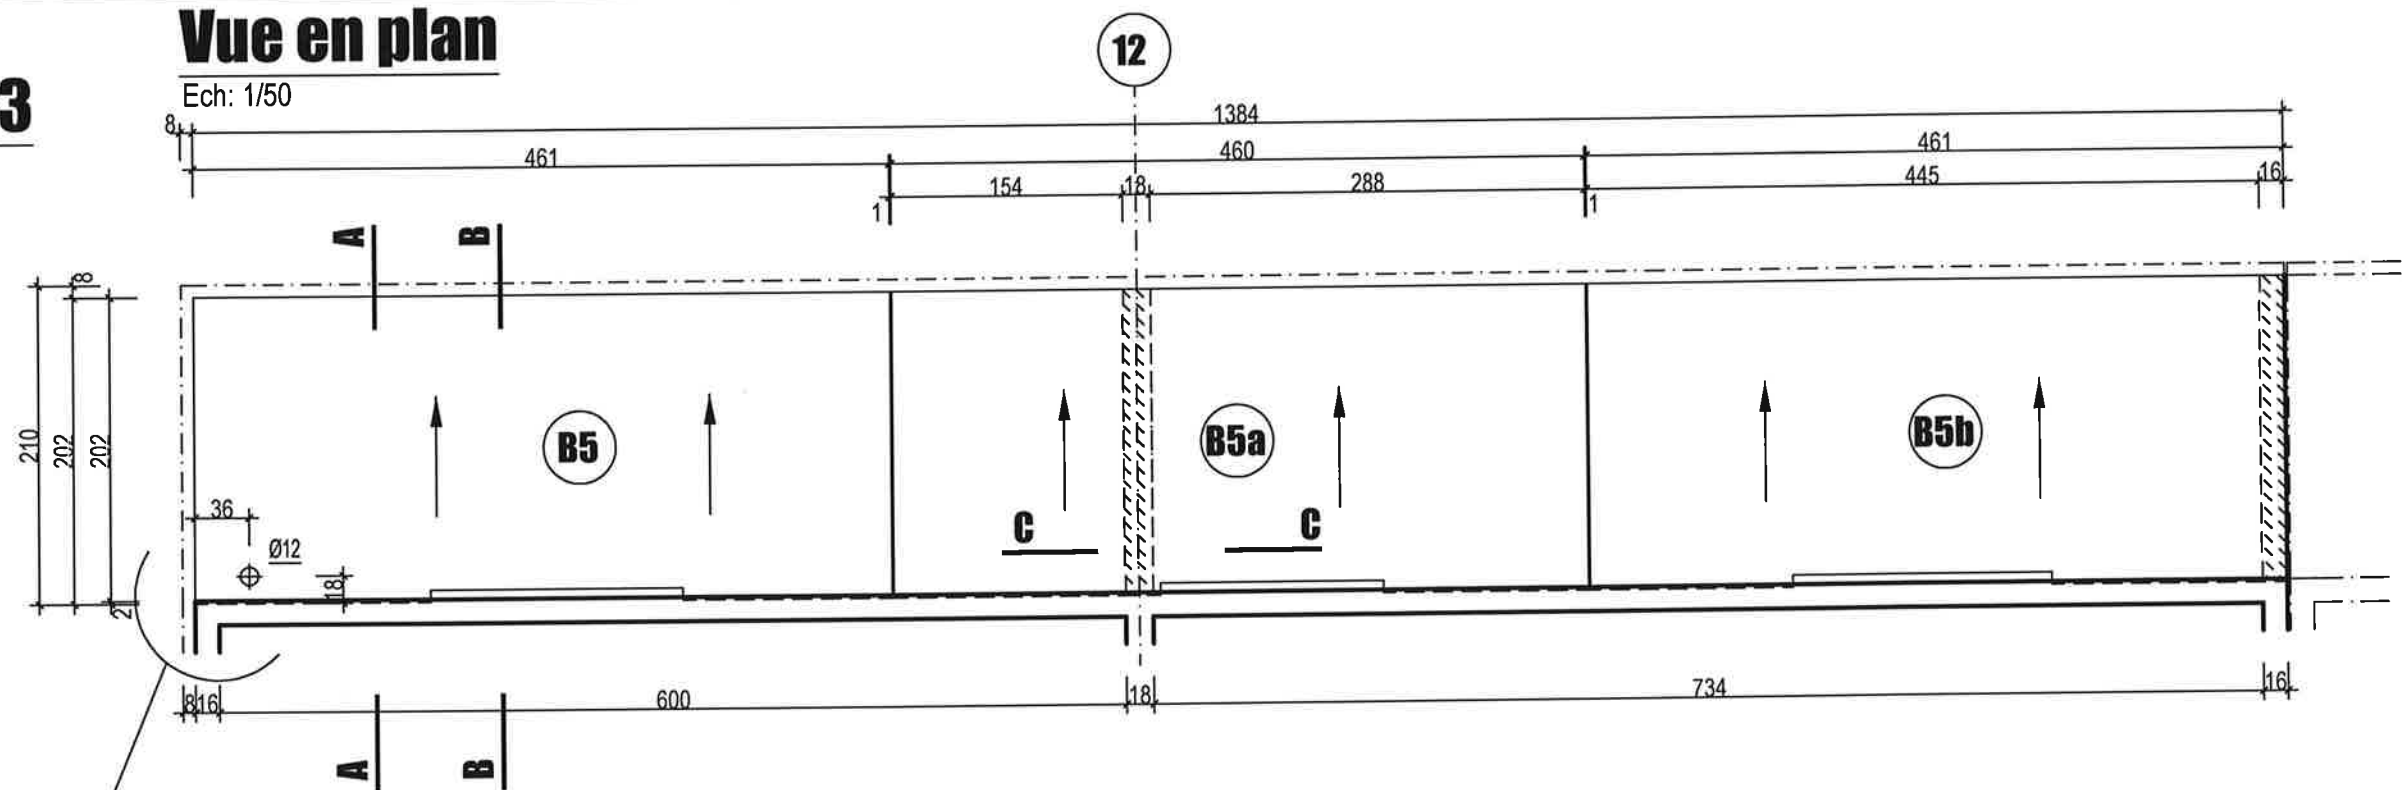

DETAIL


Ech: 1/10

GARDE-CORPS
VERRE

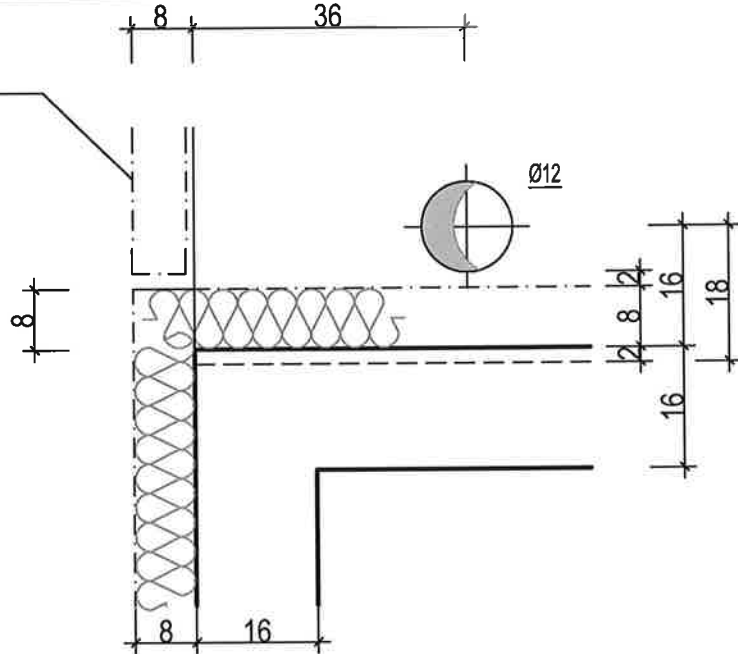


COUPE A

Ech: 1/25

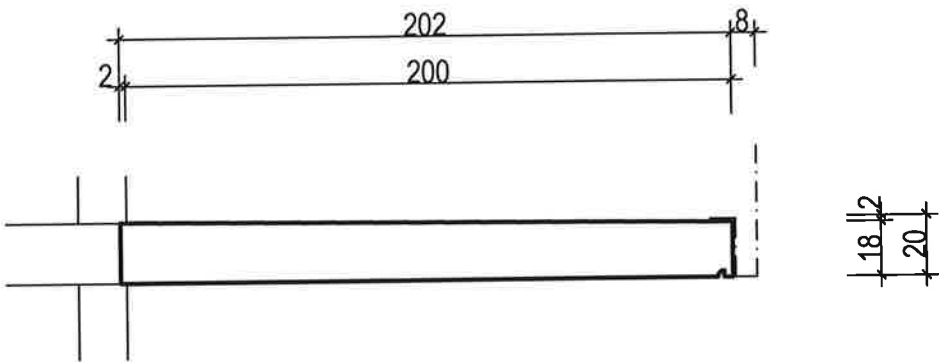


COUPE B

Ech: 1/25

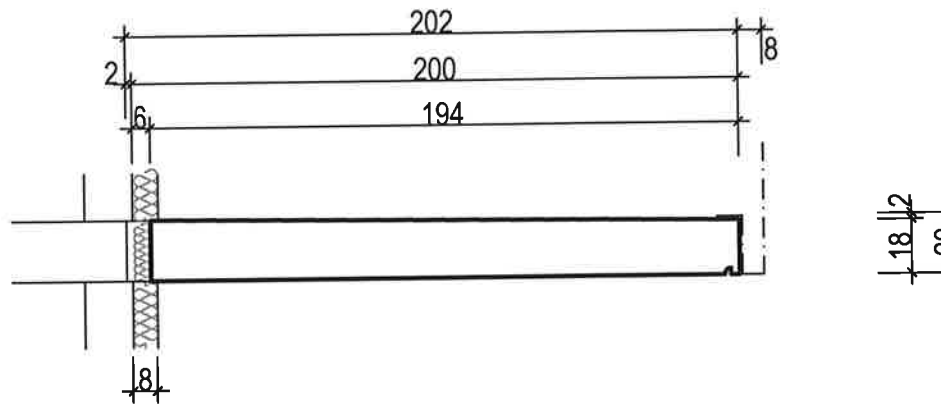

COUPE C

Ech: 1/25

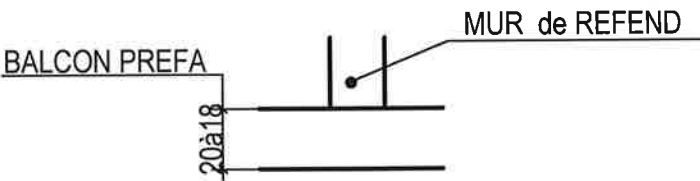



B5

1 p


Poids: 4850 Kg

DETAIL


Ech: 1/10

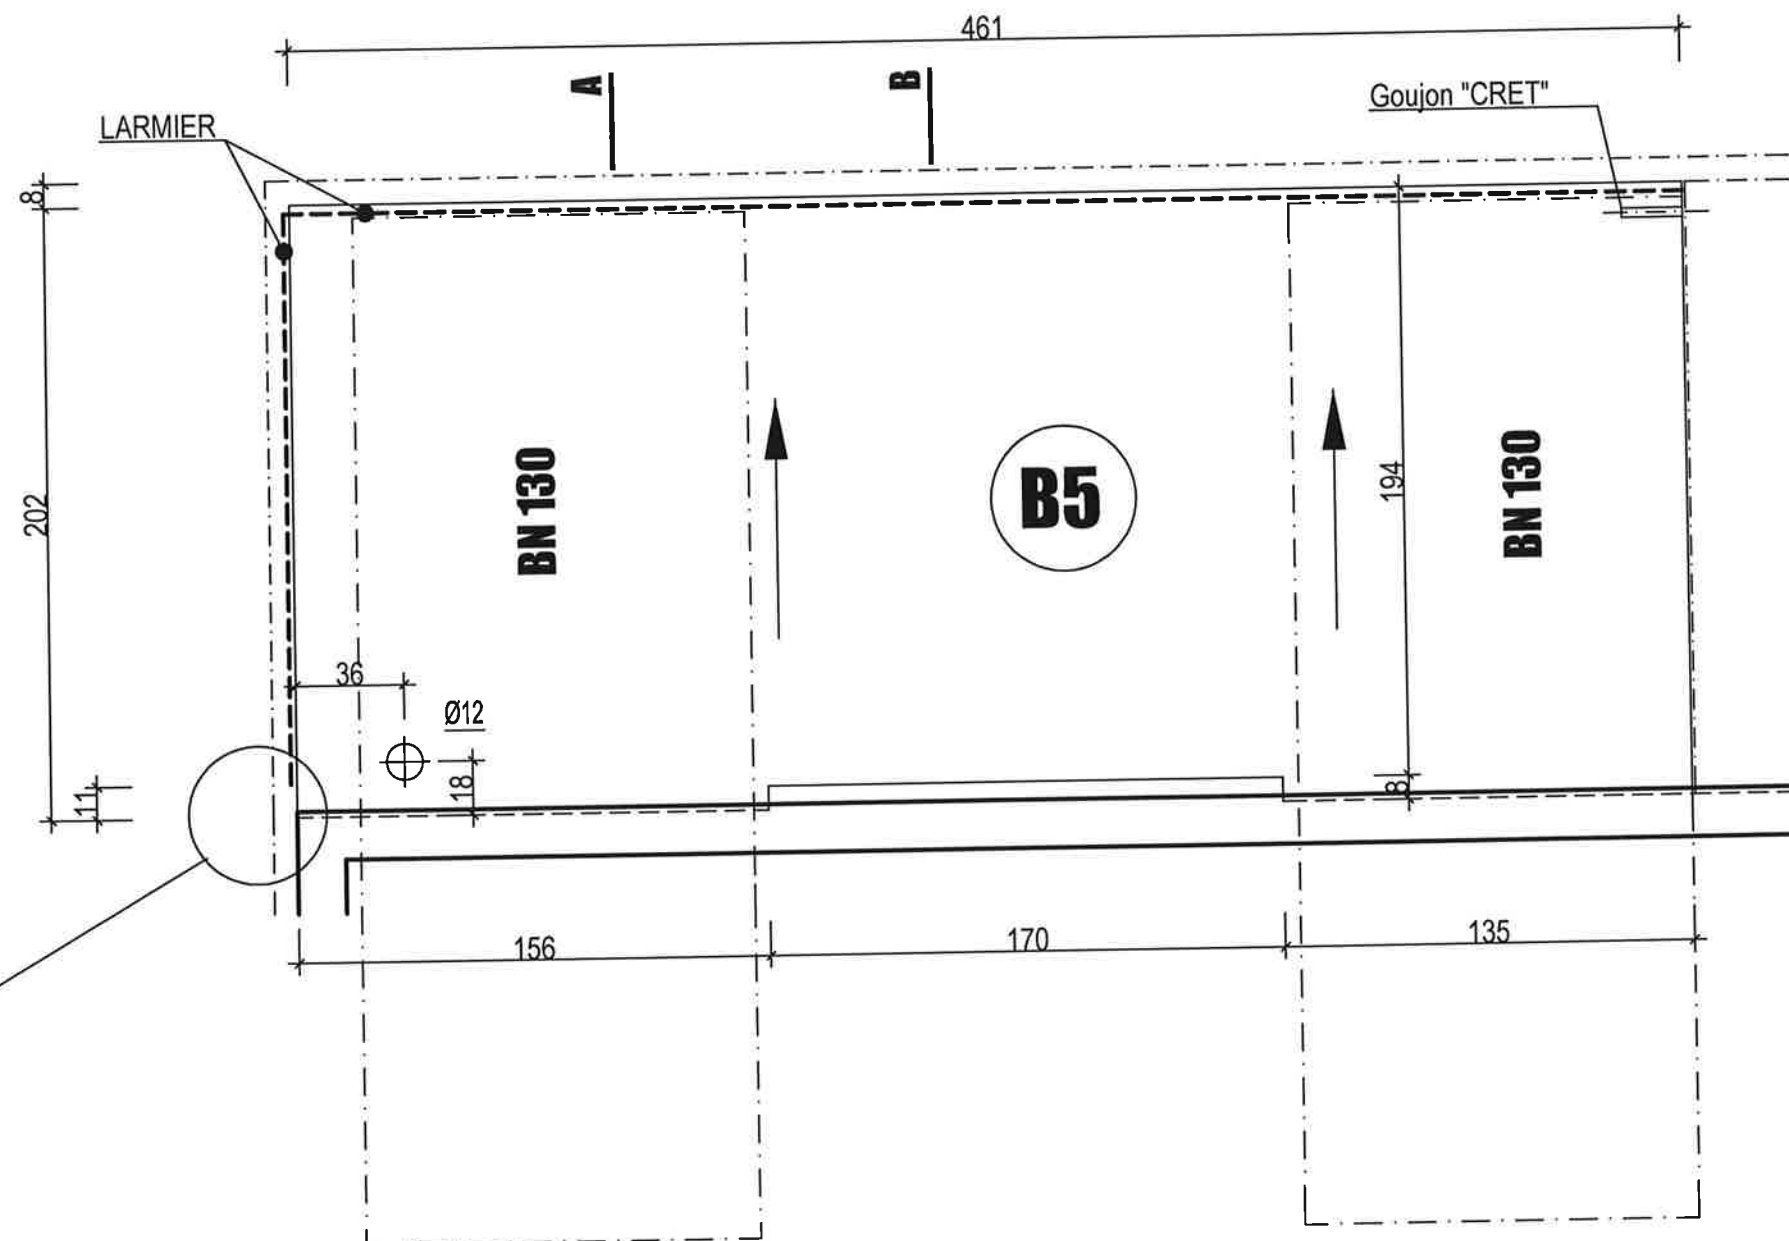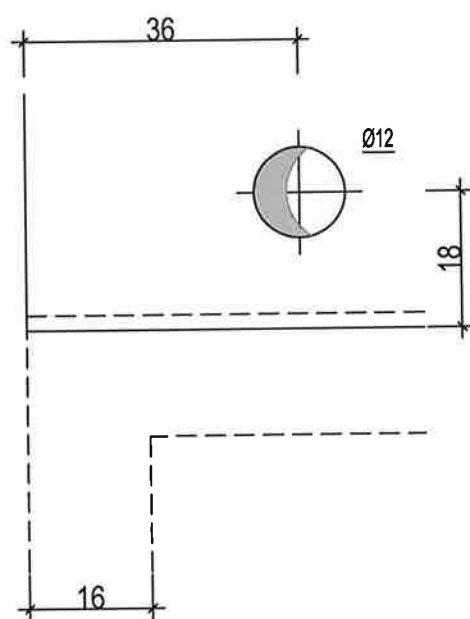**COUPE A**

Ech: 1/25

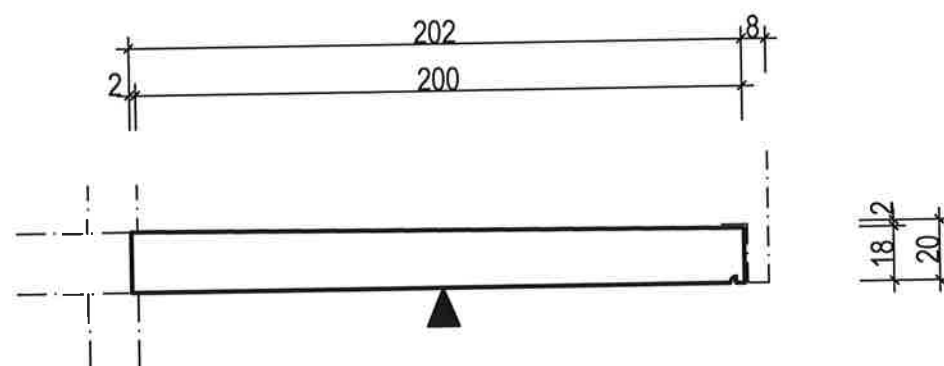
**COUPE B**

Ech: 1/25

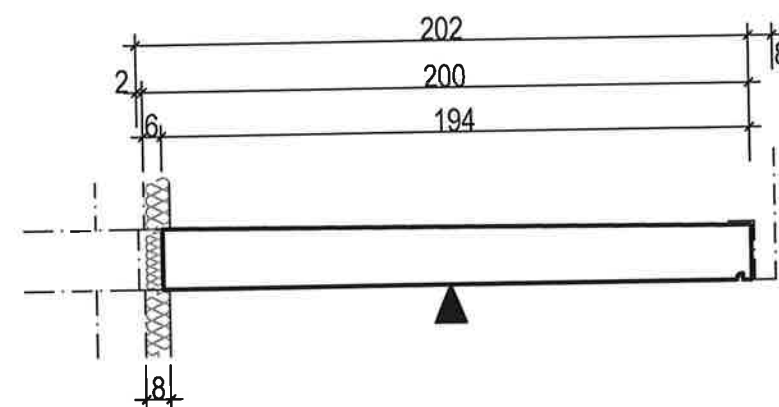


B5a 1 p

Poids: 4850 Kg

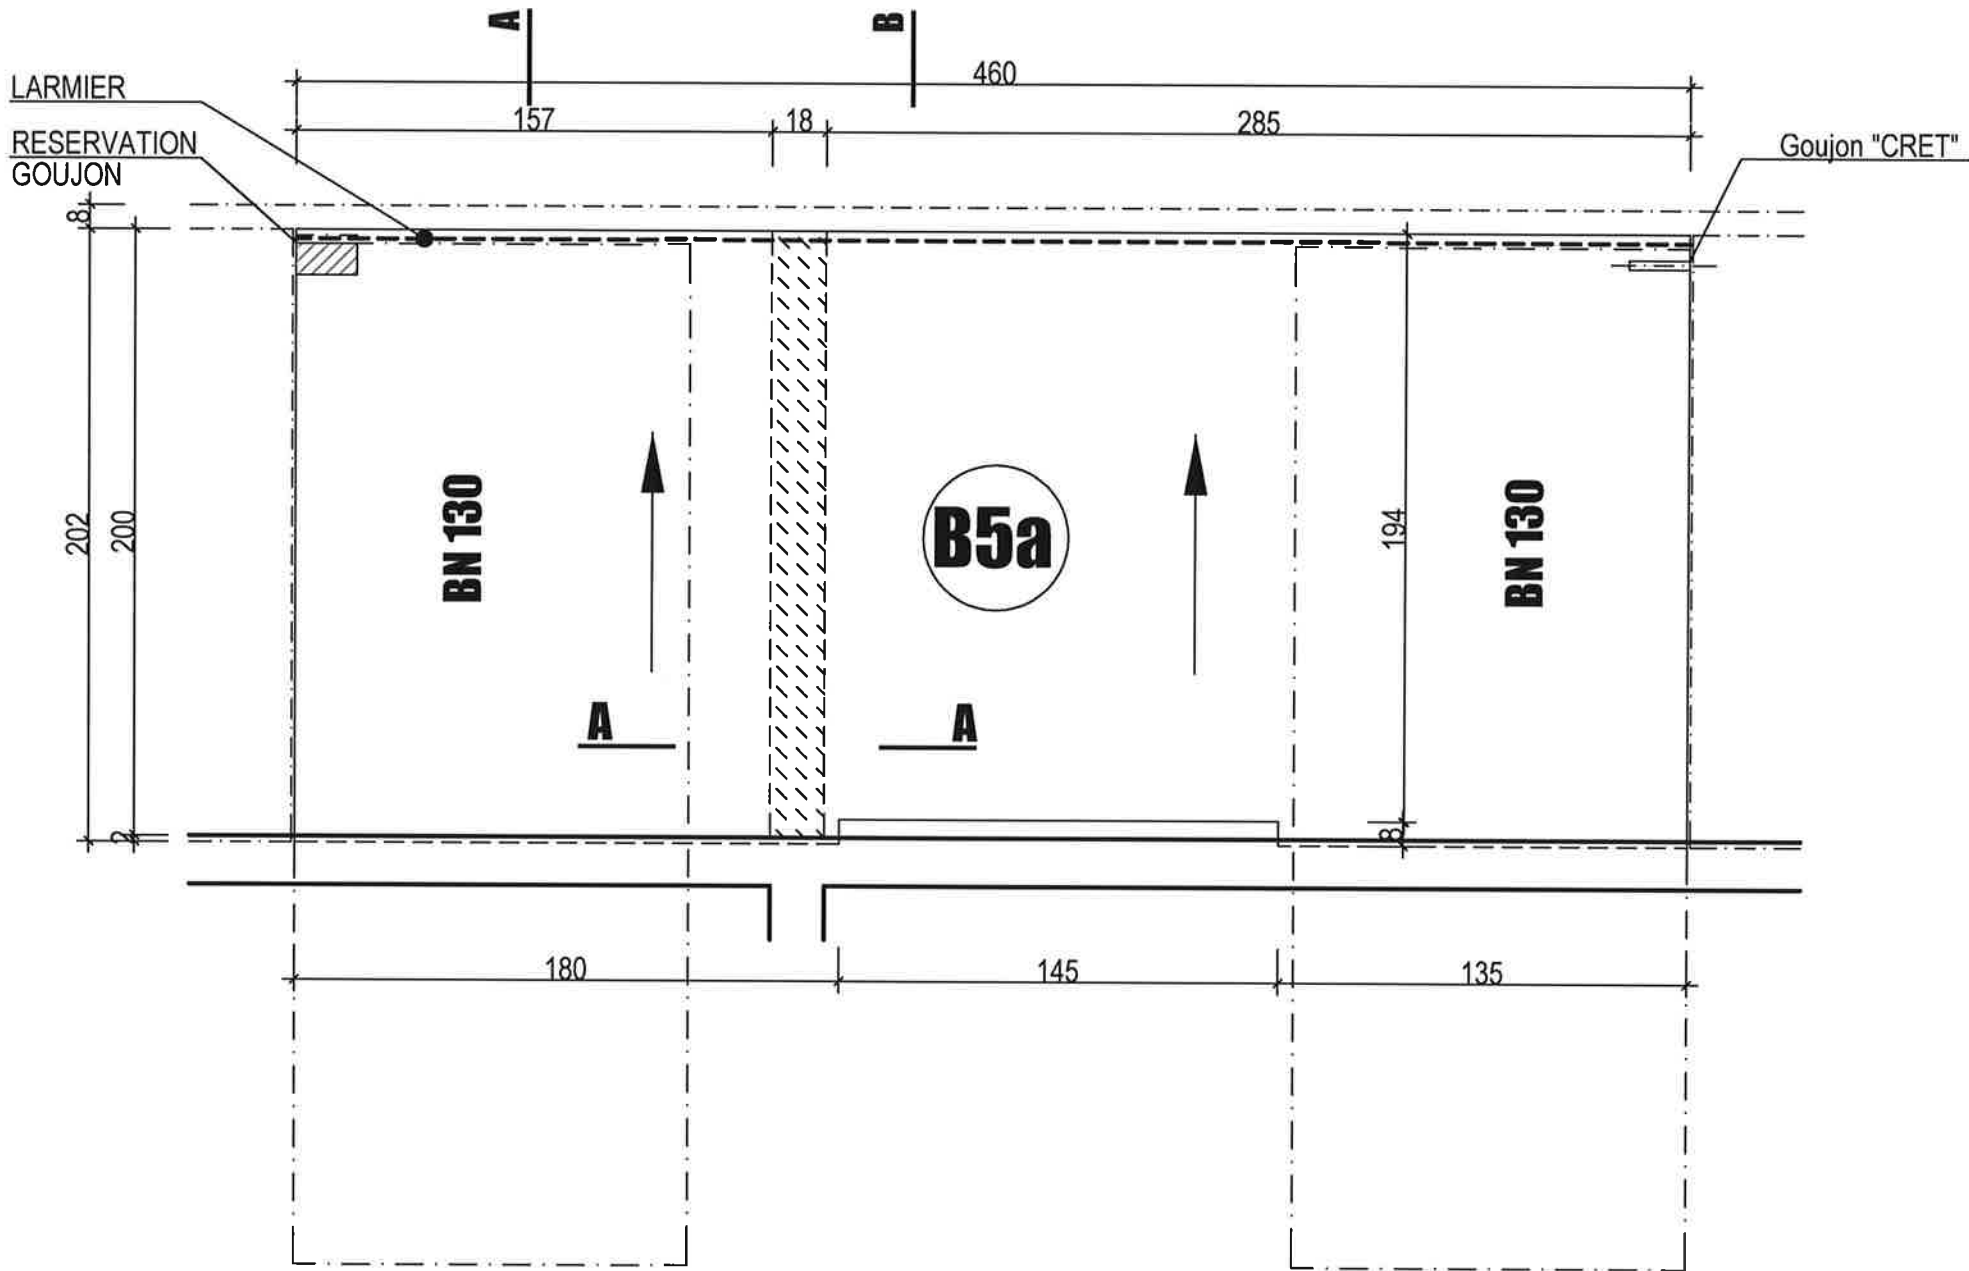


COUPE A

Ech: 1/10

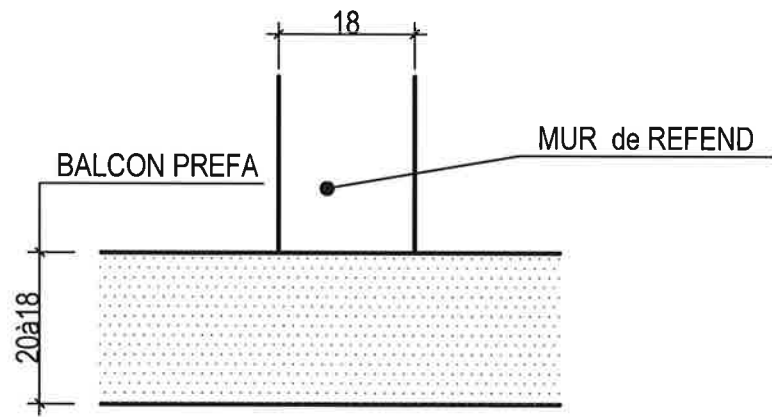


COUPE A

Ech: 1/25

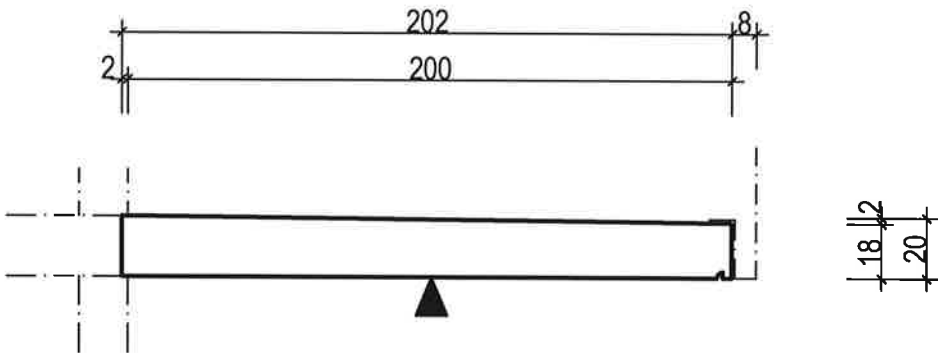


COUPE B


Ech: 1/25

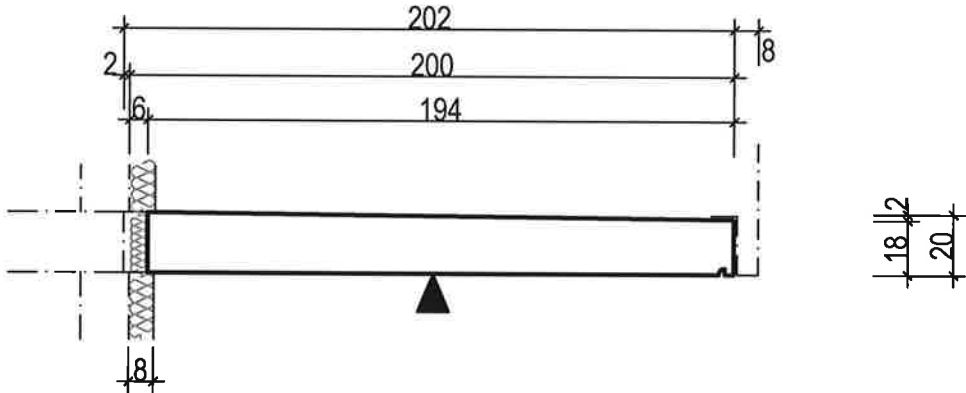


B5b 1 p
Poids: 4850 Kg

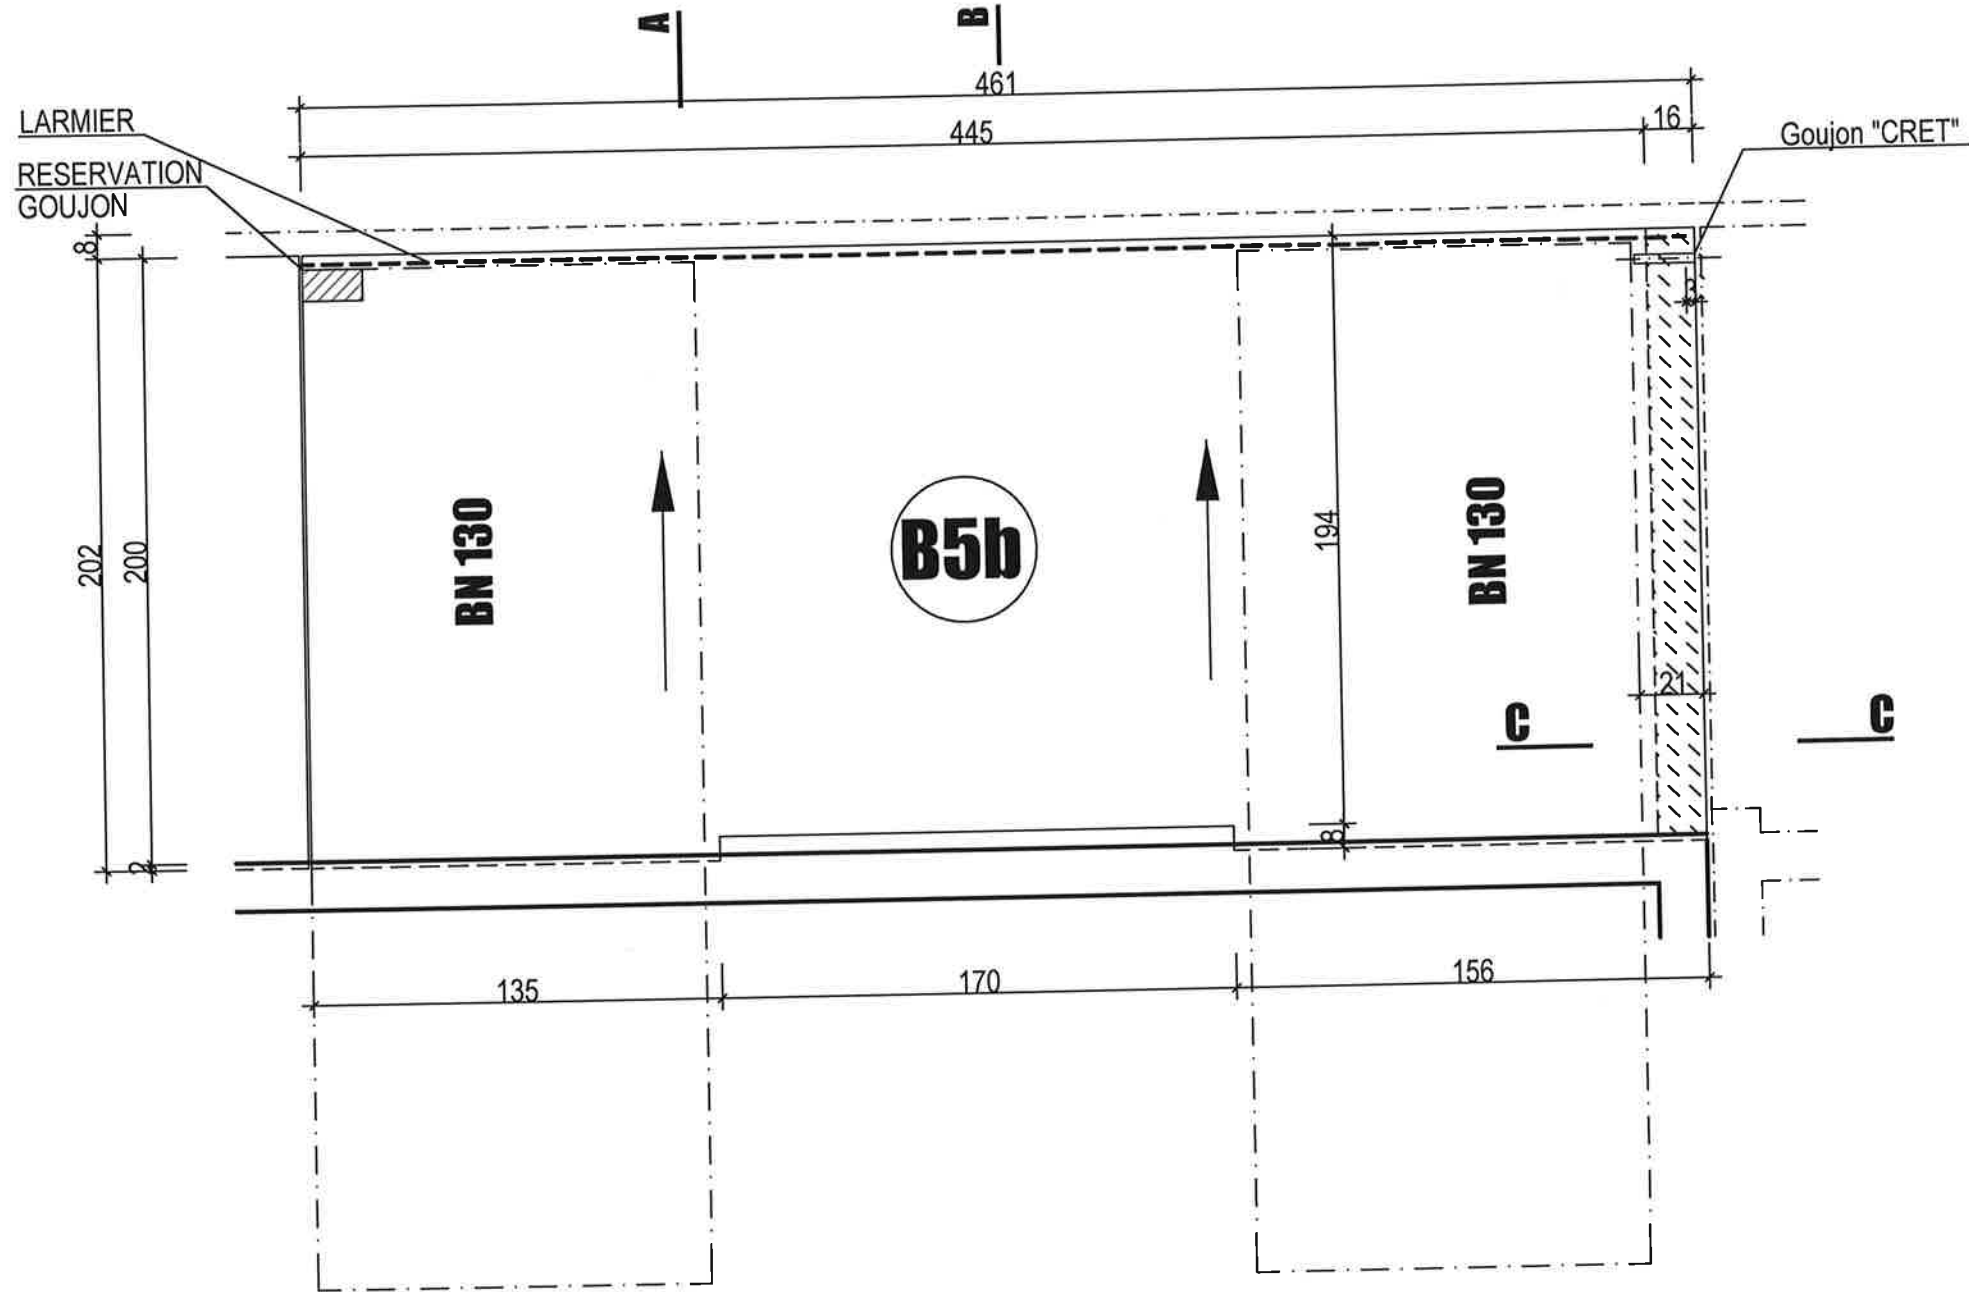


COUPE C
Ech: 1/10

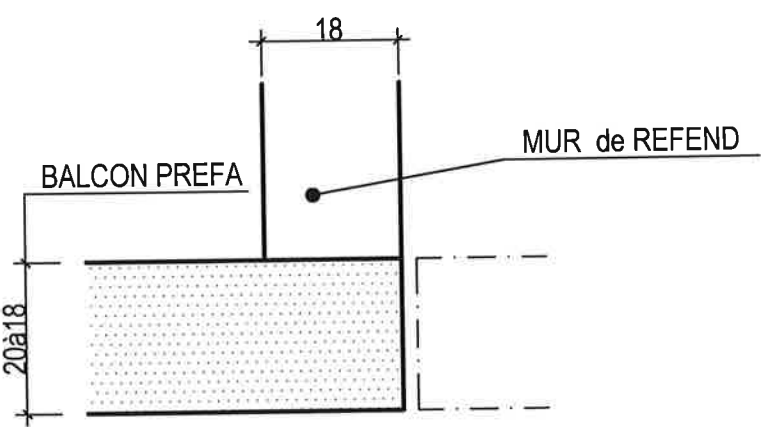

COUPE A
Ech: 1/25

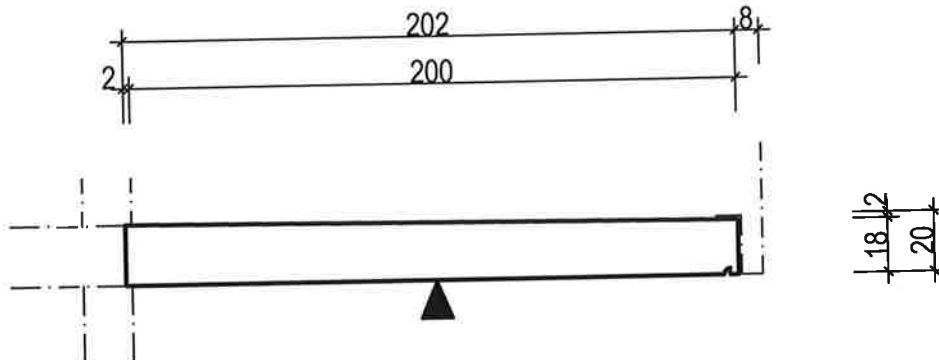

COUPE B
Ech: 1/25

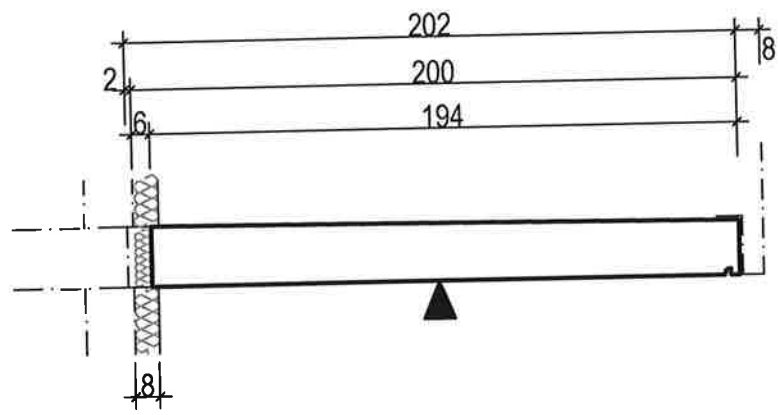


18
20

PLANCHER sur -2

Vue en plan


Ech: 1/50

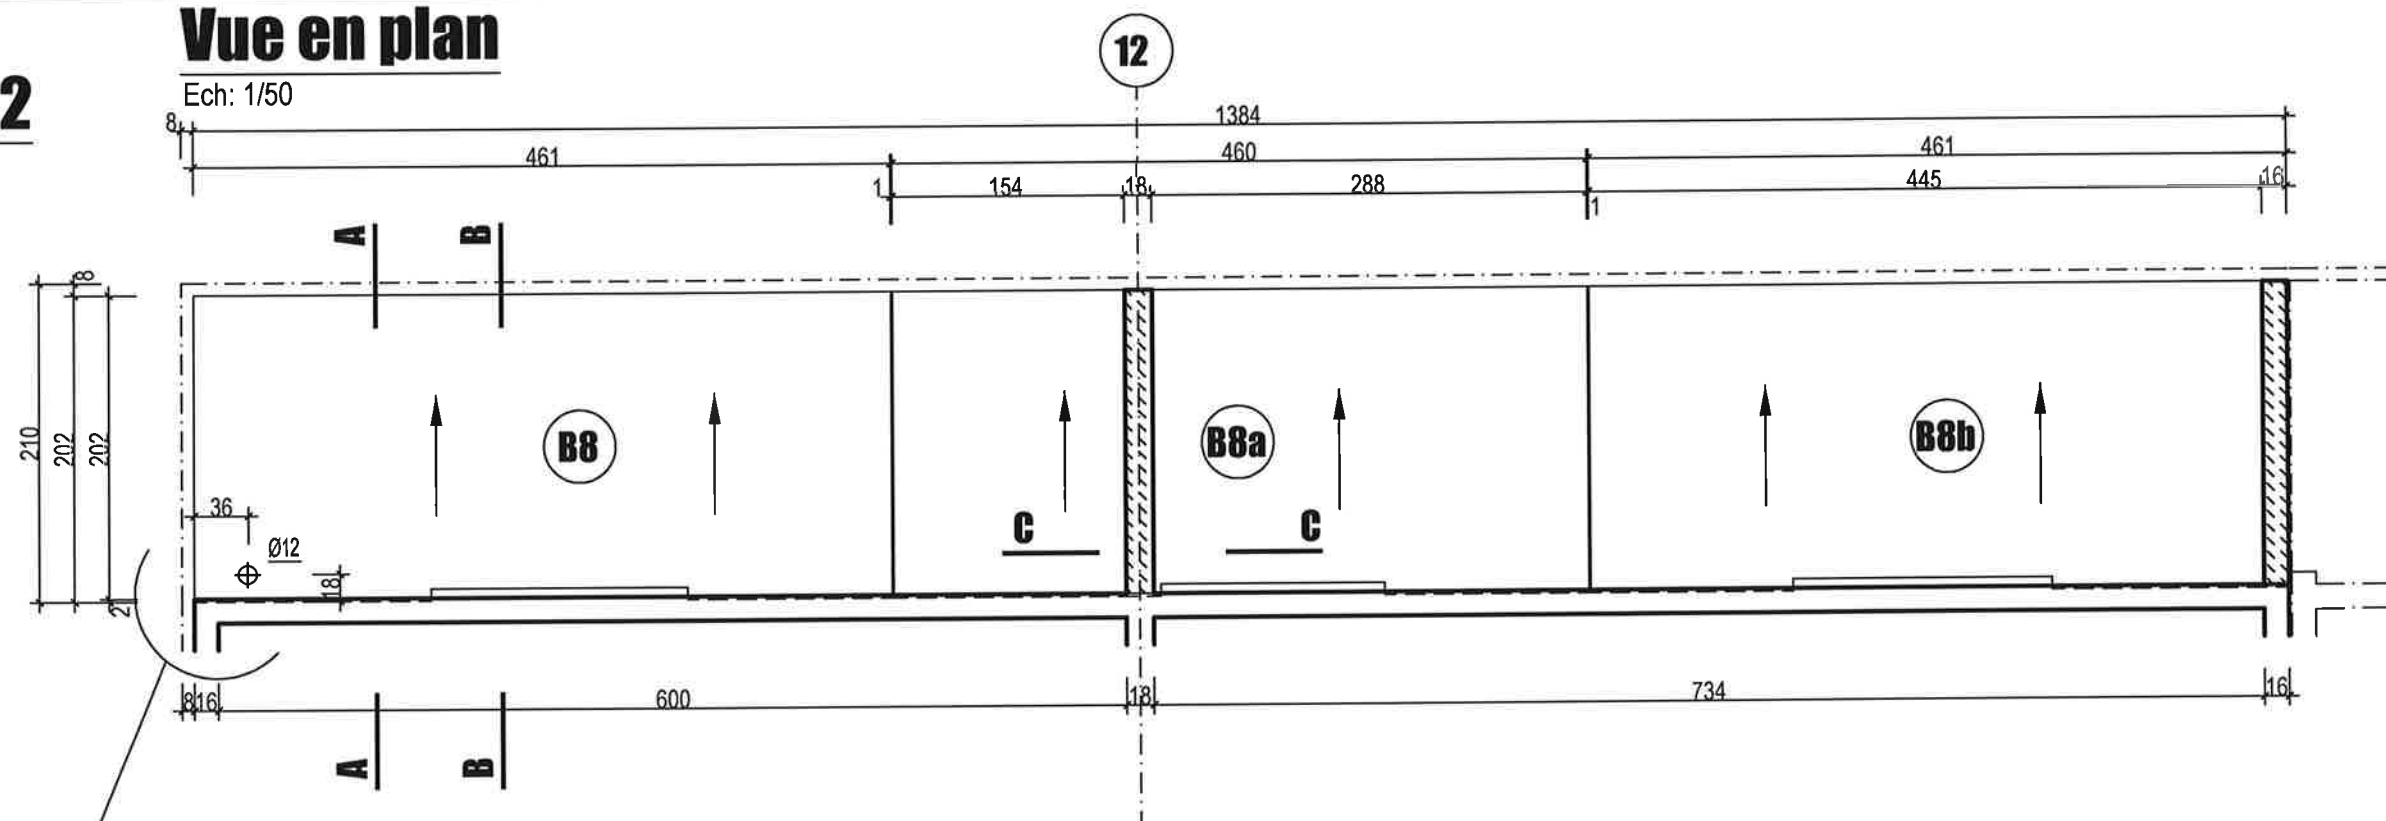

DETAIL


Ech: 1/10

GARDE-CORPS
VERRE

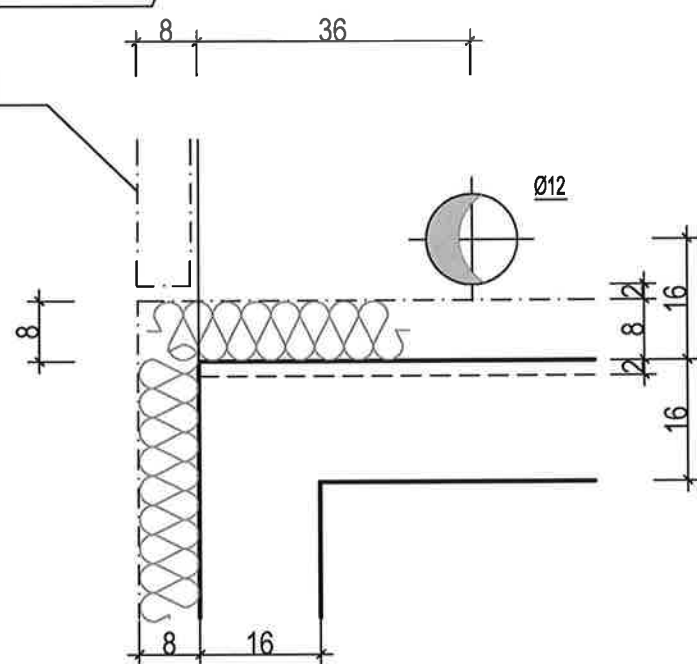


COUPE C

Ech: 1/25

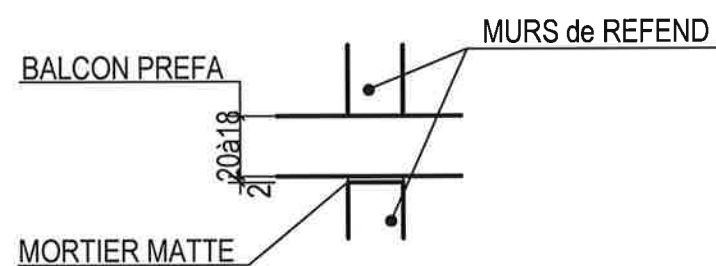


COUPE A

Ech: 1/25

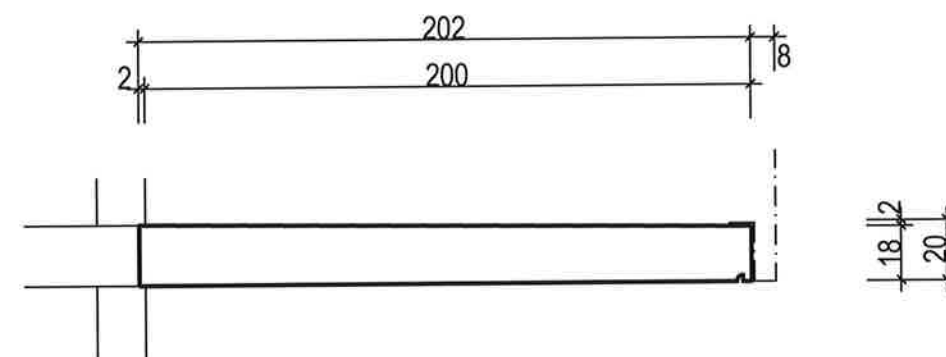

COUPE B

Ech: 1/25

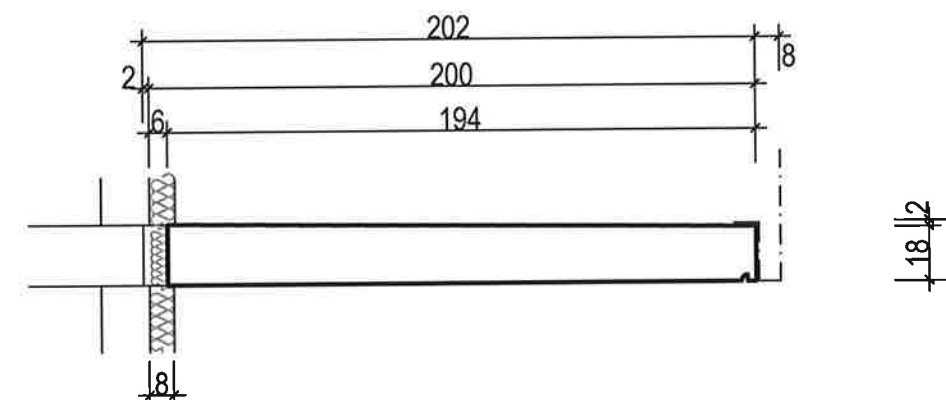



B8

1 p


Poids: 4850 Kg

DETAIL


Ech: 1/10

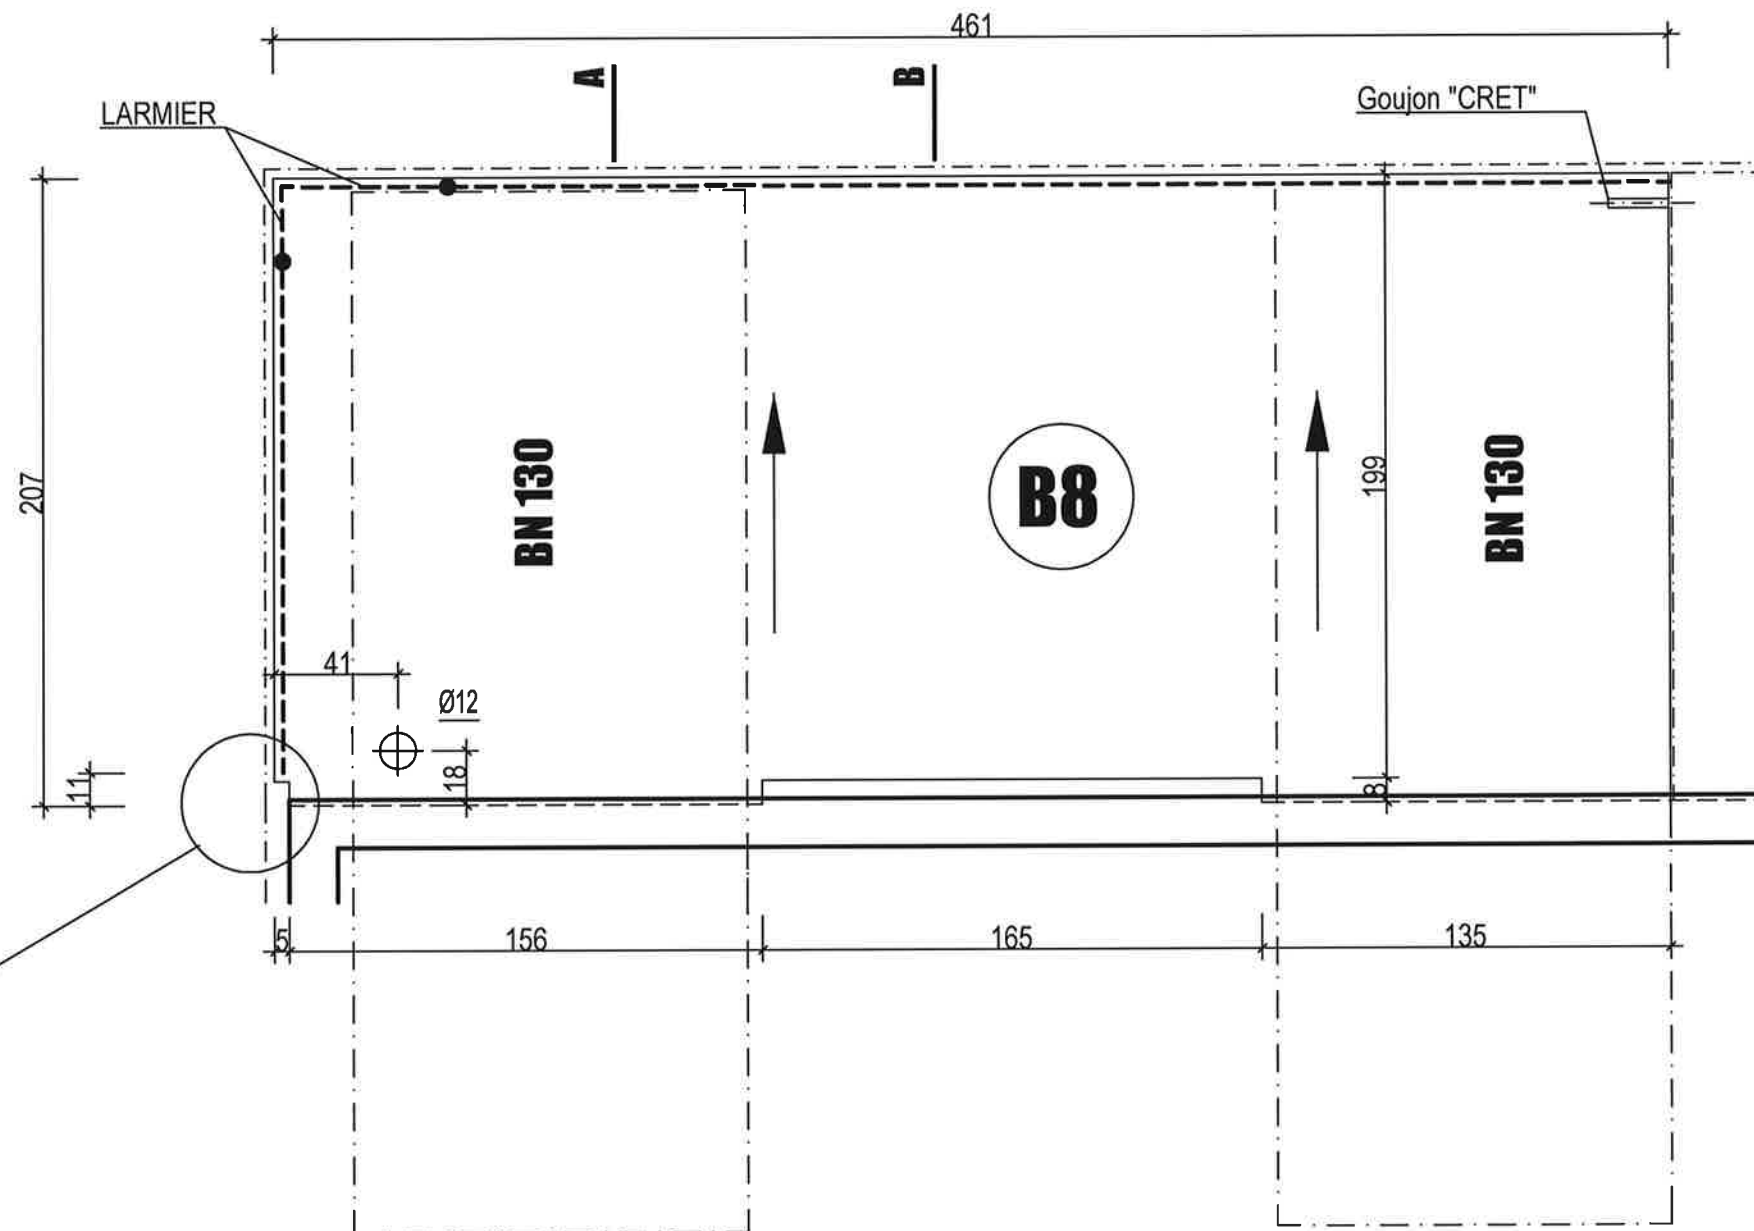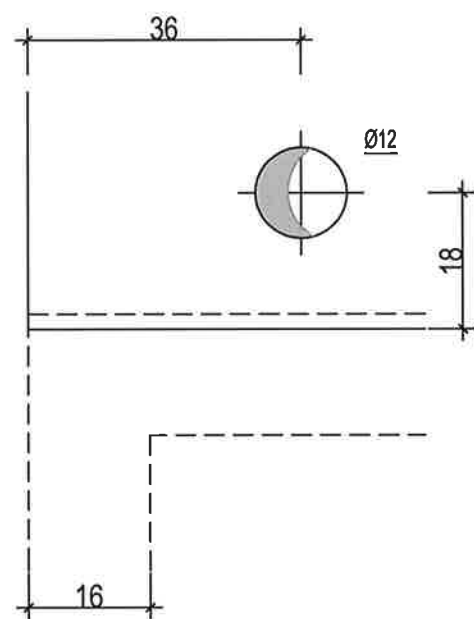**COUPE A**

Ech: 1/25

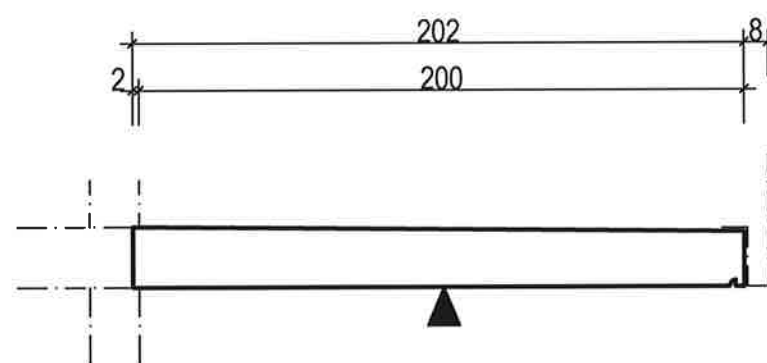
**COUPE B**

Ech: 1/25

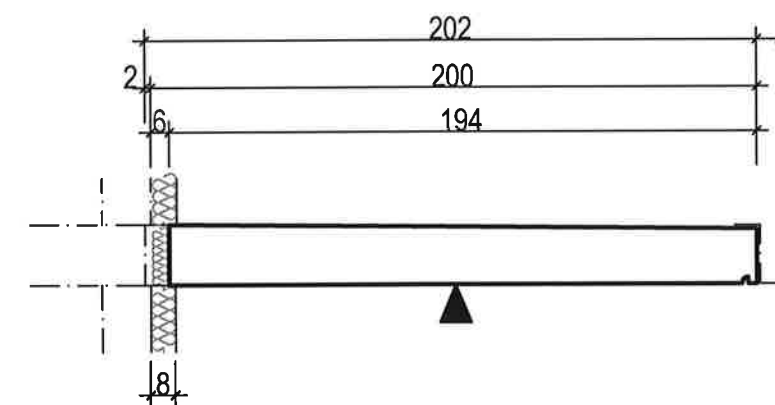


B8a 1 p

Poids: 4850 Kg

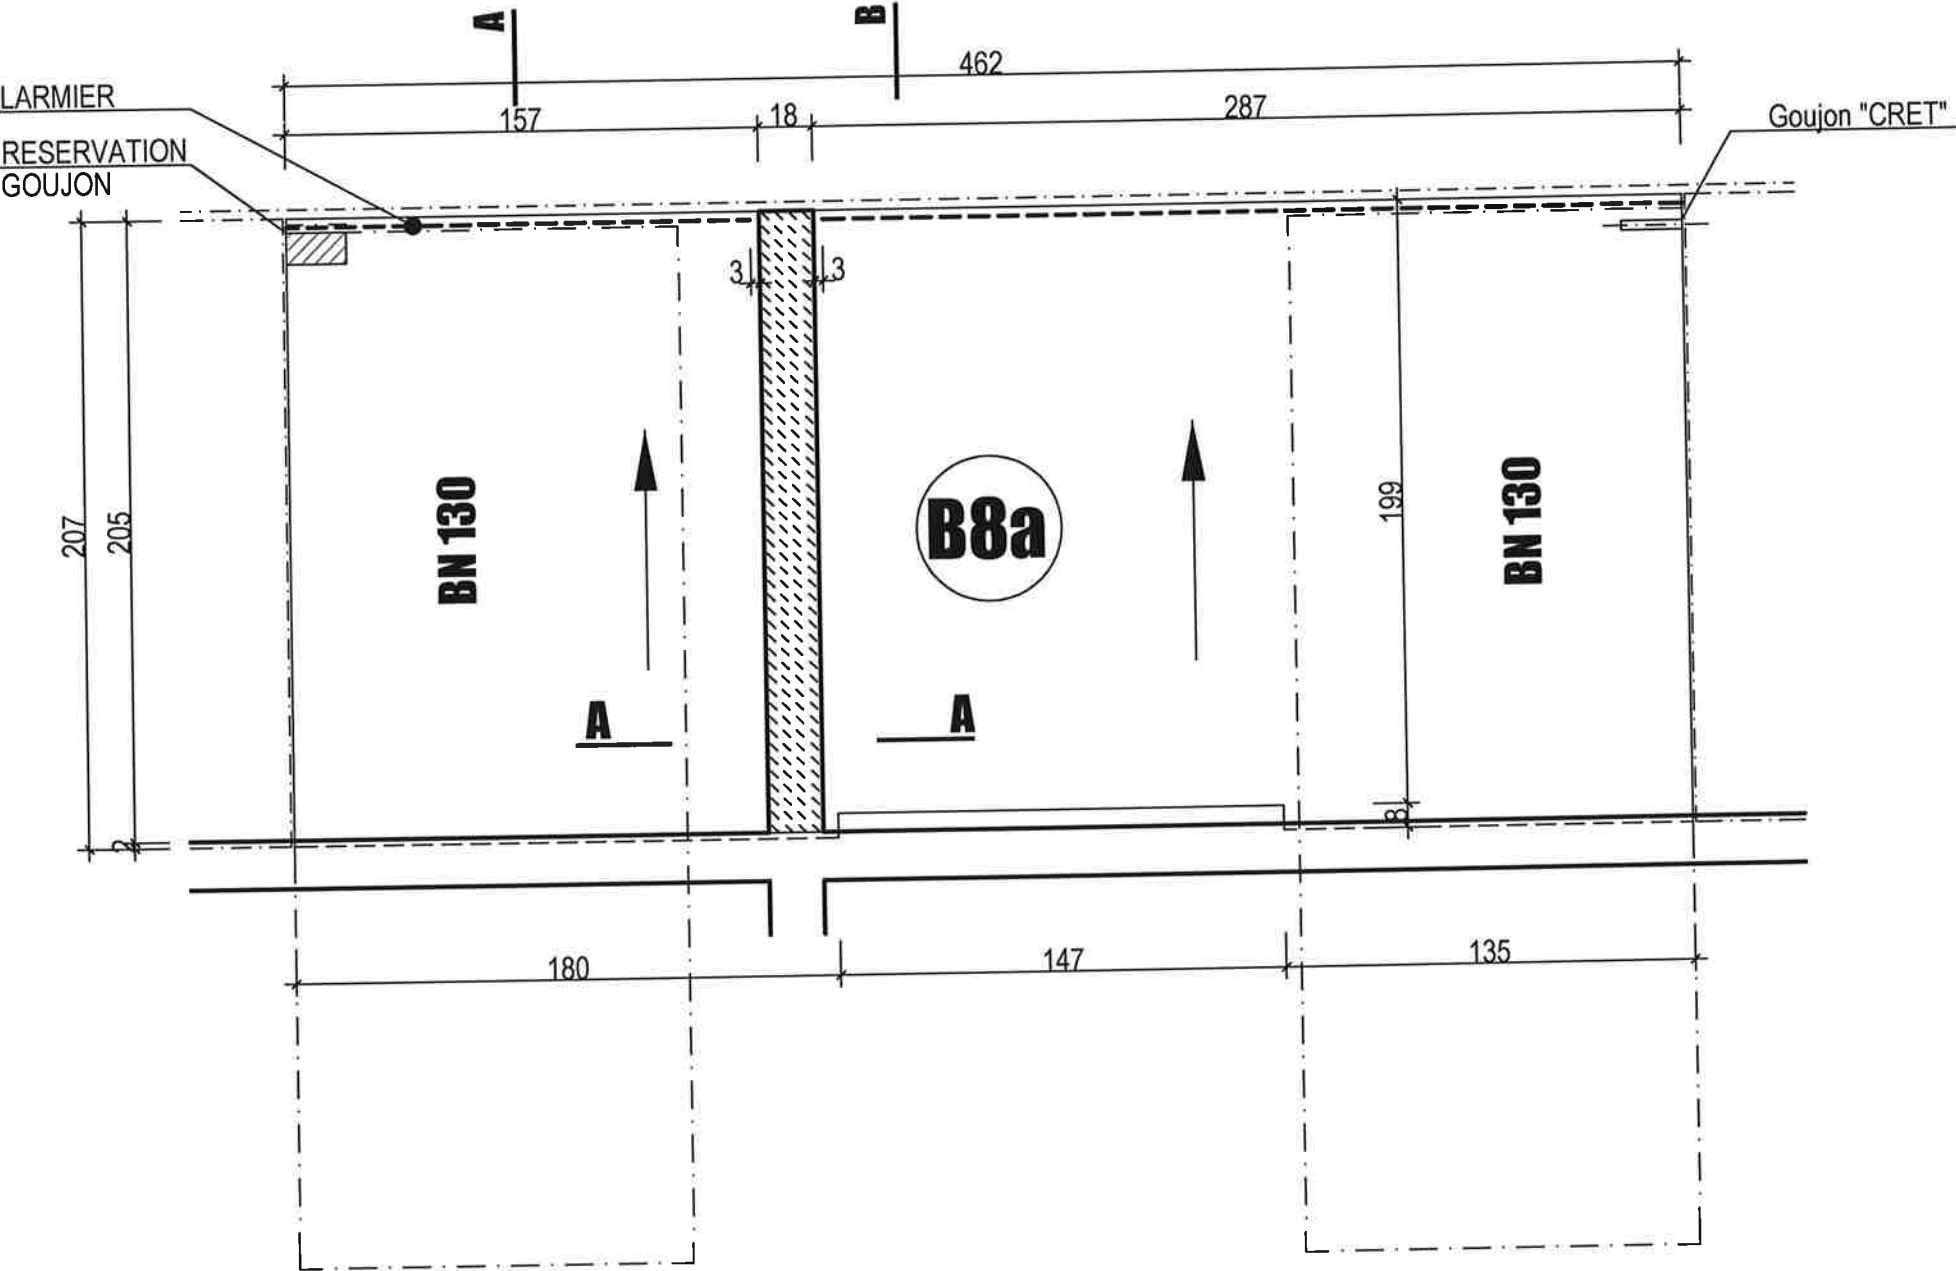


COUPE A

Ech: 1/10

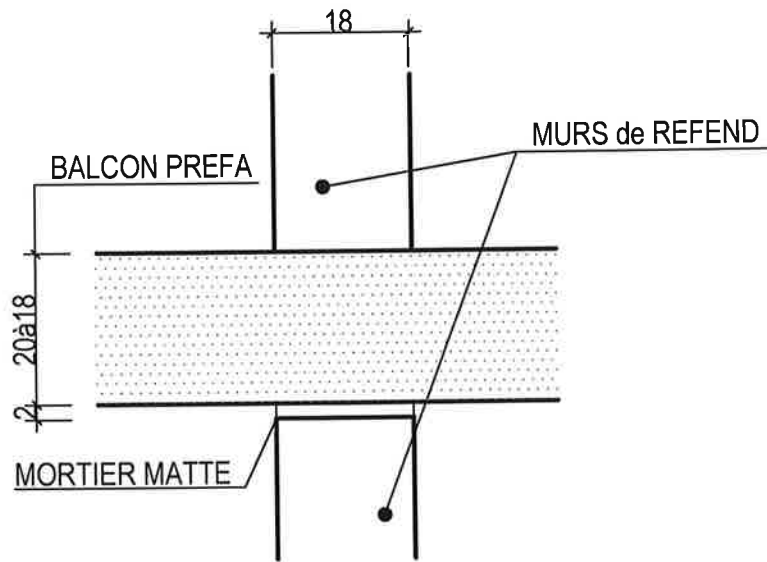


COUPE A

Ech: 1/25

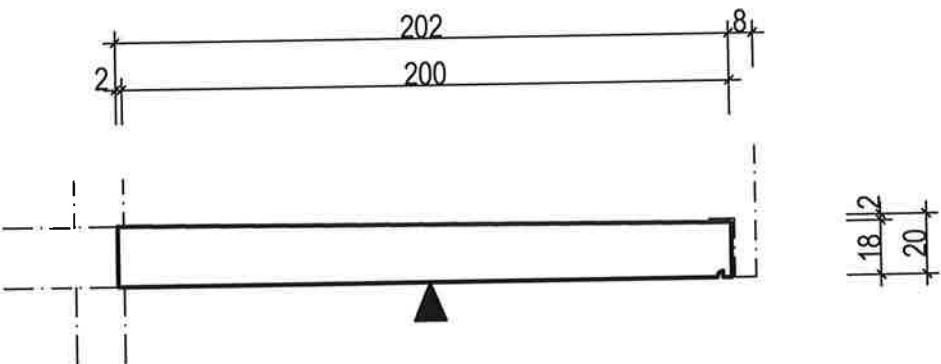


COUPE B

Ech: 1/25

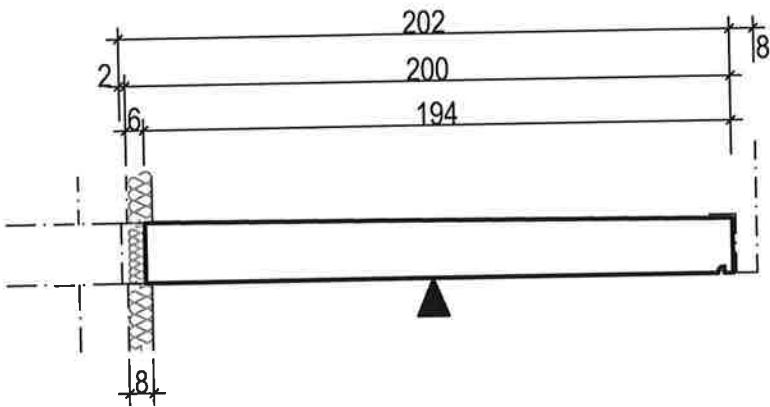


B8b 1 p
Poids: 4850 Kg

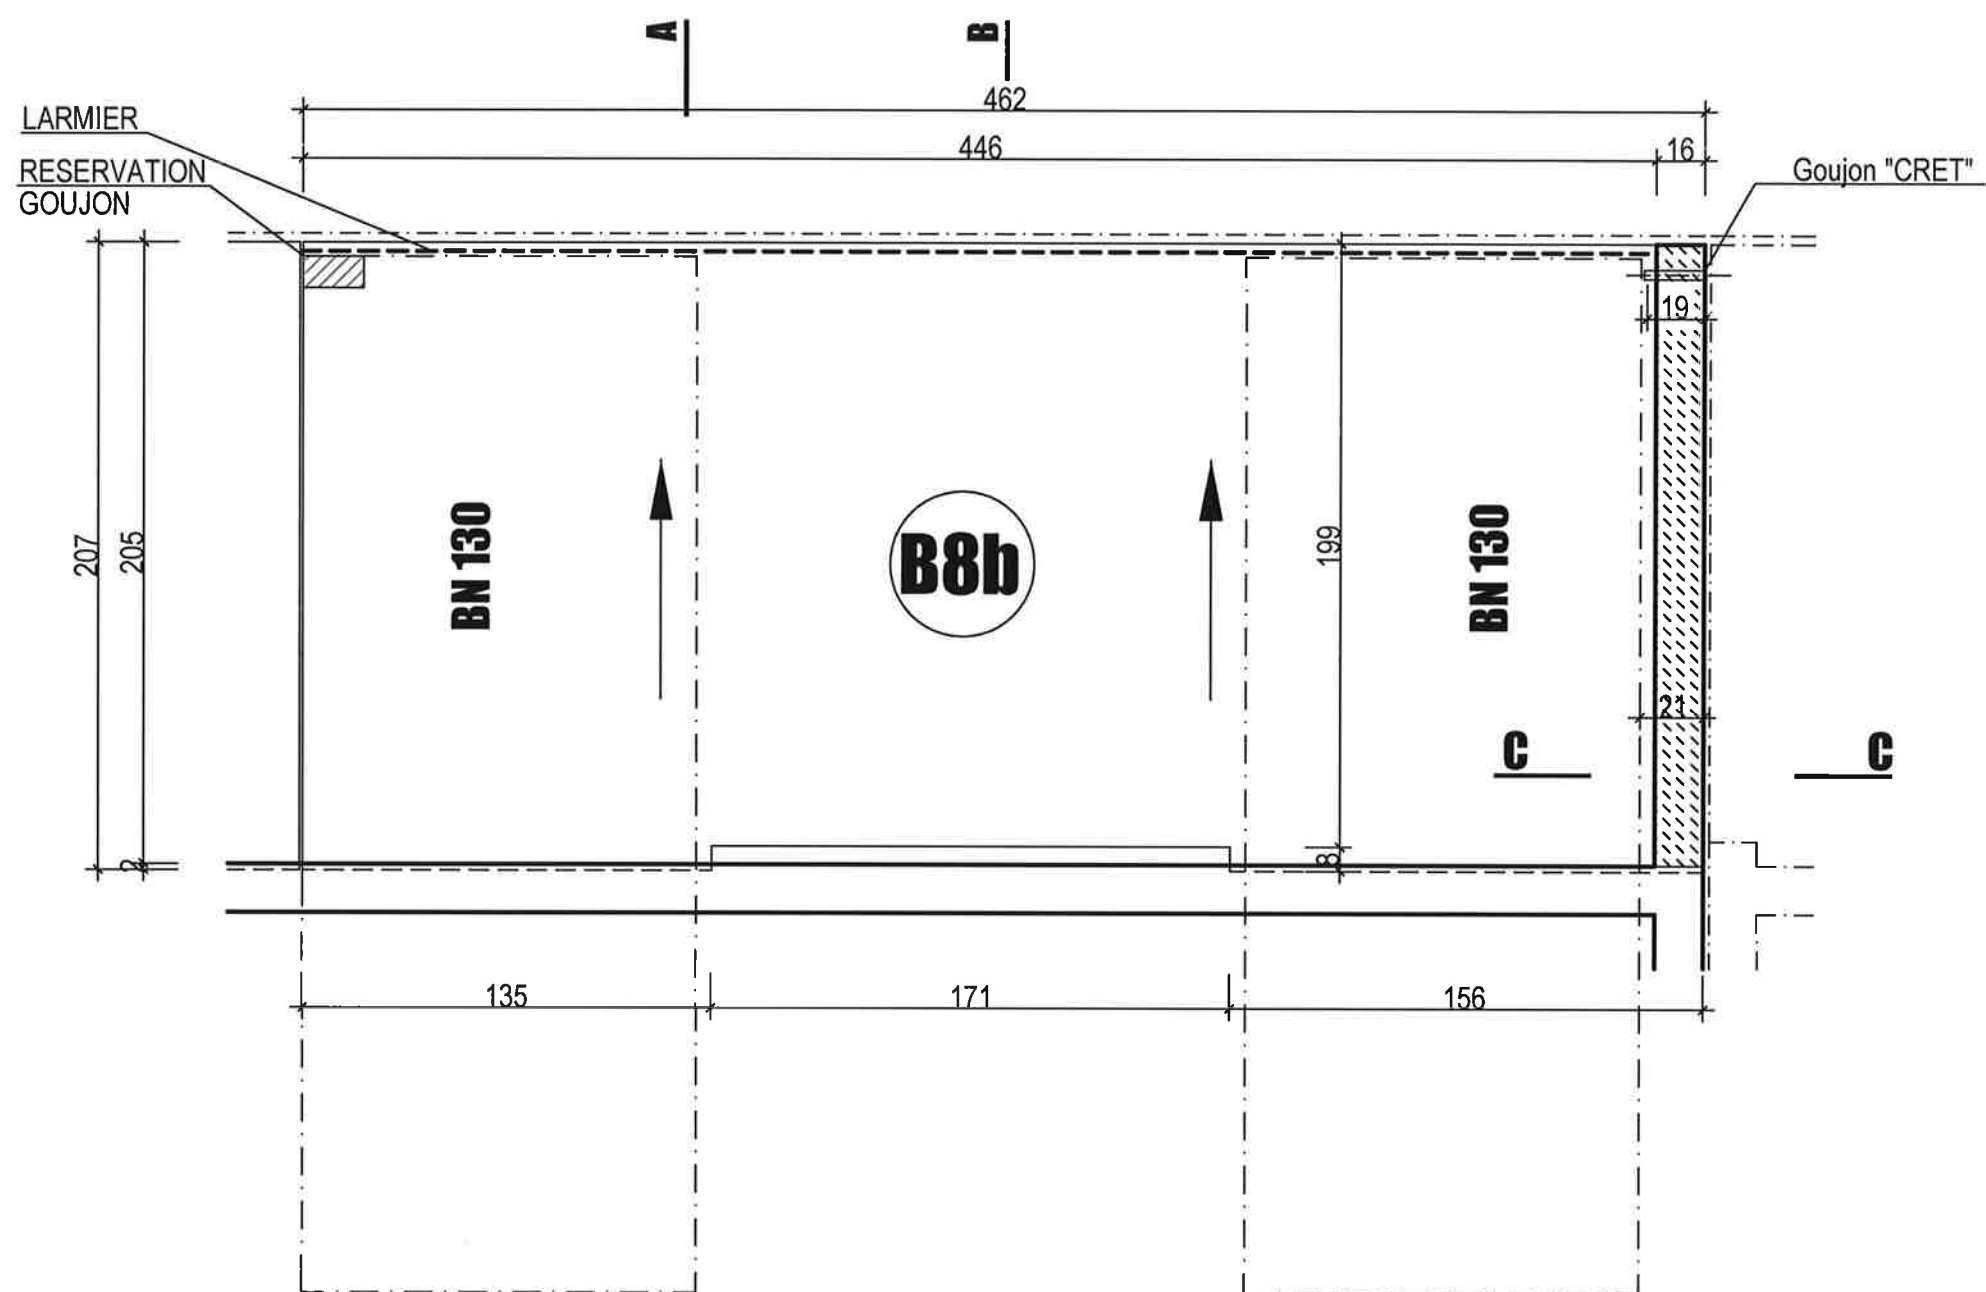


COUPE C

Ech: 1/10

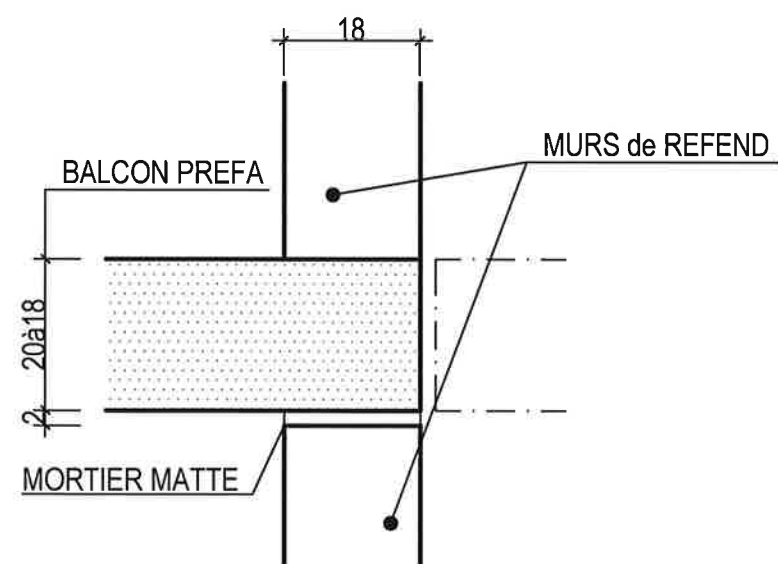


COUPE A

Ech: 1/25

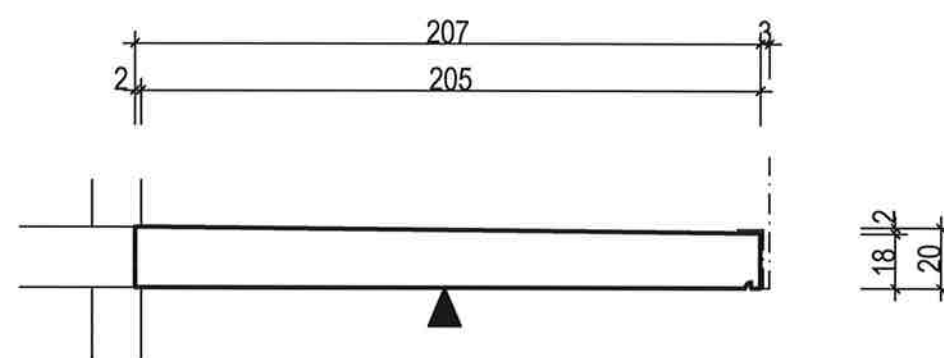

COUPE B


Ech: 1/25

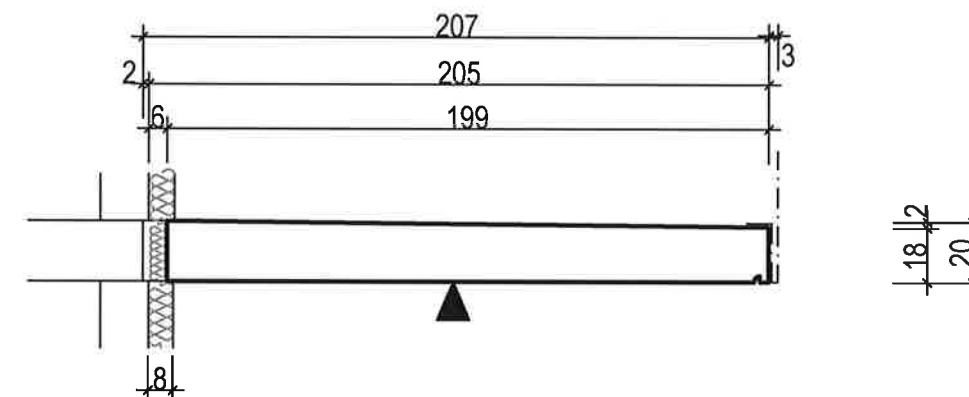

Vue en plan


Ech: 1/50

(12

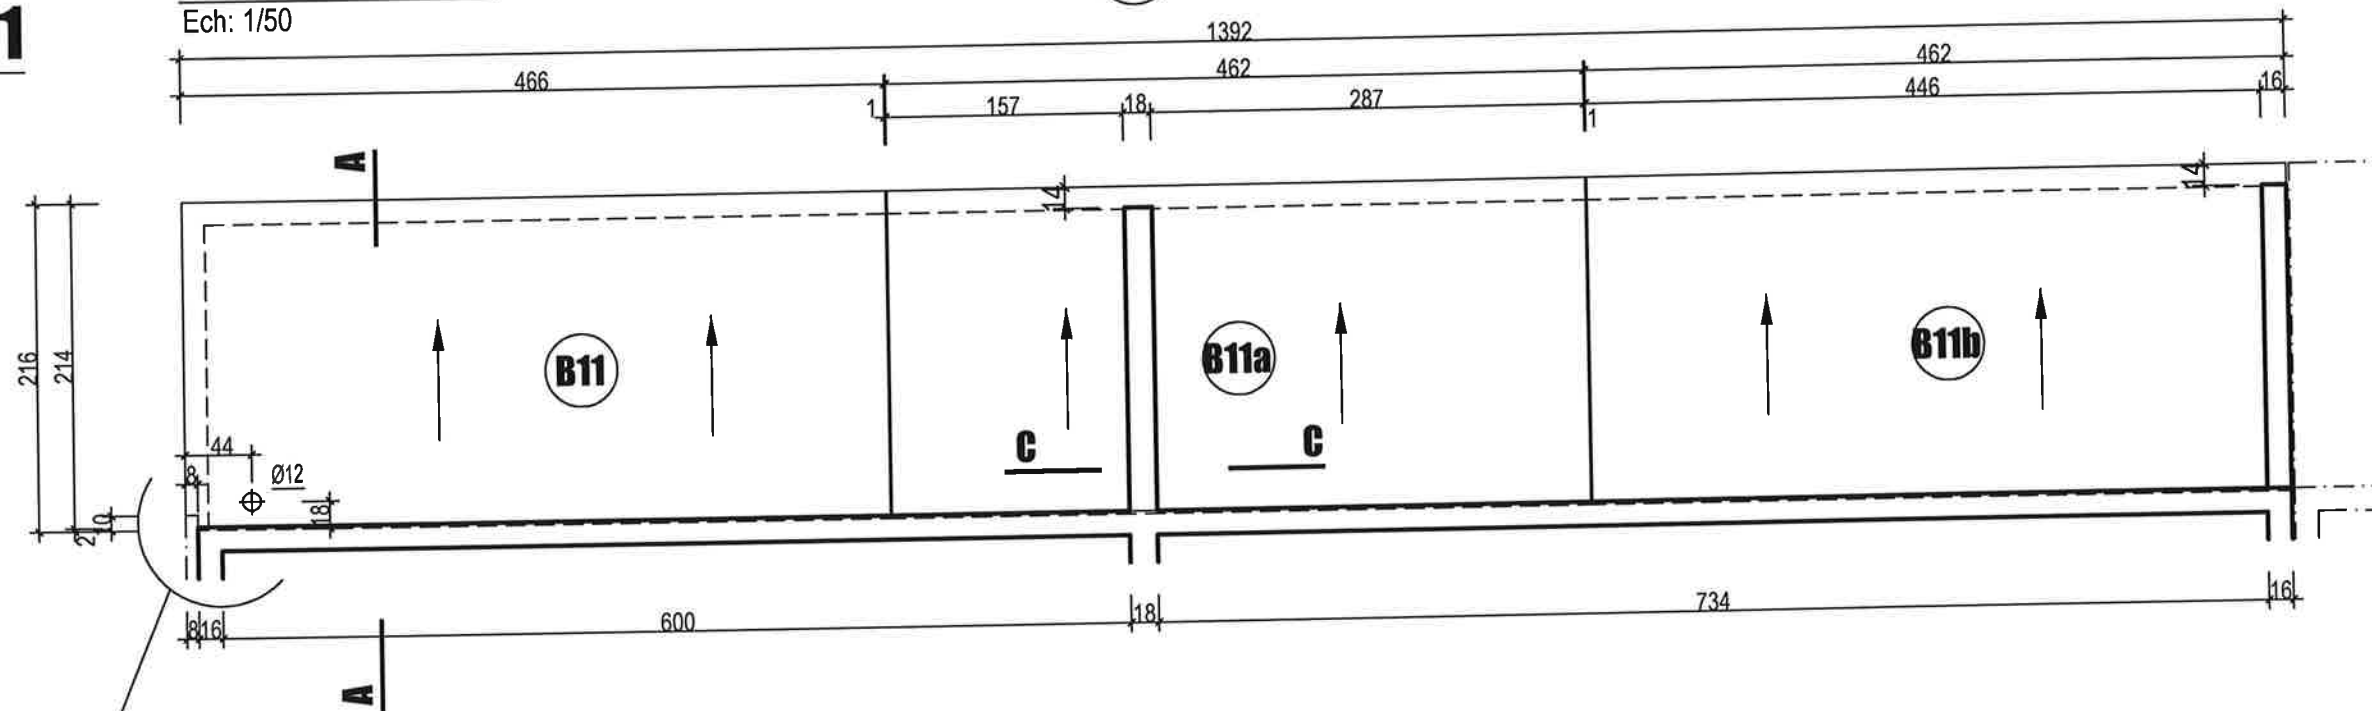


DETAIL

Ech: 1/10

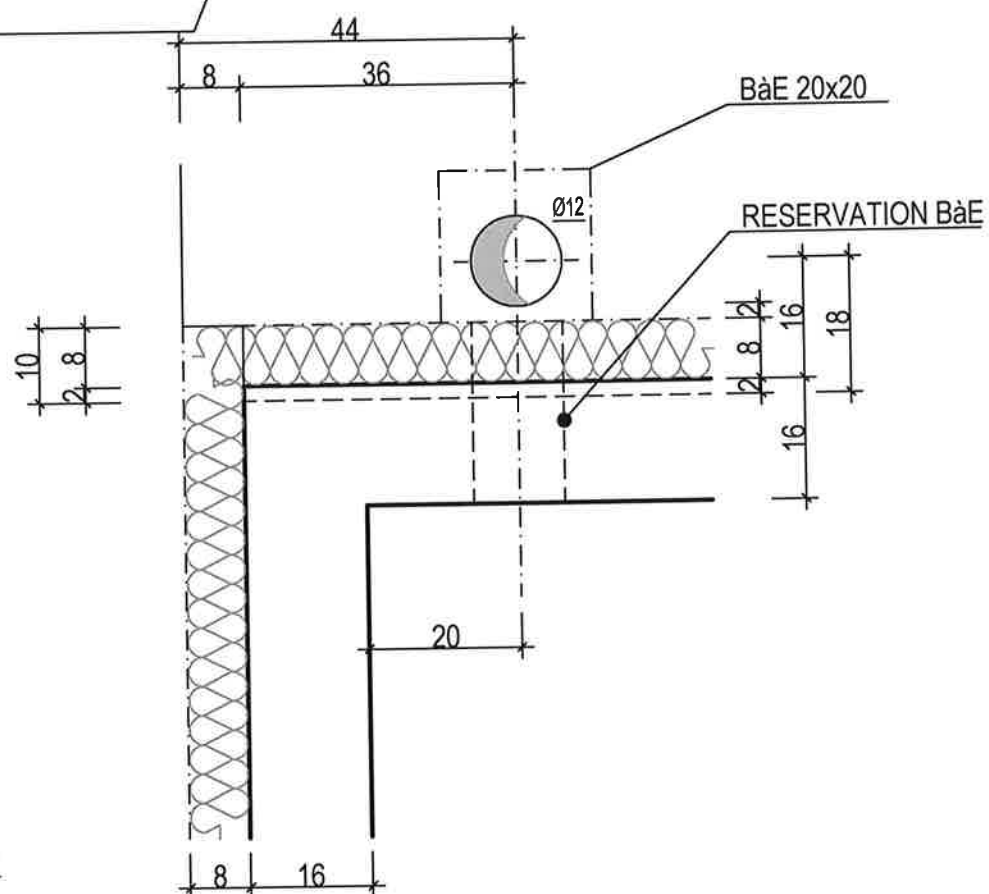


COUPE A

Ech: 1/25

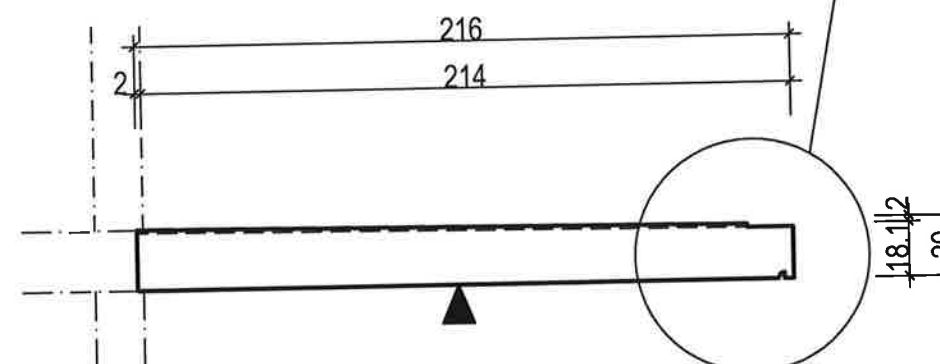


DETAIL

Ech: 1/10

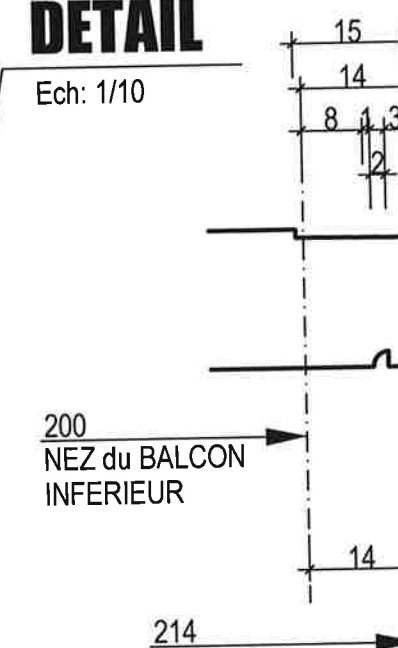

COUPE C


Ech: 1/25

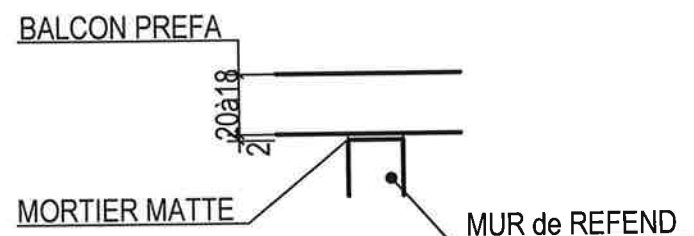

B11


1 p

Poids: 4850 Kg

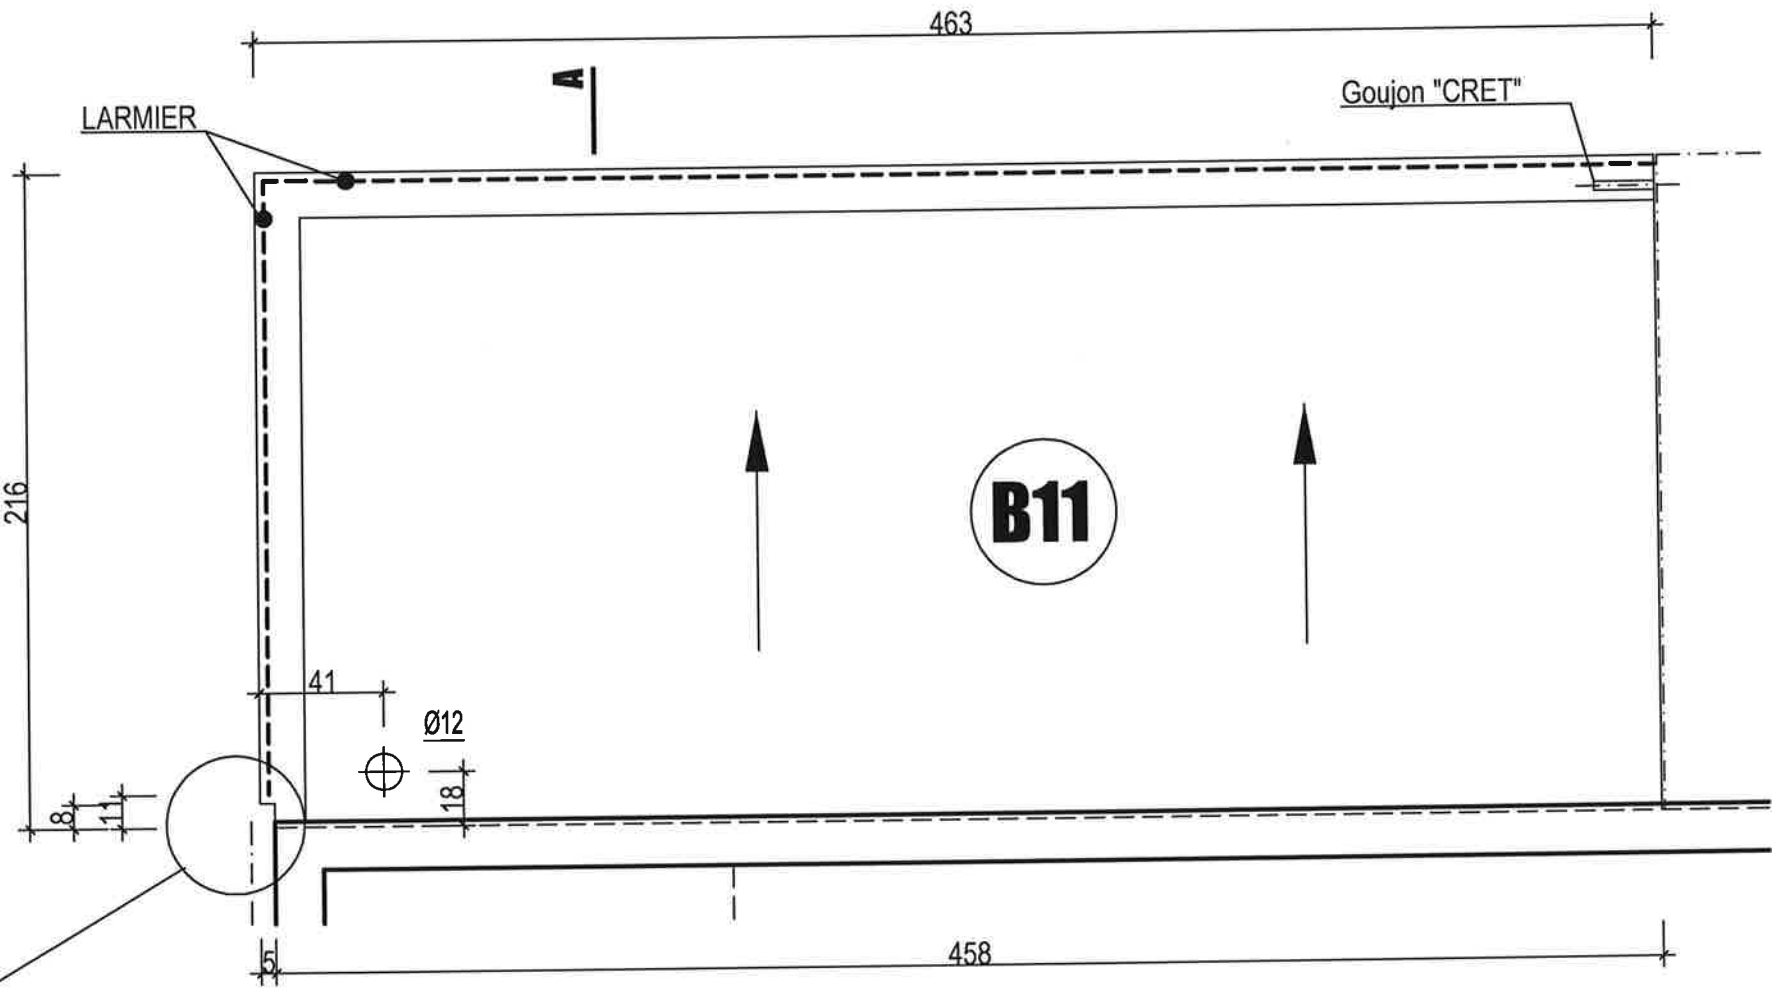


DETAIL


Ech: 1/10

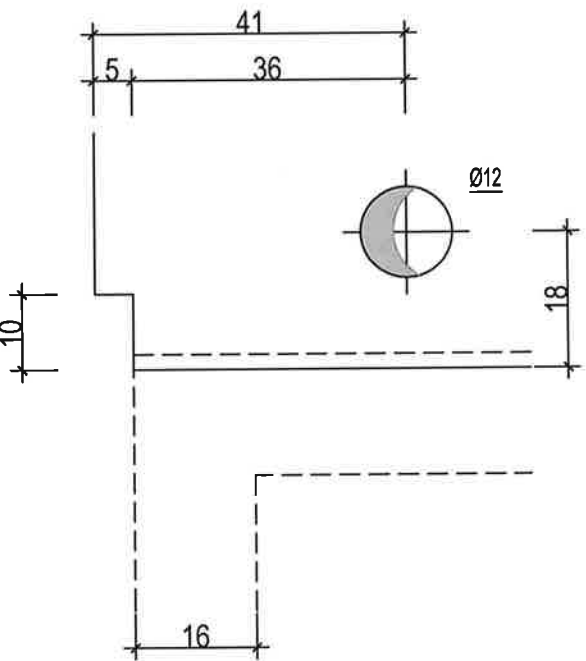


COUPE A

Ech: 1/25

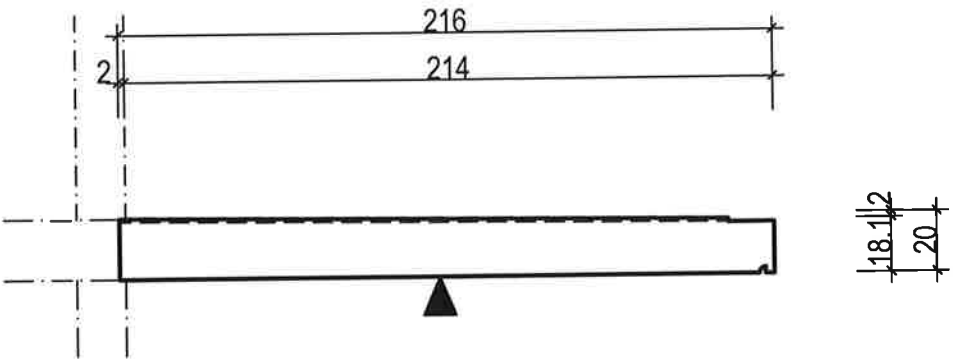


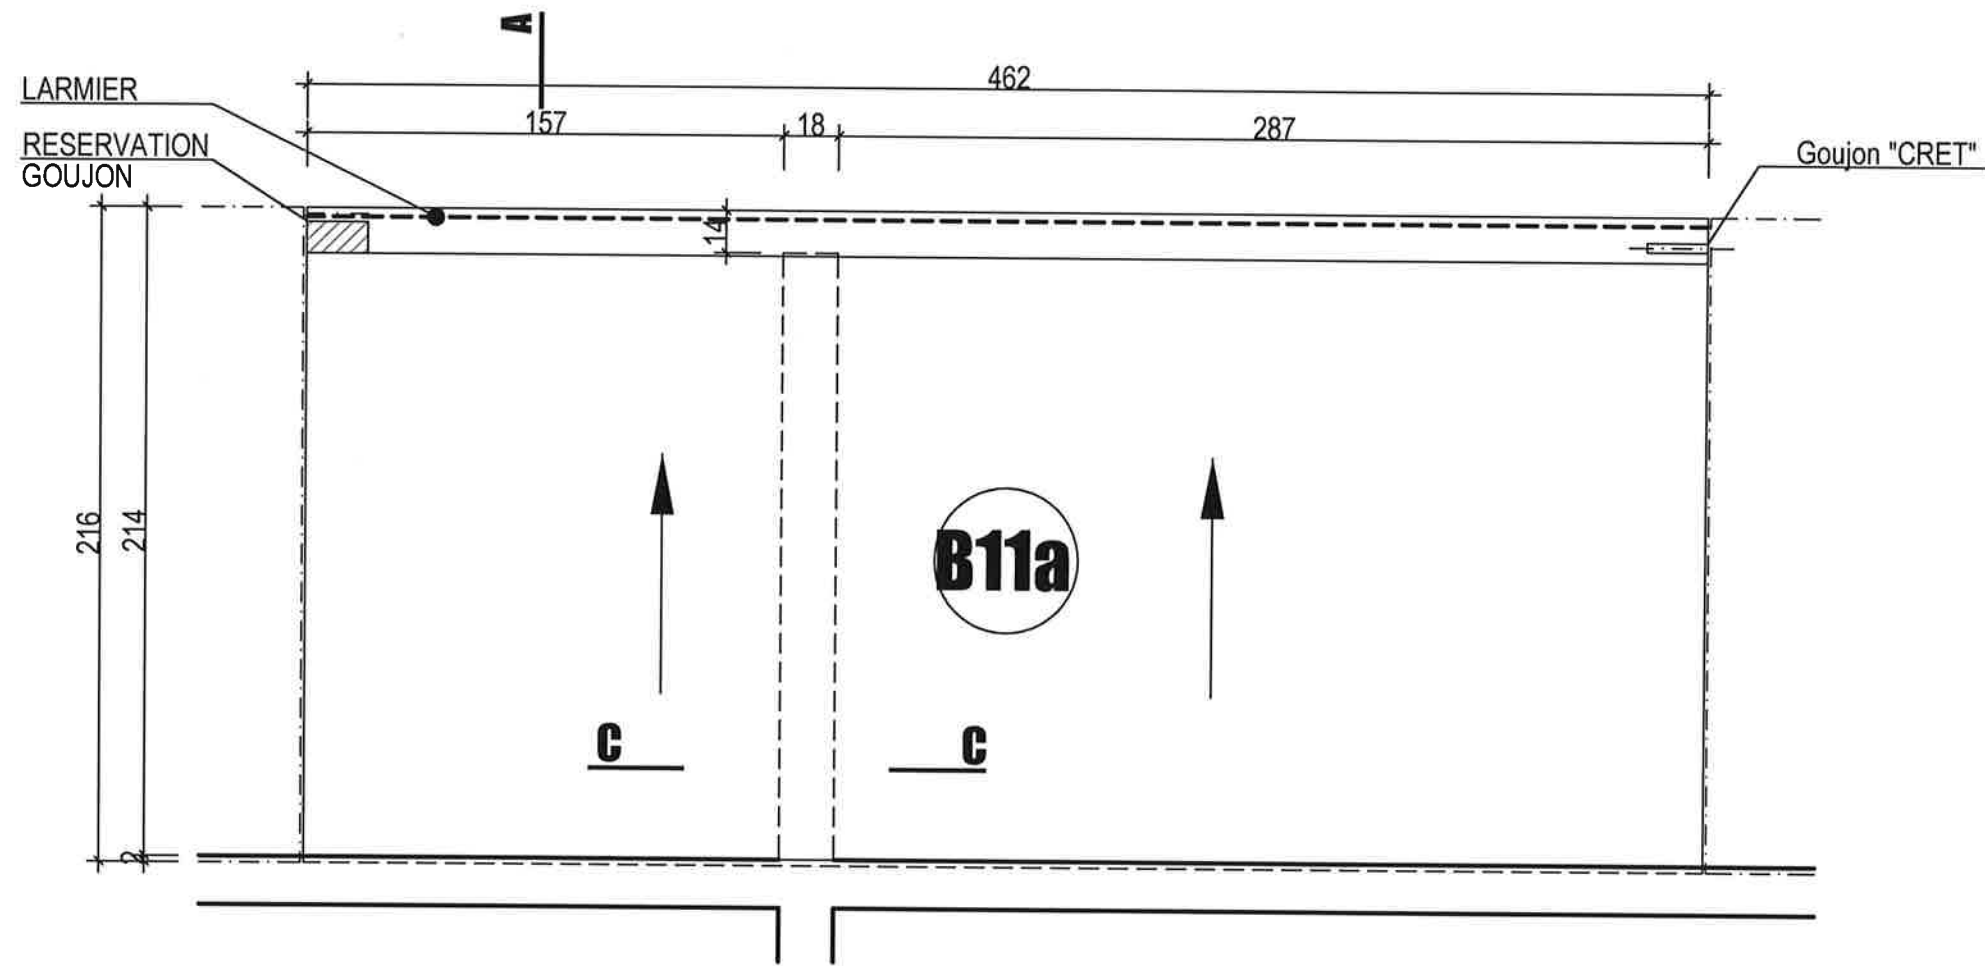

COUPE C
Ech: 1/10

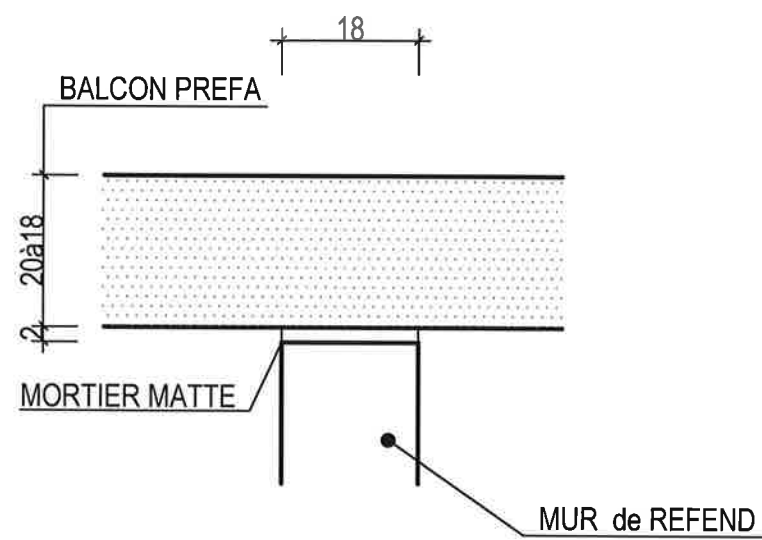

COUPE A
Ech: 1/25

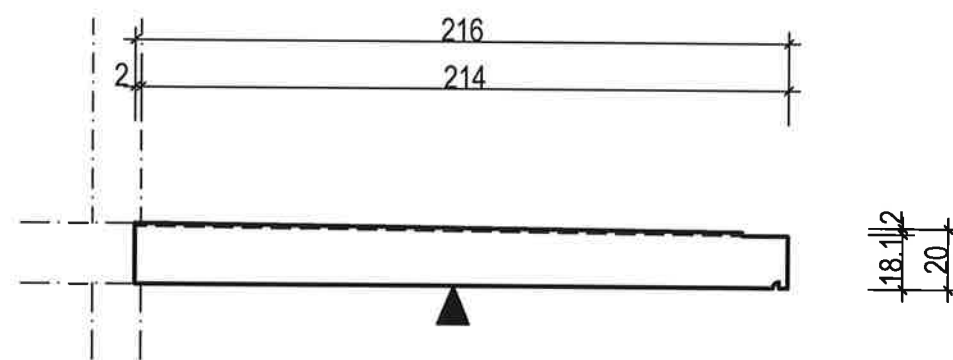

B11b

1 p

Poids: 4850 Kg

LARMIER

RESERVATION
GOUJON

216

214

462

446

16

Goujon "CRET"

B11b

C

C

COUPE C

Ech: 1/10

18

BALCON PREFA

20 à 18

MORTIER MATTE

MUR de REFEND

COUPE A

Ech: 1/25

216


214

18.1/2

20


Vue en plan

Ech: 1/50

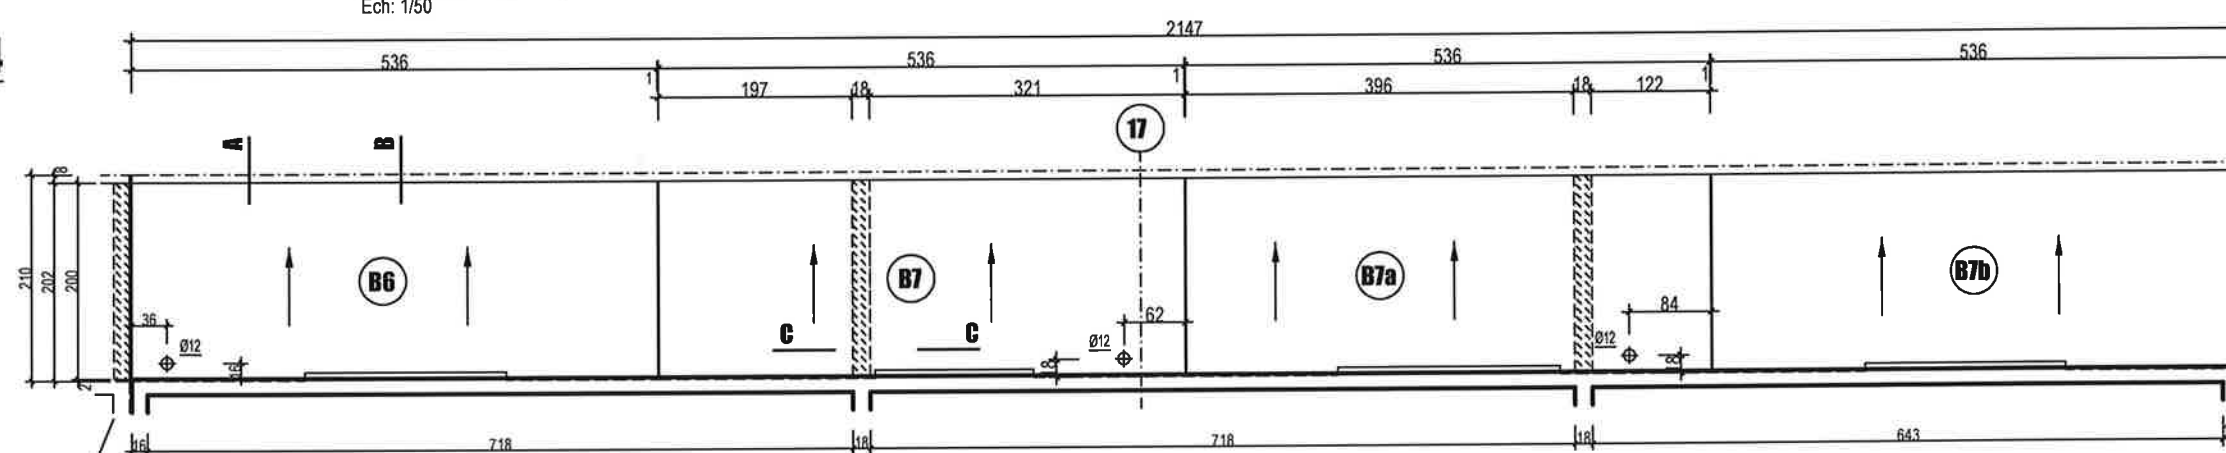


DETAIL

Ech: 1/10

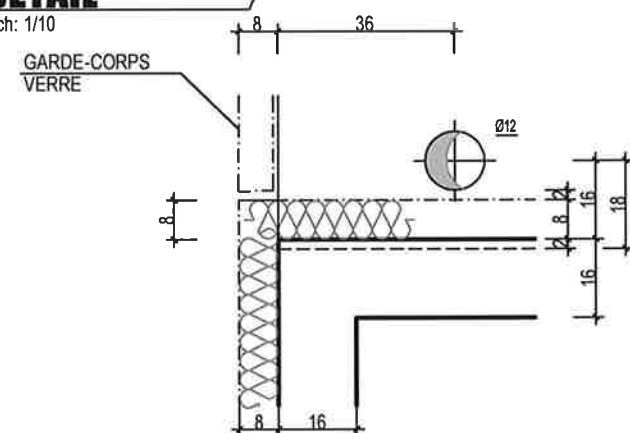


COUPE A

Ech: 1/25

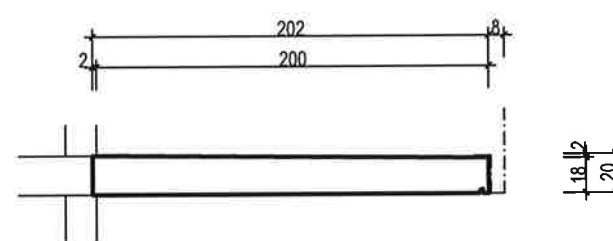


COUPE B

Ech: 1/25

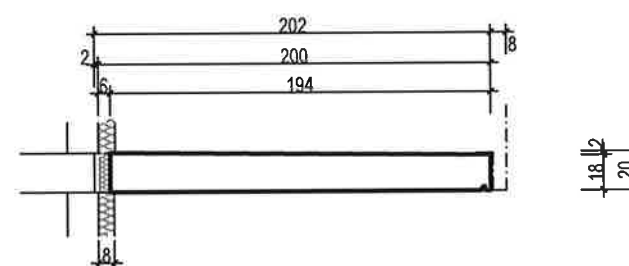

COUPE C

Ech: 1/25

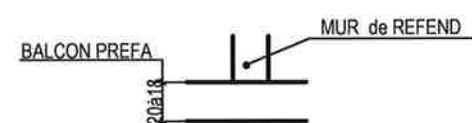



B6

1 p


Poids: 5350 Kg

DETAIL


Ech: 1/10

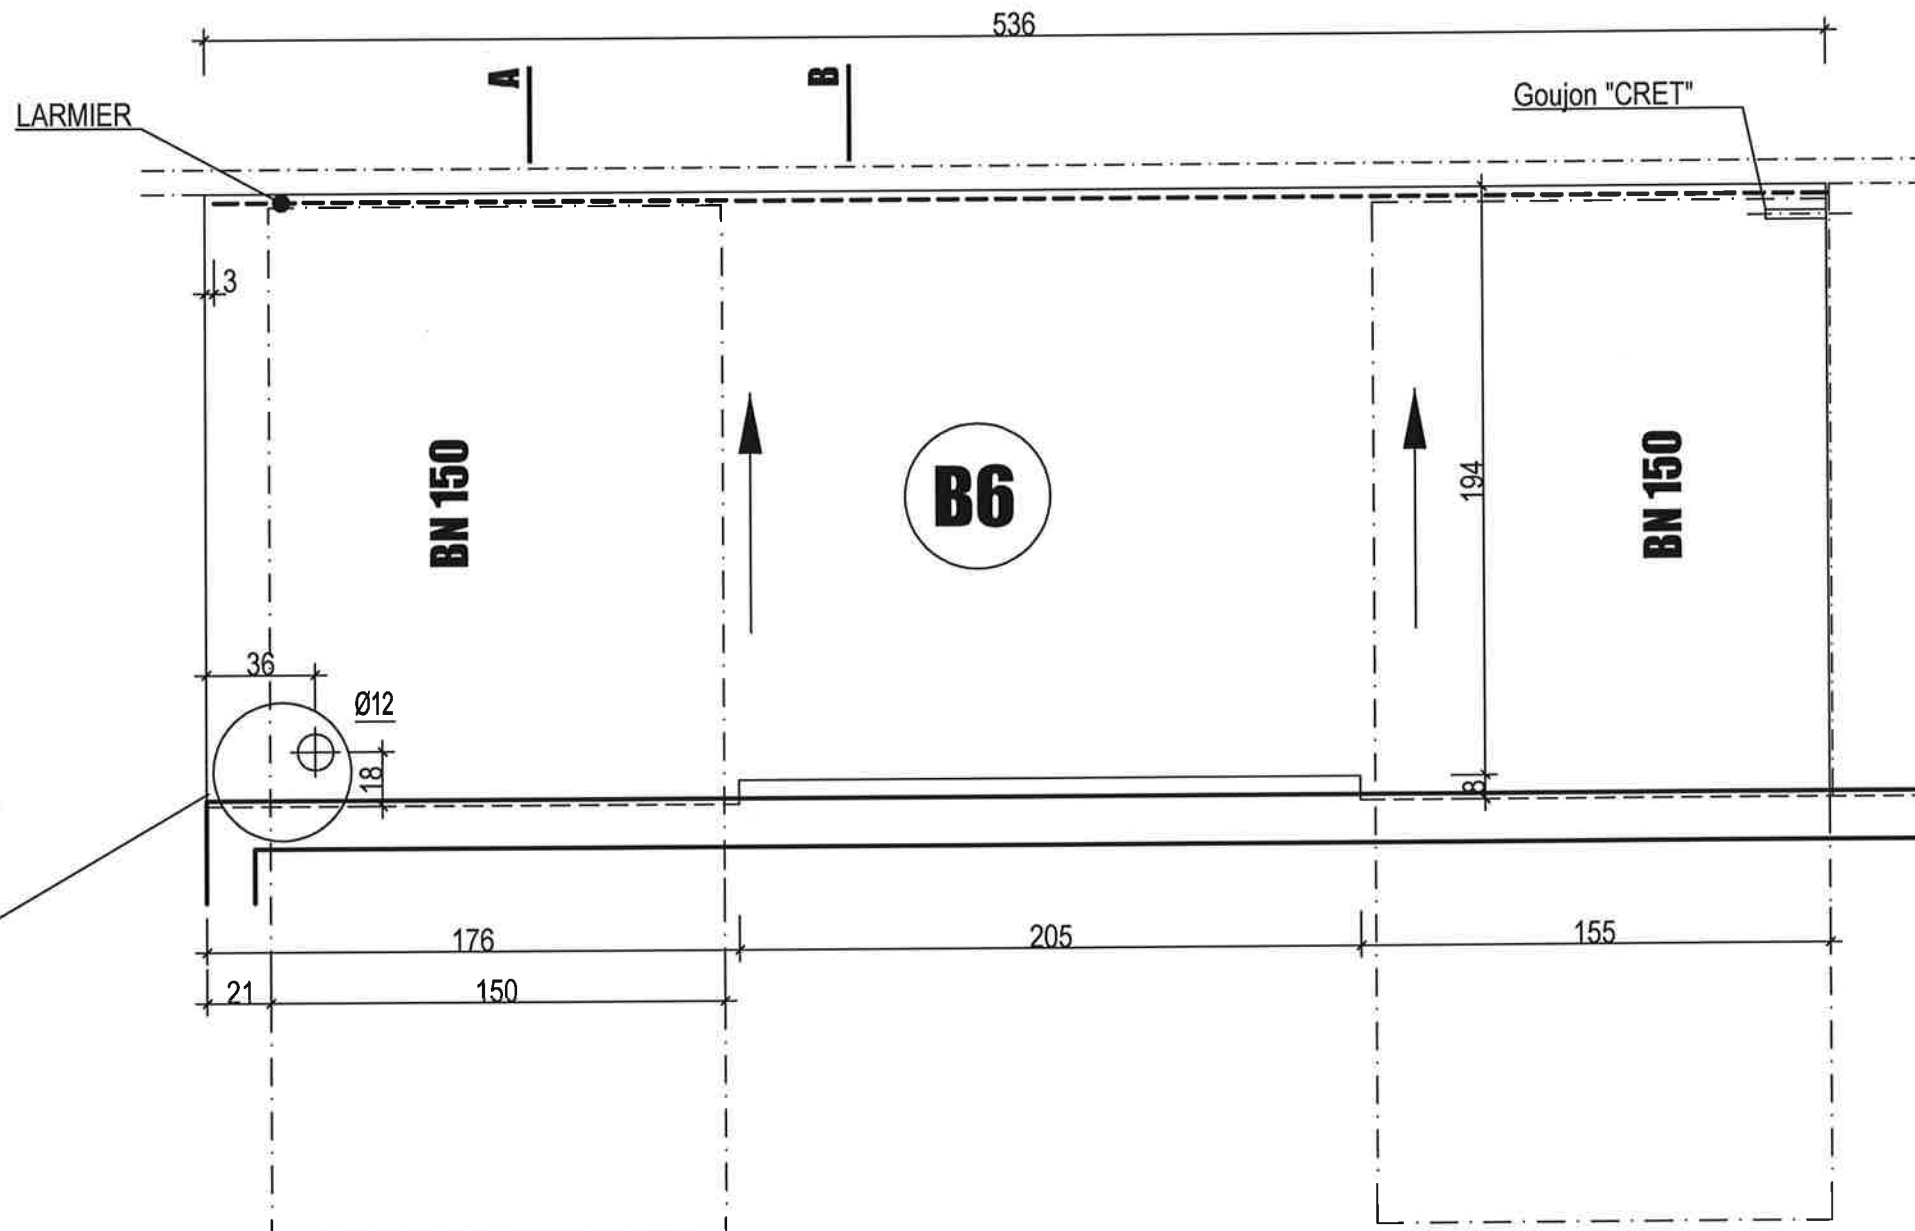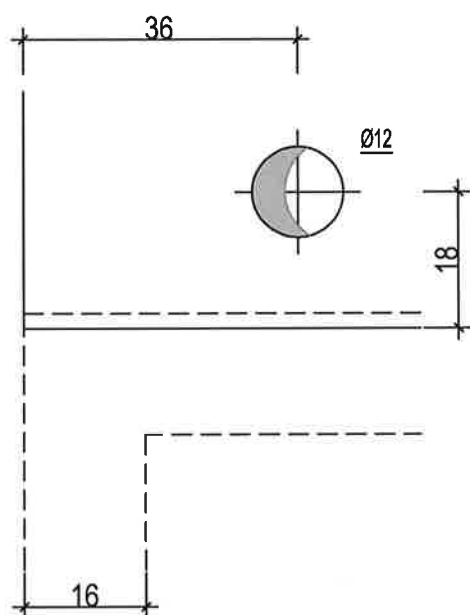**COUPE A**

Ech: 1/25

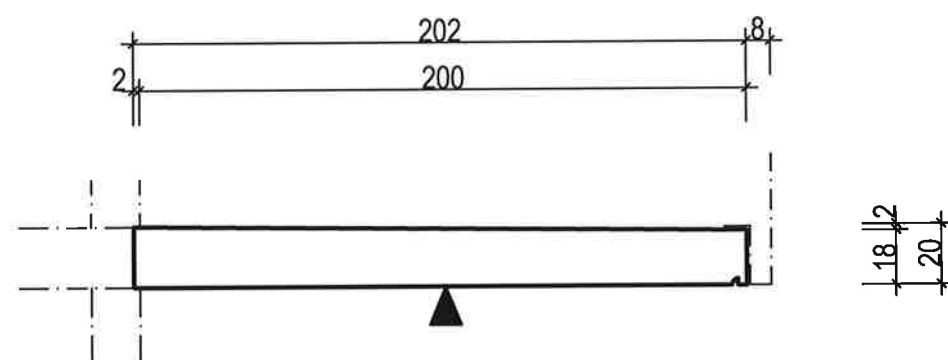**COUPE B**


Ech: 1/25

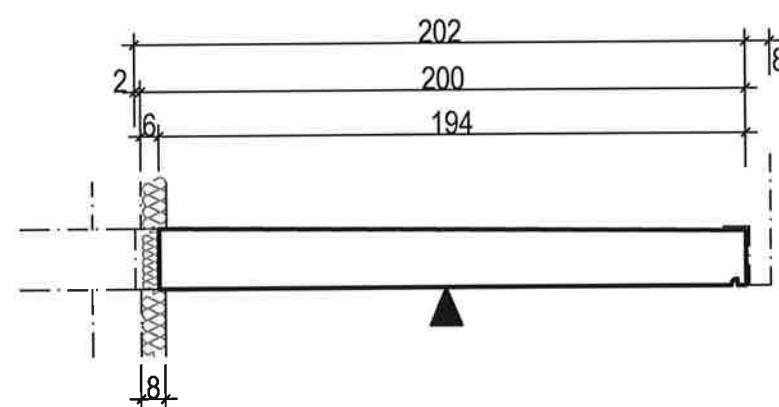


B7

1 p


Poids: 5350 Kg

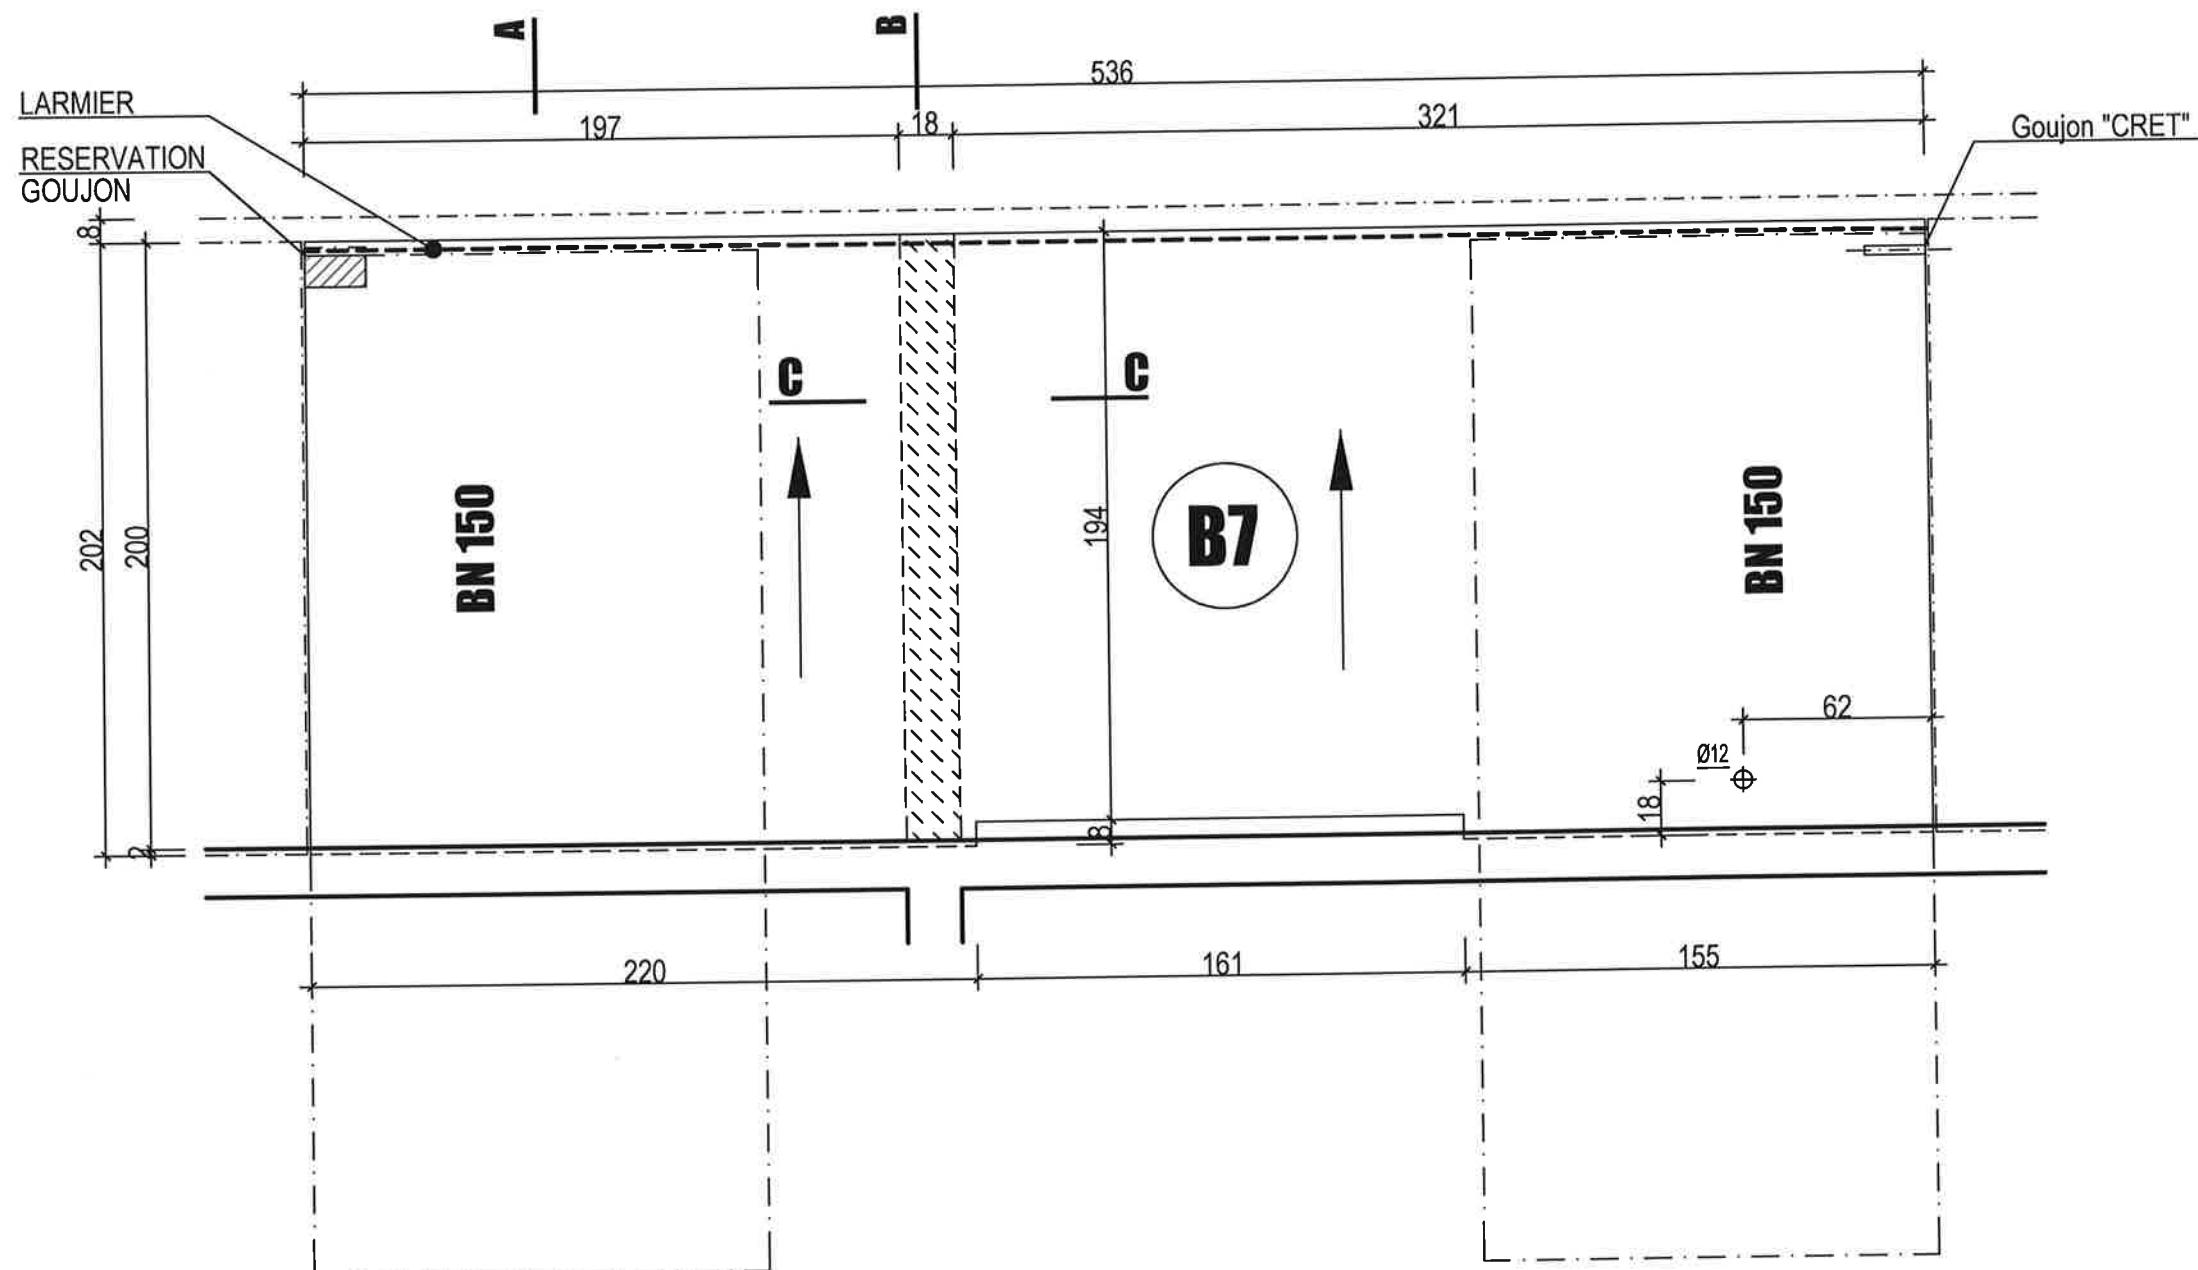**COUPE C**


Ech: 1/10

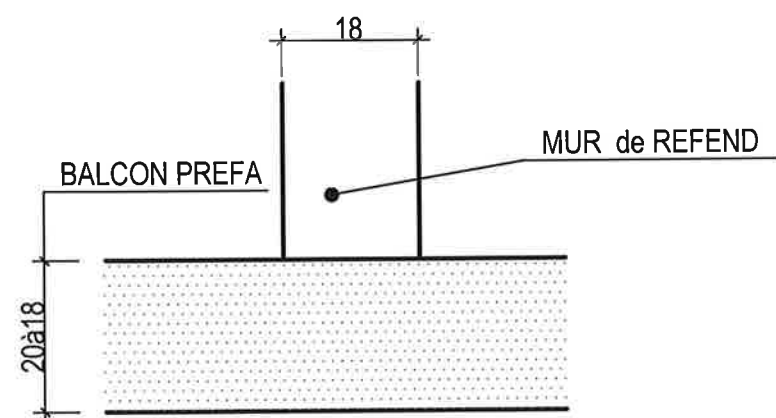**COUPE A**


Ech: 1/25

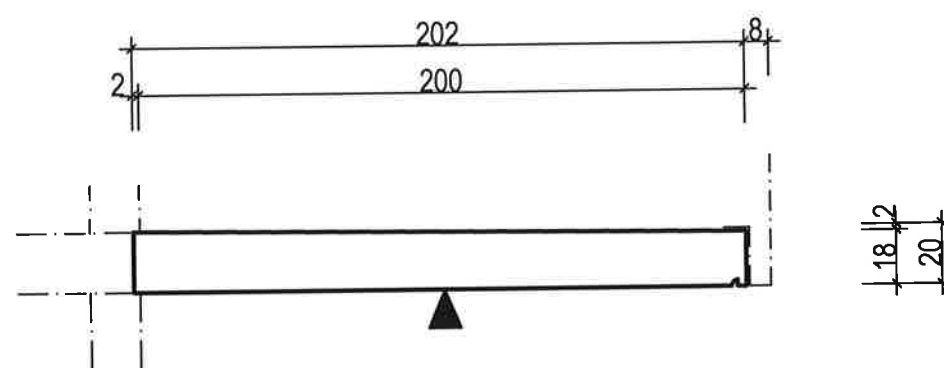**COUPE B**


Ech: 1/25

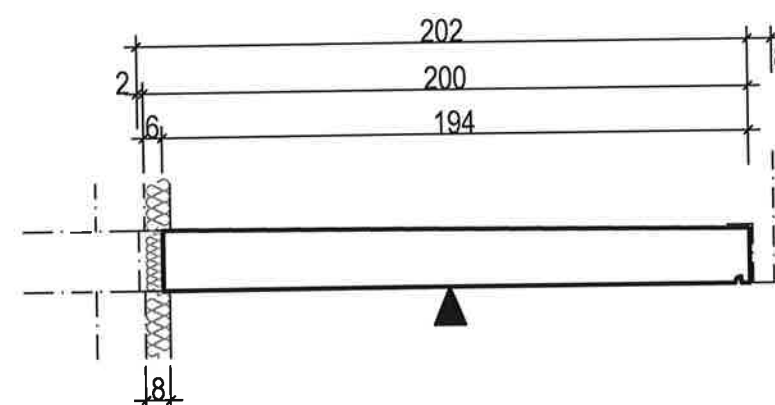


B7a 1 p
Poids: 5350 Kg

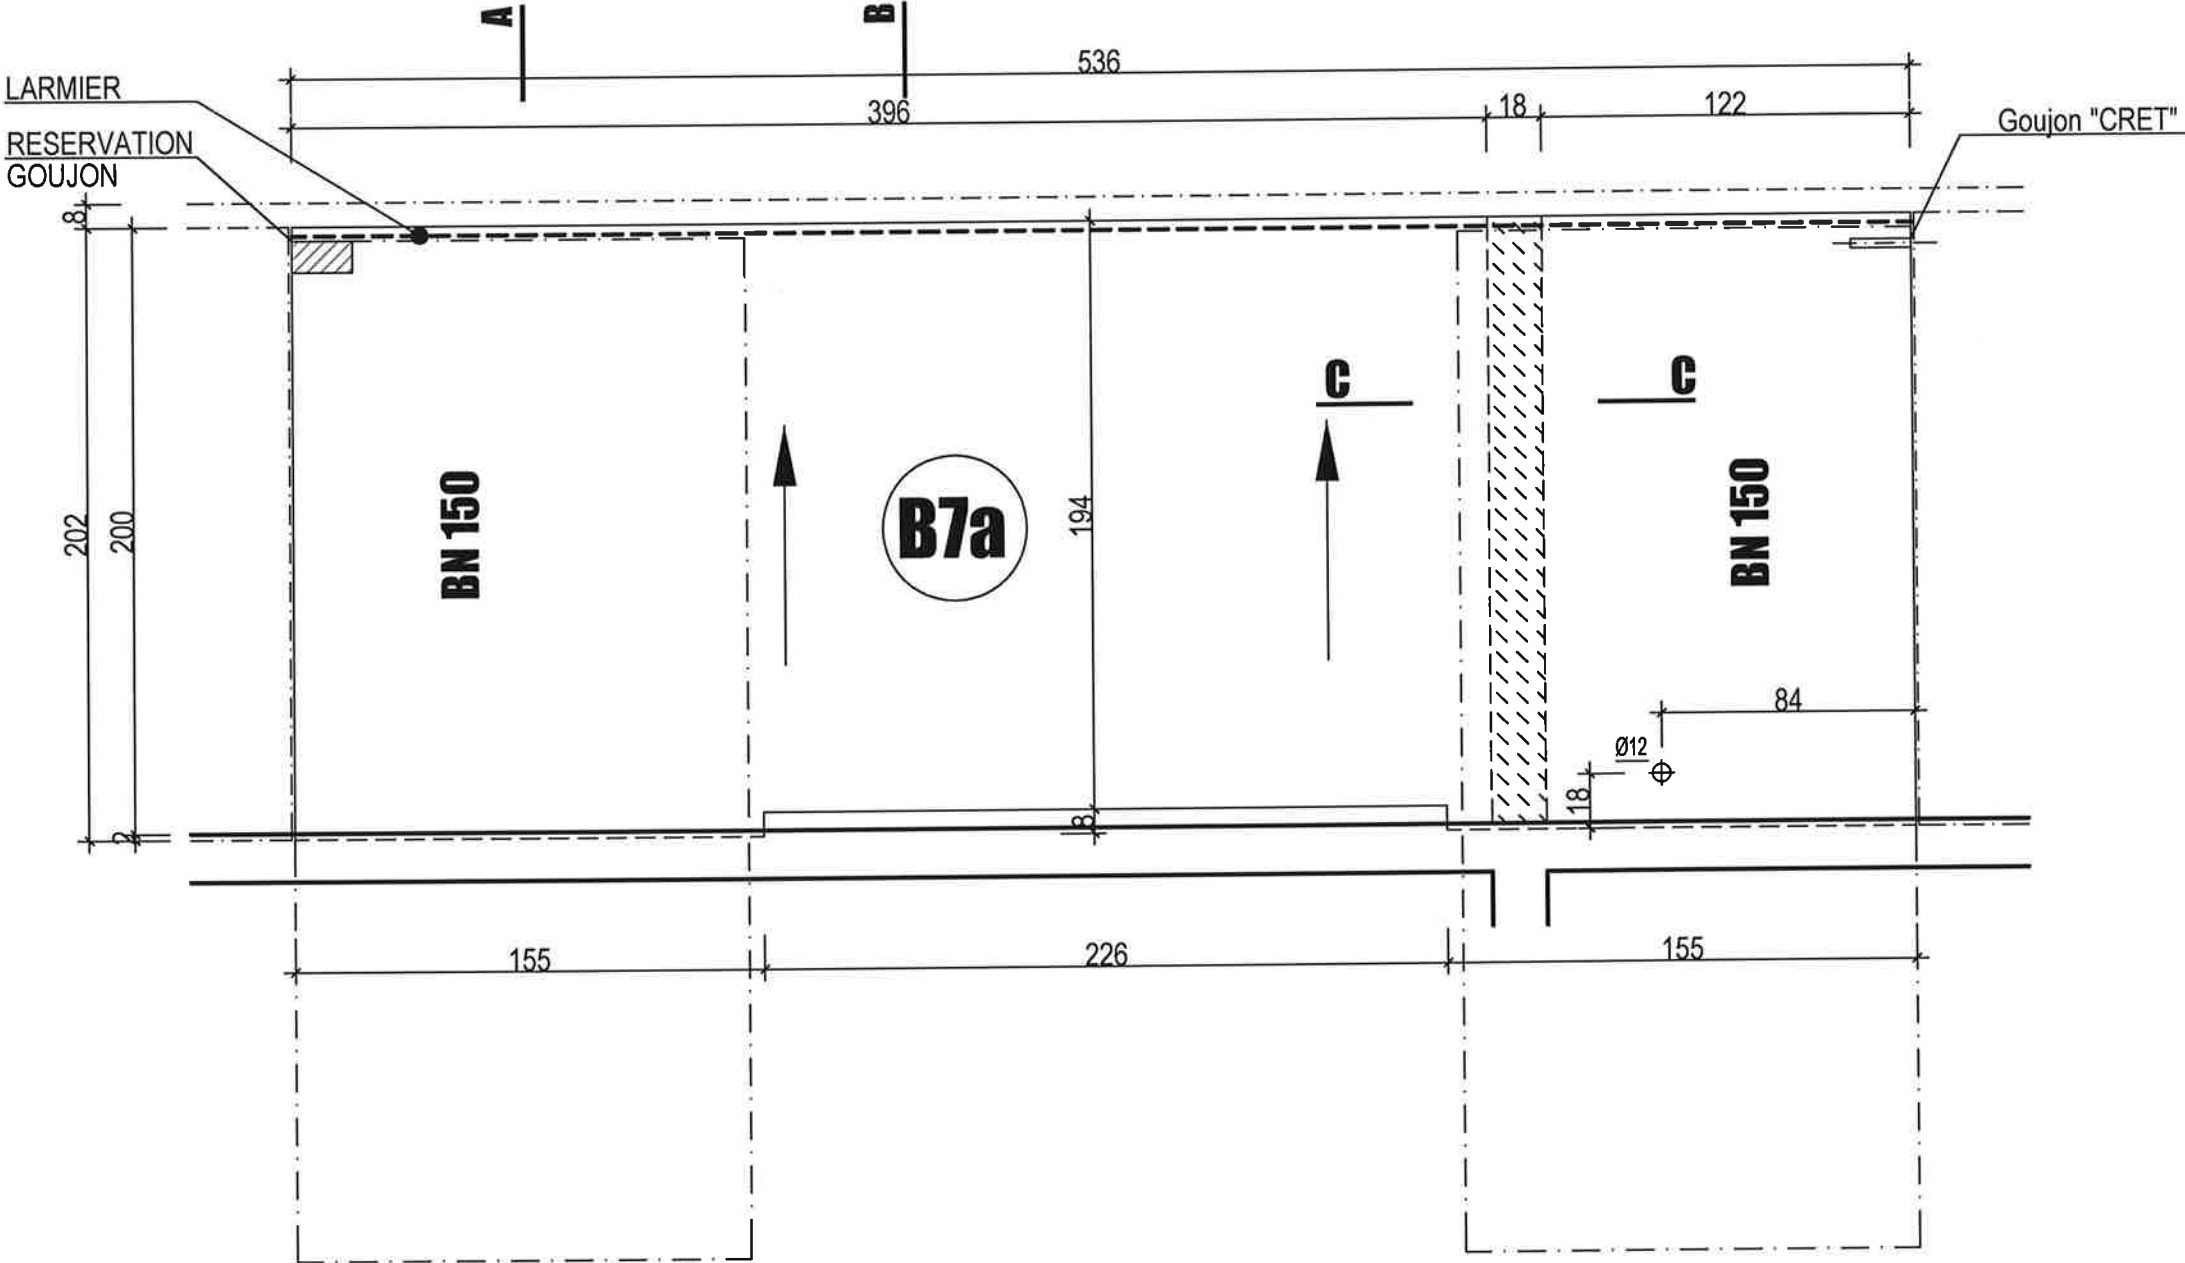


COUPE C
Ech: 1/10

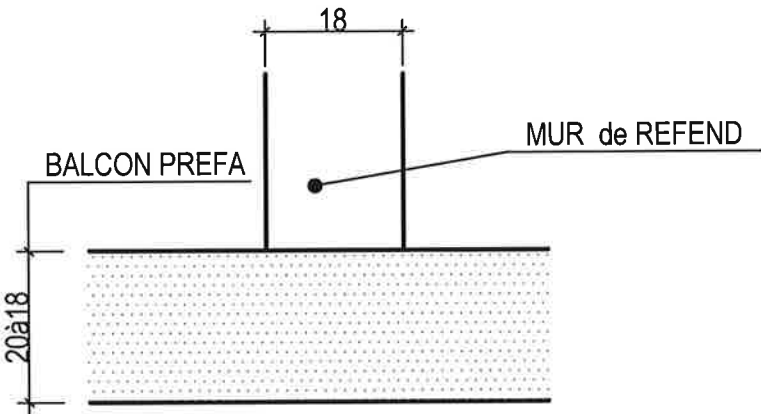

COUPE A
Ech: 1/25

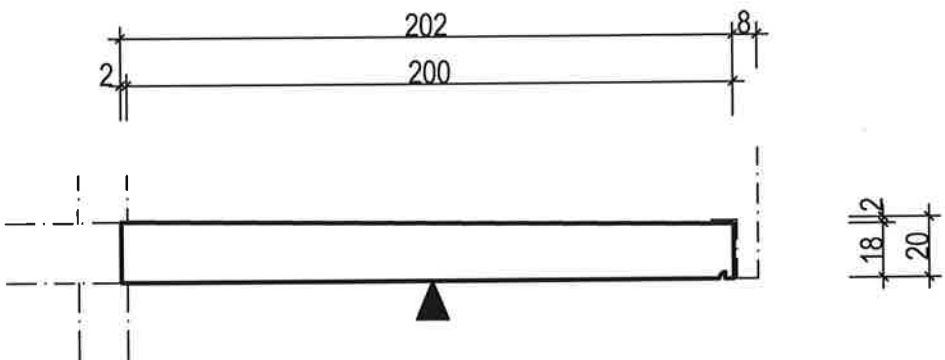


COUPE B
Ech: 1/25

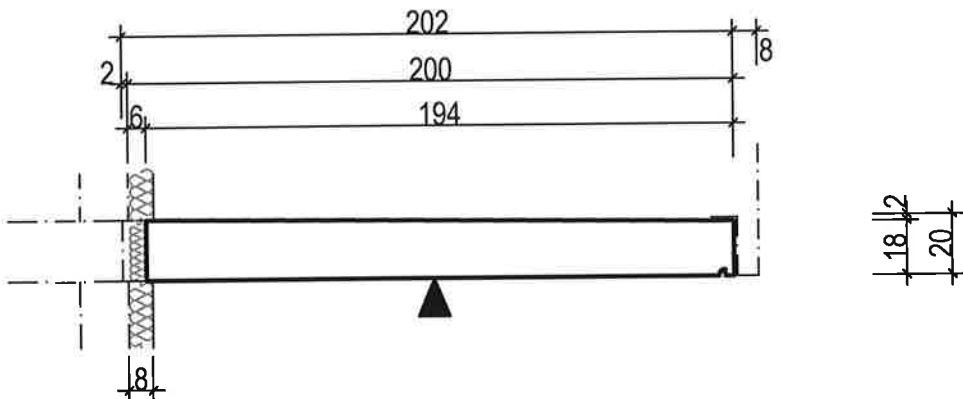


B7b 1 p

Poids: 5350 Kg

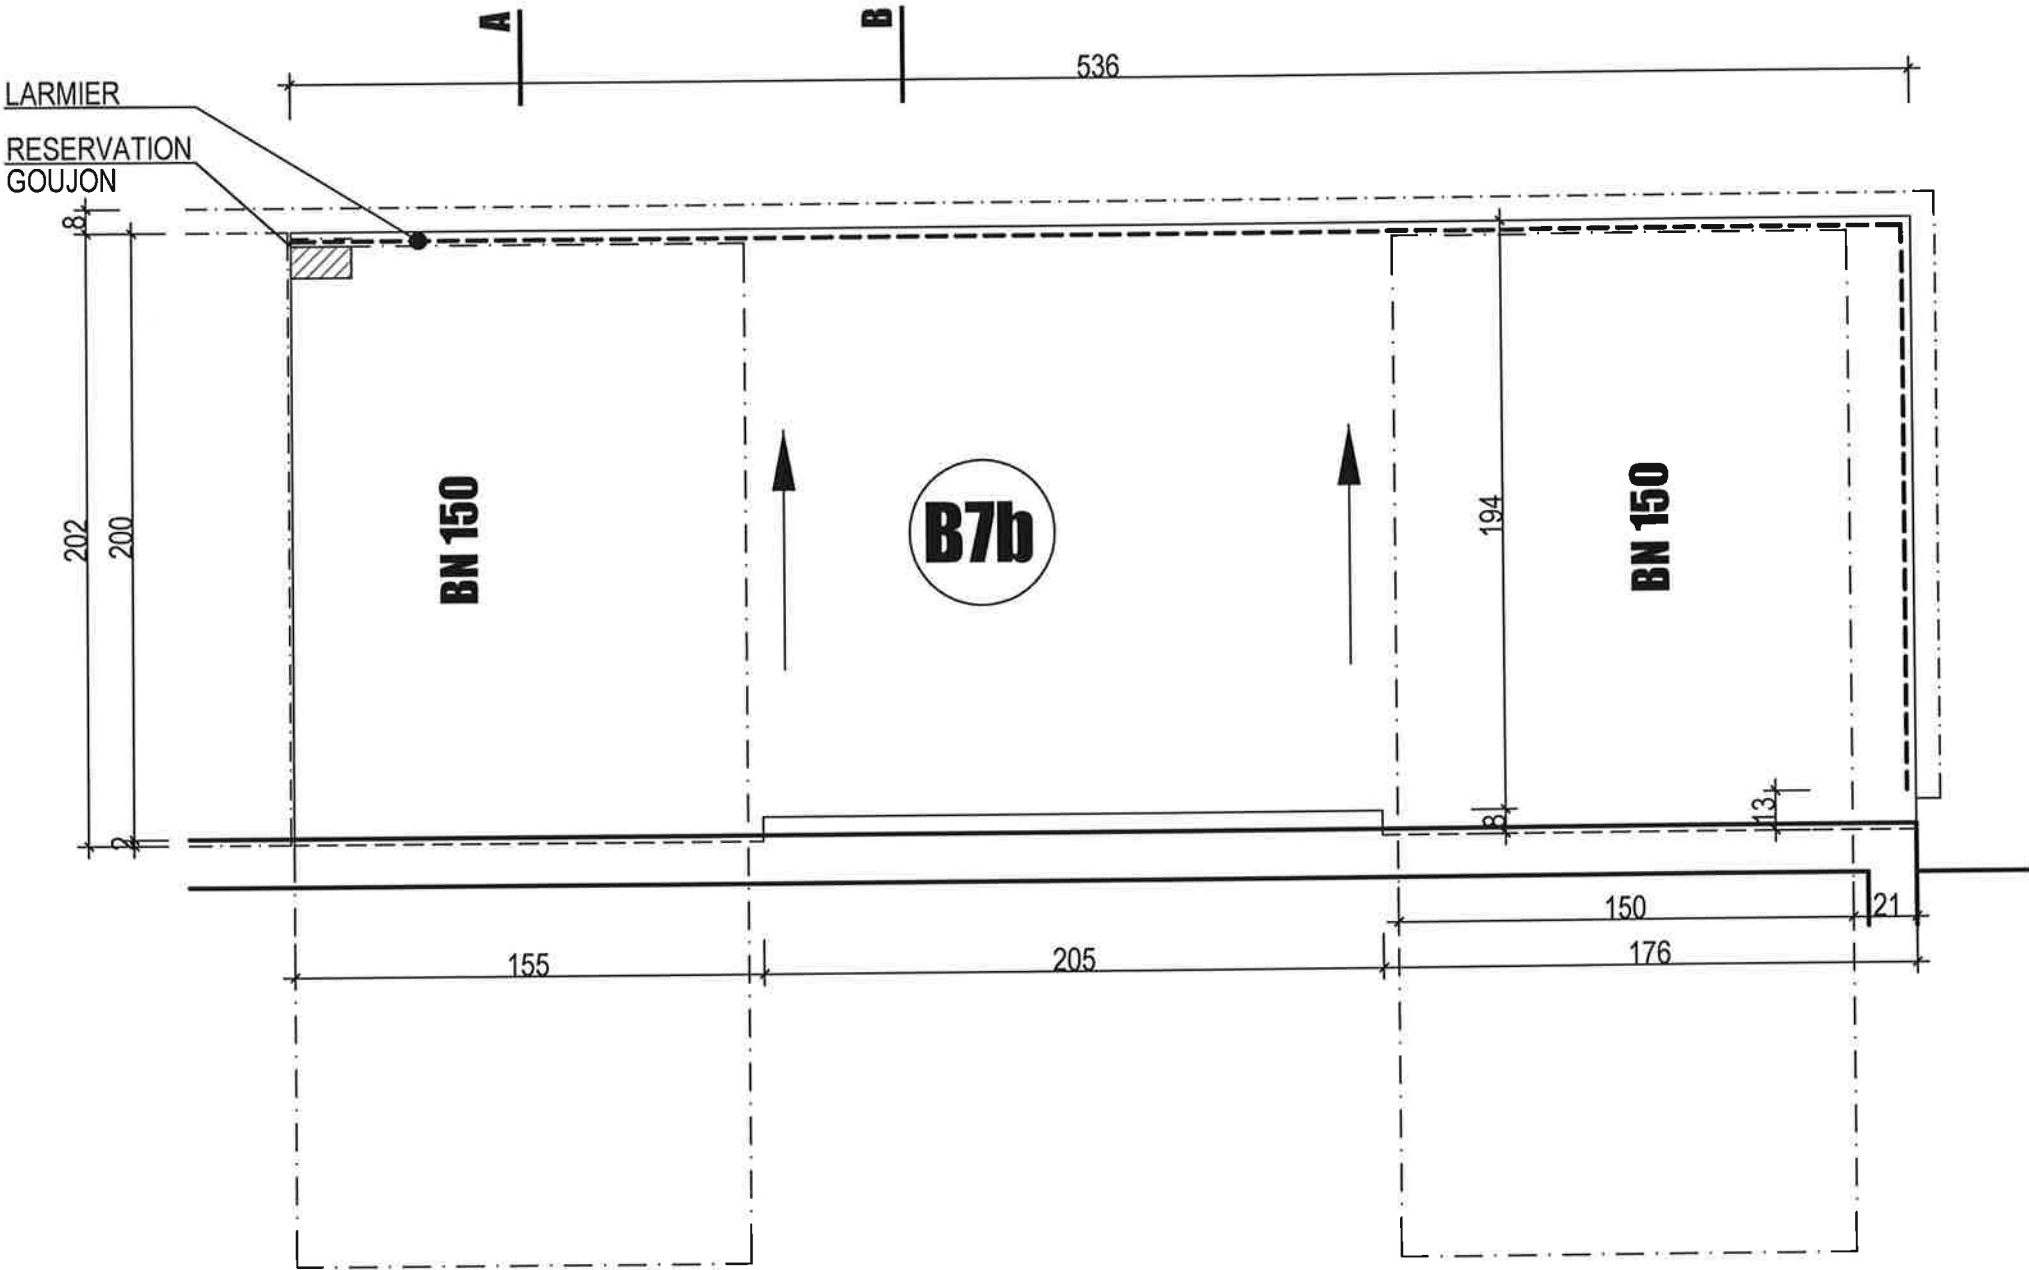


COUPE A

Ech: 1/25

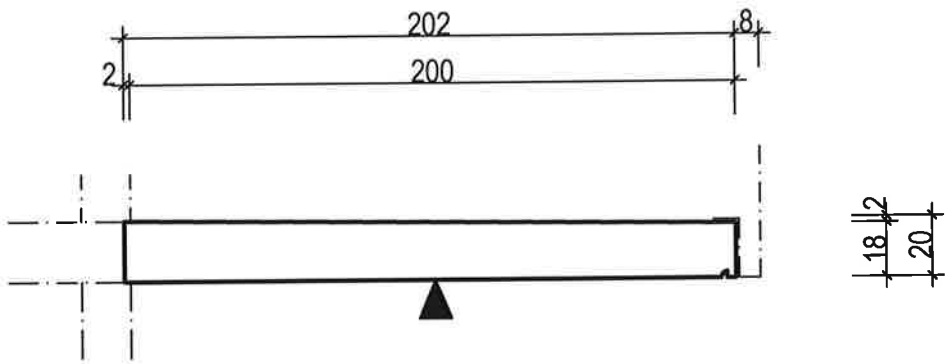

COUPE B


Ech: 1/25

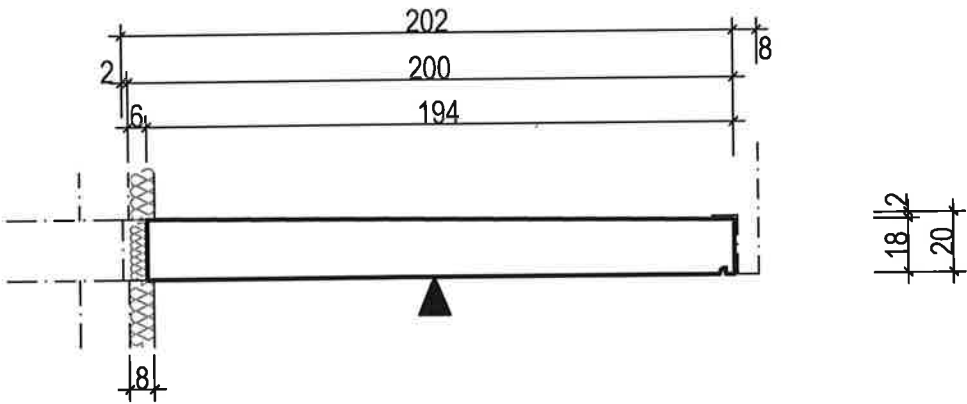

PLANCHER sur -3


Vue en plan

Ech: 1/50

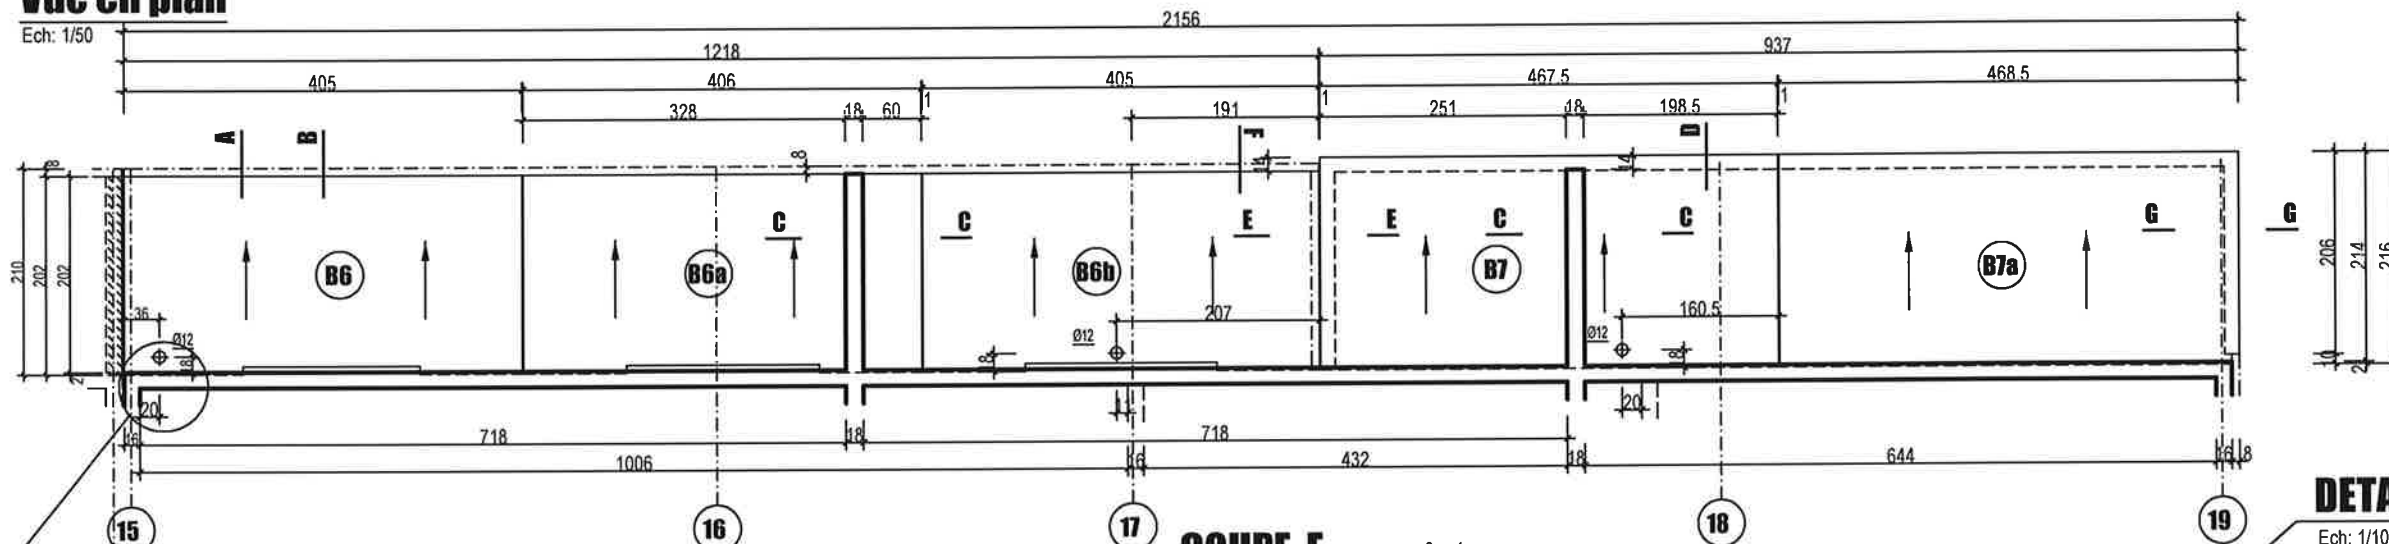


DETAIL

Ech: 1/10

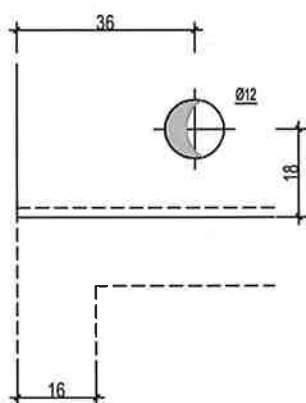


COUPE A

Ech: 1/25

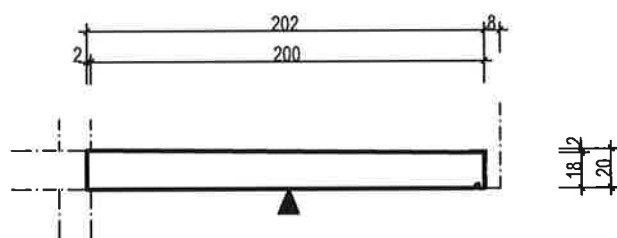


COUPE B

Ech: 1/25

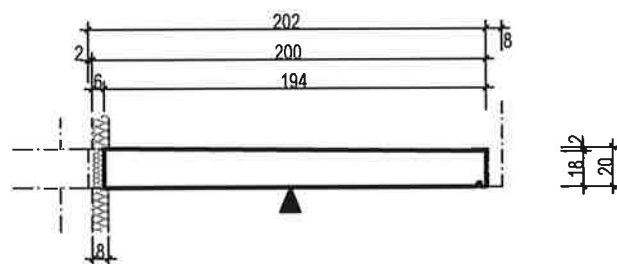


COUPE E

Ech: 1/10

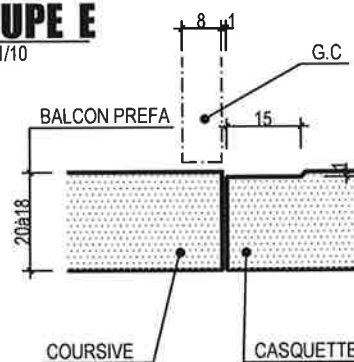


COUPE C

Ech: 1/10

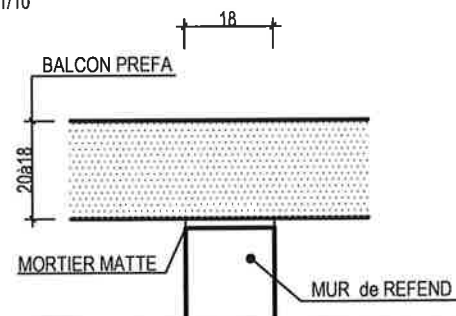


DETAIL

Ech: 1/10

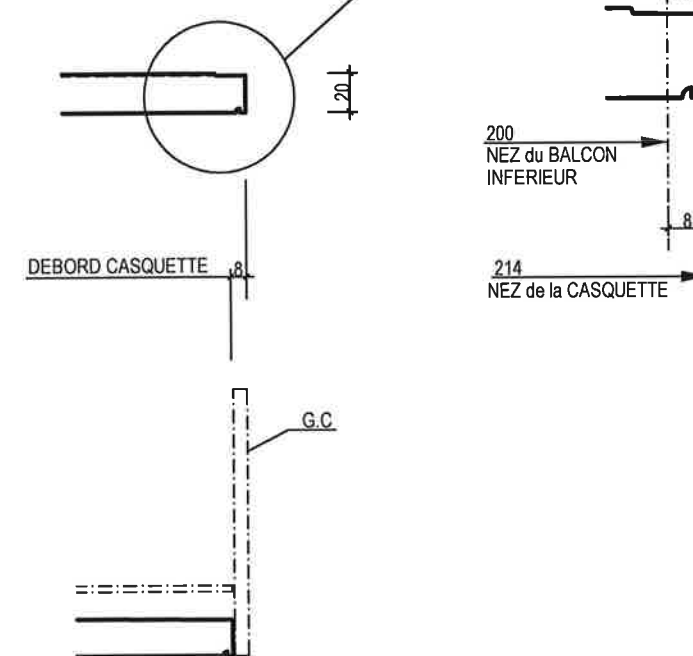


COUPE D

Ech: 1/25

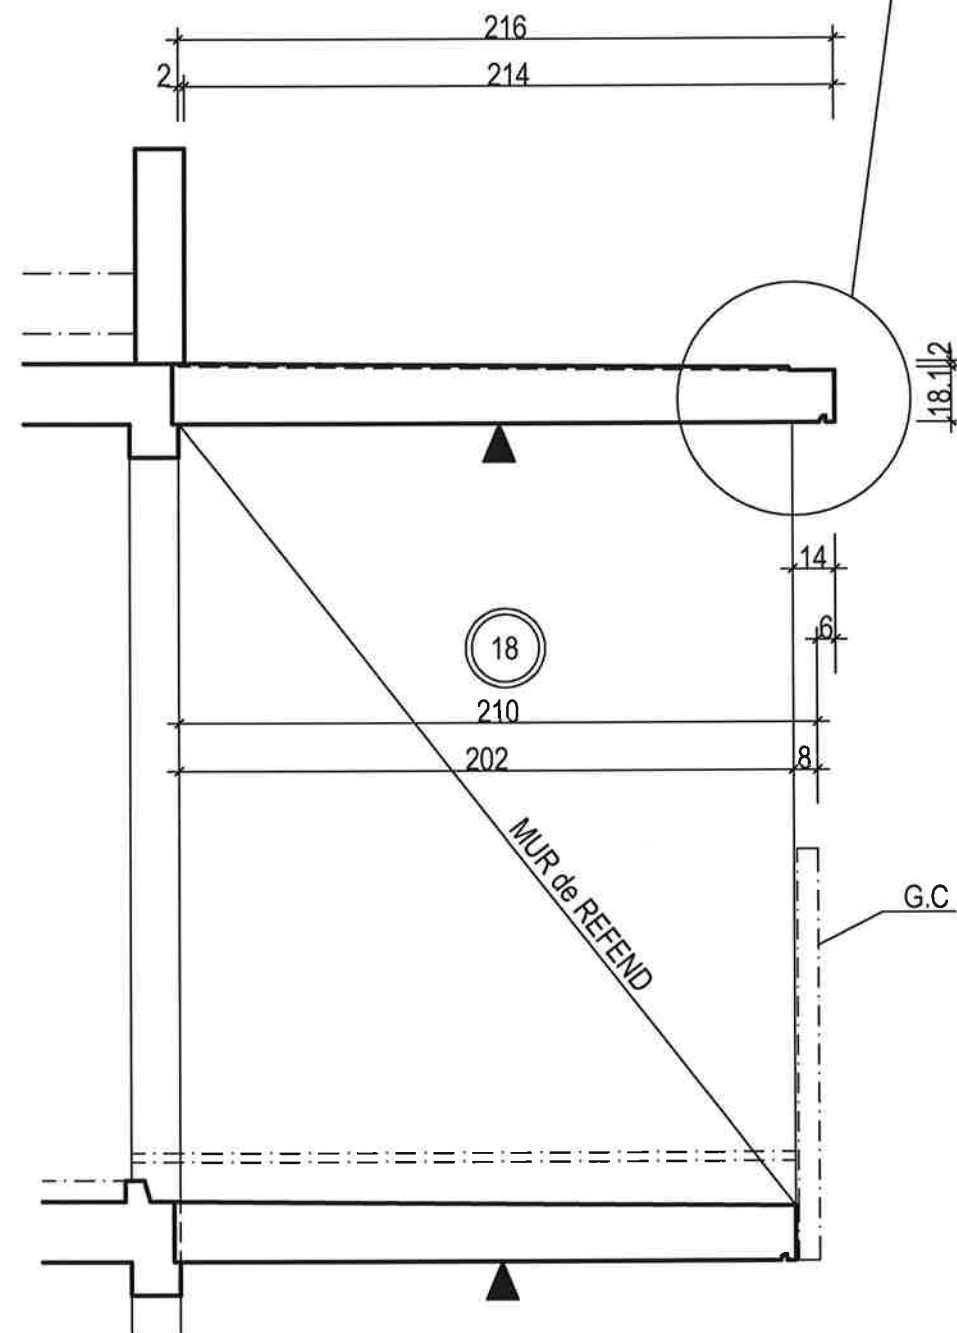


DETAIL

Ech: 1/10

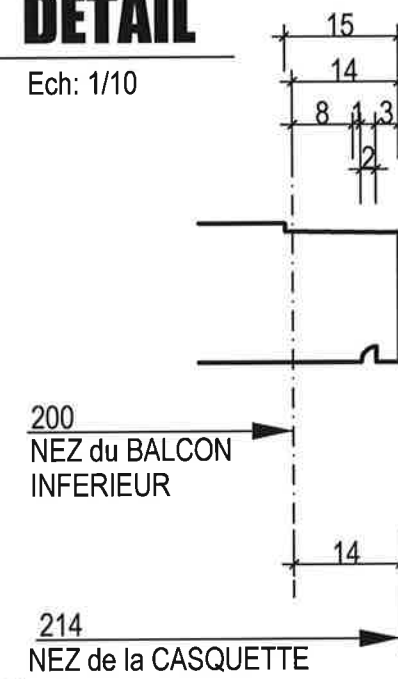

COUPE F

Ech: 1/10

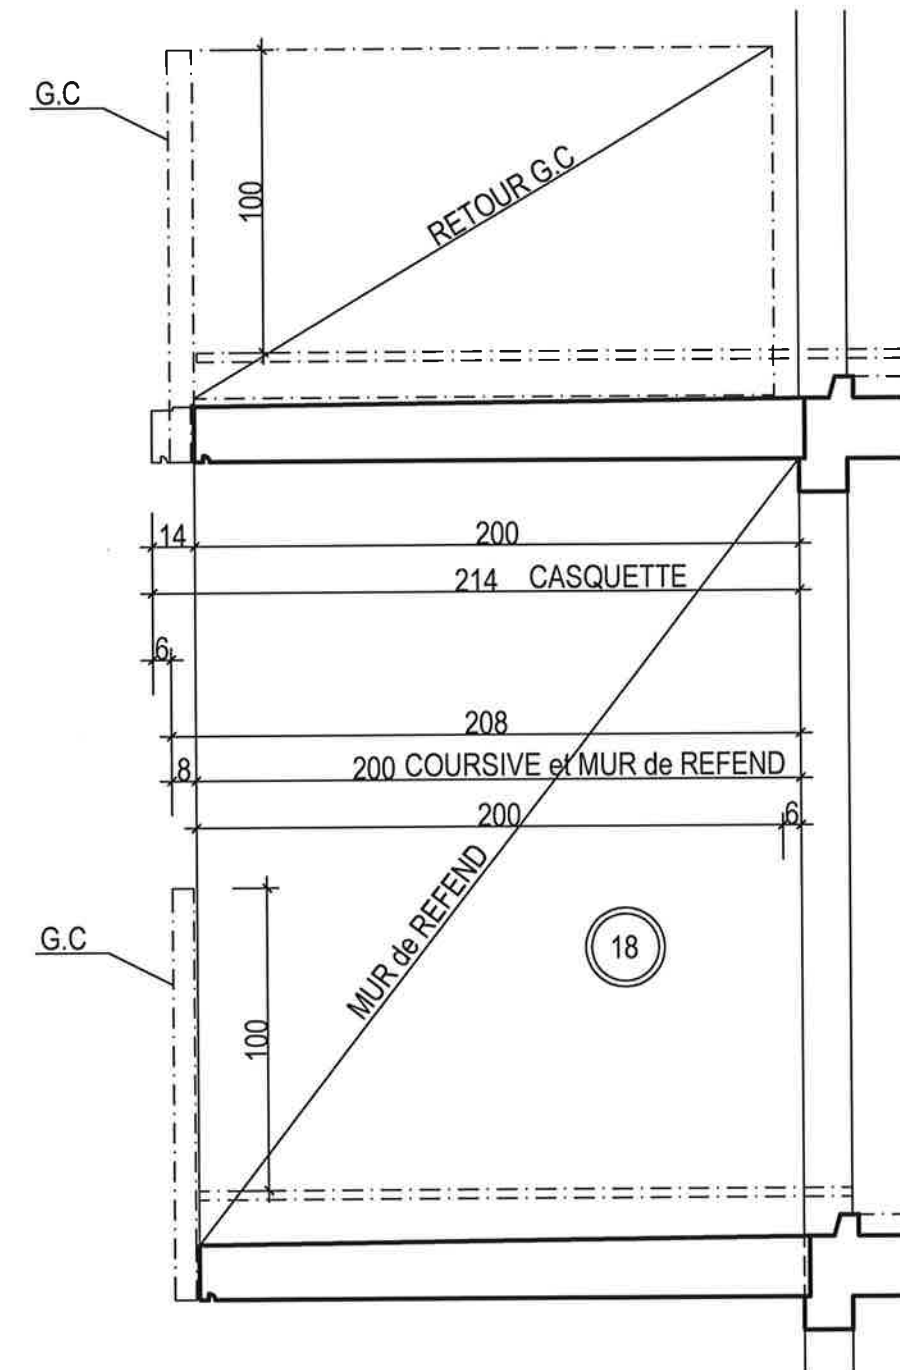



B6

1 p


Poids: 4250 Kg

DETAIL


Ech: 1/10

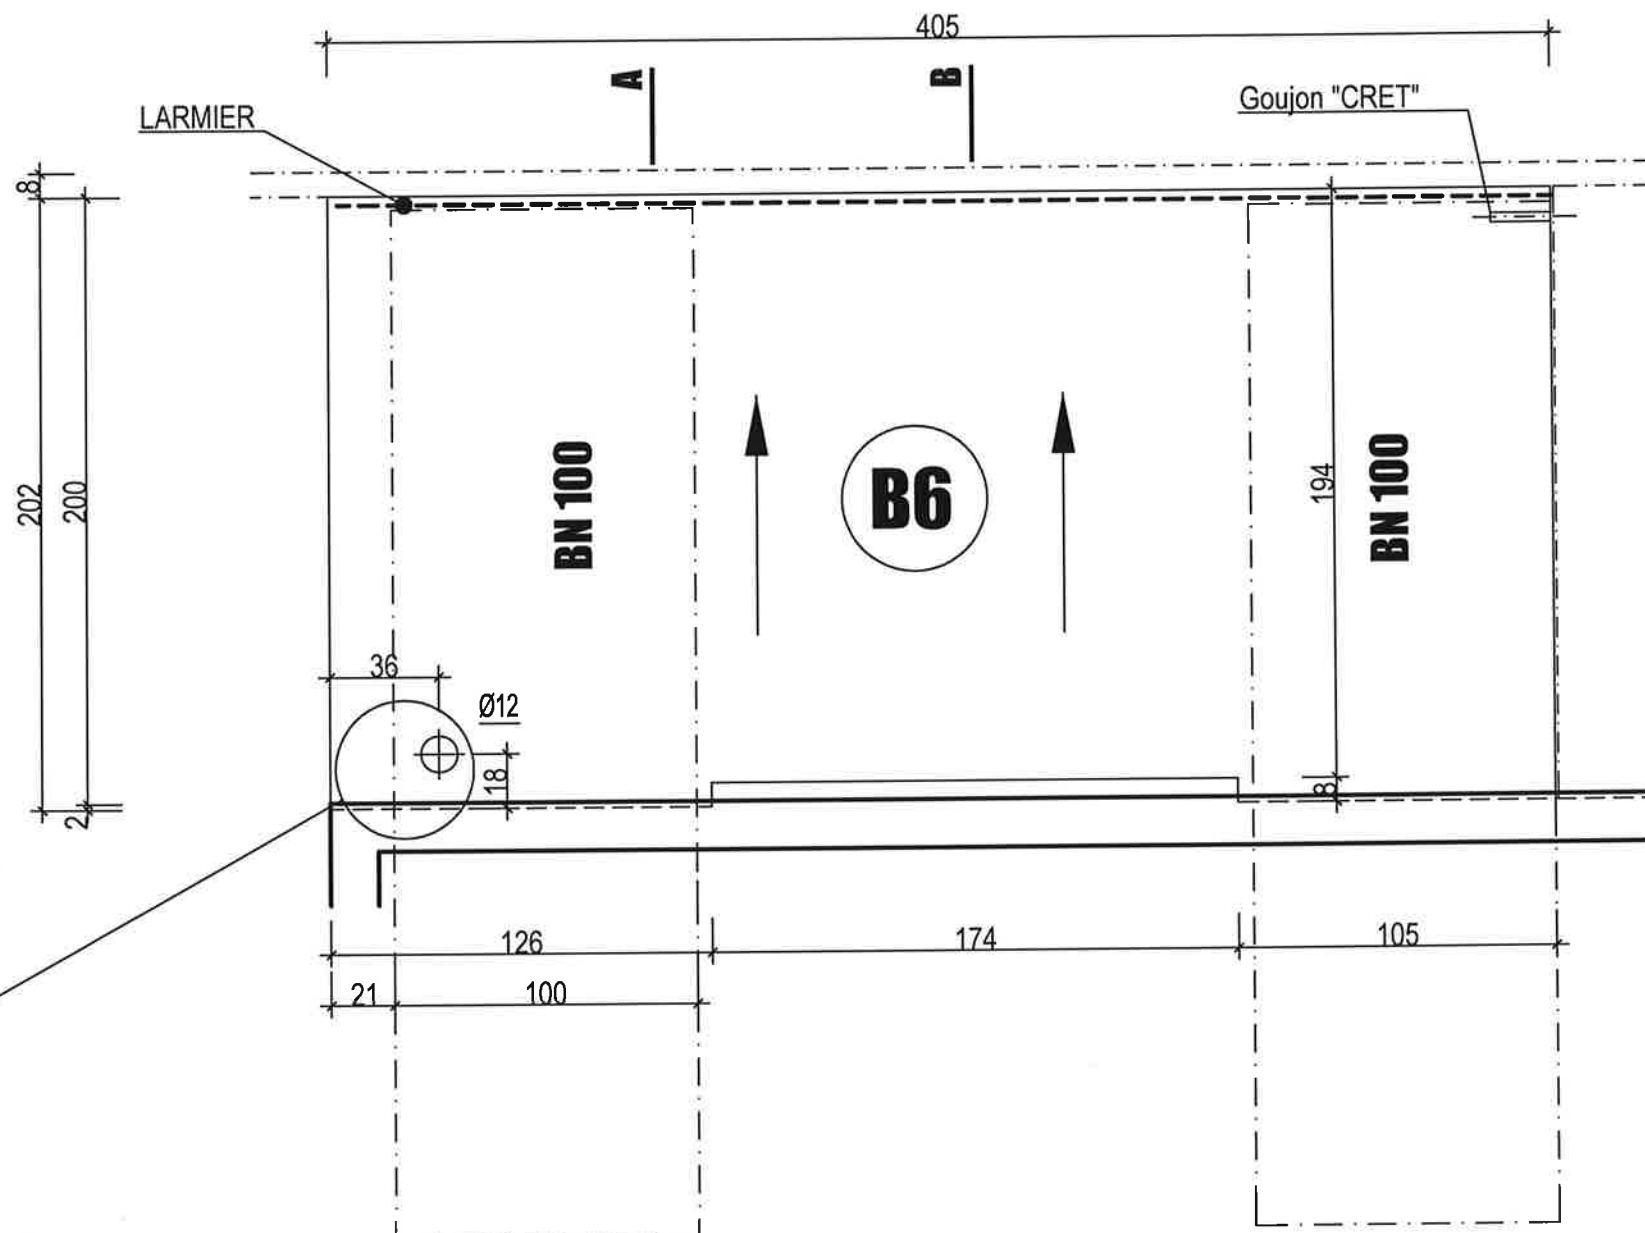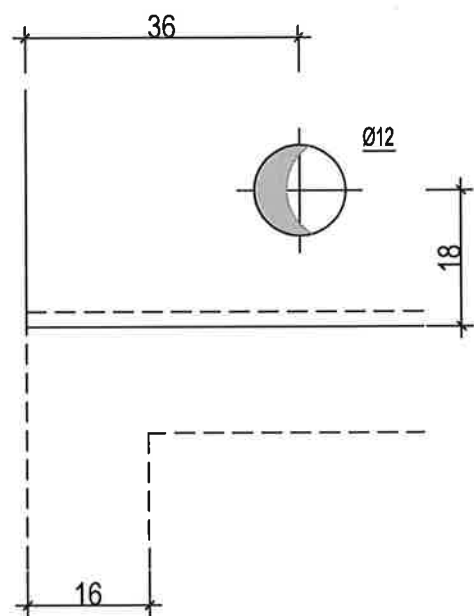**COUPE A**

Ech: 1/25

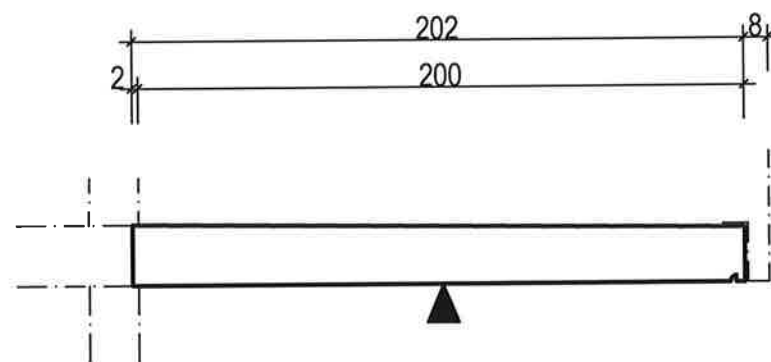**COUPE B**


Ech: 1/25

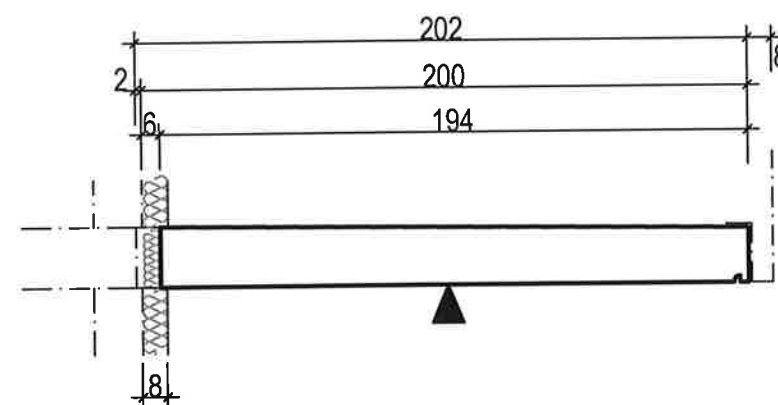

B6a


1 p

Poids: 4250 Kg

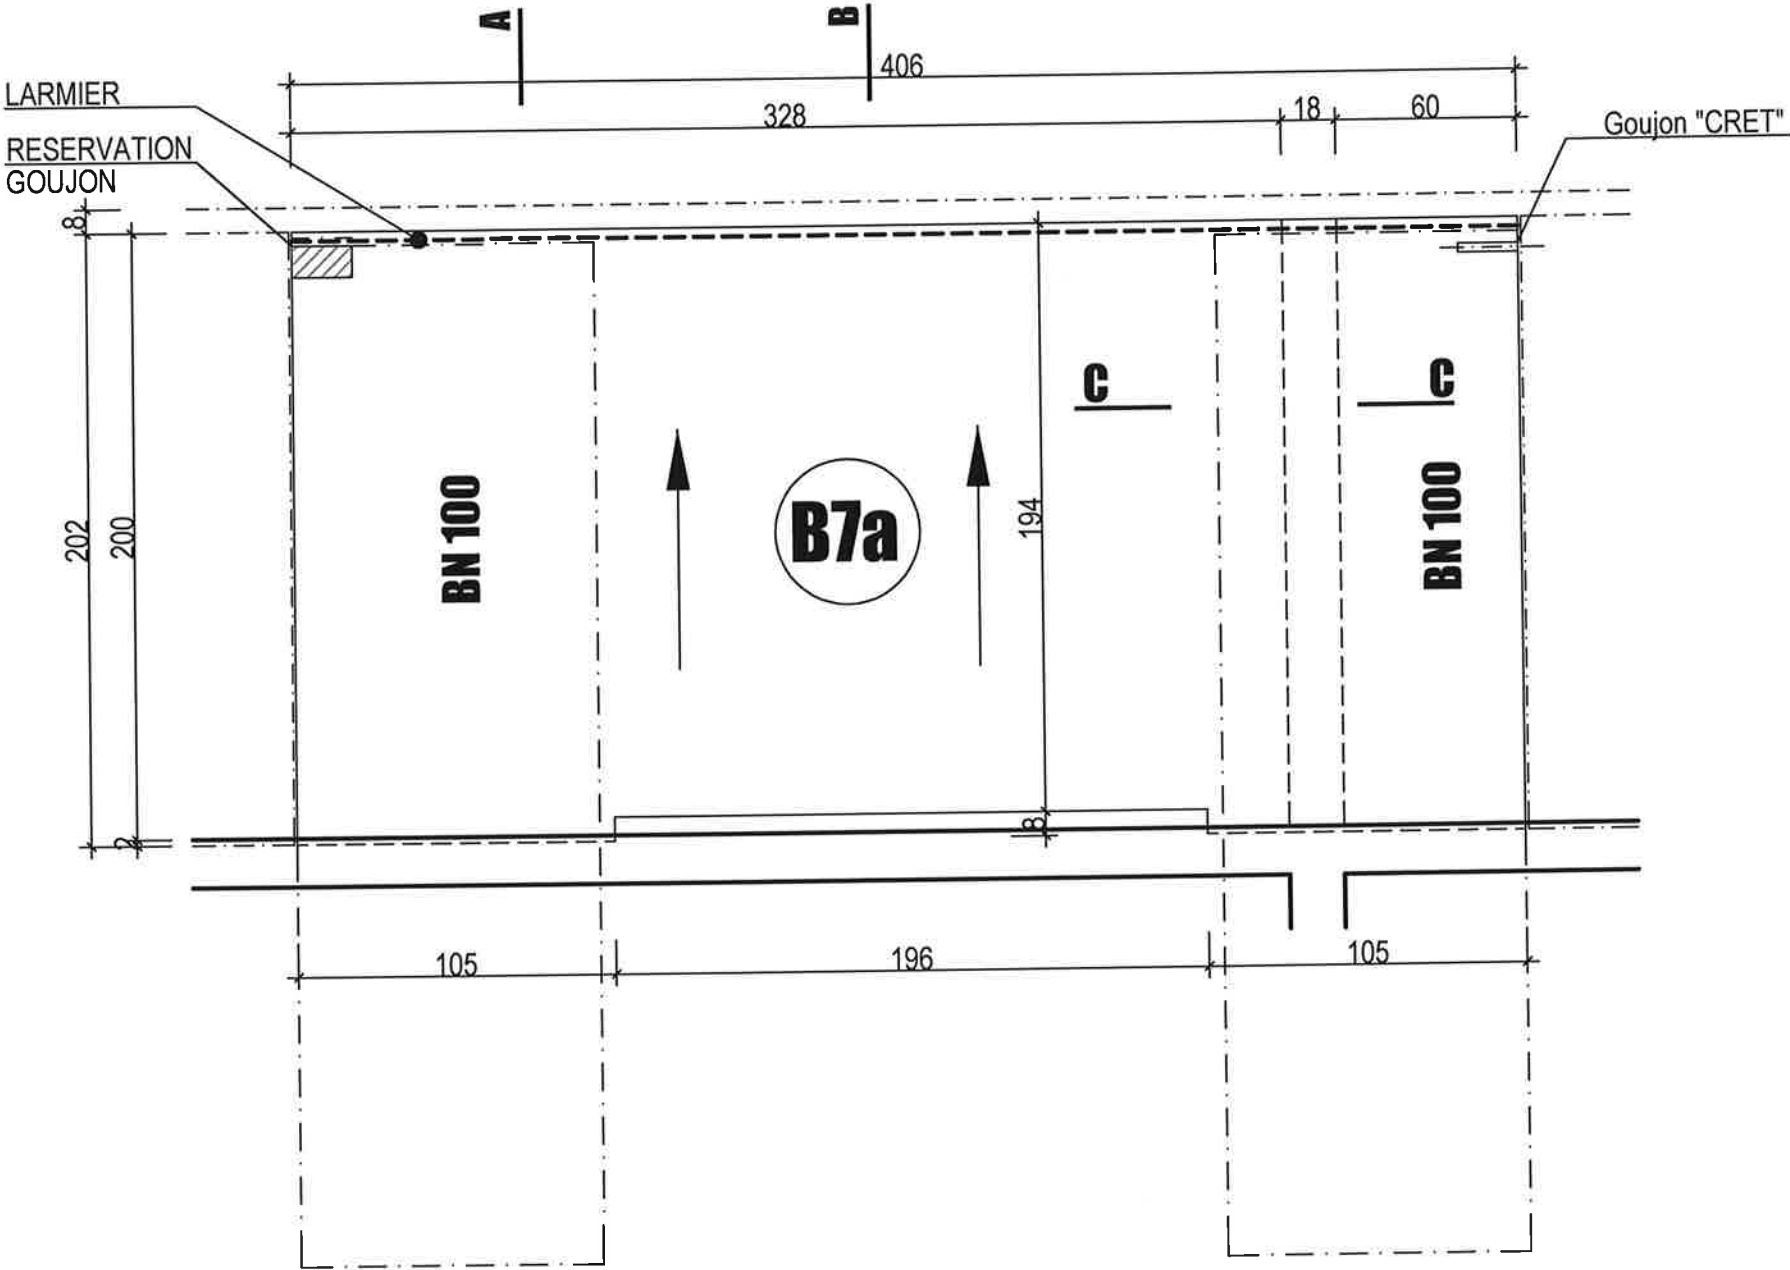


COUPE C

Ech: 1/10

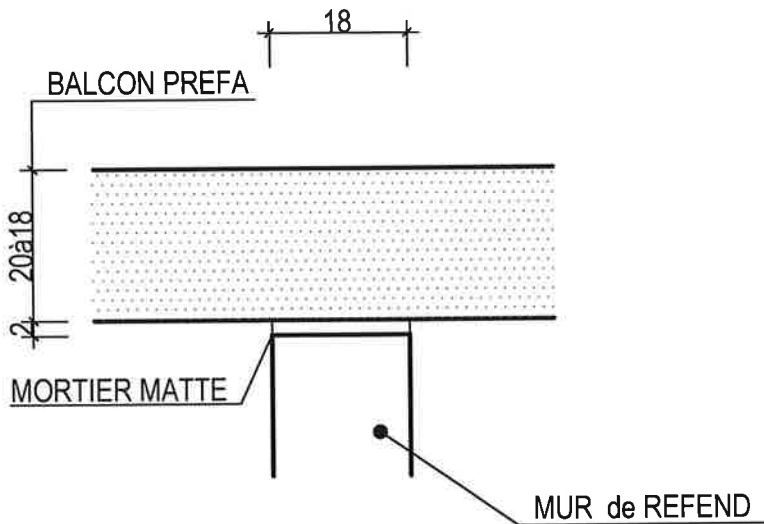


COUPE A


Ech: 1/25

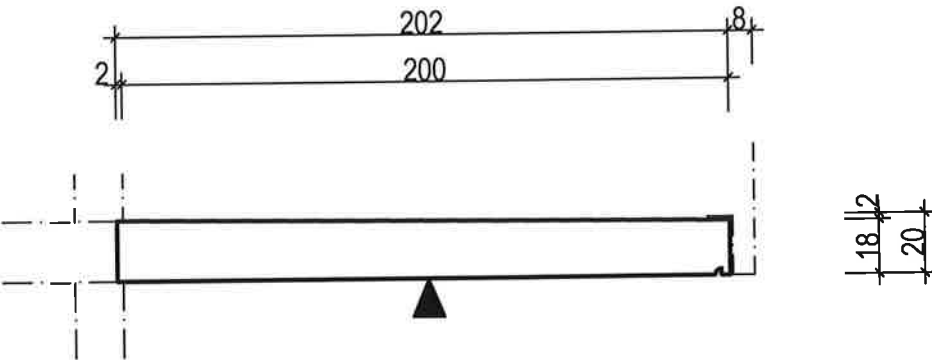


COUPE B

Ech: 1/25

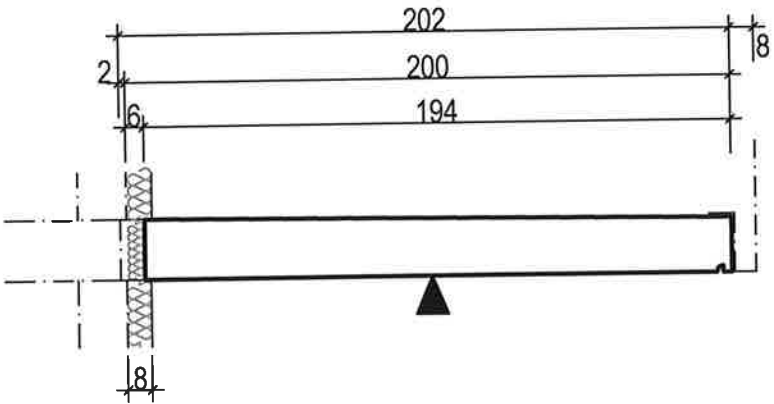


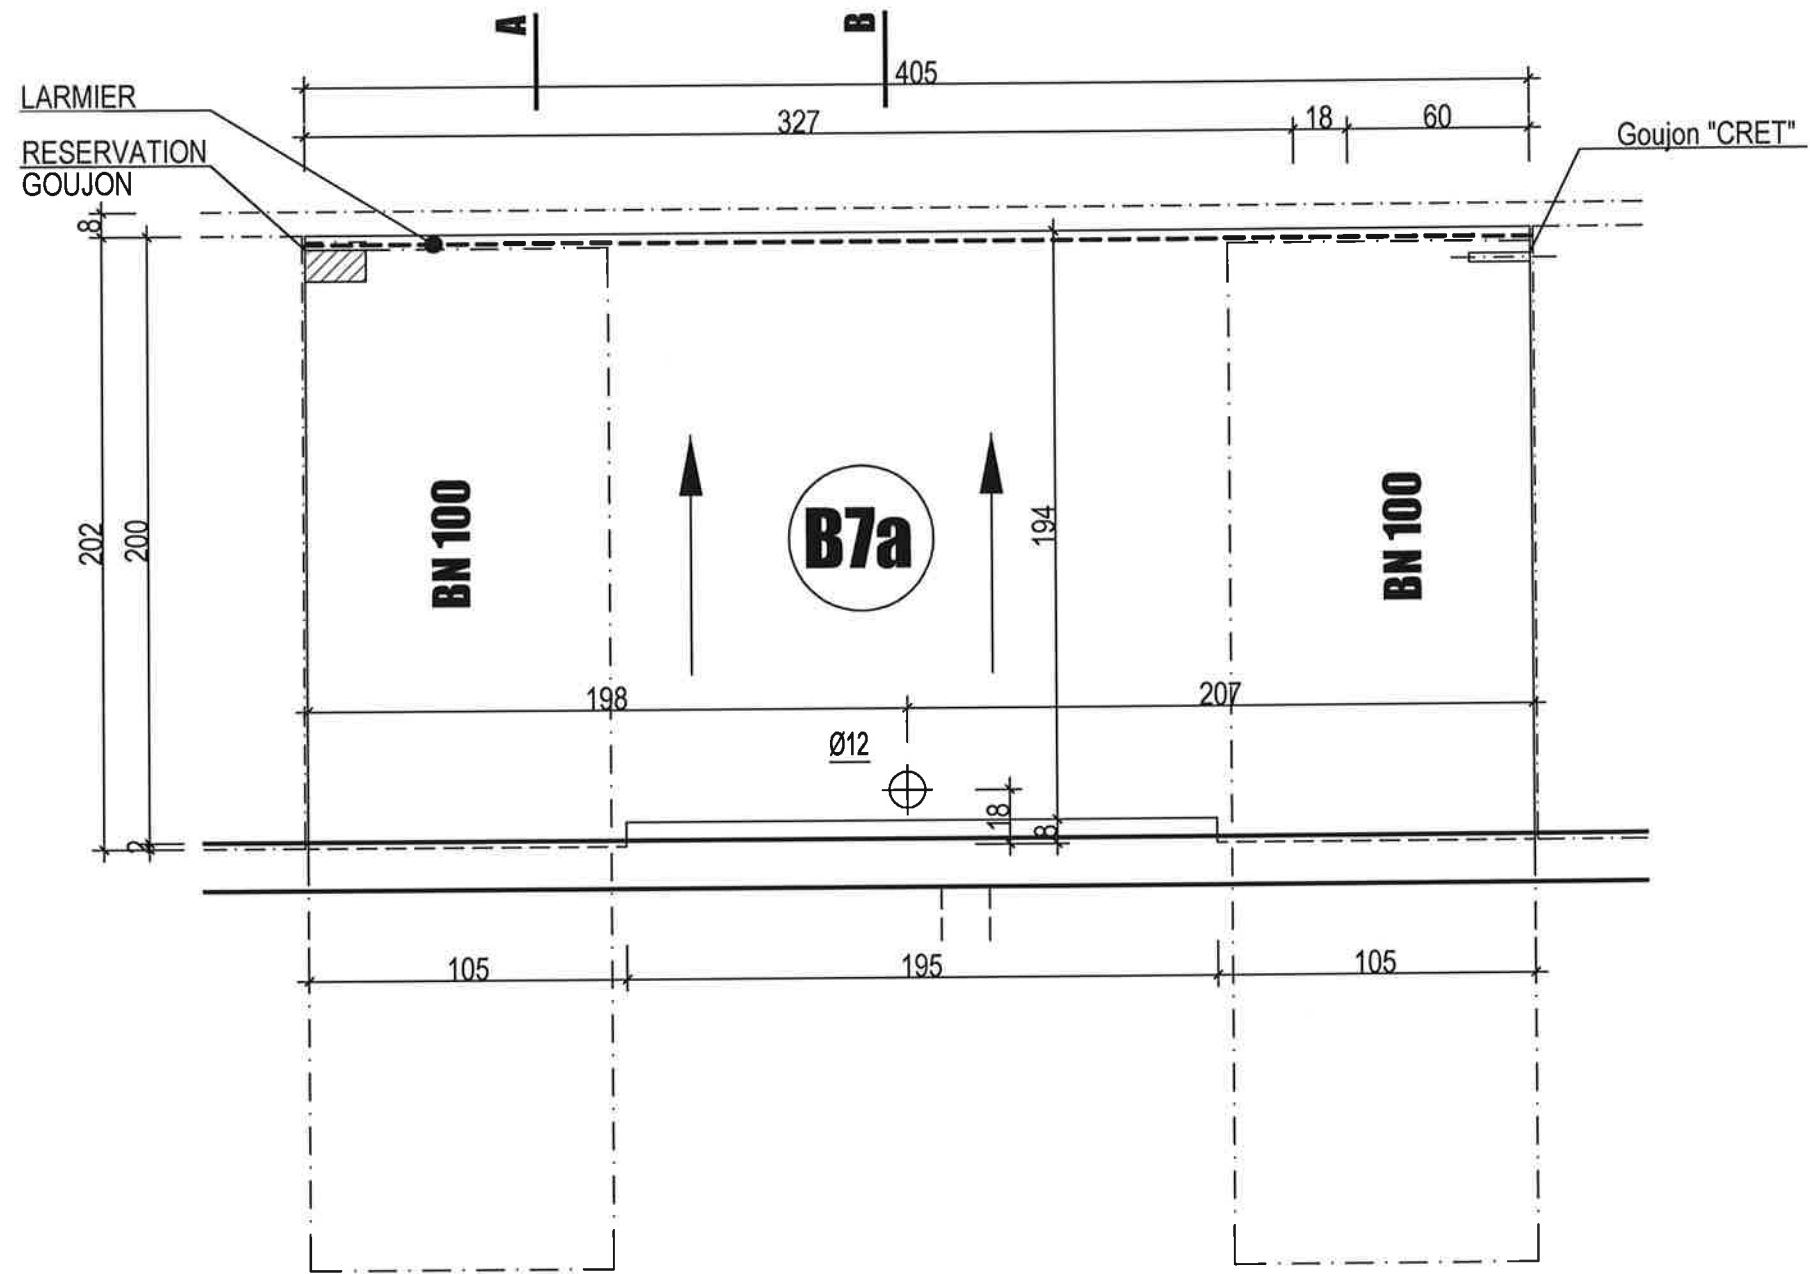


COUPE A
Ech: 1/25

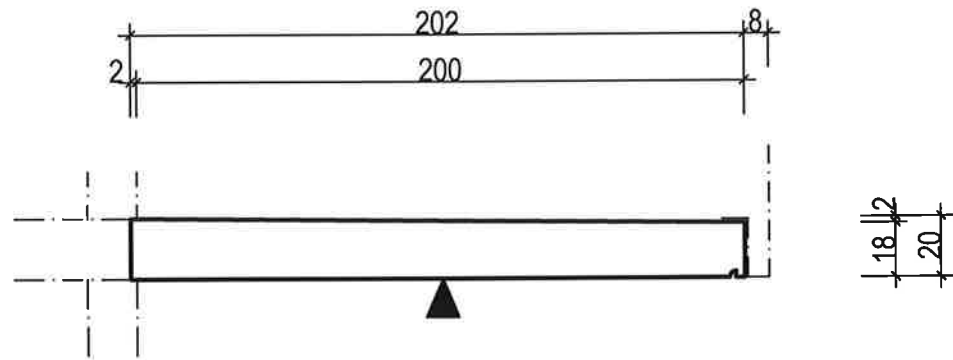


COUPE B
Ech: 1/25

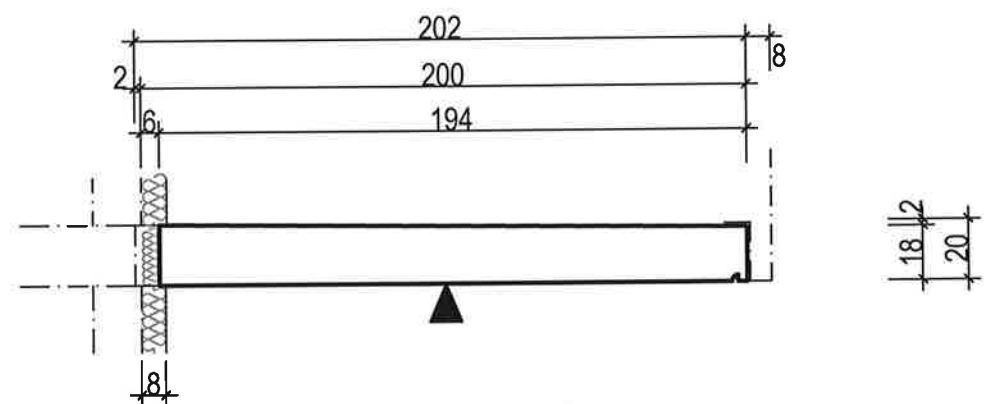


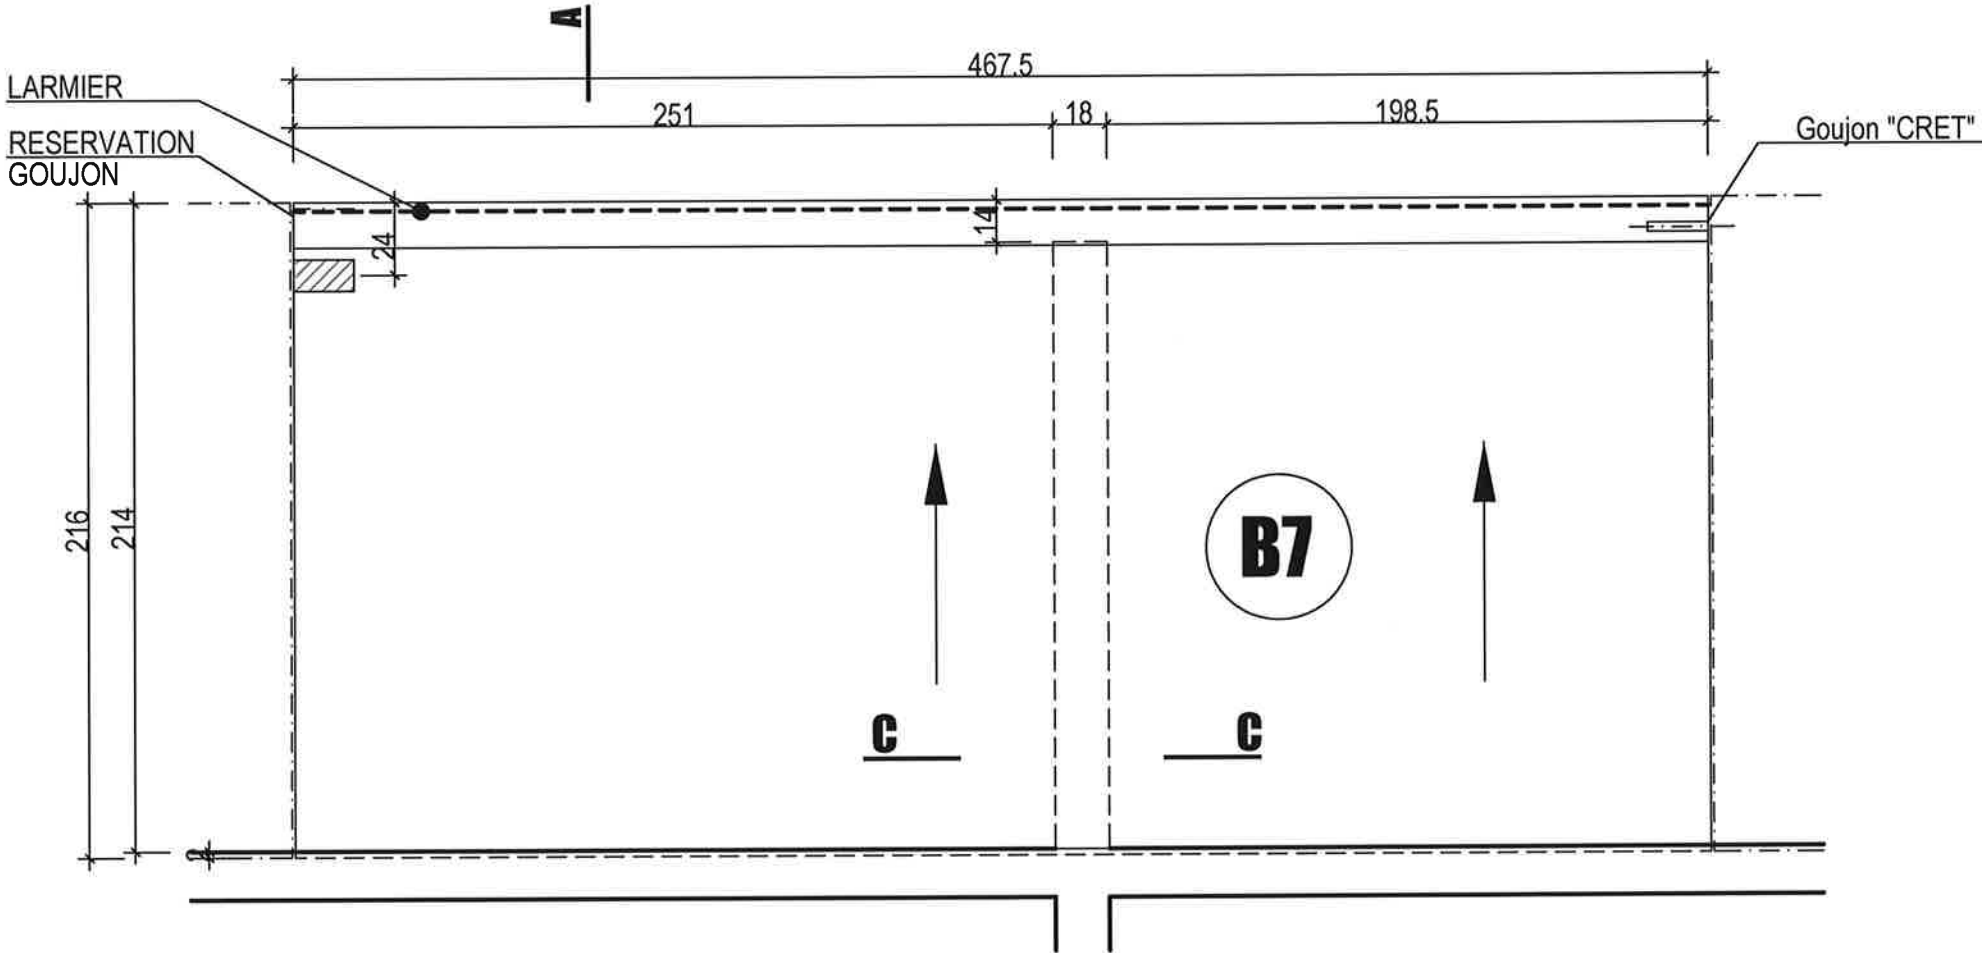


COUPE C
Ech: 1/10

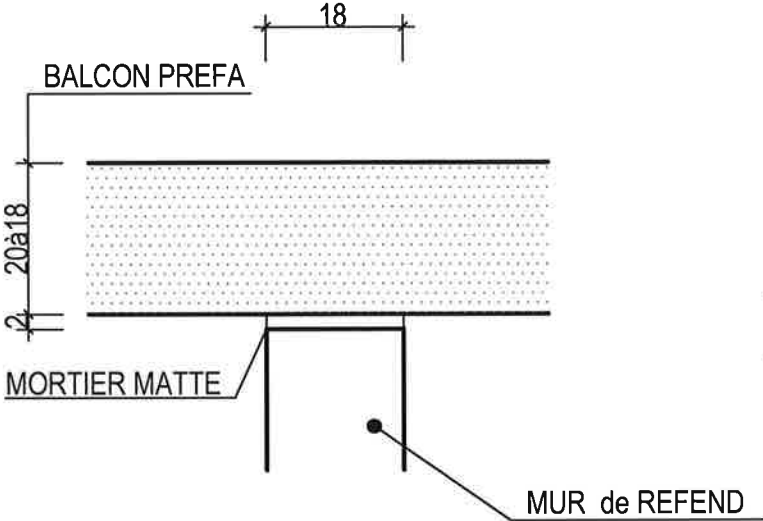


COUPE A
Ech: 1/25

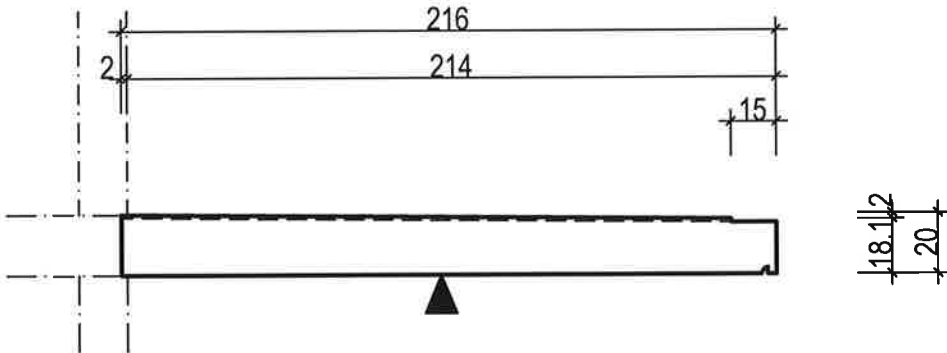

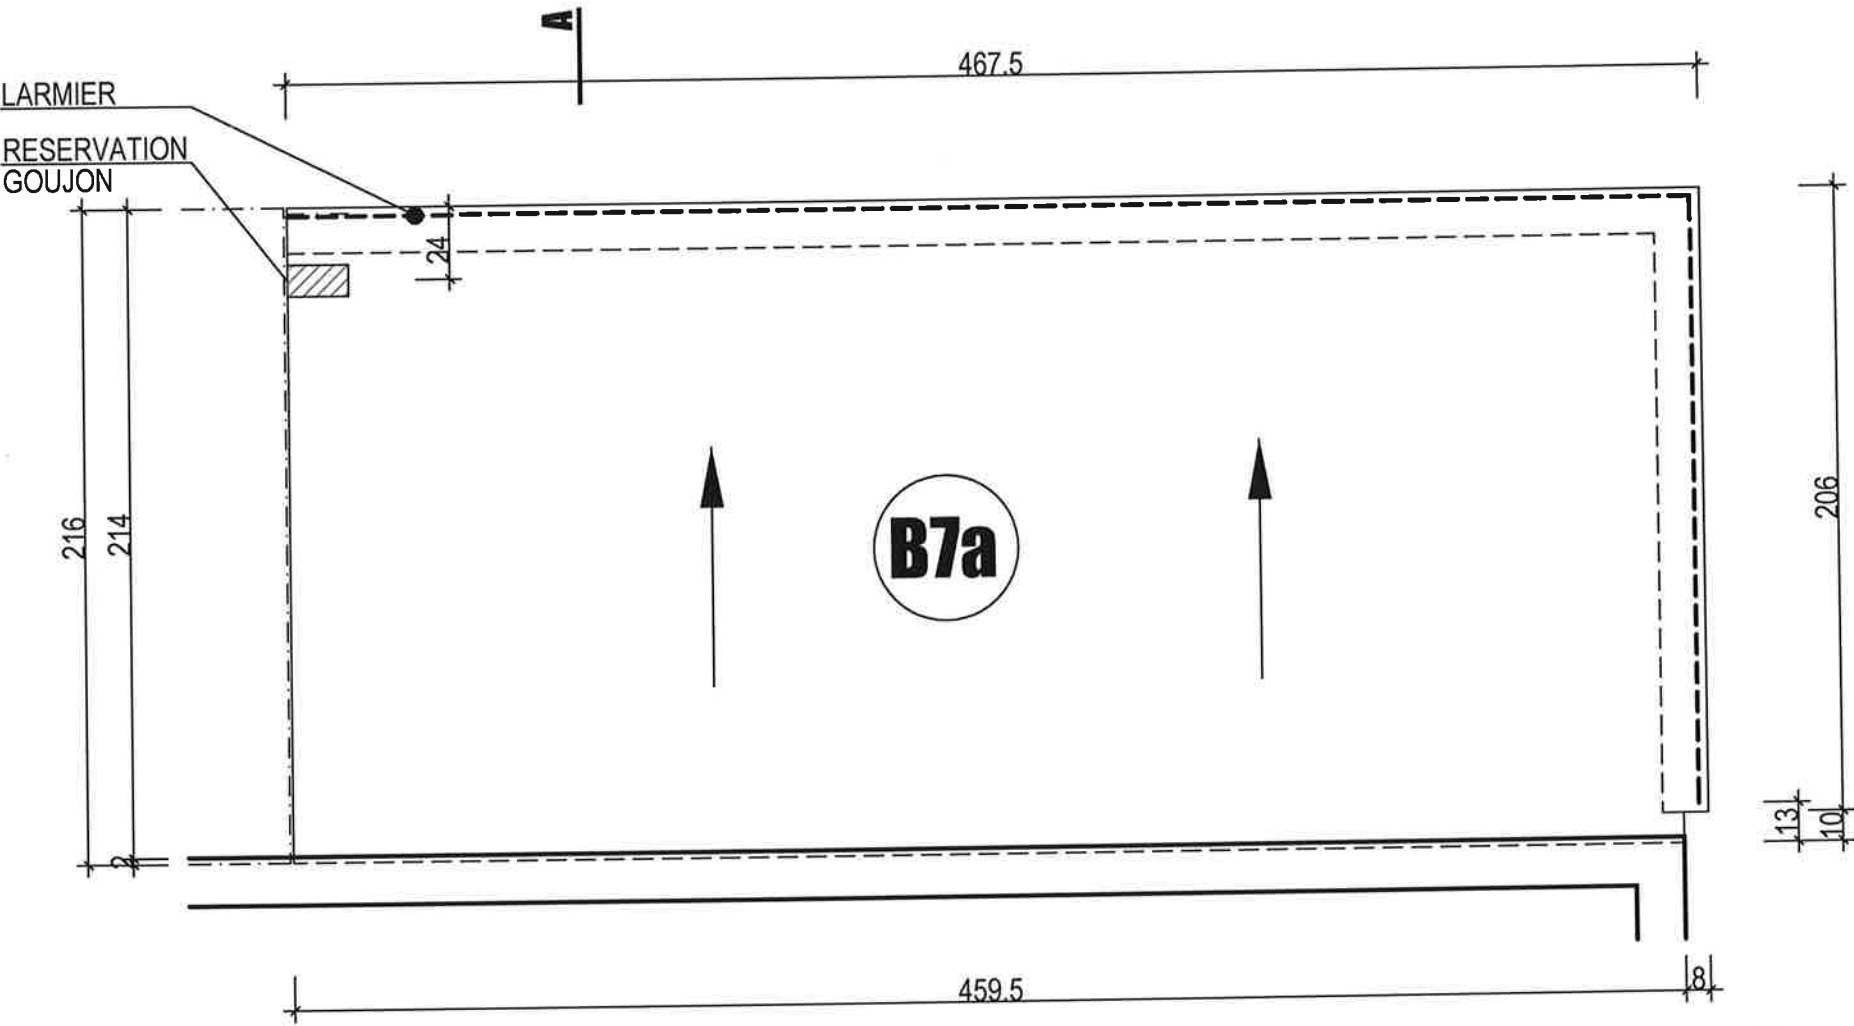


COUPE A
Ech: 1/25

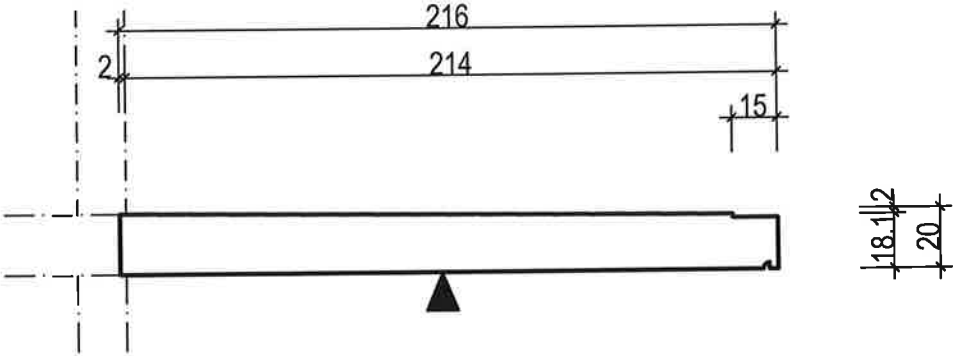

PLANCHER sur -2


Vue en plan

Ech: 1/50

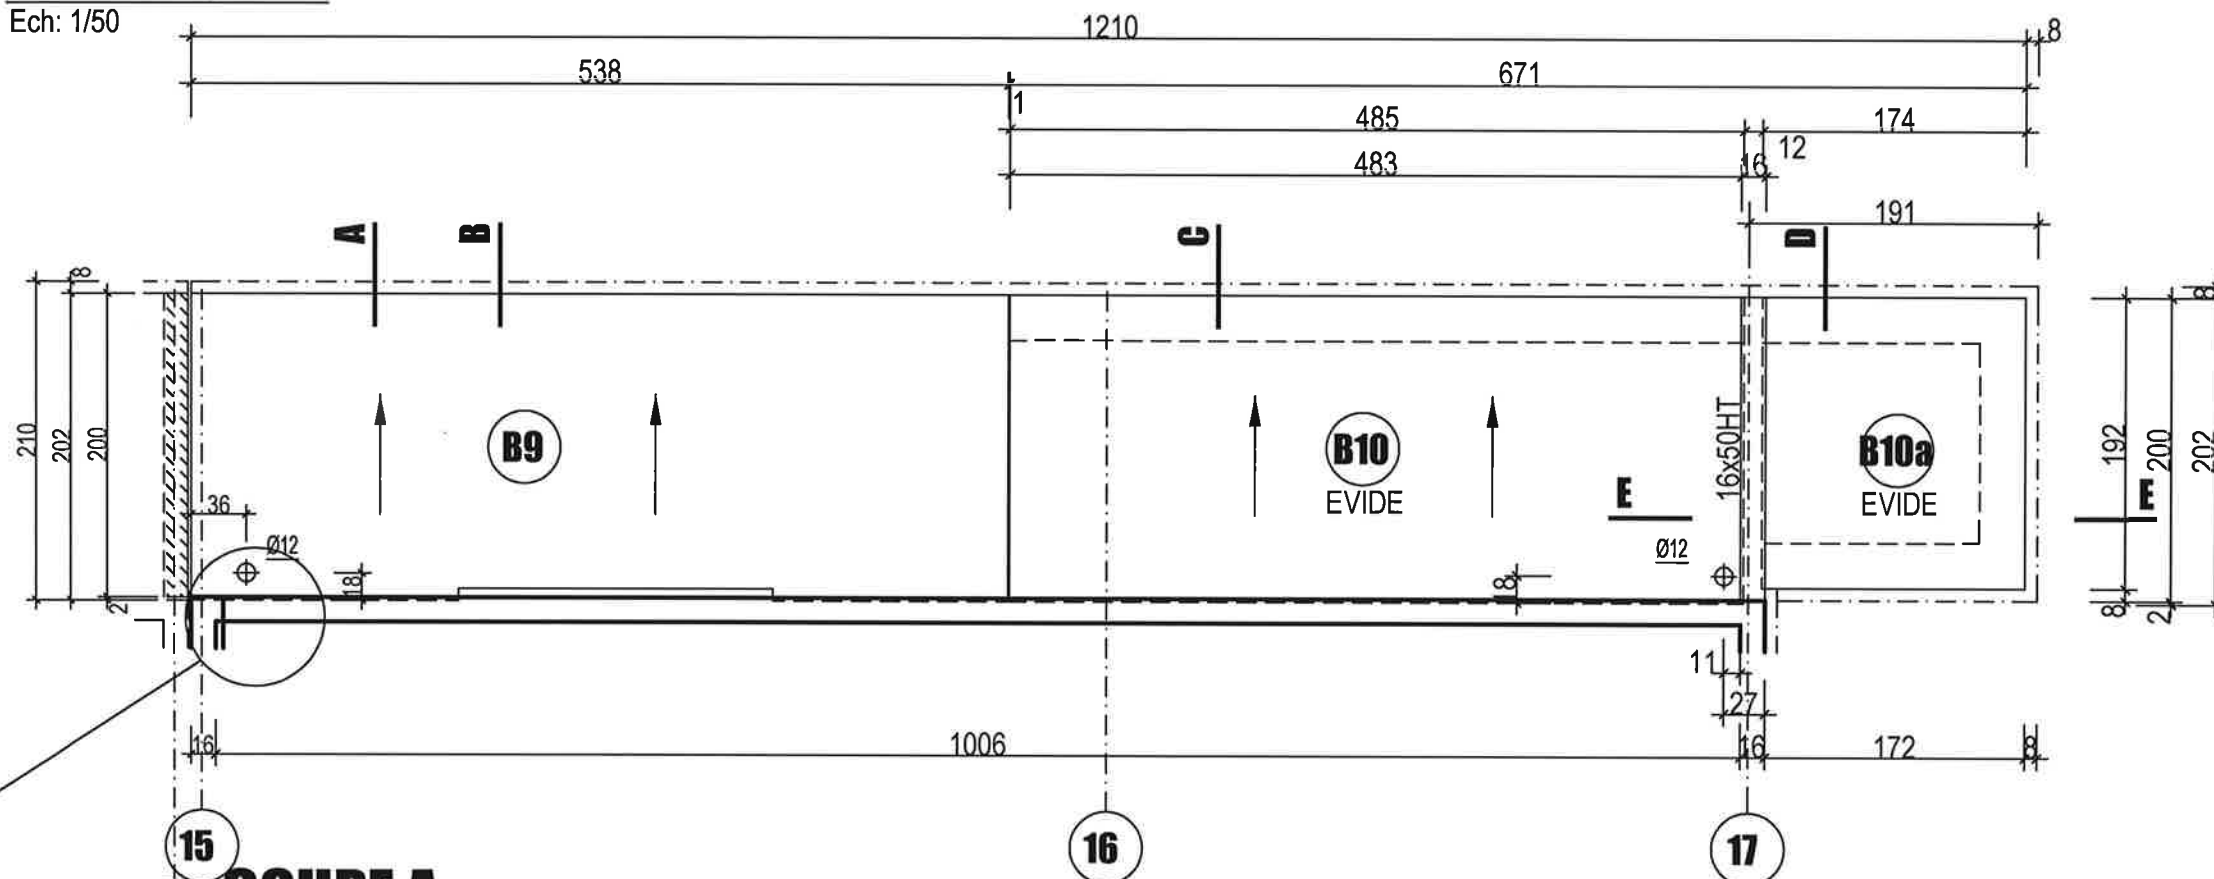


DETAIL

Ech: 1/10

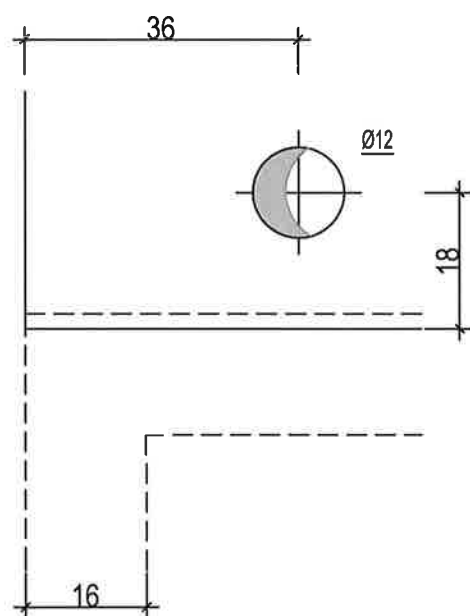


COUPE A

Ech: 1/25

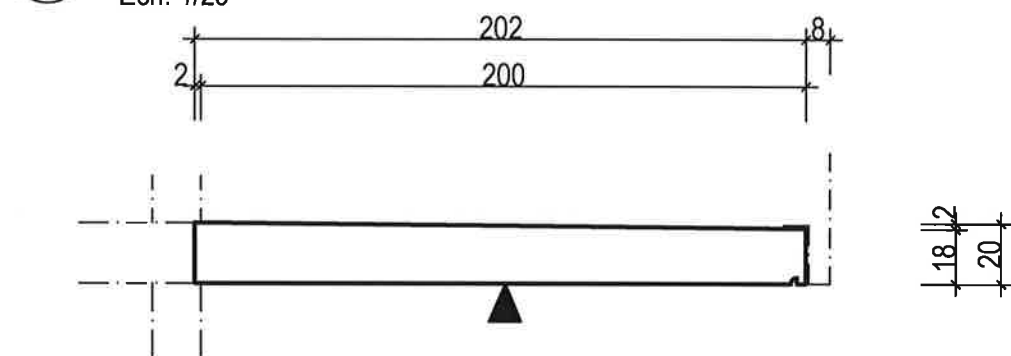


COUPE B

Ech: 1/25

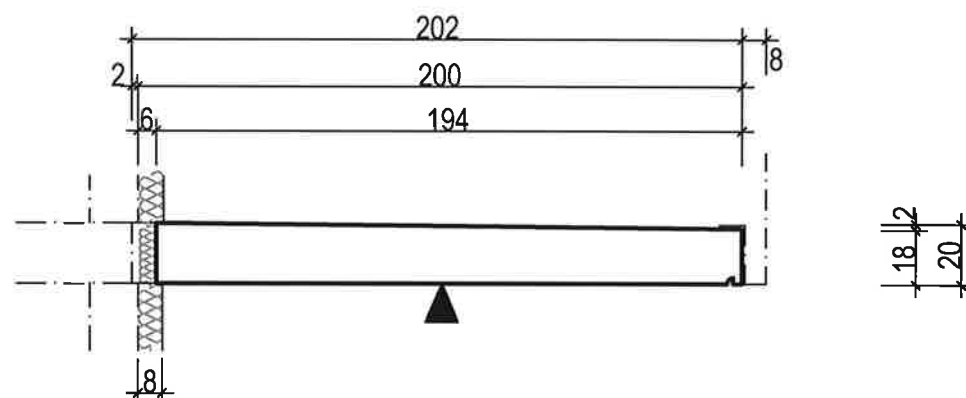


COUPE C

Ech: 1/25

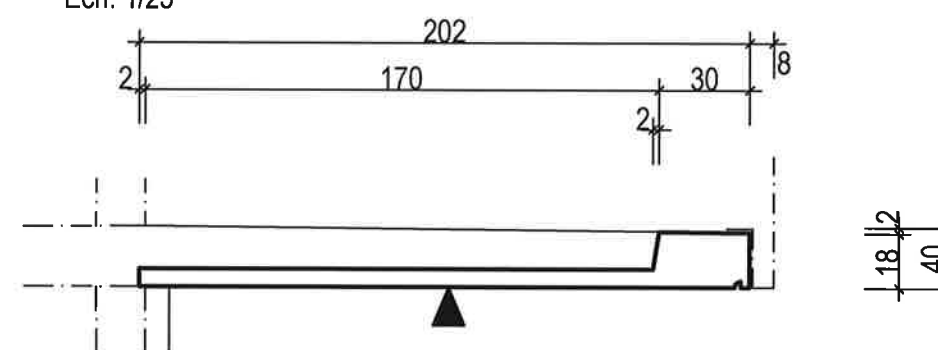


COUPE D

Ech: 1/25

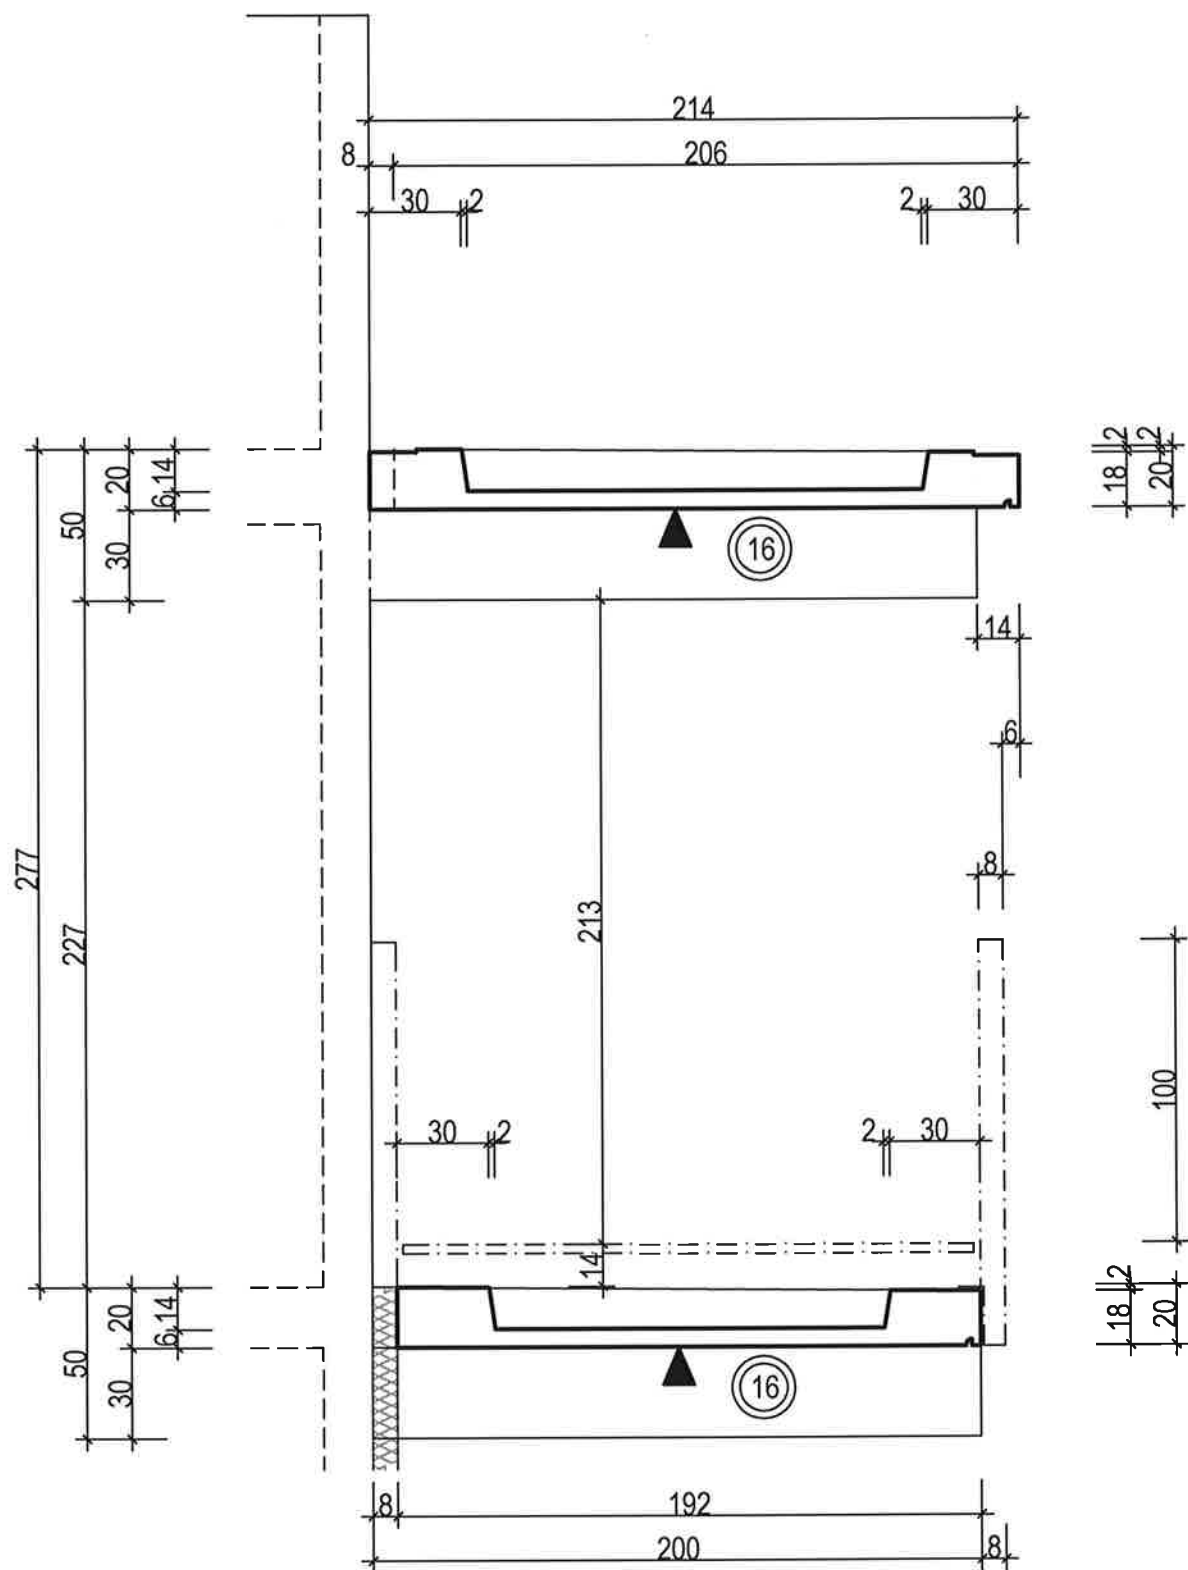

COUPE E

Ech: 1/25

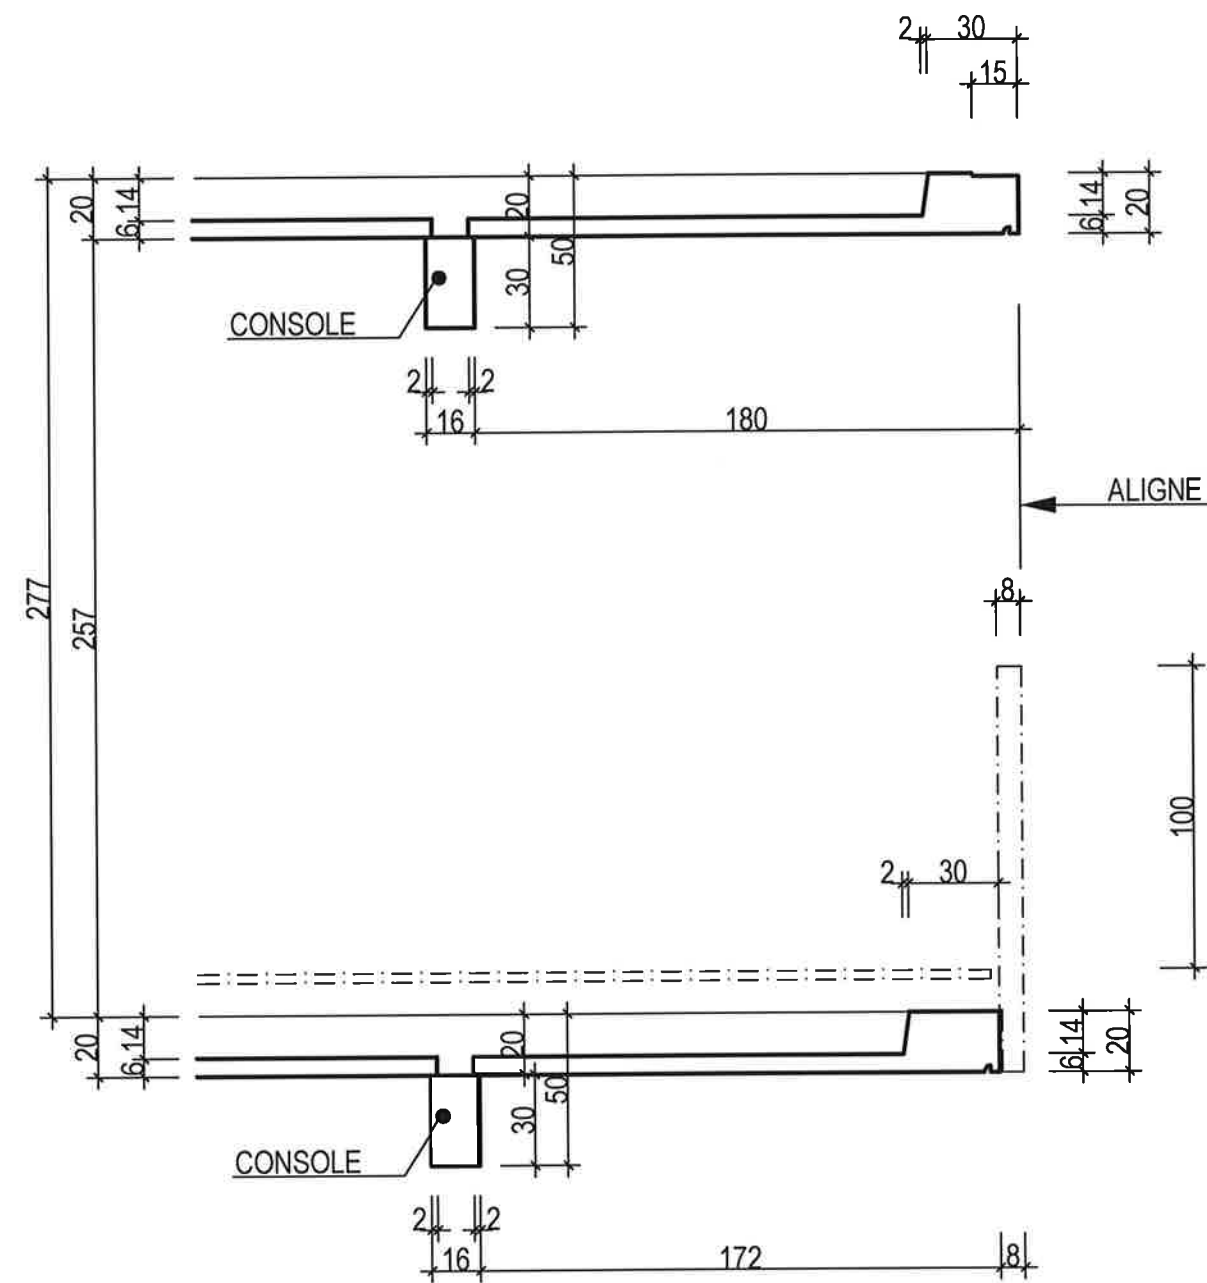


B9

1 p


Poids: 5350 Kg

DETAIL


Ech: 1/10

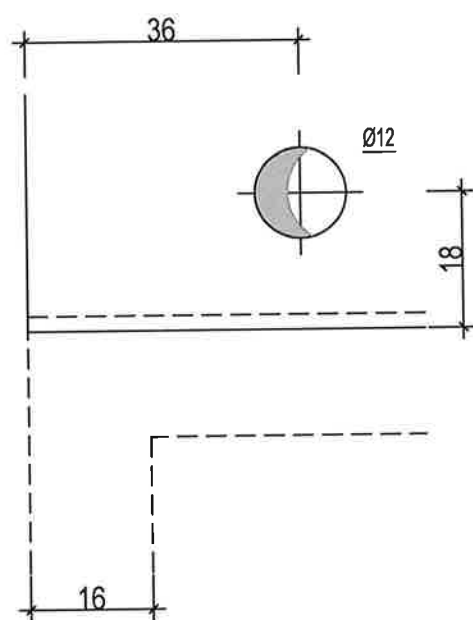


LARMIER

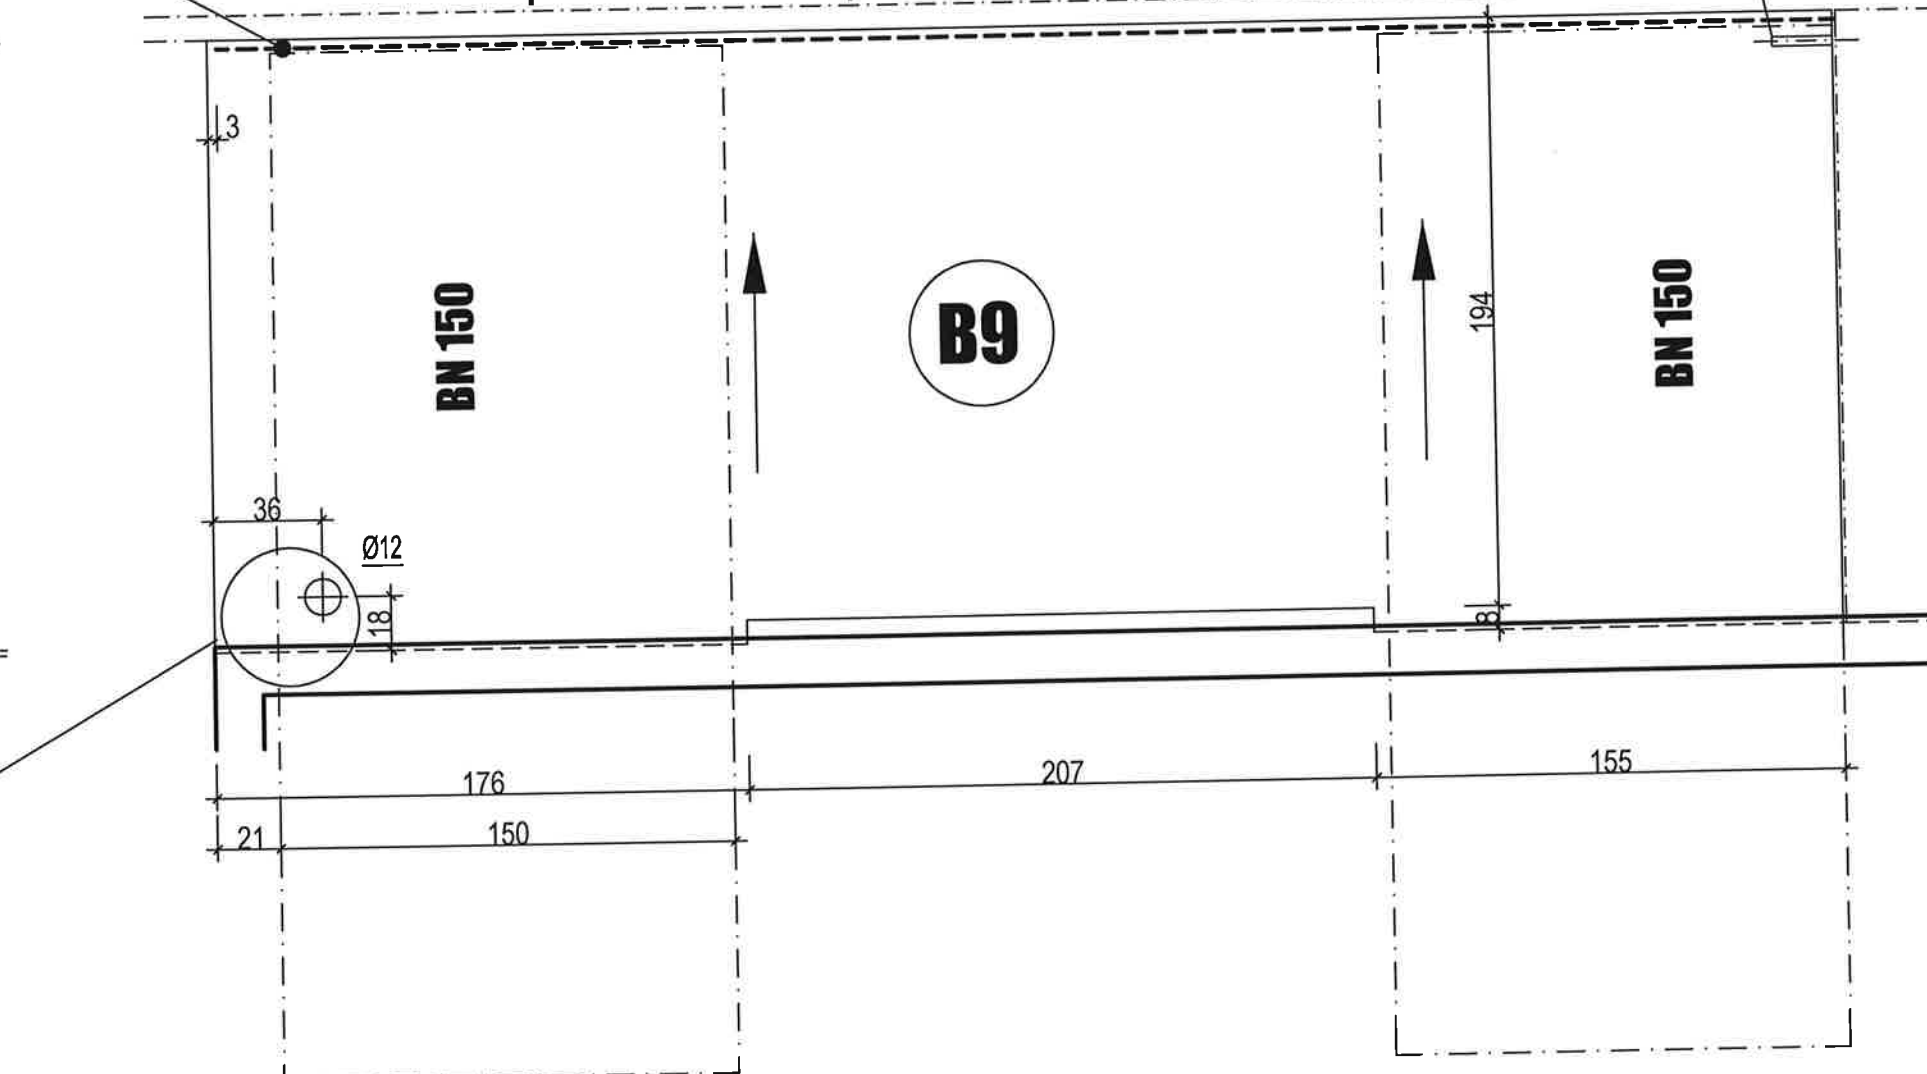**COUPE A**


Ech: 1/25

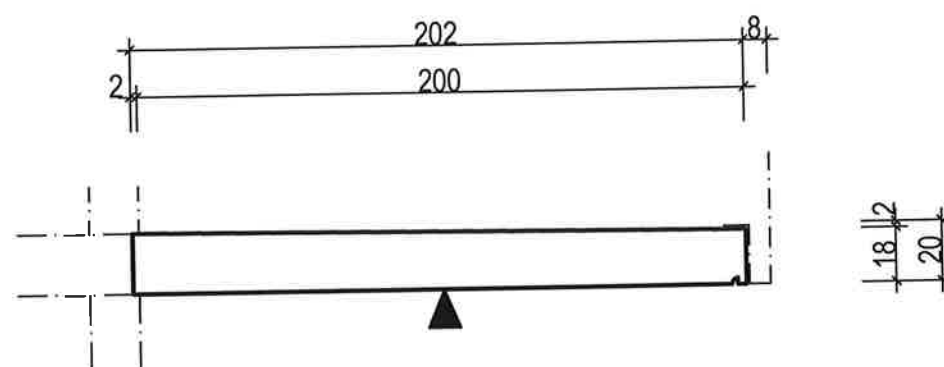**COUPE B**


Ech: 1/25

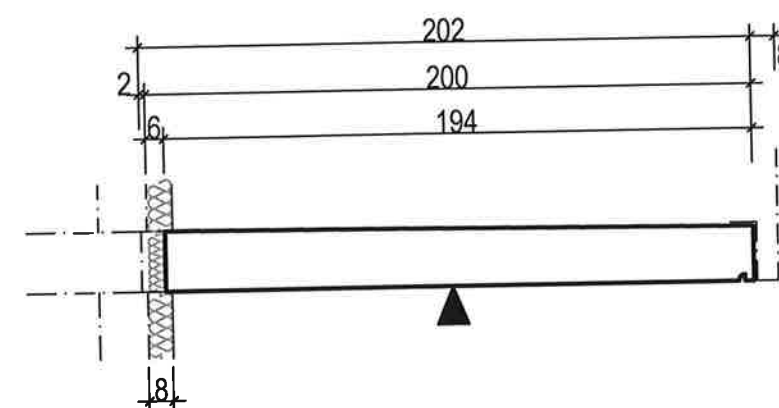


Poids: 2050 Kg

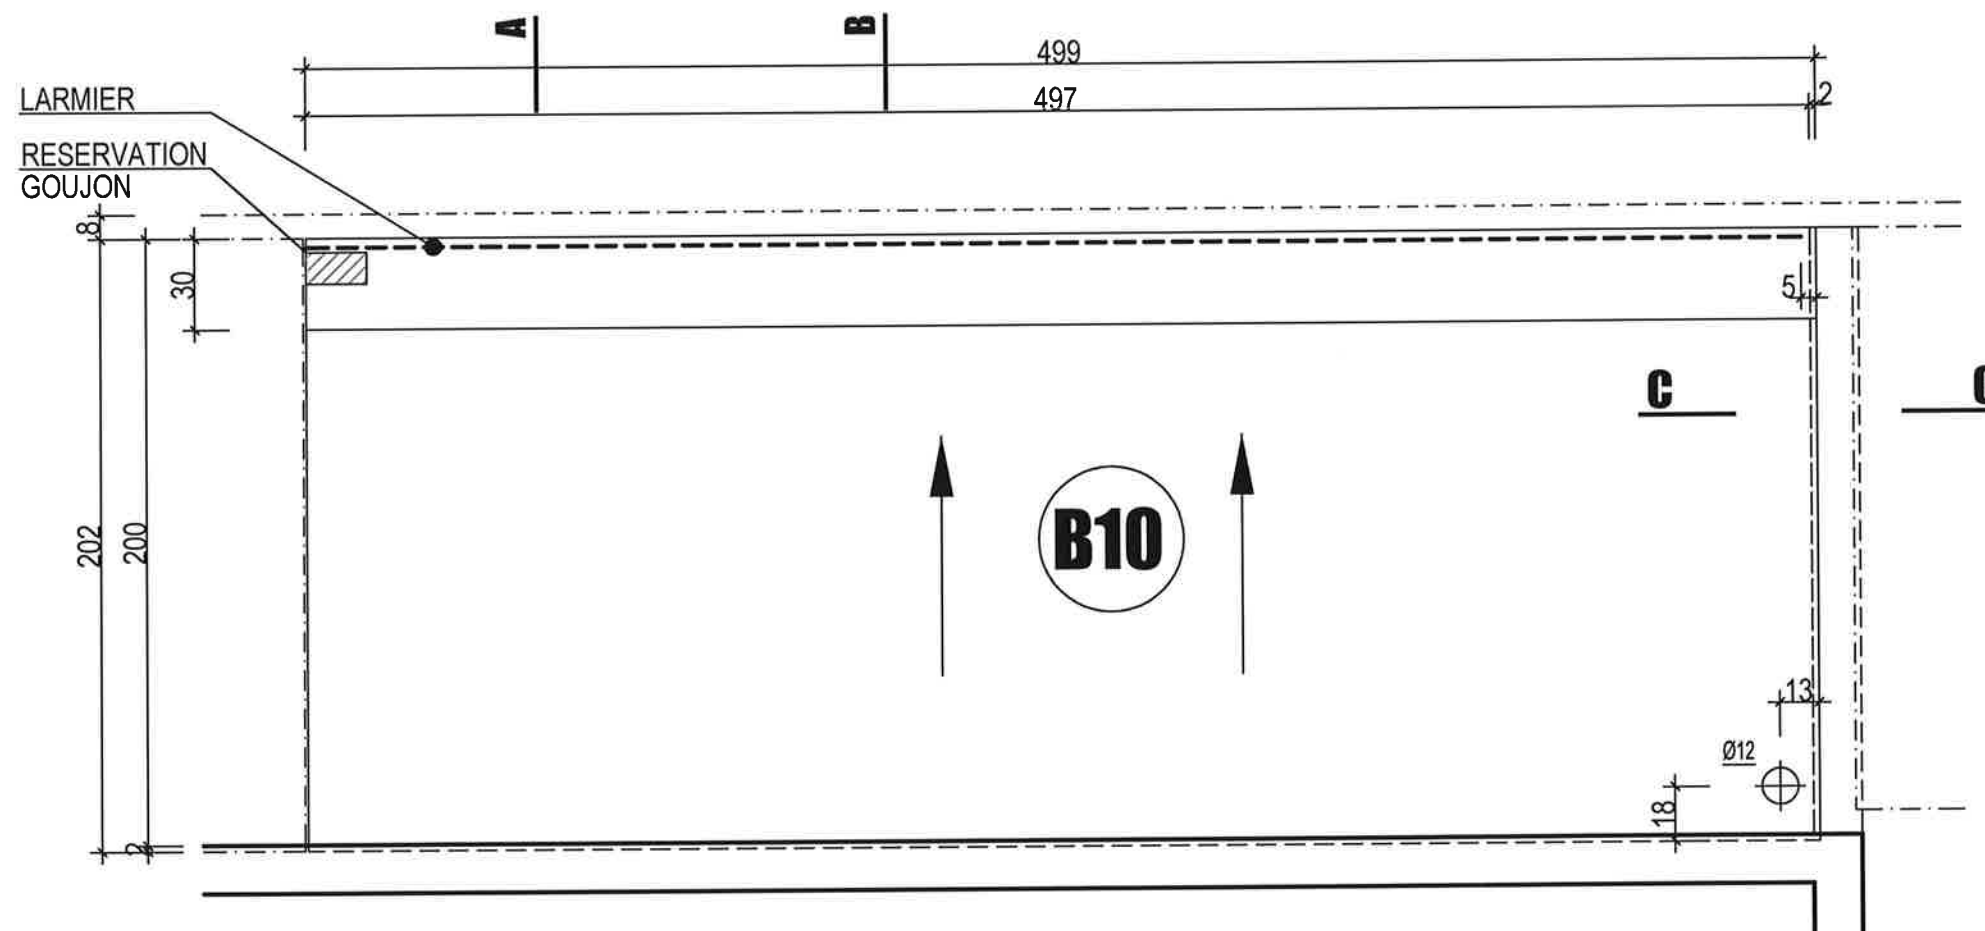

Ech: 1/25

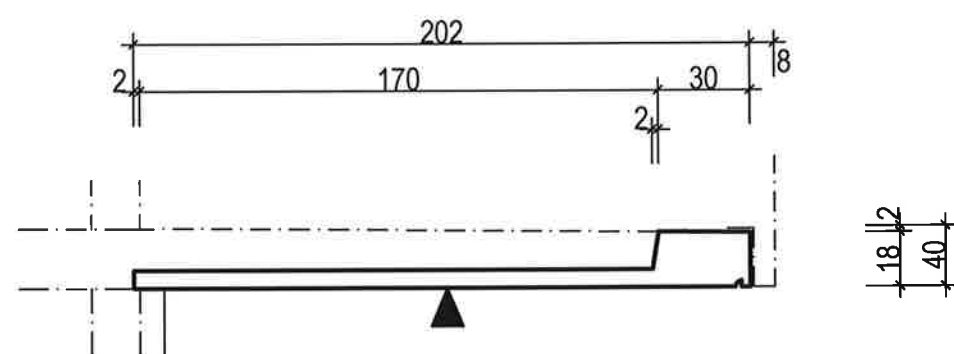


Ech: 1/10

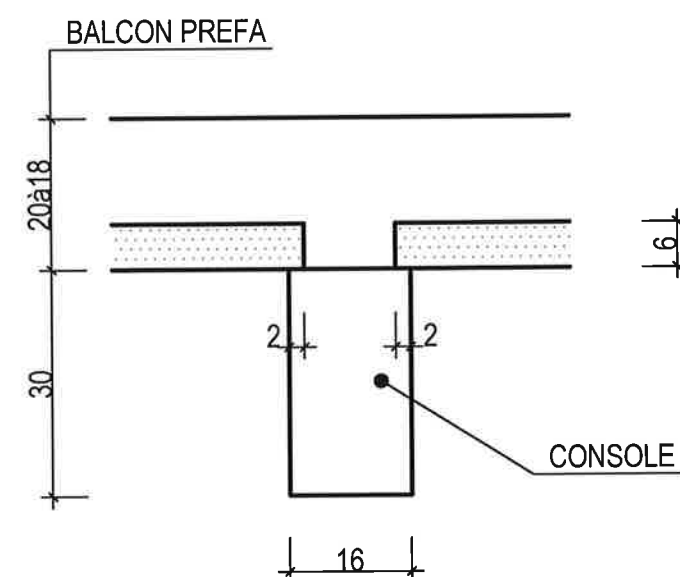


B10a 1 p

Poids: 1000 Kg

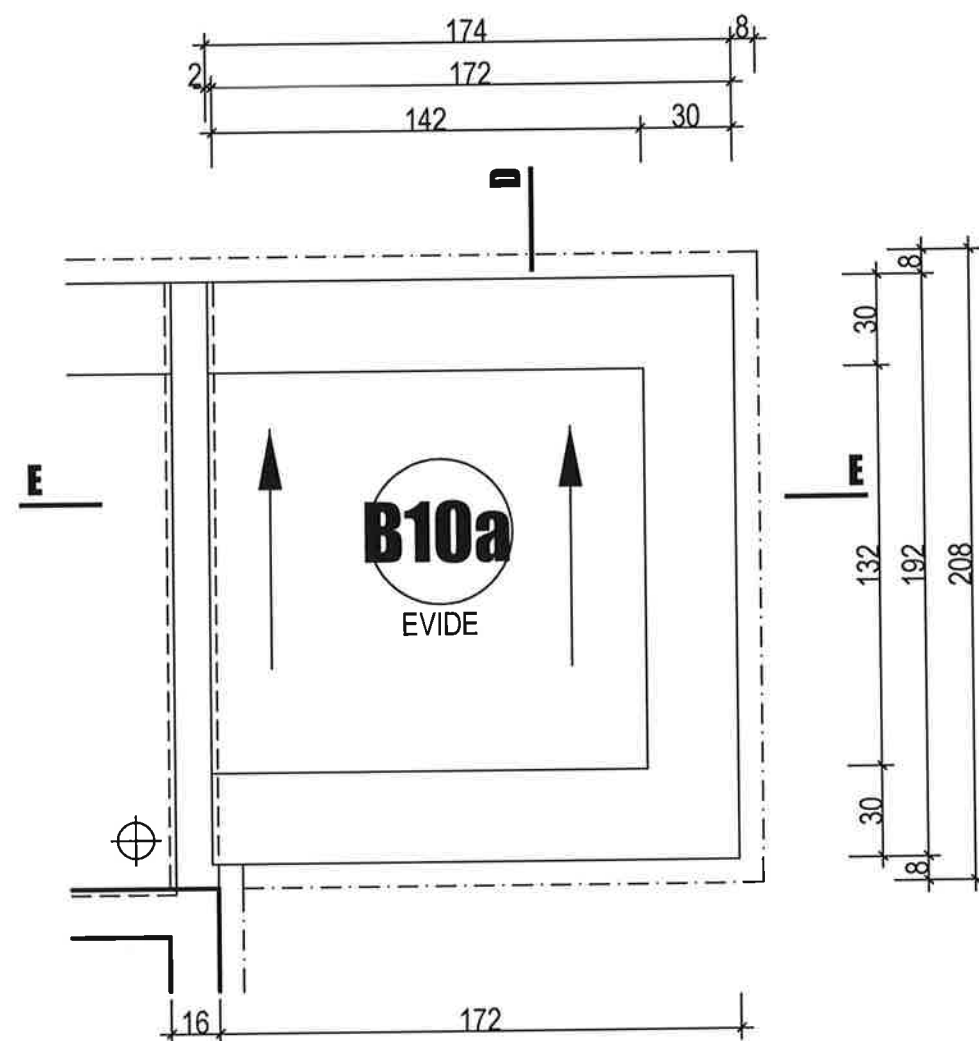


COUPE D

Ech: 1/25

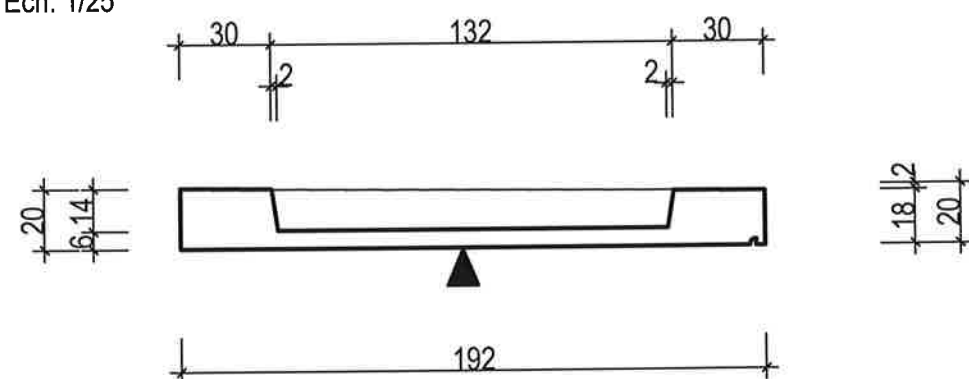

COUPE E


Ech: 1/25

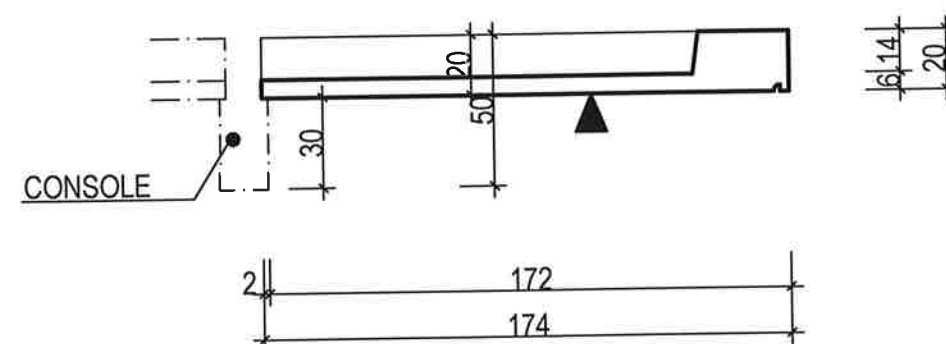

PLANCHER sur -1


Vue en plan

Ech: 1/50

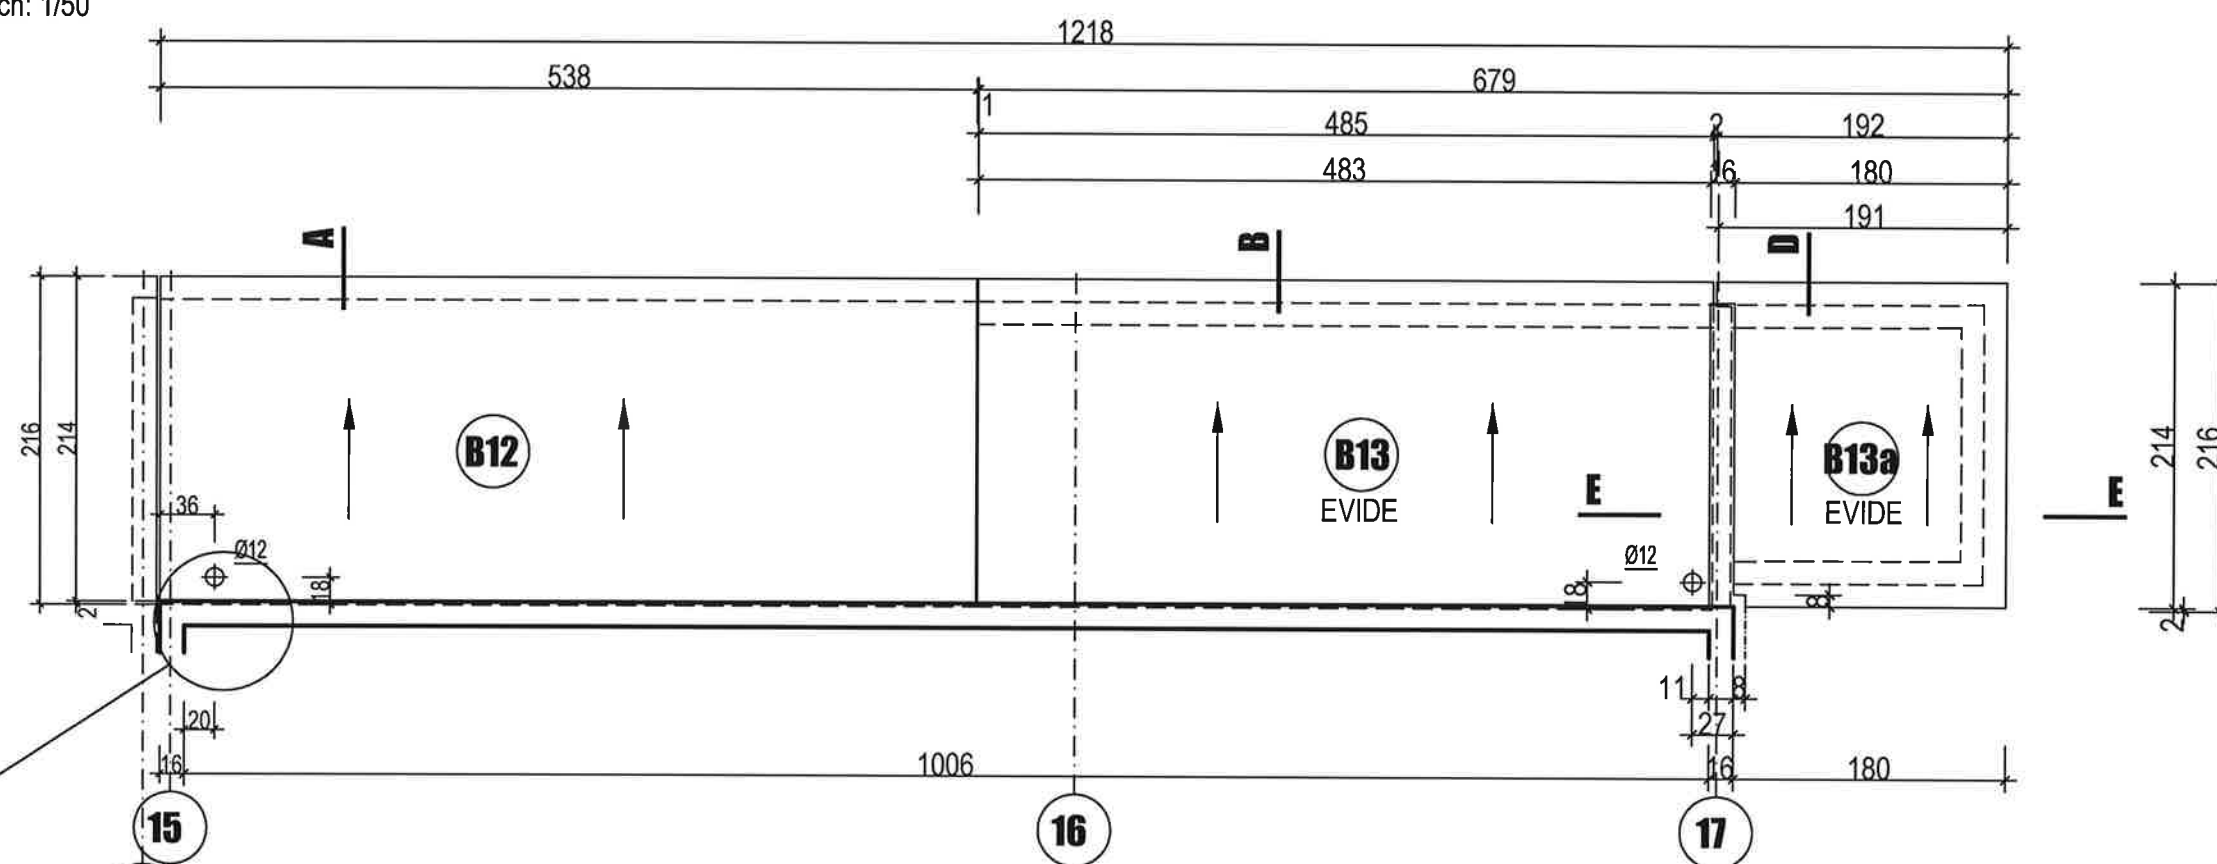


DETAIL

Ech: 1/10

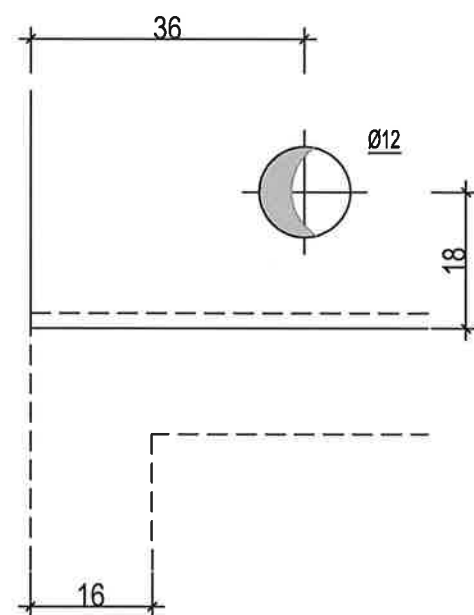

COUPE A

Ech: 1/25

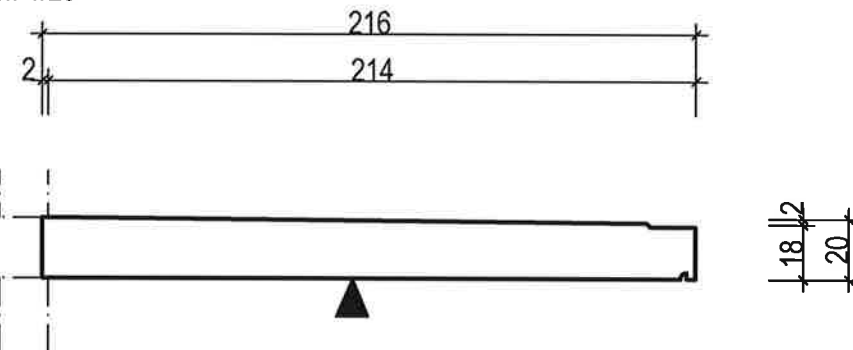

COUPE B

Ech: 1/25

