VUE EN PLAN
Ech: 1/50

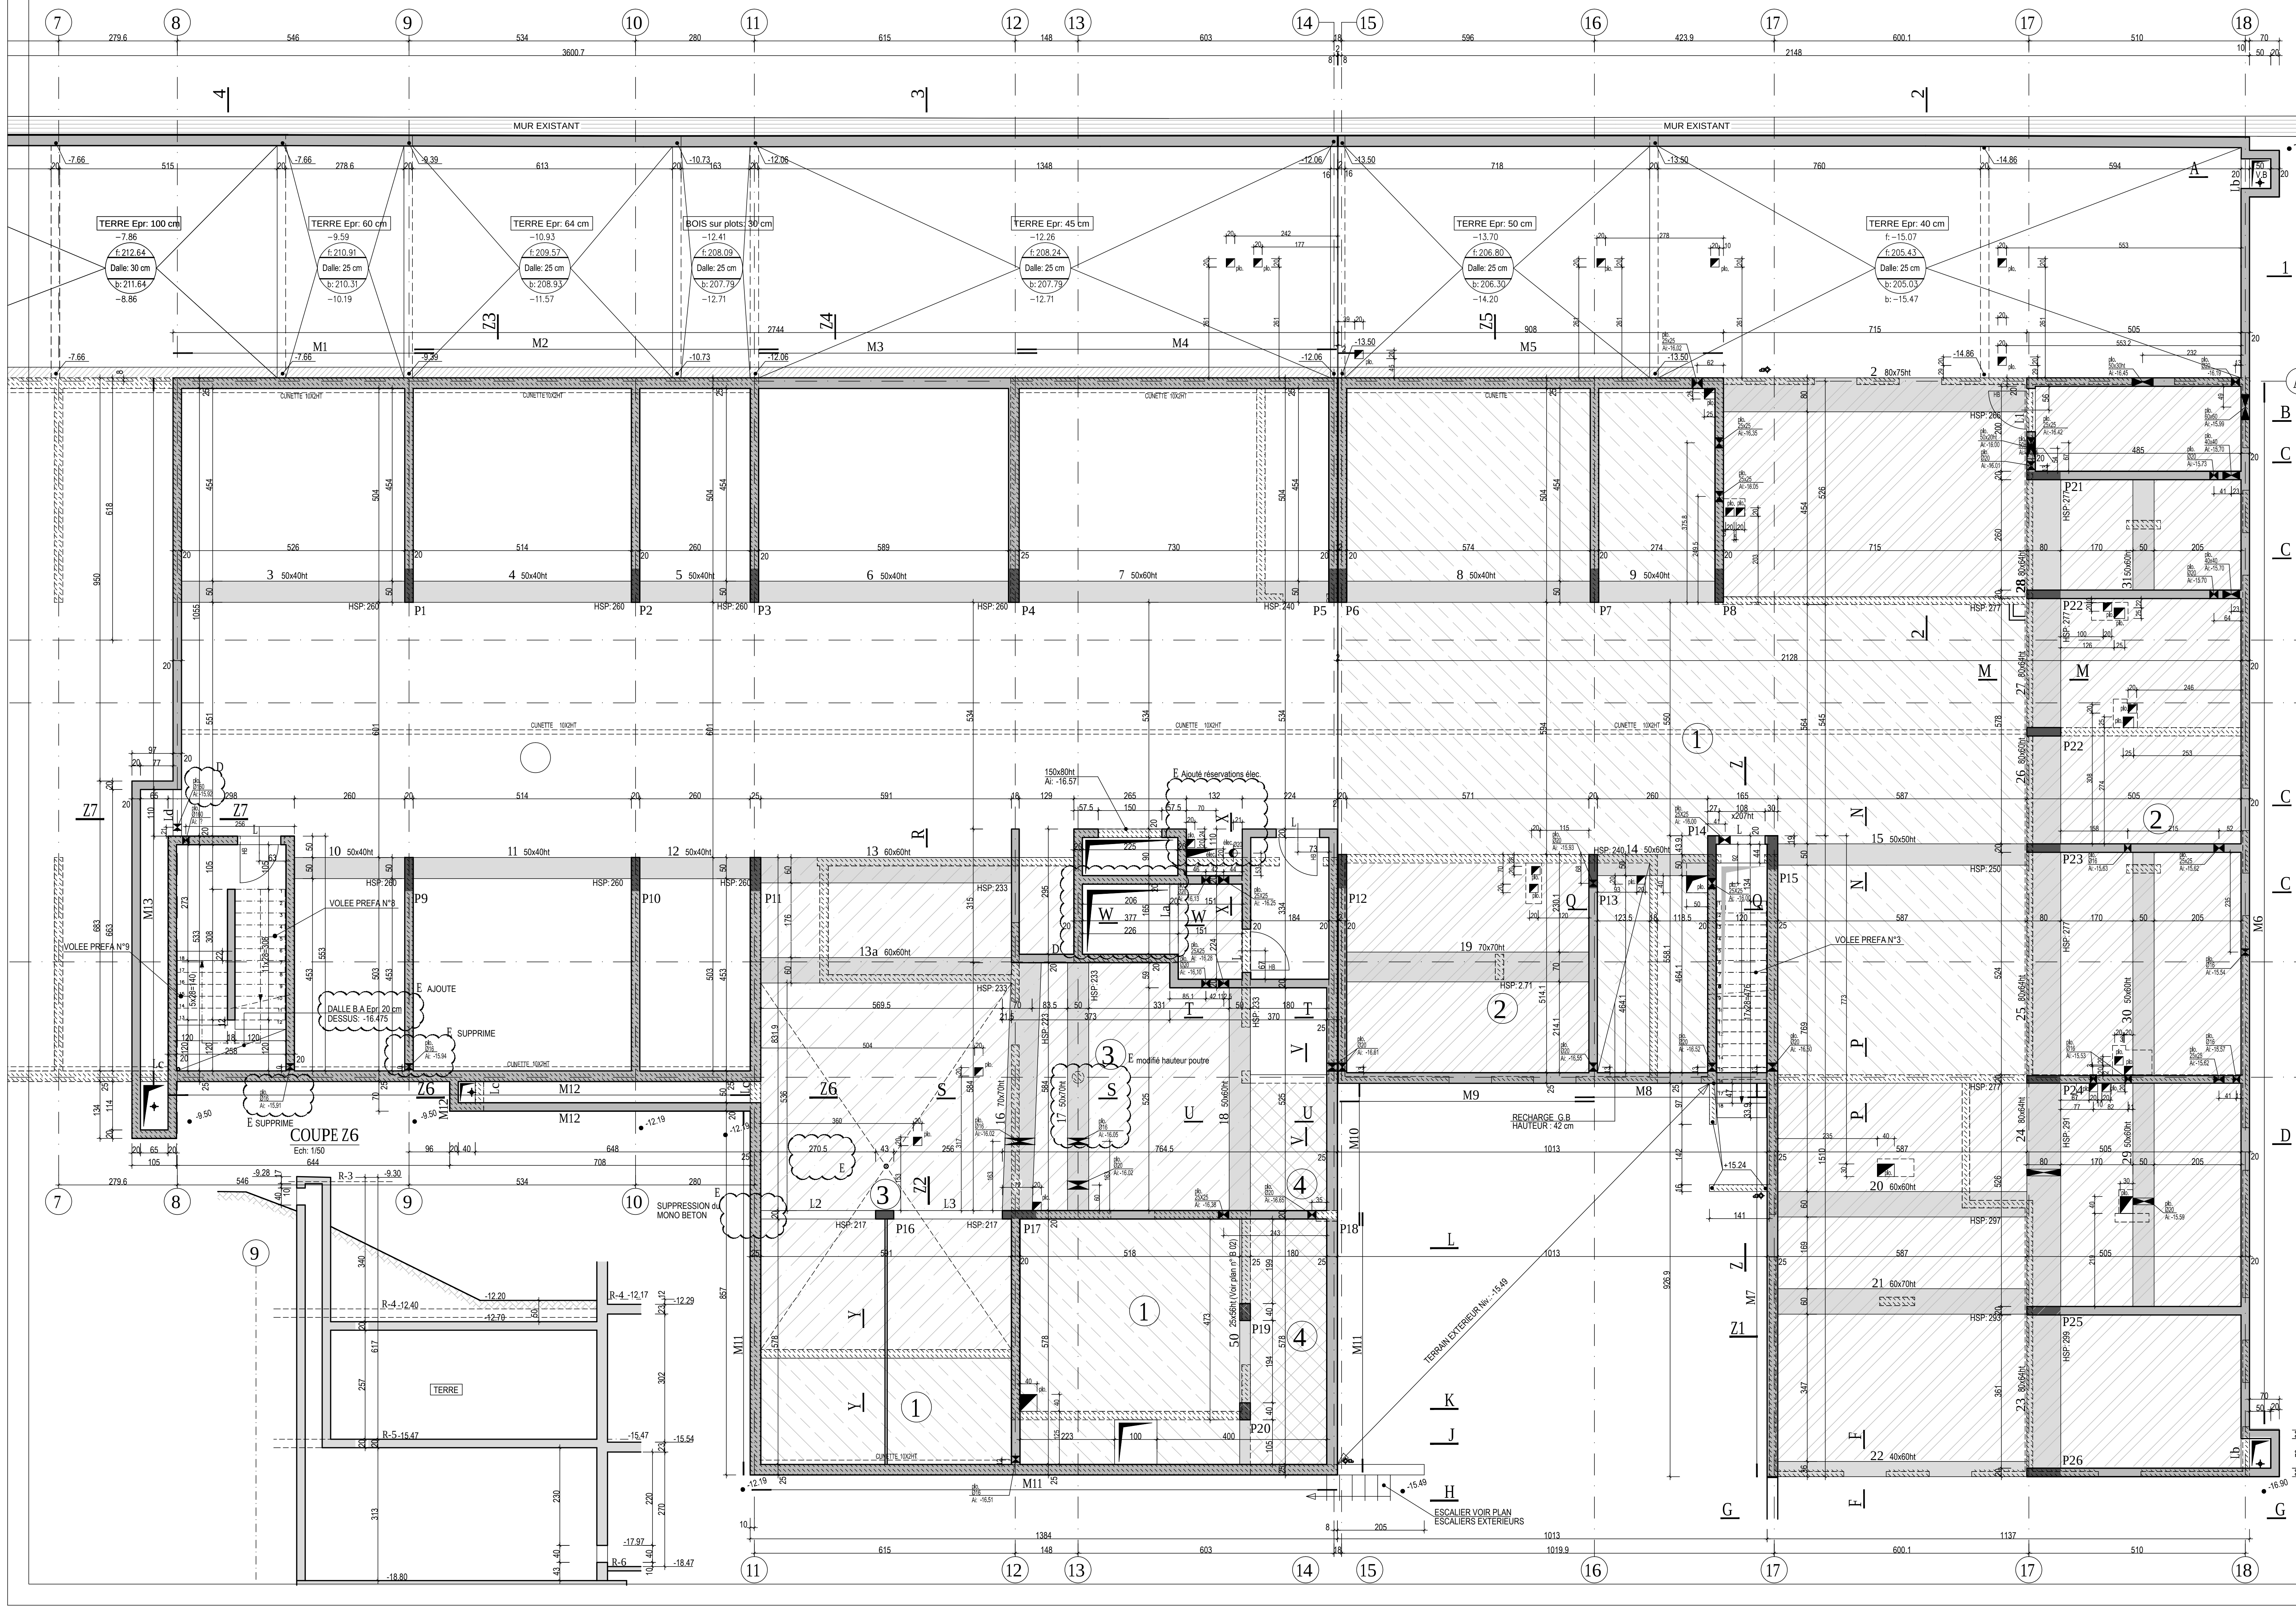
7
8
9
10
11
12
13
14
15
16
17
18
MUR EXISTANT
TERRE Epr: 100 cm
Dalle: 30 cm
TERRE Epr: 60 cm
TERRE Epr: 64 cm
BOIS sur plots: 30 cm
TERRE Epr: 45 cm
TERRE Epr: 50 cm
TERRE Epr: 40 cm
Dalle: 25 cm
M1
M2
M3
M4
M5
M6
M7
M8
M9
M10
M11
M12
M13
P1
P2
P3
P4
P5
P6
P7
P8
P9
P10
P11
P12
P13
P14
P15
P16
P17
P18
P19
P20
P21
P22
P23
P24
P25
P26
CUNETTE 10X2HT
VOLEE PREFA N°9
VOLEE PREFA N°8
VOLEE PREFA N°3
DALLE B.A Epr: 20 cm
DESSUS: -16.475
E AJOUTE
E SUPPRIME
E Ajouté réservations élec.
E modifié hauteur poutre
SUPPRESSION du MONO BETON
RECHARGE G.B
HAUTEUR : 42 cm
TERRAIN EXTERIEUR Niv.: -15.49
ESCALIER VOIR PLAN ESCALIERS EXTERIEURS
COUPE Z6
Ech: 1/50
TERRE
R-3
R-4
R-5
R-6

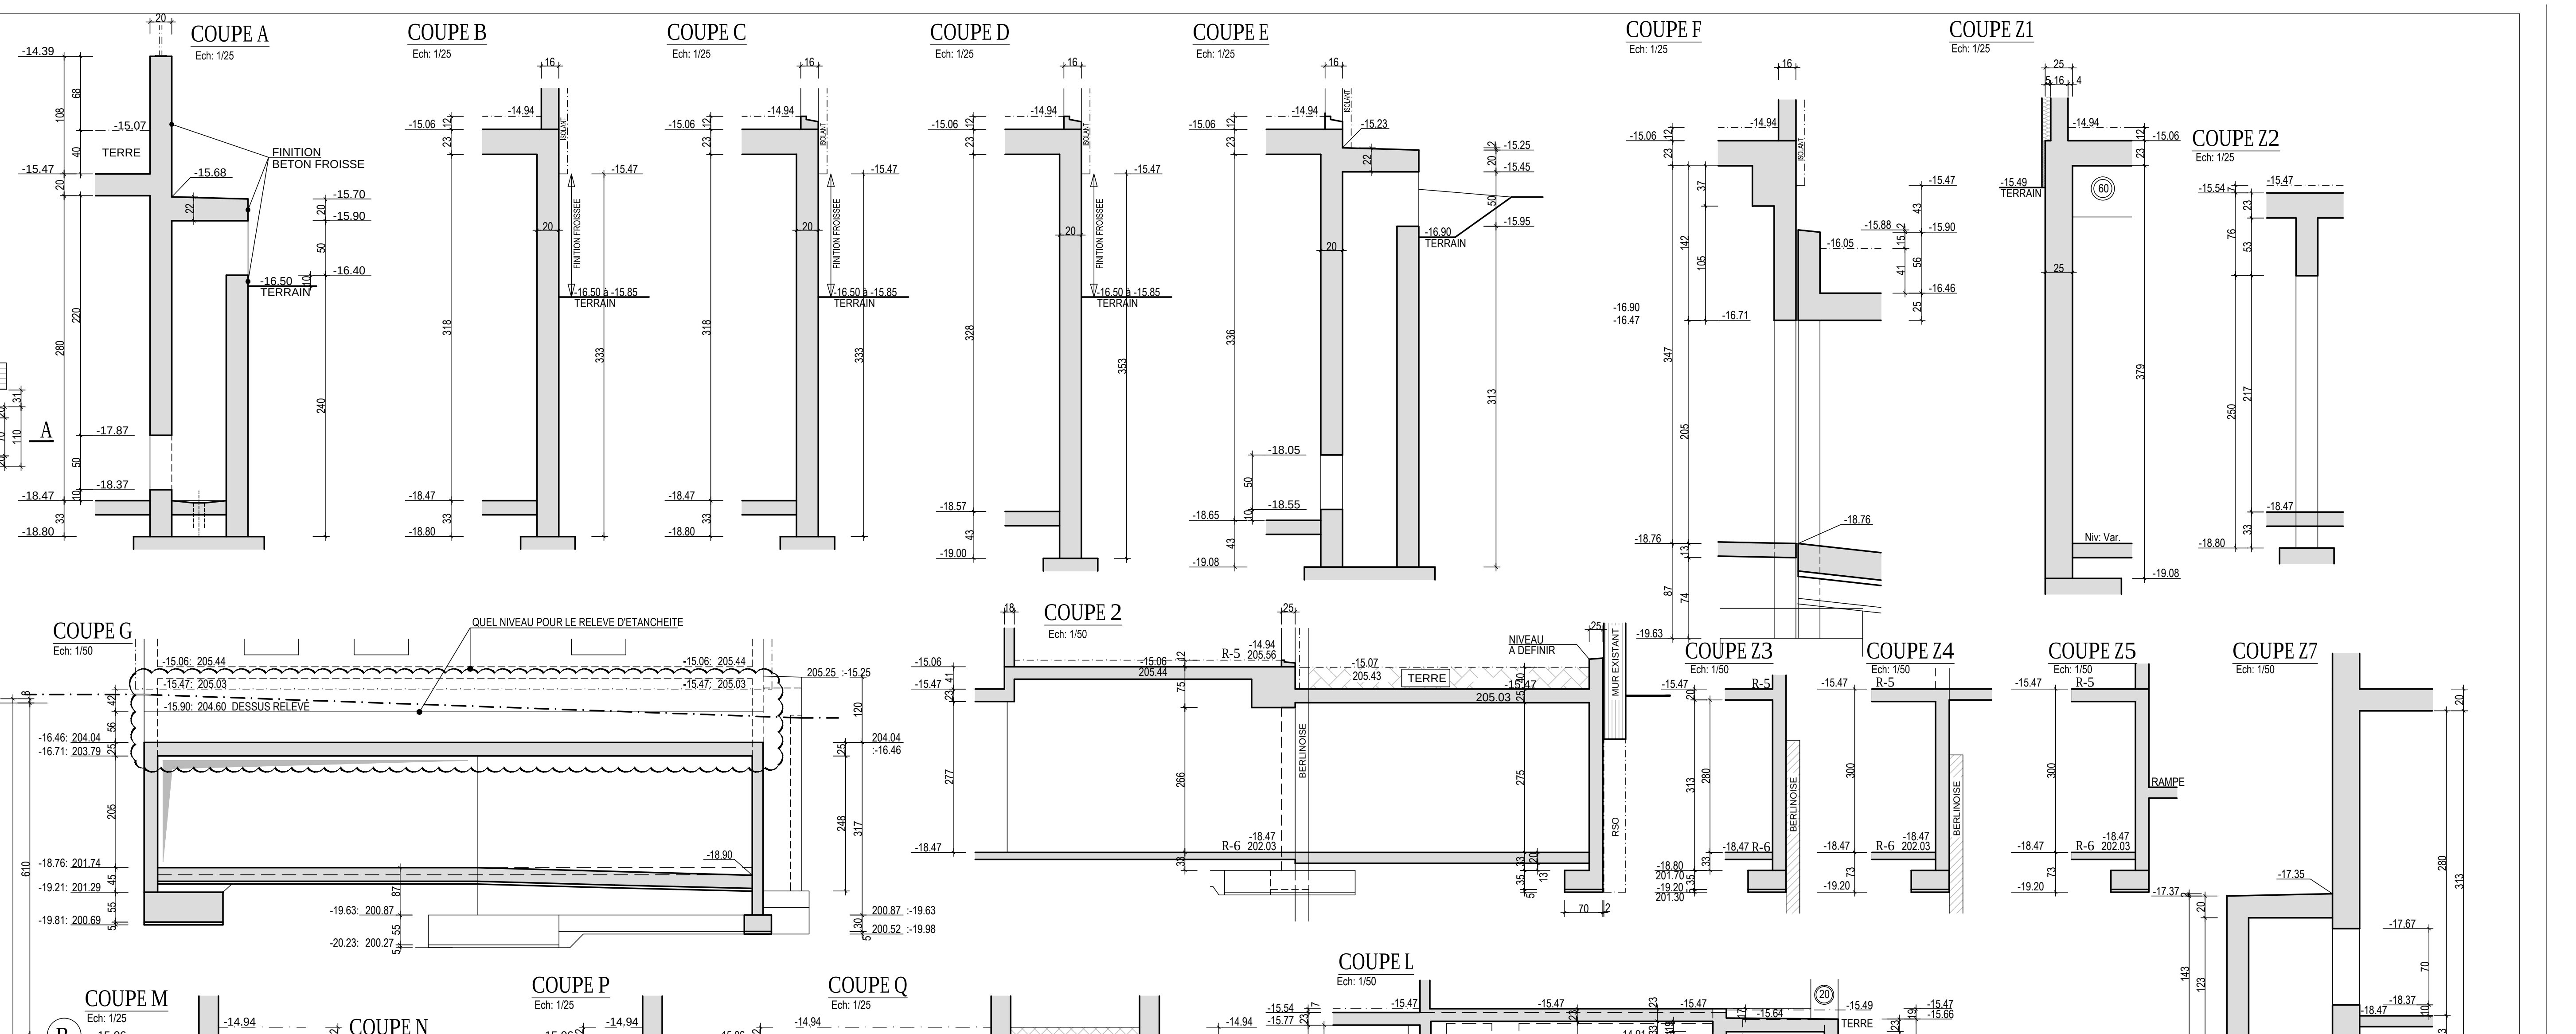
COUPE A
Ech: 1/25
TERRE
FINITION BETON FROISSE
TERRAIN
COUPE B
Ech: 1/25
COUPE C
Ech: 1/25
COUPE D
Ech: 1/25
COUPE E
Ech: 1/25
FINITION FROISSEE
ISOLANT
COUPE F
Ech: 1/25
COUPE Z1
Ech: 1/25
COUPE Z2
Ech: 1/25
COUPE G
Ech: 1/50
QUEL NIVEAU POUR LE RELEVE D'ETANCHEITE
DESSUS RELEVE
COUPE 2
Ech: 1/50
NIVEAU A DEFINIR
MUR EXISTANT
BERLINOISE
RSO
COUPE Z3
Ech: 1/50
COUPE Z4
Ech: 1/50
COUPE Z5
Ech: 1/50
RAMPE
COUPE Z7
Ech: 1/50

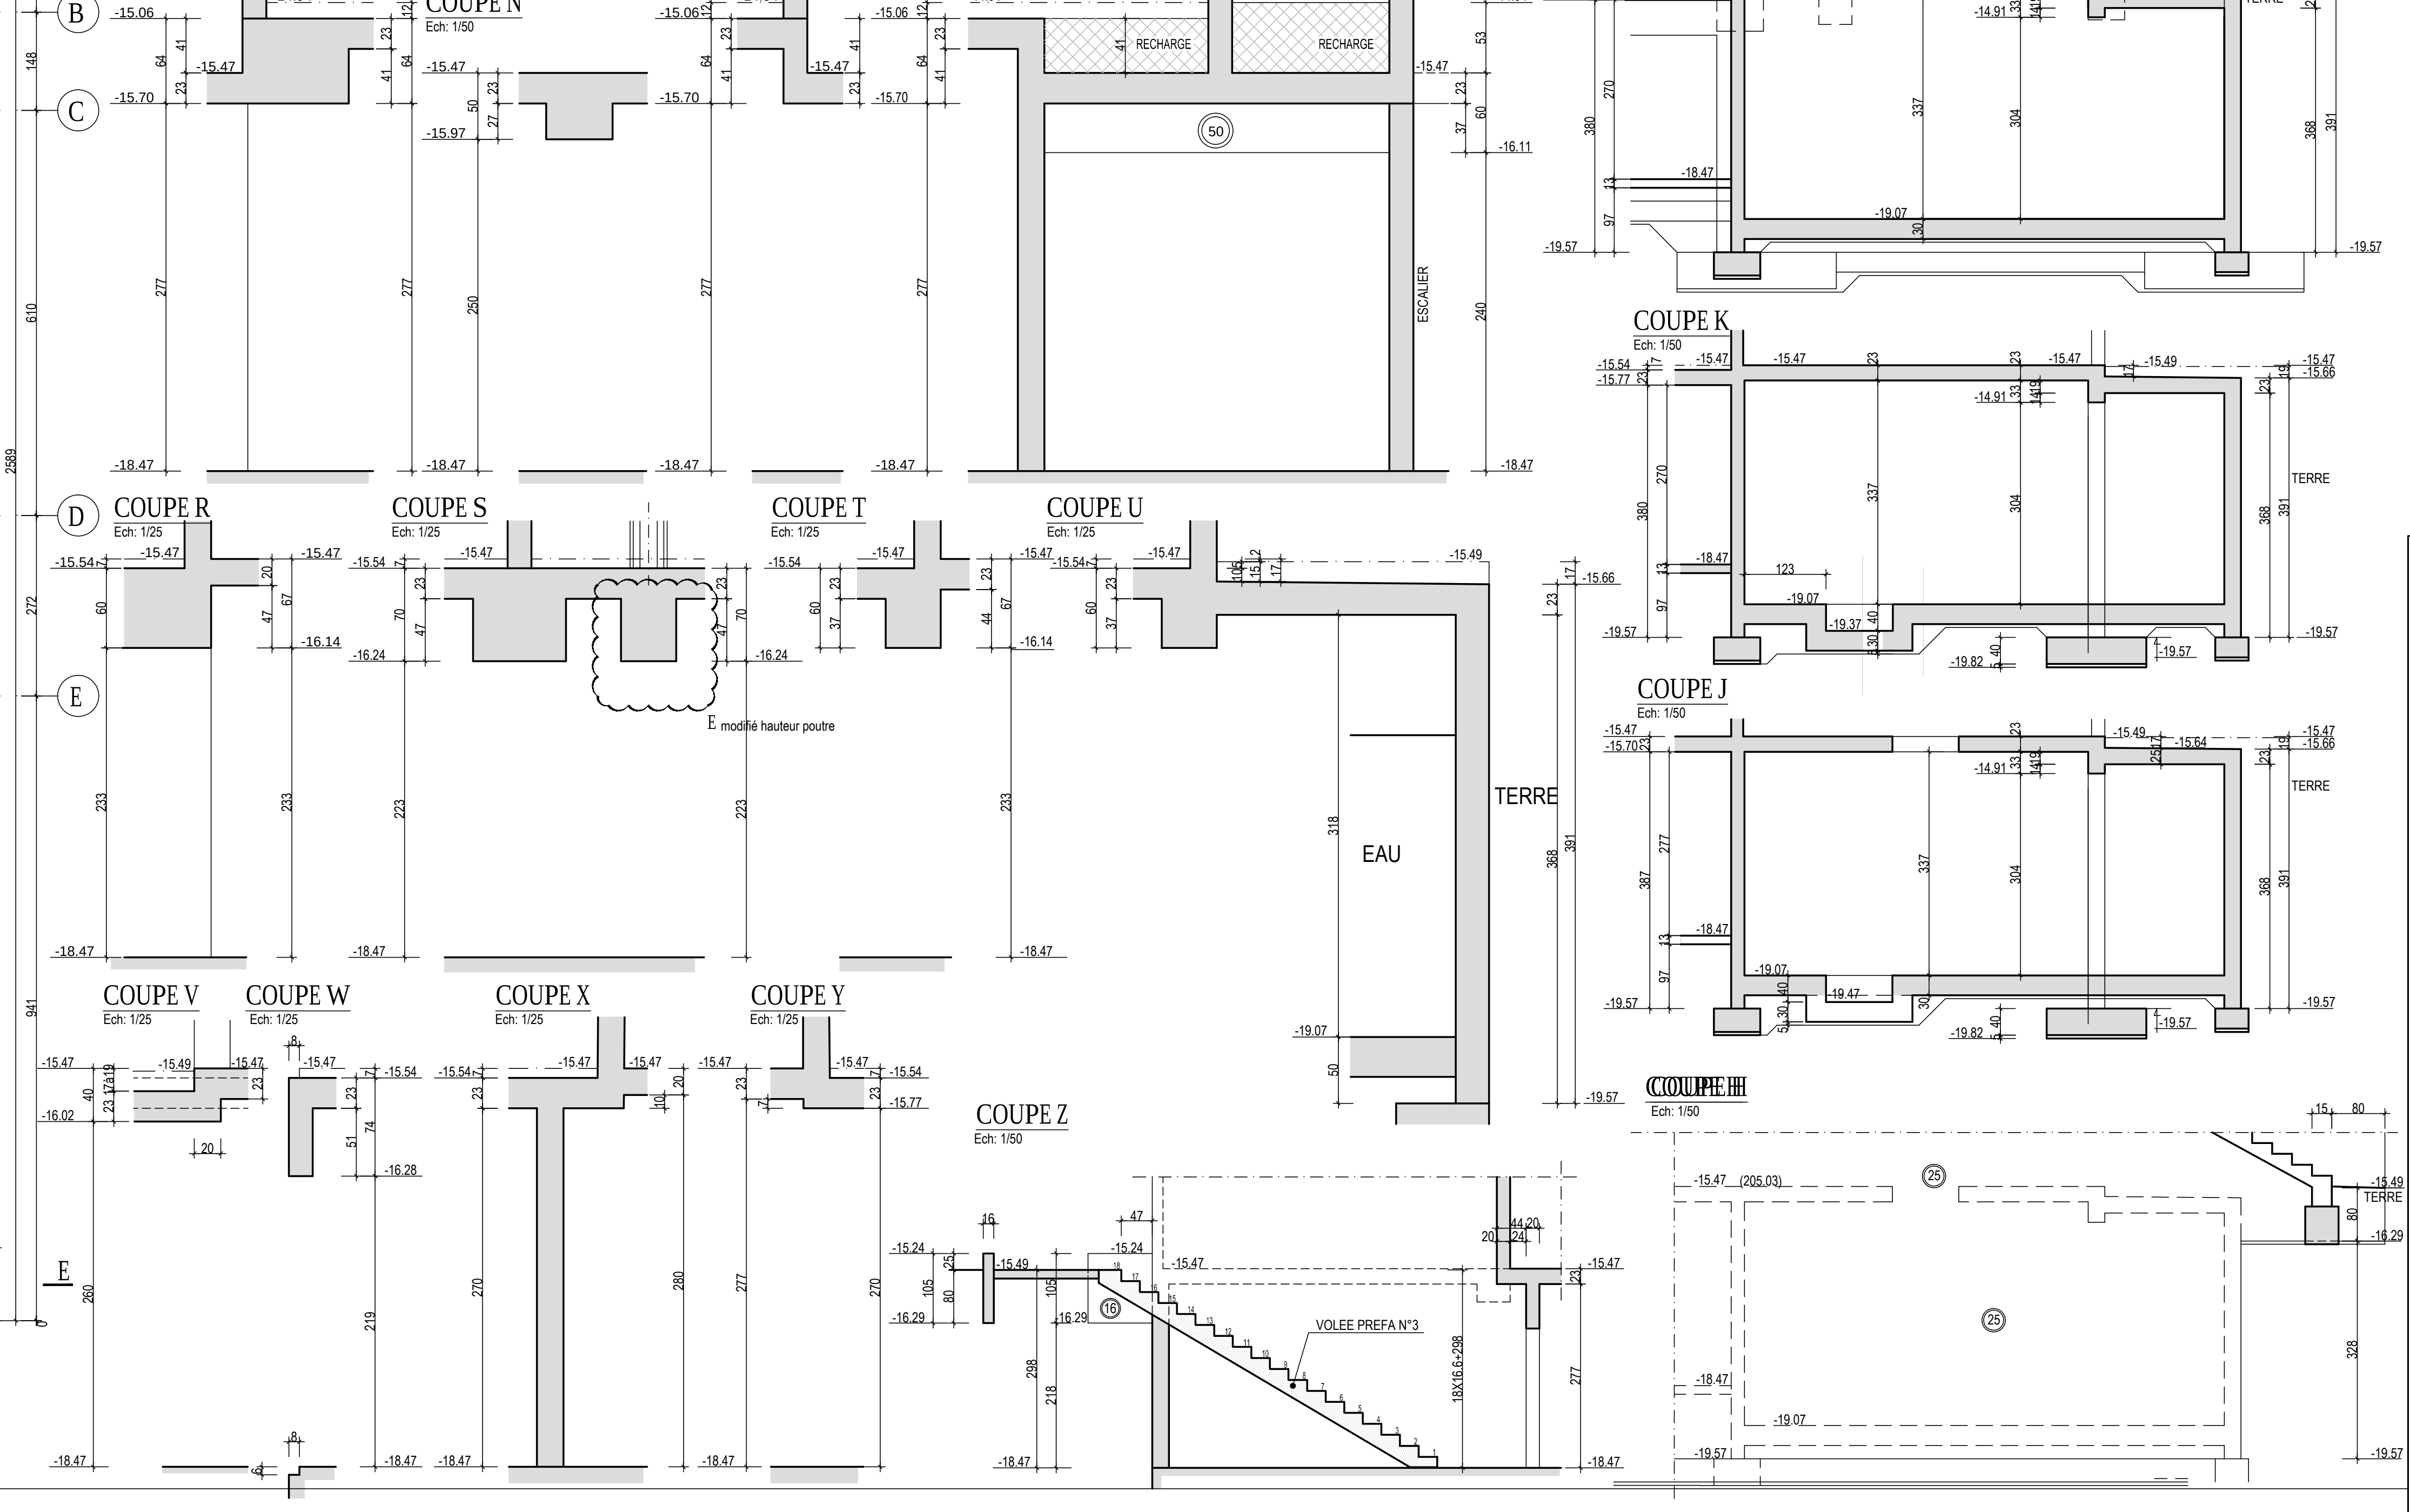
COUPE M
Ech: 1/25
COUPE N
Ech: 1/50
COUPE P
Ech: 1/25
COUPE Q
Ech: 1/25
RECHARGE
ESCALIER
COUPE L
Ech: 1/50
COUPE K
Ech: 1/50
COUPE J
Ech: 1/50
TERRE
COUPE R
Ech: 1/25
COUPE S
Ech: 1/25
E modifié hauteur poutre
COUPE T
Ech: 1/25
COUPE U
Ech: 1/25
EAU
TERRE
COUPE V
Ech: 1/25
COUPE W
Ech: 1/25
COUPE X
Ech: 1/25
COUPE Y
Ech: 1/25
COUPE Z
Ech: 1/50
VOLEE PREFA N°3
COUPE H
Ech: 1/50

DALLES

○ FINI: -15.47=205.03 DALLE BA Epr: 20 cm DESSUS BRUT:-15.47 RESERVE: 0 cm	① FINI: -15.47=205.03 DALLE BA Epr: 23 cm DESSUS BRUT:-15.47 RESERVE: 0 cm
② FINI: -14.94=205.56 DALLE BA Epr: 23 cm DESSUS BRUT:-15.06 RESERVE: 12 cm	③ FINI: -15.47=205.03 DALLE BA Epr: 23 cm DESSUS BRUT:-15.54 RESERVE: 7 cm
④ FINI: -15.49=205.01 DALLE BA Epr: 25 à 23 cm DESSUS BRUT:-15.64=204.86 à -15.66=204.84 RESERVE: 15 à 17 cm (BETON DESACTIVE +PENTE)	

COUPES 1 à 5 VOIR PLAN DE LA RAMPE

NOAHO

Chemin de Fontanière - 69350 La Mulatière

Création de logements

Les entreprises réalisant les travaux devront tenir compte des derniers plans architecte lors de la réalisation des travaux
Les plans du be MATTE ne doivent servir qu'au corps d'état concerné et doivent être des plans d'exécution.

ARCHITECTE(S): ATELIER DE LA PASSERELLE
BET STRUCTURE: MATTE SAS
BET FLUIDES: PRELEM
ECONOMISTE: EXECO
BUREAU DE CONTROLE: Bureau VERITAS
MO DELEGUE:
MOE: PSO Ingénierie
CSPS: SUD EST COORDINATION
OPC:
ENTREPRISE(S): Fontanel-pbc

Bât: B
PLANCHER sur -6
Coffrage

EXE

Contrainte de sol: 8 bars ELS
Aciers HA (T) FeE500
Aciers Doux (Ø) FeE 235
Aciers TS FeE 500
Béton fc28 >= 25MPa
Enrobage = 3 cm

INDICE	DATE	MODIFICATIONS
A	30/09/2015	MISE A JOUR V.B ,AJOUTE REPERAGE MURS
B	07/10/2015	AJOUTE RESERVATIONS
C	09/10/2015	MISE A JOUR COUPE V.B
D	15/10/2015	MODIFIE fosse ascenseur et réservations suivant D
E	19/10/2015	Ajouté réservations élec., modifié hauteur poutre 17

PLAN N°
B07 E
DATE : 25/09/2015

MATTÉ
BUREAU D'ÉTUDES
STRUCTURES ET FLUIDES
119 BOULEVARD STALINGRAD 69100 VILLEURBANNE
Tél. 04 72 44 02 87 Fax 04 72 44 26 59
E-mail : bet@matte.fr

Dessiné par : J.BO
Contrôlé par : P.LIN
Echelle : 1/50°

Affaire N°
13.12.119