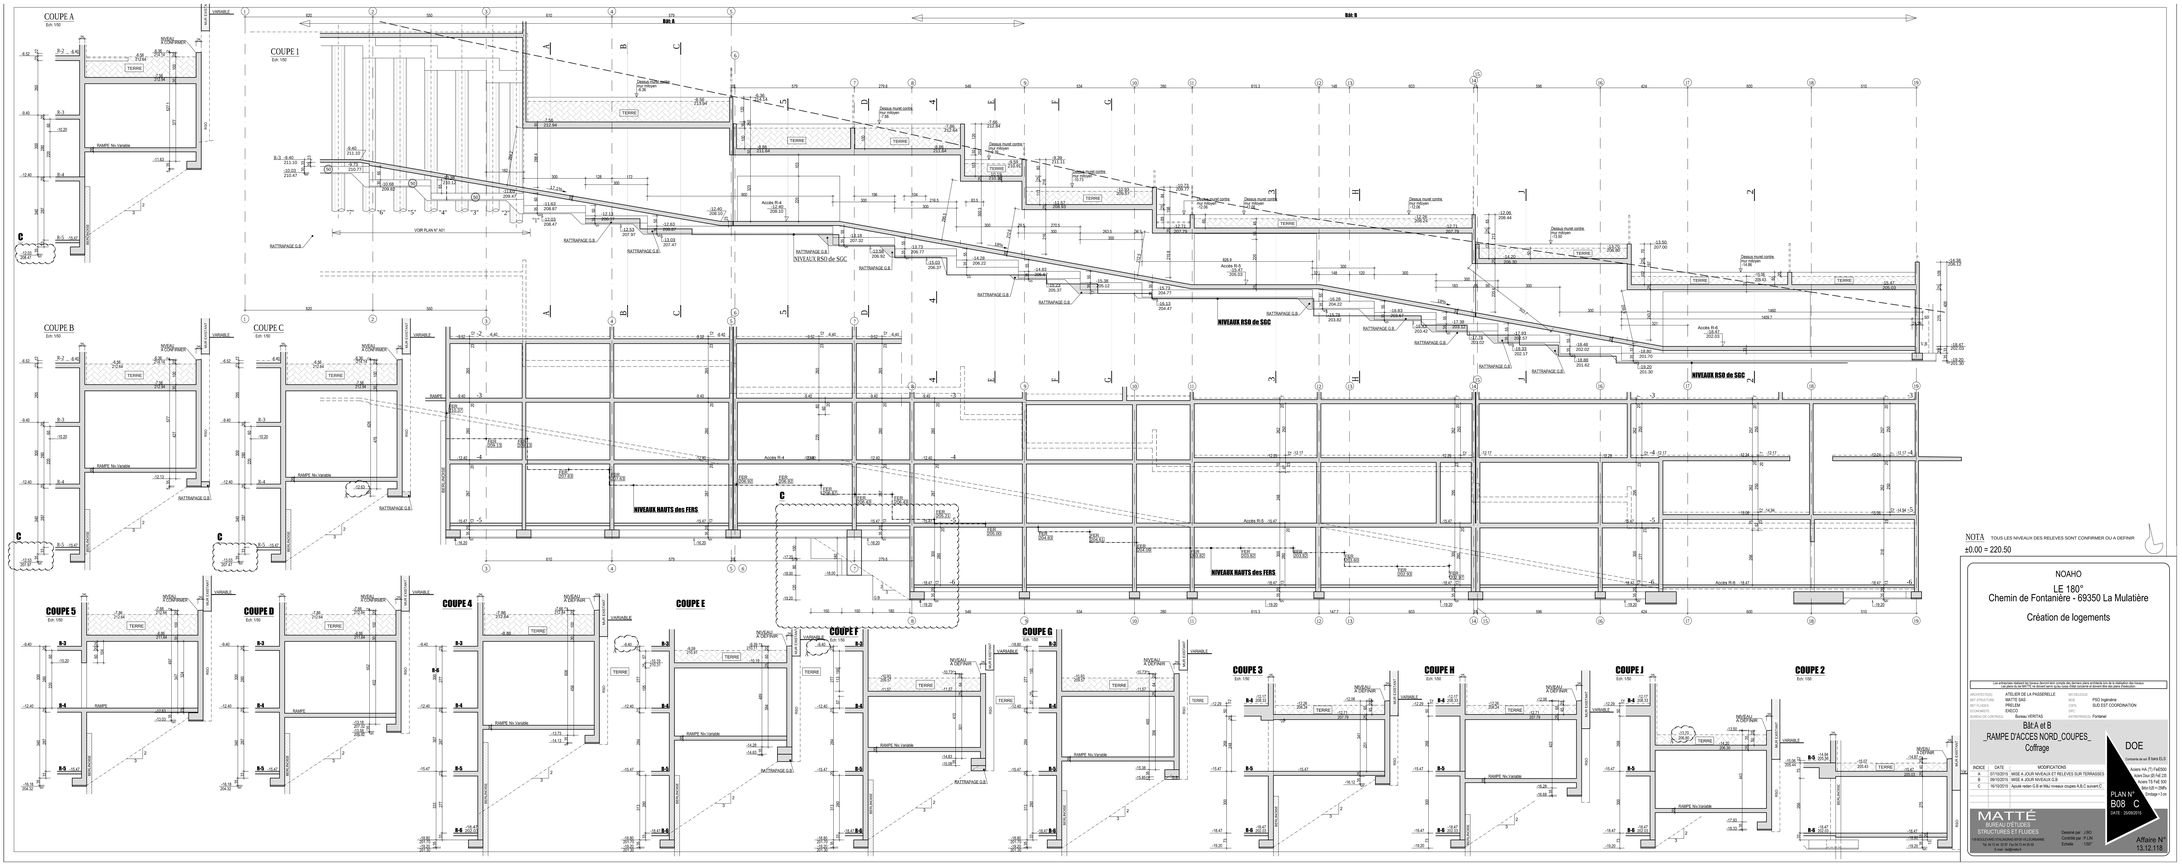

COUPE A
Ech: 1/50
COUPE 1
Ech: 1/50
Bât: A
Bât: B
COUPE B
Ech: 1/50
COUPE C
Ech: 1/50
COUPE 5
Ech: 1/50
COUPE D
Ech: 1/50
COUPE 4
COUPE E
COUPE F
Ech: 1/50
COUPE G
Ech: 1/50
COUPE 3
Ech: 1/50
COUPE H
Ech: 1/50
COUPE J
Ech: 1/50
COUPE 2
Ech: 1/50
NIVEAU A CONFIRMER
NIVEAU A DEFINIR
MUR EXISTANT
VARIABLE
TERRE
RAMPE Niv.Variable
RAMPE
RSO
BERLINOISE
RATTRAPAGE G.B
NIVEAUX RSO de SGC
NIVEAUX HAUTS des FERS
Dessus muret contre mur mitoyen
Accès R-4
Accès R-5
Accès R-6
VOIR PLAN N° A01
17.1%
18%
FER
V.B
R-2
R-3
R-4
R-5
R-6
C

NOTA TOUS LES NIVEAUX DES RELEVES SONT CONFIRMER OU A DEFINIR

±0.00 = 220.50

NOAHO

LE 180°
Chemin de Fontanière - 69350 La Mulatière

Création de logements

Les entreprises réalisant les travaux devront tenir compte des derniers plans architecte lors de la réalisation des travaux
Les plans du be MATTE ne doivent servir qu'au corps d'état concerné et doivent être des plans d'exécution.

ARCHITECTE(S):	ATELIER DE LA PASSERELLE	MO DELEGUE:	
BET STRUCTURE:	MATTE SAS	MOE:	PSO Ingénierie
BET FLUIDES:	PRELEM	CSPS:	SUD EST COORDINATION
ECONOMISTE:	EXECO	OPC:	
BUREAU DE CONTROLE:	Bureau VERITAS	ENTREPRISE(S):	Fontanel

Bât:A et B
_RAMPE D'ACCES NORD_COUPES_
Coffrage

DOE

Contrainte de sol: 8 bars ELS

Aciers HA (T) FeE500
Aciers Doux (Ø) FeE 235
Aciers TS FeE 500
Béton fc28 >= 25MPa
Enrobage = 3 cm

INDICE	DATE	MODIFICATIONS
A	07/10/2015	MISE A JOUR NIVEAUX ET RELEVES SUR TERRASSES
B	09/10/2015	MISE A JOUR NIVEAUX G.B
C	16/10/2015	Ajouté redan G.B et MàJ niveaux coupes A,B,C suivant C

PLAN N°
B08 C
DATE : 25/09/2015

MATTÉ
BUREAU D'ÉTUDES
STRUCTURES ET FLUIDES
119 BOULEVARD STALINGRAD 69100 VILLEURBANNE
Tél. 04 72 44 02 87 Fax 04 72 44 26 59
E-mail : bet@matte.fr

Dessiné par : J.BO
Contrôlé par : P.LIN
Echelle : 1/50°

Affaire N°
13.12.118