
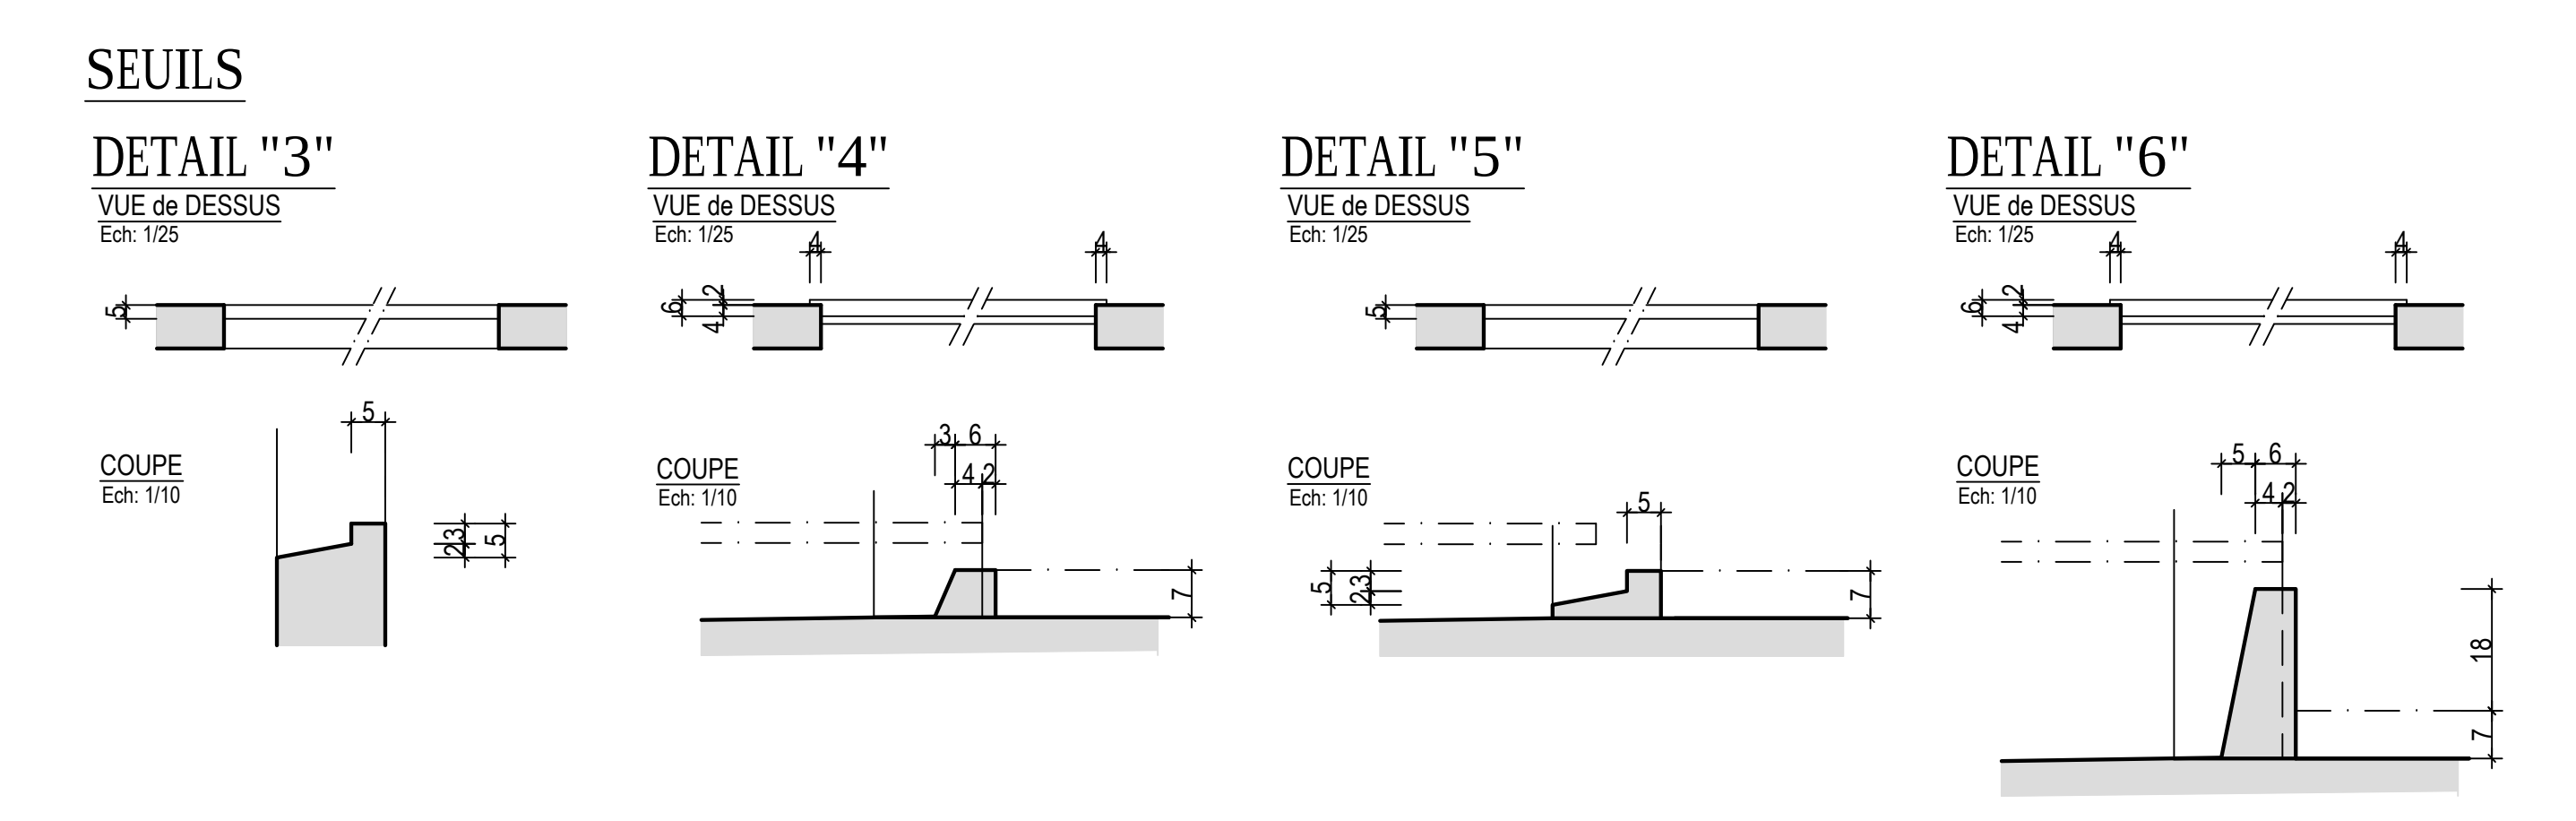
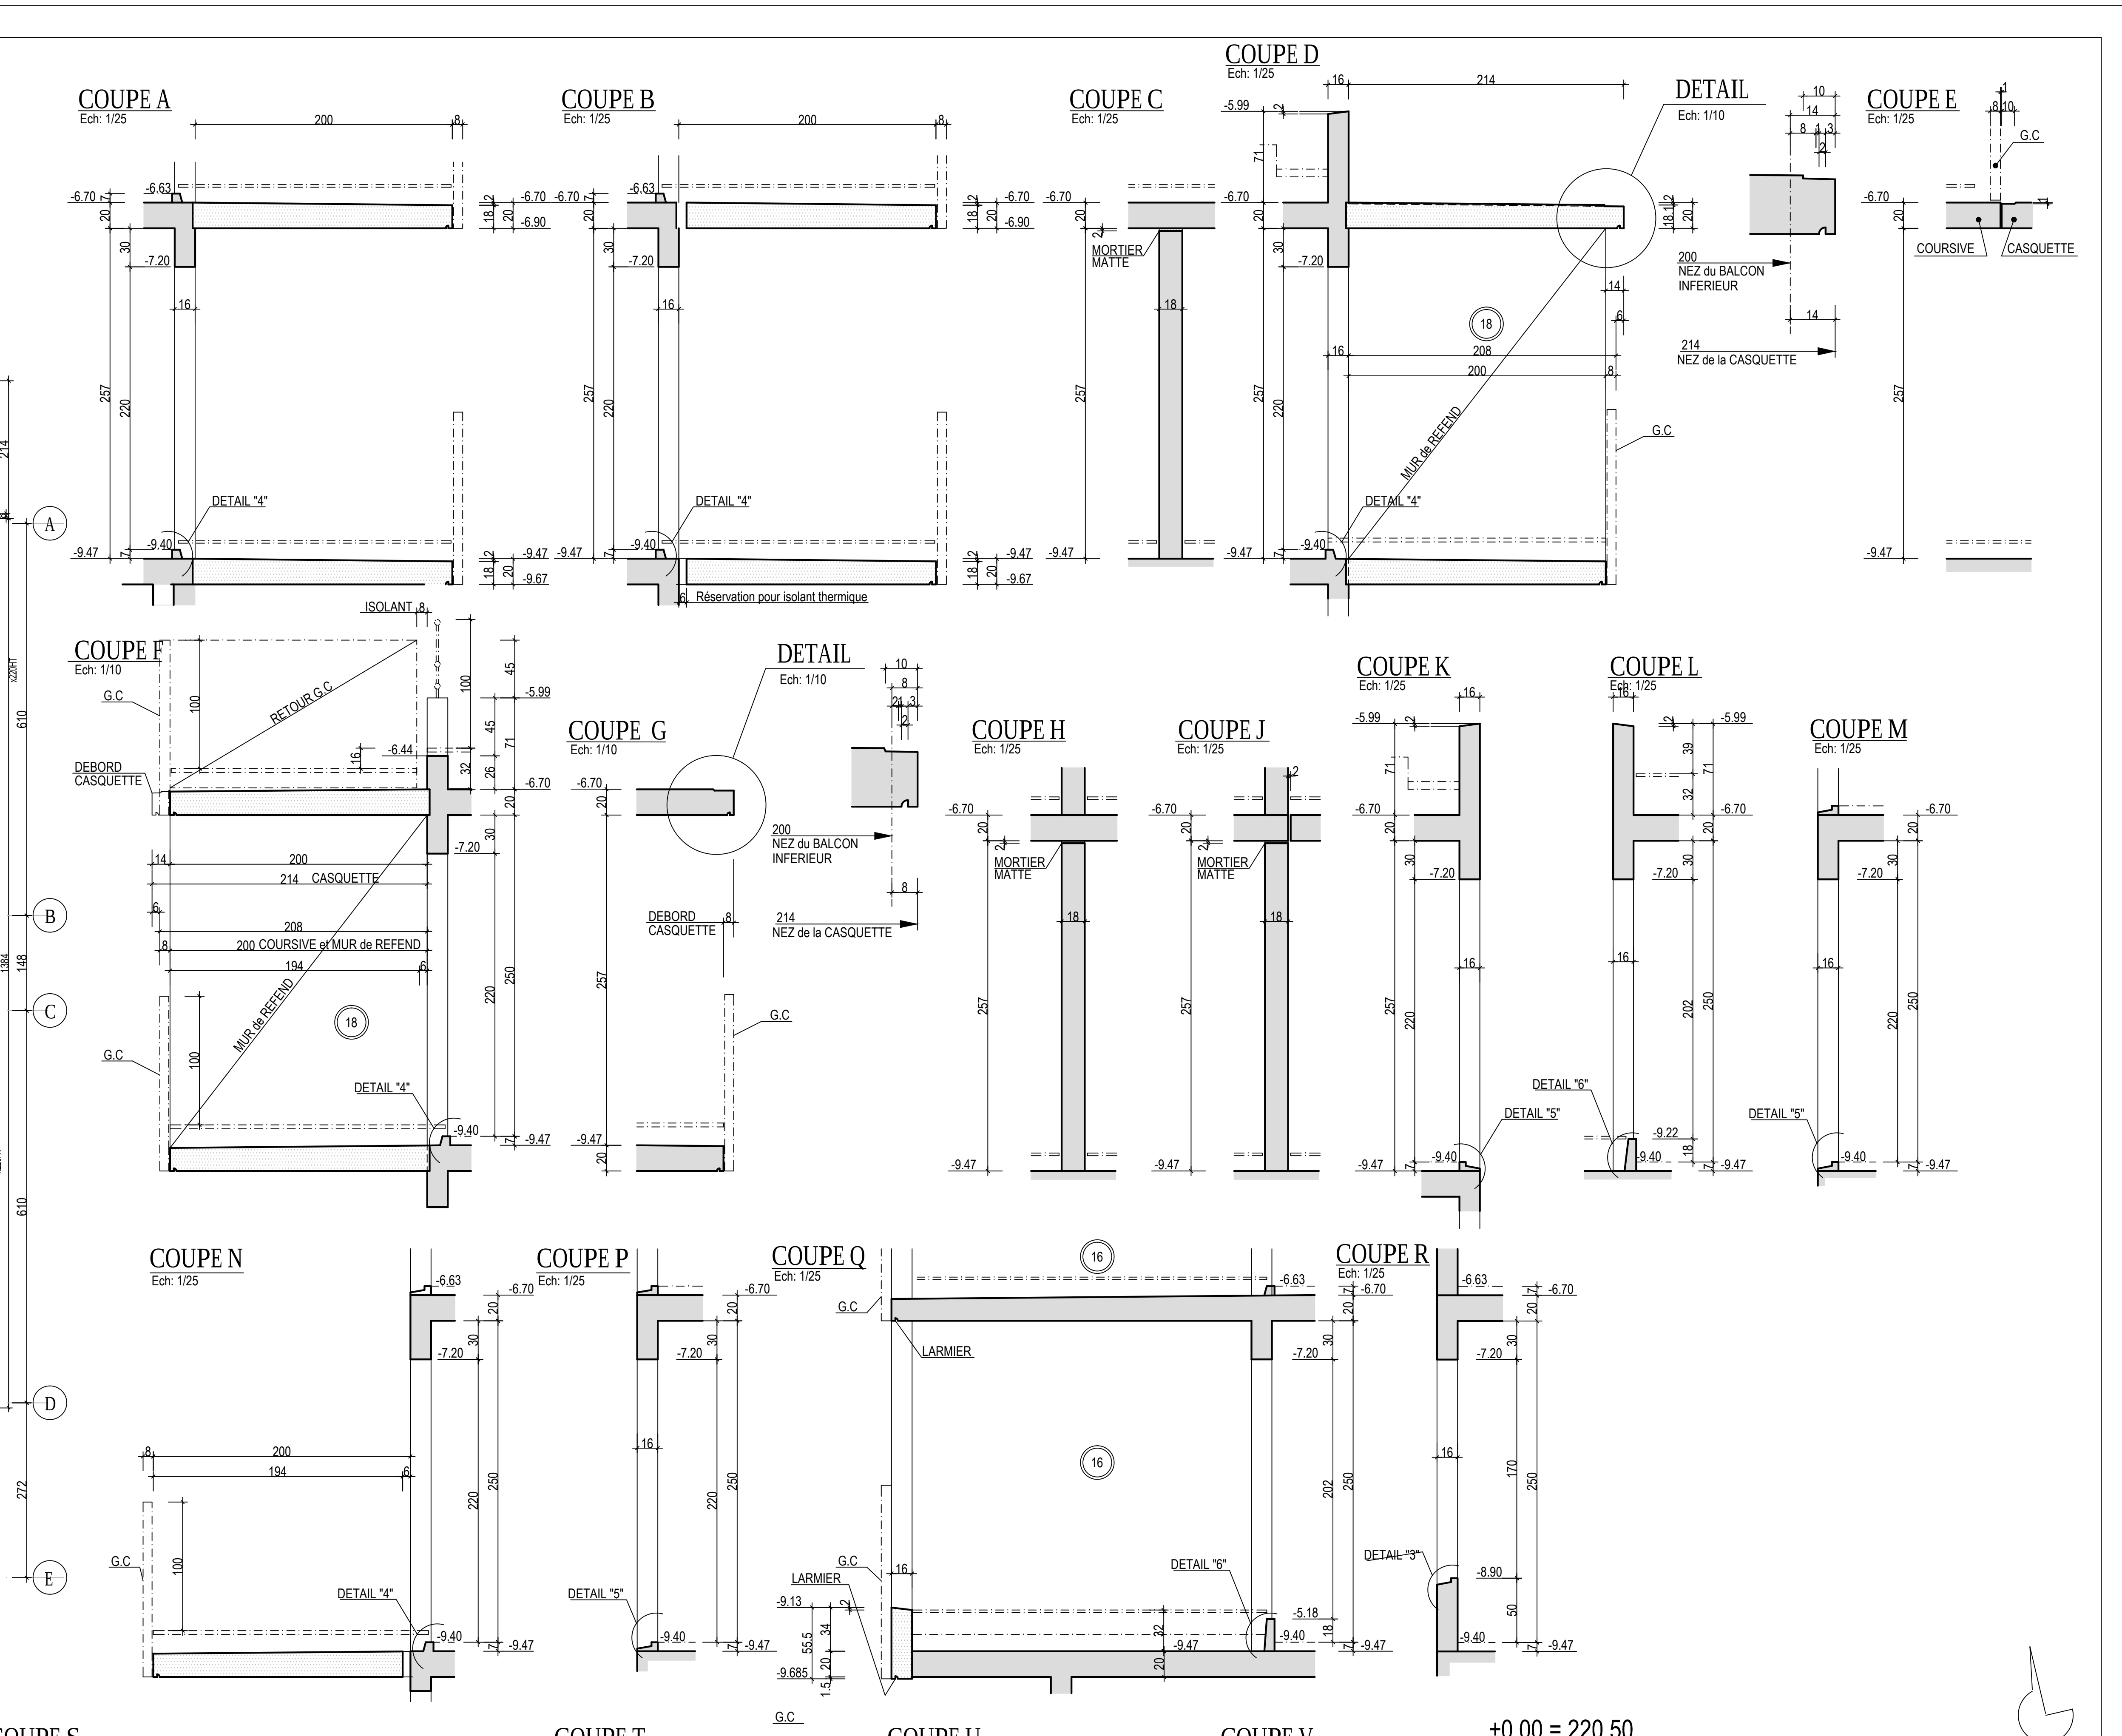


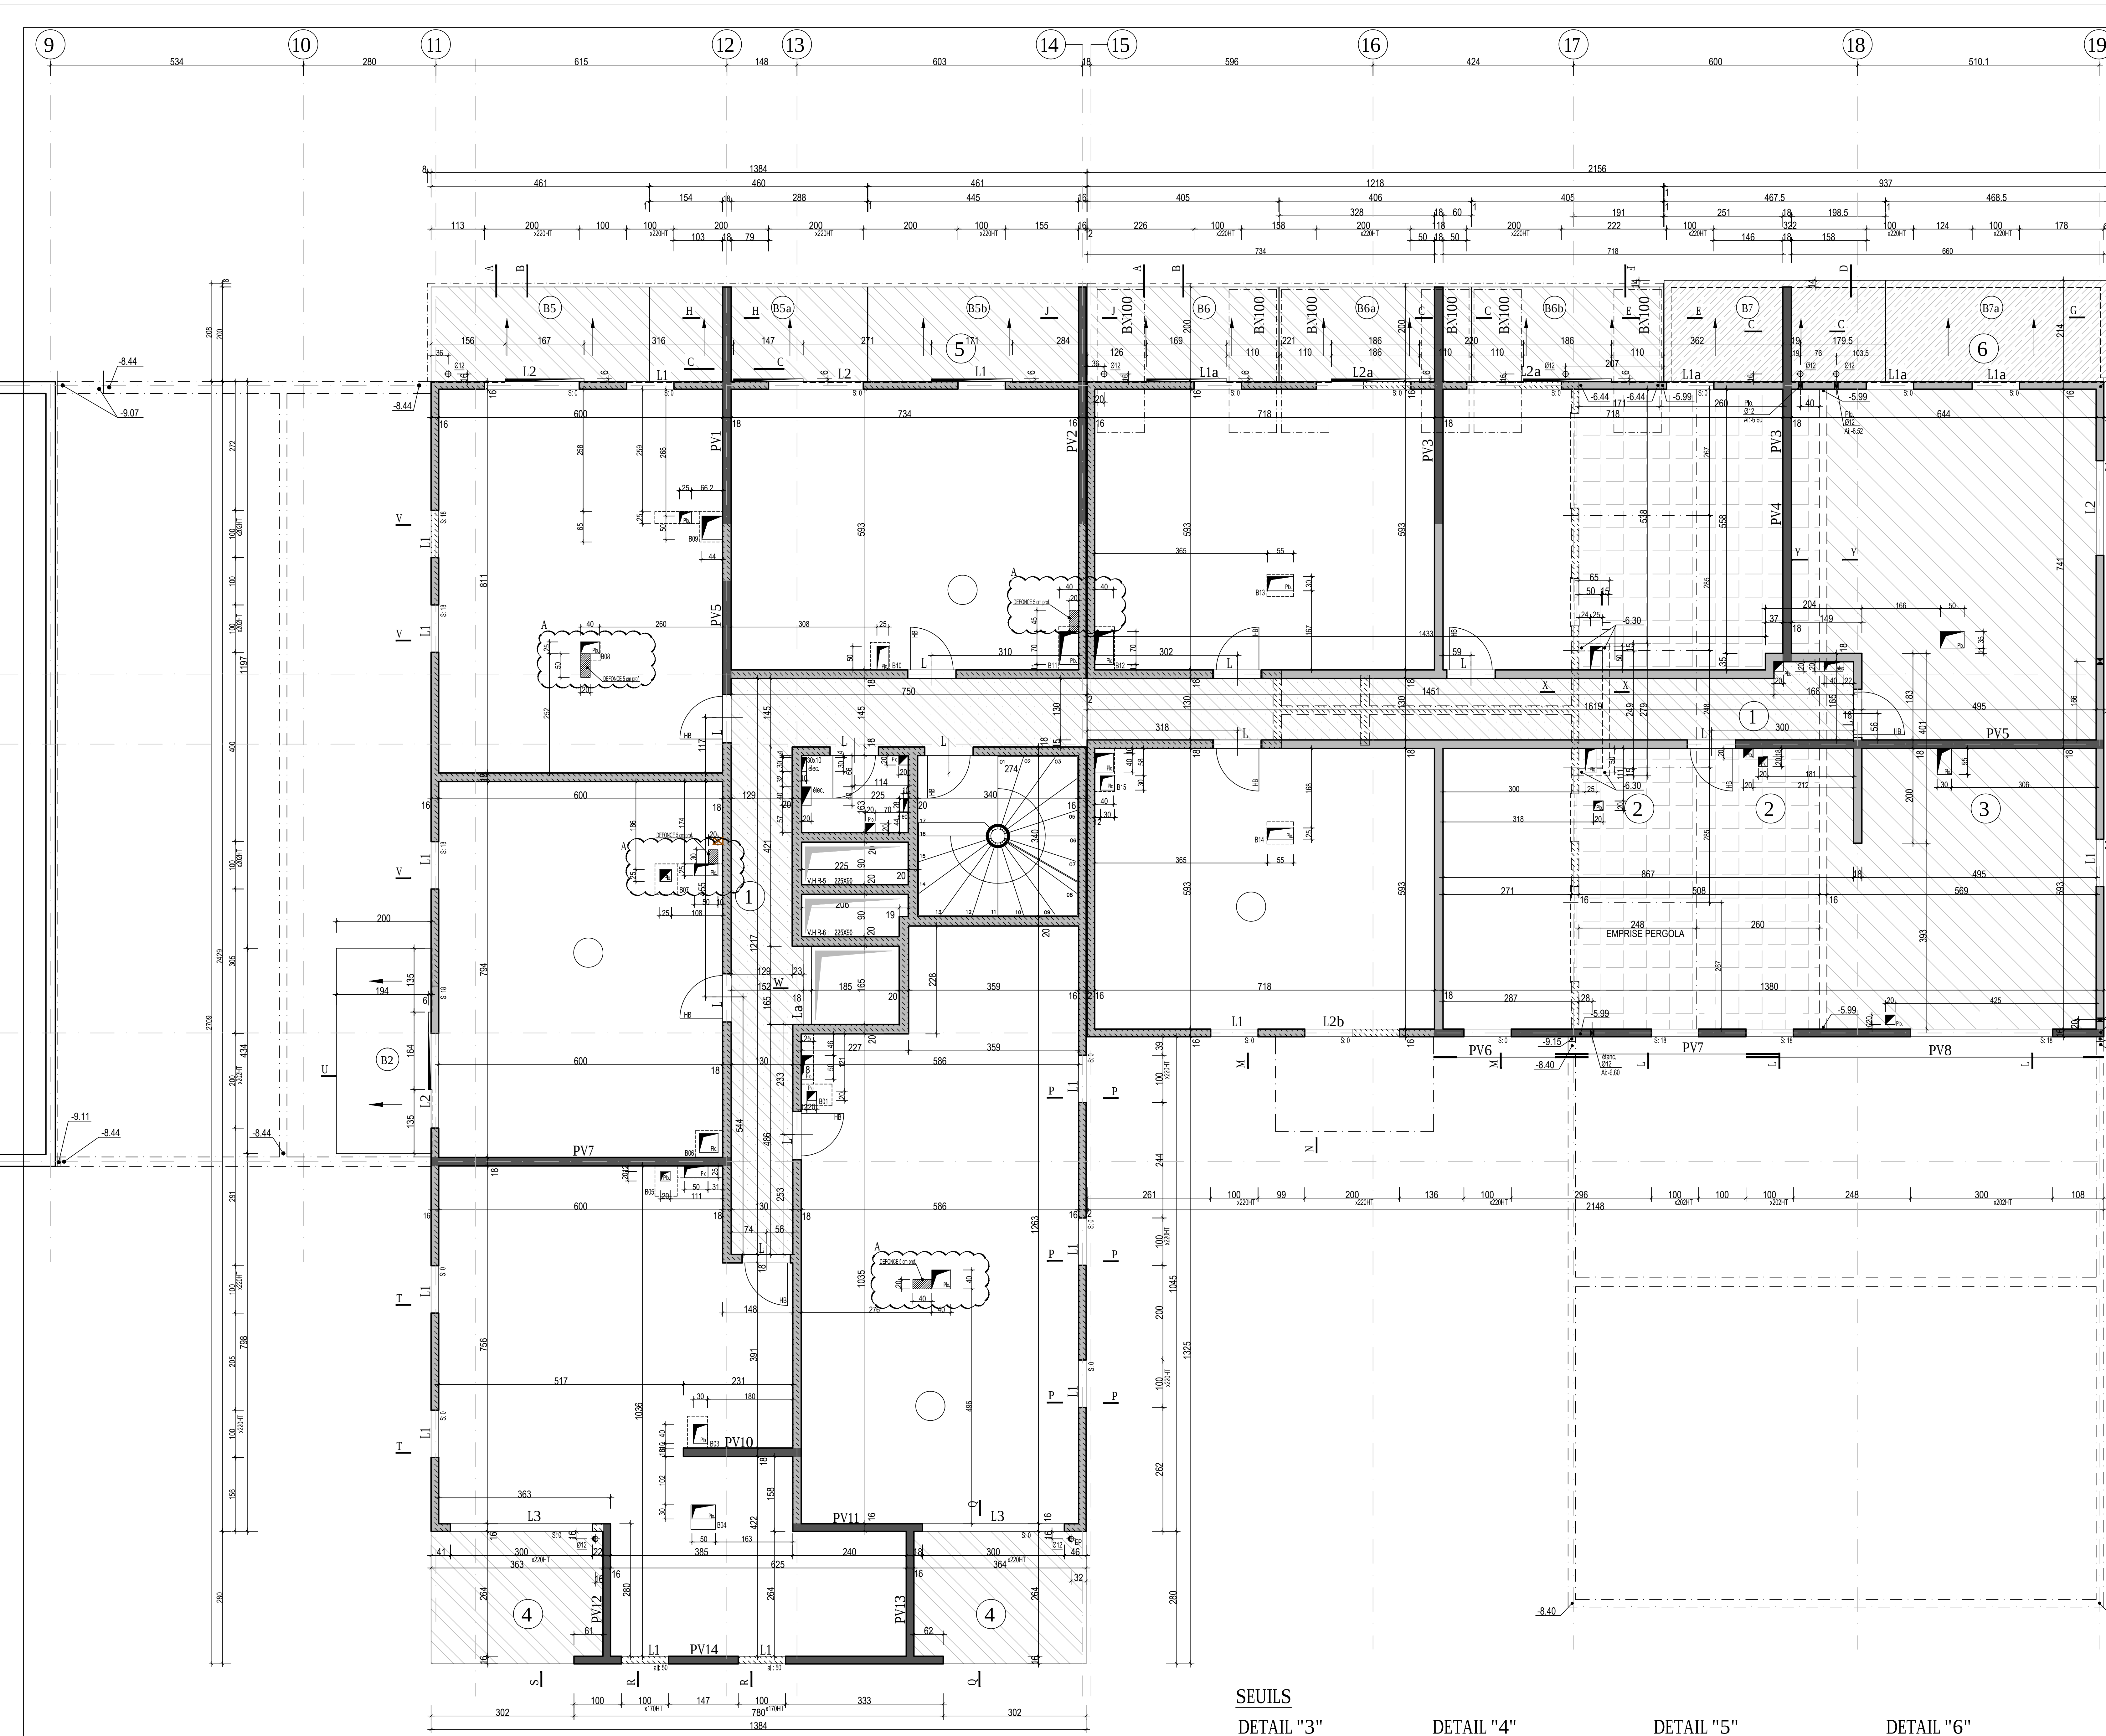

±0.00 = 220.50

NOAHO

Chemin de Fontanière - 69350 La Mulatière

Création de logements

Les entreprises dessinant les plans doivent leur copier les données et les modifier en fonction de la notation des travaux.

Les plans de la MATTE ne doivent servir qu'à la construction et ne doivent pas être utilisés pour d'autres fins.

INDICE	DATE	MODIFICATIONS
A	10/12/2015	AJOUTÉ DECAISSÉS DE S.d.B. suivant A
B		
C		

Bât B
PLANCHER sur -3
Coffrage

EXE
Contrainte de sol:

PLAN N°
B22 A
DATE : 19/11/2015

MATTÉ
BUREAU D'ETUDES
STRUCTURES ET FLUIDES

119 BOULEVARD ETAL INGRES 69100 VILLEURBANNE
Tél. 04 72 44 00 00 Fax 04 72 44 00 00
E-mail : info@matte.fr

Dessiné par : J.B.O.
Contrôlé par : P.L.N.
Echelle : 1/50'

Affaire N°
13.12.119

FINI: -6.63+213.87
DALLE BA Epr: 20 cm
DESSUS BRUT: -6.70
RESERVE: 7 cm

1 FINI: -6.63+213.87
DALLE BA Epr: 25 cm
DESSUS BRUT: -6.70
RESERVE: 7 cm

2 FINI: -6.38+214.12
DALLE BA Epr: 20 cm
DESSUS BRUT: -6.70
RESERVE: 32 cm

3 FINI: -6.40+214.10
DALLE BA Epr: 20 cm
DESSUS BRUT: -6.70
RESERVE: 30 cm

4 FINI: -6.56+213.94
DALLE BA Epr: 20 à 17 cm
DESSUS BRUT: -6.70 à -6.73
RESERVE: 14 cm

5 FINI: -6.56+213.94
DALLE BA Epr: 20 à 18 cm
DESSUS BRUT: -6.70 à -6.72
RESERVE: 14 cm

6 FINI: -6.56+213.94
DALLE BA Epr: 20 à 18 cm
DESSUS BRUT: -6.70 à -6.72
RESERVE: 0 cm