


ARMATURES INFÉRIEURES

RH1 (2p)

2 HA 10 x 50 L=349
15 HA 8 x 40

RH2 (2p)


2 HA 10 x 277
14 HA 8 x 40

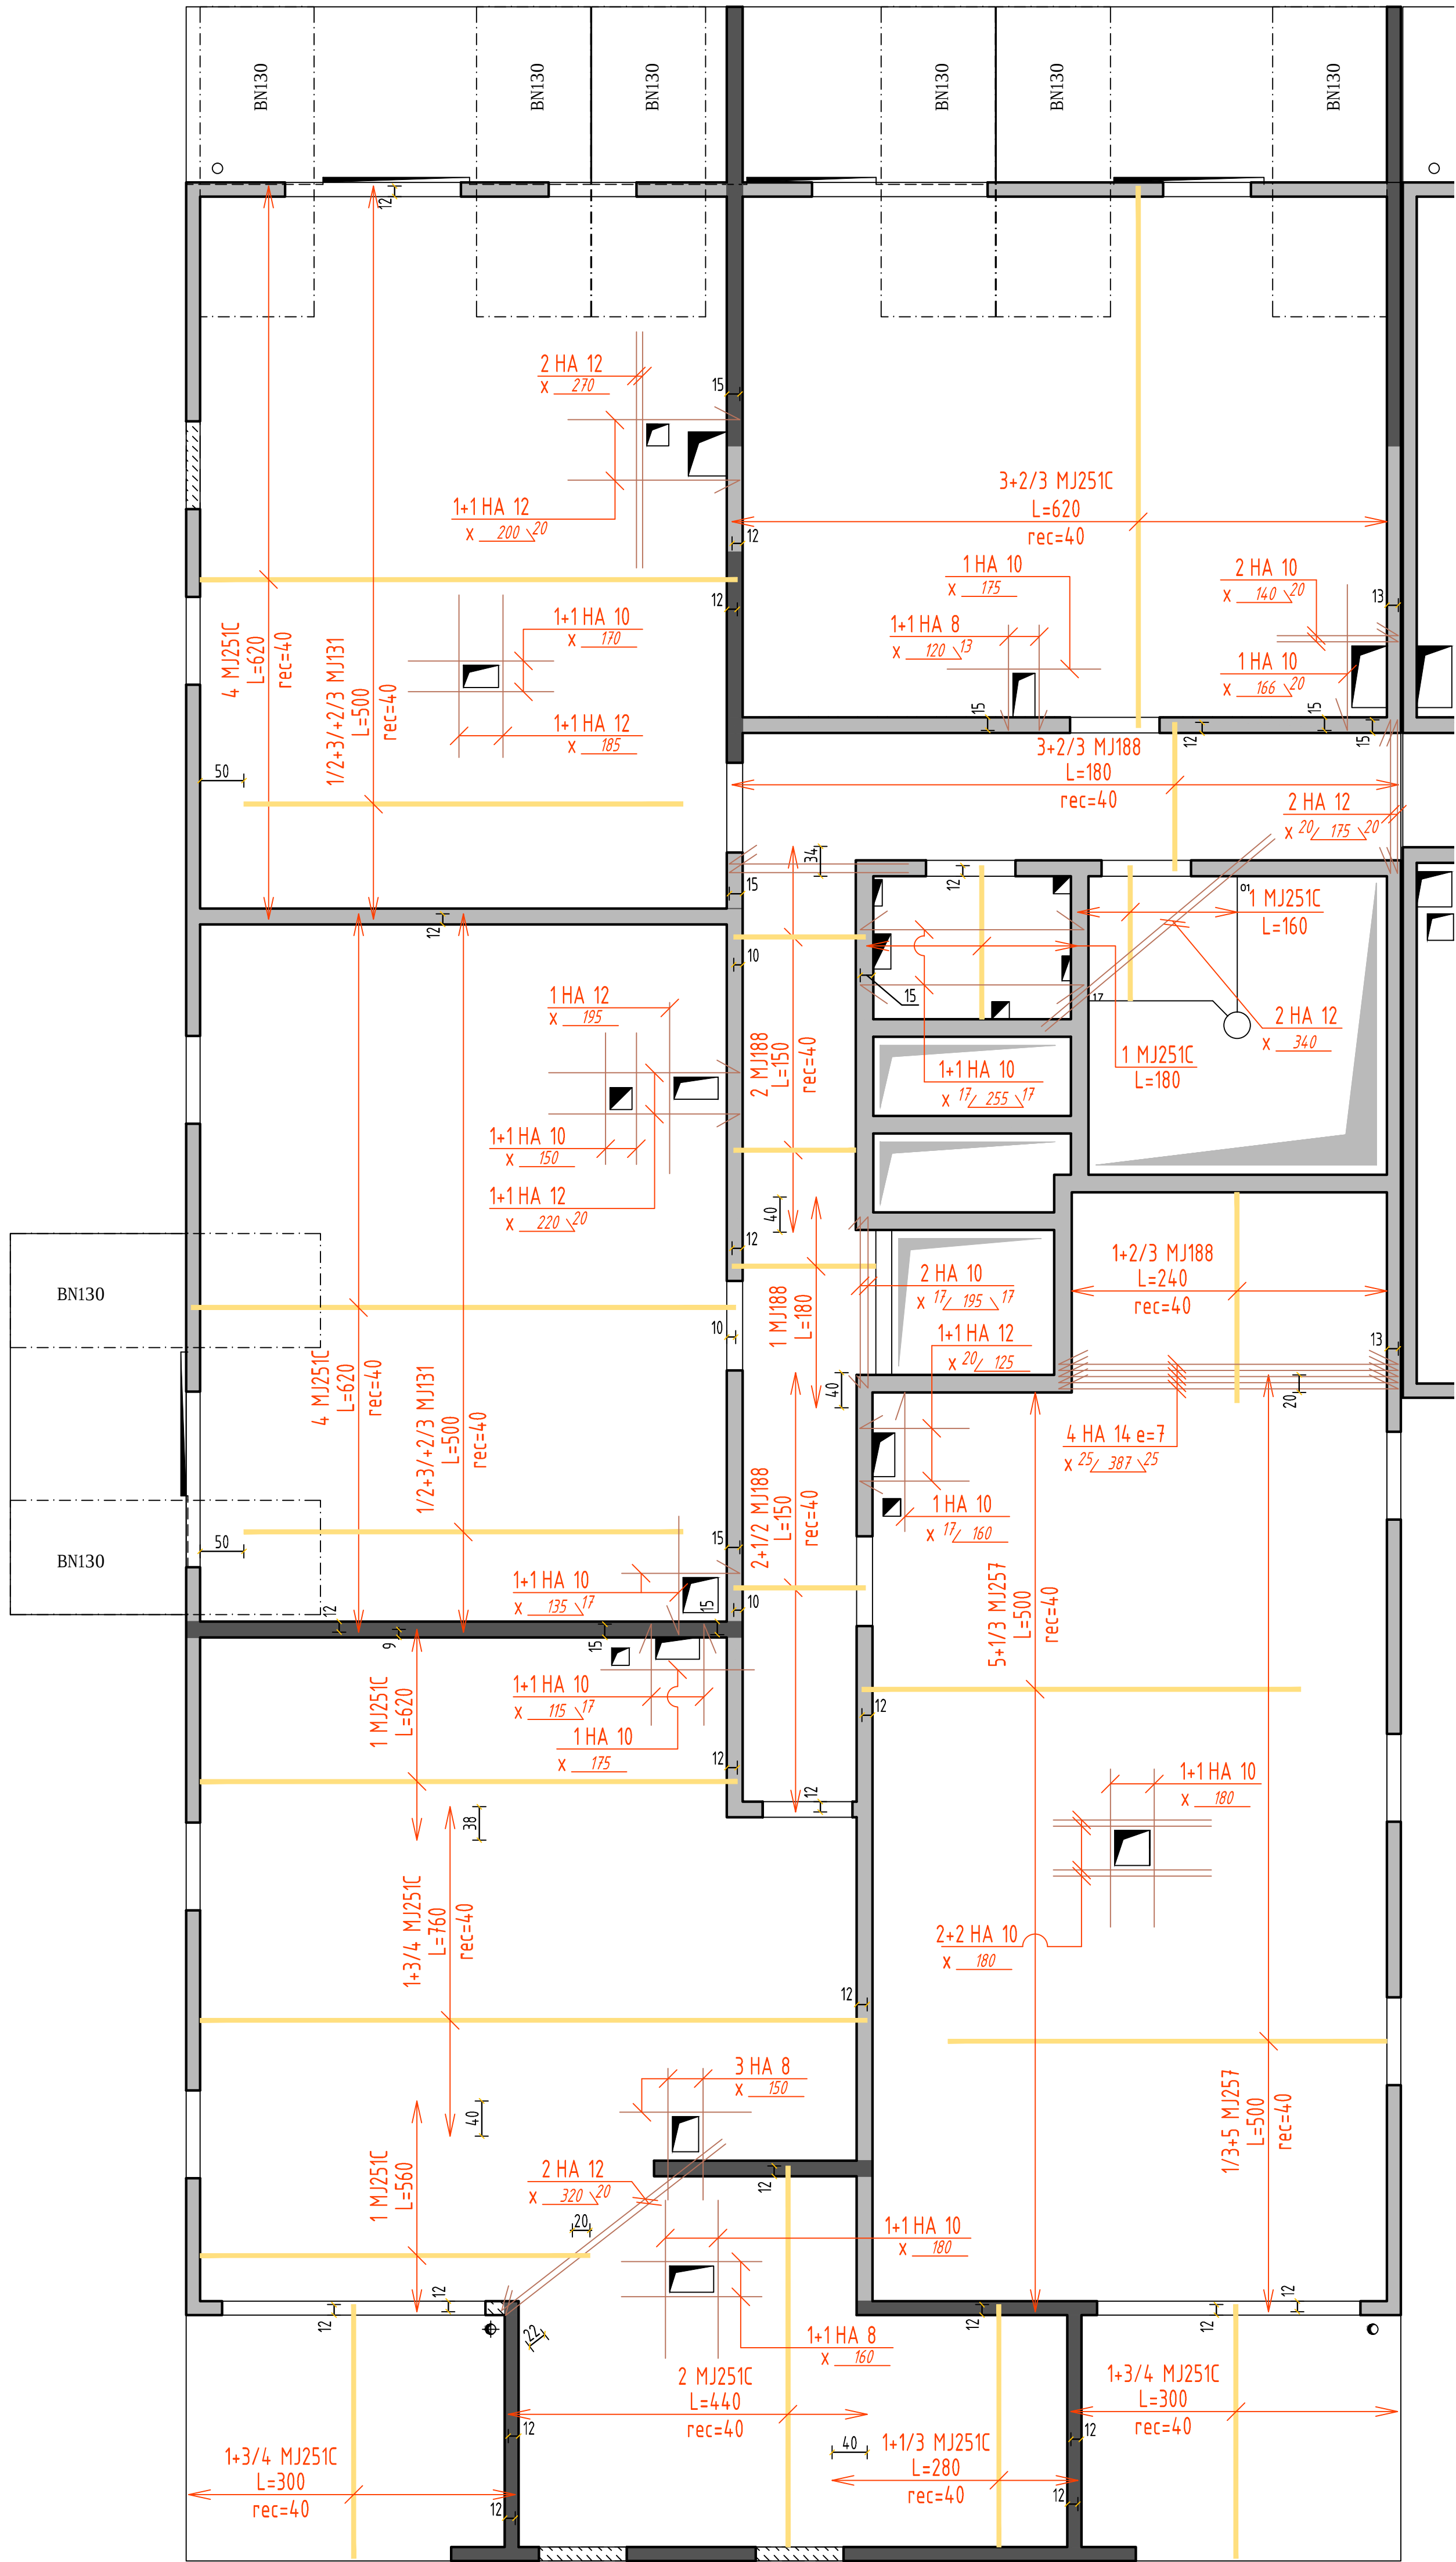

TREILLIS INF DES DALLES

Treillis	Lgr (cm)	Nbr
MJ131	500	9
MJ188	150	4+1/2
	180	5
	240	2
MJ251C	180	1
	280	1+1/2
	300	4
	440	2
	560	1
	620	13
	760	2
MJ257	500	11

ARMATURES SUPÉRIEURES

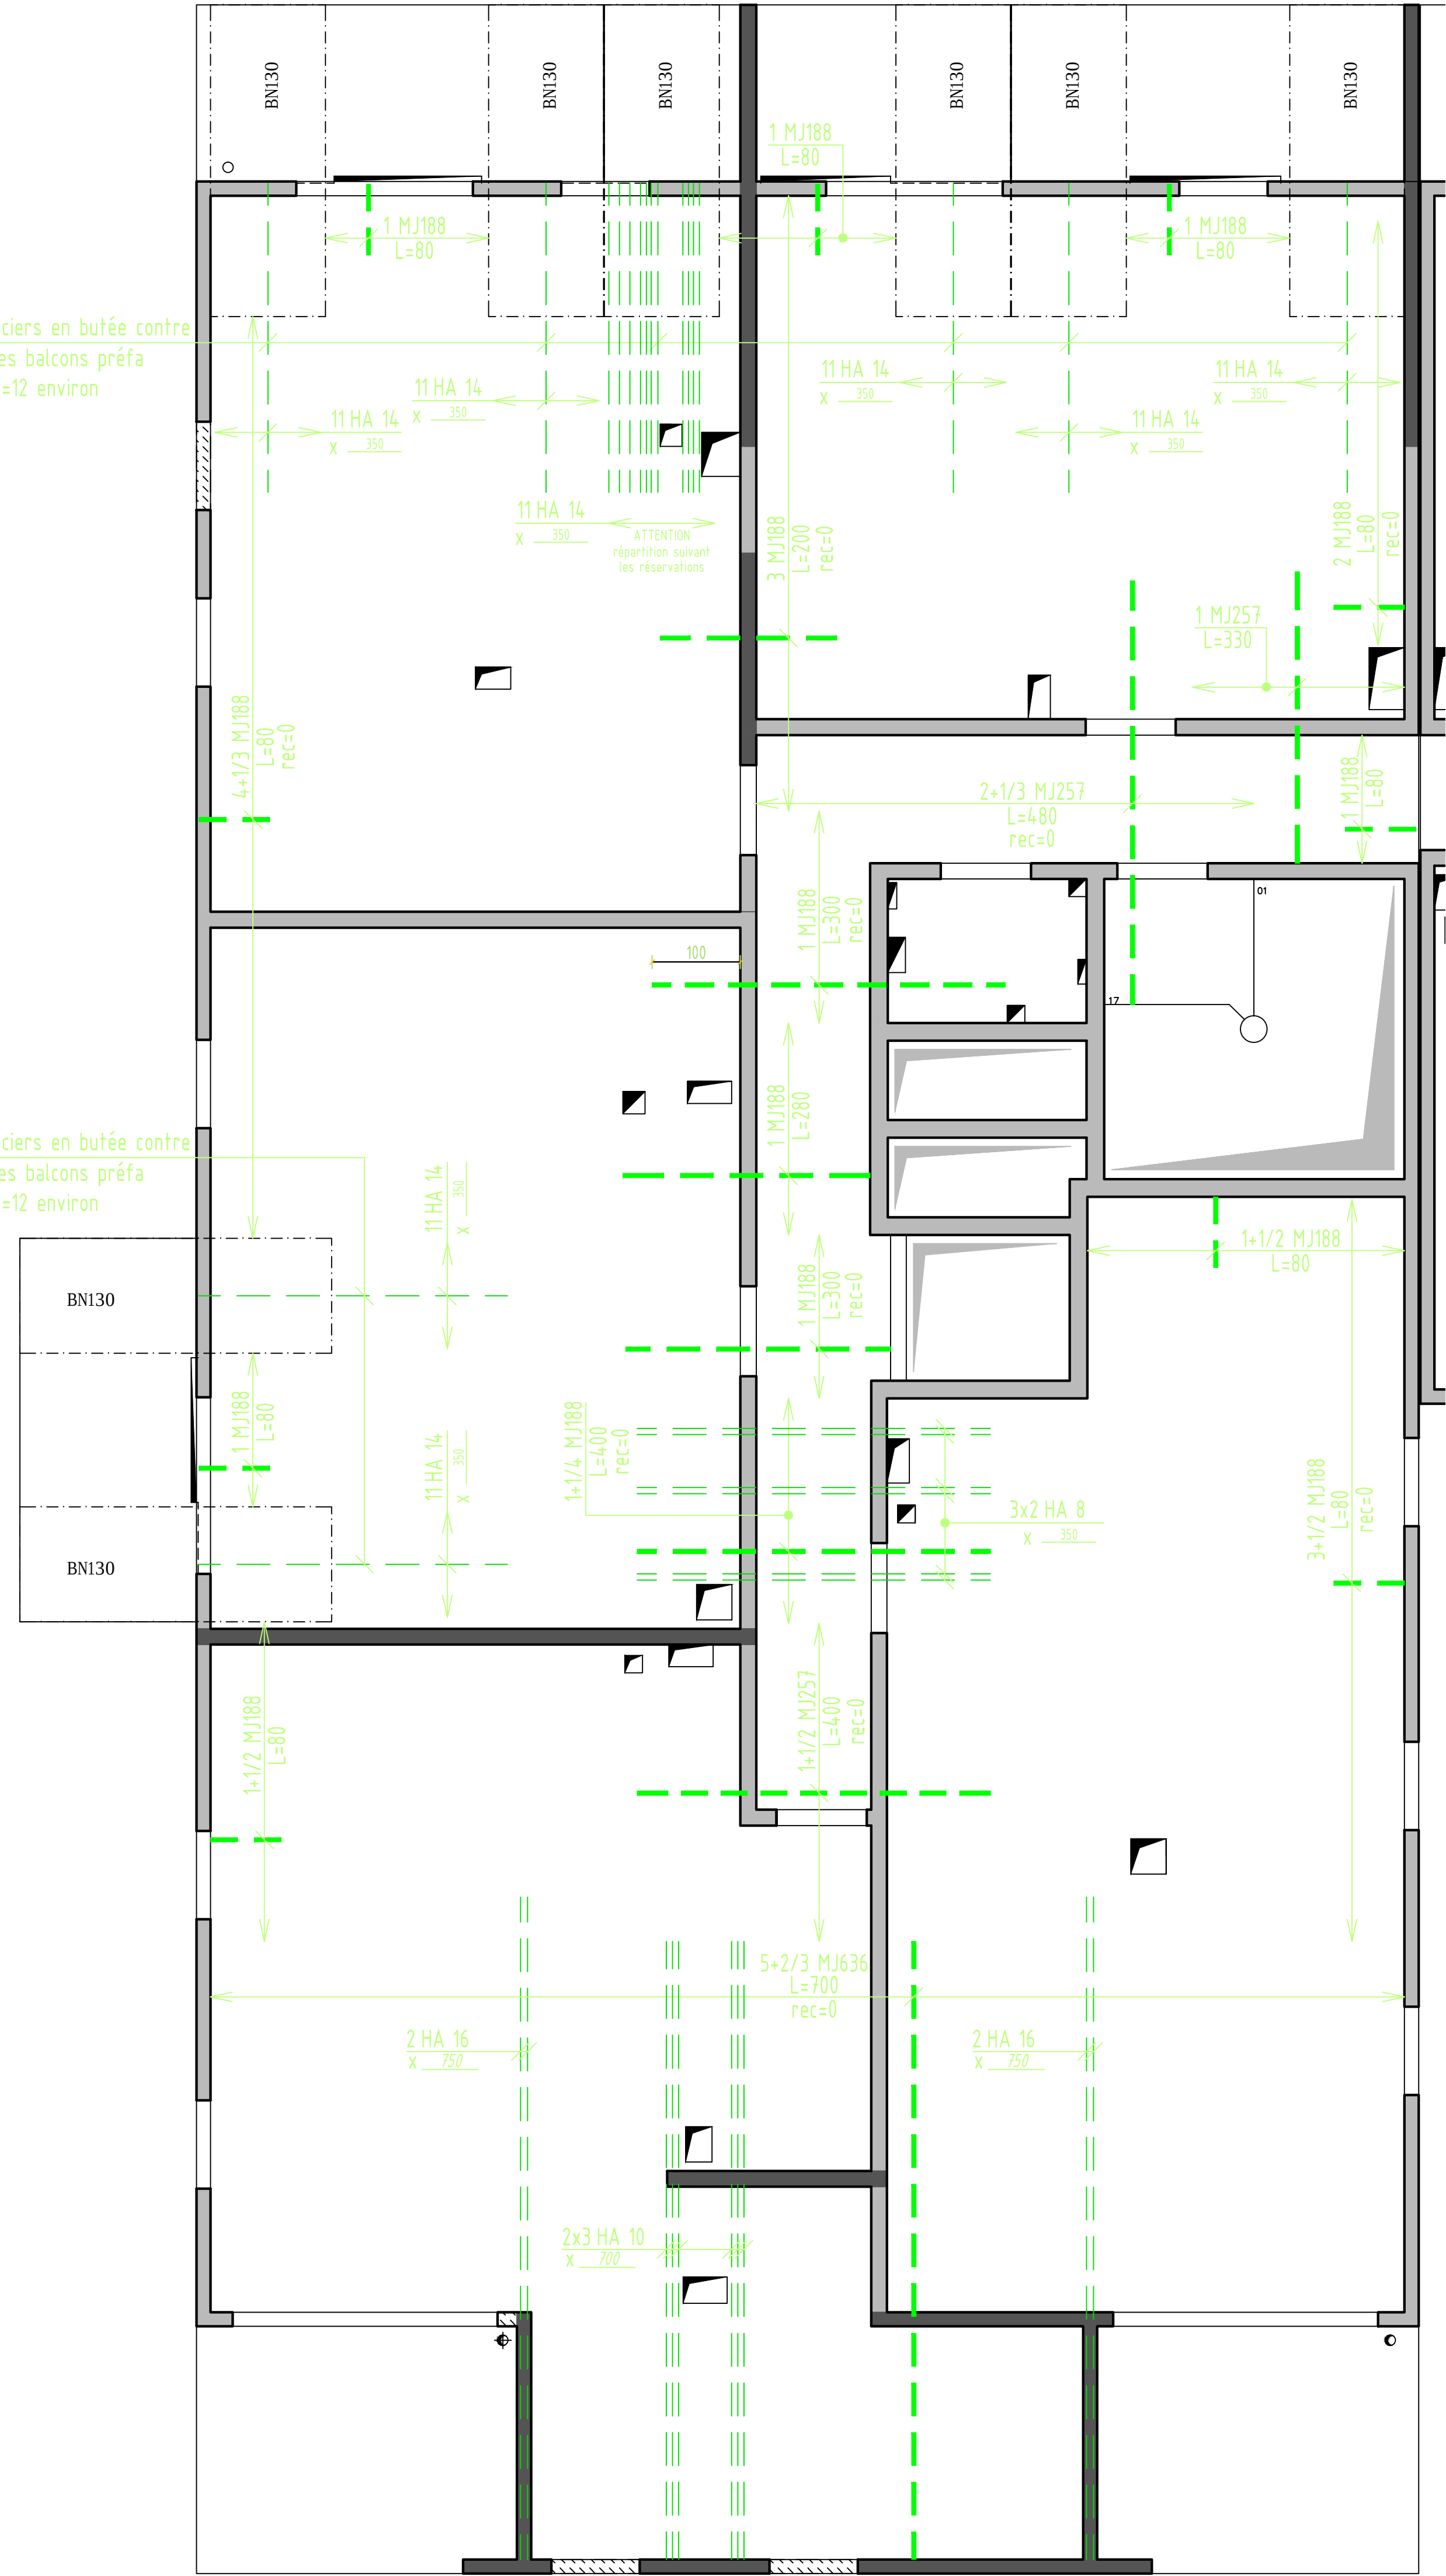

TREILLIS SUP DES DALLES

Treillis	Lgr (cm)	Nbr
MJ188	80	16+1/2
	200	3
	280	1
	300	2
	400	1+1/2
MJ257	330	1
	400	1+1/2
	480	2+1/2
MJ636	700	6

DETAIL D'ABOUTS DE CHAINAGES INTERIEURS:

Position des épaves d'angles dans dalle 2 HA 14 x 14
Les plans du boi MATTE ne doivent servir qu'au corps d'entente et doivent être des plans d'exécution

chaînage int. arrivant sur mur de façade
chaînage int. arrivant sur mur int.



DETAIL D'ABOUTS DE CHAINAGES EN ANGLE SUR FACADES:

Position des épaves d'angles dans dalle 3 HA 14 x 14
Les plans du boi MATTE ne doivent servir qu'au corps d'entente et doivent être des plans d'exécution

coupe
vue en plan



NOAHO

Chemin de Fontanière - 69350 La Mulatière

Création de logements

Les entreprises réalisant les travaux devront tenir compte des derniers plans architecte lors de la réalisation des travaux. Les plans du boi MATTE ne doivent servir qu'au corps d'entente et doivent être des plans d'exécution.

ARCHITECTES:	ATELIER DE LA PASSERELLE	MO DELEGUE:	PSO Ingénierie
BET STRUCTURE:	MATTE SAS	MO:	SUD EST COORDINATION
BET FLUIDES:	PRELEM	CSPS:	
ECONOMISTE:	EXECO	OPC:	
BUREAU DE CONTROLE:	Bureau VERITAS	ENTREPRISE(S):	Fontanel pbc

Bât: B
PLANCHER sur -3 de la file 11 à 14
NAPPES SUPERIEURES et INFÉRIEURES
Armatures des dalles

INDICE	DATE	MODIFICATIONS
A		
B		
C		

MATTÉ
BUREAU D'ÉTUDES
STRUCTURES ET FLUIDES
119 BOULEVARD STALINGRAD 69100 VILLEURBANNE
Tel: 04 72 44 02 97 Fax: 04 72 44 26 59
E-mail: bat@matte.fr

Dessiné par: J.B.O.
Contrôle par: P.L.N.
Echelle: :

EXE

Contrainte de sol:
Aciers HA (T) FeE500
Aciers Dux (B) FeE235
Aciers TS FeE500
Soudure = 50MPa
Enrobage = 3 cm

PLAN N°
B25 0
DATE: 03/12/2015

Affaire N°
13.12.119