


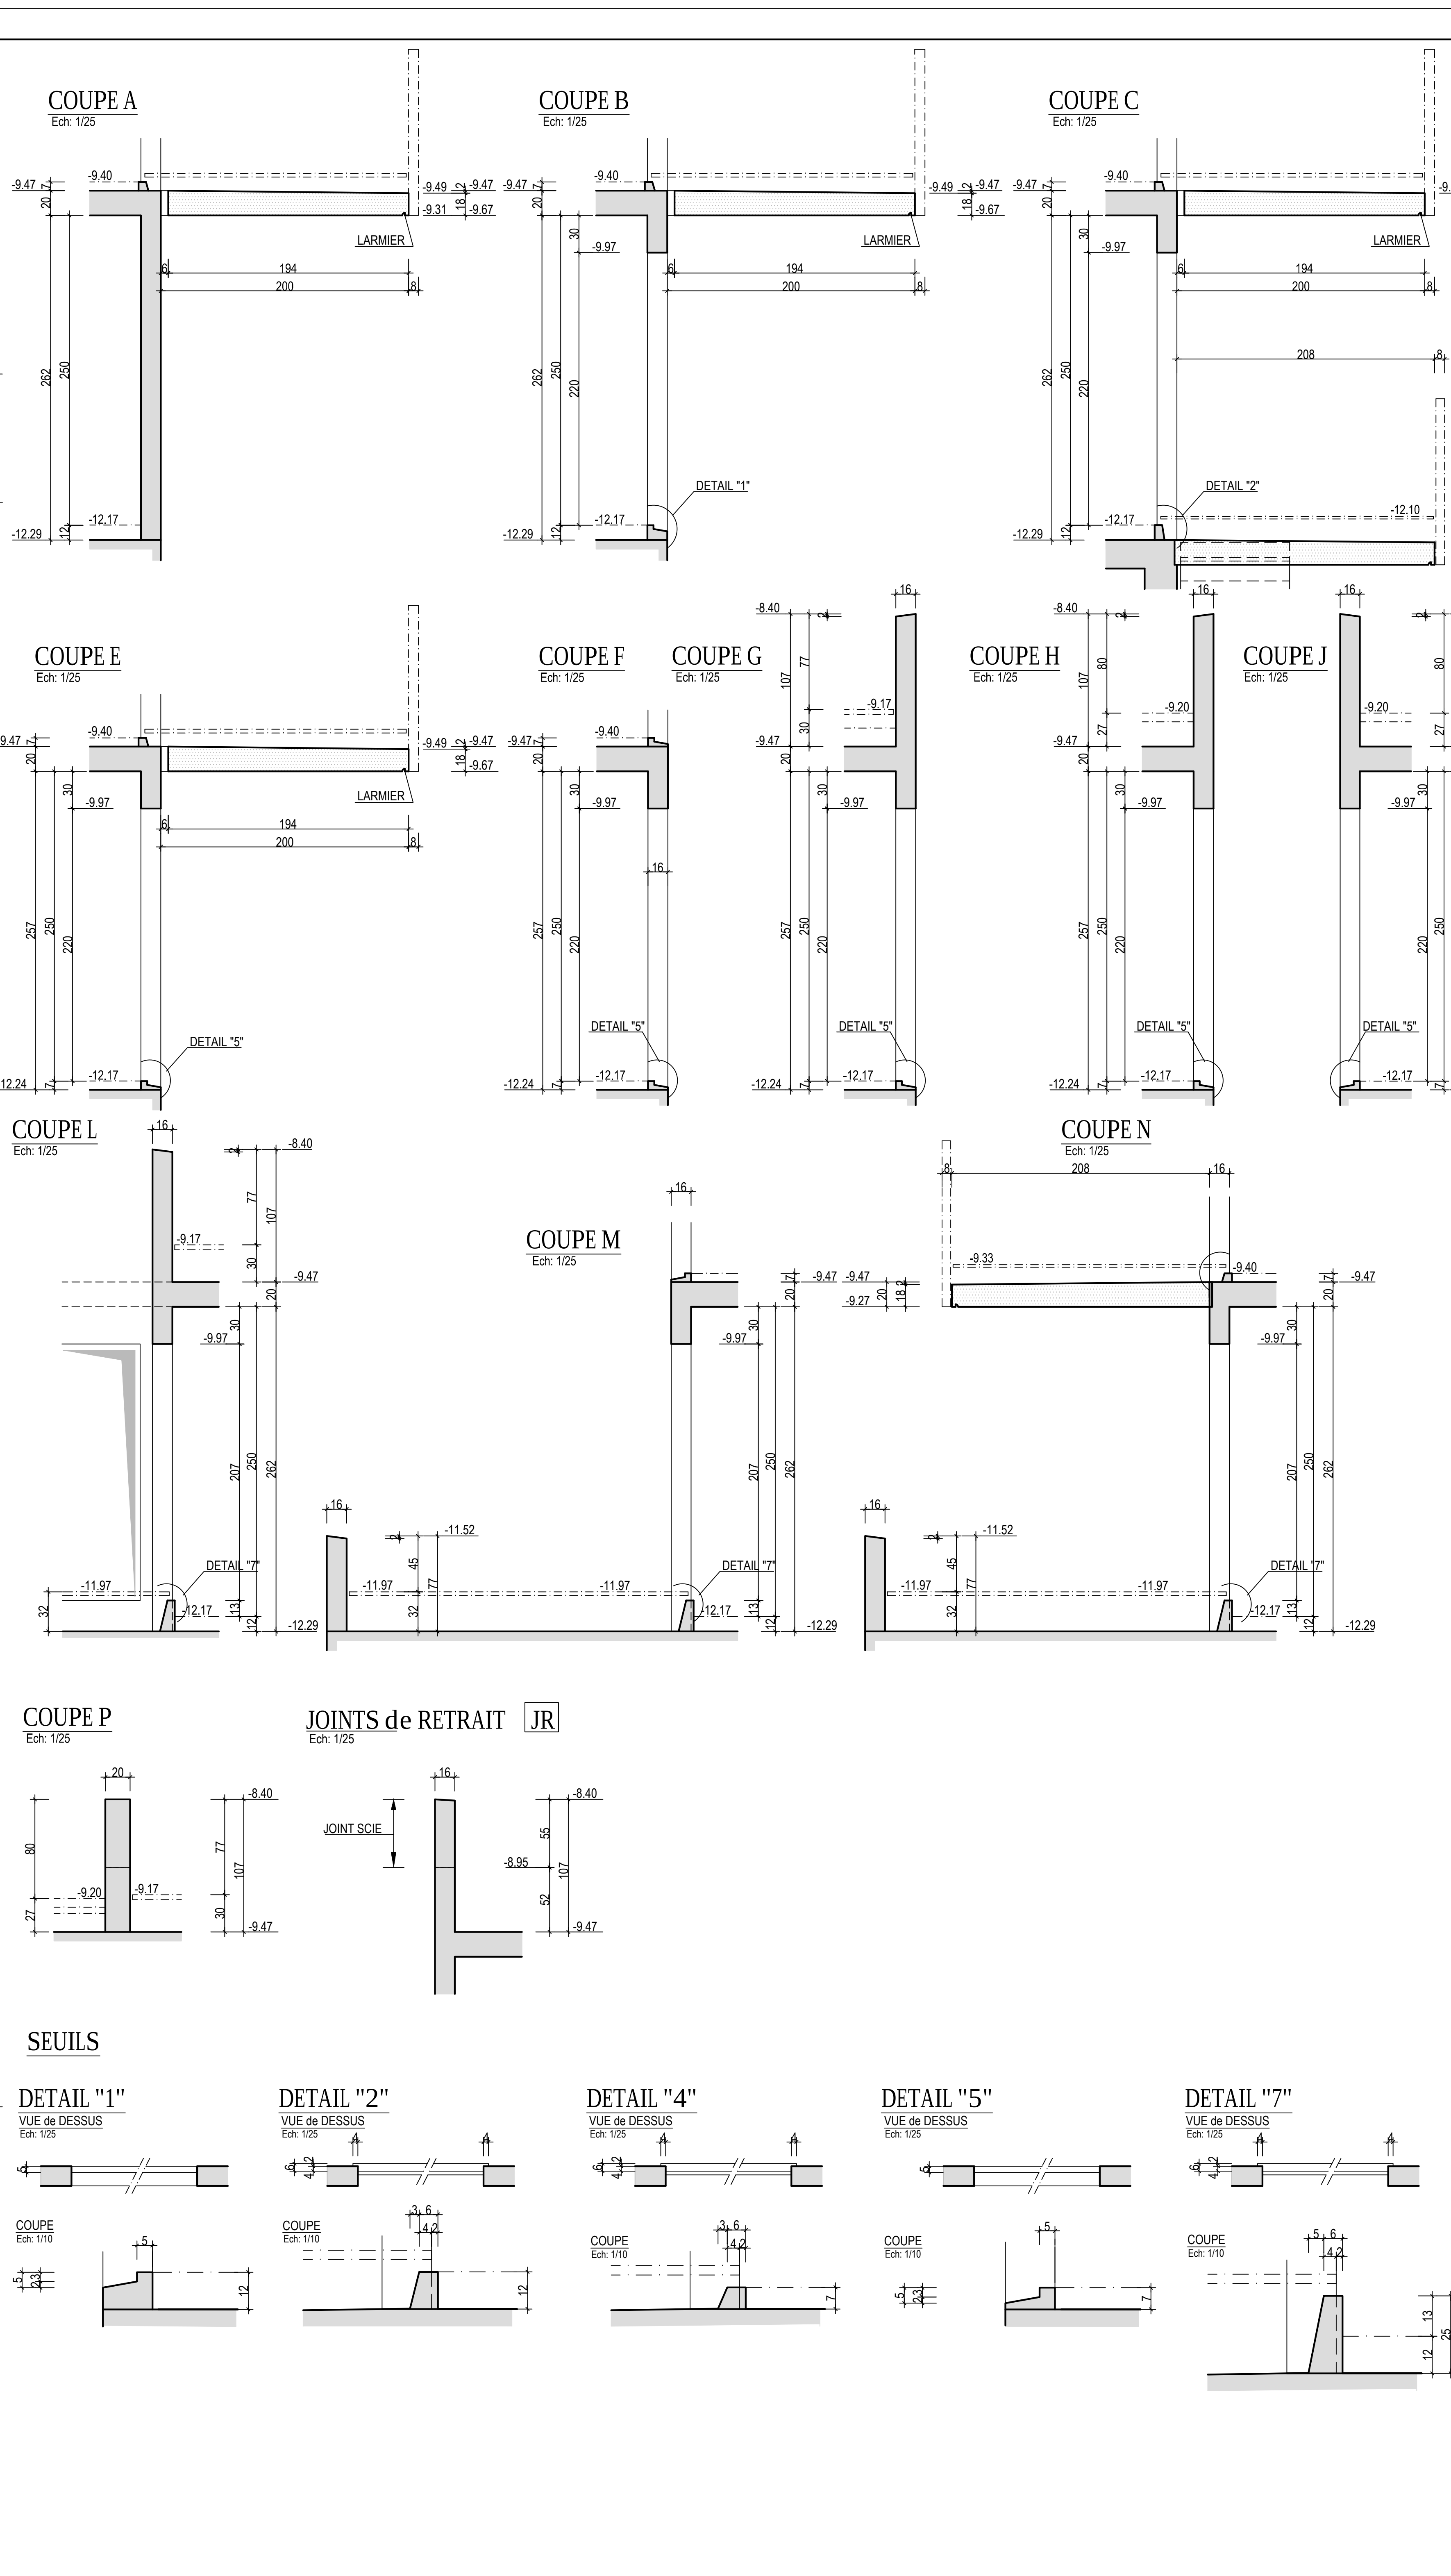

COUPE D
Ech: 1/25

COUPE K
Ech: 1/25

DALLES

①	FINI: -9.40=211.10 DALLE BA Epr: 20 cm DESSUS BRUT:-9.47 RESERVE: 7 cm	①	FINI: -9.40=211.10 DALLE BA Epr: 25 cm DESSUS BRUT:-9.47 RESERVE: 7 cm
②	FINI: -9.17=211.33 DALLE BA Epr: 20 cm DESSUS BRUT:-9.47 RESERVE: 30 cm	③	FINI: -9.20=211.30 DALLE BA Epr: 20 cm DESSUS BRUT:-9.47 RESERVE: 27 cm

±0.00 = 220.50

NOAHO

Chemin de Fontanière - 69350 La Mulatière

Création de logements

ARCHITECTE(S): BET STRUCTURE: BET FLUIDES: ECONOMISTE: BUREAU DE CONTRÔLE:	ATELIER DE LA PASSERELLE MATTÉ SAS PRÉLIM: EXECO Bureau VERITAS	MO DELEGUE: MDE: COPS: ENTREPRISES:	PSO Ingénierie SUD EST COORDINATION BPC: Fontanel-pbc
--	---	--	--

Bât: B
PLANCHER sur -4
Coffrage

INDICE	DATE	MODIFICATIONS
A	28/03/2016	COMPLETE
B	31/03/2016	MISE A JOUR REPERAGE ARMATURES
C	14/04/2016	AJOUTE REPERAGE PREFEA

MATTÉ
BUREAU D'ETUDES
STRUCTURES ET FLUIDES
119 BOULEVARD STALINGRAD 69100 VILLEURBANNE
TEL: 04 72 44 12 87 Fax 04 72 44 26 59
E-mail: info@matte.fr

Dessiné par : J.B.O
Contrôle par : P.LIN
Echelle : 1/50'

DOE
Contrainte de sac 8 bars ELS
Aciers HA (T) FeE500
Aciers Dosa (D) FeE 235
Aciers TS FeE 500
Béton C25 => 28Mpa
Enrobage = 3 cm

PLAN N° C
DATE : 26/03/2016

Affaire N°
13.12.119