
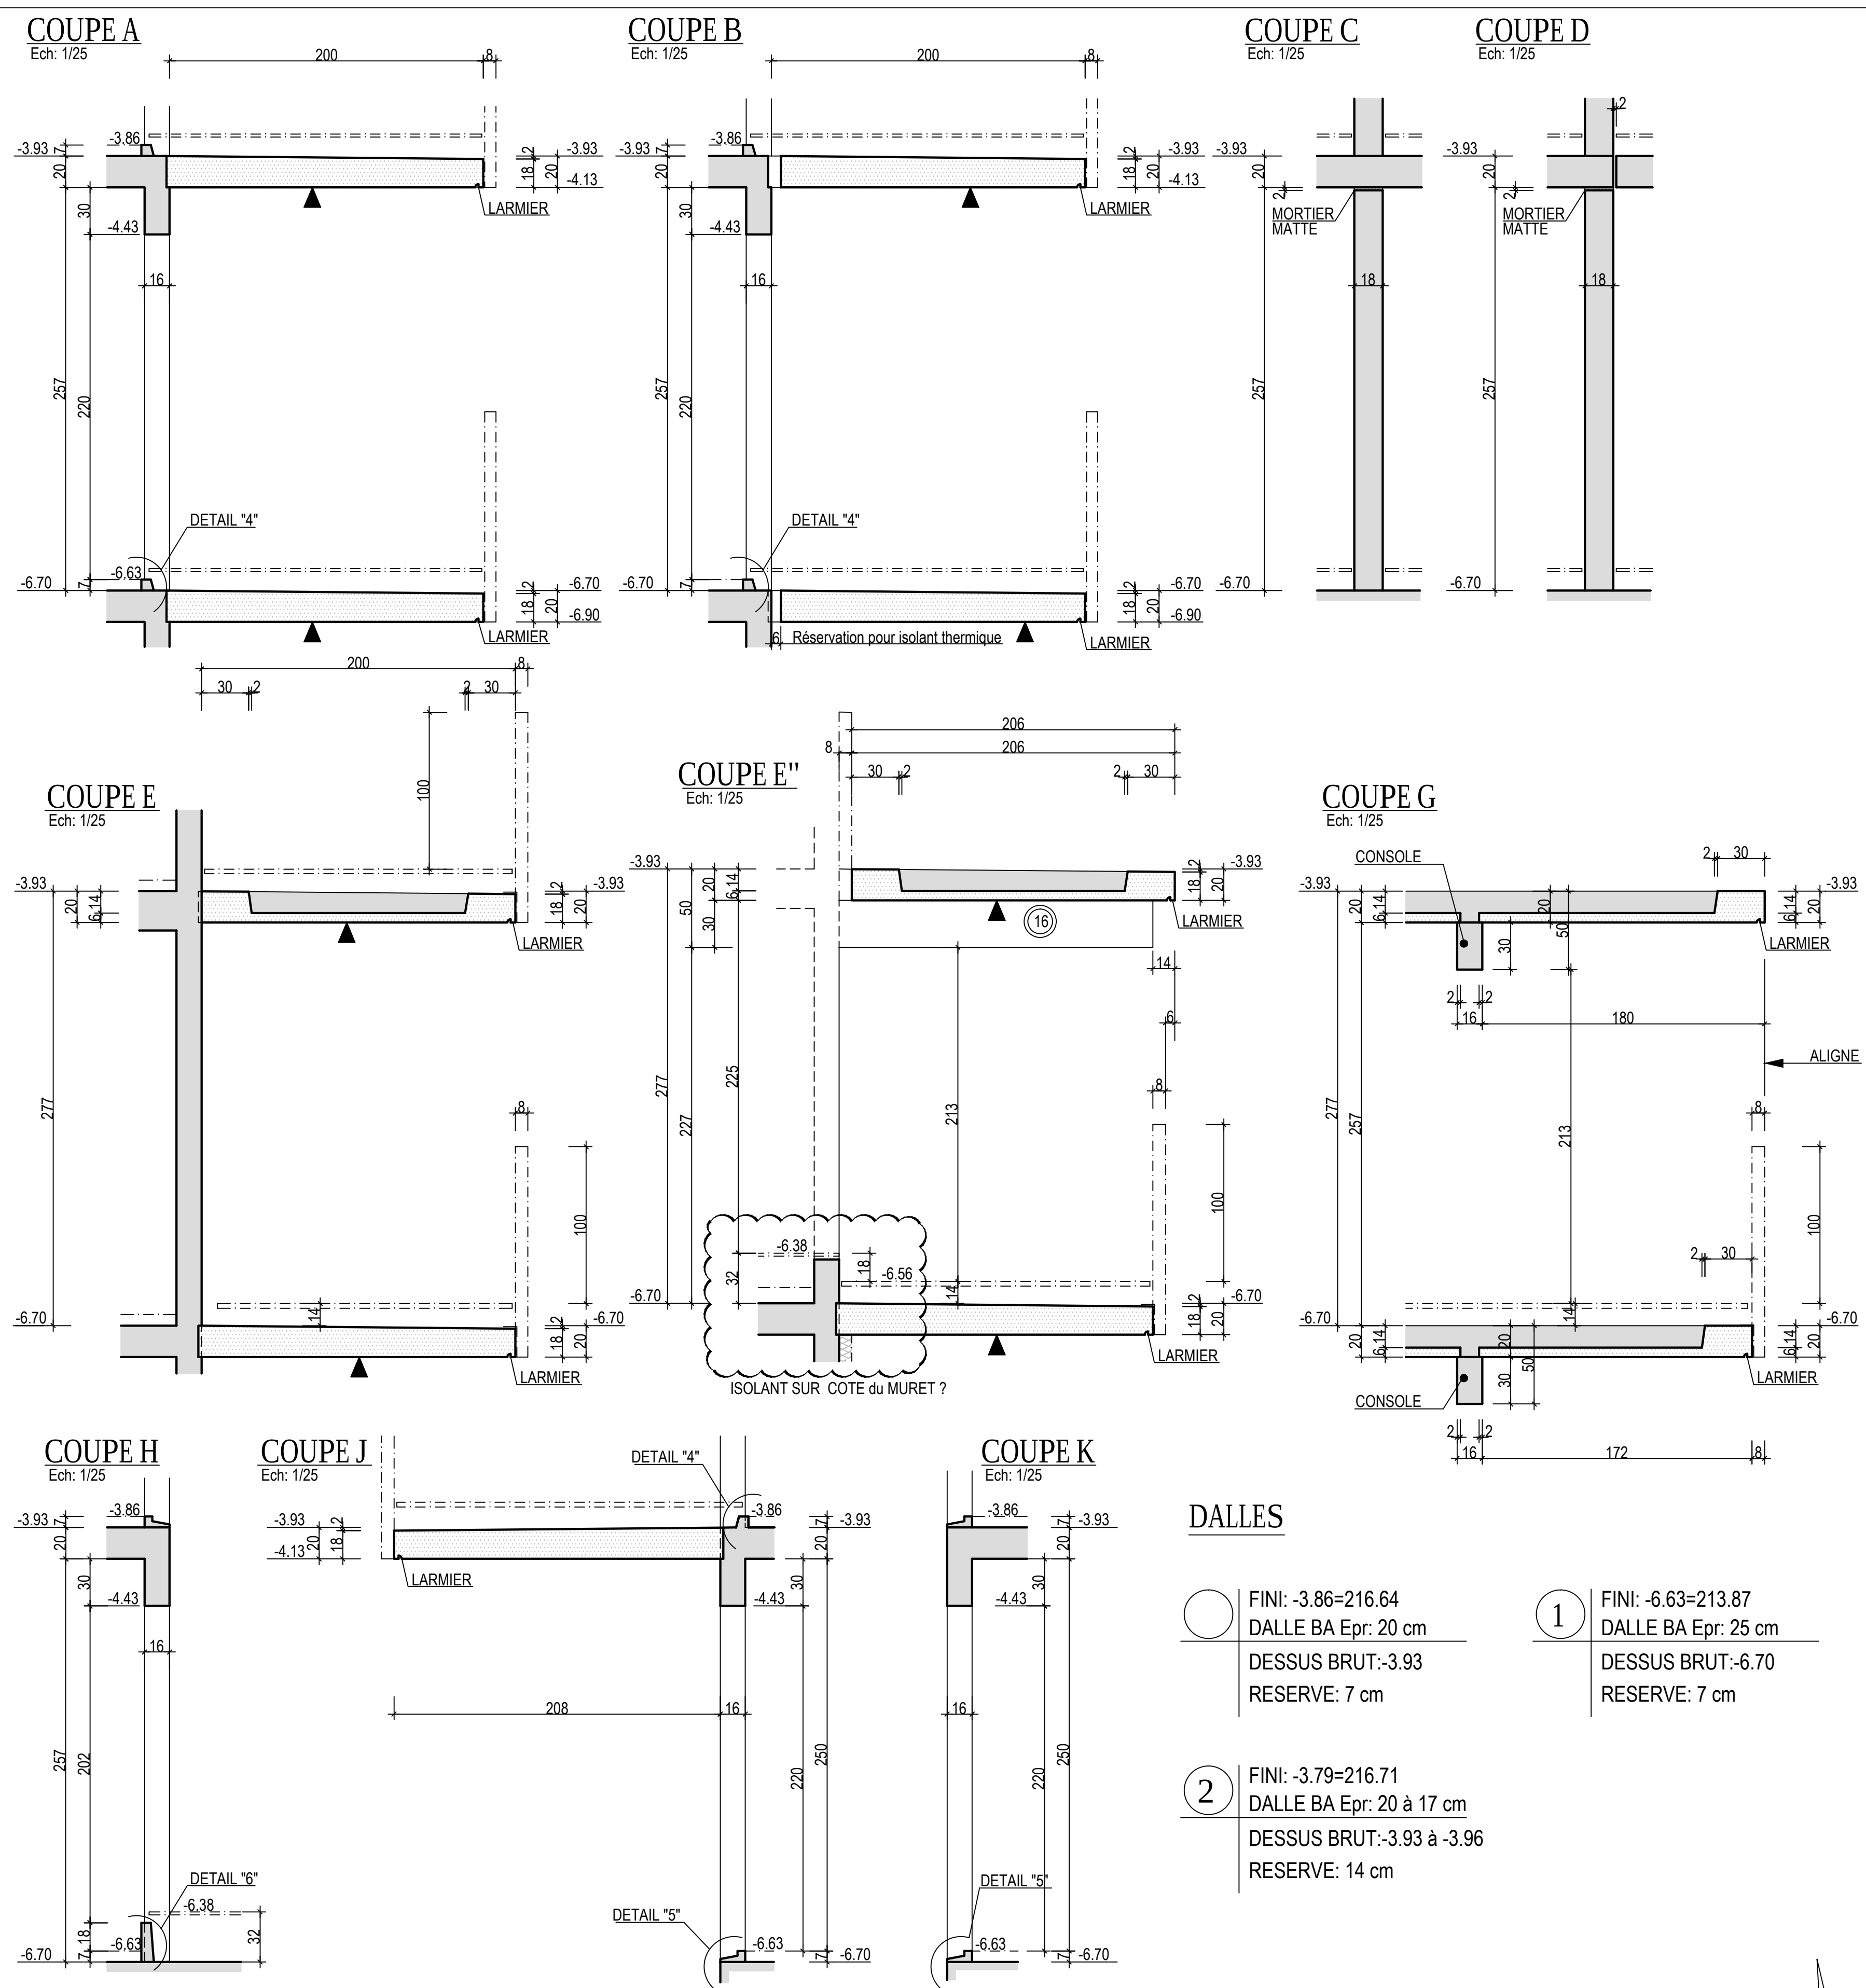


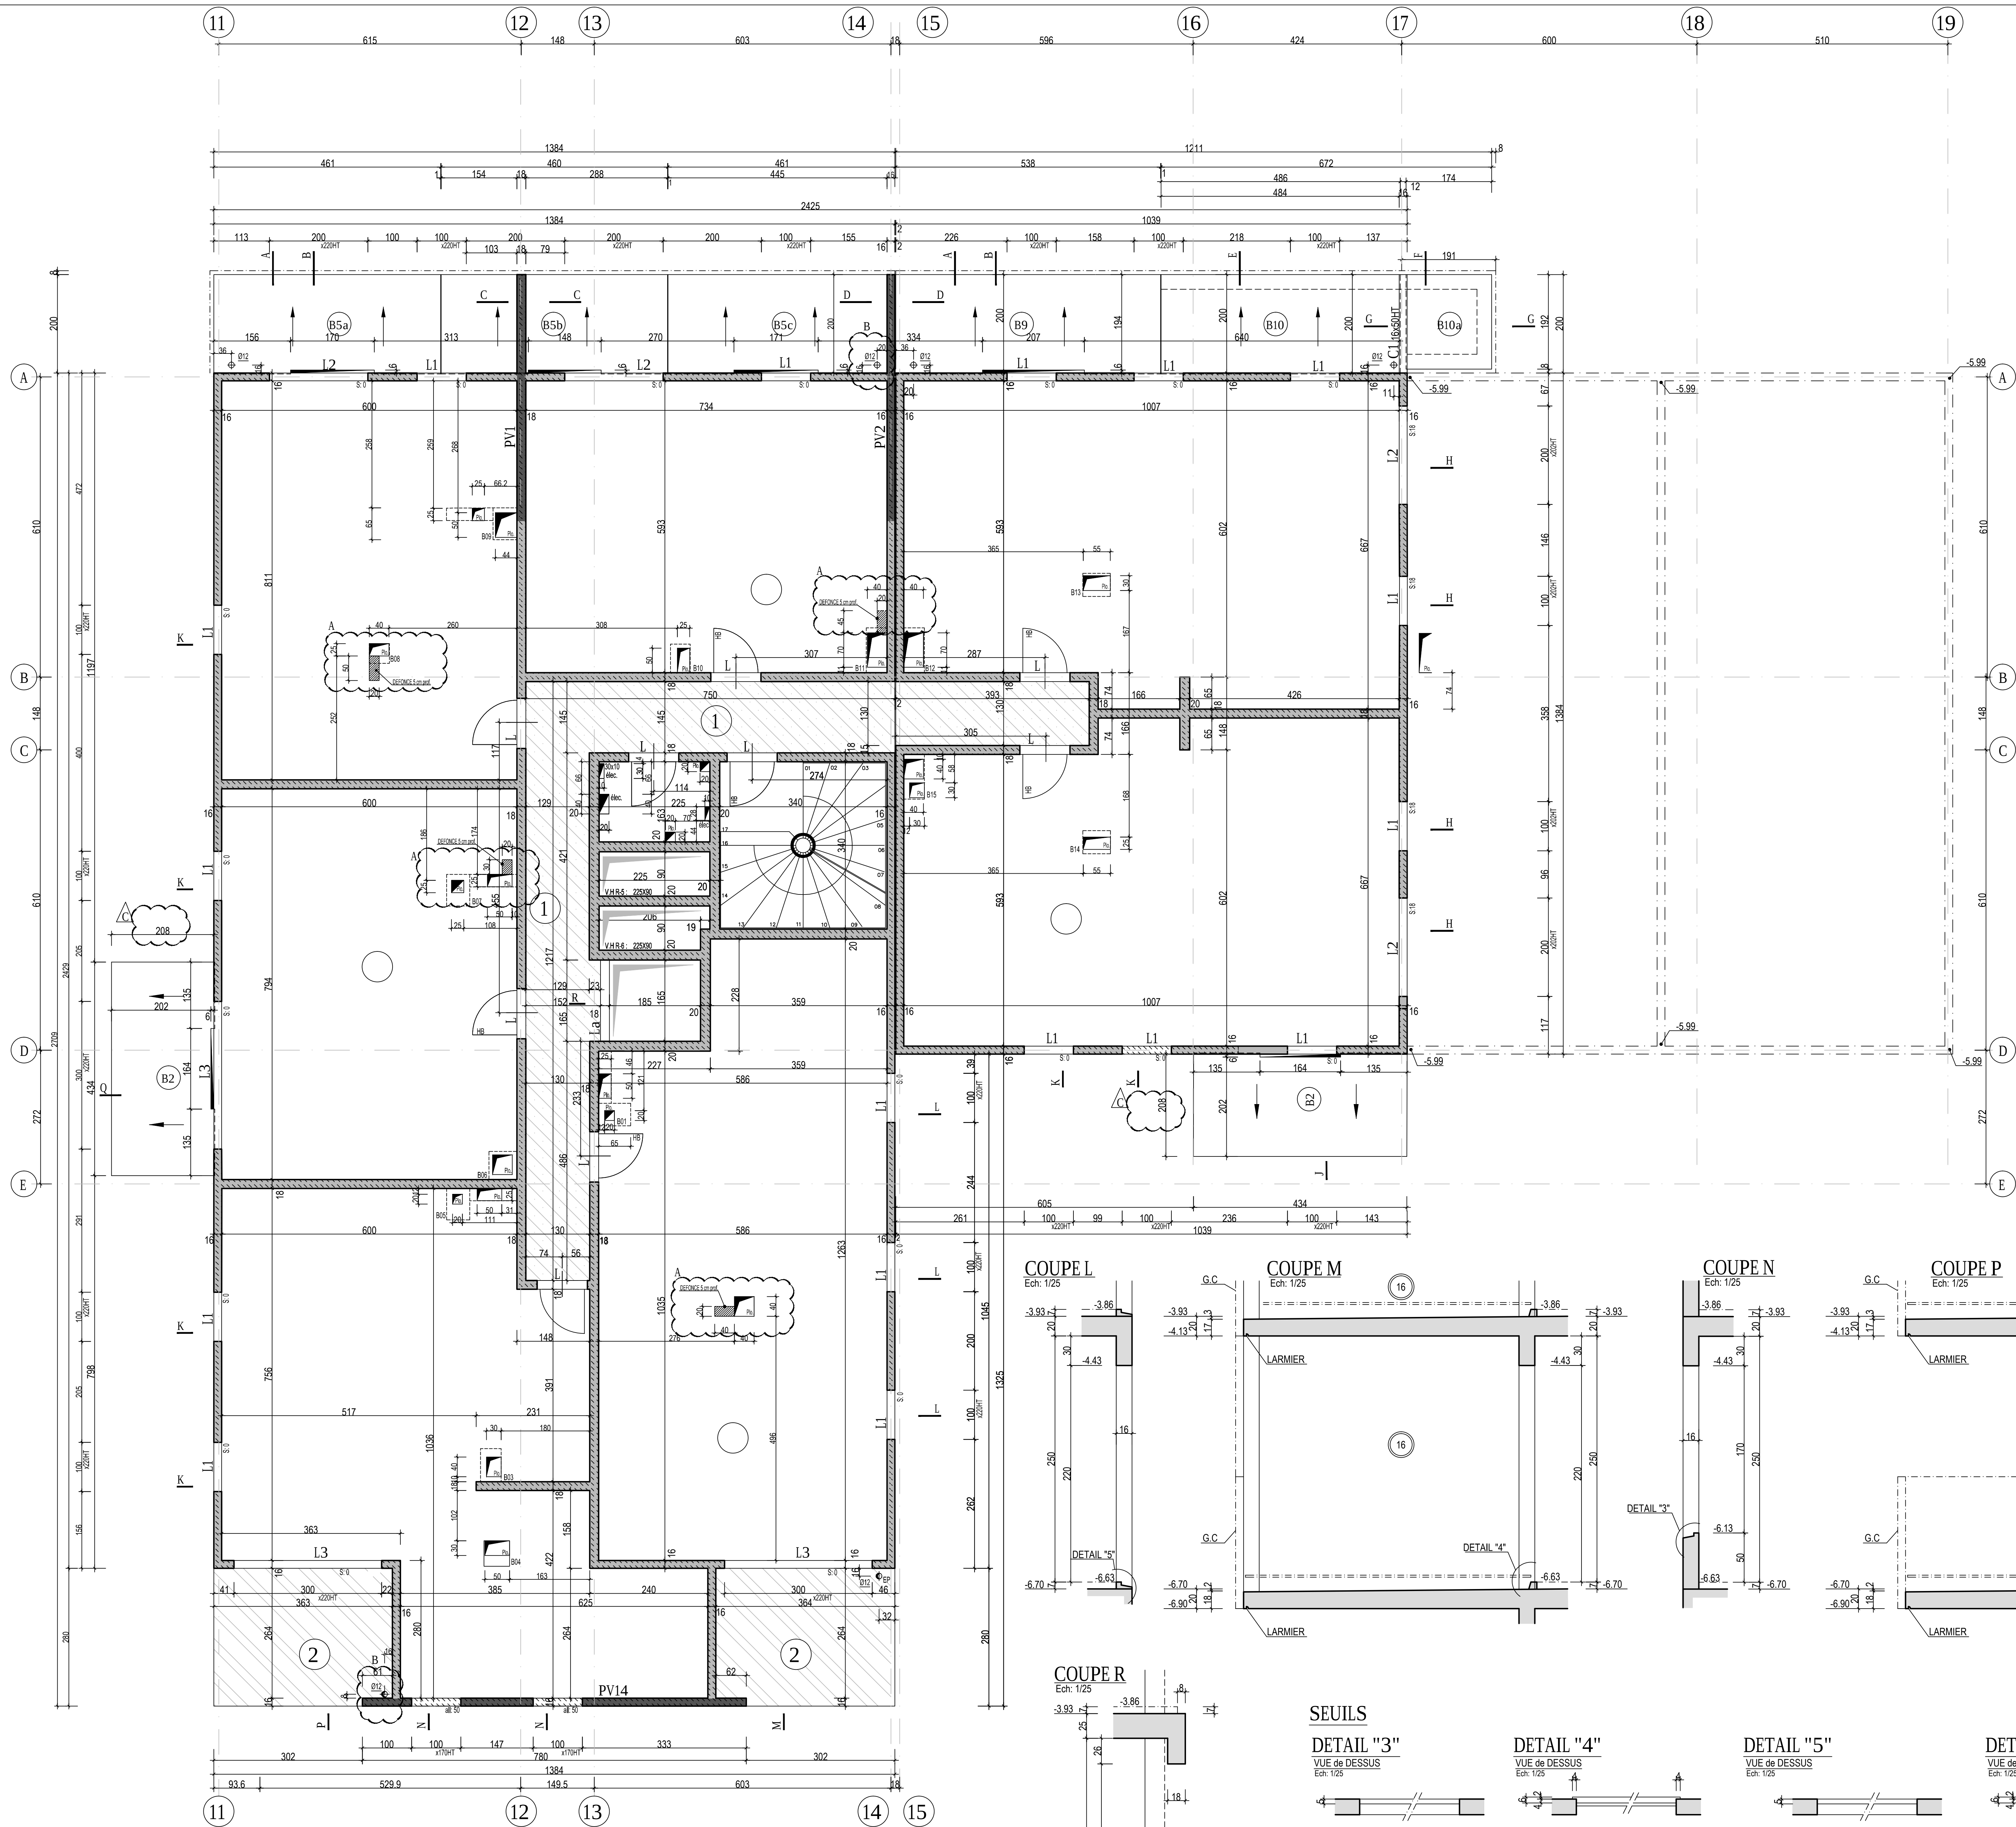

DALLES	
○ FINI: -3.86=216.64 DALLE BA Epr: 20 cm DESSUS BRUT: -3.93 RESERVE: 7 cm	① FINI: -6.63=213.87 DALLE BA Epr: 25 cm DESSUS BRUT: -6.70 RESERVE: 7 cm
② FINI: -3.79=216.71 DALLE BA Epr: 20 à 17 cm DESSUS BRUT: -3.93 à -3.96 RESERVE: 14 cm	

±0.00 = 220.50

NOAHO

Chemin de Fontanière - 69350 La Mulatière

Création de logements

Les entreprises réalisant les travaux devront tenir compte des derniers plans architectes lors de la réalisation des travaux

Les plans du **BATTE** ne doivent servir qu'au corps d'état concerné et doivent être des plans d'exécution

ARCHITECTES: ATELIER DE LA PASSERELLE

MO DELÉGUE: MATTE SAS

RESTRUCTURE: MISE

RETRAIRES: PRELEM

ECONOMISTE: EXECO

BUREAU DE CONTRÔLE: Bureau VERITAS

MO DELÉGUE: PSO Ingénierie

CSFB: SUD EST COORDINATION

OPC: ENTREPRISES: Fontanel-pbc

Bât: B

PLANCHER sur -2

Coffrage

DOE

Contrainte de sol

INDICE	DATE	MODIFICATIONS
A	10/12/2015	AJOUTE DEFONCE DANS S.d.B suivant A
B	13/01/2016	MISE A JOUR EP
C	19/01/2016	MISE A JOUR LARGEURS BALCONS ISOLÉS

MATTÉ

BUREAU D'ETUDES

STRUCTURES ET FLUIDES

119 SOLLECHARD STRASBOURG 67000 VILLERMANNE

Tel: 04 72 44 02 87 Fax: 04 72 44 28 99

Email: bat@matte.fr

Destiné par: J BO

Contrôle par: P LIN

Echelle: 1/50"

PLAN N° B28 A

DATE: 19/11/2015

Affaire N° 13.12.119