

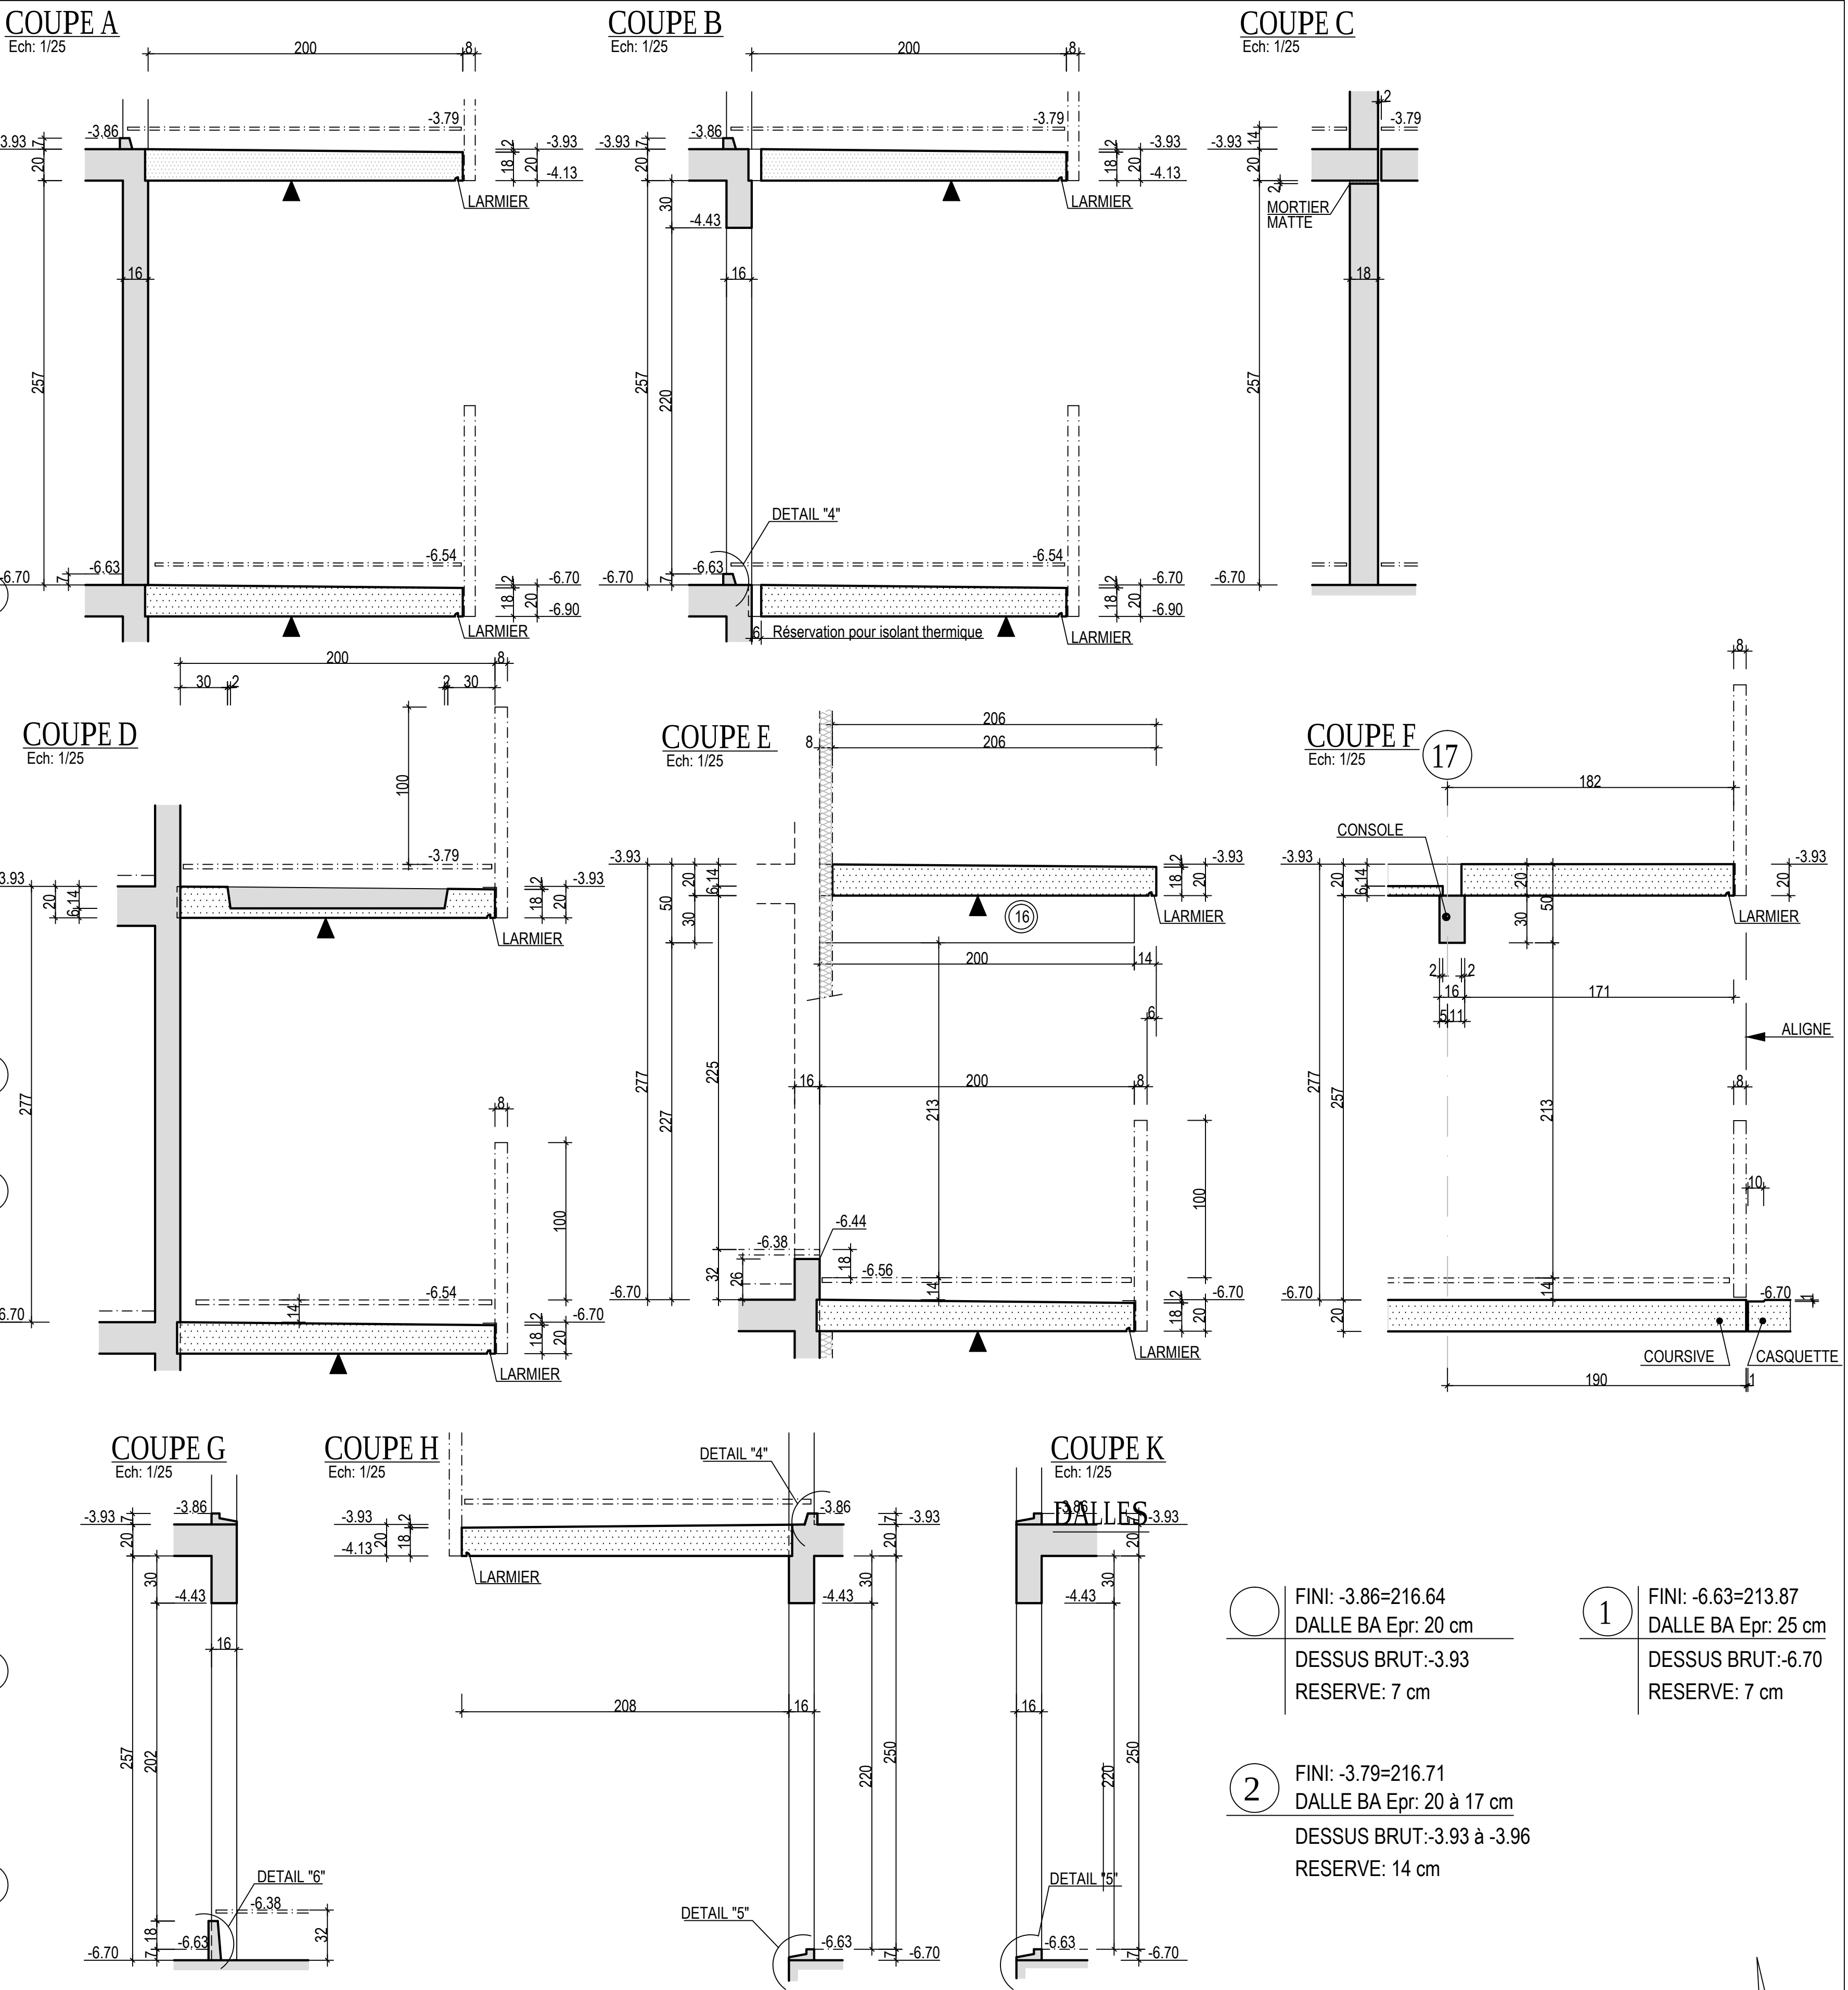


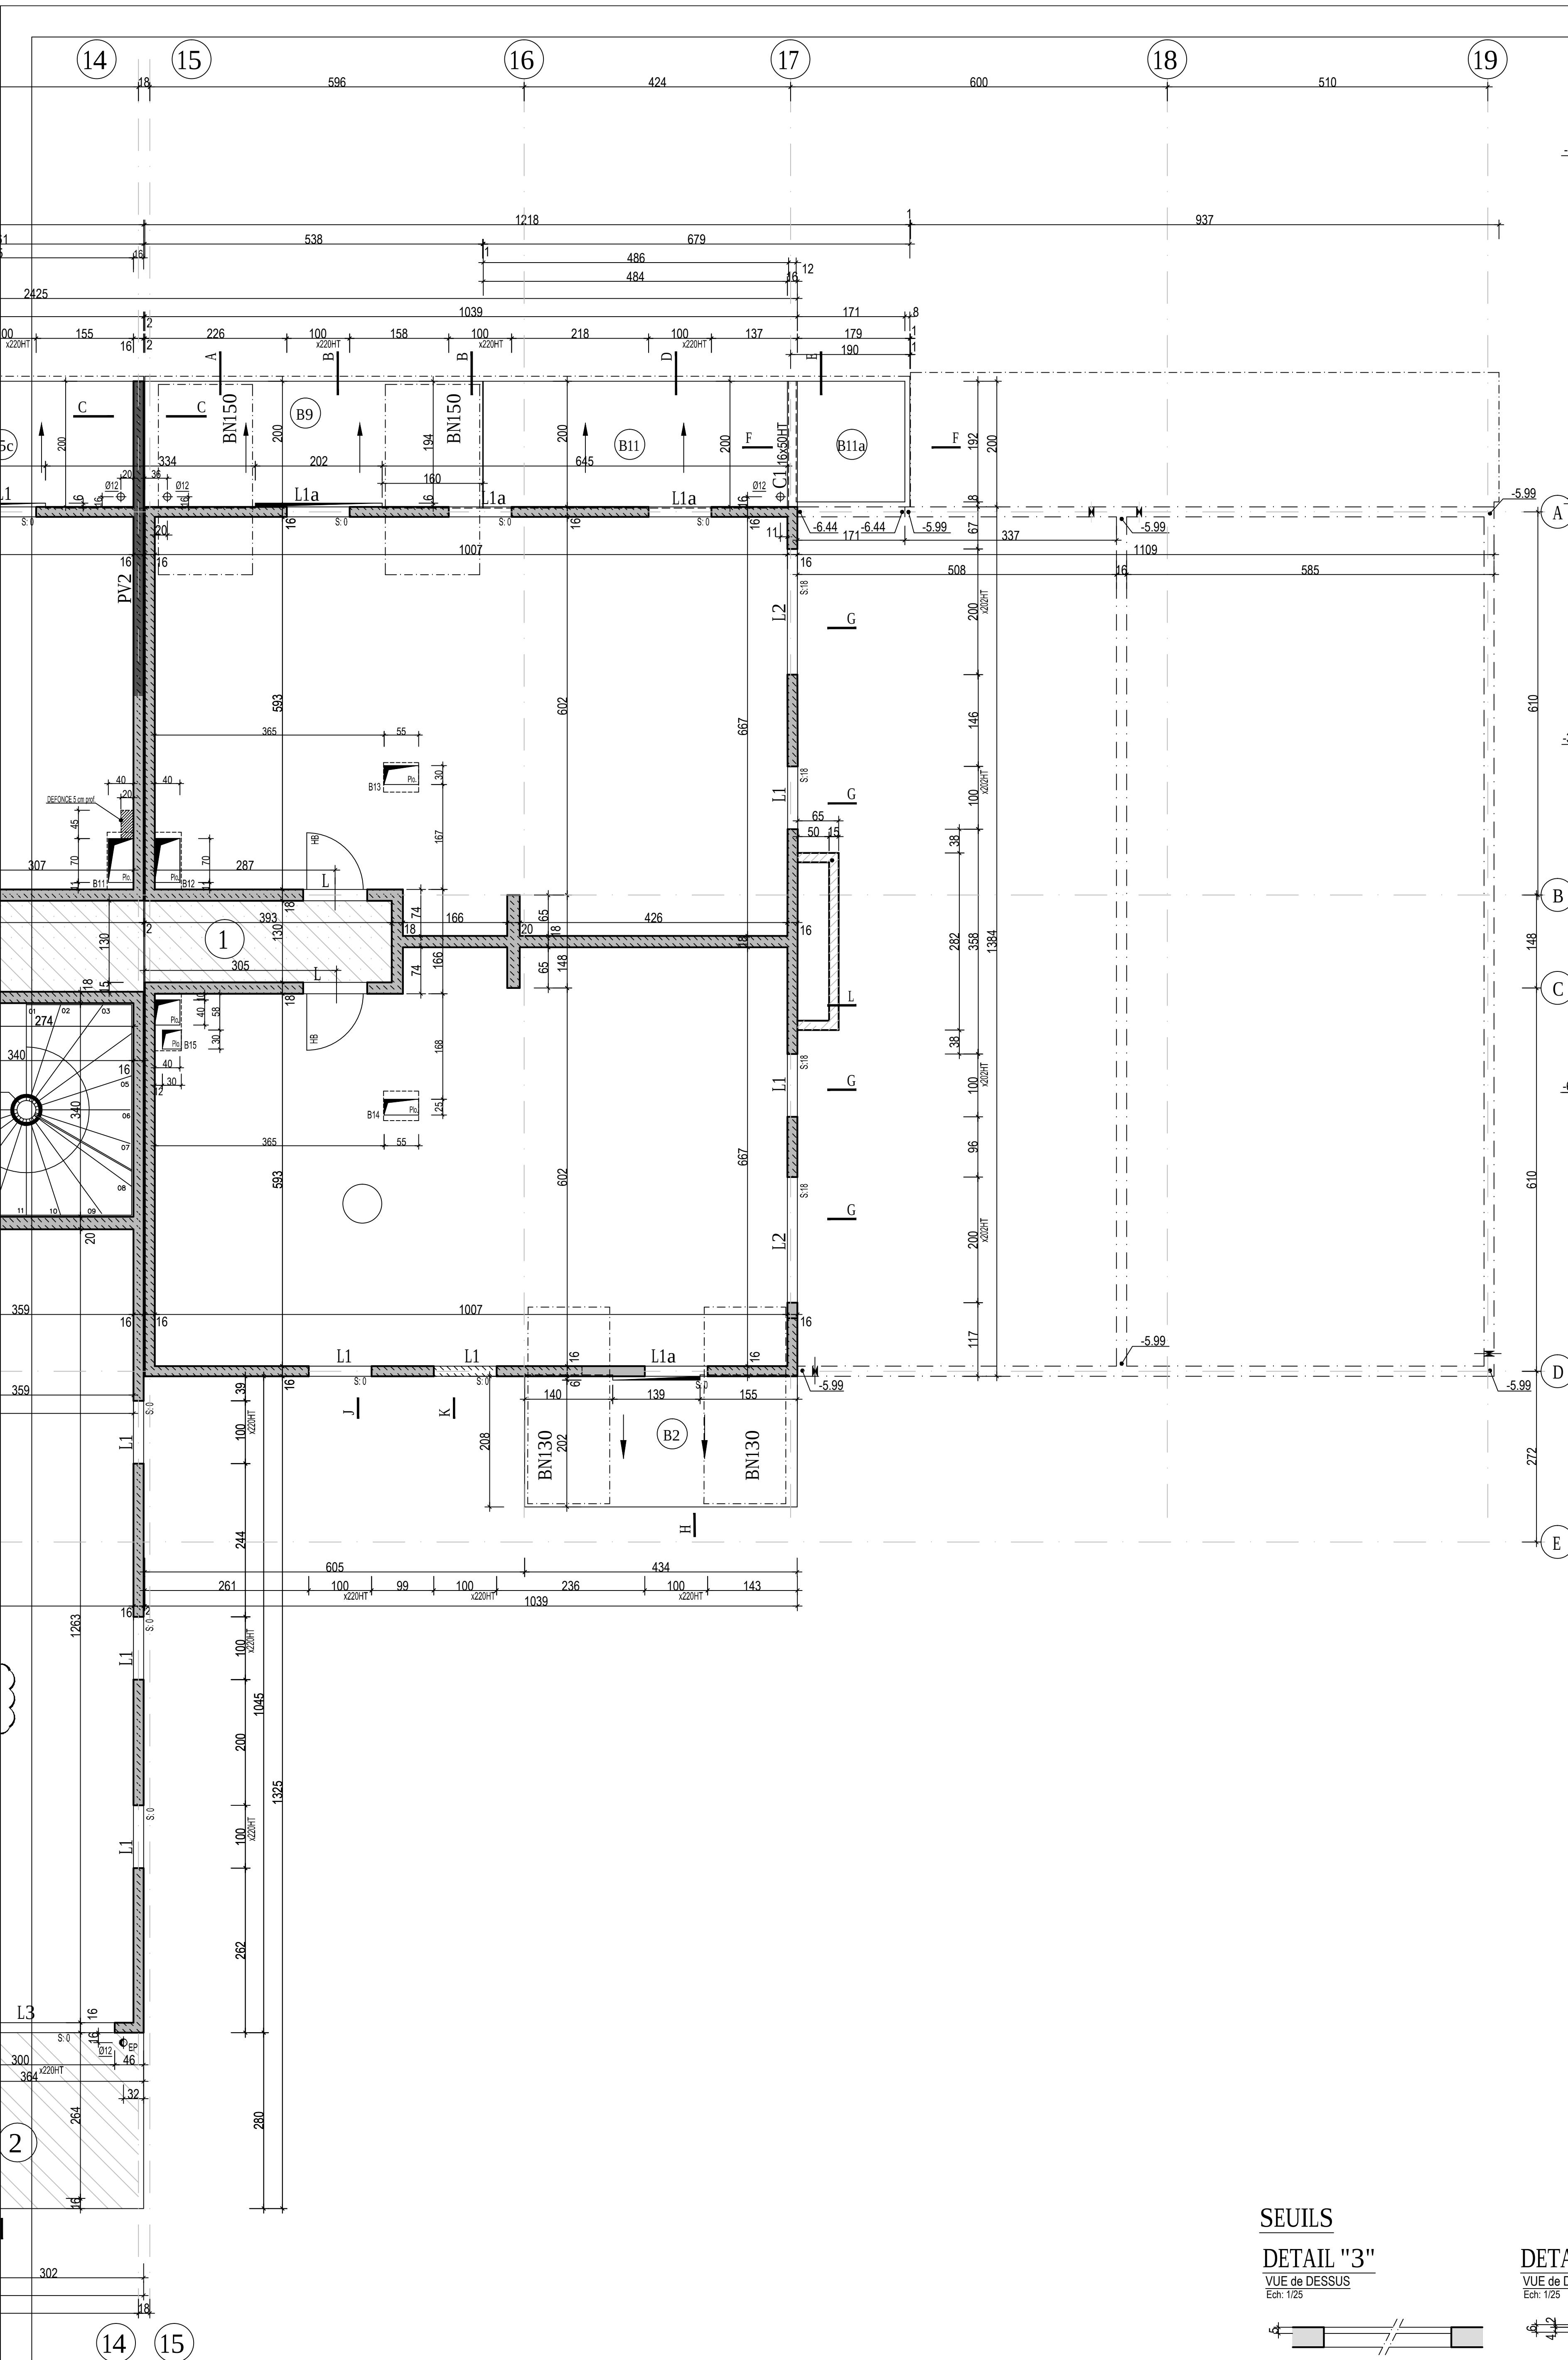


±0.00 = 220.50

SEUILS


DETAIL "3"
VUE de DESSUS
Ech: 1/25

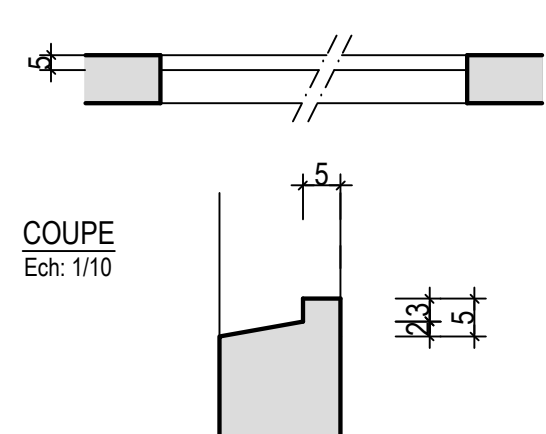


DETAIL "4"
VUE de DESSUS
Ech: 1/25

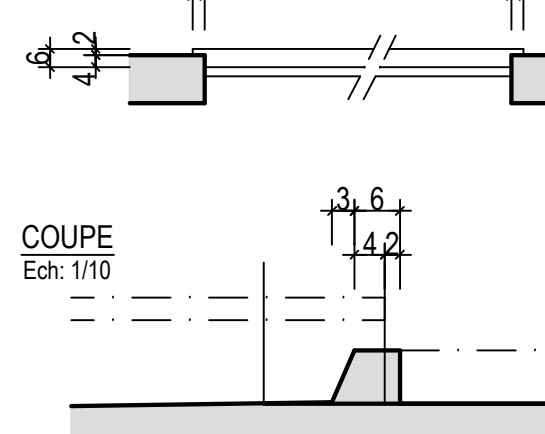

DETAIL "5"
VUE de DESSUS
Ech: 1/25

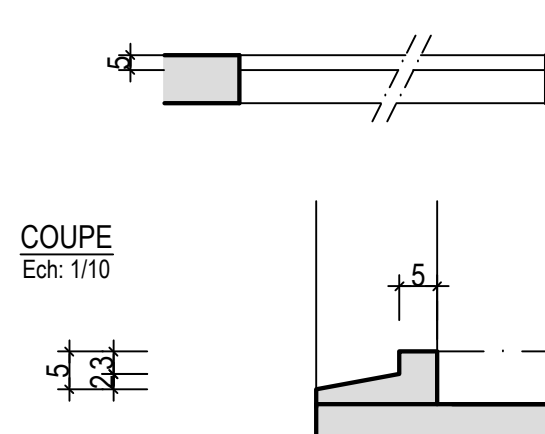

DETAIL "6"
VUE de DESSUS
Ech: 1/25

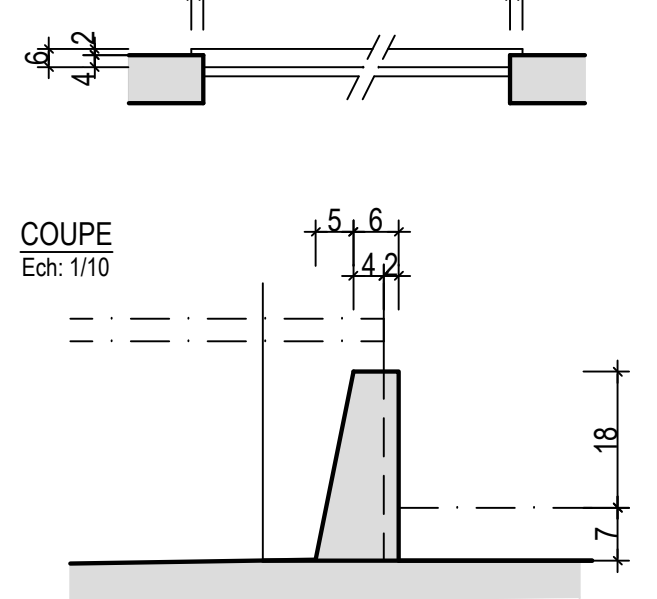

NOAHO

Chemin de Fontanière - 69350 La Mulatière
Création de logements

Les entreprises réalisant les travaux devront tenir compte des derniers plans architectes lors de la réalisation des travaux Les plans du bt MATTE ne doivent servir qu'au corps d'état concerné et doivent être des plans d'exécution		
ARCHITECTES:	ATELIER DE LA PASSERELLE	MO DELEGUE:
BET STRUCTURE:	MATTE SAS	MSE:
BET FLUIDES:	PRELEM	CSPS:
ECONOMISTE:	EXECO	OPC:
BUREAU DE CONTRÔLE:	Bureau VERITAS	ENTREPREISES:

Bât B
PLANCHER sur -2 entre files 14 ET 19
Coffrage

INDICE	DATE	MODIFICATIONS
A	31/03/2016	MISE A JOUR REPERAGE ARMATURES
B	14/04/2016	AJOUTE REPERAGE PREFA

MATTE

BUREAU D'ETUDES

STRUCTURES ET FLUIDES

119 RUE LEONARD ETLINGHOFF 69100 VILLEURBANNE

Tel : 04 72 44 12 87 Fax 04 72 44 26 59

E-mail : mat@matte.fr

Dessiné par : J. BO

Contrôlé par : P. L. N.

Echelle : 1/150"

DOE

Contrainte de sol DOE

PLAN N°

B29 A

DATE : 29/03/2016

Affaire N°

13.12.119