

NOHAO

Chemin de Fontanière-69350 La Mulatière

Création de logements

Les entreprises réalisant les travaux devront tenir compte des derniers plans architecte lors de la réalisation des travaux
Les plans du be MATTE ne doivent servir qu'au corps d'état concerné et doivent être des plans d'exécution.

ARCHITECTE(S): Atelier DE LA PASSERELLE
BET STRUCTURE: BET MATTE
BET FLUIDES: PRELEM
ECONOMISTE: EXECO
BUREAU DE CONTROLE: VERITAS

M.O. Délégué: .
M.O.: .
CSPS: PSO ingénierie
M.O.E.: SUD EST COORDINATION
ENTREPRISE(S): Fontanel-pbc

Bât: B
BA au -2 entre files 11 et 14

DOE

INDICE	DATE	MODIFICATIONS
--------	------	---------------

A		

Aciers HA (T) FeE500
Aciers Doux (Ø) FeE 235
Aciers TS FeE 500
Béton fc28 >= 25MPa
Enrobage = 3 cm

**PLAN N°
B30 0**

DATE : 10-12-2015

MATTÉ
BUREAU D'ÉTUDES
STRUCTURES ET FLUIDES


119 BOULEVARD STALINGRAD 69100 VILLEURBANNE
Tél. 04 72 44 02 87 Fax 04 72 44 26 59
E-mail : bet@matte.fr

Dessiné par : J.BONDETTI
Contrôlé par : P. LIN
Ech :

**Affaire N°
S.13.12.118**

POUTRE VOILE : PV1

2 HA 10 FILANTS
2x2.50 = 5.00 ml Env

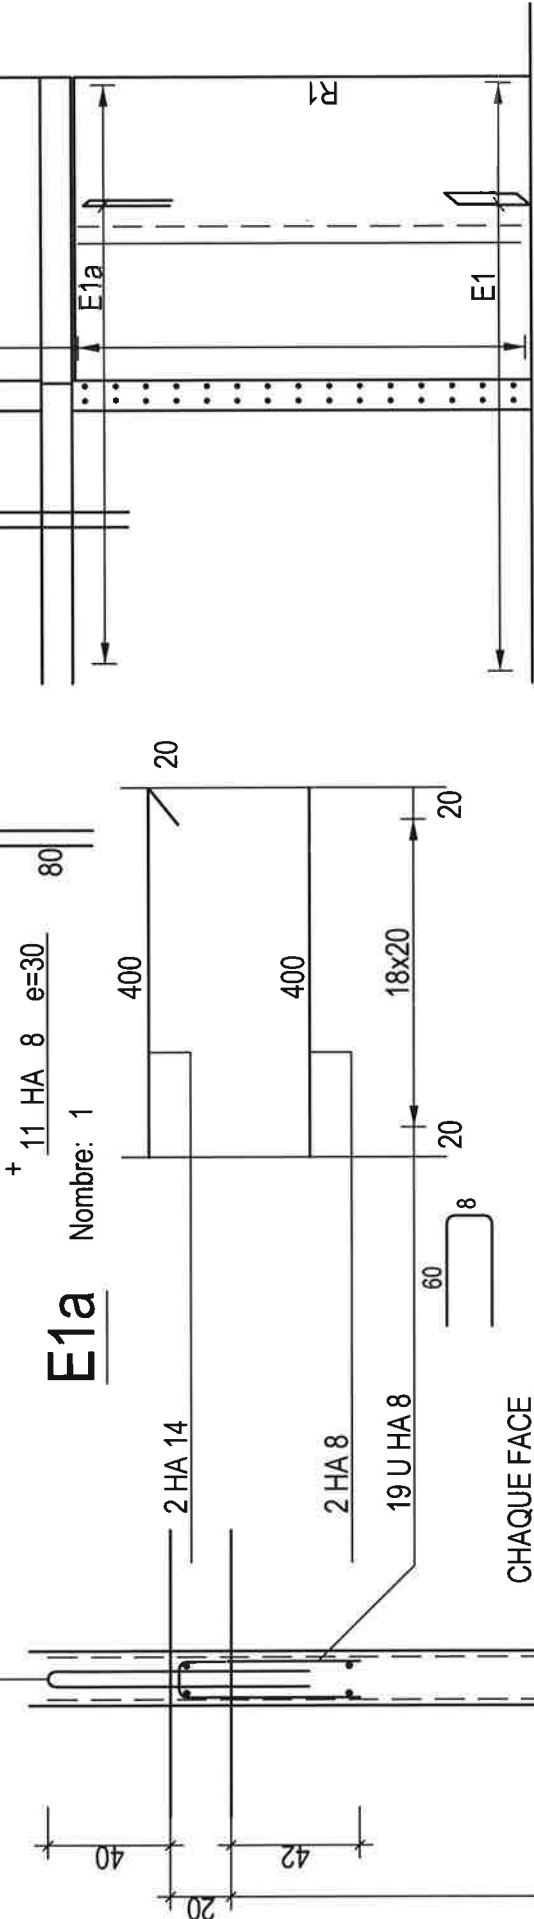


E1


Nombre: 1

R1

Nombre: 1

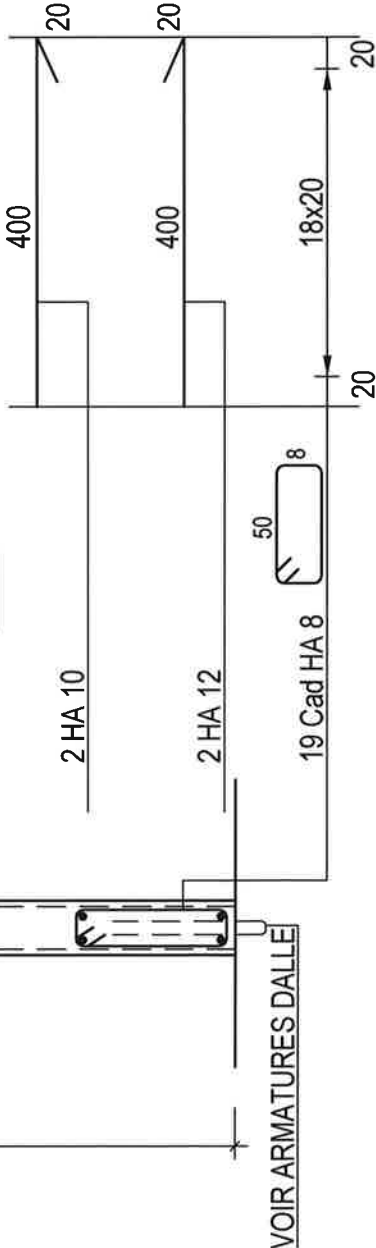

POUTRE VOILE : PV2

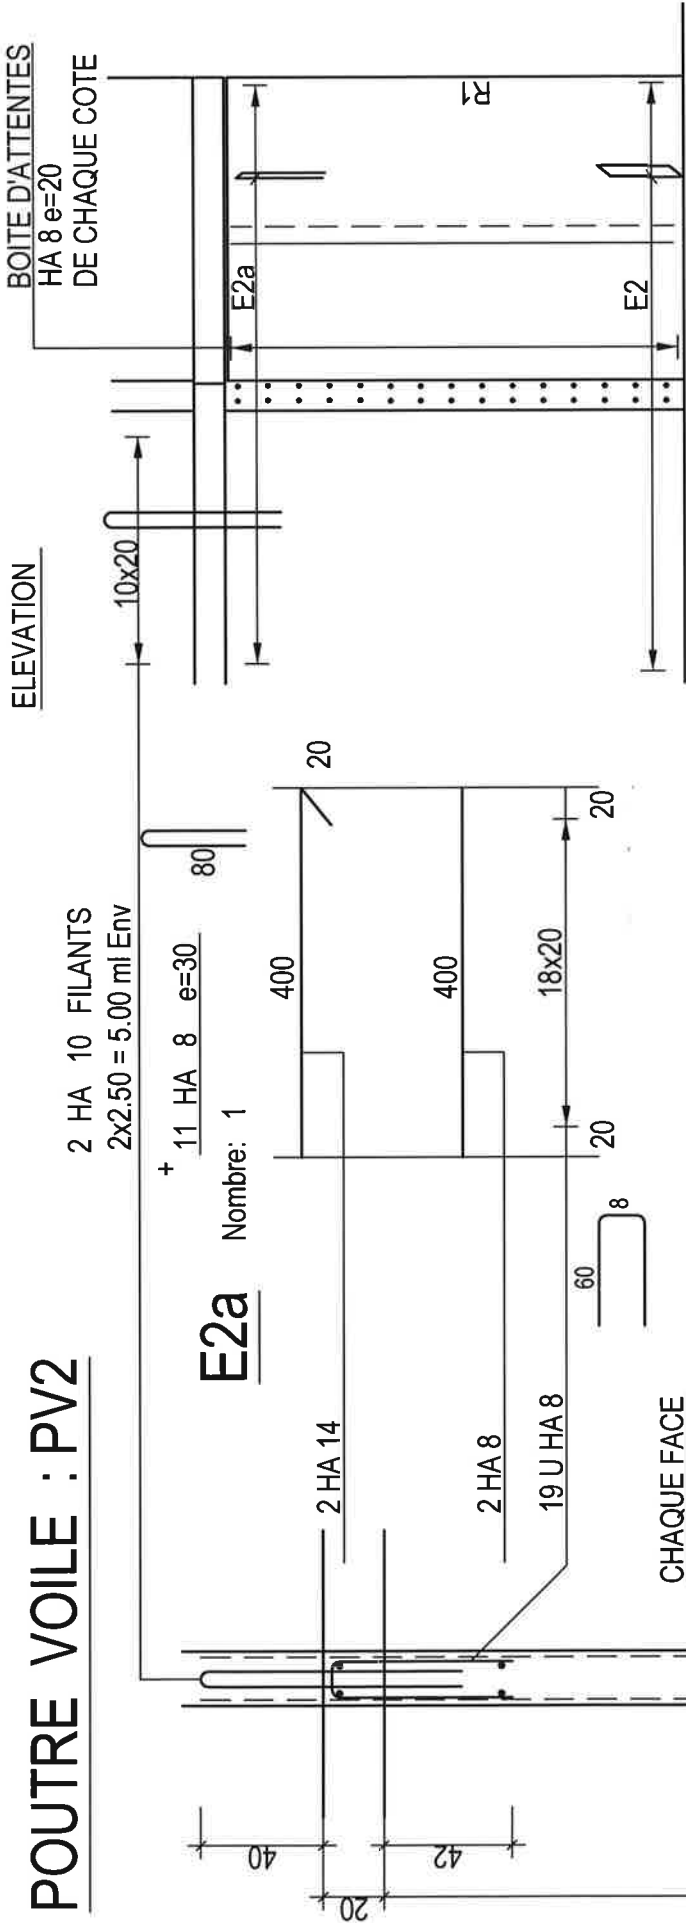


E2


Nombre: 1

R2

Nombre: 1

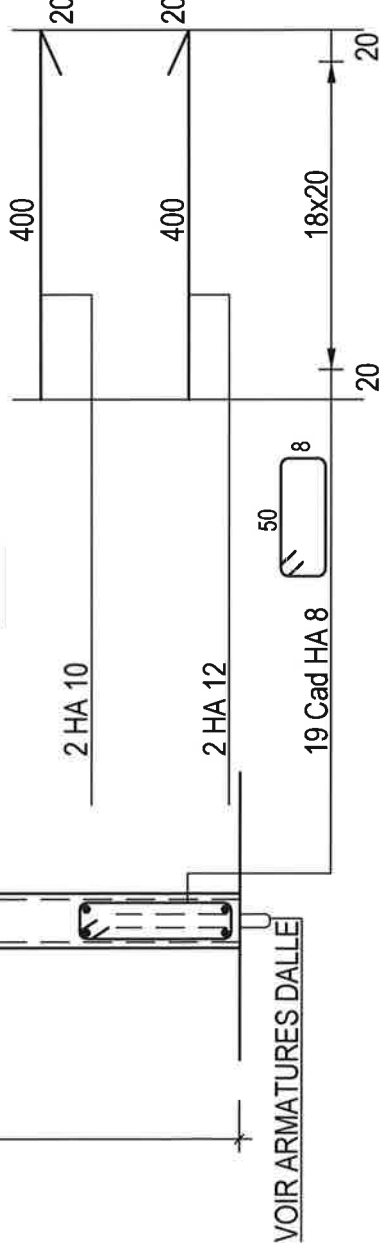

PV14

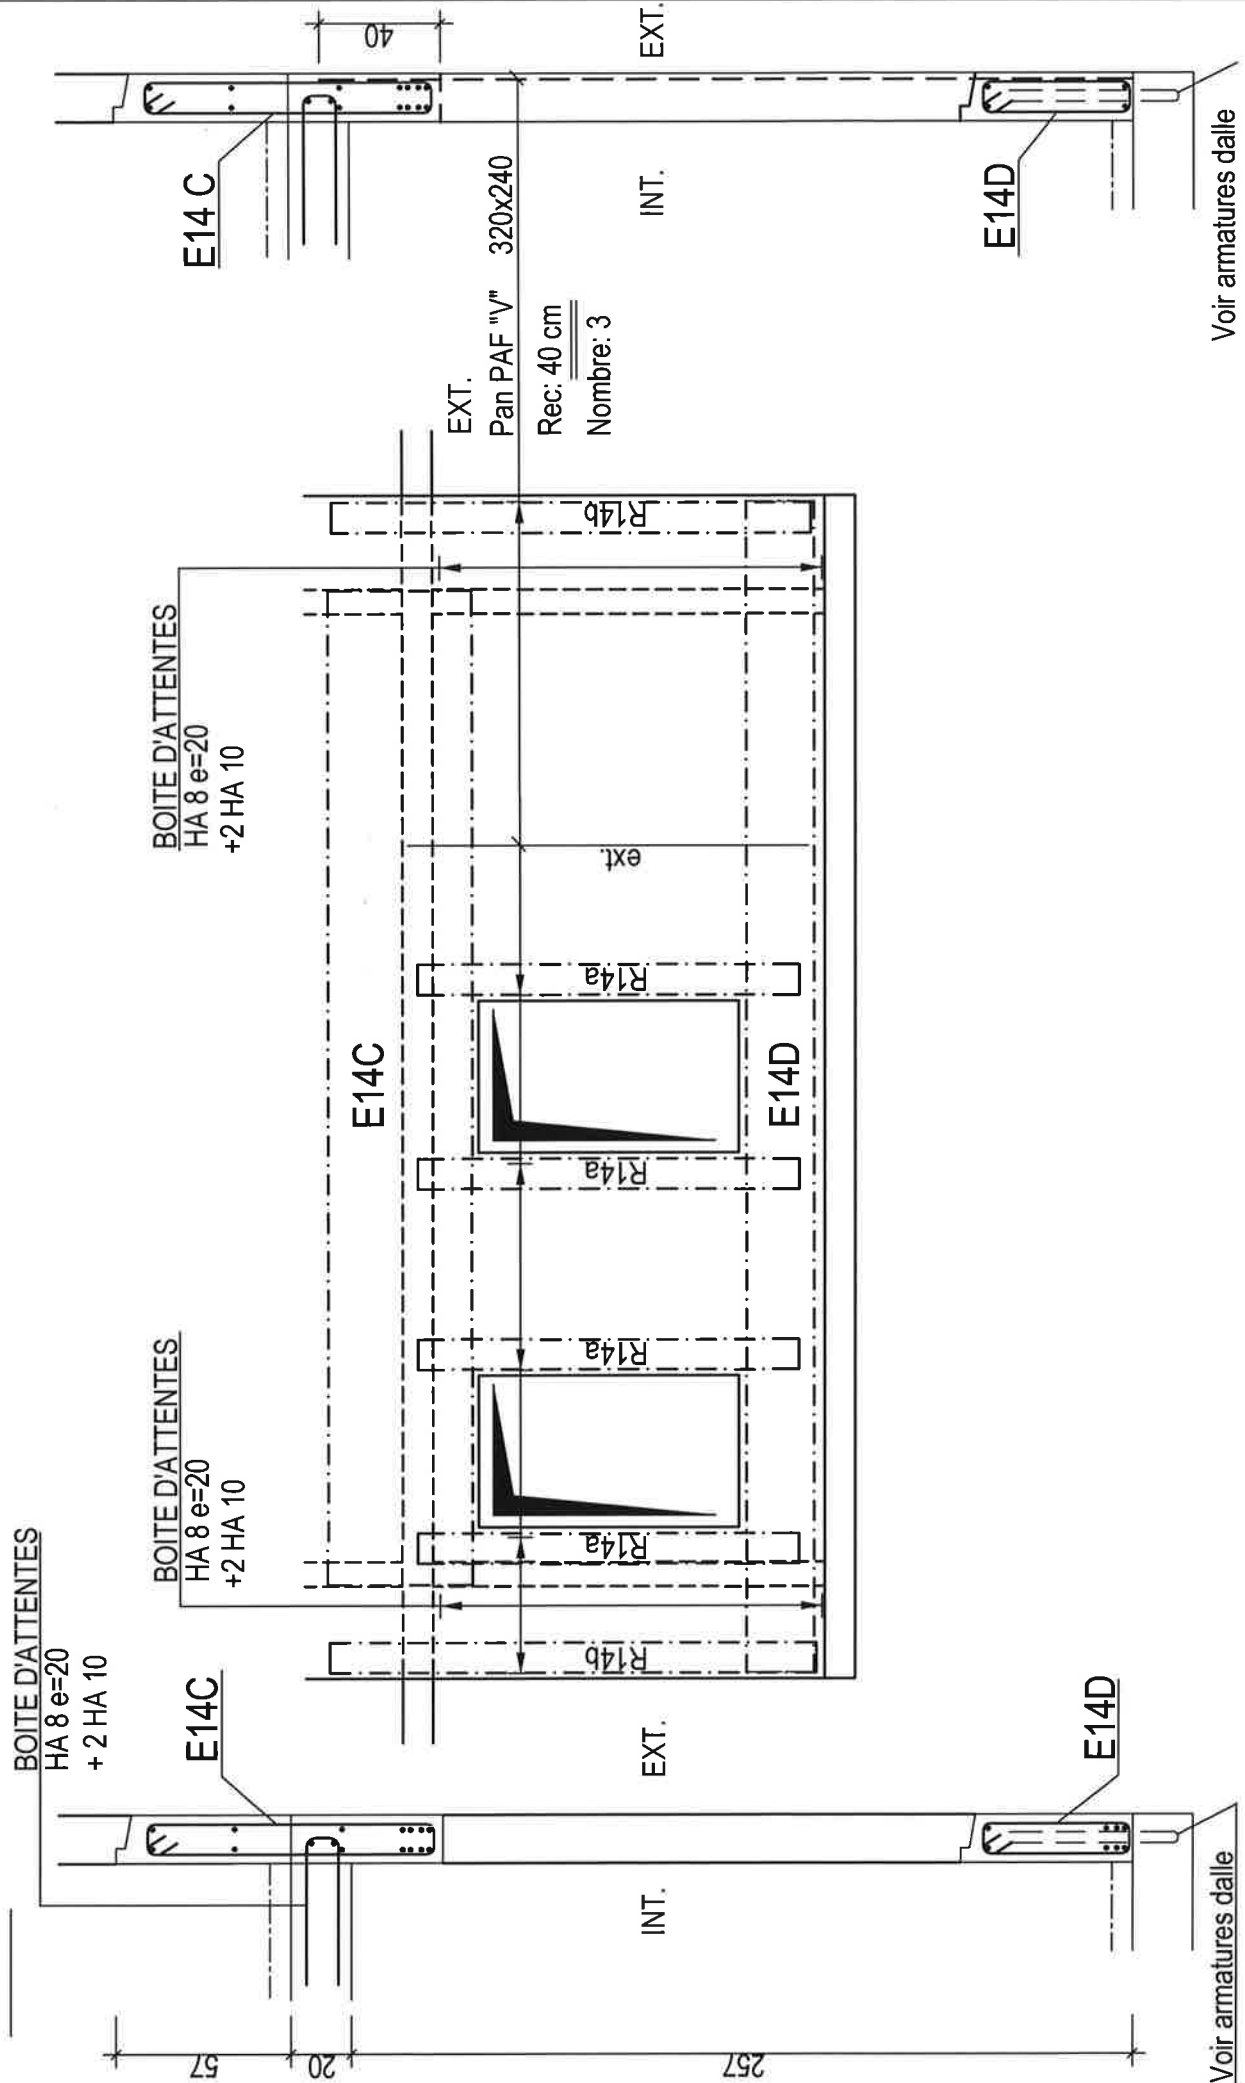


AFF: S.13.12.119	Bât: B	LA MULATIERE-69350 La Mulatiere CREATION de LOGEMENTS	BA au -2	Plan n° B 30	Page: 4
PV14	COUPE				
	R14 a				
	R14 b				


Section : 16 x 95ht


Fc28= 25 MPa Fe= 500 MPa Fissuration peu préjudiciable Coupe feu 1 H

Elévation
Echelle=1/50

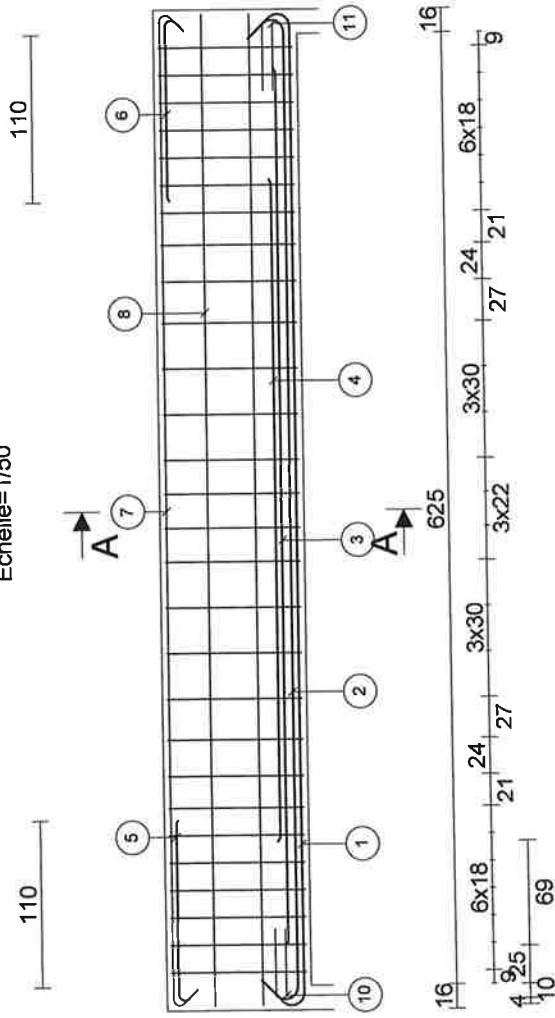

Coupe A-A
Echelle=1/20

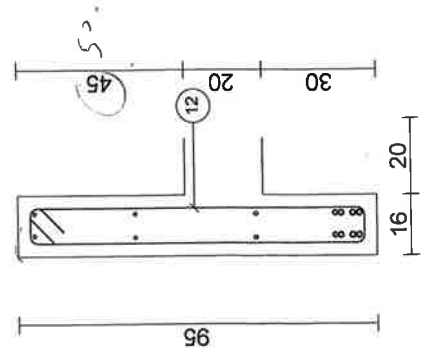

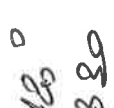Barre		Lg	Forme
1	2HA14	708	 135° 652 135°
2	2HA14	693	 135° 644 135°
3	2HA14	578	 578
4	2HA12	436	 436
5	2HA8	132	 119 135°
6	2HA8	132	 135° 119
7	2HA8	676	 135° 650 135°
8	4HA8	651	 651
9	28HA8	26	 9
10	2HA10	92	 44
11	2HA10	92	 44
12	28HA8	214	 10
			
Barre		Lg/Poids	
HA8		112.0/44.2	
HA10		3.7/2.3	
HA12		8.7/7.7	
HA14		39.6/47.8	


ARMATURES TETES DE MURS
et OUVERTURES

(VALABLE 18 fois)

ANGLES MURS

(VALABLE 3 fois)


MURS EXTERIEURS

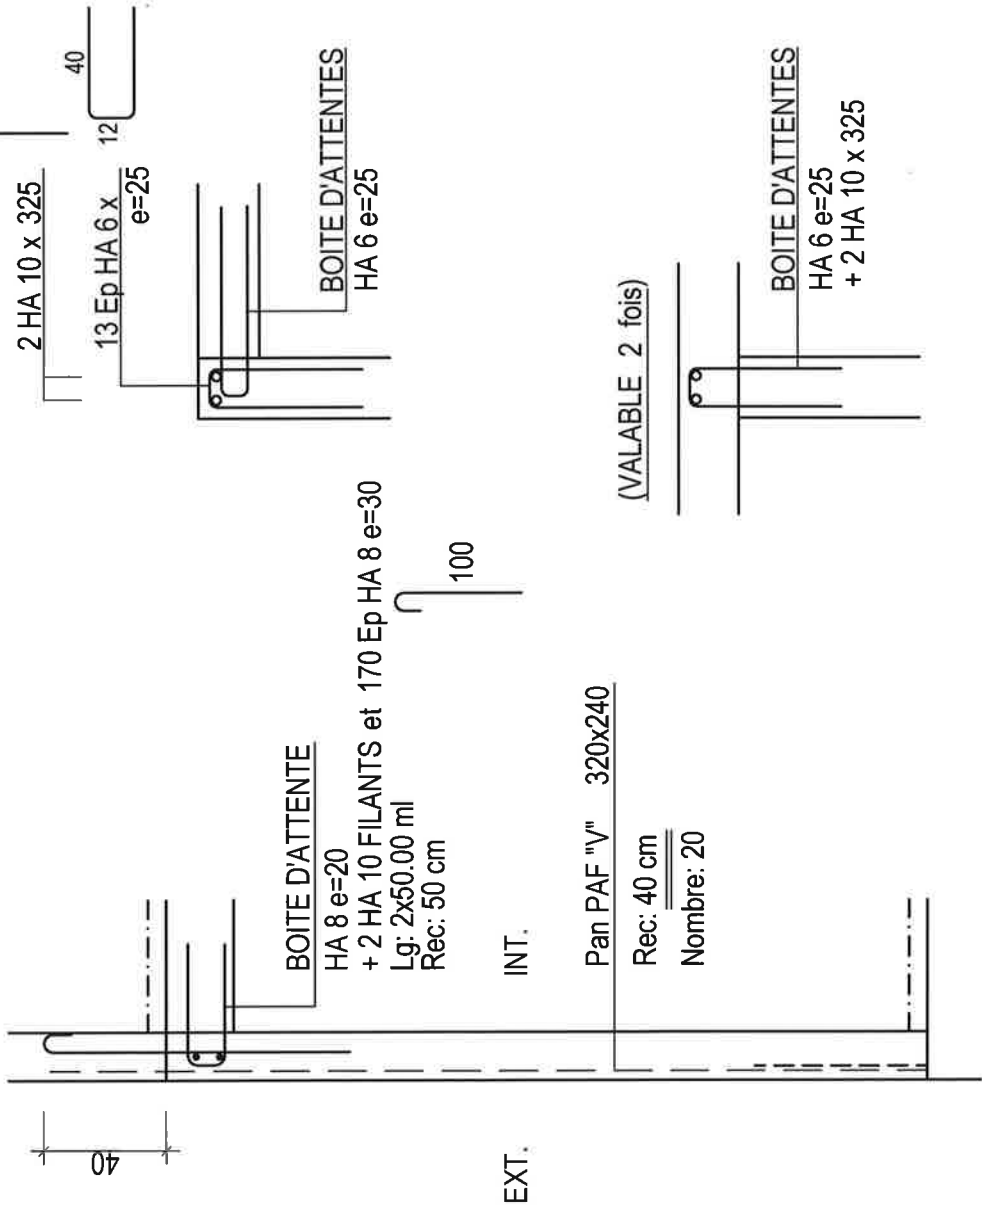


ARMATURES REJINGOT

(VALABLE 1 fois)


A COUPER SUIVANT OUVERTURES

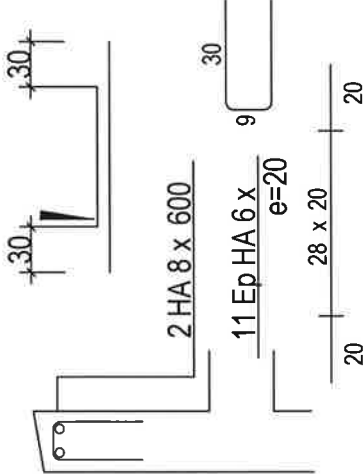


MURS INTERIEURS AVEC CONTINUITE

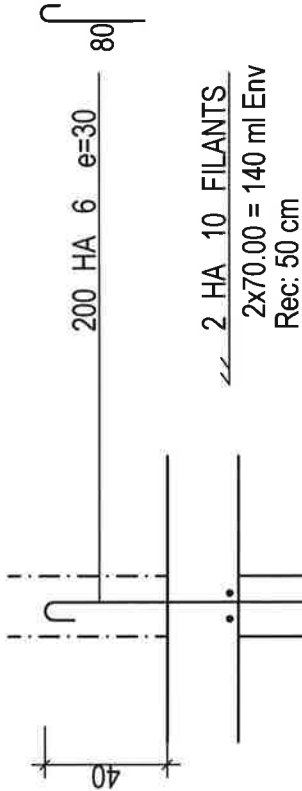


ARMATURES TETES DE MURS

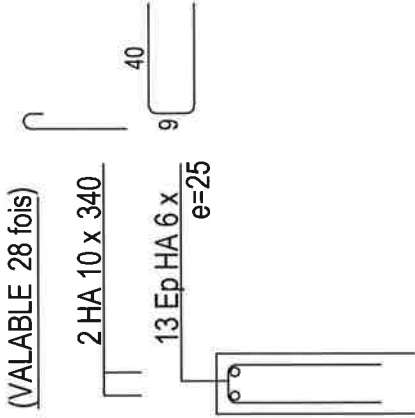

ANGLES MURS

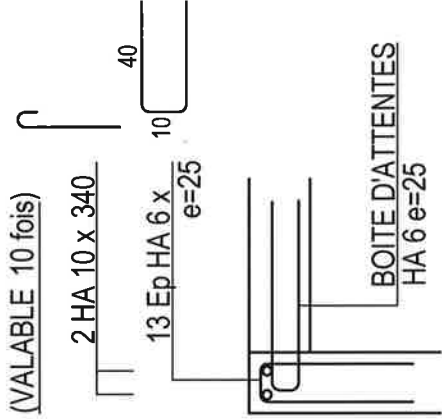


BOITE D'ATTENTES
HA 6 e=25
+ 2 HA 10 x 340

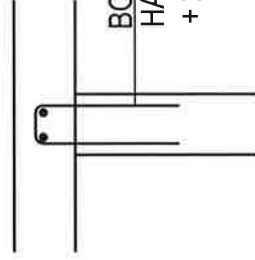


LINTEAUX INT.

L Nombre: 6

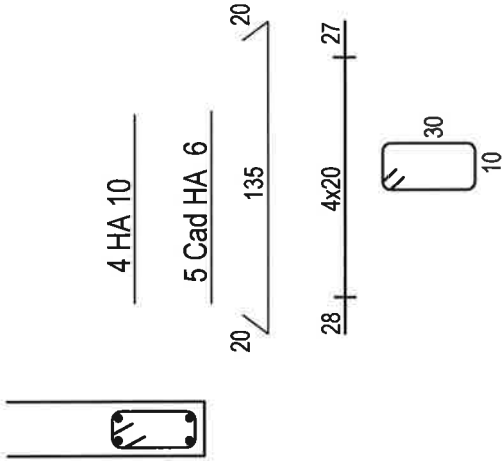


La Nombre: 1

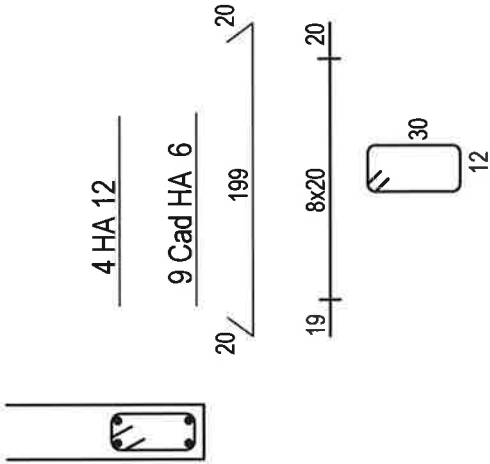

LINTEAUX EXT. L1

Nombre: ~~10~~ 9
PORTEE: 100

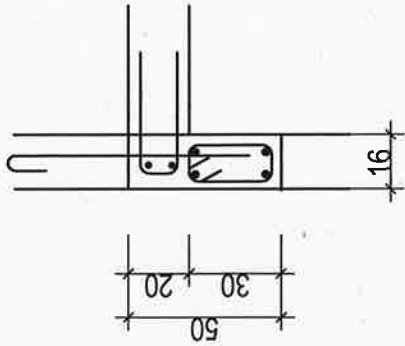

2 HA 10


2 HA 10

5 Cad HA 6



LINTEAUX EXT. L3

Nombre: 2
PORTEE: 300

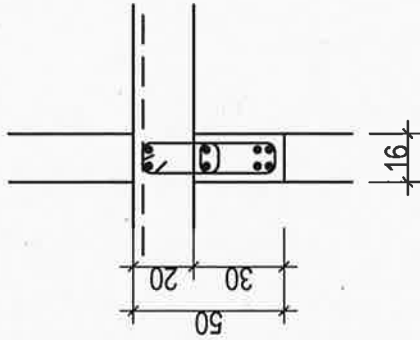

2 HA 10

2 HA 8

2 HA 16 x 300 AXES

2 HA 16

15 Cad HA 6

15 Ep HA 6

