



ARMATURES INFÉRIEURES

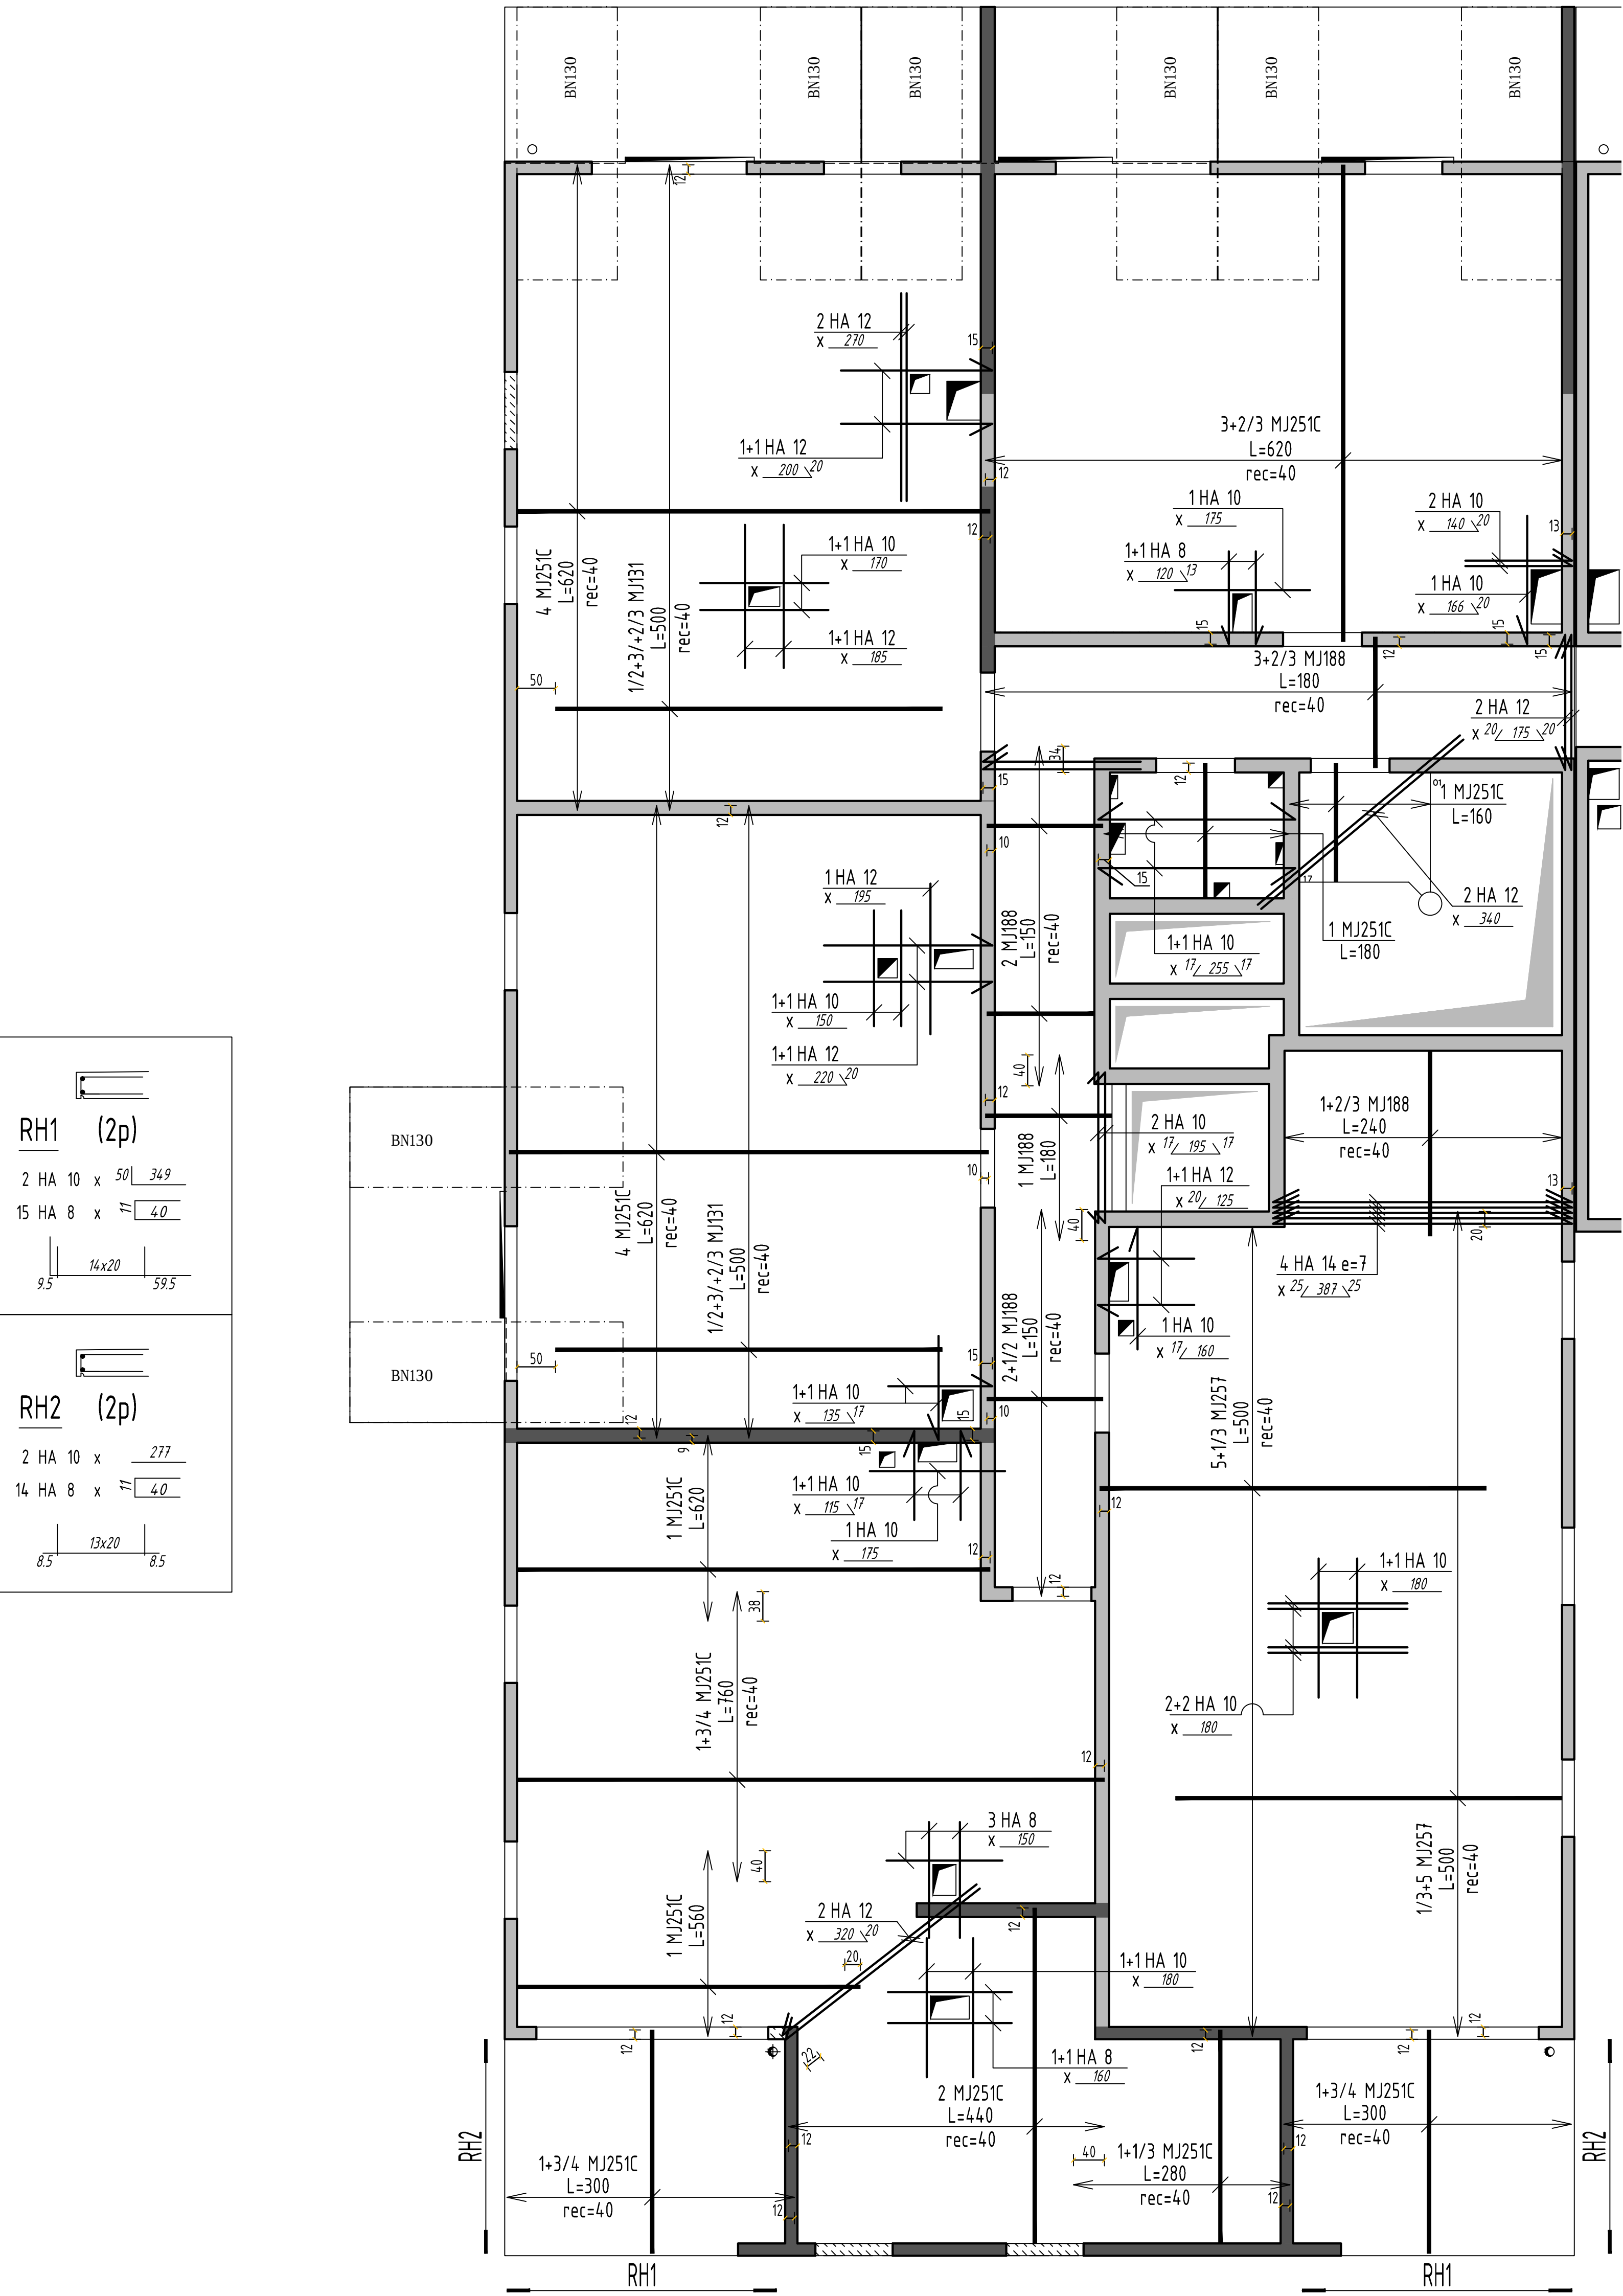

TREILLIS INF DES DALLES

Trellis	Lgr (cm)	Nbr
MJ131	500	9
MJ188	150	4+1/2
	180	5
	240	2
MJ251C	180	1
	280	1+1/2
	300	4
	440	2
	560	1
	620	13
	760	2
MJ257	500	11

ARMATURES SUPÉRIEURES

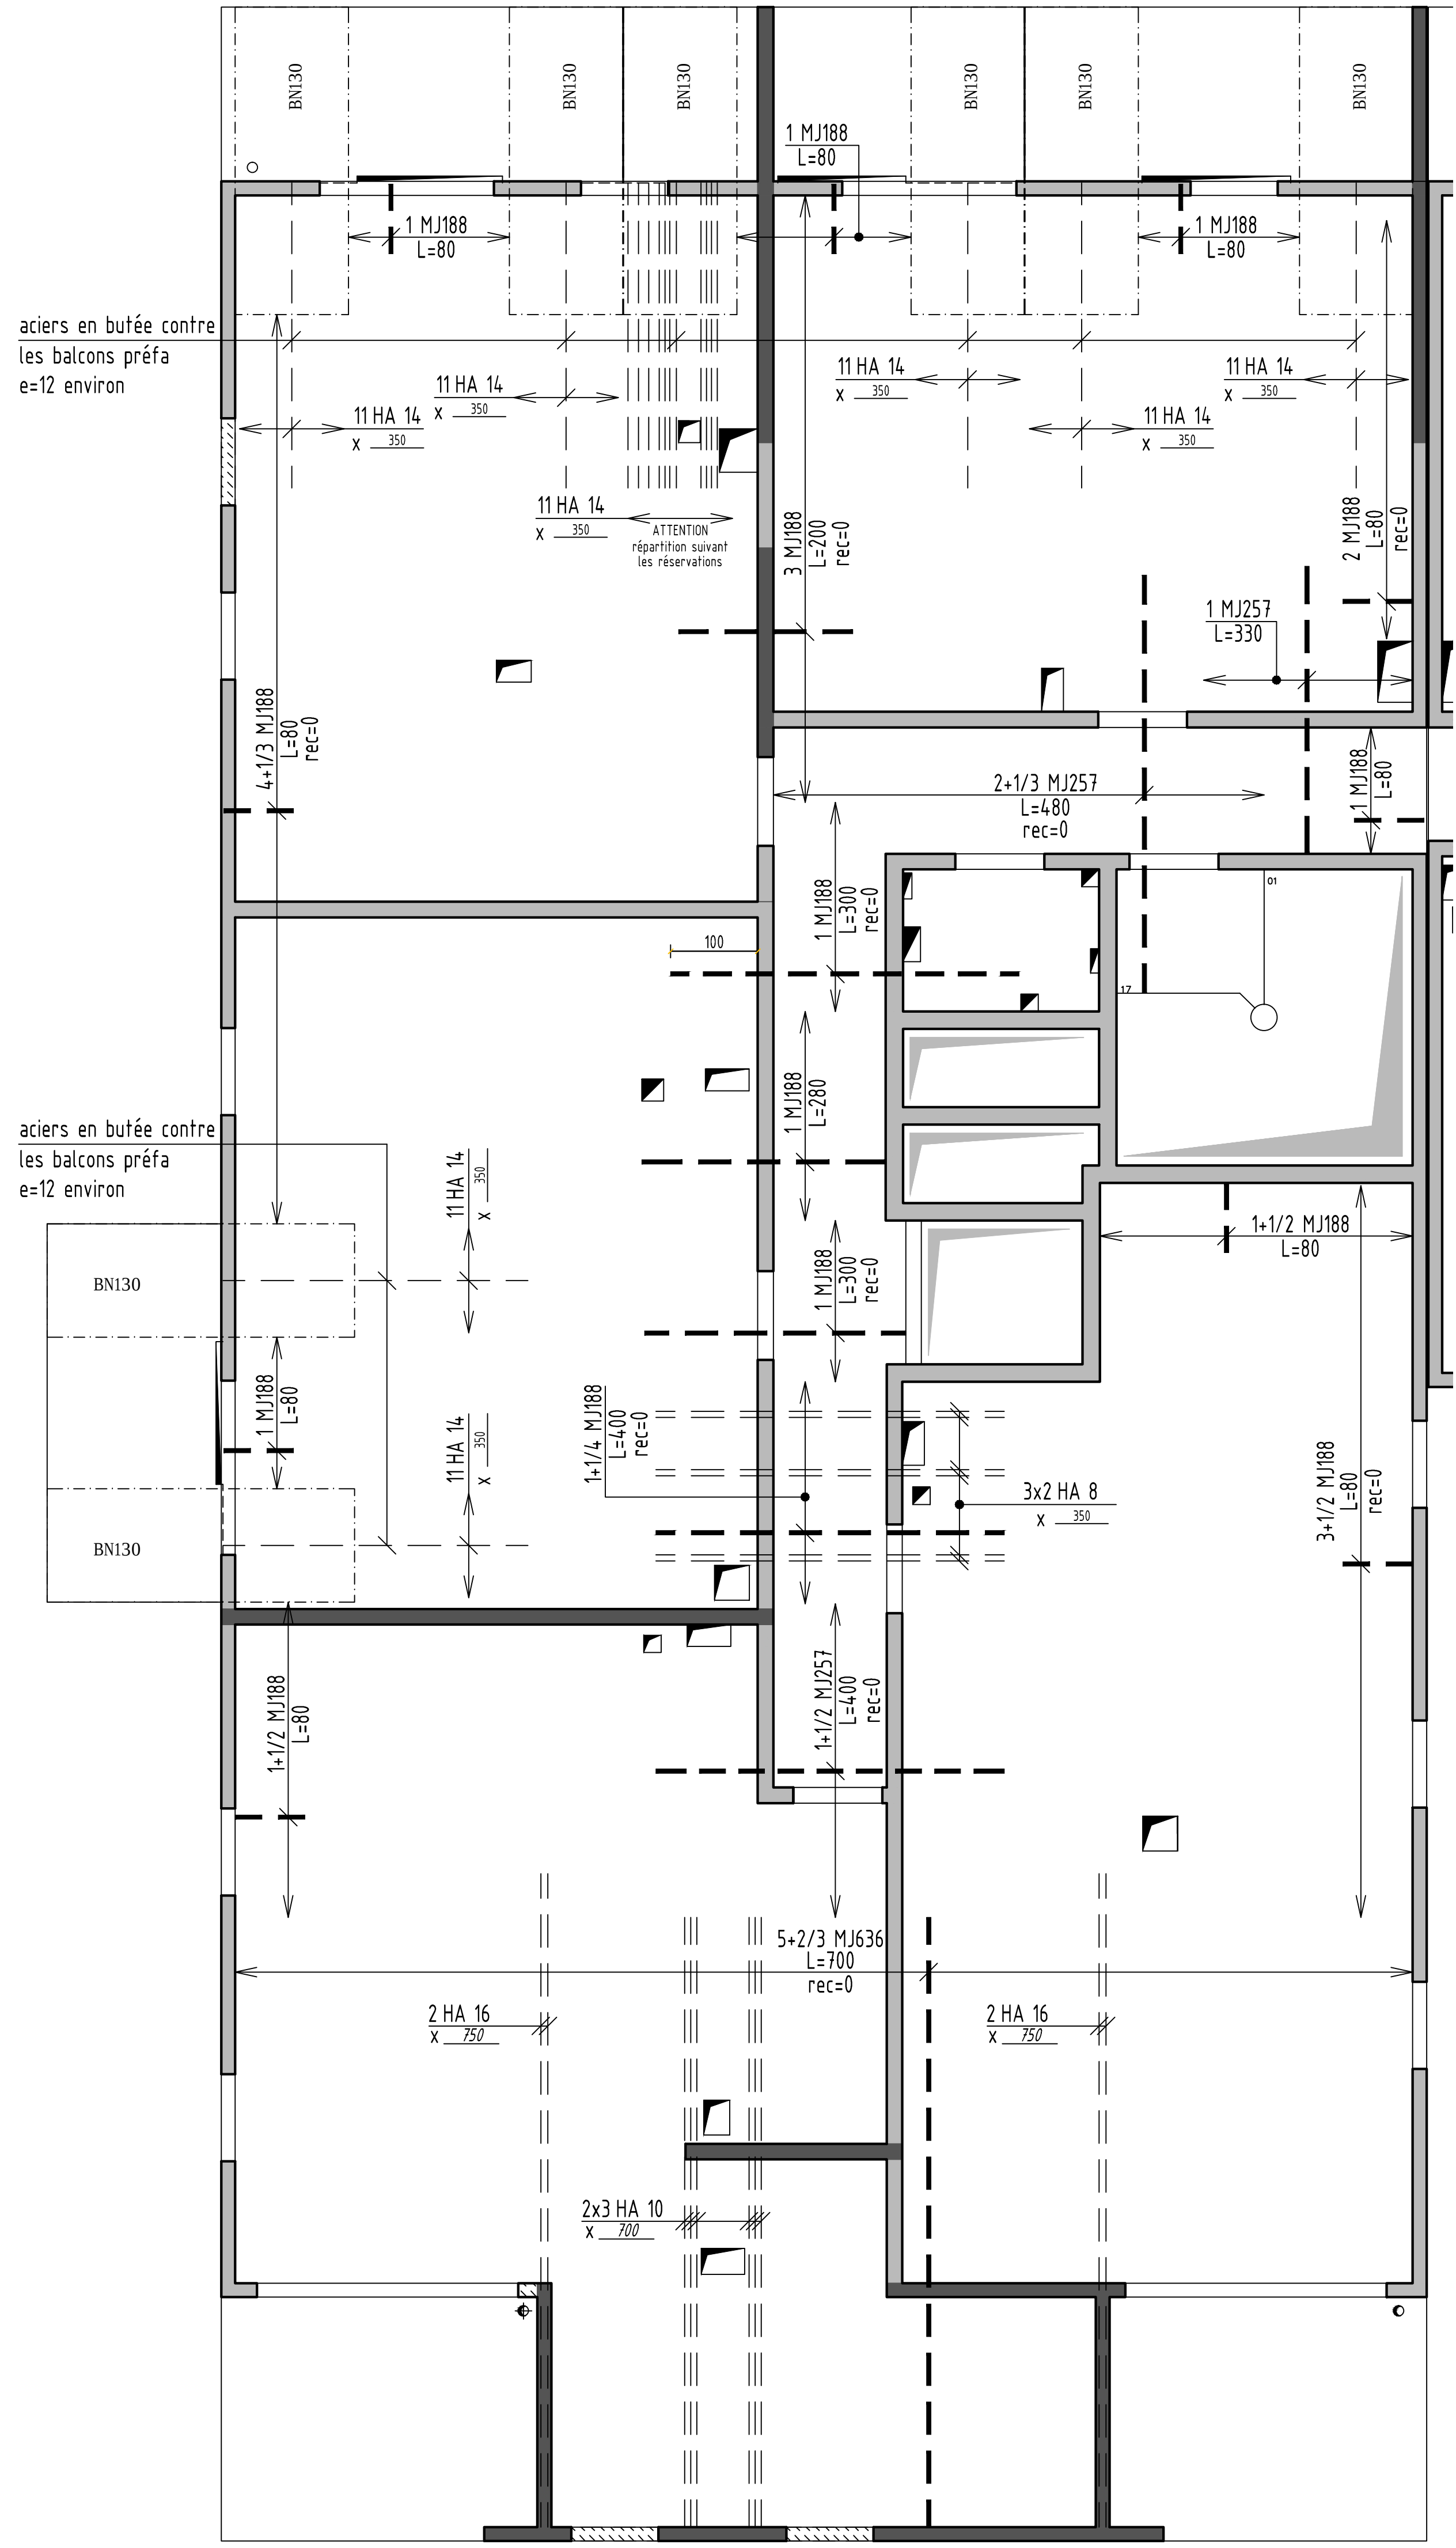


TREILLIS SUP DES DALLES

Trellis	Lgr (cm)	Nbr
MJ188	80	16+1/2
	200	3
	280	1
	300	2
	400	1+1/2
MJ257	330	1
	400	1+1/2
	480	2+1/2
MJ636	700	6

DETAIL D'ABOUTS DE CHAINAGES

INTERIEURS:


Position des équerres d'angles dans dalle 2 HA 14 x 360
à plan
vues en plan

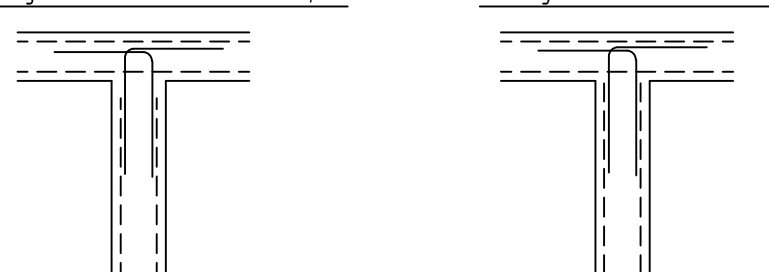

DETAIL D'ABOUTS DE CHAINAGES

EN ANGLE SUR FACADES:

Position des équerres d'angles dans dalle 3 HA 14 x 360
à plan
coupe

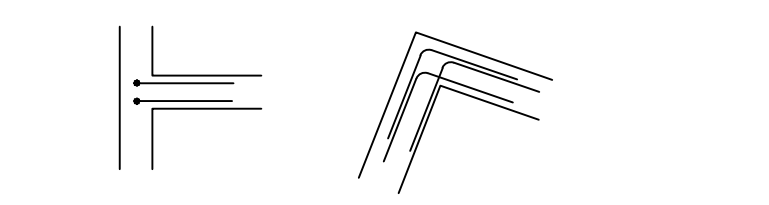

NOAHO

Chemin de Fontanière - 69350 La Mulatière

Création de logements

Les entreprises réalisant les travaux devront tenir compte des derniers plans architecte lors de la réalisation des travaux.
Les plans du lot N°115 ne doivent servir qu'à titre d'information et doivent être consultés en dernier lieu.

ARCHITECTES: ATELIER DE LA PASSERELLE
BET STRUCTURE: MATTE SAS
BET FLUIDES: PRELEM
ECONOMISTE: ENECO
BUREAU DE CONTRÔLE: Bureau VERITAS

MO DELEGUE: PSO Ingénierie
MODE: COPS
ENTREPRISE(S): Fontanet-pbc

Bât B
PLANCHER sur -2 entre files 11 à 14
NAPPES SUPÉRIEURES et INFÉRIEURES
Armatures des dalles

DOE

Contraintes de sol

Aciers HA (T) FeE500

Aciers Doux (B) FeE235

Aciers TS FeE 500

Sol: 120 kN/m²

Enrobage: +3 cm

PLAN N°
B31 0
DATE: 08/12/2015

MATTÉ
BUREAU D'ÉTUDES
STRUCTURES ET FLUIDES
119 BOULEVARD STALINGRAD 69100 VILLEURBANNE
Tél: 04 72 44 12 87 Fax: 04 72 44 26 93
E-mail: matt@matte.fr

Dessiné par: J. BO
Contrôlé par: P. LIN
Echelle: 1:50

Affaire N°
13.12.119