
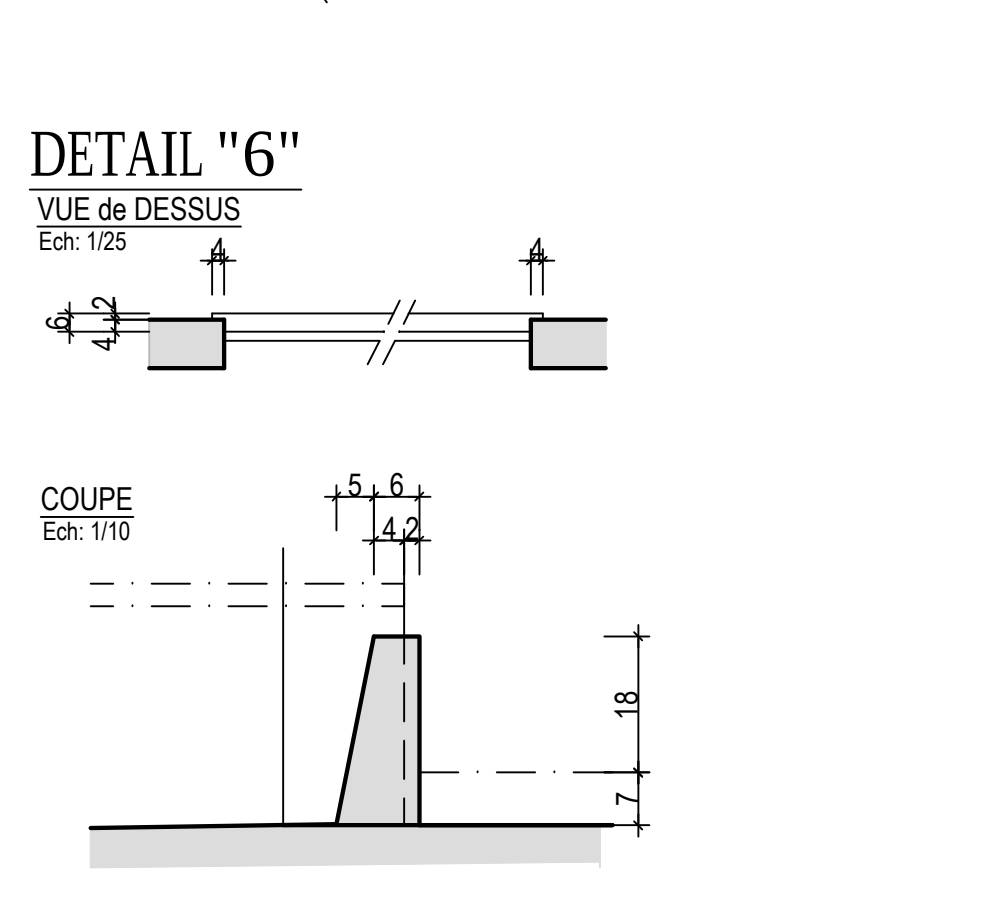
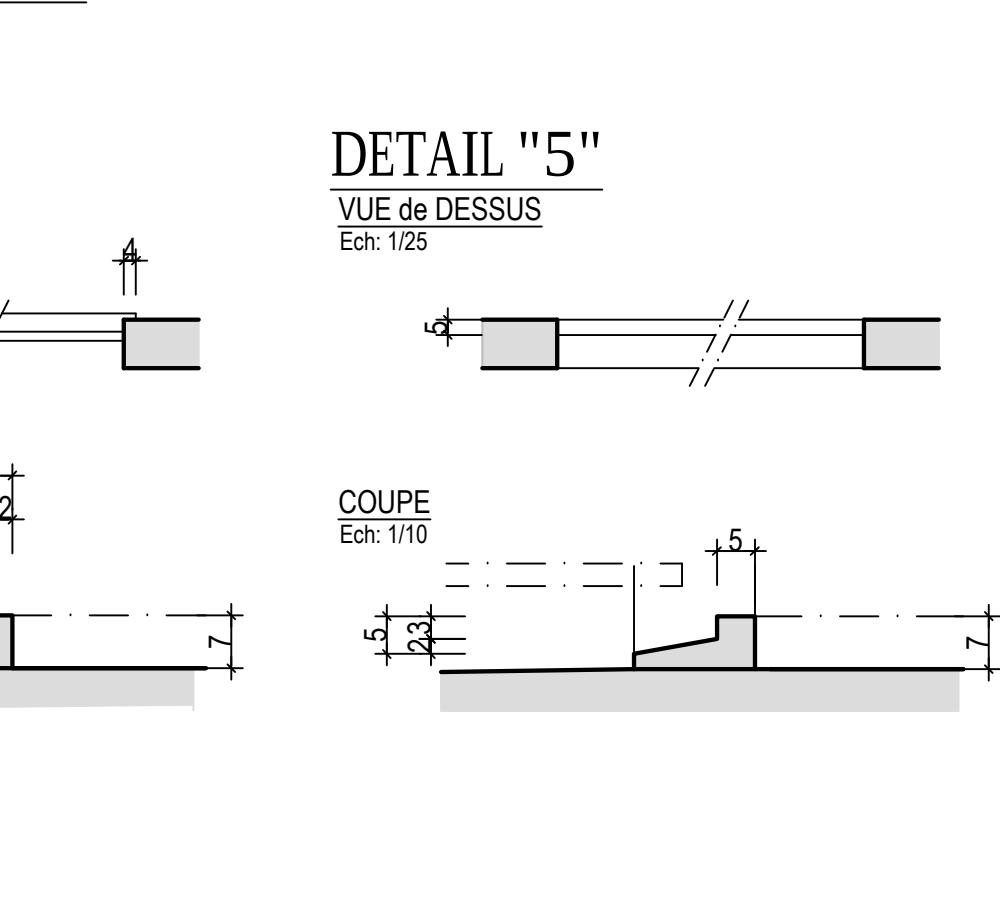
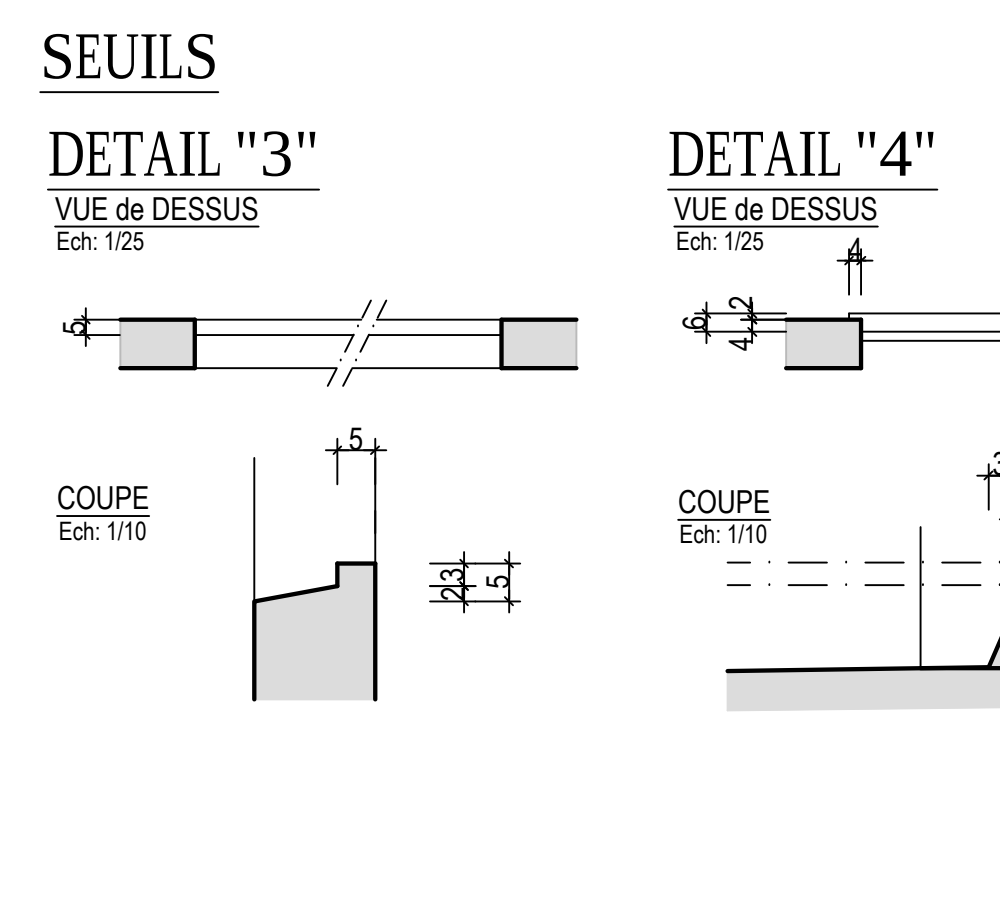
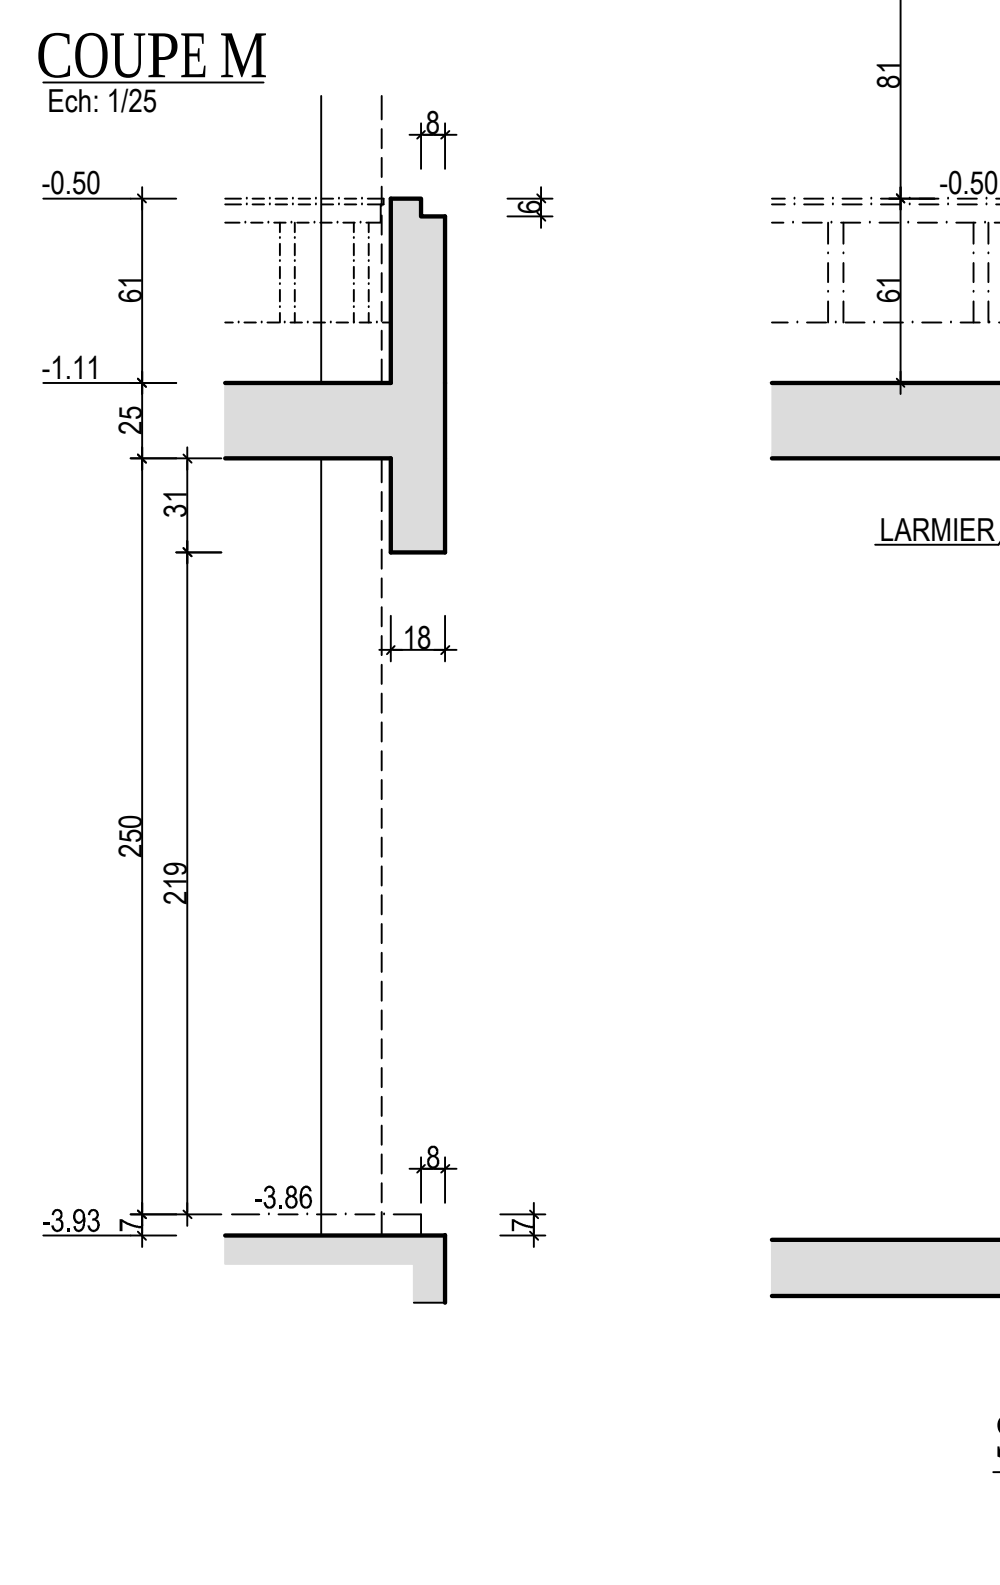
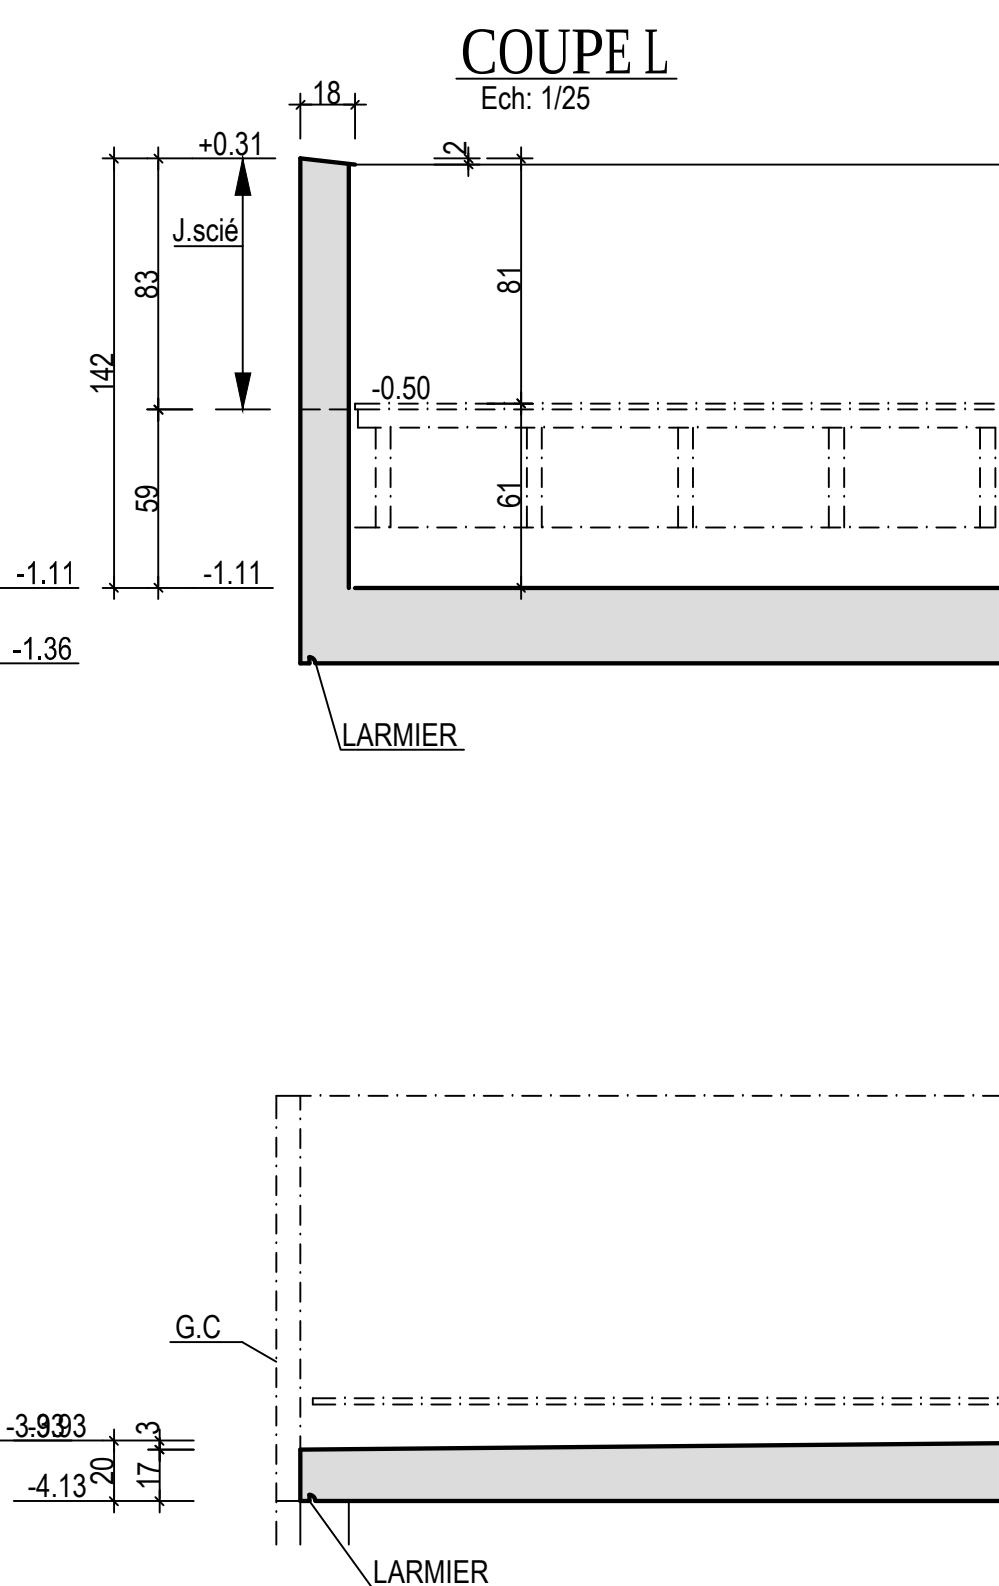
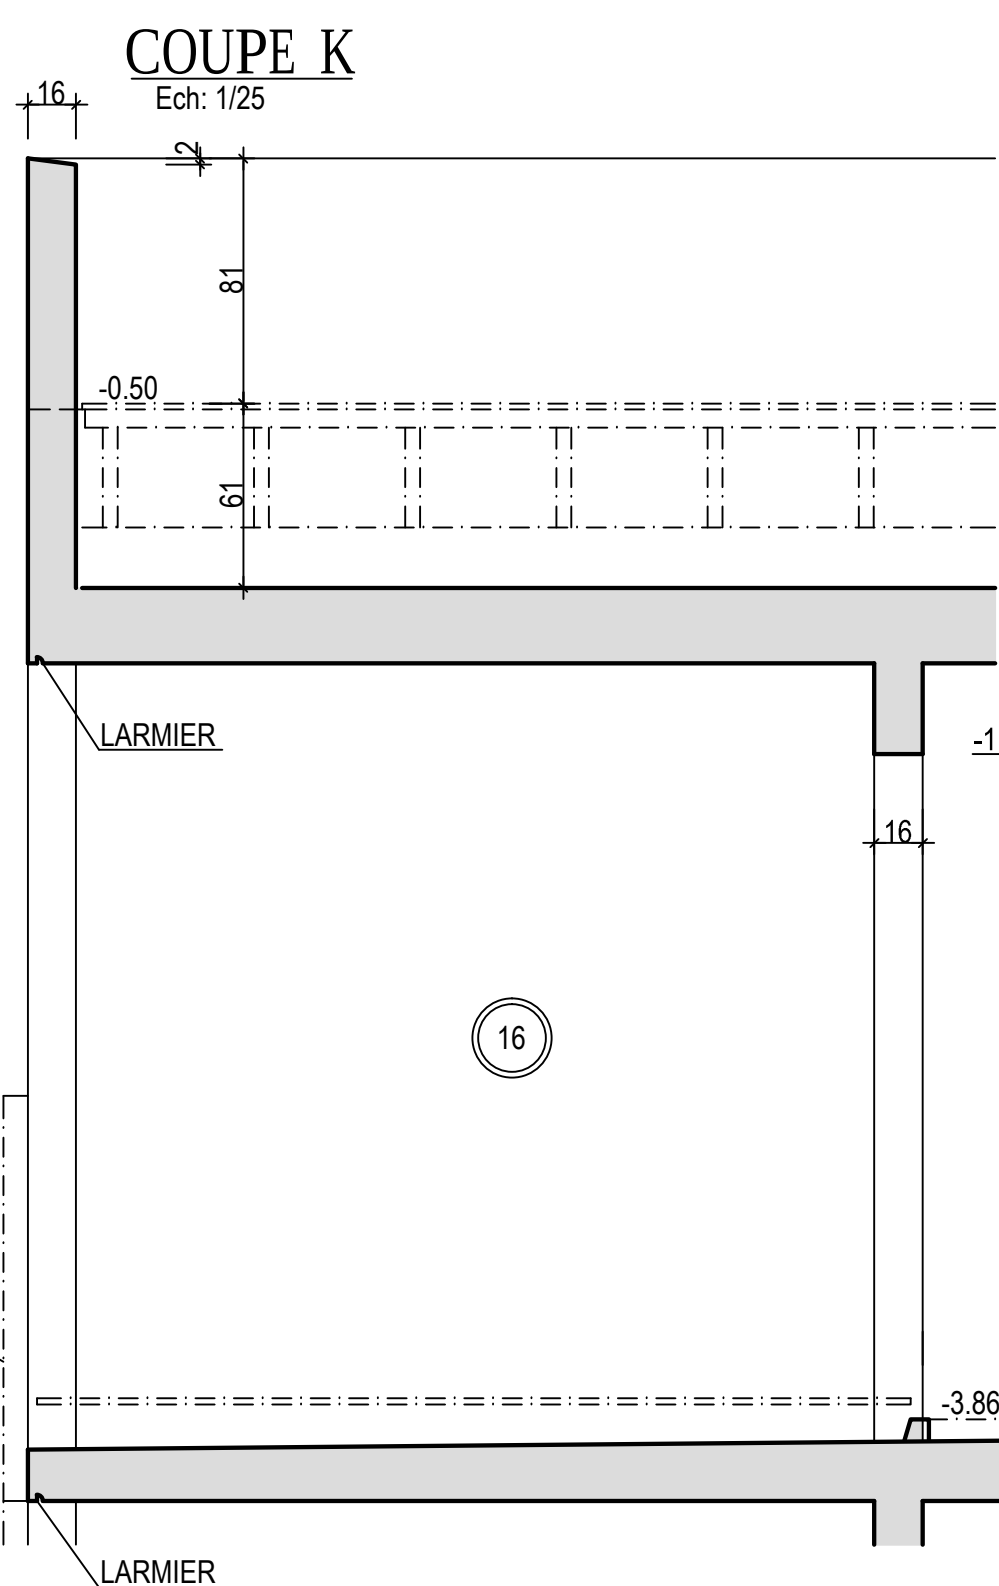
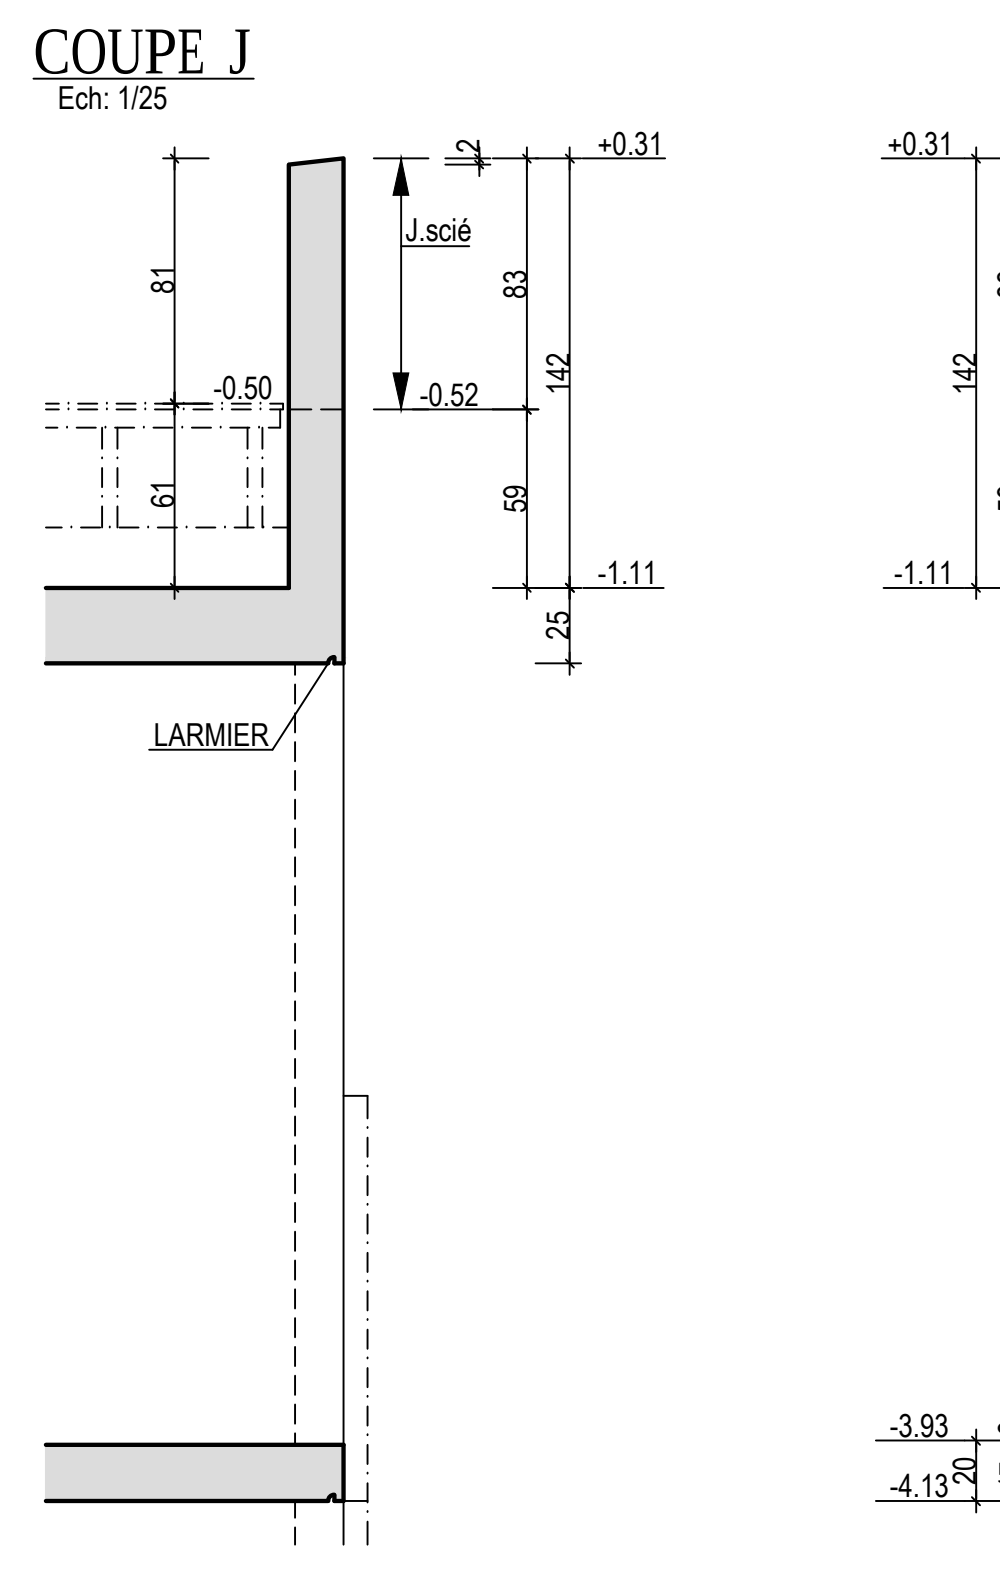
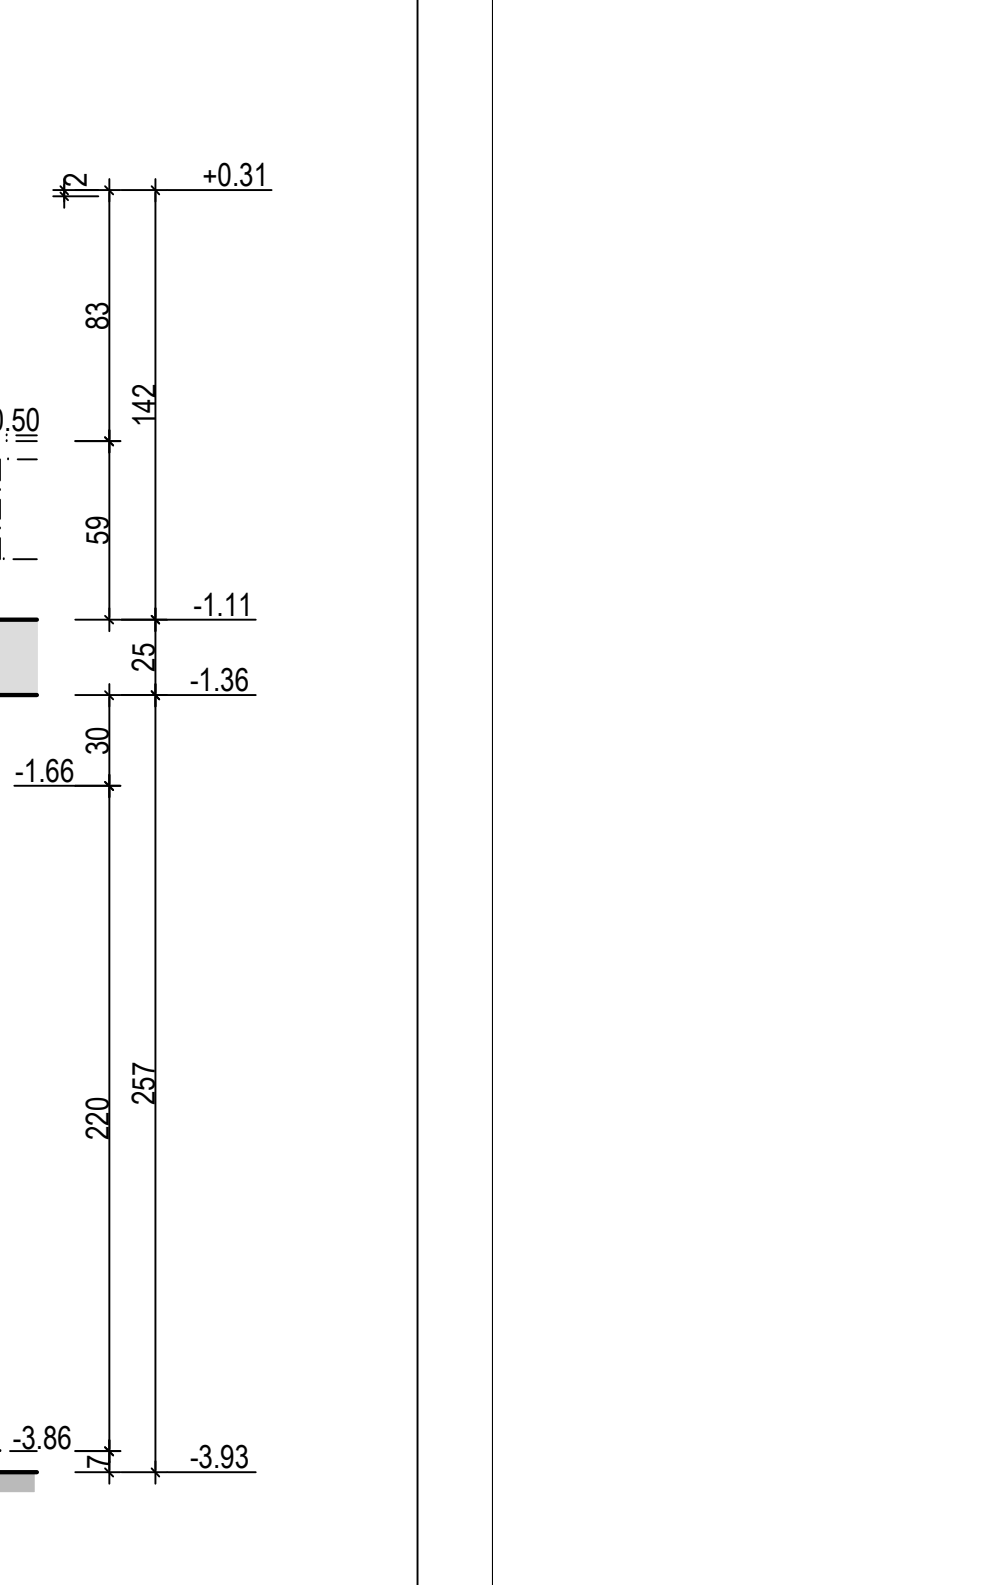
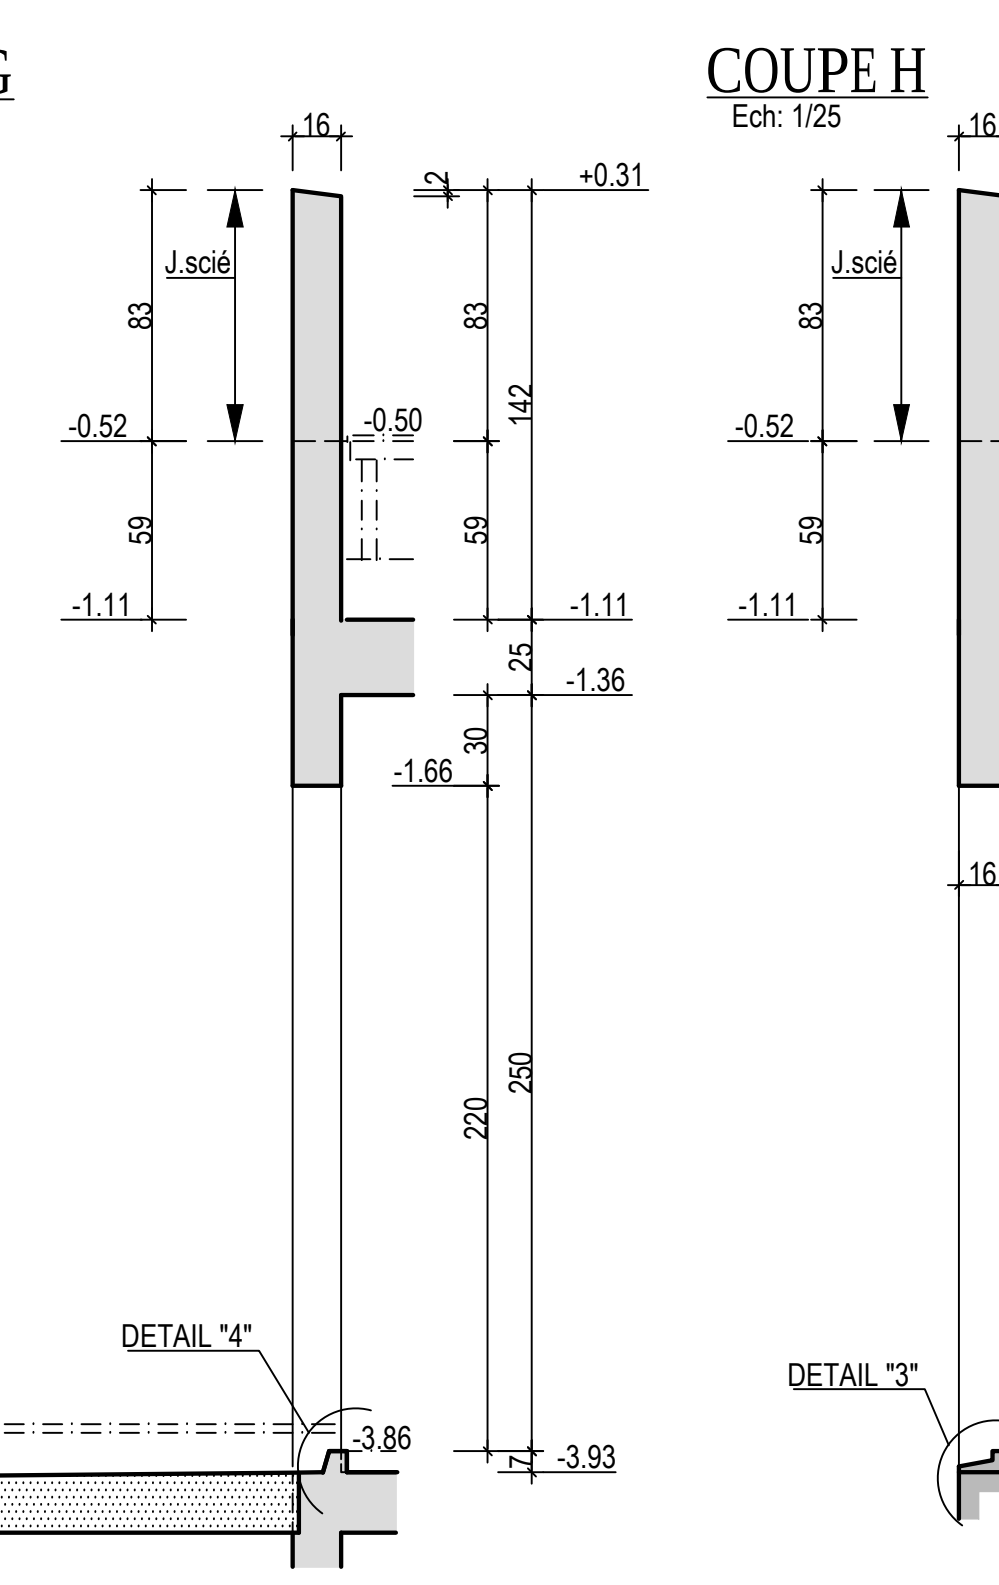
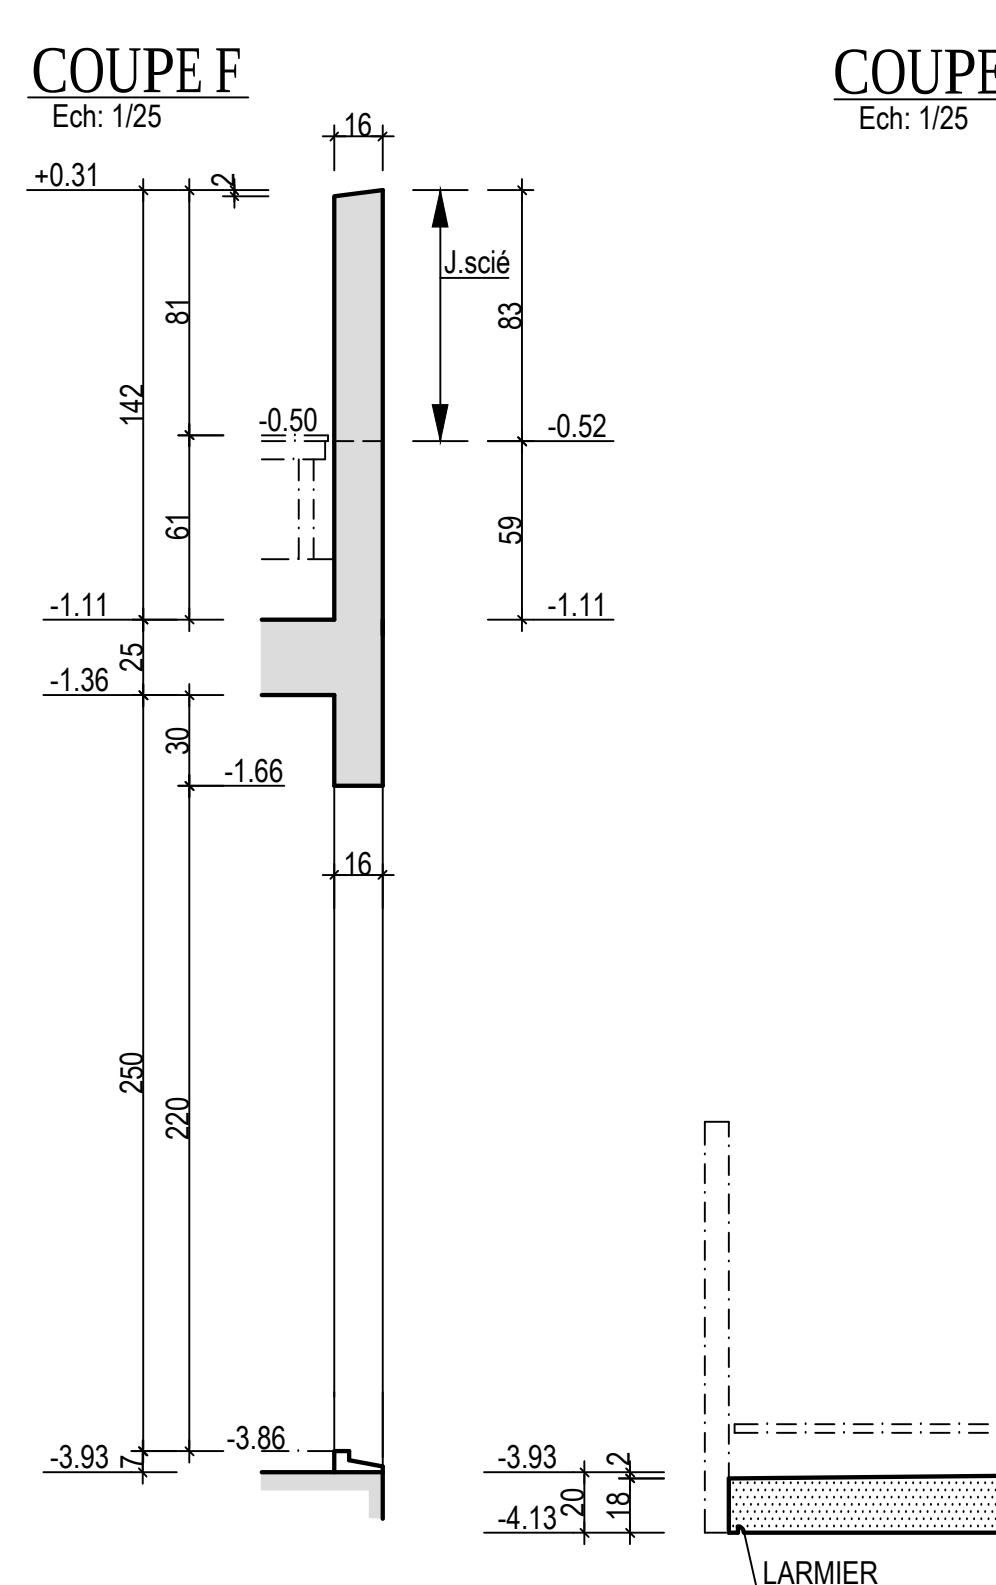
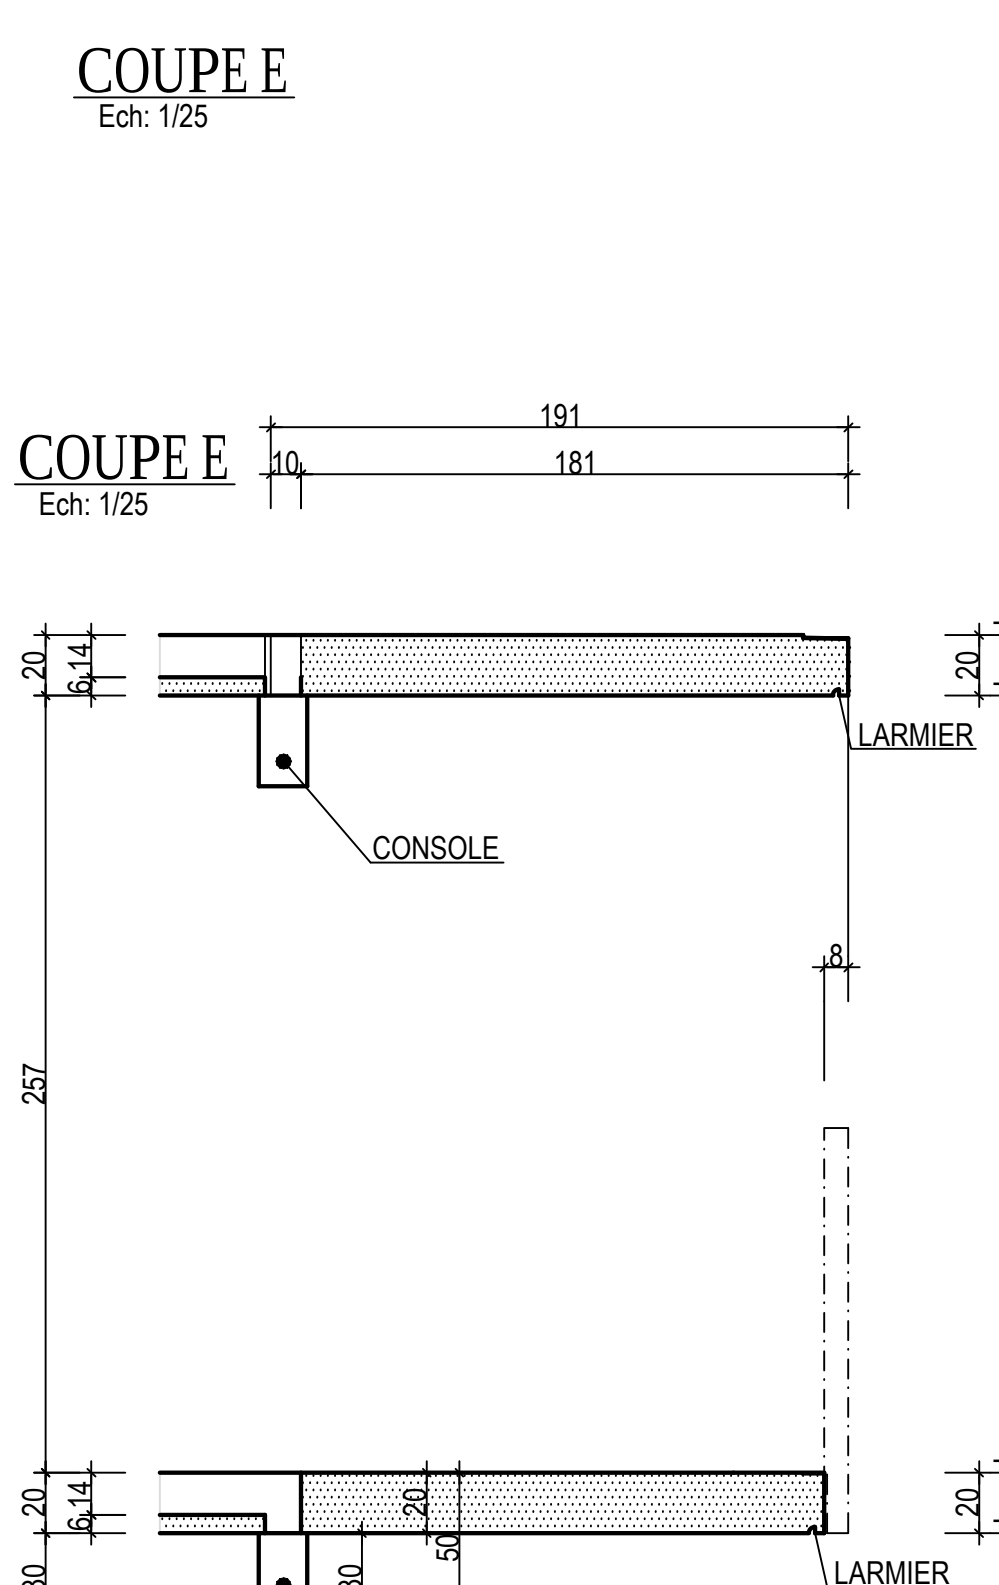
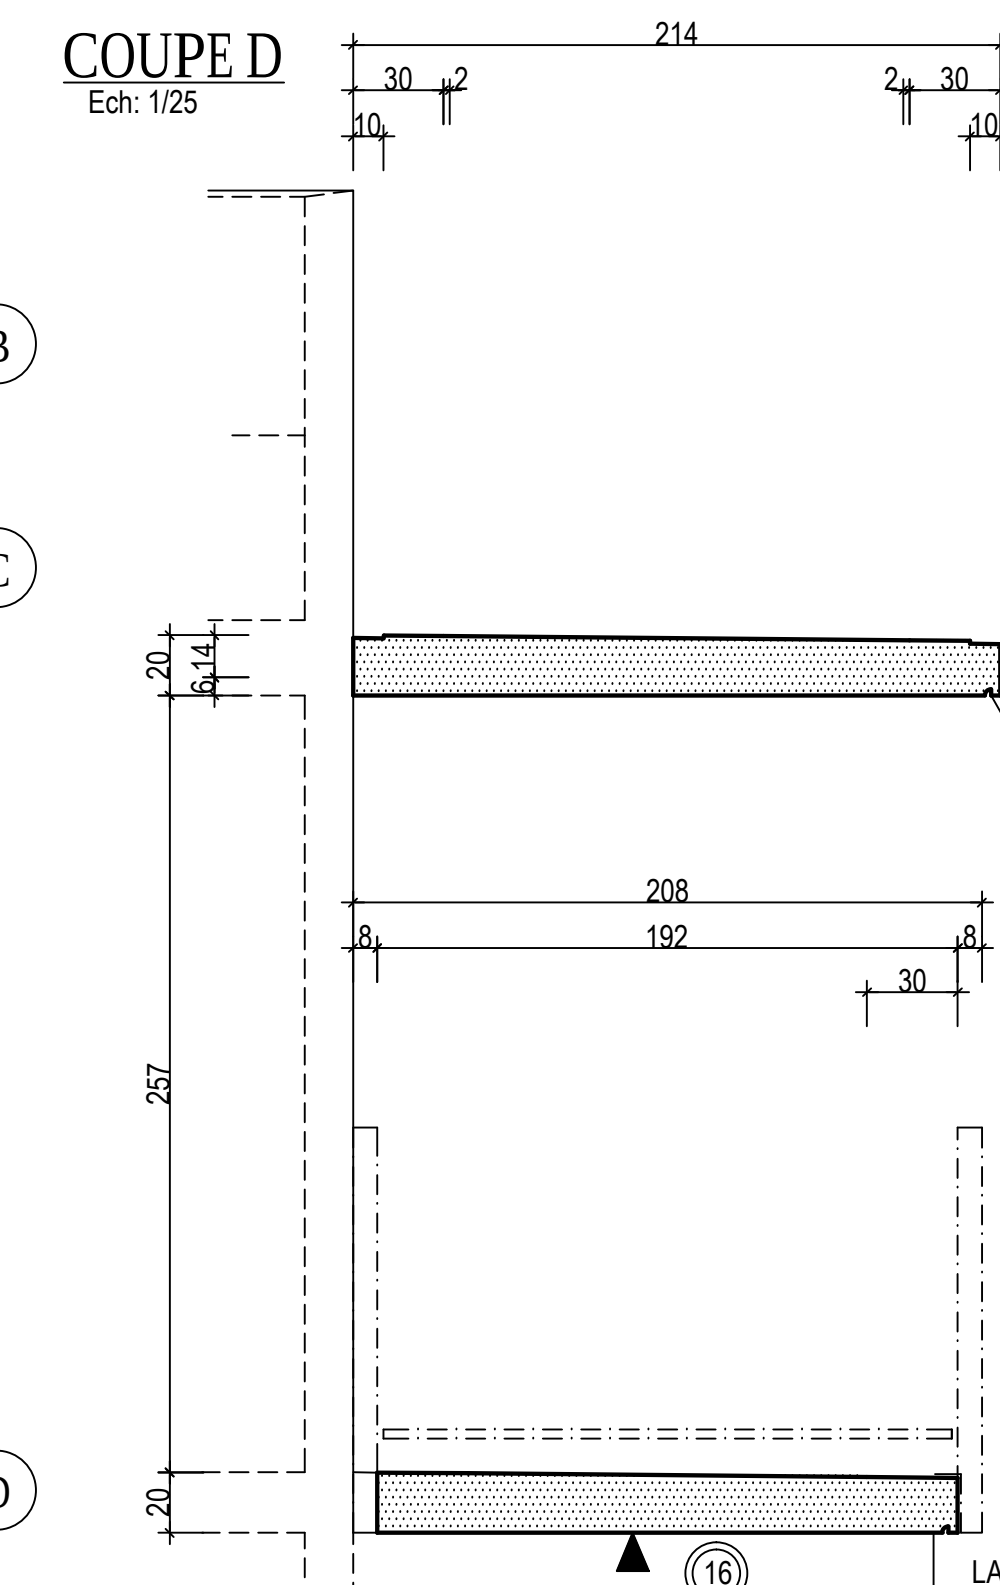
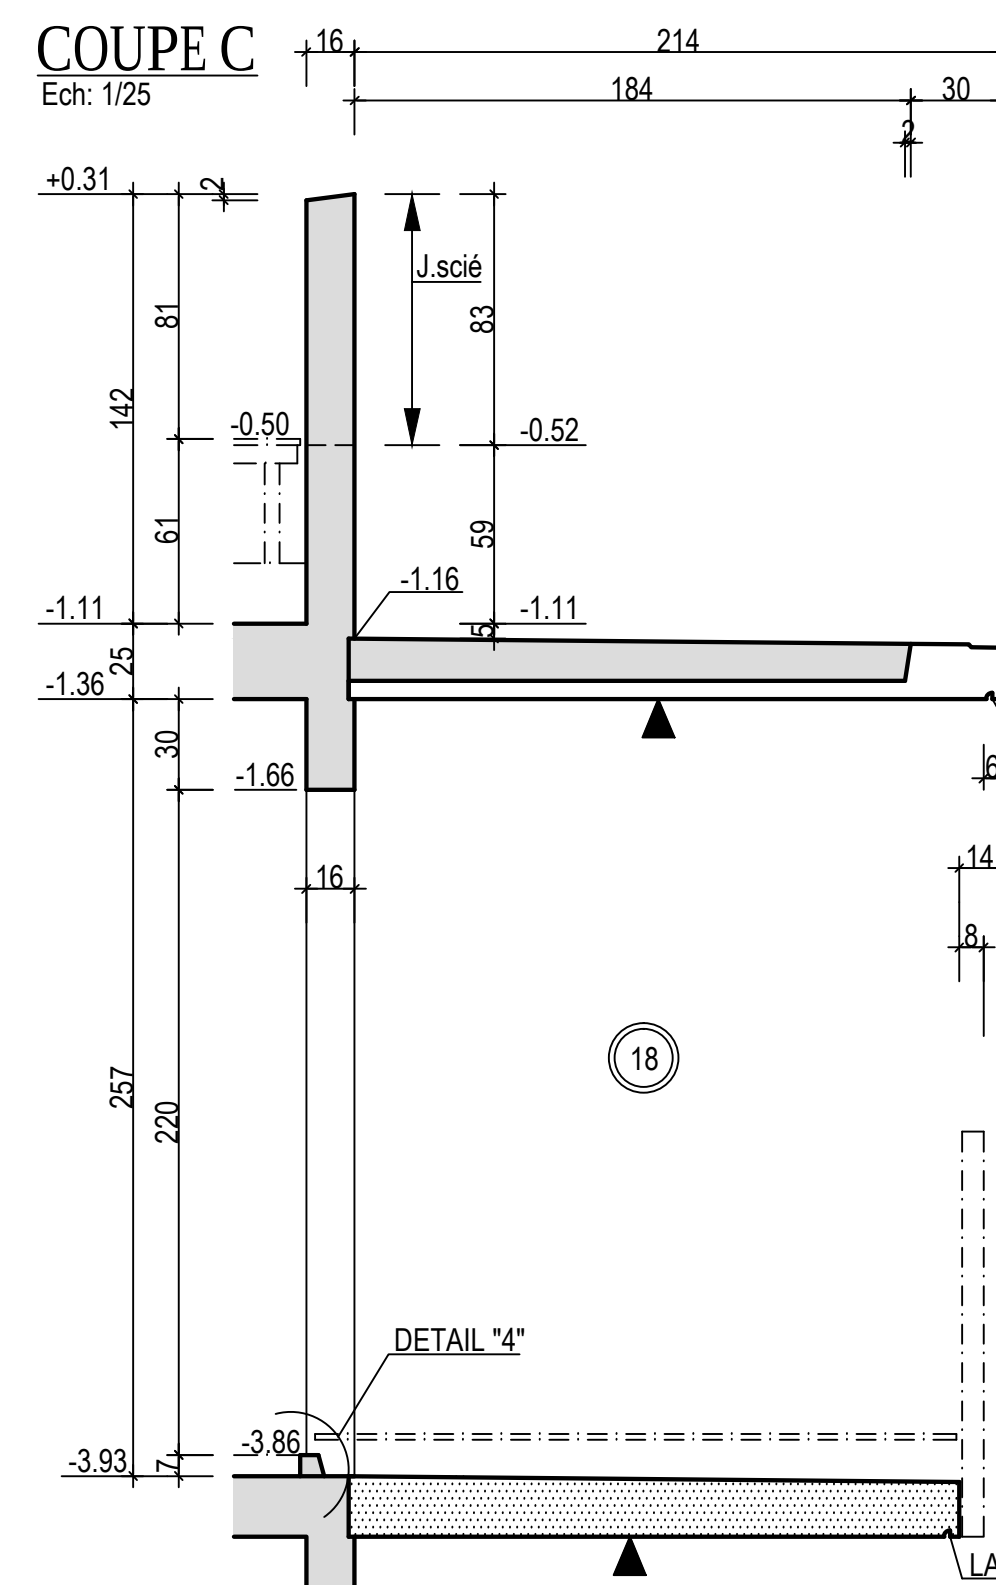
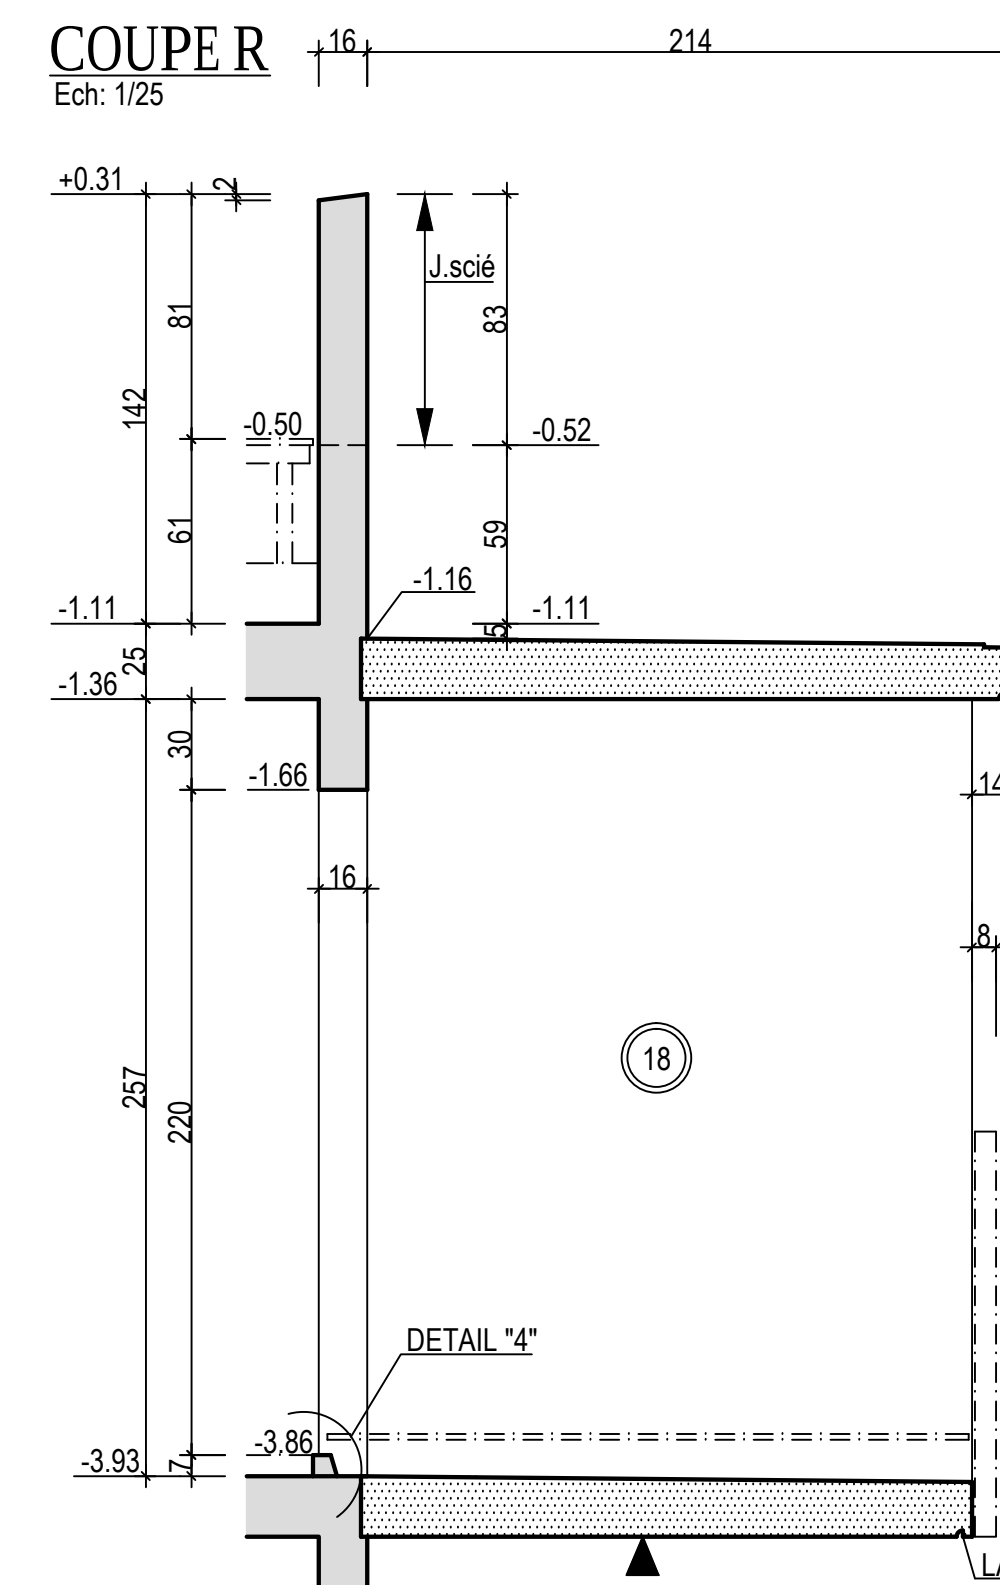
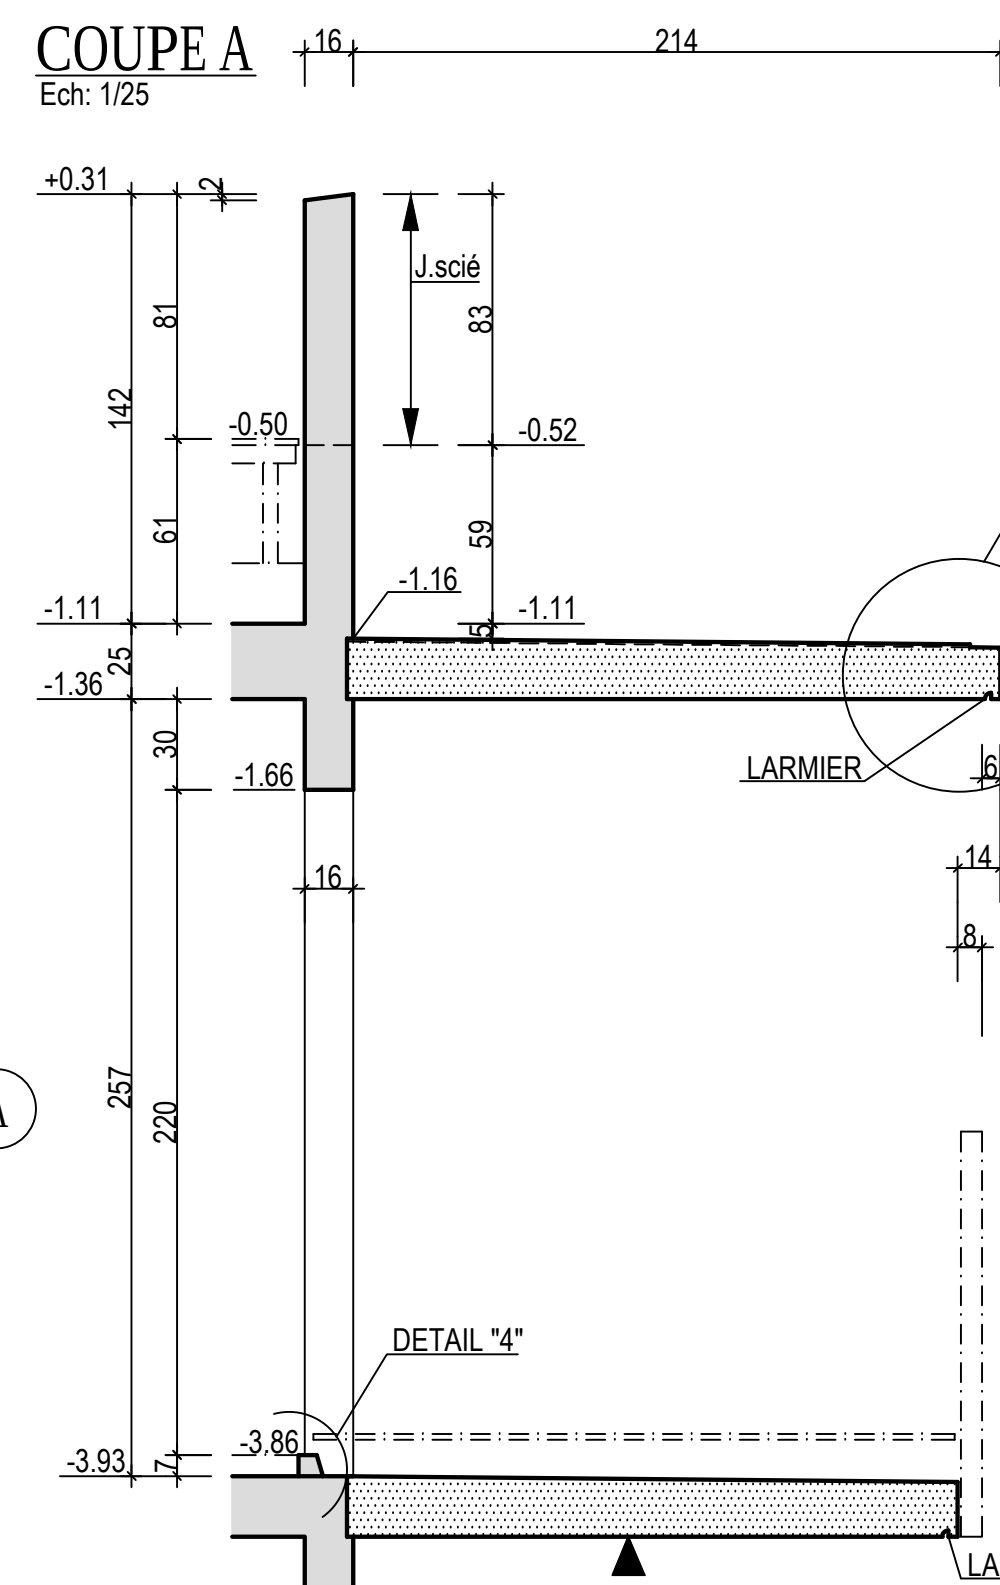


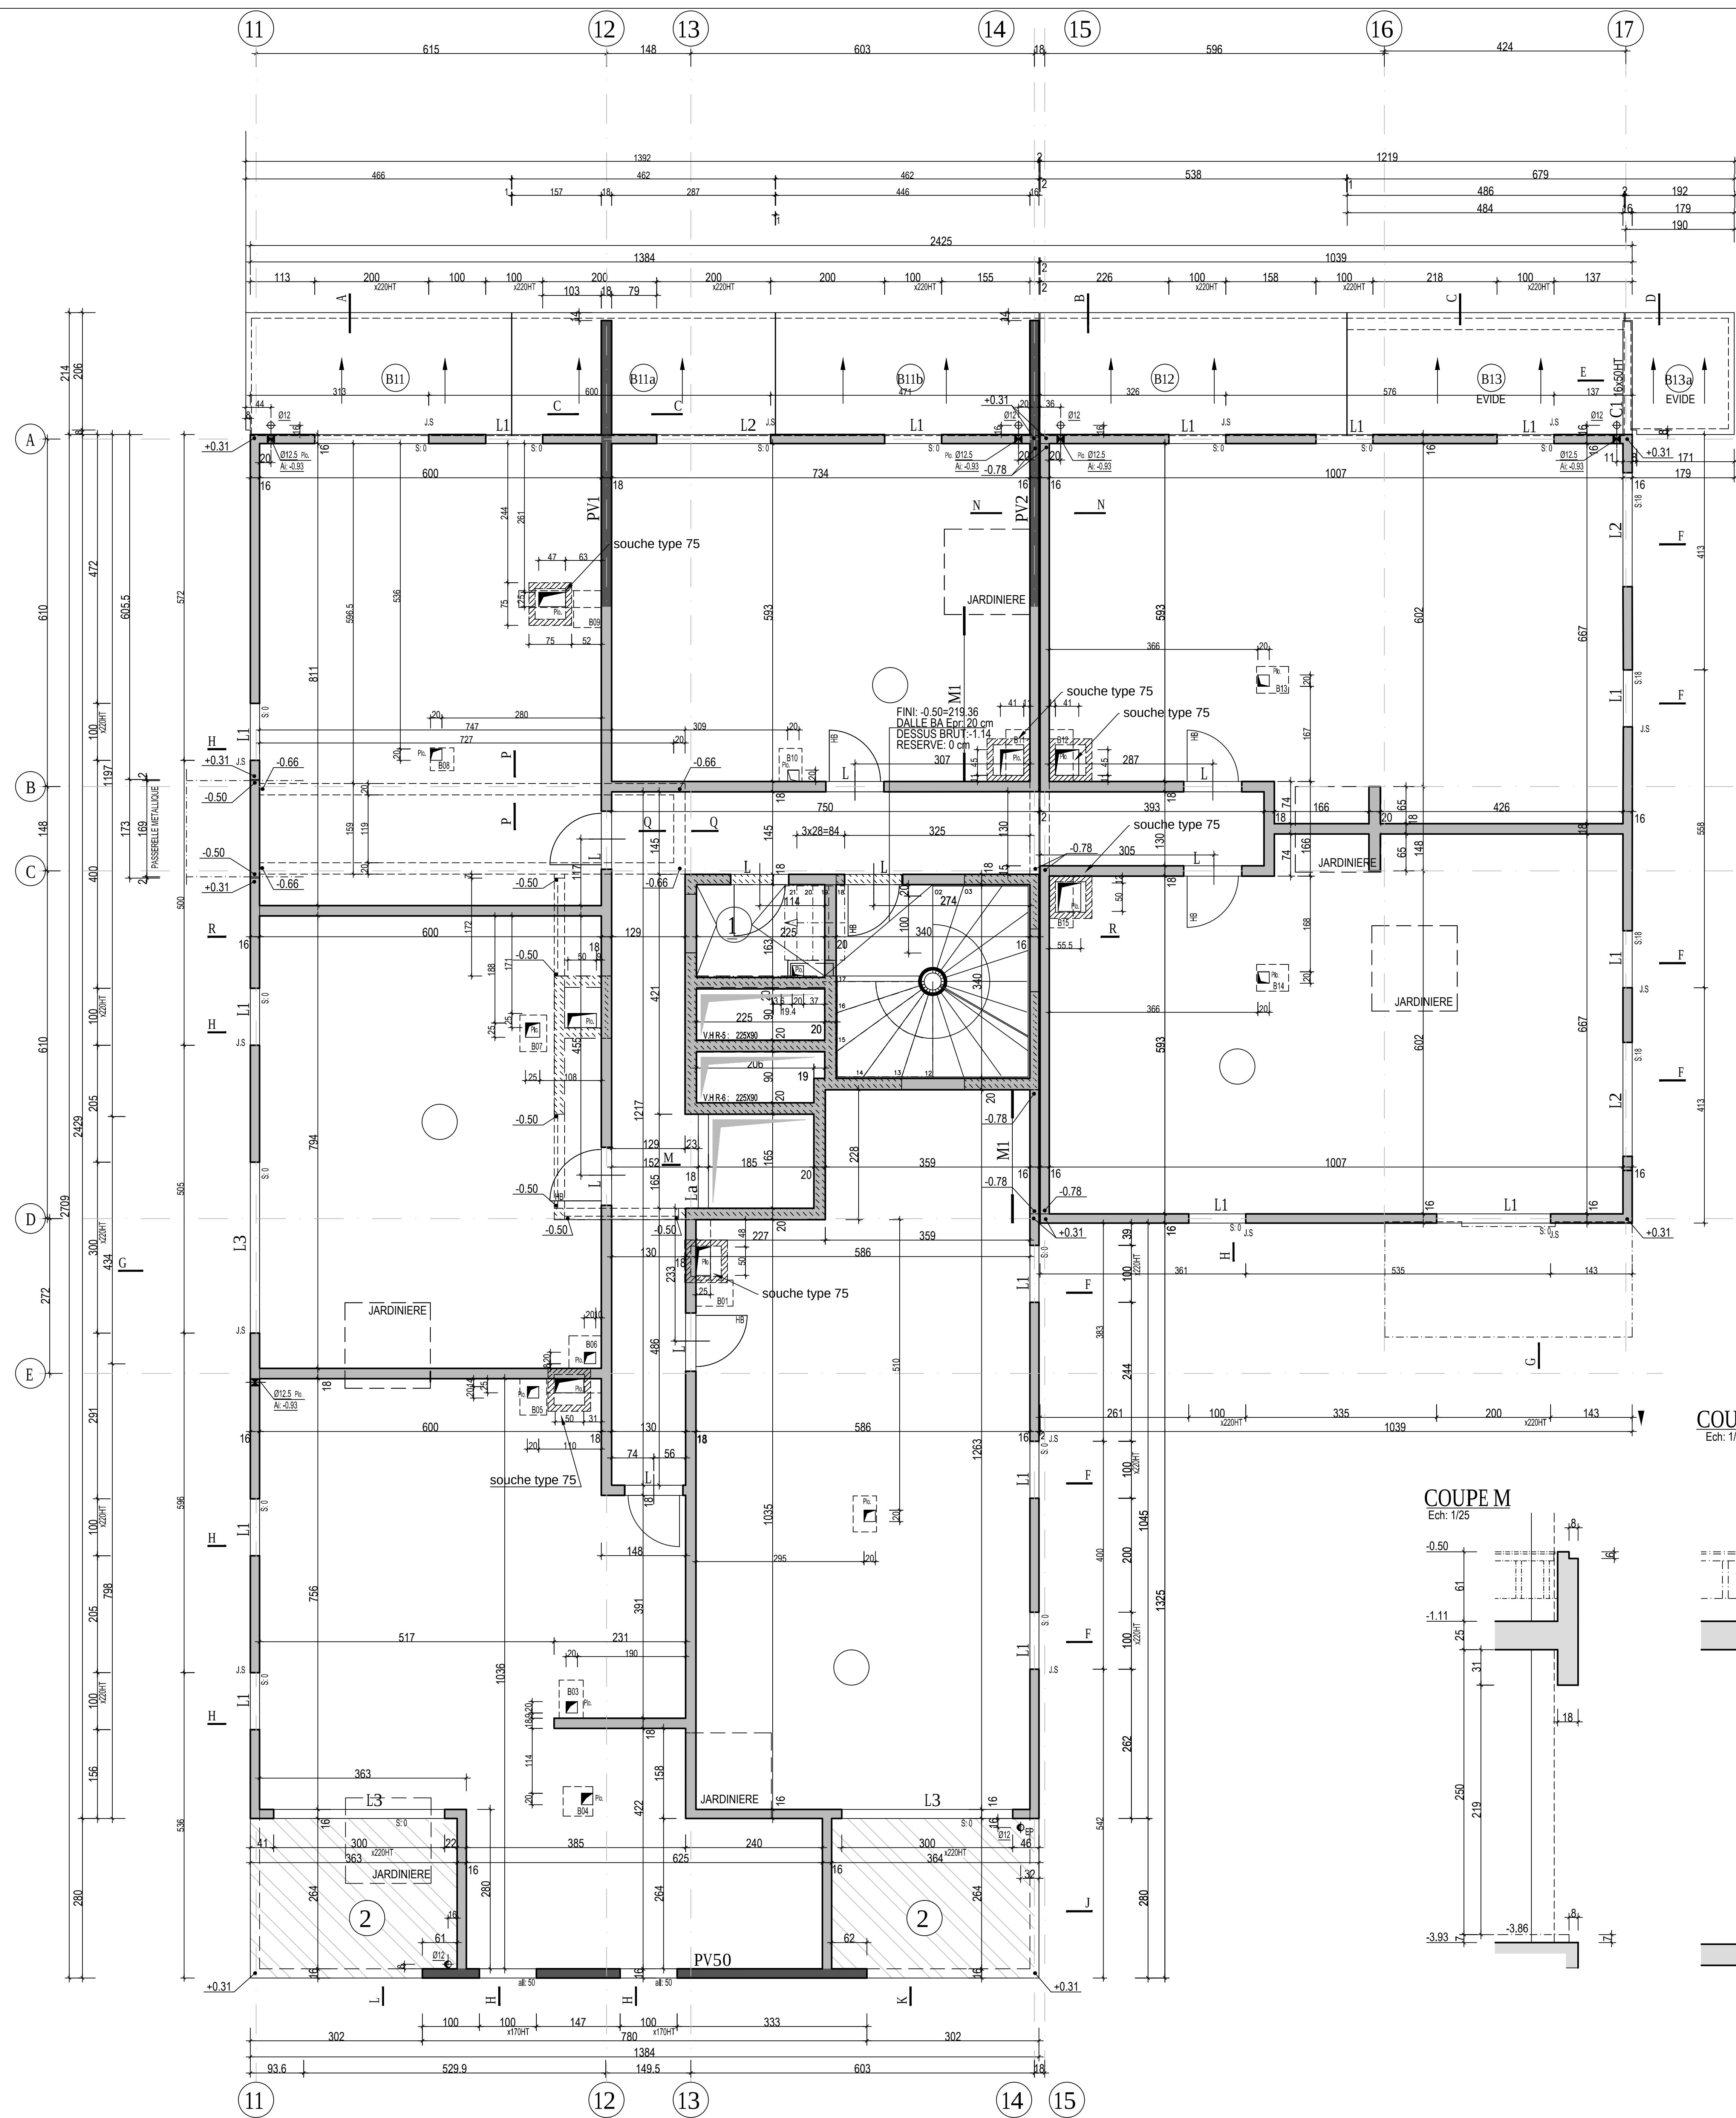

DALLES
FINI: -0.50=-220.00
DALLE BA Epr: 25 cm
DESSUS BRUT: -1.11
RESERVE: 61 cm

COUPES D et E N'EXISTE PAS
±0.00 = 220.50

NOAHO

Chemin de Fontanière - 69350 La Mulatière

Création de logements

Les entreprises réalisant les travaux devront tenir compte des derniers plans architecturaux lors de la réalisation des travaux

Les plans du Bât: MATTE ne doivent servir qu'au corps d'état concerné et doivent être des plans d'exécution

ARCHITECTES: ATELIER DE LA PASSERELLE

MO DELEGUE: MATTE SAS

BET STRUCTURE: PRELEM

BET FLUIDES: EXECO

ECONOMISTE: BUREAU DE CONTROLE: Bureau VERITAS

MO: PSO Ingénierie

CSFR: SUD EST COORDINATION

OPC: ENTREPRISES: Fontanel-pbc

Bât: B

PLANCHER sur -1

Coffrage

INDICE

DATE

MODIFICATIONS

A 14/04/2016 AJOUTE CHARGES

B 15/04/2016 AJOUTE REPERAGE PREFA

C

MATTE

BUREAU D'ETUDES

STRUCTURES ET FLUIDES

119 BOULEVARD STANISLAS 69100 VILLEURBANNE

Tel: 04 72 44 02 87 Fax: 04 72 44 26 99

E-mail: bat@matte.fr

Destiné par: J BO

Contrôle par: P LIN

Echelle: 1/50"

COUPE

DATE: 19/11/2015

PLAN N° B34 E

Affaire N° 13.12.119