

NOHAO

Chemin de Fontanière-69350 La Mulatière

Création de logements

Les entreprises réalisant les travaux devront tenir compte des derniers plans architecte lors de la réalisation des travaux
Les plans du be MATTE ne doivent servir qu'au corps d'état concerné et doivent être des plans d'exécution.

ARCHITECTE(S):	Atelier DE LA PASSERELLE	M.O. Délégué:	.
BET STRUCTURE:	BET MATTE	M.O.:	.
BET FLUIDES:	PRELEM	CSPS:	PSO ingénierie
ECONOMISTE:	EXECO	M.O.E.:	SUD EST COORDINATION
BUREAU DE CONTROLE:	VERITAS	ENTREPRISE(S):	Fontanel-pbc

Bât: B
BA au -1 entre files 11 et 14

DOE

INDICE	DATE	MODIFICATIONS

Aciers HA (T) FeE500
Aciers Doux (Ø) FeE 235
Aciers TS FeE 500
Béton fc28 >= 25MPa
Enrobage = 3 cm

**PLAN N°
B35 0**

DATE : 25/01/2016

MATTÉ
BUREAU D'ÉTUDES
STRUCTURES ET FLUIDES

119 BOULEVARD STALINGRAD 69100 VILLEURBANNE

Tél. 04 72 44 02 87 Fax 04 72 44 26 59

E-mail : bet@matte.fr

Dessiné par : J.BONDETTI
Contrôlé par : P. LIN
Ech :

**Affaire N°
S.13.12.118**


POUTRE VOILE : PV1

2 HA 10 FILANTS
2x2.50 = 5.00 ml Env

ELEVATION

BOITE D'ATTENTES
HA 8 e=20 + 2 HA 10
DE CHAQUE COTE

E1a
Nombre: 1

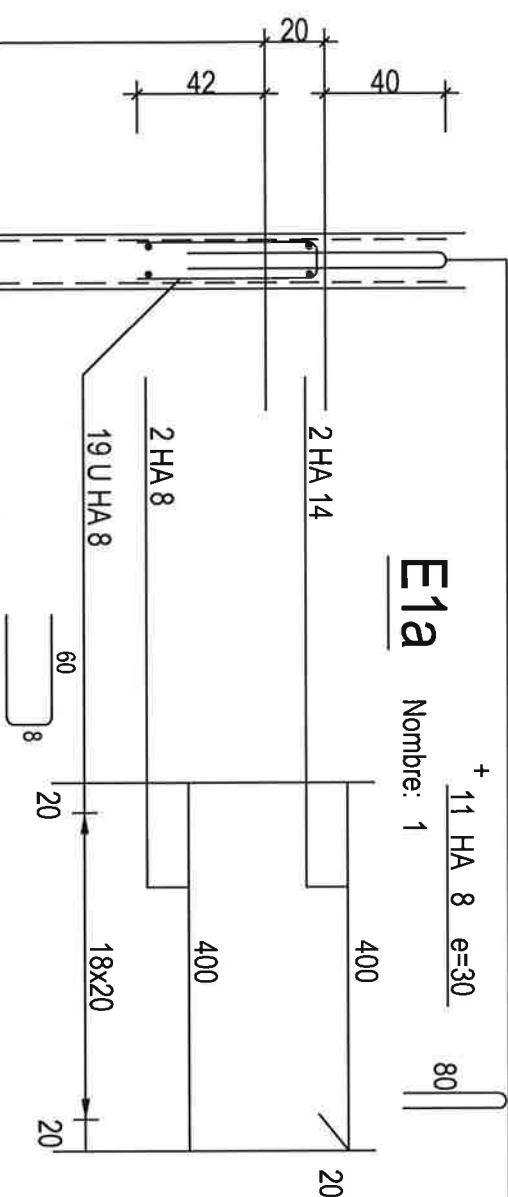


CHAQUE FACE

Pan MJ251C x 240



Rec: 40 cm

Nombre: 2x2


E1
Nombre: 1

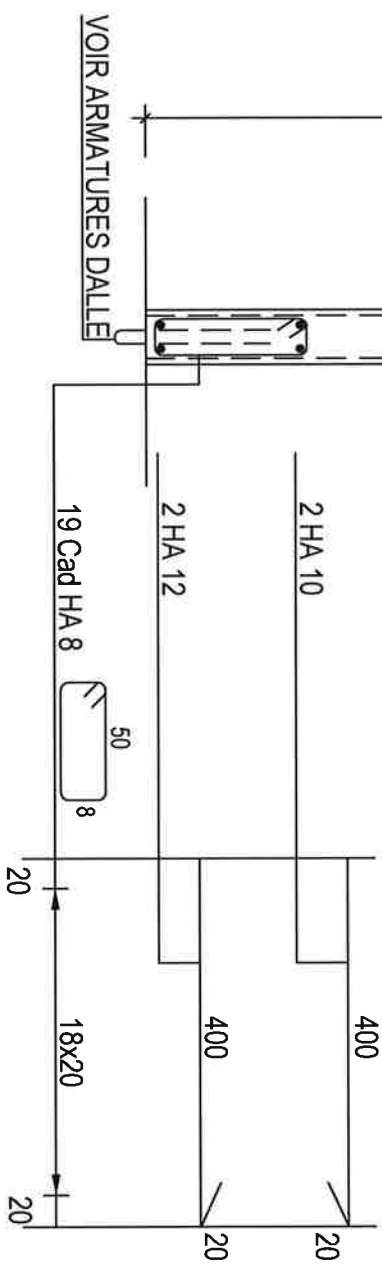

R1
Nombre: 1

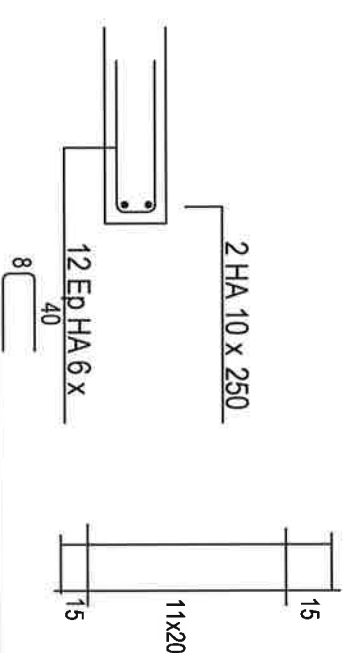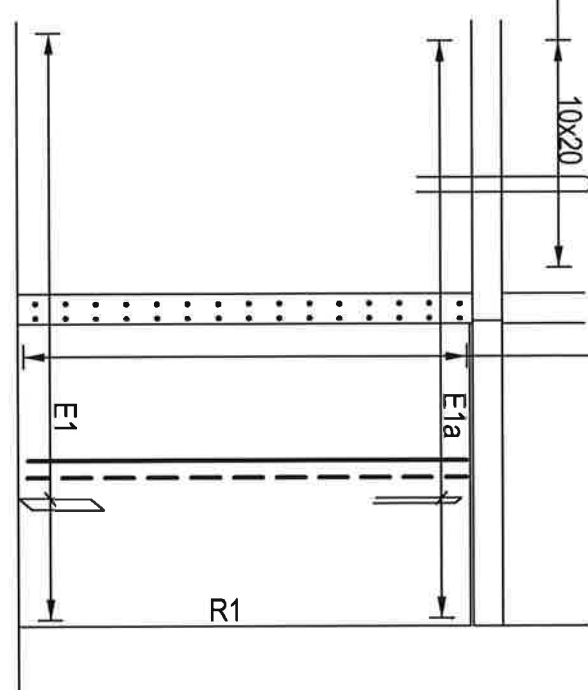

PV50

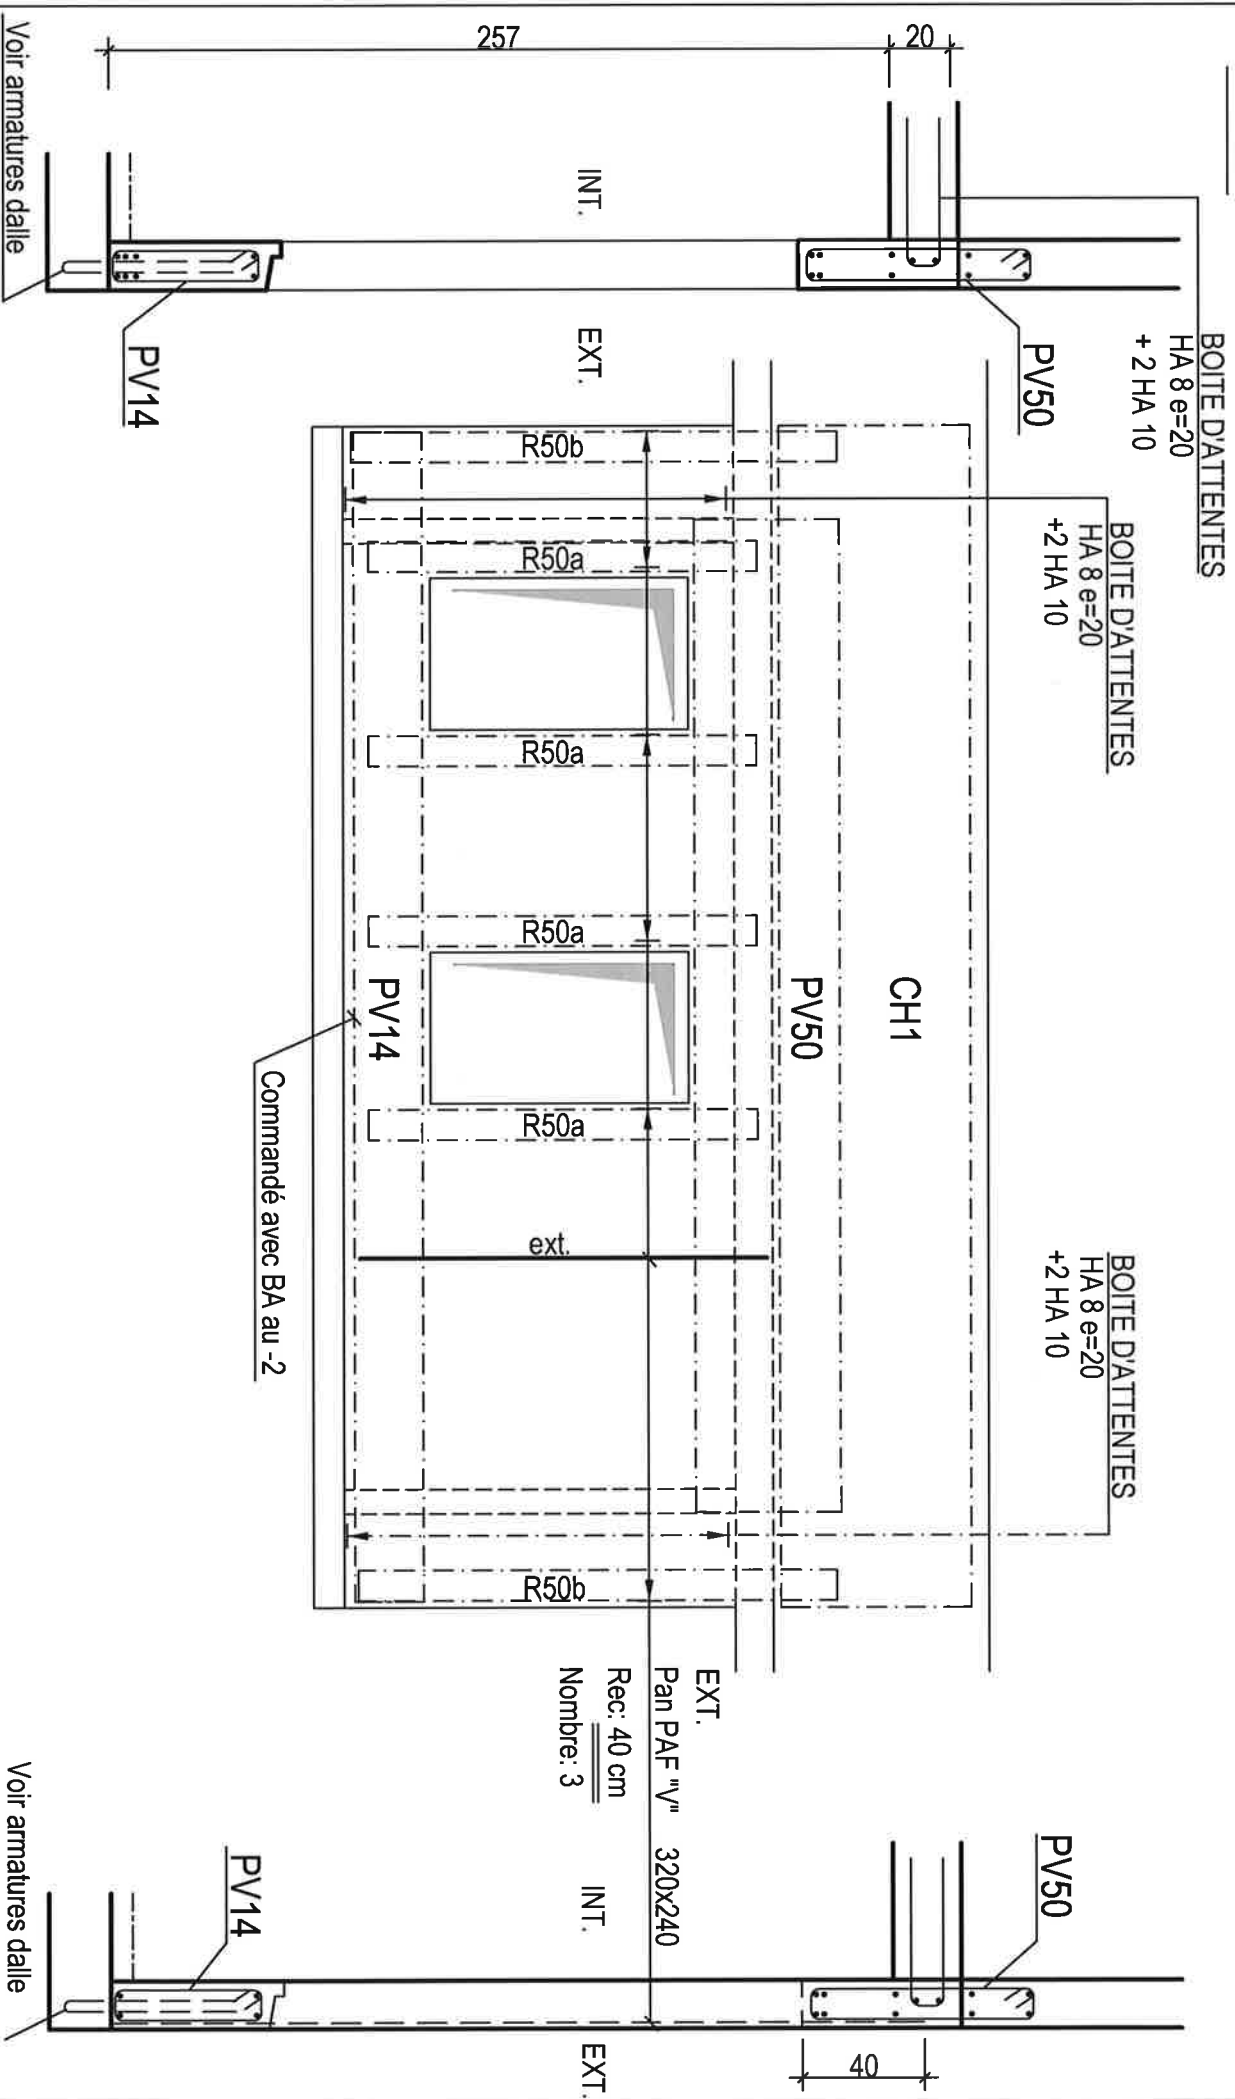

AFF: S.13.12.119	Bât: B	LA MULATIERE-69350 LaMulatiere NOMINATION de LOGEMENTS	BA au -1	Plan n° B 35	Page: 4
PV50 COUPE CH1 Nombre: 2 Rec: 60 cm 2 HA 10 x 600 18 U HA 6 e=30 8 40 45 17x30 45 600 2 HA 16 x 200 axes sous chaque joint 100 100 Rec: 40 cm Nombre: 2x4 Pan PAF 10 A COUPER Rec: 40 cm Nombre: 2x4 2 HA 10 x 600 18 U HA 6 e=30 8 40 45 17x30 45 600 2 HA 16 x 200 axes sous chaque joint 100 100 Rec: 40 cm Nombre: 2x4 Pan PAF 10 A COUPER Rec: 40 cm Nombre: 2x4 VUE EN PLAN EXT. EXT. (Loggia) BOITE D'ATTENTES HA 8 e=20 + 2 HA 10 PV14					
R50 a 4 pièces 4 HA 10 x 80 2 HA 10 x 165 10 35 8X18 10 40 40 170 9 U HA 6 4 HA 10 x 80 R50 b 2 pièces 4 HA 10 x 80 2 HA 10 x 165 10 35 8X18 10 40 40 170 9 U HA 6 4 HA 10 x 80					

PH-2

PV50

Béton=0.68 m³

Acier=53.7 kg d=78.6 kg/m³



Fi=8.8 mm Cof=7.6 m²

Ed=3.0 cm
Eh=3.0 cm
EI=3.0 cm


1

Section : 16 x 75ht
Fc28= 25 MPa Fe= 500 MPa Fissuration peu préjudiciable Coupe feu 1 H

Elévation
Echelle=1/50

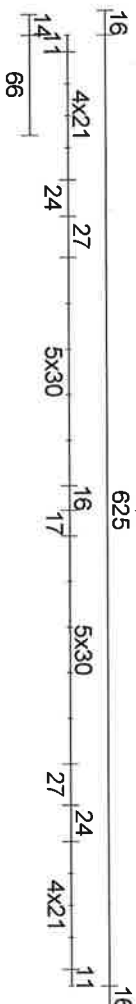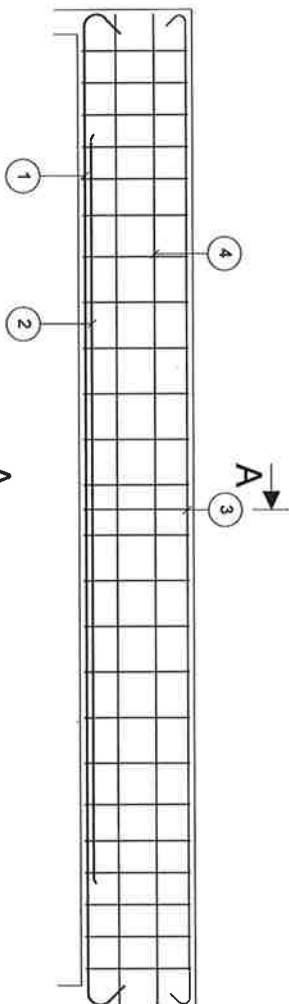

Coupe A-A
Echelle=1/20

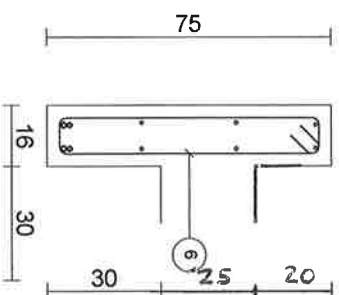

Barre	Lg	Forme
1 2HA14	701	135° 652 135°
2 2HA12	492	492
3 2HA8	676	135° 650 135°
4 4HA8	651	651
5 28HA8	27	10
6 25HA6	170	10


LA PULVATIERE
Plan n° 335
Page 05

Barre	Lg/Poids
HA6	42.5/9.4
HA8	47.1/18.6
HA12	9.8/8.7
HA14	14.0/16.9

MURS EXTERIEURS

CH1 Nombre: 11

Rec: 60 cm

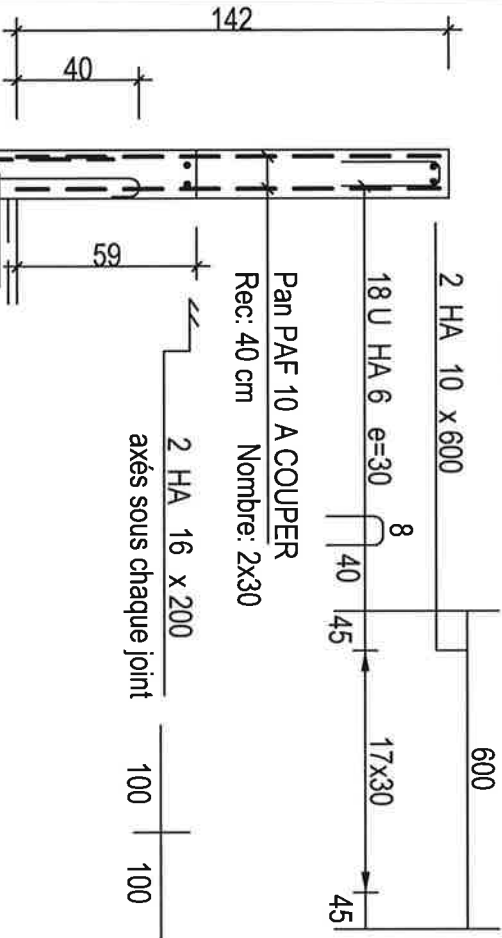

Pan PAF 10 A COUPER
Rec: 40 cm Nombre: 2x30

2 HA 16 x 200
axés sous chaque joint 100 100

BOITE D'ATTENTE

HA 8 e=20
+ 2 HA 14 FILANTS et 190 Ep HA 8 e=30
Lg: 2x57.00 ml
Rec: 70 cm


EXT. INT.

Pan PAF V 320x240

Rec: 40 cm
Nombre: 30

ANGLES MURS


(VALABLE 4 fois)

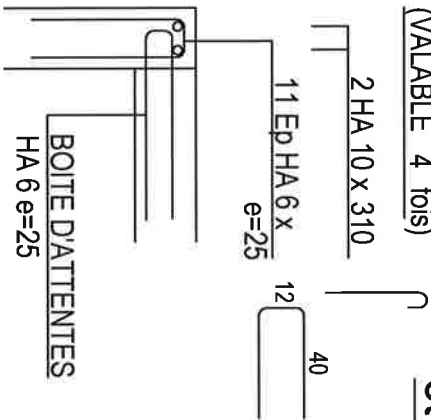


BOITE D'ATTENTES
HA 6 e=25

ARMATURES TETES DE MURS

et OUVERTURES (VALABLE 28 fois)

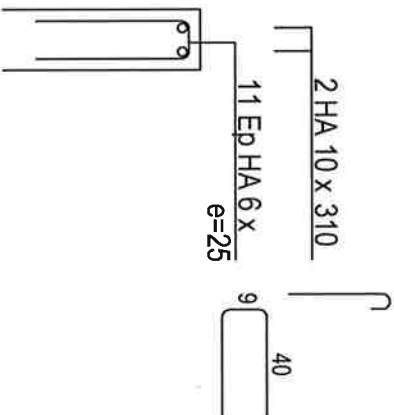


(VALABLE 3 fois)

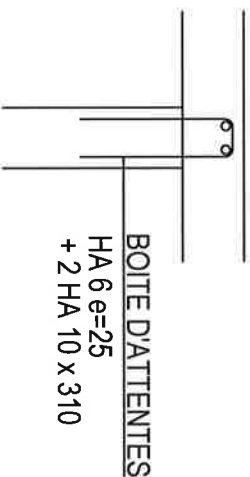


BOITE D'ATTENTES

HA 6 e=25
+ 2 HA 10 x 310



MURS INTERIEURS AVEC CONTINUITE

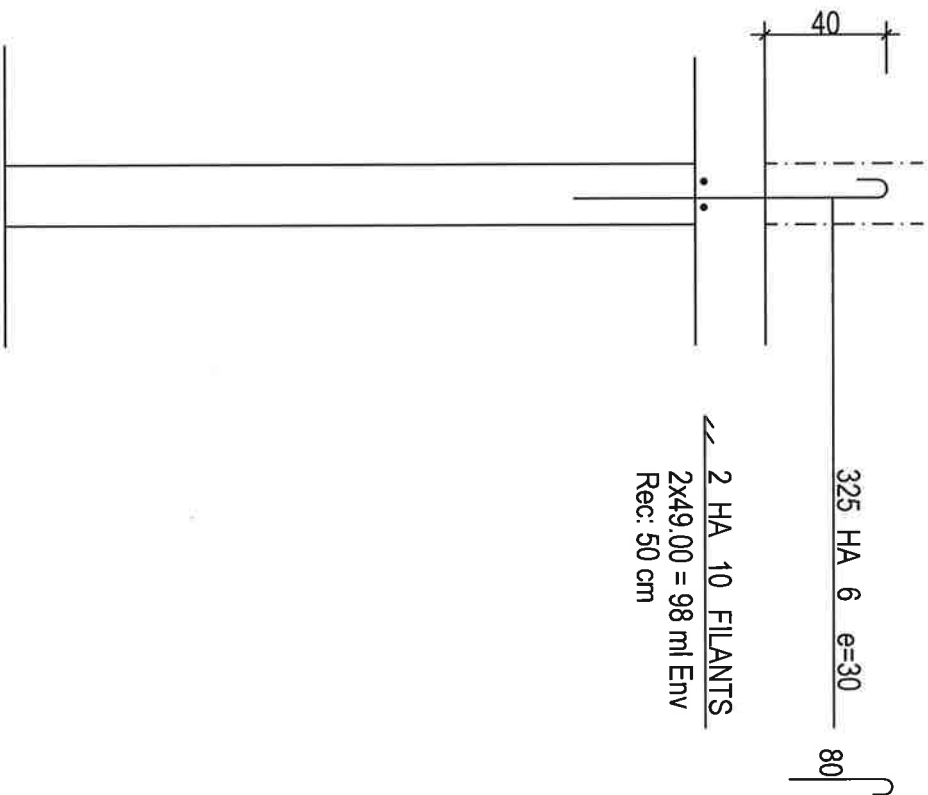

ARMATURES TETES DE MURS

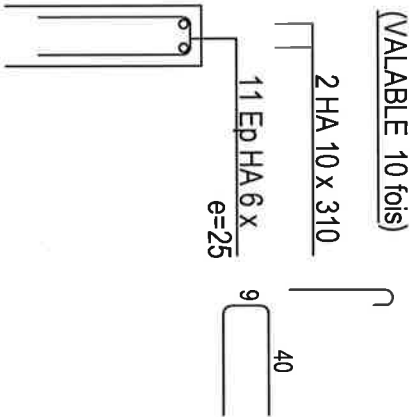

ANGLES MURS

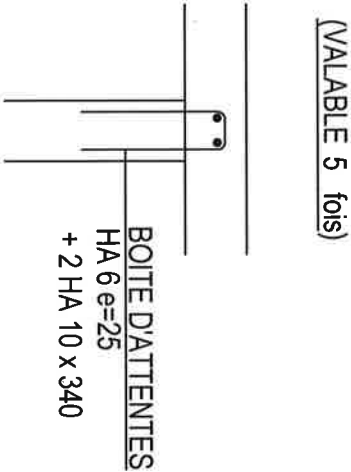
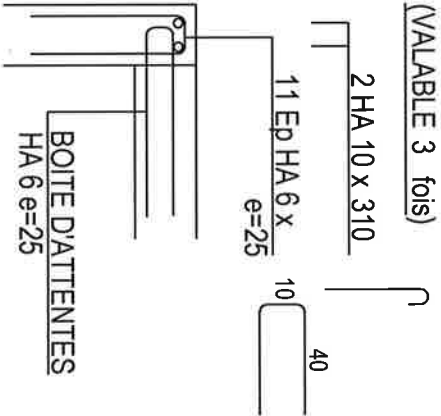


AFF: S.13.12.119	Bât: B	LA MULATIERE-69350 LaMulatiere CREATION de LOGEMENTS	BA au -1	Plan n° B 35	Page: 9
------------------	--------	---	----------	--------------	---------

MURS INTERIEURS SANS CONTINUITE

CH2 Nombre: 6


Rec: 60 cm

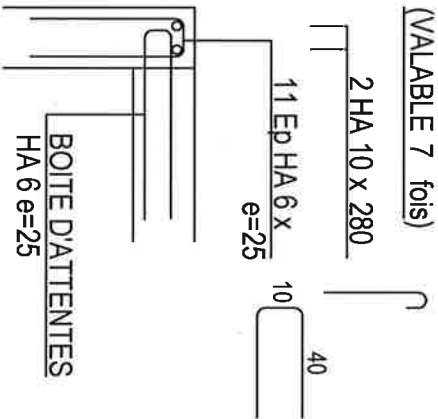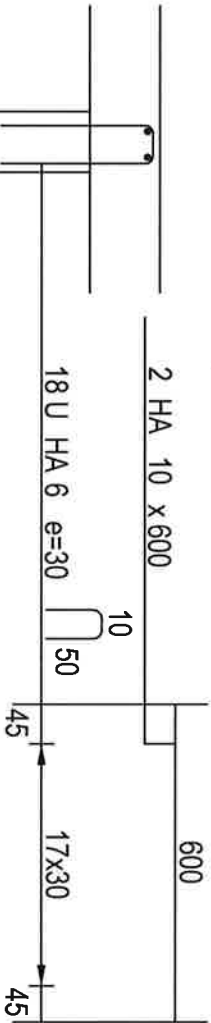

BOITE D'ATTENTES
HA 6 e=25


ARMATURES TETES DE MURS

(VALABLE 4 fois)

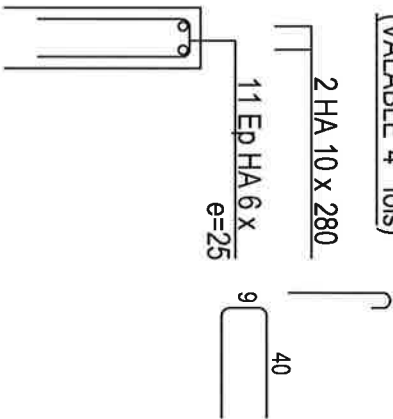

ANGLES MURS

(VALABLE 6 fois)

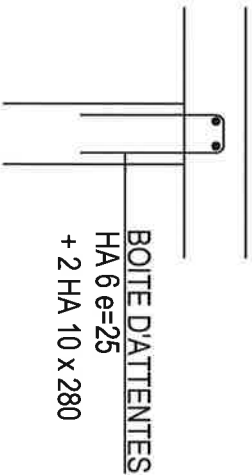

BOITE D'ATTENTES
HA 6 e=25
+ 2 HA 10 x 280

AFF: S.13.12.119	Bât: B	LA MULATIERE-69350 LaMulatiere CREATION de LOGEMENTS	BA au -2	Plan n° B 30	Page: 10
------------------	--------	---	----------	--------------	----------

LINTEAUX INT.

L Nombre: 7




4 HA 10

5 Cad HA 6

20 / 135 \ 20

28 | 4x20 | 27

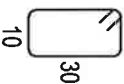

La Nombre: 1




4 HA 12

9 Cad HA 6

20 / 199 \ 20

19 | 8x20 | 20

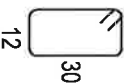

LINTEAUX EXT.

L1


Nombre: 9

PORTEE: 100

L2

Nombre: 2



PORTEE: 200

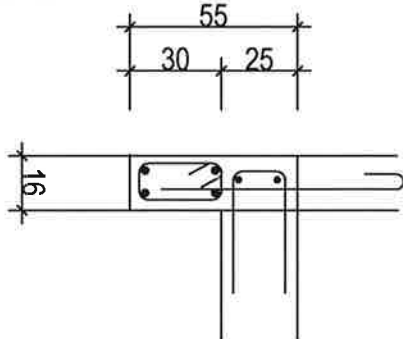

2 HA 10

2 HA 10

5 Cad HA 6

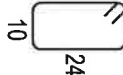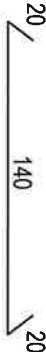


LINTEAUX EXT.

L3

Nombre: 3

PORTEE: 300

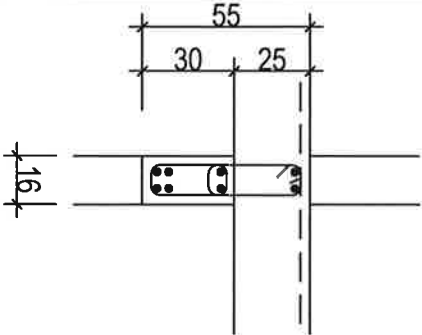

2 HA 10



2 HA 8

2 HA 16 x 300 AXES

2 HA 16

15 Cad HA 6

15 Ep HA 6

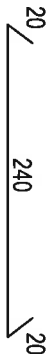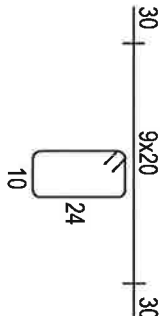

2 HA 10

2 HA 16

10 Cad HA 8

