


ARMATURES SUPERIEURES

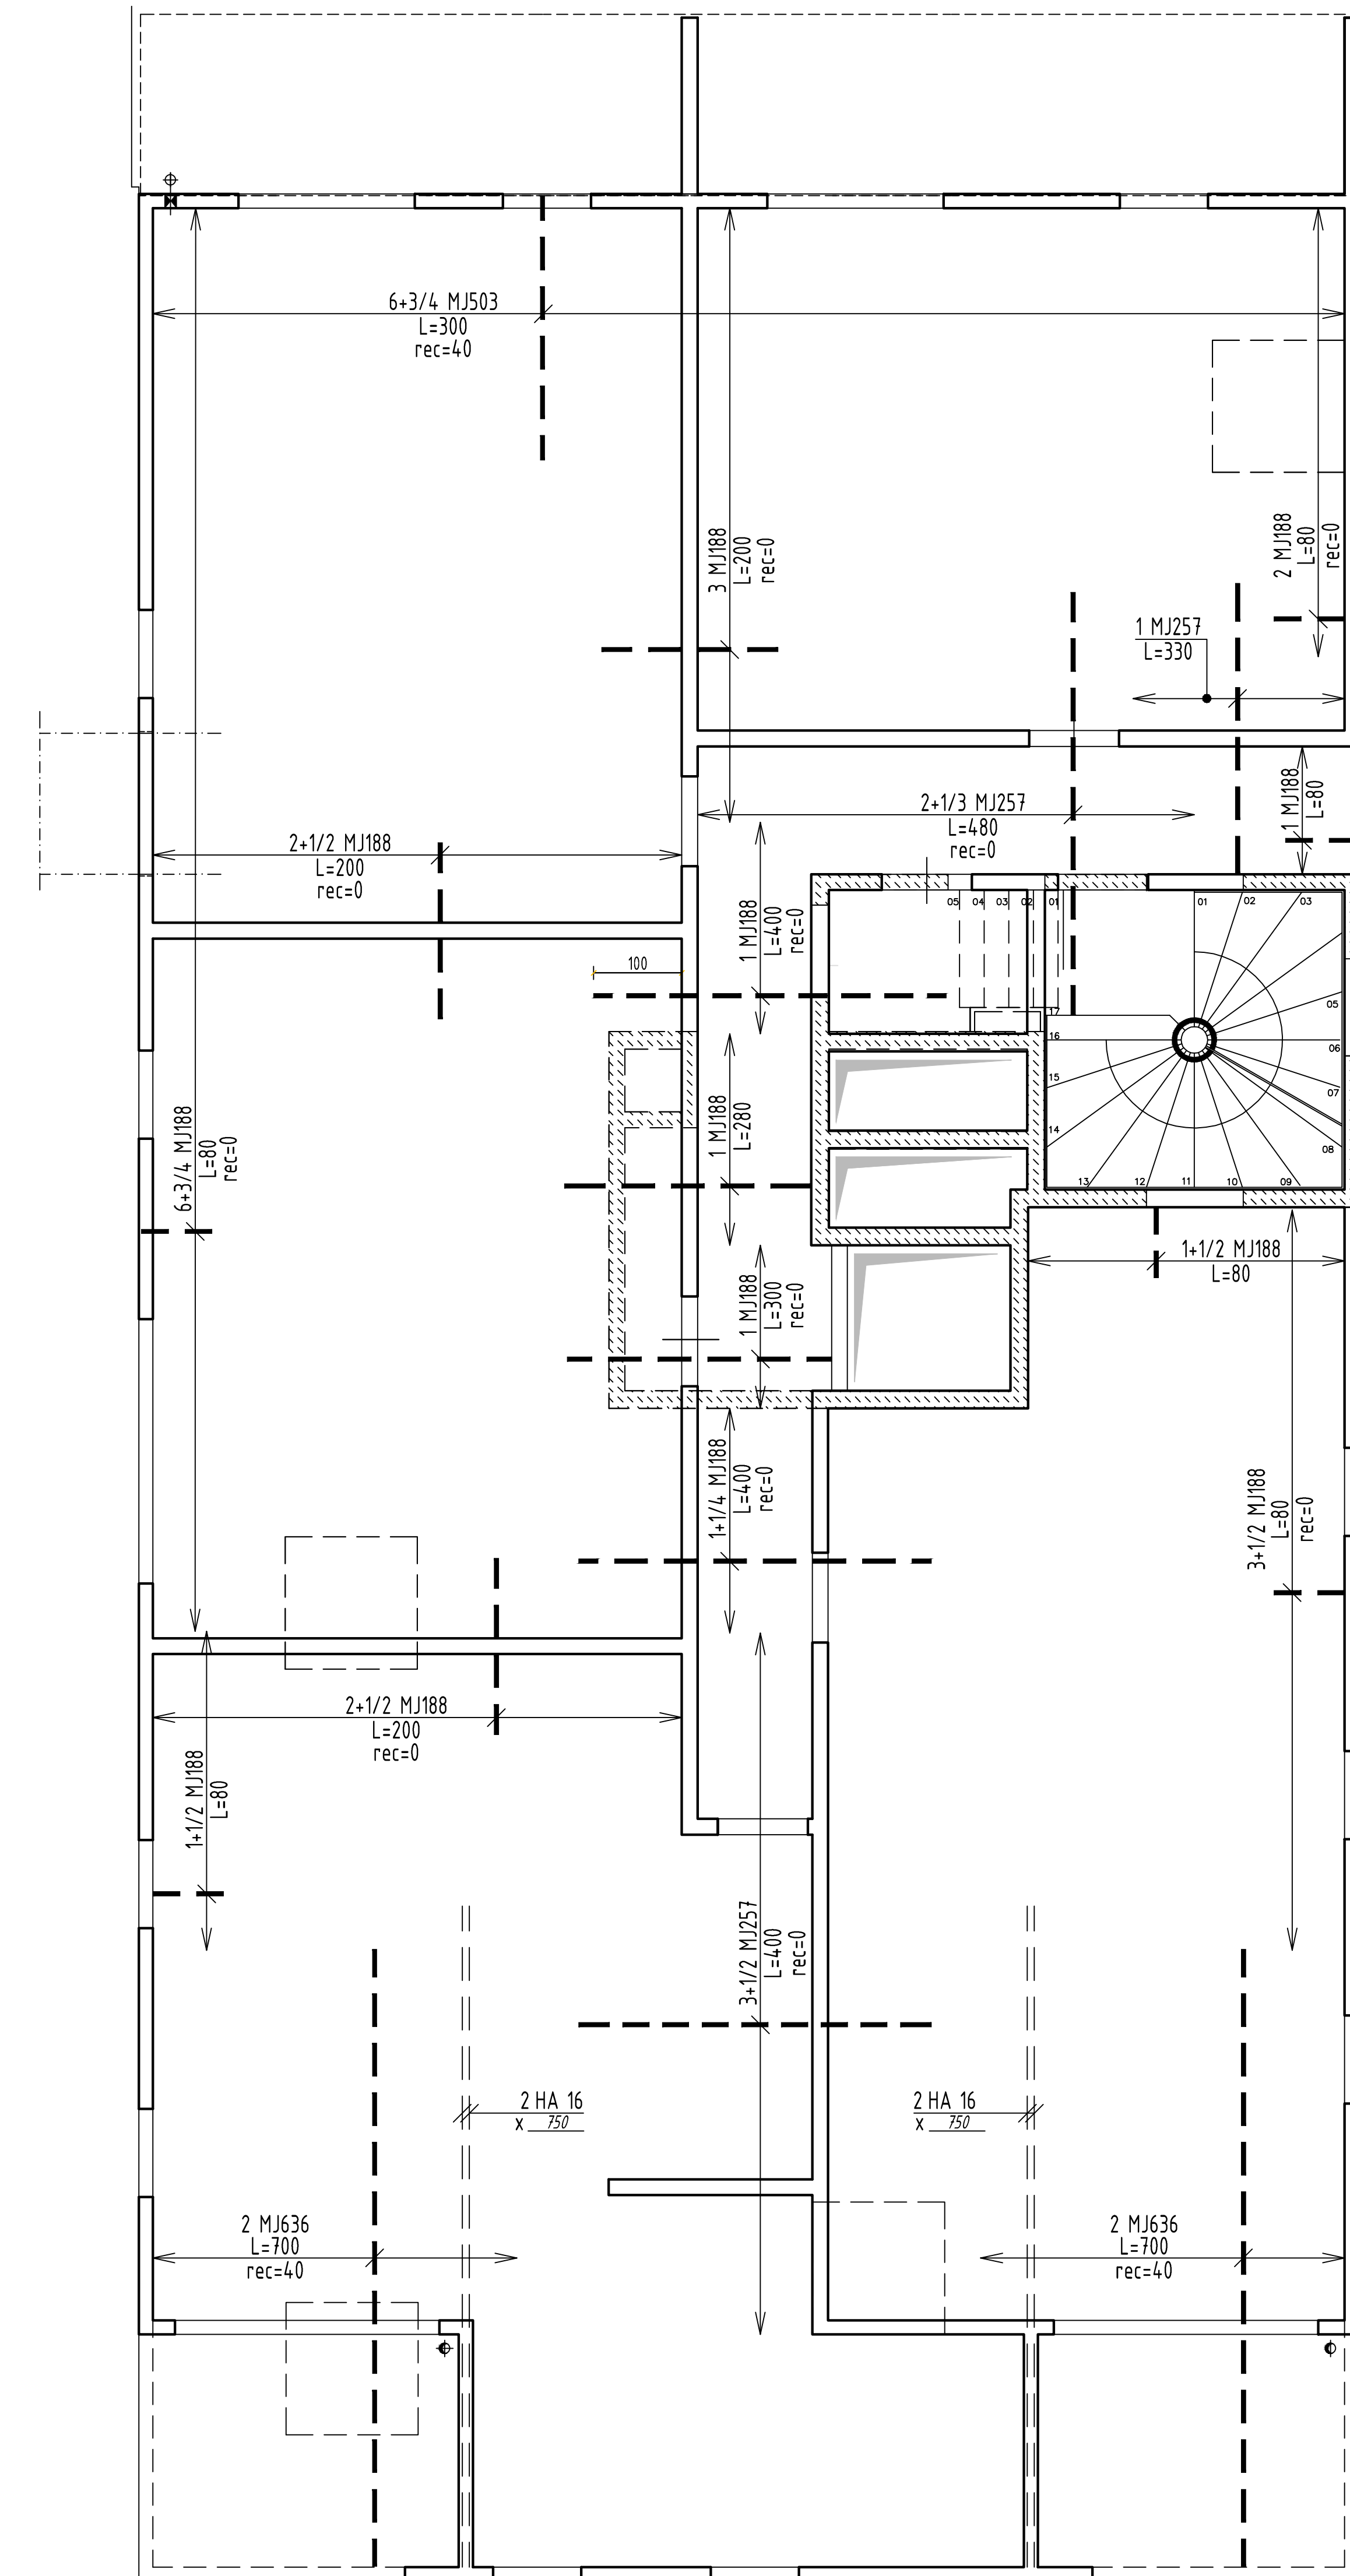

Position des équerres d'angles dans dalle 3 MA 14 x

100
100 | 3 plat

coupe vue en plan

Affaire N°
13.12.119

Trellis	Lgr (cm)	Nbr
MJ188	570	17
MJ251C	180	1
	160	1
	240	1+2/3
	280	1+1/3
	300	3+1/2
	440	2
	560	1
MJ257	620	4+2/3
	760	1+3/4
	150	4+1/2
	180	4+2/3
	560	10+2/3

Treillis	Lgr (cm)	Nbr
MJ188	80	20+1/2
	200	8
	280	1
	300	1
	400	2+1/4
MJ257	330	1
	400	3+1/2
	480	2+1/3
MJ503	300	6+3/4
MJ636	700	4