




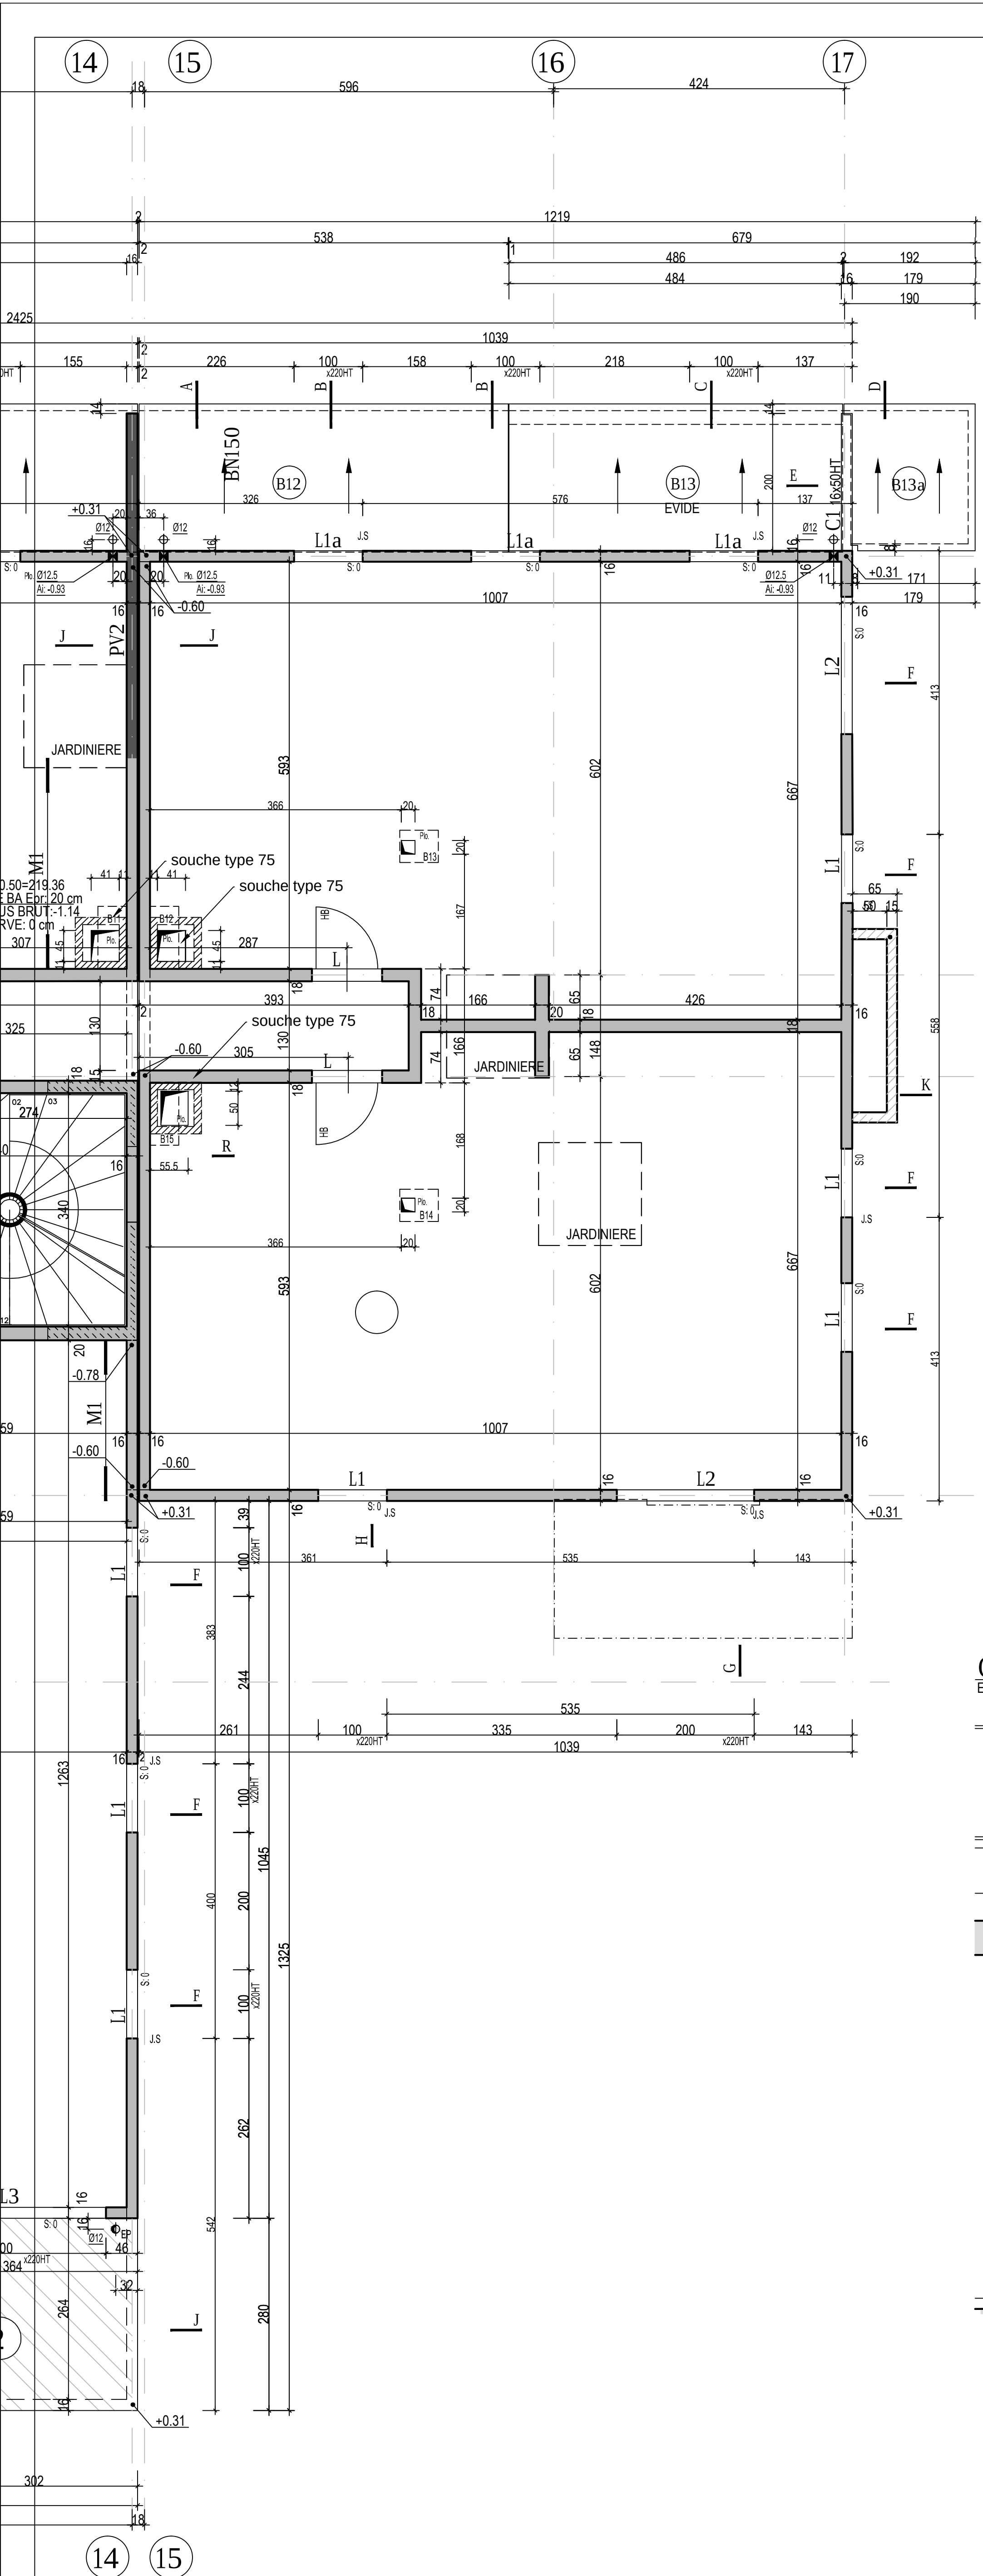


COUPE A
Ech: 1/25

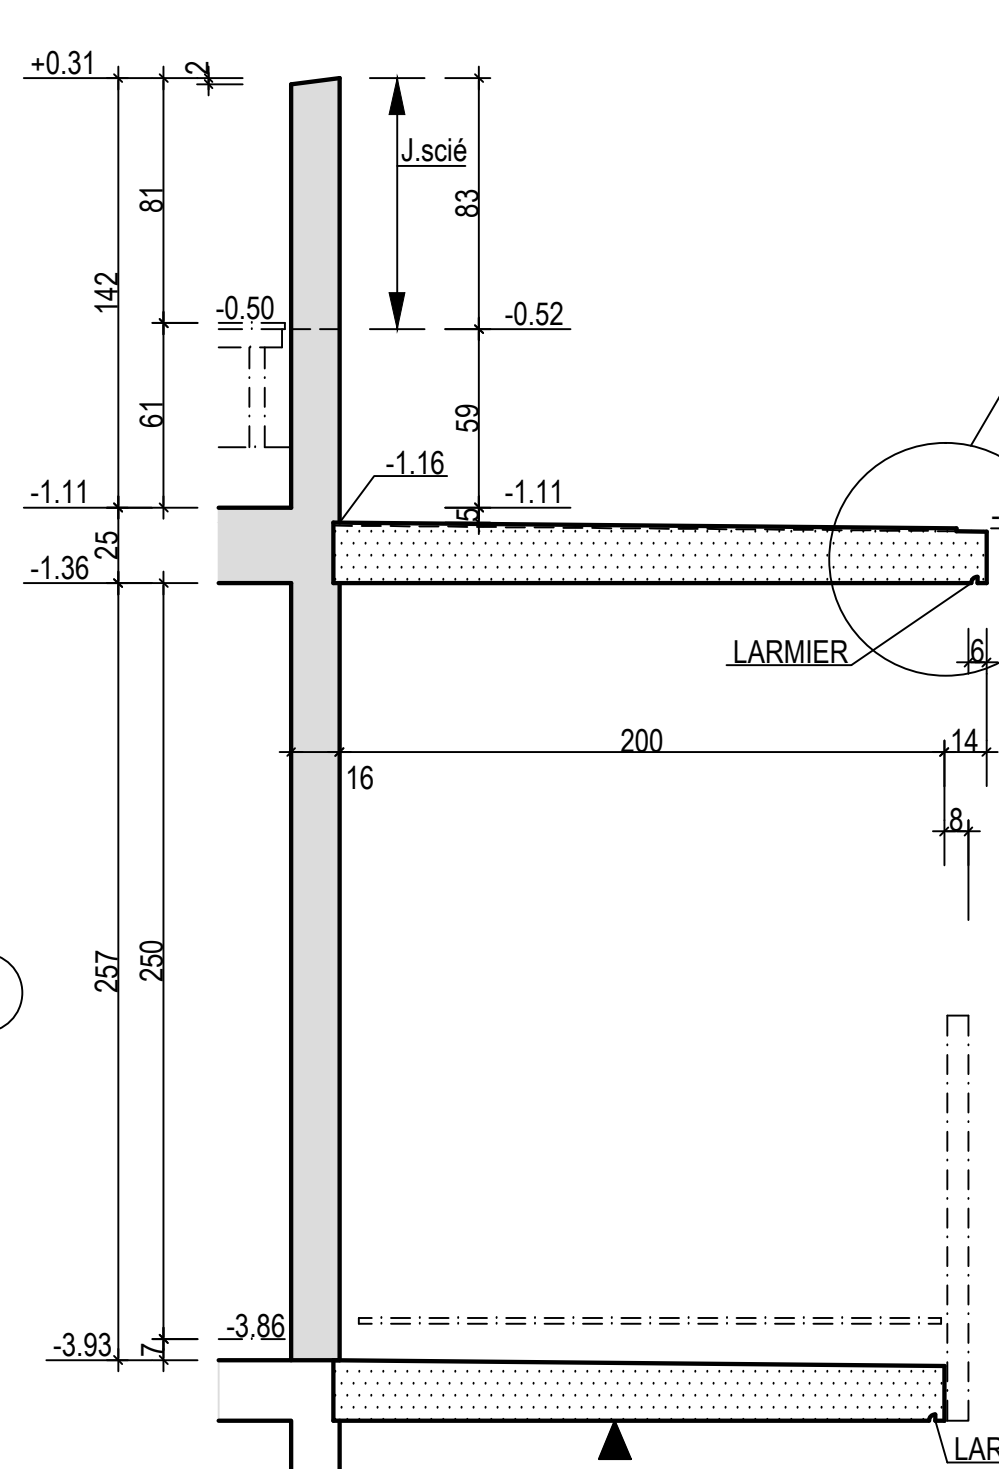


COUPE B
Ech: 1/25

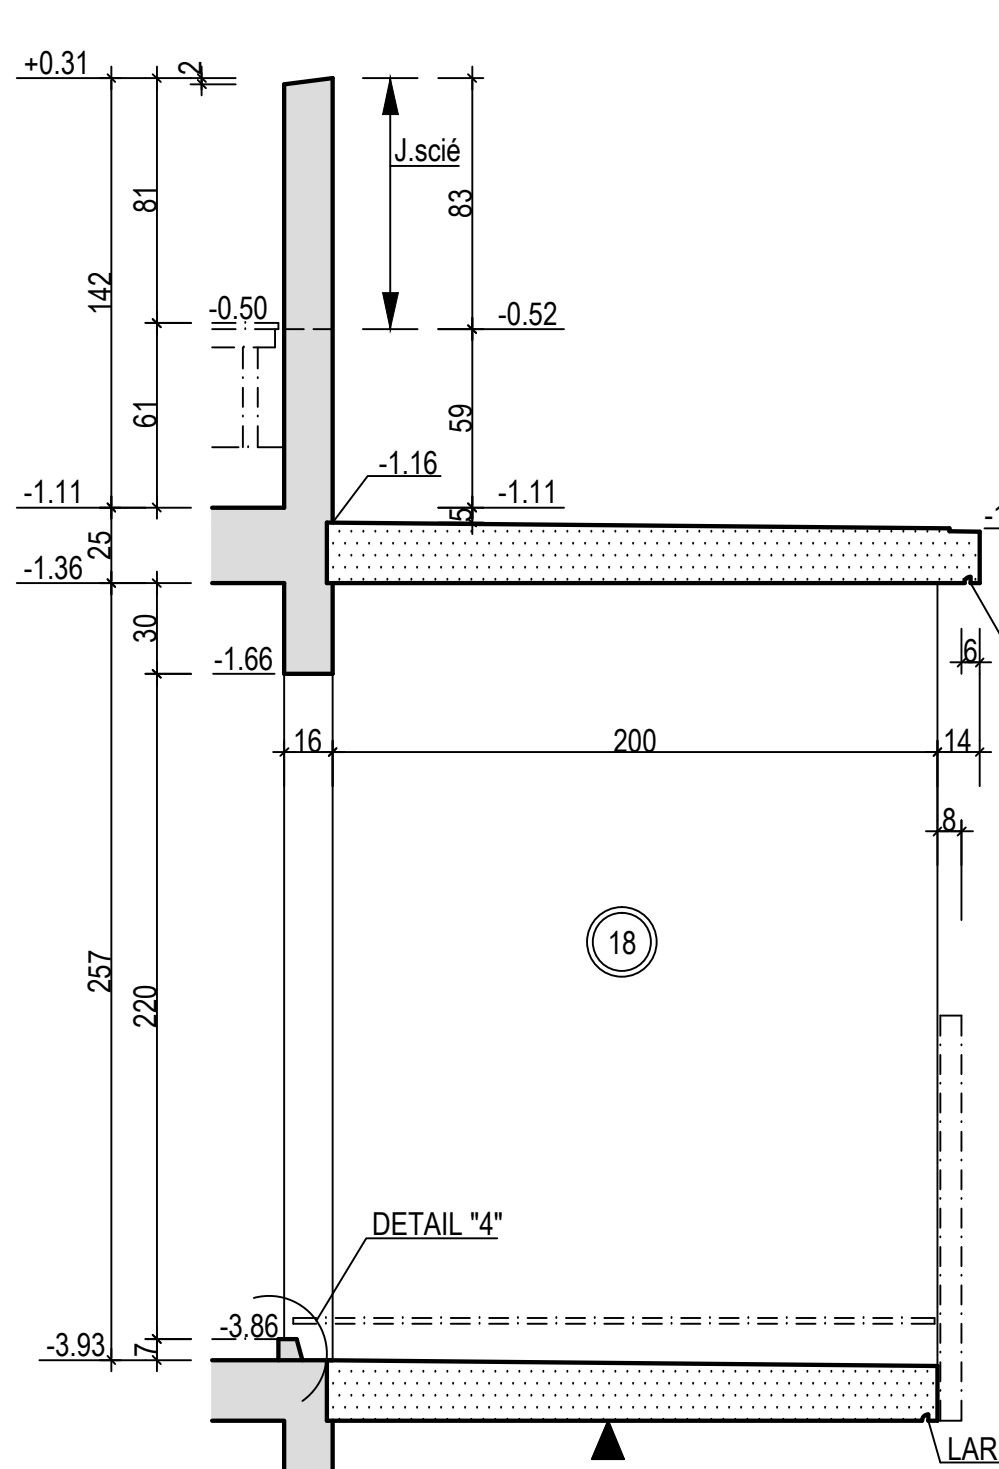


COUPE C
Ech: 1/25

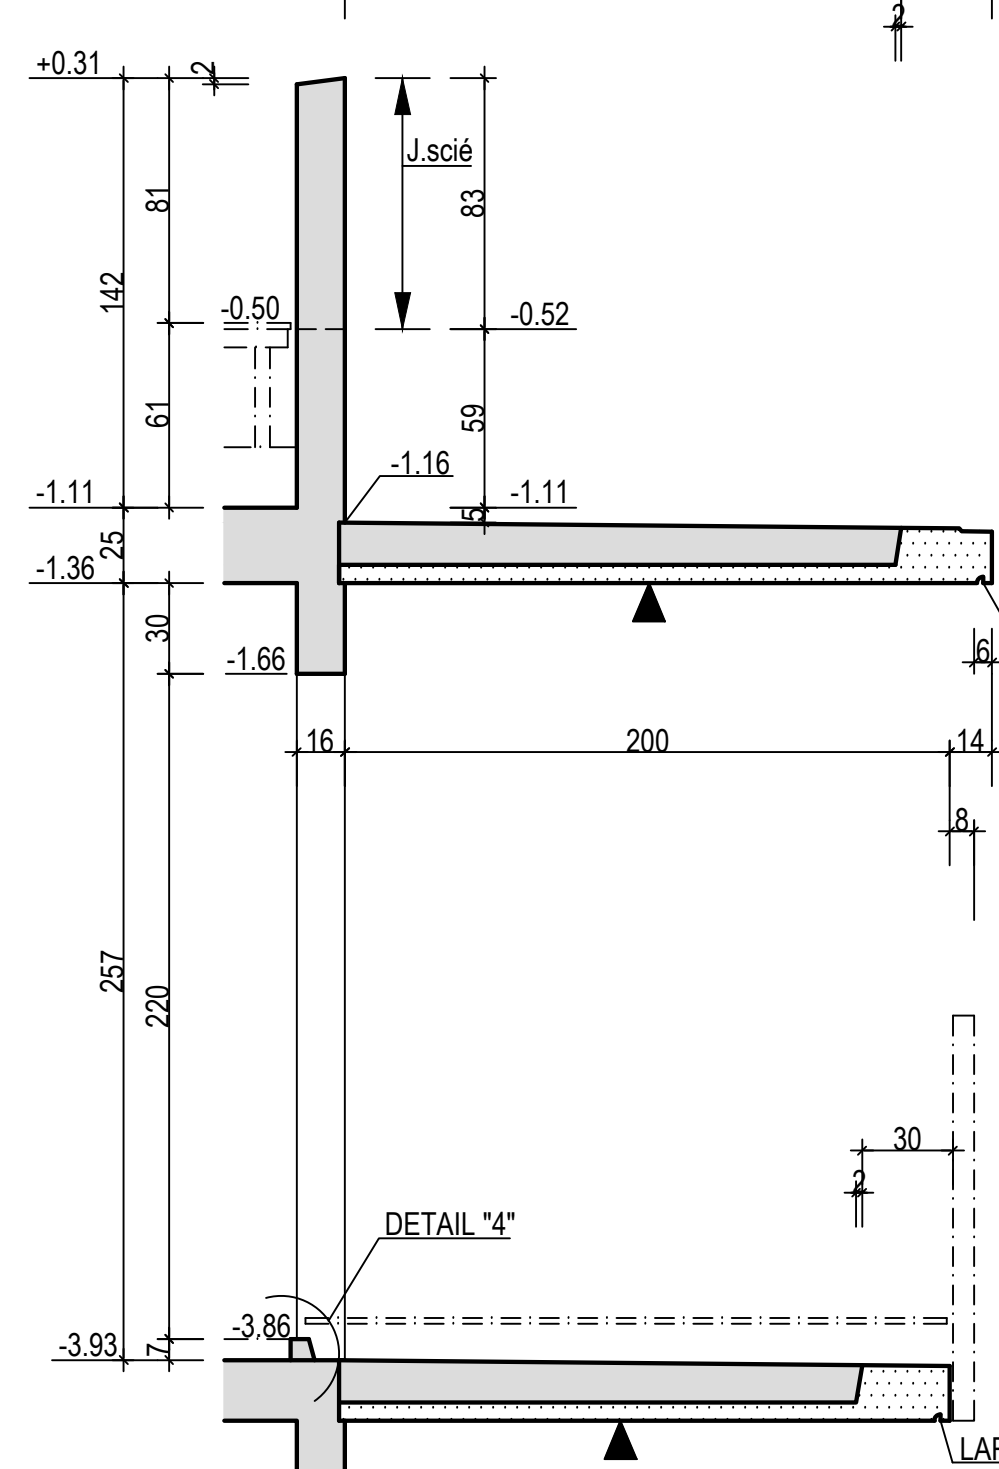


COUPE D
Ech: 1/25

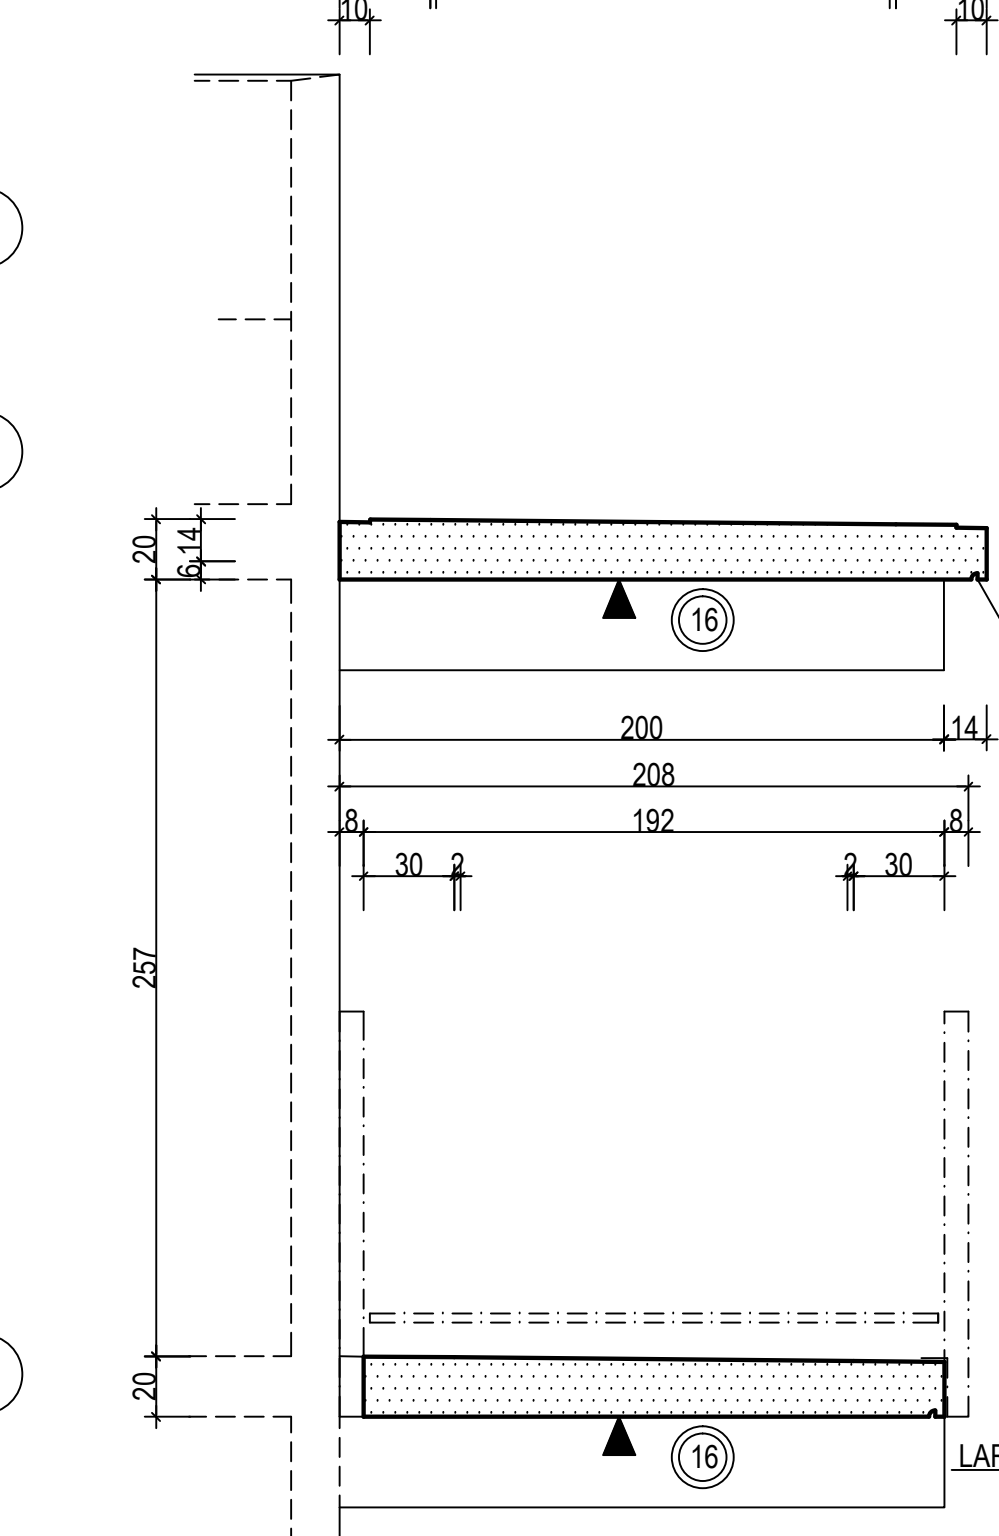

COUPE E
Ech: 1/25

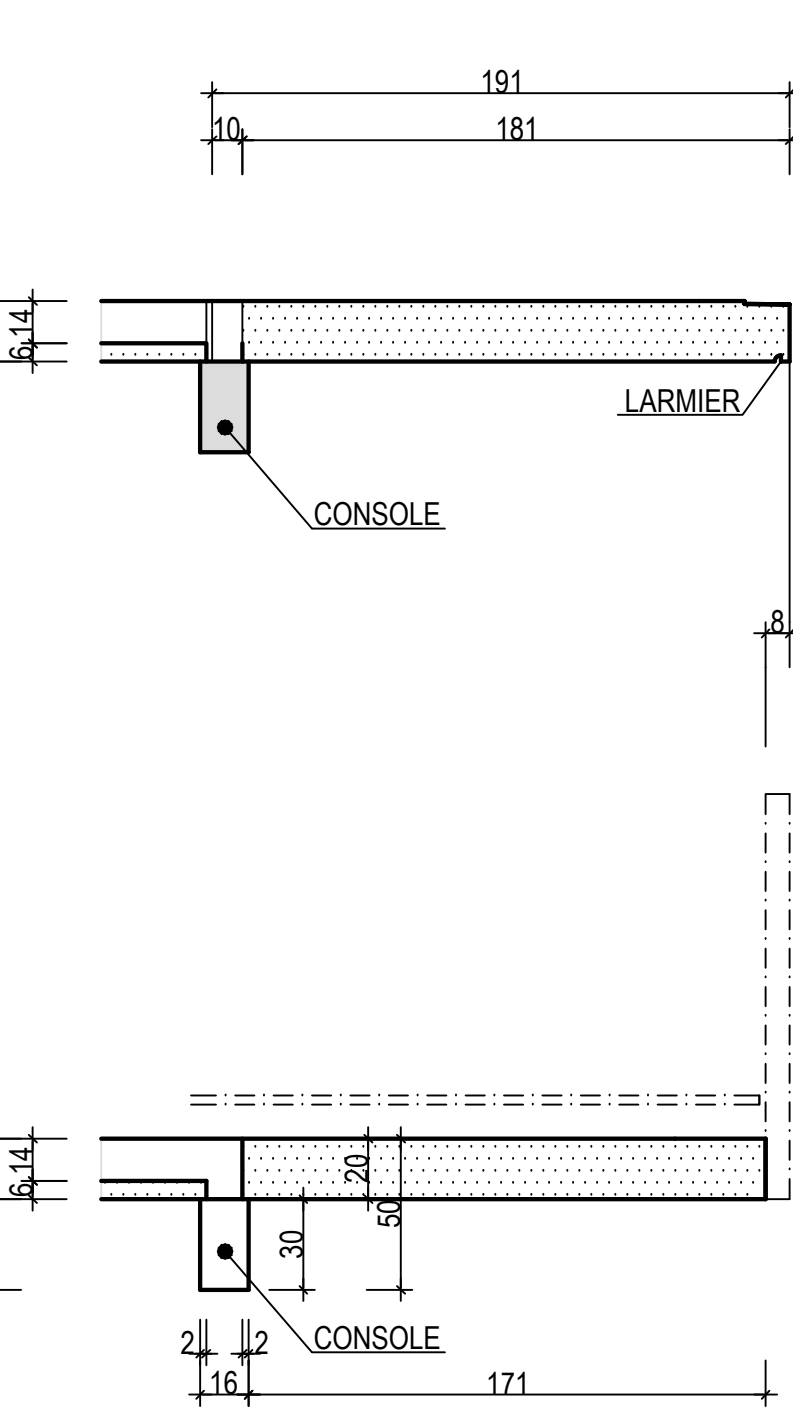


COUPE F
Ech: 1/25

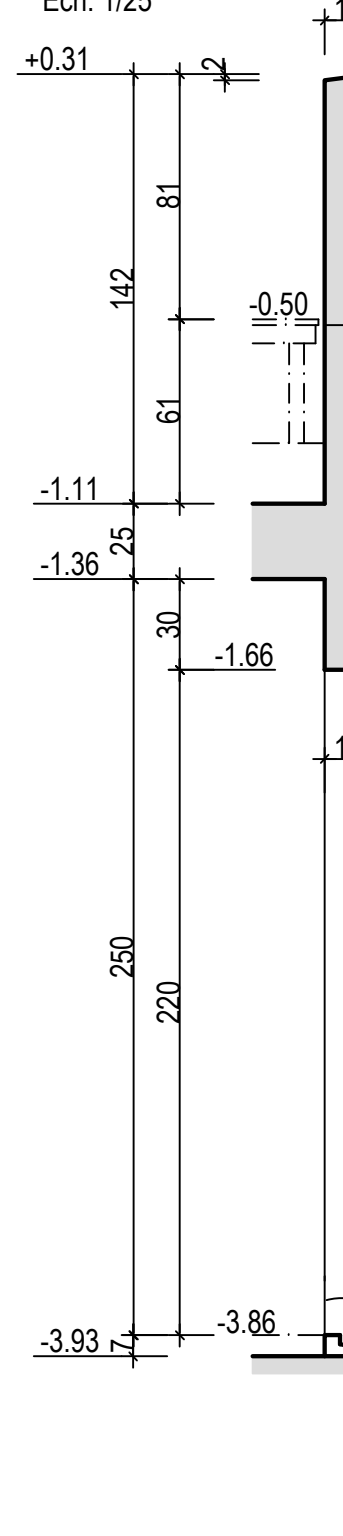

COUPE G
Ech: 1/25



COUPE H
Ech: 1/25

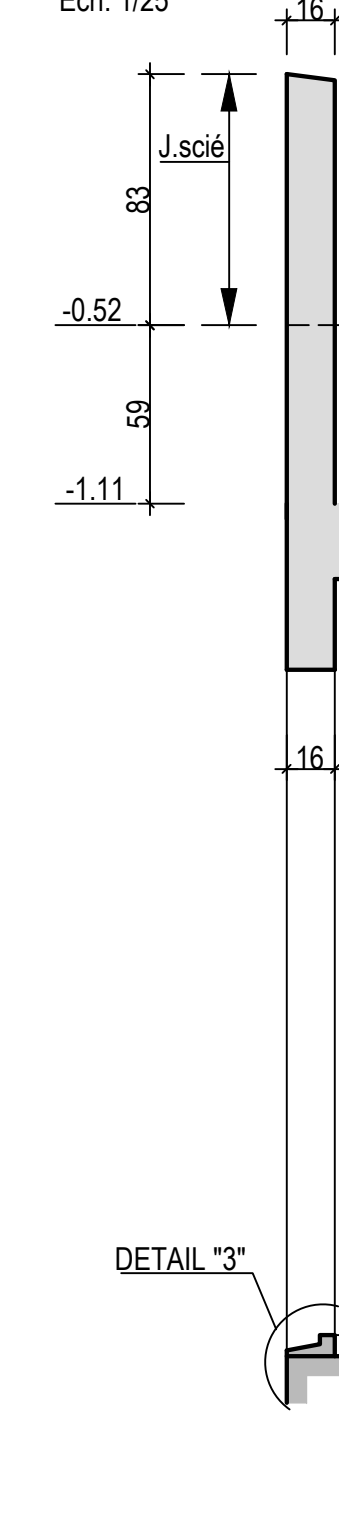


DALLES


FINI: -0.50=-220.00
DALLE BA Epr: 25 cm
DESSUS BRUT: -1.11
RESERVE: 61 cm

COUPES D et E N'EXISTE PAS
±0.00 = 220.50

COUPE J
Ech: 1/25

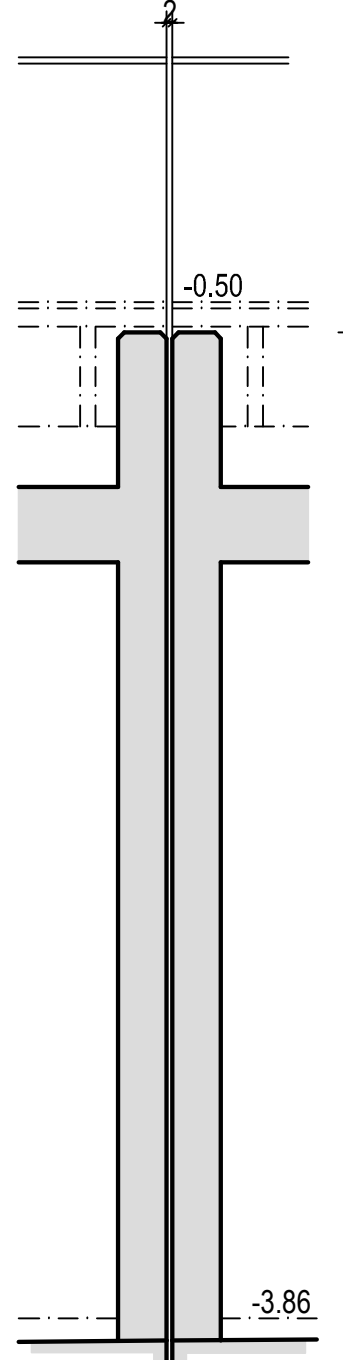


COUPE K
Ech: 1/25

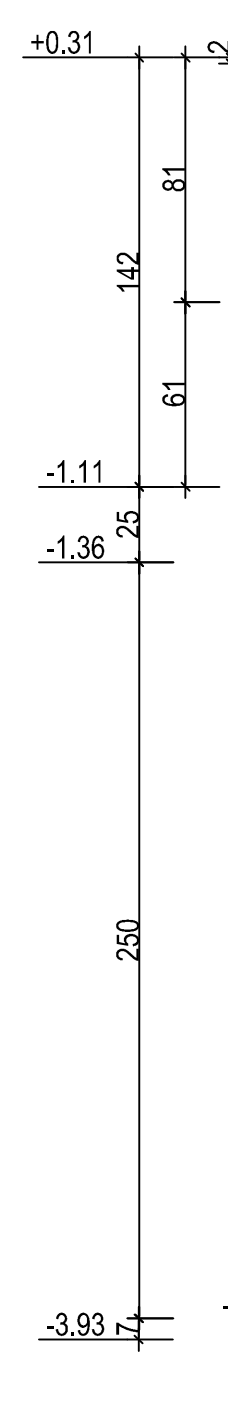


SEUILS


DETAIL "3"

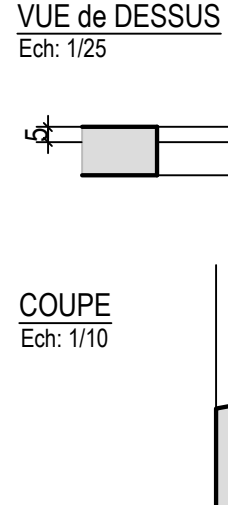


DETAIL "4"

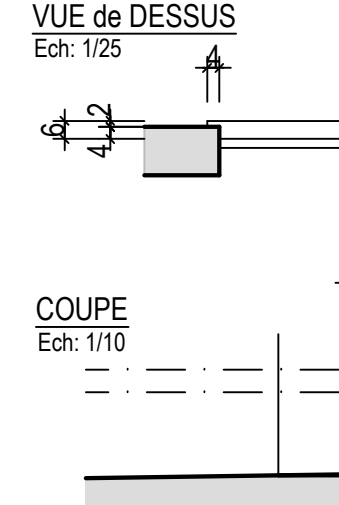

DETAIL "5"

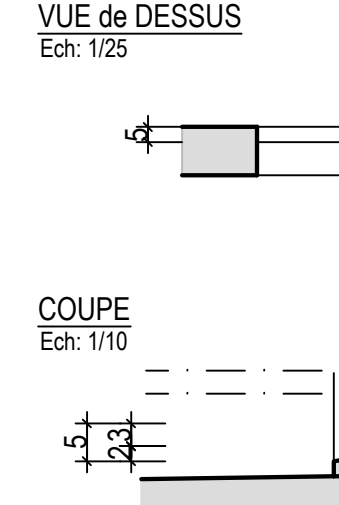

DETAIL "6"

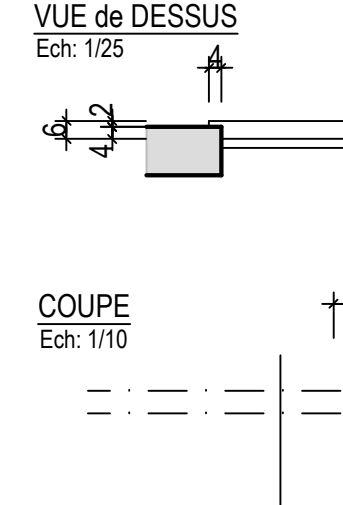

NOAHO

Chemin de Fontanière - 69350 La Mulatière
Création de logements

Les entreprises réalisant les travaux devront tenir compte des derniers plans architecturaux lors de la réalisation des travaux.
Les plans du bureau MATTE ne doivent servir qu'au corps d'état concerné et doivent être des plans d'exécution.

ARCHITECTES: ATELIER DE LA PASSERELLE
BET STRUCTURE: MATTE SAS
BET FLUIDES: PRELEM
ECONOMISTE: EXECO
BUREAU DE CONTRÔLE: Bureau VERITAS

MO DELEGUE: PSO Ingénierie
CSPS: SUD EST COORDINATION
OPC:
ENTREPRISES: Fontanel-pbc

Bât B
PLANCHER sur -1 entre files 14 et 19
Coffrage

INDICE	DATE	MODIFICATIONS
A	05/04/2016	MISE A JOUR COUPE K
B	14/04/2016	MODIFIE HAUTEUR OUVERTURES FACADE EST
C	10/05/2016	MISE A JOUR OUVERTURES FILES 17 et COUPE F

MATTE
BUREAU D'ETUDES
STRUCTURES ET FLUIDES
119 RUE LOUIS STALINSKI 69100 VILLEURBANNE
Tél : 04 72 44 12 87 Fax 04 72 44 26 59
E-mail : mat@matte.fr

Dessiné par : J.B.O.
Contrôlé par : P.L.M.
Echelle : 1/150"

DOE
Contrainte de sol:
Aciers HA (T) FeE500
Aciers Dux (O) FeE235
Aciers TS FeE500
Béton C20/25
Enrobage = 3 cm

PLAN N°
B37 C
DATE : 29/03/2015

Affaire N°
13.12.119