

NOHAO

Chemin de Fontanière-69350 La Mulatière

Création de logements

Les entreprises réalisant les travaux devront tenir compte des derniers plans architecte lors de la réalisation des travaux
Les plans du be MATTE ne doivent servir qu'au corps d'état concerné et doivent être des plans d'exécution.

ARCHITECTE(S):	Atelier DE LA PASSERELLE	M.O. Délégué:	.
BET STRUCTURE:	BET MATTE	M.O.:	.
BET FLUIDES:	PRELEM	CSPS:	PSO ingénierie
ECONOMISTE:	EXECO	M.O.E.:	SUD EST COORDINATION
BUREAU DE CONTROLE:	VERITAS	ENTREPRISE(S):	Fontanel-pbc

Bât: B
BA au REZ entre files 11 et 14

DOE

INDICE	DATE	MODIFICATIONS

Aciers HA (T) FeE500
Aciers Doux (Ø) FeE 235
Aciers TS FeE 500
Béton fc28 >= 25MPa
Enrobage = 3 cm

PLAN N°
B41 0

DATE : 11/02/2016


MATTÉ
BUREAU D'ÉTUDES
STRUCTURES ET FLUIDES

119 BOULEVARD STALINGRAD 69100 VILLEURBANNE
Tél. 04 72 44 02 87 Fax 04 72 44 26 59
E-mail : bet@matte.fr


Dessiné par : J.BONDETTI
Contrôlé par : P. LIN
Ech :

Affaire N°
S.13.12.118


REPERAGE

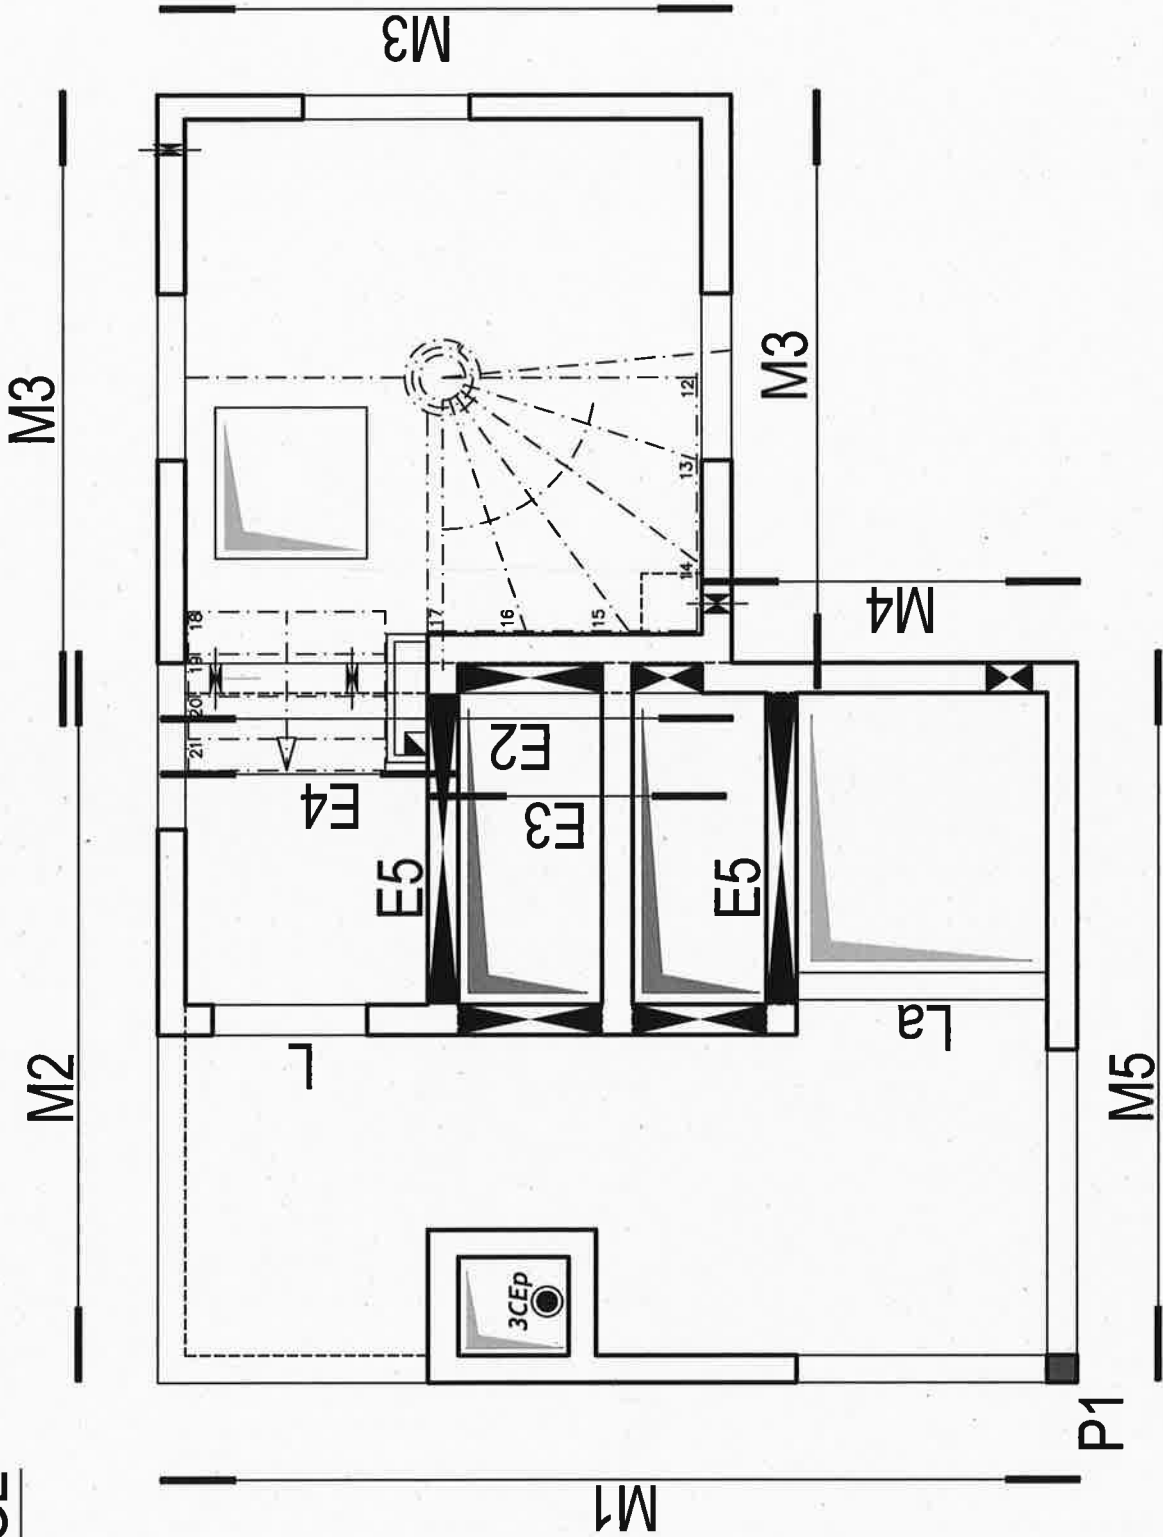


MURETS POUR PASSERELLE AU NIVEAU -1.11

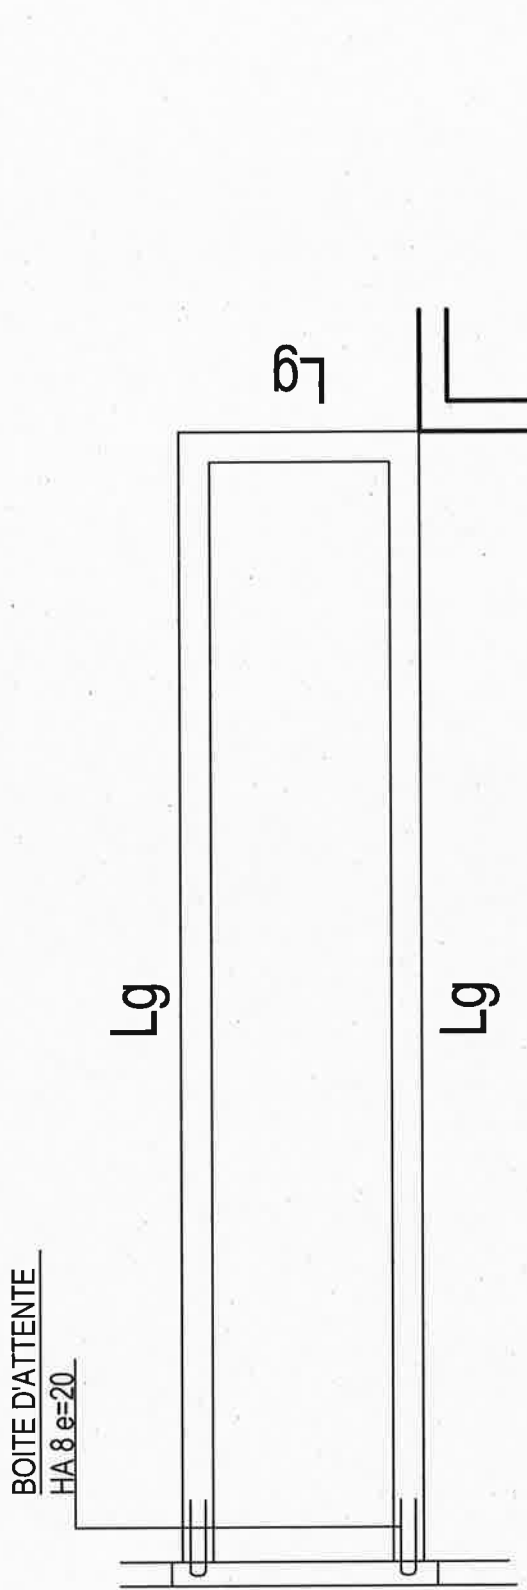

ANGLES MURS

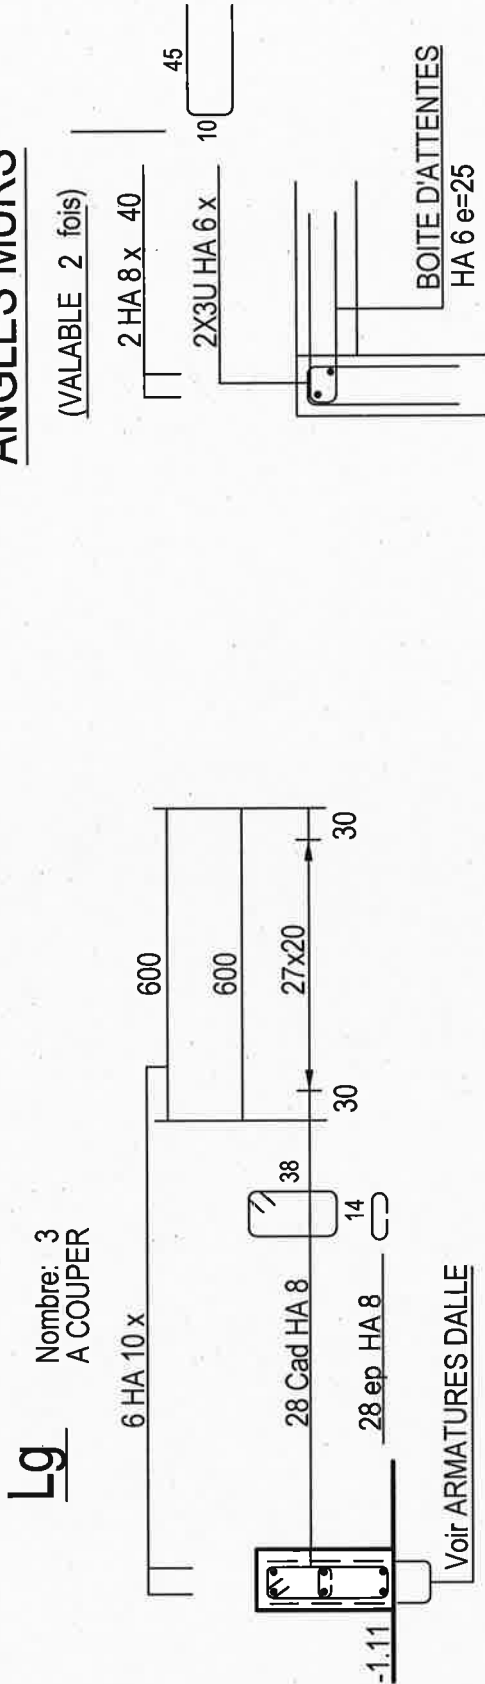


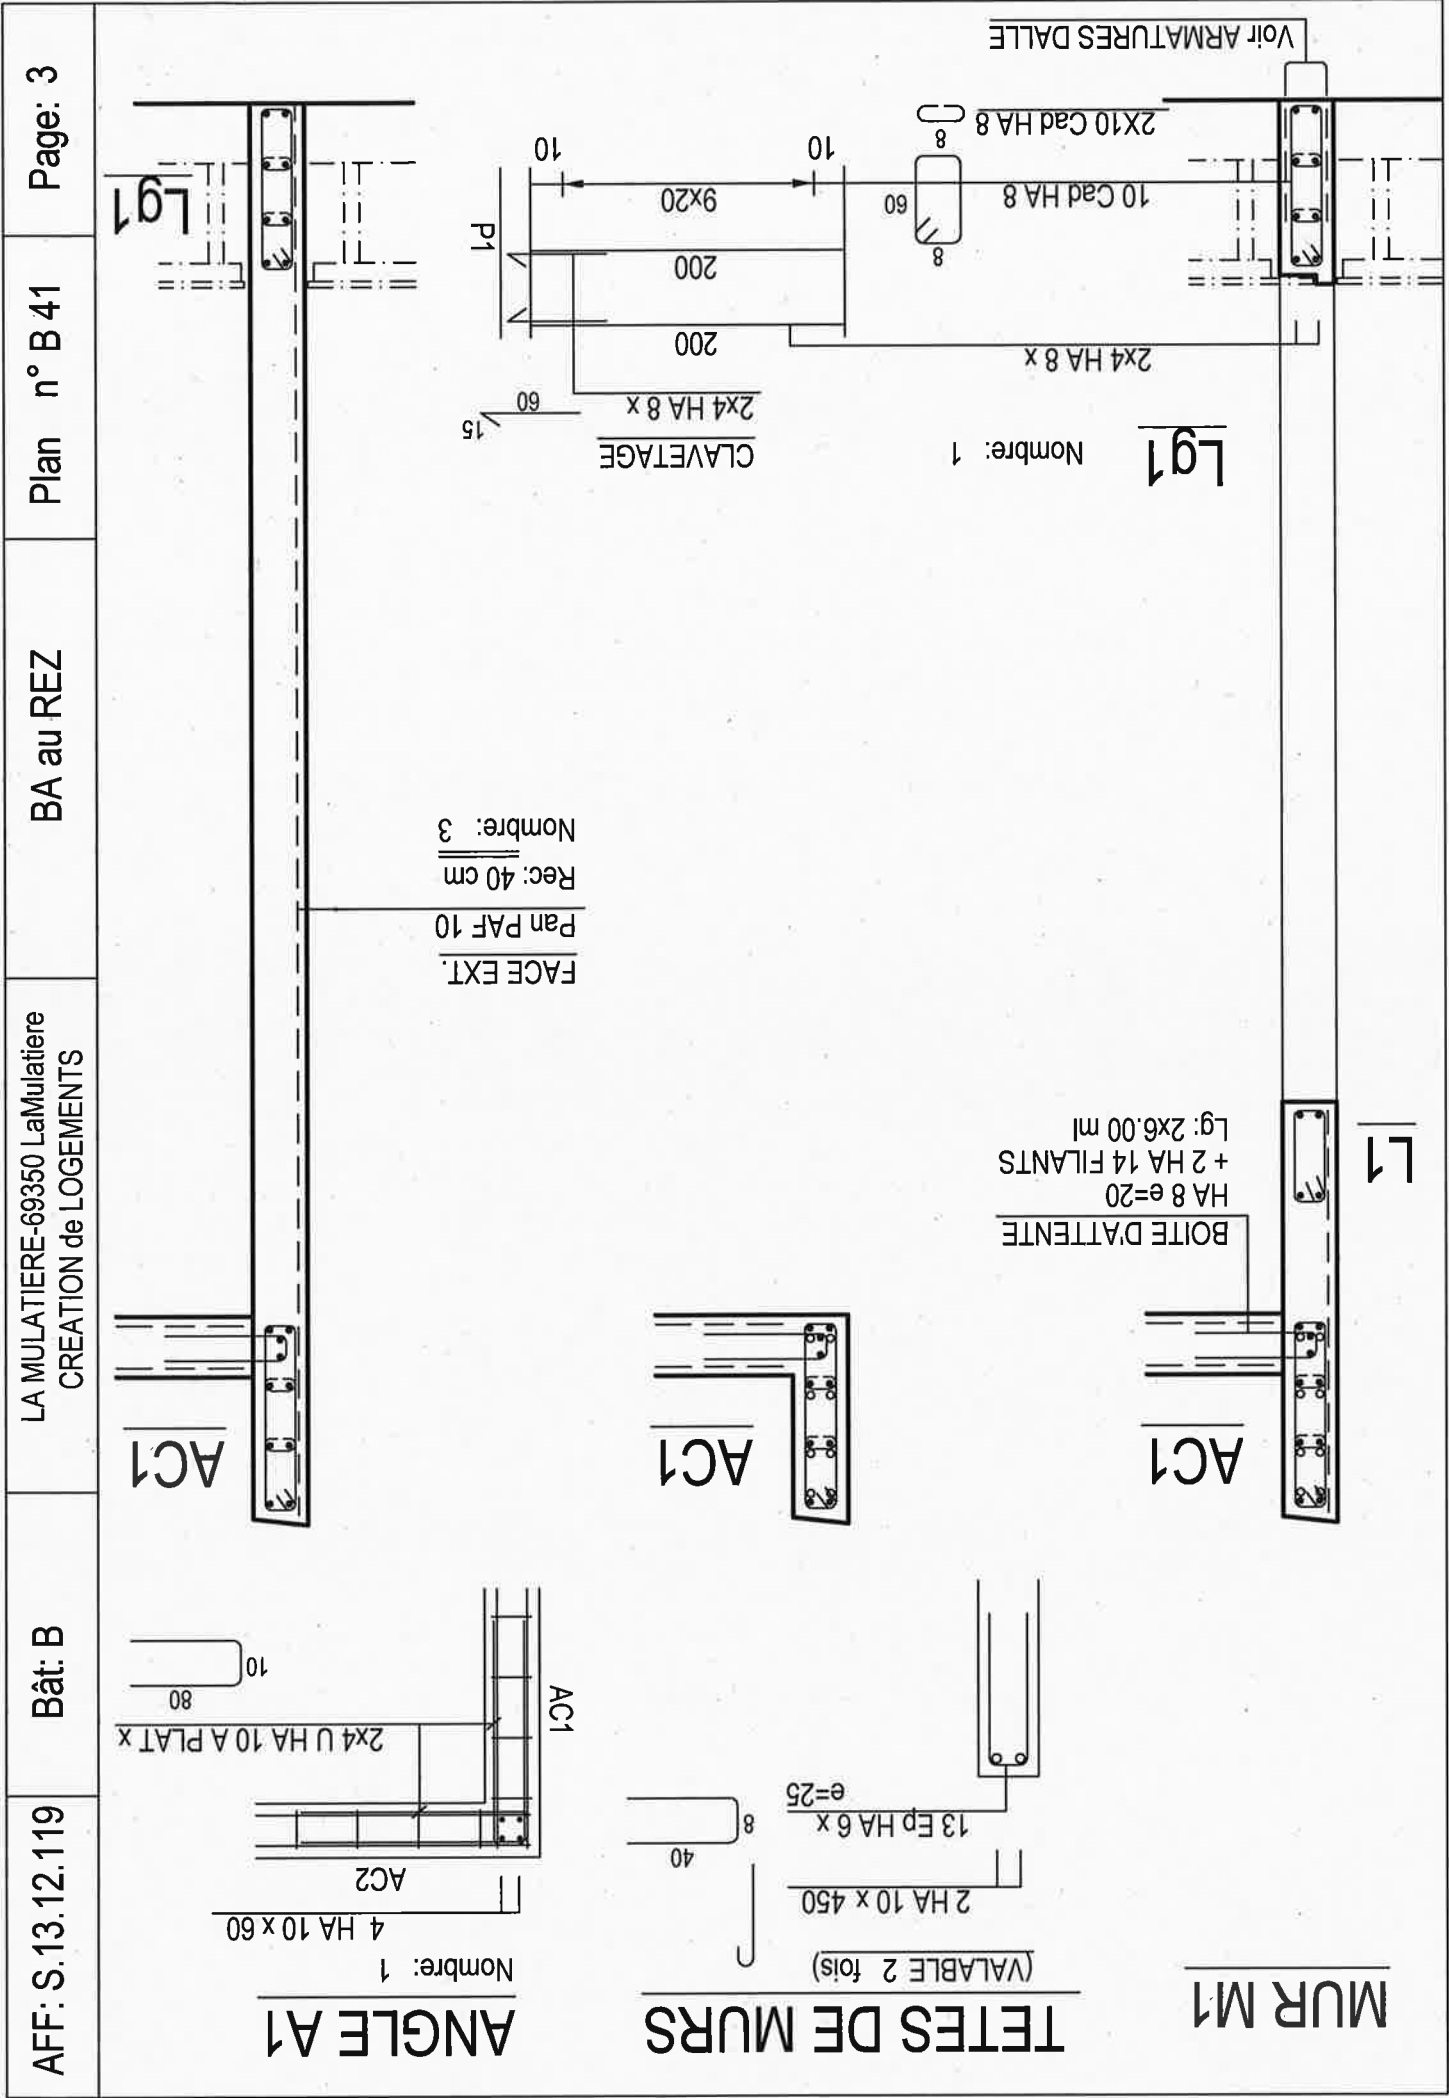

MUR M1


AC1

Nombre: 1

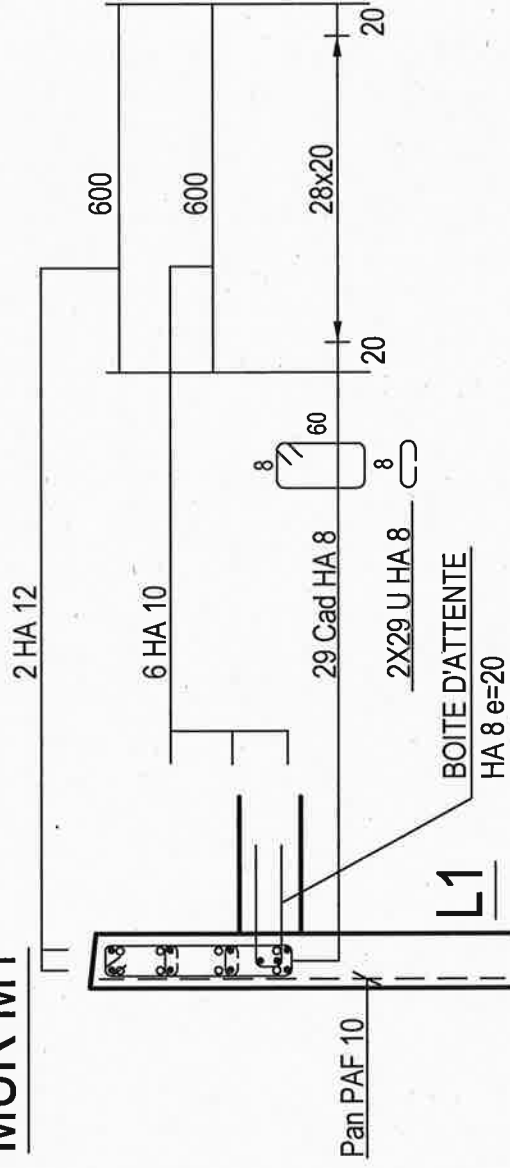


12

Nombre: 1

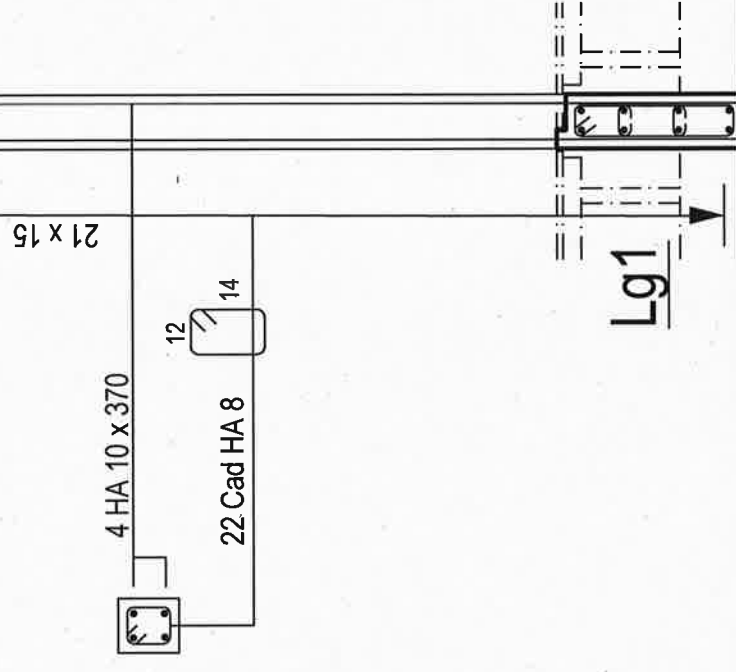

Nombre: 1

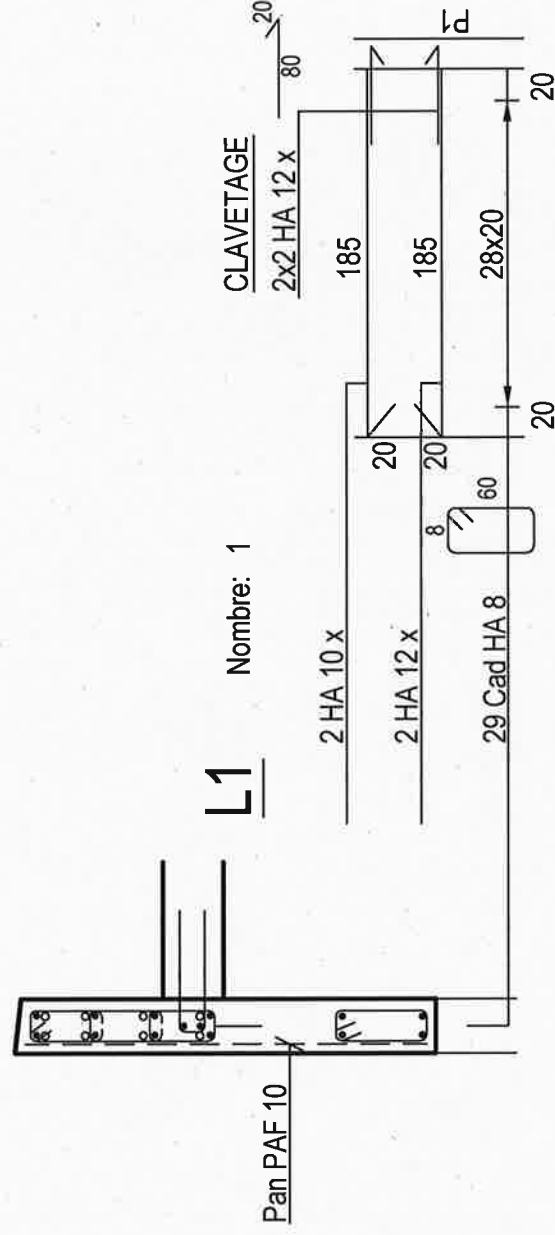


Lq1

AFF: S.13.12.119	Bât: B	LA MULATIERE-69350 LaMulatiere CREATION de LOGEMENTS	BA au REZ	Plan n° B 41	Page: 5
MUR M2 AC1 AC2					

MUR M2


ANGLE A1

VOIR PAGE 0

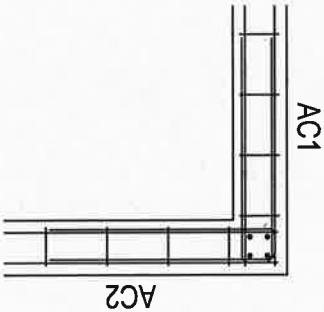


FACE EXT.
Pan PAF 10
Rec: 40 cm
Nombre: 1

BOITE D'ATTENTE
HA 8 e=20
+ 2 HA 14 FILANTS
Lg: 2x6.00 ml

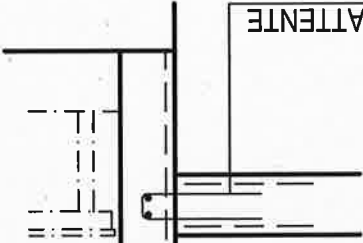


MUR M2

AC2 Nombre: 1

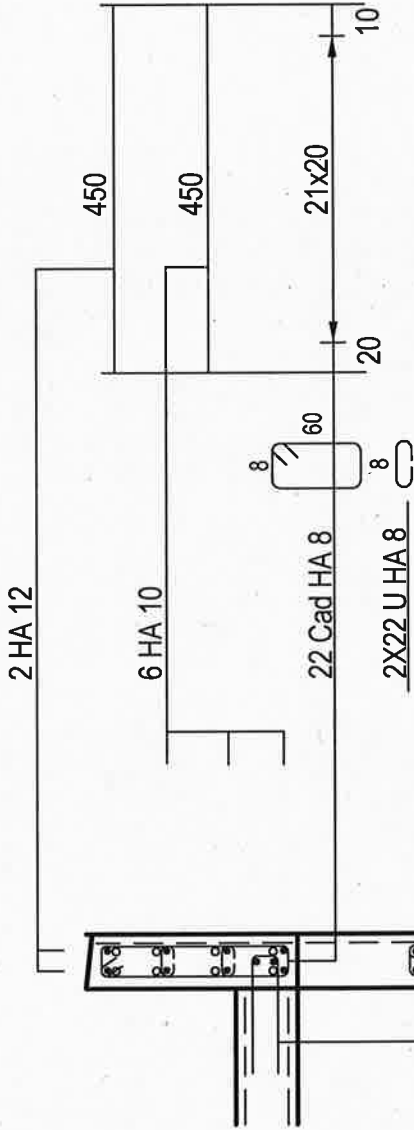


BOITE D'ATTENTE
HA 8 e=20
+ 2 HA 14 FILANTS
Lg: 2x6.00 ml

L2 Nombre: 1

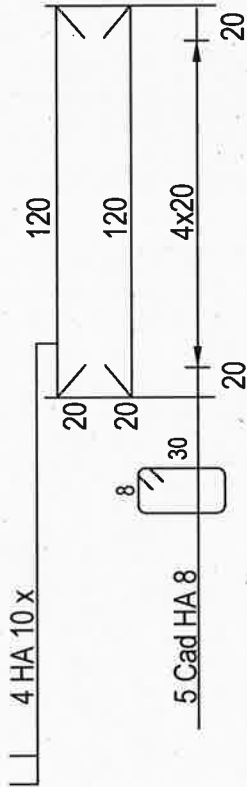


E2

Nombre: 1

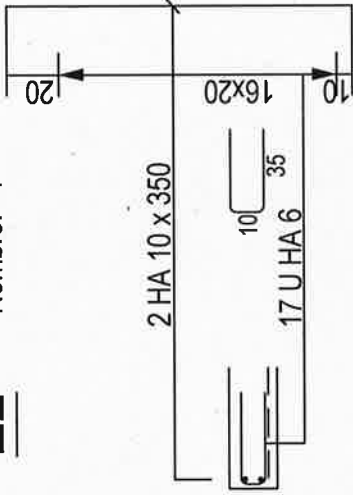

MUR M3

AC3
Nombre: 3

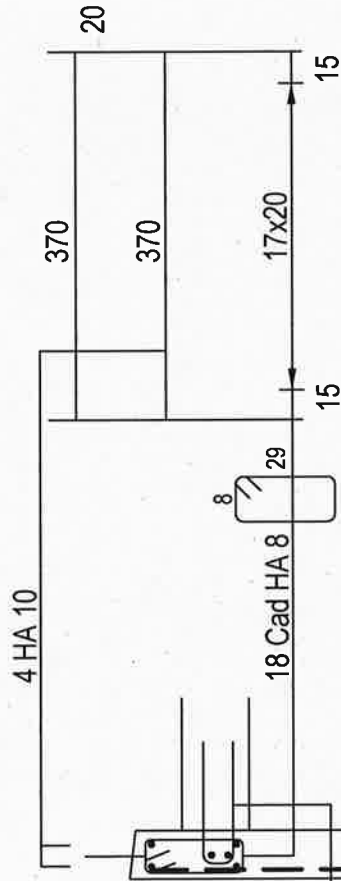


BOITE D'ATTENTE
HA 8 e=20
+ 2 HA 14 FILANTS
Lg: 2x12.00 ml

EXT.


INT.

Pan PAF 10
Rec: 40 cm
Nombre: 2x6


ANGLES MURS

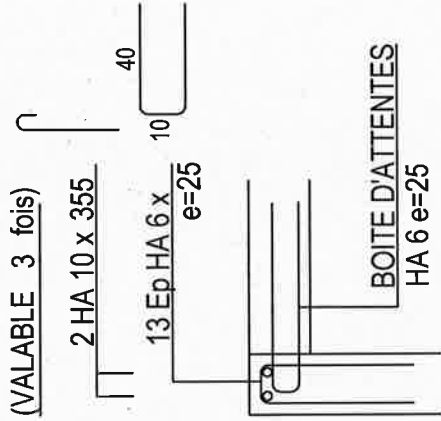


ARMATURES TETES DE MURS

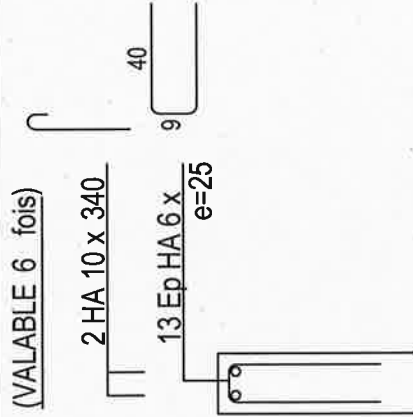



ARMATURES REJINGOT

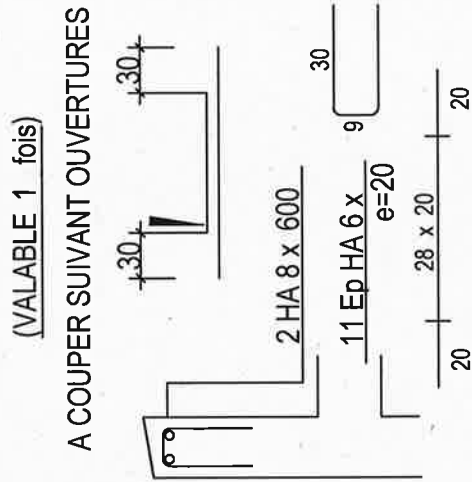


MUR M4

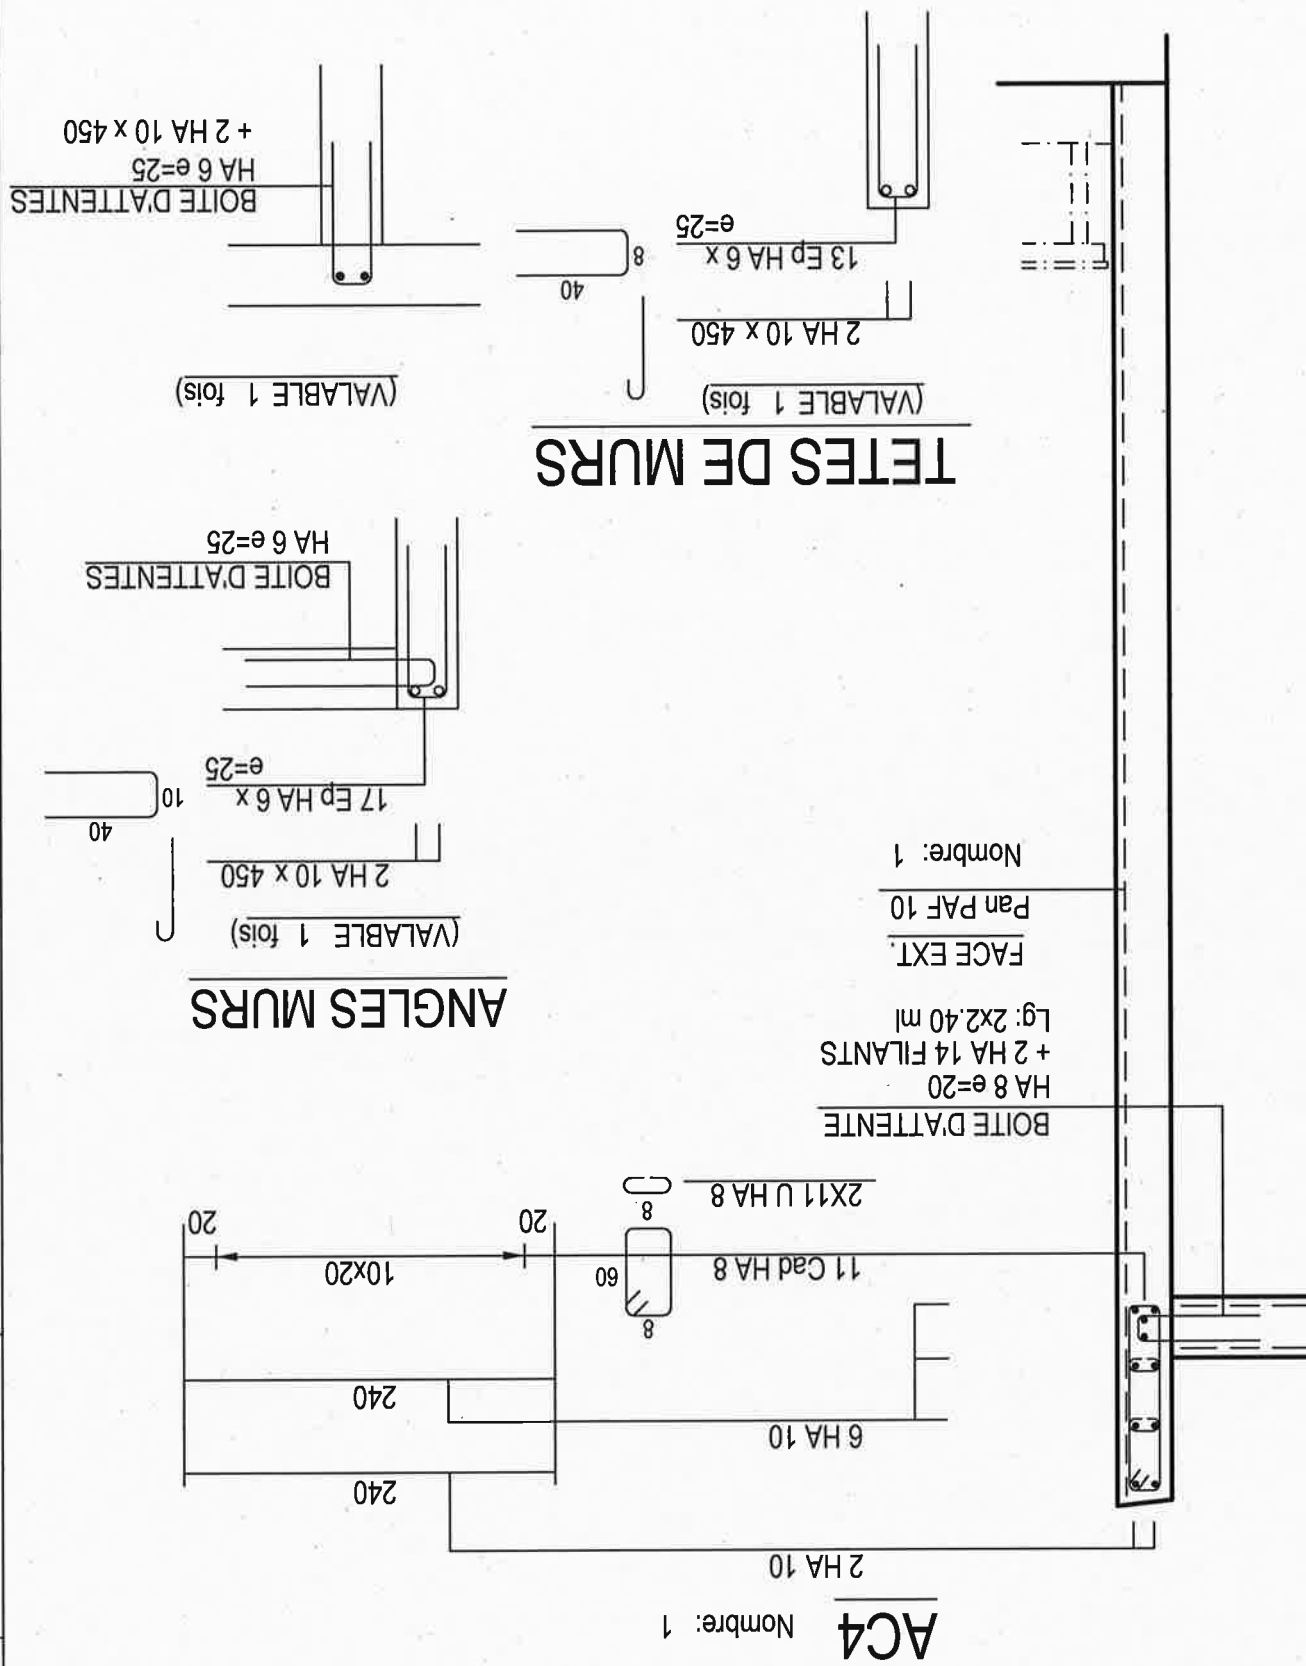

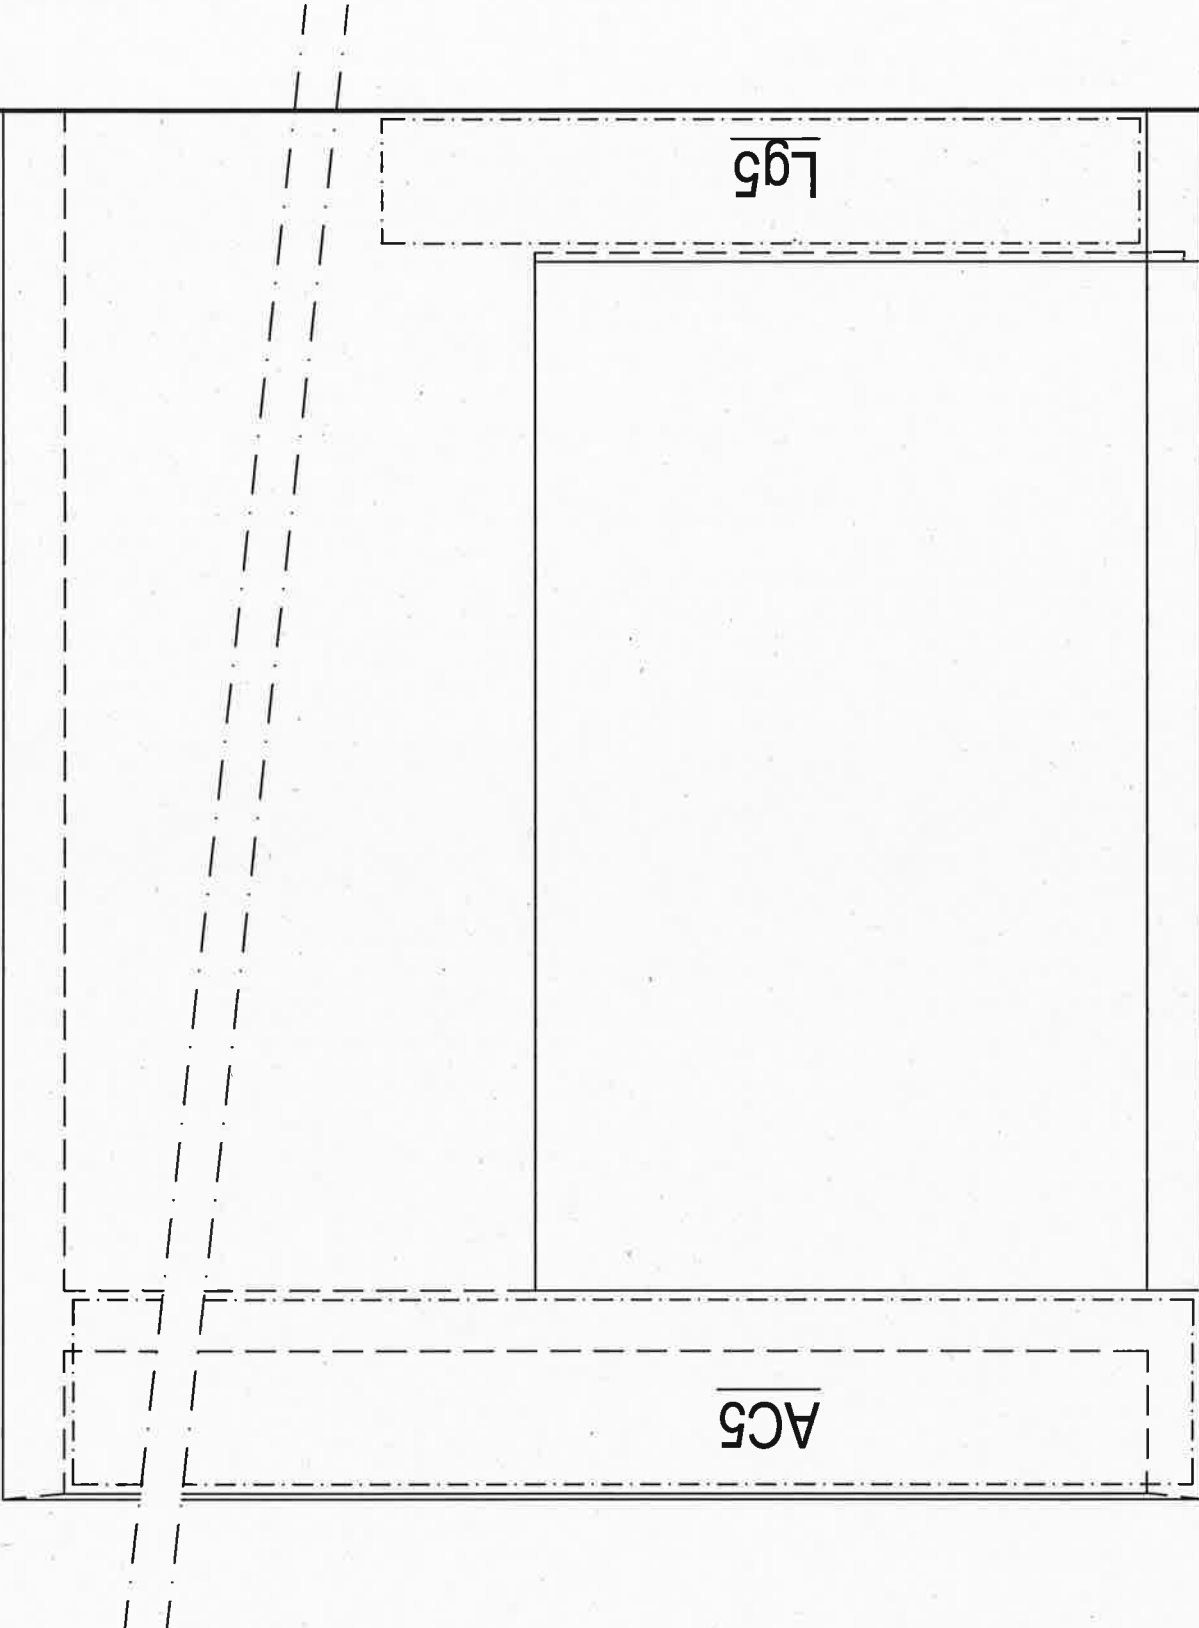AFF: S.13.12.119	Bât: B	LA MULATIERE-69350 LaMulatiere CREATION de LOGEMENTS	BA au REZ	Plan n° B 41	Page: 10
MUR M5 					

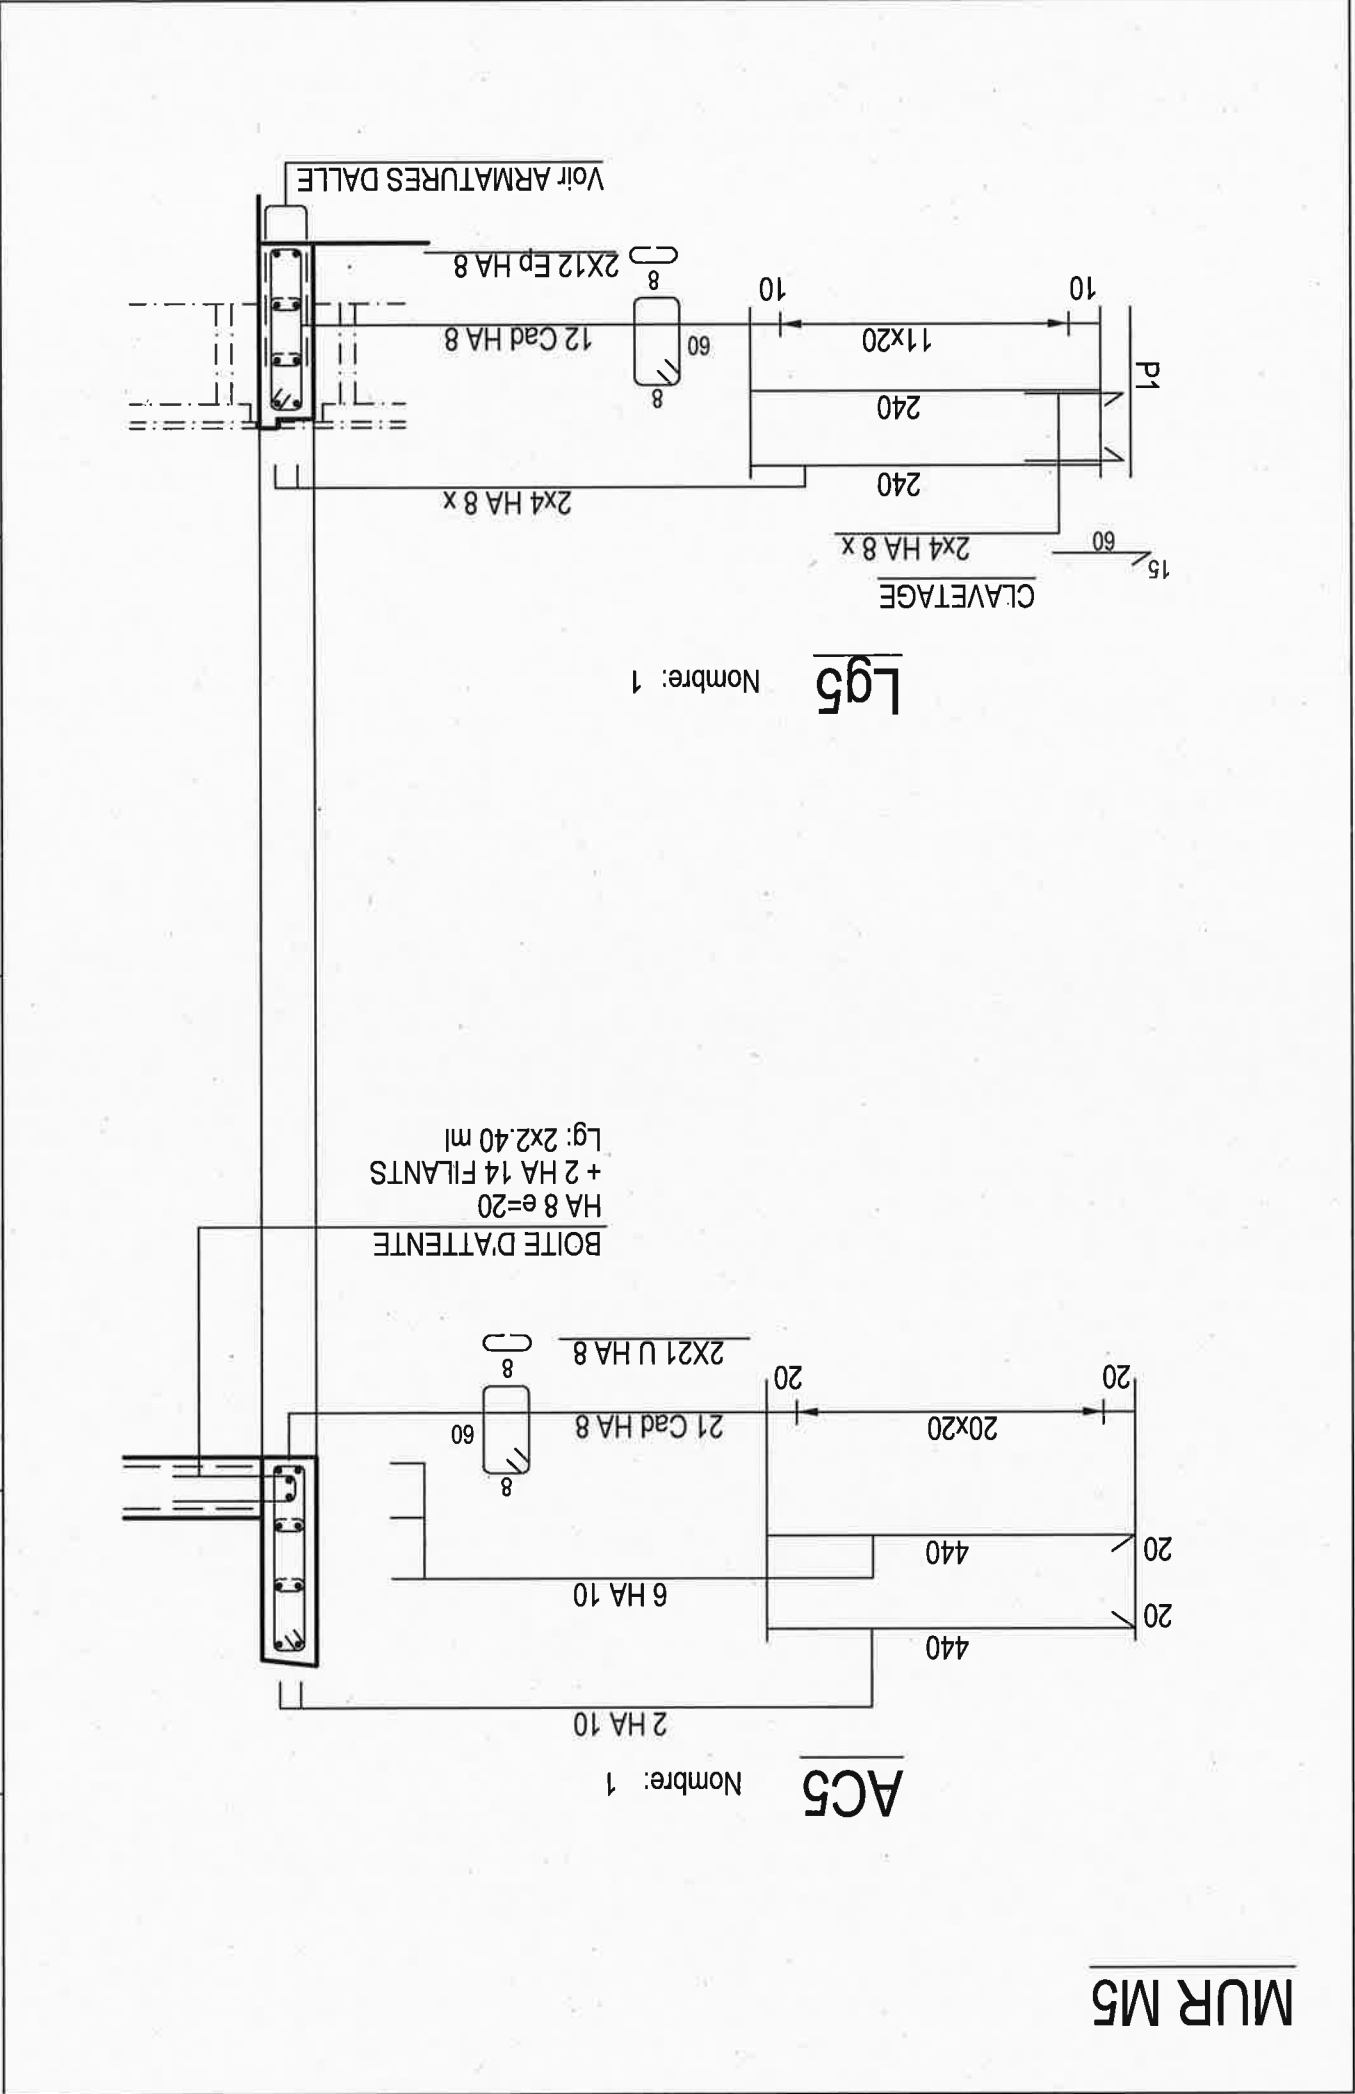


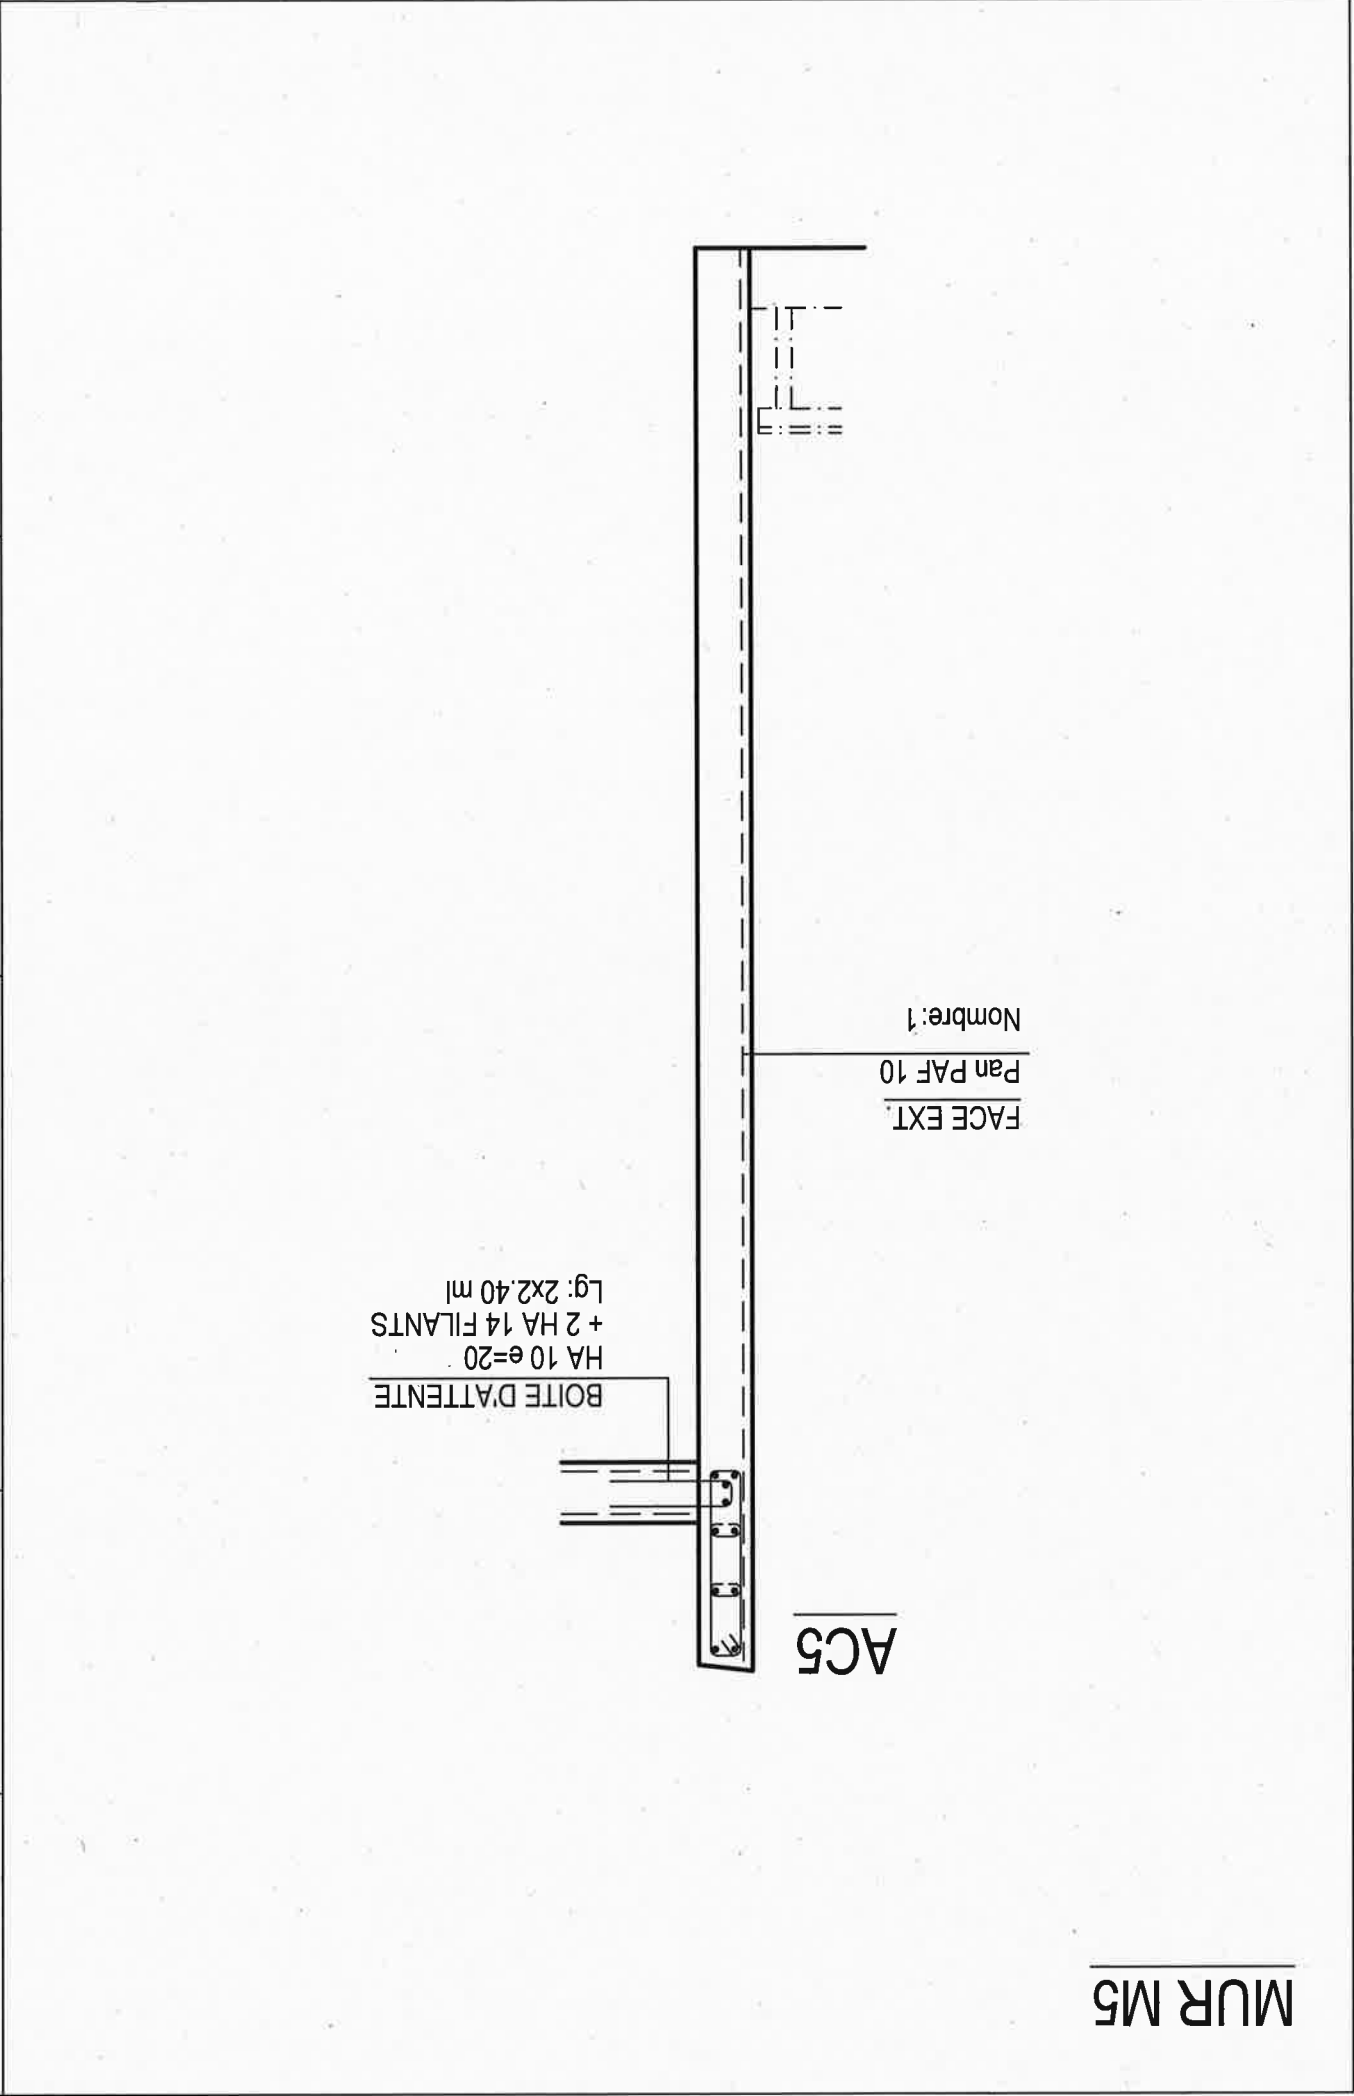


AFF: S.13.12.119	Bât: B	LA MULATIERE-69350 LaMulatiere CREATION de LOGEMENTS	BA au REZ	Plan n° B 41	Page: 13
E3 Nombre: 1 E2 Nombre: 1					
E4 Nombre: 1 E5 Nombre: 2					
BOITE D'ATTENTE HA 8 e=20 + 2 HA 14 FILANTS Lg: 2x6.00 ml					

LINTEAUX INT.

L Nombre: 1

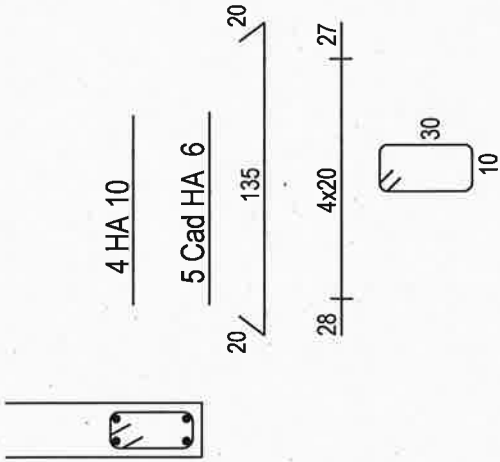


La Nombre: 1

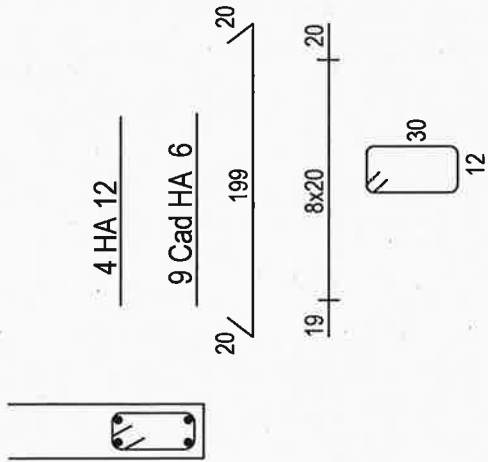

DETAIL "1"

COUPE HORIZONTALE

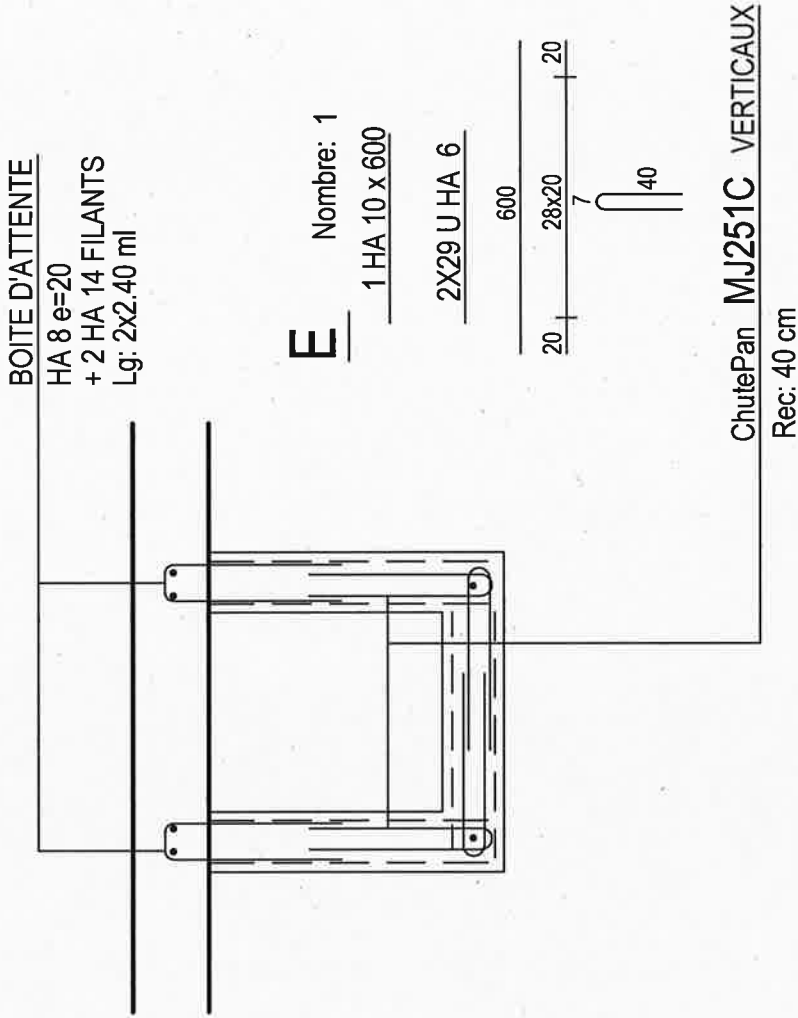


PALIER

HAUT et BAS

Chute Pan ST 15C
510x240 Rec: 40 cm

HAUT et BAS

Chute Pan ST 15C
510x240 Rec: 40 cm

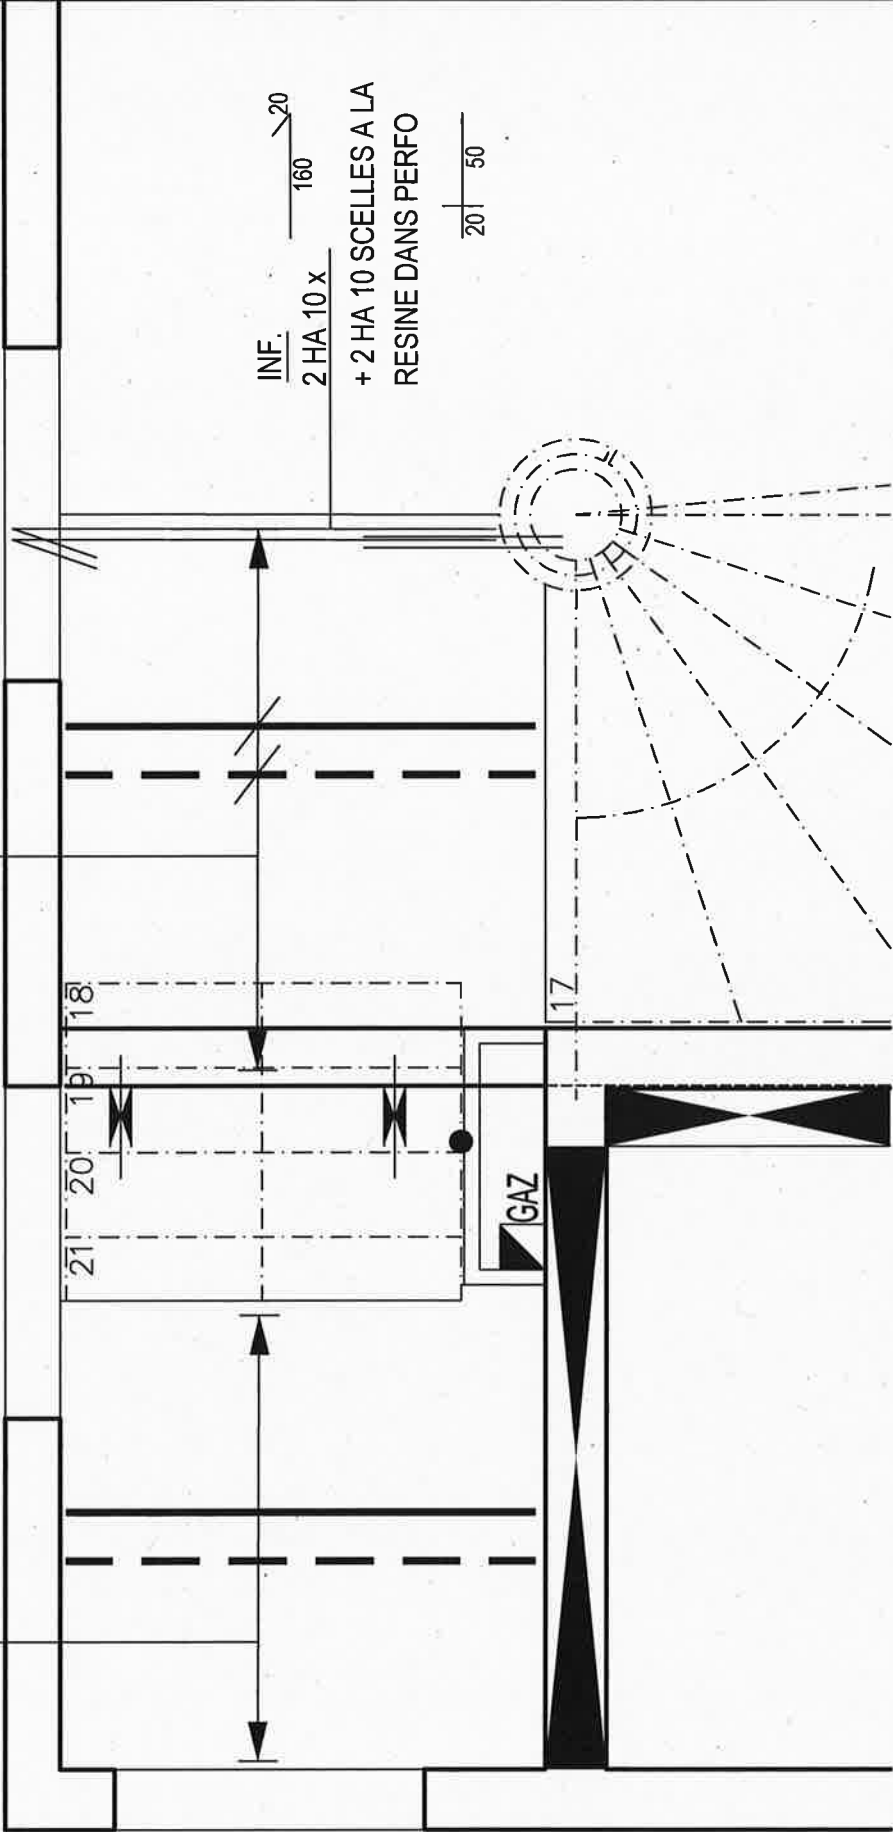

DALLES TERRASSE

HAUT et BAS

1.5 Pan ST 35
A COUPER Rec: 40 cm

INF. 20 370
2X2 HA 10 x

SUP. 20 370
2X2 HA 10 x

1 Pan MJ257
420X240 Rec: 40 cm

2 Pan MJ188
240X240 Rec: 40 cm


HAUT
1.5 Pan ST188
330X240 Rec: 40 cm

BAS
1.5 Pan MJ 335
330X240 Rec: 40 cm

INF. 20 370
2X2 HA 10 x

SUP. 20 370
2X2 HA 10 x

INF. 3 Pan MJ 335
A COUPER Rec: 40 cm

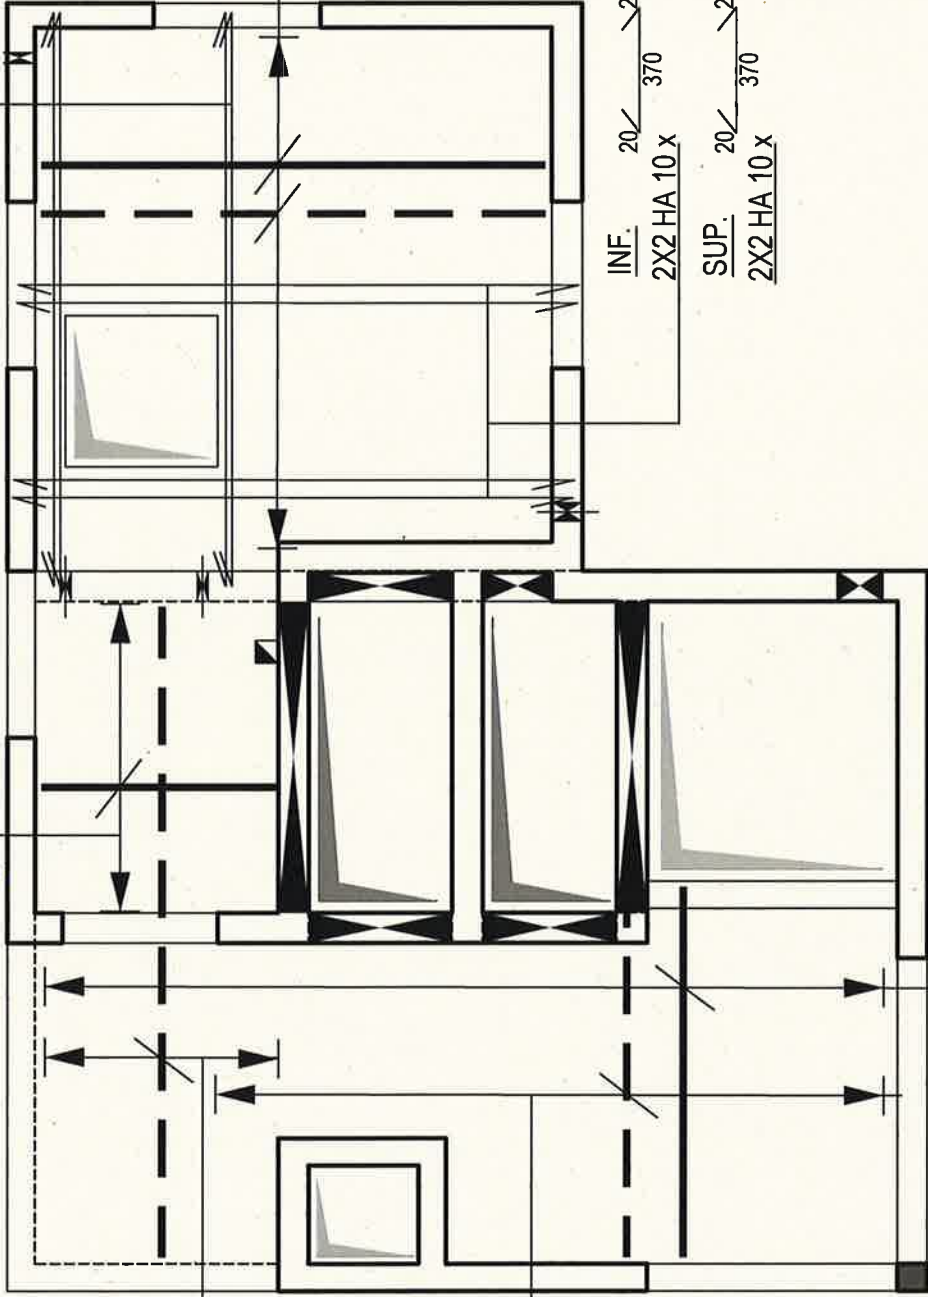

DALLES ASCENSEUR

