

NOHAO

Chemin de Fontanière-69350 La Mulatière

Création de logements

Les entreprises réalisant les travaux devront tenir compte des derniers plans architecte lors de la réalisation des travaux
Les plans du be MATTE ne doivent servir qu'au corps d'état concerné et doivent être des plans d'exécution.

ARCHITECTE(S): Ateler D'IS
BET STRUCTURE: BET MATTE
BET FLUIDES: PRELEM
ECONOMISTE: EXECO
BUREAU DE CONTROLE: VERITAS

M.O. Délégué: .
M.O.: .
CSPS: PSO ingénierie
M.O.E.: SUD EST COORDINATION
ENTREPRISE(S): Fontanel-pbc

Bât: A et B

ESCALIERS EXTERIEURES

Coffrage Armatures

DOE

INDICE	DATE	MODIFICATIONS
--------	------	---------------

A		

Aciers HA (T) FeE500
Aciers Doux (Ø) FeE 235
Aciers TS FeE 500
Béton fc28 >= 25MPa
Enrobage = 3 cm

PLAN N°
B47 0

DATE : 19/05/2016


MATTÉ
BUREAU D'ÉTUDES
STRUCTURES ET FLUIDES

119 BOULEVARD STALINGRAD 69100 VILLEURBANNE
Tél. 04 72 44 02 87 Fax 04 72 44 26 59
E-mail : bet@matte.fr

Dessiné par : J.BONDETTI
Contrôlé par : P. LIN
Ech :

Affaire N°
S.13.12.119


Ech: 1/50


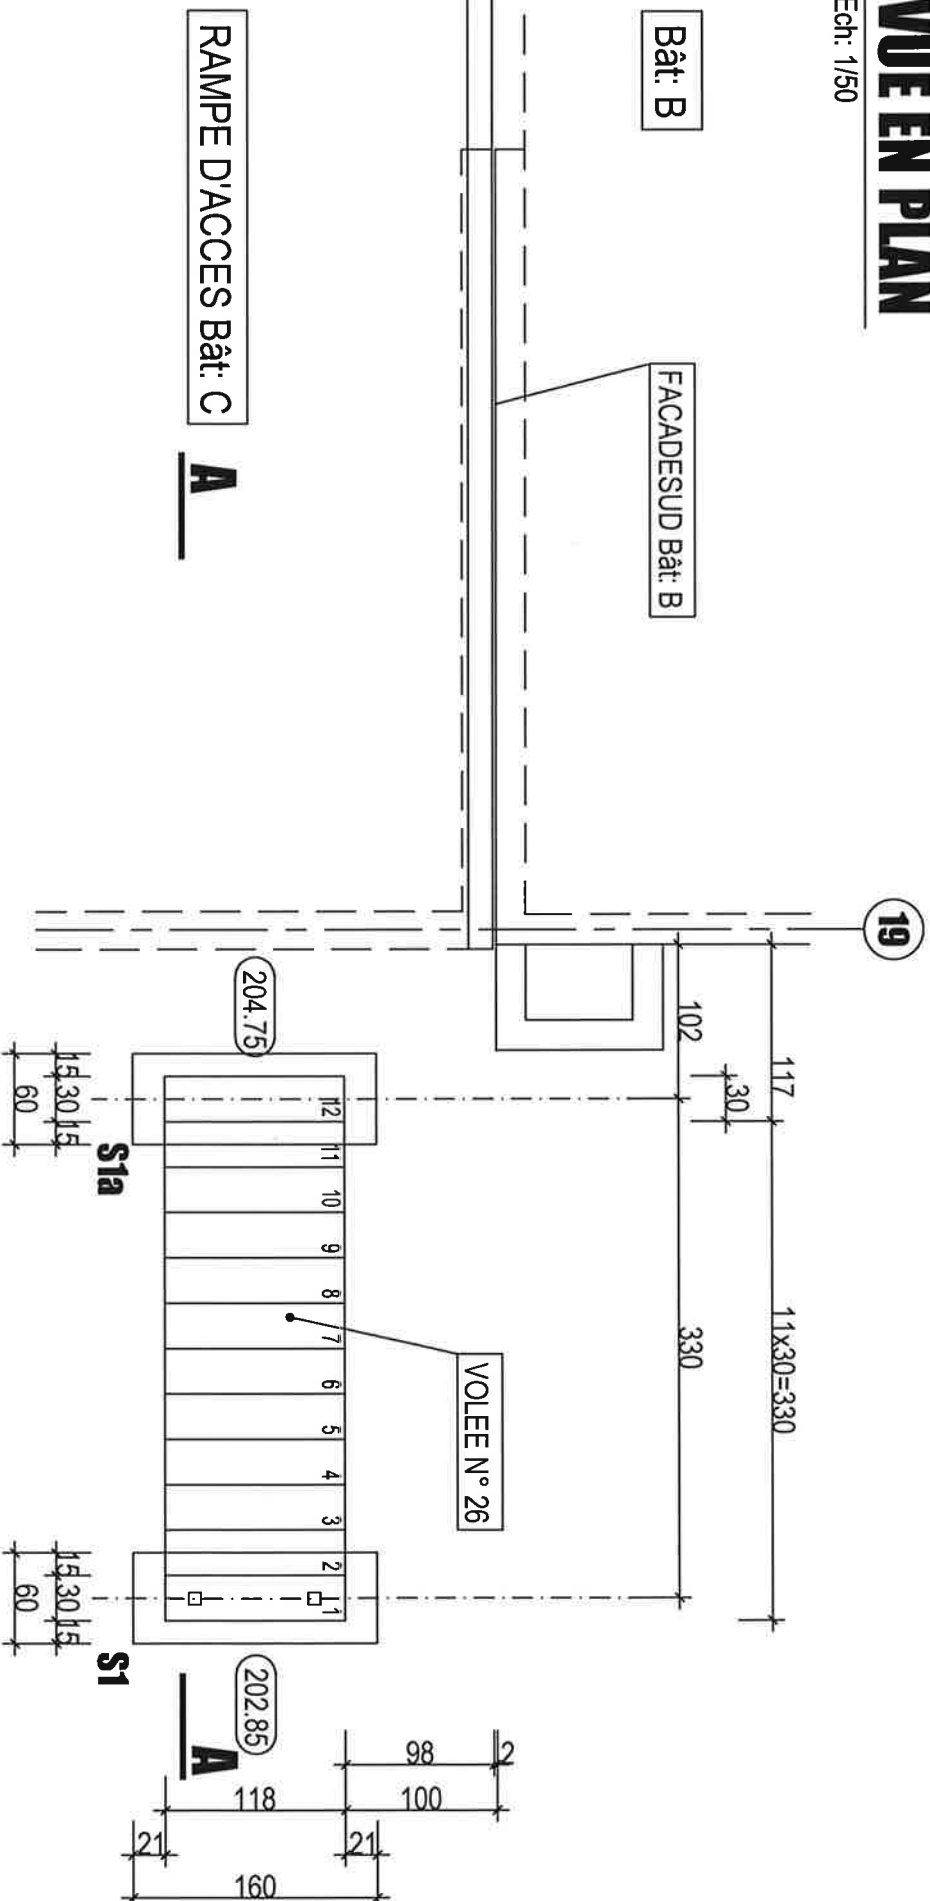


ESCALIER FILE 19 FACADE SUD

GOUPÉA

Ech: 1/50


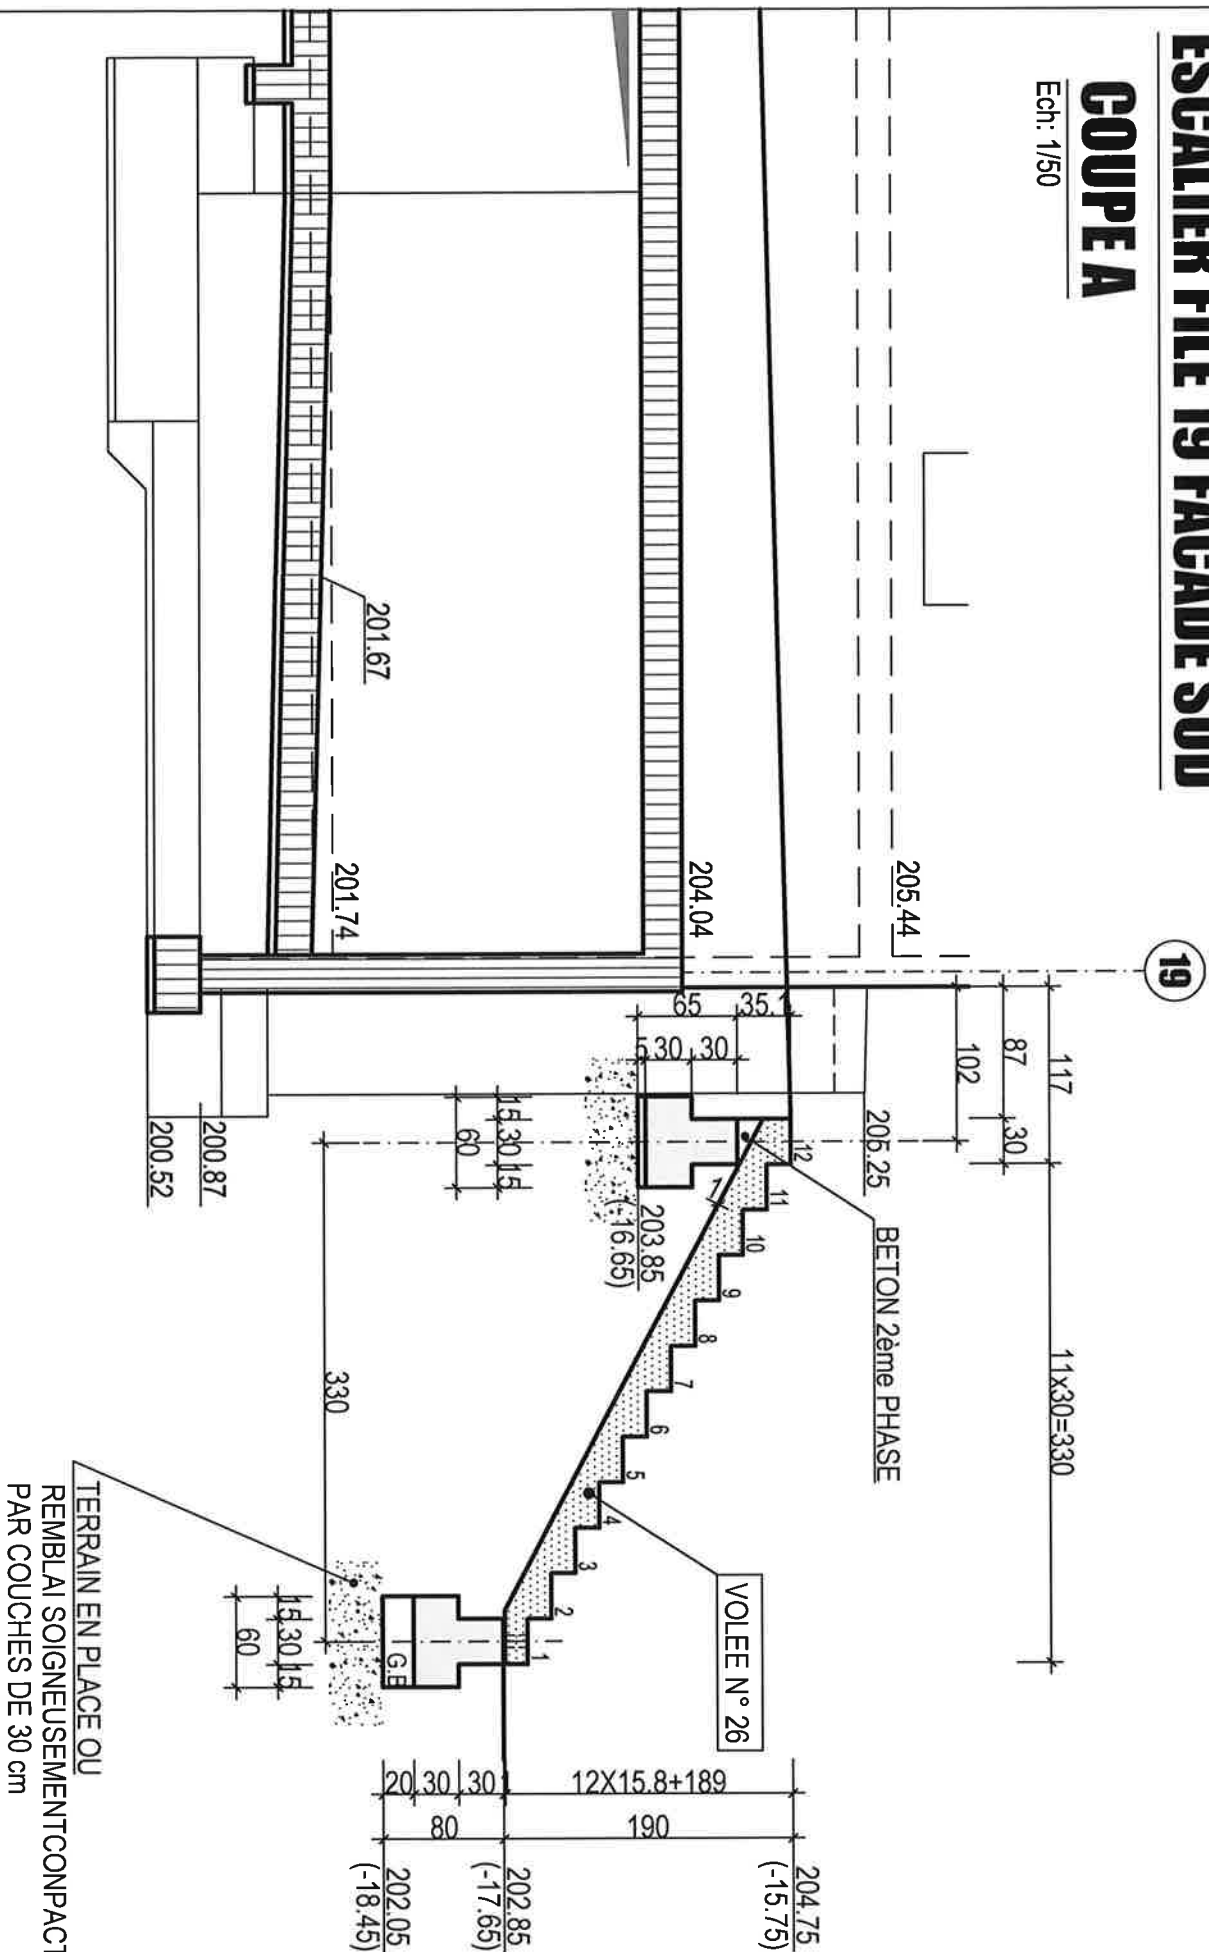


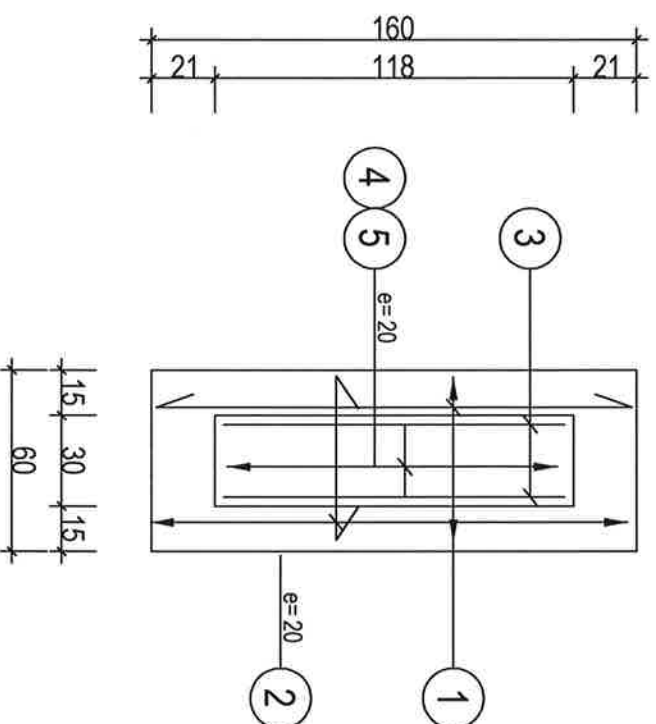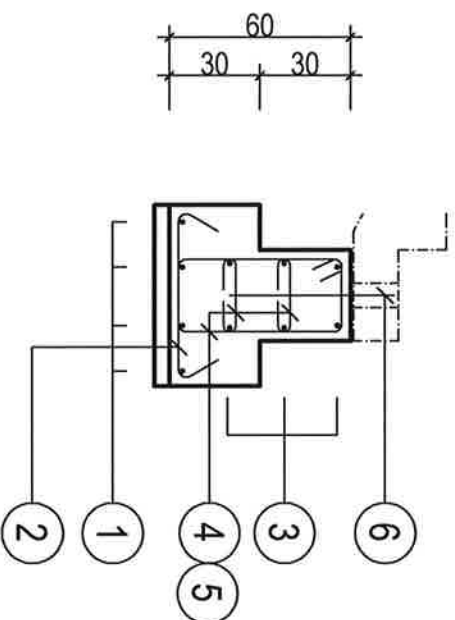ESCALIER FILE 19 FACADE SUD**S1** 1 p

1	4 HA 10 x	
2	8 HA 10 x	
3	6 HA 10 x	
4	6 HA 8 x	
5	2X6 HA 6 x	
6	2 HA 14 x	
7		
8		
9		
10		
11		
12		
13		
14		
15		

ESCALIER FILE 19 FACADE SUD

S1a 1 p

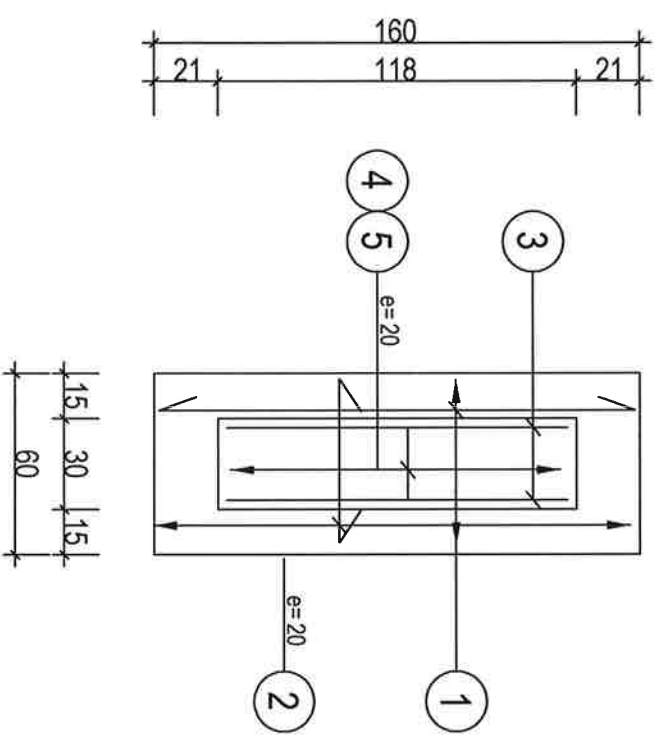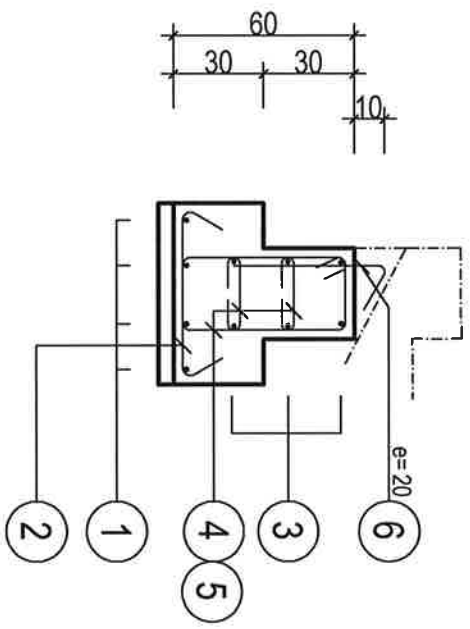

1	4 HA 10 x	
2	8 HA 10 x	
3	6 HA 10 x	
4	6 HA 8 x	
5	2X6 HA 6 x	
6	6 HA 8 x	
7		
8		
9		
10		
11		
12		
13		
14		
15		